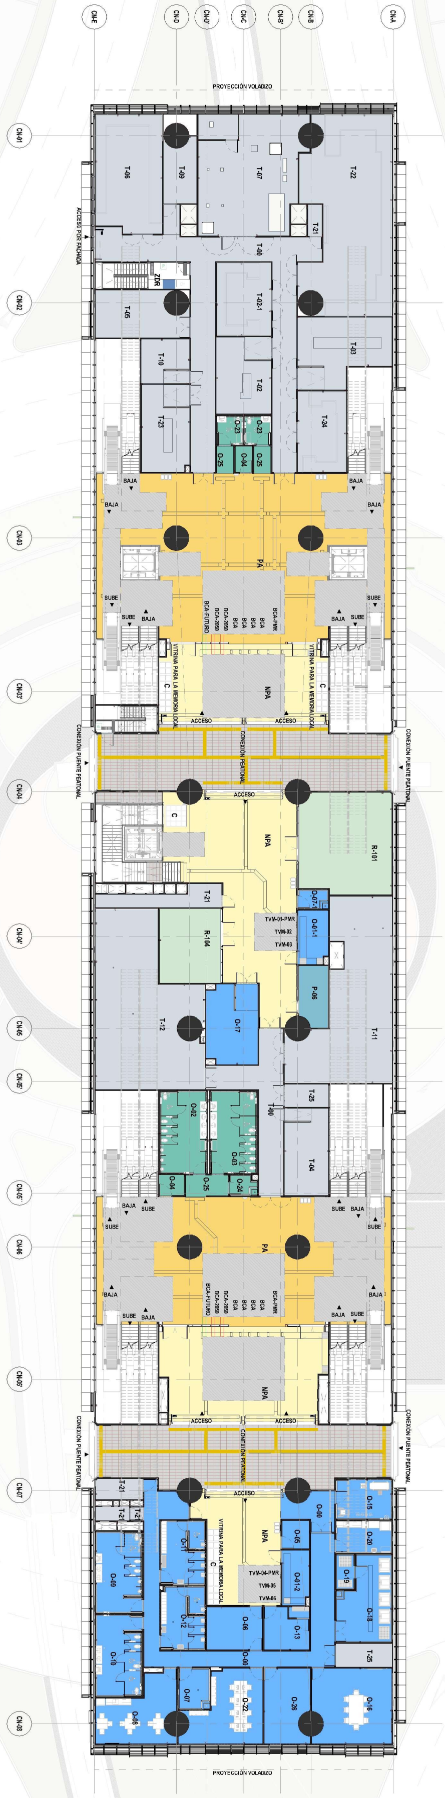
CN-E
CN-D
CN-D'
CN-C
CN-B'
CN-B
CN-A
PROYECCIÓN VOLADIZO
ACCESO PUERTA PACHECO
T-06
T-09
T-07
T-22
T-21
T-08
T-05
T-02-1
T-10
T-02
T-03
T-23
T-24
O-23
O-04
O-25
BAJA
SUBE
PA
BCA-PMR
BCA
BCA-2000
BCA-FUTURO
VITRINA PARA LA MEMORIA LOCAL
NPA
C
ACCESO
CONEXIÓN PUENTE PEATONAL
R-101
R-104
TVM-01-PMR
TVM-02
TVM-03
O-17
P-06
T-12
T-11
O-02
O-03
T-25
T-04
O-24
TVM-04-PMR
TVM-05
TVM-06
O-09
O-10
O-11
O-12
O-13
O-05
O-15
O-20
O-19
O-18
O-16
O-22
O-26
O-07
O-08
O-06
N
NP