Índice

Código de plano	REV.	Nombre del plano
L1T1-5445-308-CON-ED-INS-PL-0009_01	VDD	DISEÑO DETALLADO DEL NIVEL DE SÓTANO (SISTEMA CCTV) - DISPOSICIÓN GENERAL
L1T1-5445-308-CON-ED-INS-PL-0009_02	VDD	DISEÑO DETALLADO DEL NIVEL DE SÓTANO (SISTEMA CCTV) - COBERTURA
L1T1-5445-308-CON-ED-INS-PL-0009_03	VDD	DISEÑO DETALLADO DEL NIVEL DE ACCESO (SISTEMA CCTV) - DISPOSICIÓN GENERAL
L1T1-5445-308-CON-ED-INS-PL-0009_04	VDD	DISEÑO DETALLADO DEL NIVEL DE ACCESO (SISTEMA CCTV) -COBERTURA
L1T1-5445-308-CON-ED-INS-PL-0009_05	VDD	DISEÑO DETALLADO DEL NIVEL INTERMEDIO (SISTEMA SISTEMA CCTV) - DISPOSICIÓN GENERAL
L1T1-5445-308-CON-ED-INS-PL-0009_06	VDD	DISEÑO DETALLADO DEL NIVEL INTERMEDIO (SISTEMA SISTEMA CCTV) - COBERTURA
L1T1-5445-308-CON-ED-INS-PL-0009_07	VDD	DISEÑO DETALLADO DEL NIVEL DE PLATAFORMA (SISTEMA CCTV) - DISPOSICIÓN GENERAL
L1T1-5445-308-CON-ED-INS-PL-0009_08	VDD	DISEÑO DETALLADO DEL NIVEL DE PLATAFORMA (SISTEMA CCTV) - COBERTURA

VDD

KEY PLAN

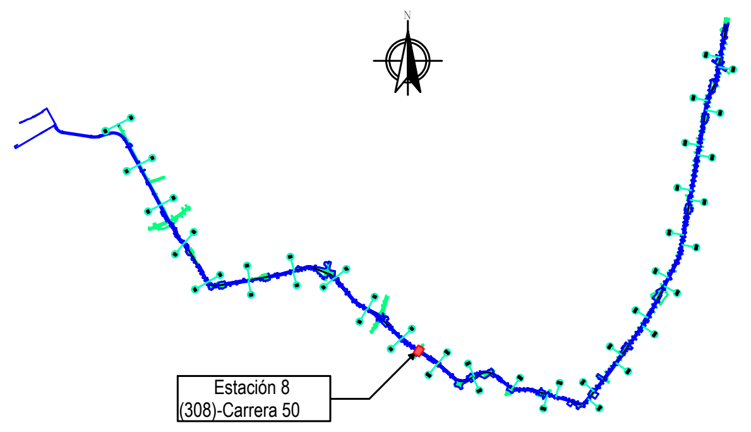

NOTAS

CONVENCIONES

N.°	PLANOS DE REFERENCIA	REV.

N.°	MODELO BIM DE REFERENCIA	REV.

N.°	PAQUETE DE TRABAJO DE REFERENCIA	REV.

METRO BOGOTÁ

GCS
Consorcio Consultores PMO Bogotá

CONSORCIO SUPERVISOR PLMB

wsp
Líder de Diseño Interfaz y Gerencia de Integración

DISEÑÓ: WANG KEJIA Mat.: R2022011515	REVISÓ: YANG BAODONG Mat.:	APROBÓ: ZHANG YUJIE Mat.:
ING_TÉCNICO_WSP Mat.: NÚMERO DE MATRÍCULA	*APRO_INTEGRACIÓN_WSP Mat.: NÚMERO DE MATRÍCULA	

REVISIÓN N.°	FECHA	DESCRIPCIÓN	REVISÓ	APROBÓ	APROBACIÓN CLIENTE
VDD	15/10/2023	Emitido para revisión y comentarios del cliente e Interventoría - Incluye comentarios / modificado donde se indica en el control de cambios	Y.B.	Z.Y.	
VCC	15/06/2023	Emitido para revisión y comentarios del cliente e Interventoría - Incluye comentarios / modificado donde se indica en el control de cambios	Y.B.	Z.Y.	
VBB	11/10/2022	Emitido para revisión y comentarios del cliente e Interventoría	Y.B.	Z.Y.	
VA0	25/09/2022	Emitido para comentarios internos - Emisión preliminar para comentarios	Y.B.	Z.Y.	

METRO LÍNEA 1

METRO LÍNEA 1
CONTRATO DE CONCESIÓN N.º 163 DE 2019

PROYECTO PRIMERA LÍNEA DEL METRO DE BOGOTÁ - TRAMO 1

SISTEMAS Y EQUIPOS

TELECOMUNICACIONES

ESTACIÓN CARRERA 50 - DISEÑO DETALLADO
SISTEMA CCTV
TABLA DE CONTENIDO

DIRECTOR INTERVENTORÍA: J. DESCARGA N. Mat.: 25202-68697 CND	ESPECIALISTA INTERVENTORÍA: Mat.:	PLANCHA N.º L1T1-5445-308-CON-ED-INS-PL-0009_00_VDD	ESCALA: GRÁFICO	REVISIÓN N.º VDD	HOJA N.º 0 DE 8
		ARCHIVO: L1T1-5445-308-CON-ED-INS-PL-0009_VDD.dwg	FECHA: SEPTIEMBRE 2022		

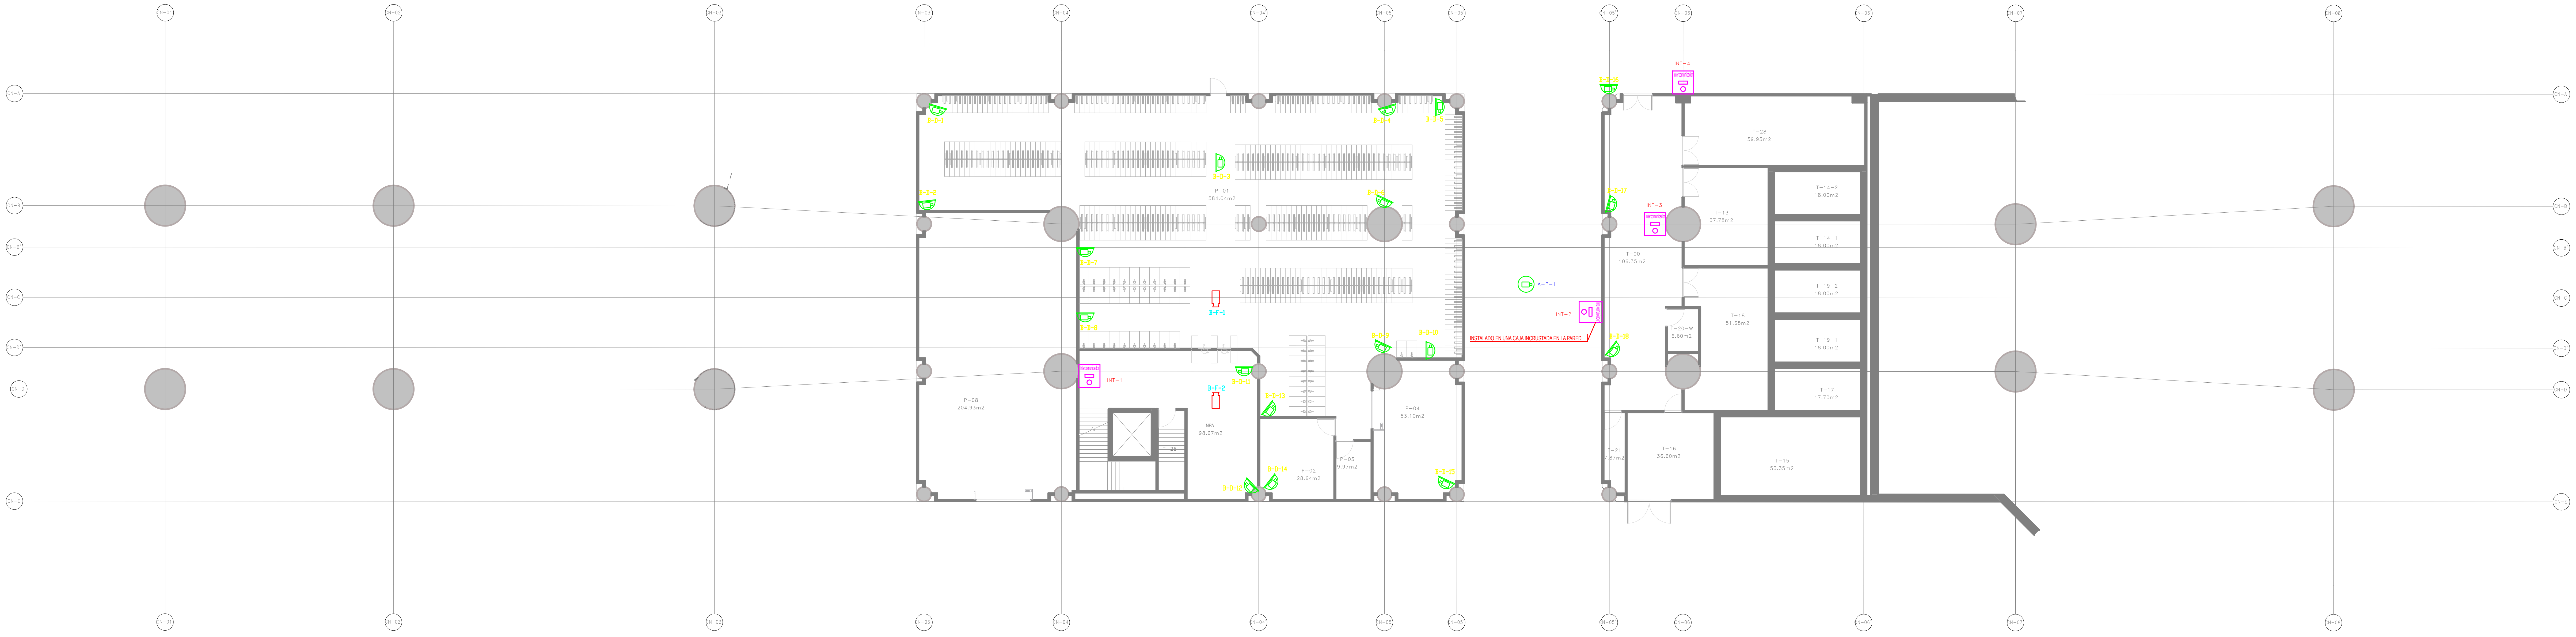
CN-03'
CN-04
CN-04'
CN-05
CN-05'
CN-06
CN-06'
CN-07
CN-A
CN-B
CN-B'
CN-C
CN-D'
CN-D
CN-E
B-D-1
B-D-2
B-D-3
B-D-4
B-D-5
B-D-6
B-D-7
B-D-8
B-D-9
B-D-10
B-D-11
B-D-12
B-D-13
B-D-14
B-D-15
B-D-16
B-D-17
B-D-18
B-F-1
B-F-2
A-P-1
INT-1
INT-2
INT-3
INT-4
Intercomunicador
P-01
584.04m2
P-08
204.93m2
NPA
98.67m2
T-25
P-02
28.64m2
P-03
9.97m2
P-04
53.10m2
T-00
106.35m2
T-28
59.93m2
T-13
37.78m2
T-14-2
18.00m2
T-14-1
18.00m2
T-19-2
18.00m2
T-18
51.68m2
T-20-W
6.60m2
T-19-1
18.00m2
T-17
17.70m2
T-21
7.87m2
T-16
36.60m2
T-15
53.35m2

INSTALADO EN UNA CAJA INCRUSTADA EN LA PARED

KEY PLAN

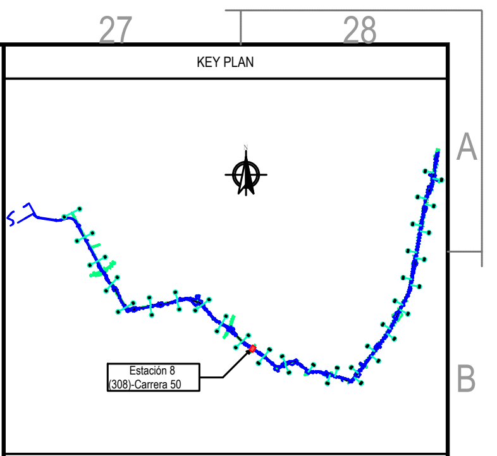
Estación 8
(308)-Carrera 50

NOTAS

1.Este plano debe revisarse junto con el informe de diseño de L1T1-5445-000-CON-ED-INS-IN-0001 y L1T1-5420-308-CON-ED-INS-PL-0001.
2.Para el listado de equipo, consulte L1T1-5445-000-CON-ED-INS-CO-0001.
3.Para el listado del cable Ethernet (incluyendo el Ethernet para los puertos de contacto seco conectados a los intercomunicadores), se incluye en los planos de los enlaces de acceso de RMS.
4.Para el listado de cables conectados a la detección de intrusos, se incluye en los planos del ACS.
5.La información de las bandejas de cables y tuberías se refiere a los planos de CNL.
6. Los criterios de denominación de las cámaras son los siguientes:
  Nivel - tipo de cámara - código de la cámara.
    Definición de nivel:
      B: como nivel del sótano;
      A: como nivel de acceso;
      I: como nivel intermedio;
      P: como nivel de plataforma.
    Definición del tipo de cámara:
      D: como cámara domo;
      F: como cámara fija;
      P: como cámara PTZ.
E.G: B-F-1 es una cámara fija con código 1 en el nivel del sótano.

CONVENCIONES

DESCRIPCIÓN DE LOS ICONOS

⌓	Cámara de domo
▭	Cámara fija (tipo inteligente)
⊖	Cámara PTZ
PAM	Monitor de vigilancia de pasajeros
DEC	Decodificador de vídeo
Intercomunicador	Intercomunicador

N.º	PLANOS DE REFERENCIA	REV.
1	L1T1-5420-308-CON-ED-INS-PL-0001	VCC

N.º	MODELO BIM DE REFERENCIA	REV.
1	L1T1-0000-308-CON-ED-ARQ-MO-0001.RVT (BL 2023-03-03)	VCC

N.º	PAQUETE DE TRABAJO DE REFERENCIA	REV.

METRO BOGOTÁ
GCS Consorcio Consultores PMO Bogotá
CONSORCIO SUPERVISOR PLMB
wsp Líder de Diseño Interfaz y Gerencia de Integración

DISEÑO:
WANG KEJIA
Mat.: R2022011515

APROBÓ:
ZHANG YUJIE
Mat.: NÚMERO DE MATRÍCULA

ING_TÉCNICO_WSP
Mat.: NÚMERO DE MATRÍCULA

REVISÓ:
YANG BAODONG
Mat.:

MODELÓ/DIBUJÓ:
WANG KEJIA
Mat.:R2022011515

APRO_INTEGRACIÓN_WSP
Mat.: NÚMERO DE MATRÍCULA
"Aprobada bajo el marco de los límites y condiciones establecido en la tercera sección del parágrafo del apéndice 1 sección 1 del acuerdo del contrato de diseño"

REVISIÓN N.º	FECHA	DESCRIPCIÓN	REVISÓ	APROBÓ	APROBACIÓN CLIENTE
VDD	15/10/2023	Emitido para revisión y comentarios del cliente e Interventoría - Incluye comentarios / modificado donde se indica en el control de cambios	Y.B.	Z.Y.	
VCC	15/06/2023	Emitido para revisión y comentarios del cliente e Interventoría - Incluye comentarios / modificado donde se indica en el control de cambios	Y.B.	Z.Y.	
VBB	11/10/2022	Emitido para revisión y comentarios del cliente e Interventoría	Y.B.	Z.Y.	
VA0	25/09/2022	Emitido para comentarios internos - Emisión preliminar para comentarios	Y.B.	Z.Y.	

METRO LÍNEA 1

DIRECTOR INTERVENTORÍA:
JAVIER DESCARGA N.
Mat.: 25202-68697 CND

ESPECIALISTA INTERVENTORÍA:
Mat.:

FECHA:
OCTUBRE 2023

METRO LÍNEA 1
CONTRATO DE CONCESIÓN N.º 163 DE 2019

PROYECTO PRIMERA LÍNEA DEL METRO DE BOGOTÁ - TRAMO 1

SISTEMAS Y EQUIPOS

TELECOMUNICACIONES

ESTACIÓN CARRERA 50 - DISEÑO DETALLADO DE LA NIVEL SÓTANO
SISTEMA CCTV
DISPOSICIÓN GENERAL

PLANCHA N.º L1T1-5445-308-CON-ED-INS-PL-0009_01_VDD
ARCHIVO: L1T1-5445-308-CON-ED-INS-PL-0009_VDD.dwg
ESCALA: 1:100
FECHA: SEPTIEMBRE 2022
REVISIÓN N.º VDD
HOJA N.º 1 DE 8

KEY PLAN

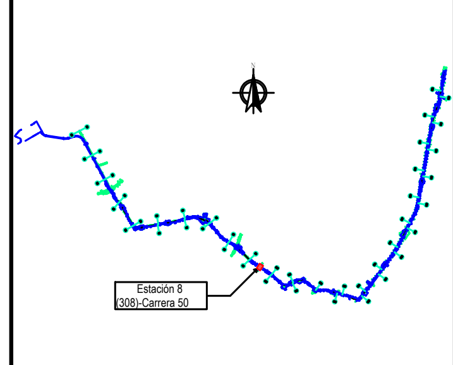

NOTAS

1.Este plano debe revisarse junto con el informe de diseño de L1T1-5445-000-CON-ED-INS-IN-0001 y L1T1-5420-308-CON-ED-INS-PL-0001.
2.Para el listado de equipo, consulte L1T1-5445-000-CON-ED-INS-CO-0001.
3.Para el listado del cable Ethernet (incluyendo el Ethernet para los puertos de contacto seco conectados a los intercomunicadores), se incluye en los planos de los enlaces de acceso de RMS.
4.Para el listado de cables conectados a la detección de intrusos, se incluye en los planos del ACS.
5.La información de las bandejas de cables y tuberías se refiere a los planos de CNL.
6. Los criterios de denominación de las cámaras son los siguientes:
  Nivel - tipo de cámara - código de la cámara.
    Definición de nivel:
      B: como nivel del sótano;
      A: como nivel de acceso;
      I: como nivel intermedio;
      P: como nivel de plataforma.
    Definición del tipo de cámara:
      D: como cámara domo;
      F: como cámara fija;
      P: como cámara PTZ.
E.G: B-F-1 es una cámara fija con código 1 en el nivel del sótano.

CONVENCIONES

DESCRIPCIÓN DE LOS ICONOS

	Cámara de domo
	Cámara fija (tipo inteligente)
	Cámara PTZ
PAM	Monitor de vigilancia de pasajeros
DEC	Decodificador de vídeo
Intercomunicador	Intercomunicador

N.º	PLANOS DE REFERENCIA	REV.
1	L1T1-5420-308-CON-ED-INS-PL-0001	VCC

N.º	MODELO BIM DE REFERENCIA	REV.
1	L1T1-0000-308-CON-ED-ARQ-MO-0001.RVT (BL 2023-03-03)	VCC

N.º	PAQUETE DE TRABAJO DE REFERENCIA	REV.

METRO BOGOTÁ
GCS Consorcio Consultores PMO Bogotá
CONSORCIO SUPERVISOR PLMB
wsp Líder de Diseño Interfaz y Gerencia de Integración

DISEÑÓ: WANG KEJIA Mat.: R2022011515	APROBÓ: ZHANG YUJIE Mat.: NÚMERO DE MATRÍCULA
REVISÓ: YANG BAODONG Mat.:	MODELÓ/DIBUJÓ: WANG KEJIA Mat.:R2022011515

ING_TÉCNICO_WSP
Mat.: NÚMERO DE MATRÍCULA

APRO_INTEGRACIÓN_WSP
Mat.: NÚMERO DE MATRÍCULA
"*Aprobada bajo el marco de los límites y condiciones establecido en la tercera sección del parágrafo del apéndice 1 sección 1 del acuerdo del contrato de diseño"

REVISIÓN N.º	FECHA	DESCRIPCIÓN	REVISÓ	APROBÓ	APROBACIÓN CLIENTE
VDD	15/10/2023	Emitido para revisión y comentarios del cliente e Interventoría - Incluye comentarios / modificado donde se indica en el control de cambios	Y.B.	Z.Y.	

METRO LÍNEA 1

METRO LÍNEA 1
CONTRATO DE CONCESIÓN N.º 163 DE 2019

PROYECTO PRIMERA LÍNEA DEL METRO DE BOGOTÁ - TRAMO 1

DIRECTOR INTERVENTORÍA:
JAVIER DESCARGA N.
Mat.: 25202-68697 CND

ESPECIALISTA INTERVENTORÍA:
Mat.:

FECHA:
OCTUBRE 2023

SISTEMAS Y EQUIPOS

TELECOMUNICACIONES

ESTACIÓN CARRERA 50 - DISEÑO DETALLADO DE LA NIVEL SÓTANO
SISTEMA CCTV
COBERTURA

PLANCHA N.º: L1T1-5445-308-CON-ED-INS-PL-0009_02_VDD
ARCHIVO: L1T1-5445-308-CON-ED-INS-PL-0009_VDD.dwg
ESCALA: 1:100
FECHA: OCTUBRE 2023
REVISIÓN N.º: VDD
HOJA N.º: 2 DE 8

CN-01
CN-02
CN-03
CN-03'
CN-04
CN-04'
CN-05
CN-05'
CN-06
CN-06'
CN-07
CN-08
CN-A
CN-B
CN-B'
CN-C
CN-D'
CN-D
CN-E
A-D-1
A-D-2
A-D-3
A-D-4
A-D-5
A-D-6
A-D-7
A-D-8
Intercomunicador
INT-5
INT-6
INT-7
NPA
984.44m2
T-08
69.68m2
T-25
7.74m2
T-20-L
7.51m2
T-26
488.22m2

KEY PLAN

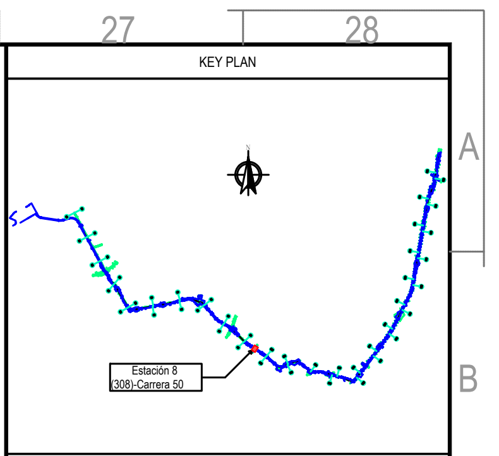

NOTAS

1.Este plano debe revisarse junto con el informe de diseño de L1T1-5445-000-CON-ED-INS-IN-0001 y L1T1-5420-308-CON-ED-INS-PL-0001.
2.Para el listado de equipo, consulte L1T1-5445-000-CON-ED-INS-CO-0001.
3.Para el listado del cable Ethernet (incluyendo el Ethernet para los puertos de contacto seco conectados a los intercomunicadores), se incluye en los planos de los enlaces de acceso de RMS.
4.Para el listado de cables conectados a la detección de intrusos, se incluye en los planos del ACS.
5.La información de las bandejas de cables y tuberías se refiere a los planos de CNL.
6. Los criterios de denominación de las cámaras son los siguientes:
  Nivel - tipo de cámara - código de la cámara.
    Definición de nivel:
      B: como nivel del sótano;
      A: como nivel de acceso;
      I: como nivel intermedio;
      P: como nivel de plataforma.
    Definición del tipo de cámara:
      D: como cámara domo;
      F: como cámara fija;
      P: como cámara PTZ.
E.G: B-F-1 es una cámara fija con código 1 en el nivel del sótano.

CONVENCIONES

DESCRIPCIÓN DE LOS ICONOS

◒	Cámara de domo
▭	Cámara fija (tipo inteligente)
⊖	Cámara PTZ
PAM	Monitor de vigilancia de pasajeros
DEC	Decodificador de vídeo
Intercomunicador	Intercomunicador

N.º	PLANOS DE REFERENCIA	REV.
1	L1T1-5420-308-CON-ED-INS-PL-0001	VCC

N.º	MODELO BIM DE REFERENCIA	REV.
1	L1T1-0000-308-CON-ED-ARQ-MO-0001.RVT (BL 2023-03-03)	VCC

N.º	PAQUETE DE TRABAJO DE REFERENCIA	REV.

Consorcio Consultores PMO Bogotá

CONSORCIO SUPERVISOR PLMB

Líder de Diseño
Interfaz y
Gerencia de Integración

DISEÑÓ: WANG KEJIA Mat.: R2022011515	APROBÓ: ZHANG YUJIE Mat.: NÚMERO DE MATRÍCULA	ING_TÉCNICO_WSP Mat.: NÚMERO DE MATRÍCULA
REVISÓ: YANG BAODONG Mat.:	MODELÓ/DIBUJÓ: WANG KEJIA Mat.:R2022011515	APRO_INTEGRACIÓN_WSP Mat.: NÚMERO DE MATRÍCULA ""Aprobada bajo el marco de los límites y condiciones establecido en la tercera sección del parágrafo del apéndice 1 sección 1 del acuerdo del contrato de diseño"

REVISIÓN N.º	FECHA	DESCRIPCIÓN	REVISÓ	APROBÓ	APROBACIÓN CLIENTE
VDD	15/10/2023	Emitido para revisión y comentarios del cliente e Interventoría - Incluye comentarios / modificado donde se indica en el control de cambios	Y.B.	Z.Y.	
VCC	15/06/2023	Emitido para revisión y comentarios del cliente e Interventoría - Incluye comentarios / modificado donde se indica en el control de cambios	Y.B.	Z.Y.	
VBB	11/10/2022	Emitido para revisión y comentarios del cliente e Interventoría	Y.B.	Z.Y.	
VA0	25/09/2022	Emitido para comentarios internos - Emisión preliminar para comentarios	Y.B.	Z.Y.	

METRO LÍNEA 1
CONTRATO DE CONCESIÓN N.º 163 DE 2019

PROYECTO PRIMERA LÍNEA DEL METRO DE BOGOTÁ - TRAMO 1

DIRECTOR INTERVENTORÍA: JAVIER DESCARGA N. Mat.: 25202-68697 CND	ESPECIALISTA INTERVENTORÍA: Mat.:	FECHA: OCTUBRE 2023

SISTEMAS Y EQUIPOS

TELECOMUNICACIONES

ESTACIÓN CARRERA 50 - DISEÑO DETALLADO DEL NIVEL ACCESO
SISTEMA CCTV
DISPOSICIÓN GENERAL

PLANCHA N.º L1T1-5445-308-CON-ED-INS-PL-0009_03_VDD	ESCALA: 1:100	REVISIÓN N.º VDD	HOJA N.º 3 DE 8
ARCHIVO: L1T1-5445-308-CON-ED-INS-PL-0009_VDD.dwg	FECHA: SEPTIEMBRE 2022		

CN-01
CN-02
CN-03
CN-04
CN-05
CN-06
CN-07
CN-08
CN-A
CN-B
CN-B'
CN-C
CN-D'
CN-D
CN-E
T-08
69.68m2
T-25
7.74m2
T-26
488.22m2

KEY PLAN

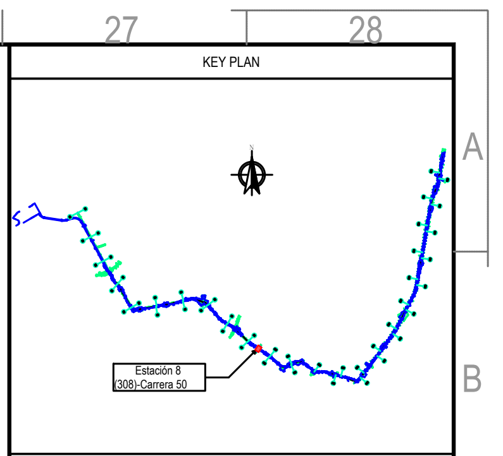

NOTAS

1.Este plano debe revisarse junto con el informe de diseño de L1T1-5445-000-CON-ED-INS-IN-0001 y L1T1-5420-308-CON-ED-INS-PL-0001.
2.Para el listado de equipo, consulte L1T1-5445-000-CON-ED-INS-CO-0001.
3.Para el listado del cable Ethernet (incluyendo el Ethernet para los puertos de contacto seco conectados a los intercomunicadores), se incluye en los planos de los enlaces de acceso de RMS.
4.Para el listado de cables conectados a la detección de intrusos, se incluye en los planos del ACS.
5.La información de las bandejas de cables y tuberías se refiere a los planos de CNL.
6. Los criterios de denominación de las cámaras son los siguientes:
  Nivel - tipo de cámara - código de la cámara.
   Definición de nivel:
    B: como nivel del sótano;
    A: como nivel de acceso;
    I: como nivel intermedio;
    P: como nivel de plataforma.
   Definición del tipo de cámara:
    D: como cámara domo;
    F: como cámara fija;
    P: como cámara PTZ.
E.G: B-F-1 es una cámara fija con código 1 en el nivel del sótano.

CONVENCIONES

DESCRIPCIÓN DE LOS ICONOS

	Cámara de domo
	Cámara fija (tipo inteligente)
	Cámara PTZ
PAM	Monitor de vigilancia de pasajeros
DEC	Decodificador de vídeo
Intercomunicador	Intercomunicador

N.º	PLANOS DE REFERENCIA	REV.
1	L1T1-5420-308-CON-ED-INS-PL-0001	VCC

N.º	MODELO BIM DE REFERENCIA	REV.
1	L1T1-0000-308-CON-ED-ARQ-MO-0001.RVT (BL 2023-03-03)	VCC

N.º	PAQUETE DE TRABAJO DE REFERENCIA	REV.

METRO BOGOTÁ

Consorcio Consultores PMO Bogotá

CONSORCIO SUPERVISOR PLMB

Líder de Diseño Interfaz y Gerencia de Integración

DISEÑO: WANG KEJIA Mat.: R2022011515	APROBÓ: ZHANG YUJIE Mat.: NÚMERO DE MATRÍCULA	ING_TÉCNICO_WSP Mat.: NÚMERO DE MATRÍCULA
REVISÓ: YANG BAODONG Mat.:	MODELÓ/DIBUJÓ: WANG KEJIA Mat.:R2022011515	APRO_INTEGRACIÓN_WSP Mat.: NÚMERO DE MATRÍCULA "Aprobada bajo el marco de los límites y condiciones establecido en la tercera sección del parágrafo del apéndice 1 sección 1 del acuerdo del contrato de diseño"

REVISIÓN N.º	FECHA	DESCRIPCIÓN	REVISÓ	APROBÓ	APROBACIÓN CLIENTE
VDD	15/10/2023	Emitido para revisión y comentarios del cliente e Interventoría - Incluye comentarios / modificado donde se indica en el control de cambios	Y.B.	Z.Y.	

METRO LÍNEA 1

METRO LÍNEA 1
CONTRATO DE CONCESIÓN N.º 163 DE 2019

PROYECTO PRIMERA LÍNEA DEL METRO DE BOGOTÁ - TRAMO 1

DIRECTOR INTERVENTORÍA: JAVIER DESCARGA N. Mat.: 25202-68697 CND	ESPECIALISTA INTERVENTORÍA: Mat.:	FECHA: OCTUBRE 2023

SISTEMAS Y EQUIPOS

TELECOMUNICACIONES

ESTACIÓN CARRERA 50 - DISEÑO DETALLADO DEL NIVEL ACCESO
SISTEMA CCTV
COBERTURA

PLANCHA N.º L1T1-5445-308-CON-ED-INS-PL-0009_04_VDD	ESCALA: 1:100	REVISIÓN N.º VDD	HOJA N.º 4 DE 8
ARCHIVO: L1T1-5445-308-CON-ED-INS-PL-0009_VDD.dwg	FECHA: OCTUBRE 2023		

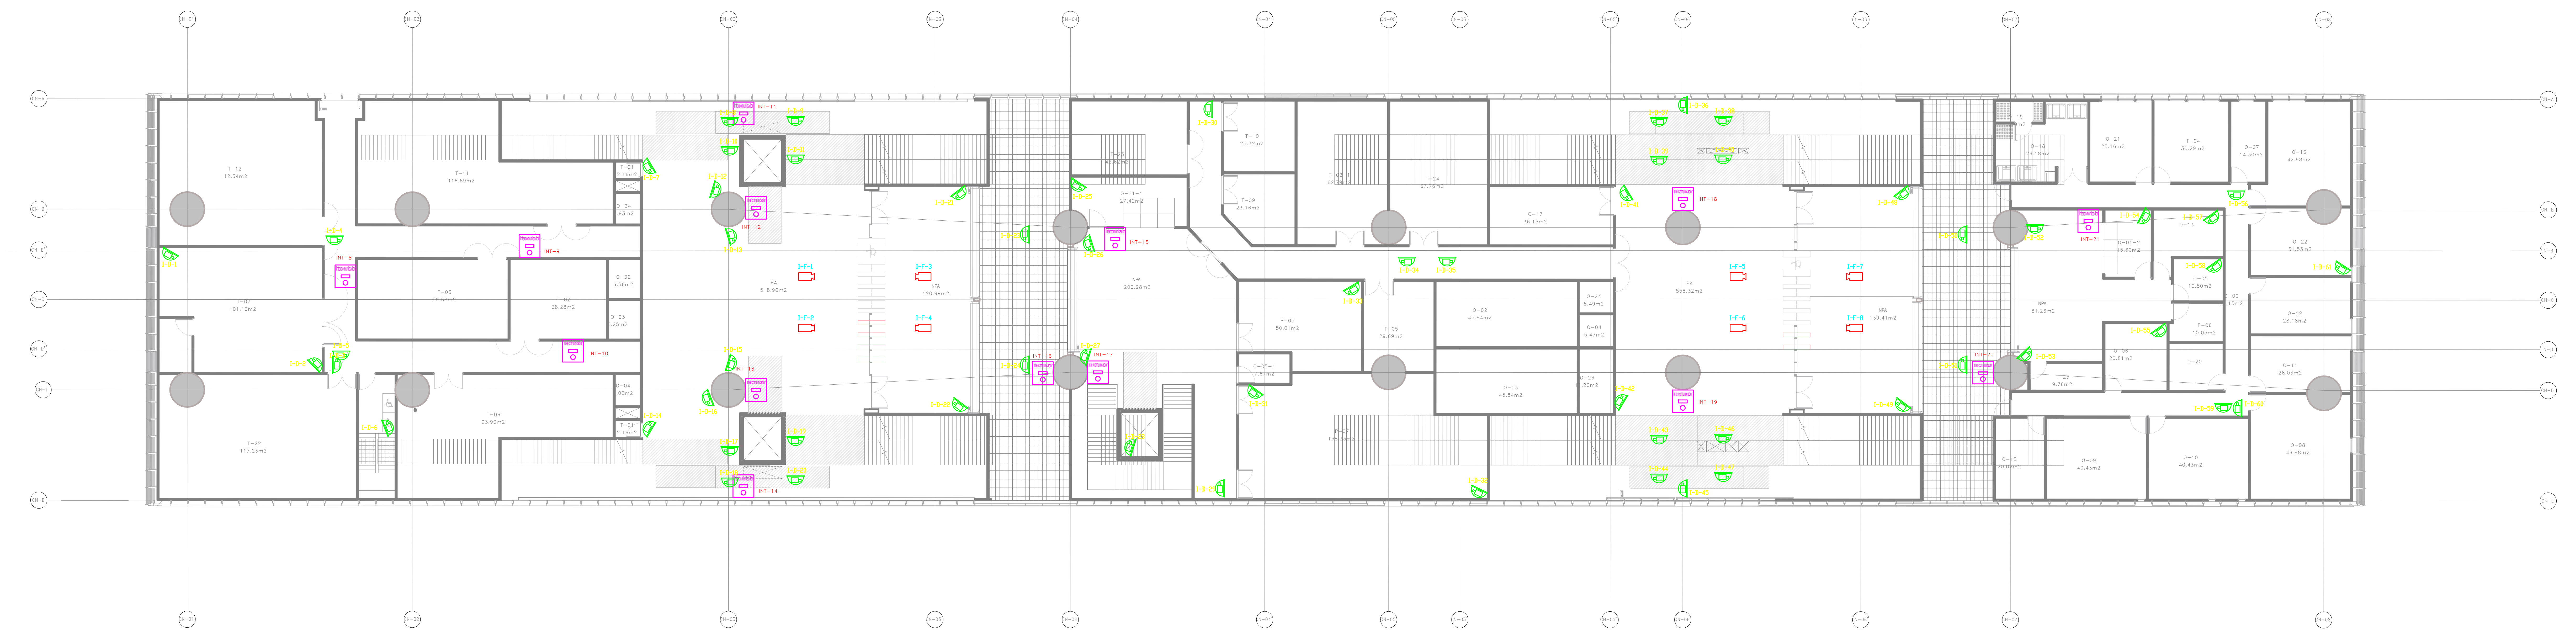

KEY PLAN

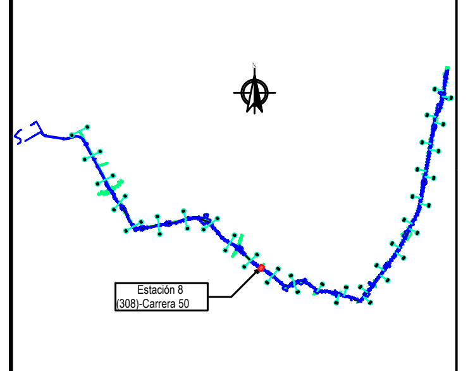

NOTAS

1.Este plano debe revisarse junto con el informe de diseño de L1T1-5445-000-CON-ED-INS-IN-0001 y L1T1-5420-308-CON-ED-INS-PL-0001.

2.Para el listado de equipo, consulte L1T1-5445-000-CON-ED-INS-CO-0001.

3.Para el listado del cable Ethernet (incluyendo el Ethernet para los puertos de contacto seco conectados a los intercomunicadores), se incluye en los planos de los enlaces de acceso de RMS.

4.Para el listado de cables conectados a la detección de intrusos, se incluye en los planos del ACS.

5.La información de las bandejas de cables y tuberías se refiere a los planos de CNL.

6. Los criterios de denominación de las cámaras son los siguientes:
Nivel - tipo de cámara - código de la cámara.
Definición de nivel:
B: como nivel del sótano;
A: como nivel de acceso;
I: como nivel intermedio;
P: como nivel de plataforma.
Definición del tipo de cámara:
D: como cámara domo;
F: como cámara fija;
P: como cámara PTZ.
E.G: B-F-1 es una cámara fija con código 1 en el nivel del sótano.

CONVENCIONES

DESCRIPCIÓN DE LOS ICONOS

◡	Cámara de domo
▭	Cámara fija (tipo inteligente)
⊖	Cámara PTZ
PAM	Monitor de vigilancia de pasajeros
DEC	Decodificador de vídeo
Intercomunicador	Intercomunicador

N.º	PLANOS DE REFERENCIA	REV.
1	L1T1-5420-308-CON-ED-INS-PL-0001	VCC

N.º	MODELO BIM DE REFERENCIA	REV.
1	L1T1-0000-308-CON-ED-ARQ-MO-0001.RVT (BL 2023-03-03)	VCC

N.º	PAQUETE DE TRABAJO DE REFERENCIA	REV.

METRO BOGOTÁ
Consorcio Consultores PMO Bogotá
CONSORCIO SUPERVISOR PLMB
Líder de Diseño Interfaz y Gerencia de Integración

DISEÑÓ: WANG KEJIA Mat.: R2022011515	APROBÓ: ZHANG YUJIE Mat.: NÚMERO DE MATRÍCULA	ING_TÉCNICO_WSP Mat.: NÚMERO DE MATRÍCULA
REVISÓ: YANG BAODONG Mat.:	MODELÓ/DIBUJÓ: WANG KEJIA Mat.:R2022011515	APRO_INTEGRACIÓN_WSP Mat.: NÚMERO DE MATRÍCULA "*Aprobada bajo el marco de los límites y condiciones establecido en la tercera sección del parágrafo del apéndice 1 sección 1 del acuerdo del contrato de diseño"

REVISIÓN N.º	FECHA	DESCRIPCIÓN	REVISÓ	APROBÓ	APROBACIÓN CLIENTE
VDD	15/10/2023	Emitido para revisión y comentarios del cliente e Interventoría - Incluye comentarios / modificado donde se indica en el control de cambios	Y.B.	Z.Y.	
VCC	15/06/2023	Emitido para revisión y comentarios del cliente e Interventoría - Incluye comentarios / modificado donde se indica en el control de cambios	Y.B.	Z.Y.	
VBB	11/10/2022	Emitido para revisión y comentarios del cliente e Interventoría	Y.B.	Z.Y.	
VA0	25/09/2022	Emitido para comentarios internos - Emisión preliminar para comentarios	Y.B.	Z.Y.	

METRO LÍNEA 1

METRO LÍNEA 1
CONTRATO DE CONCESIÓN N.º 163 DE 2019

PROYECTO PRIMERA LÍNEA DEL METRO DE BOGOTÁ - TRAMO 1

SISTEMAS Y EQUIPOS
TELECOMUNICACIONES
ESTACIÓN CARRERA 50 - DISEÑO DETALLADO DEL NIVEL INTERMEDIO
SISTEMA CCTV
DISPOSICIÓN GENERAL

DIRECTOR INTERVENTORÍA: JAVIER DESCARGA N. Mat.: 25202-68697 CND	ESPECIALISTA INTERVENTORÍA: Mat.:	FECHA: OCTUBRE 2023

PLANCHA N.º L1T1-5445-308-CON-ED-INS-PL-0009_05_VDD	ESCALA: 1:100	REVISIÓN N.º VDD	HOJA N.º 5 DE 8
ARCHIVO: L1T1-5445-308-CON-ED-INS-PL-0009_VDD.dwg	FECHA: SEPTIEMBRE 2022		

T-22
117.23m2
T-02-1
62.79m2
T-24
67.76m2
T-05
29.69m2
O-02
45.84m2
O-12
28.18m2
O-11
26.03m2
O-08
49.98m2

KEY PLAN

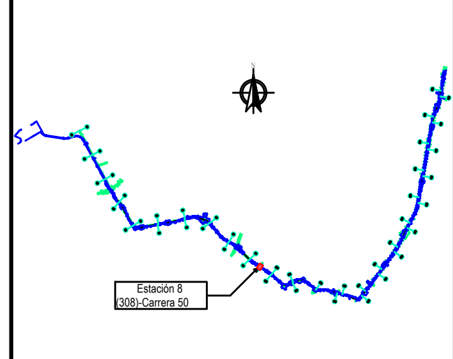

NOTAS

1.Este plano debe revisarse junto con el informe de diseño de L1T1-5445-000-CON-ED-INS-IN-0001 y L1T1-5420-308-CON-ED-INS-PL-0001.

2.Para el listado de equipo, consulte L1T1-5445-000-CON-ED-INS-CO-0001.

3.Para el listado del cable Ethernet (incluyendo el Ethernet para los puertos de contacto seco conectados a los intercomunicadores), se incluye en los planos de los enlaces de acceso de RMS.

4.Para el listado de cables conectados a la detección de intrusos, se incluye en los planos del ACS.

5.La información de las bandejas de cables y tuberías se refiere a los planos de CNL.

6. Los criterios de denominación de las cámaras son los siguientes:
  Nivel - tipo de cámara - código de la cámara.
    Definición de nivel:
      B: como nivel del sótano;
      A: como nivel de acceso;
      I: como nivel intermedio;
      P: como nivel de plataforma.
    Definición del tipo de cámara:
      D: como cámara domo;
      F: como cámara fija;
      P: como cámara PTZ.
E.G: B-F-1 es una cámara fija con código 1 en el nivel del sótano.

CONVENCIONES

DESCRIPCIÓN DE LOS ICONOS

📷	Cámara de domo
📷	Cámara fija (tipo inteligente)
◉	Cámara PTZ
PAM	Monitor de vigilancia de pasajeros
DEC	Decodificador de vídeo
Intercomunicador	Intercomunicador

N.º	PLANOS DE REFERENCIA	REV.
1	L1T1-5420-308-CON-ED-INS-PL-0001	VCC

N.º	MODELO BIM DE REFERENCIA	REV.
1	L1T1-0000-308-CON-ED-ARQ-MO-0001.RVT (BL 2023-03-03)	VCC

N.º	PAQUETE DE TRABAJO DE REFERENCIA	REV.

METRO BOGOTÁ

Consorcio Consultores PMO Bogotá

CONSORCIO SUPERVISOR PLMB

Líder de Diseño
Interfaz y
Gerencia de Integración

DISEÑÓ:
WANG KEJIA
Mat.: R2022011515

REVISÓ:
YANG BAODONG
Mat.:

APROBÓ:
ZHANG YUJIE
Mat.: NÚMERO DE MATRÍCULA

MODELÓ/DIBUJÓ:
WANG KEJIA
Mat.:R2022011515

ING_TÉCNICO_WSP
Mat.: NÚMERO DE MATRÍCULA

APRO_INTEGRACIÓN_WSP
Mat.: NÚMERO DE MATRÍCULA
*"Aprobada bajo el marco de los límites y condiciones establecido en la tercera sección del parágrafo del apéndice 1 sección 1 del acuerdo del contrato de diseño"

REVISIÓN N.º	FECHA	DESCRIPCIÓN	REVISÓ	APROBÓ	APROBACIÓN CLIENTE
VDD	15/10/2023	Emitido para revisión y comentarios del cliente e Interventoría - Incluye comentarios / modificado donde se indica en el control de cambios	Y.B.	Z.Y.	

METRO LÍNEA 1

DIRECTOR INTERVENTORÍA:
JAVIER DESCARGA N.
Mat.: 25202-68697 CND

ESPECIALISTA INTERVENTORÍA:
Mat.:

METRO LÍNEA 1
CONTRATO DE CONCESIÓN N.º 163 DE 2019

PROYECTO PRIMERA LÍNEA DEL METRO DE BOGOTÁ - TRAMO 1

FECHA:
OCTUBRE 2023

SISTEMAS Y EQUIPOS

TELECOMUNICACIONES

ESTACIÓN CARRERA 50 - DISEÑO DETALLADO DEL NIVEL INTERMEDIO
SISTEMA CCTV
COBERTURA

PLANCHA N.º L1T1-5445-308-CON-ED-INS-PL-0009_06_VDD

ARCHIVO: L1T1-5445-308-CON-ED-INS-PL-0009_VDD.dwg

ESCALA: 1:100

FECHA: OCTUBRE 2023

REVISIÓN N.º VDD

HOJA N.º 6 DE 8

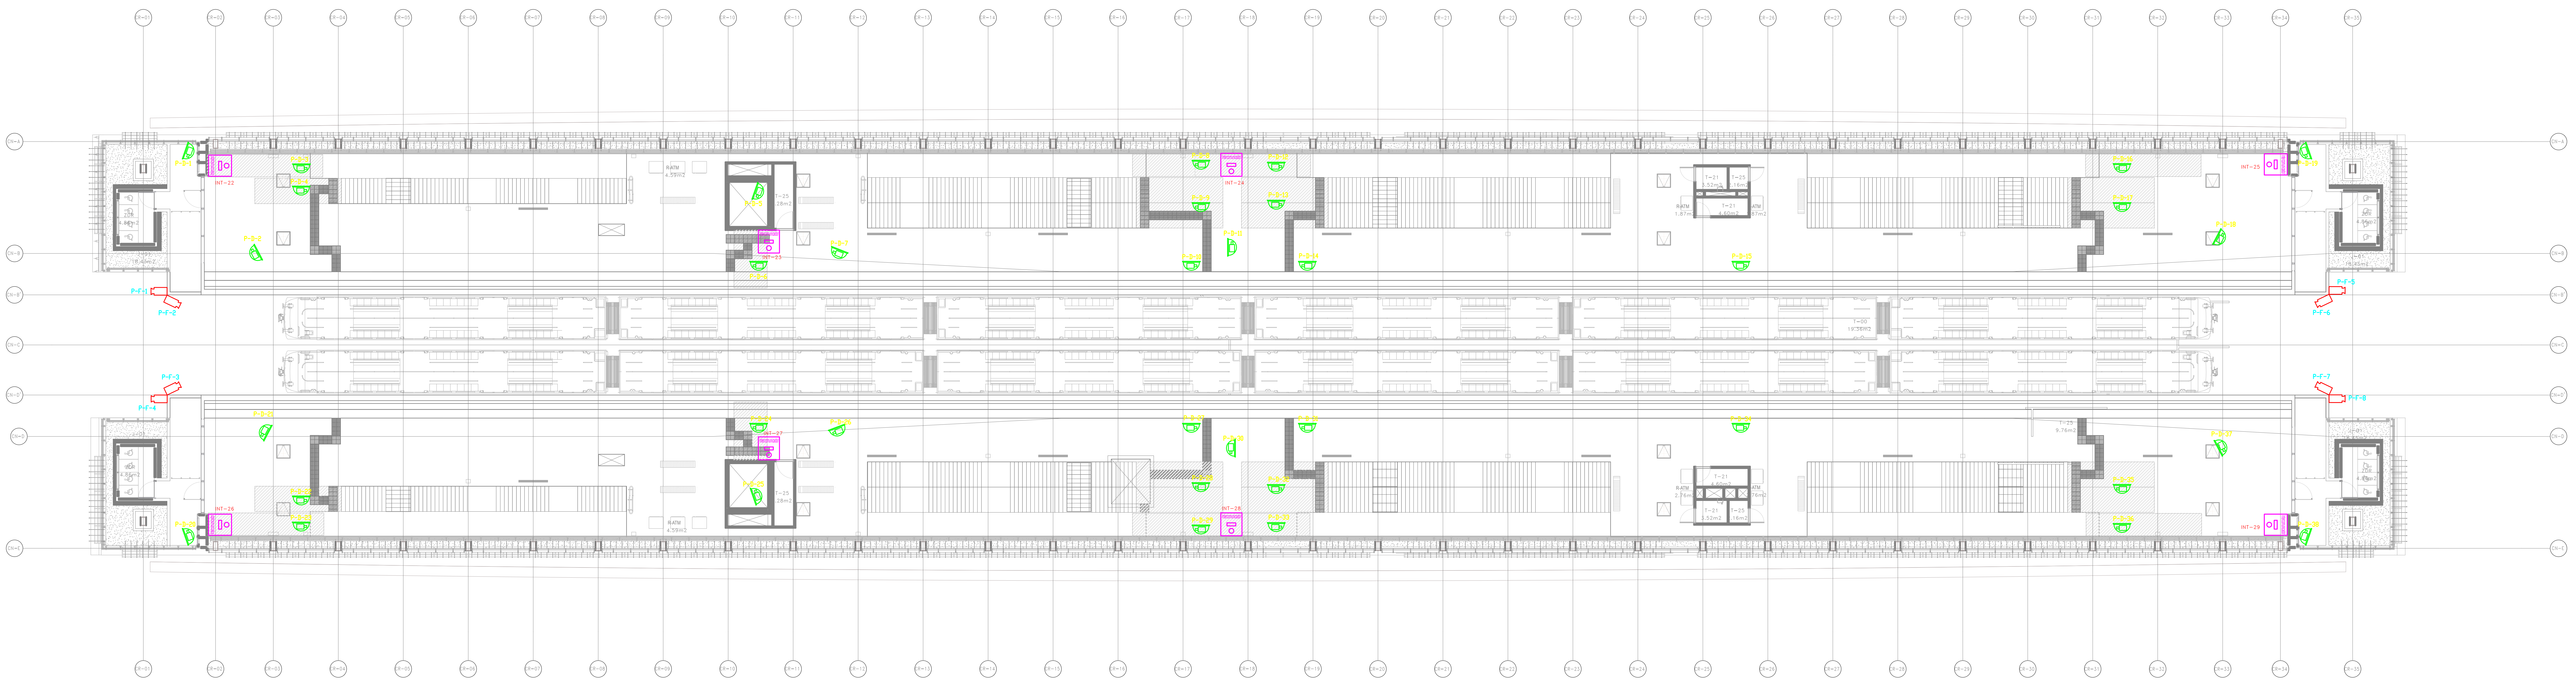
CN-A
CN-B
CN-B'
CN-C
CN-D'
CN-D
CN-E
P-D-1
P-D-2
P-D-3
P-D-4
P-D-5
P-D-6
P-D-7
P-D-8
P-D-9
P-D-10
P-D-11
P-D-12
P-D-13
P-D-14
P-D-15
P-D-16
P-D-17
P-D-18
P-D-19
P-D-20
P-D-21
P-D-22
P-D-23
P-D-24
P-D-25
P-D-26
P-D-27
P-D-28
P-D-29
P-D-30
P-D-31
P-D-32
P-D-33
P-D-34
P-D-35
P-D-36
P-D-37
P-D-38
P-F-1
P-F-2
P-F-3
P-F-4
P-F-5
P-F-6
P-F-7
P-F-8
INT-22
INT-23
INT-24
INT-25
INT-26
INT-27
INT-28
INT-29
Intercomunicador
ZDR
4.86m2
J-01
18.43m2
R-ATM
4.59m2
T-25
.28m2
T-21
3.52m2
T-25
2.16m2
T-21
4.60m2
R-ATM
1.87m2
R-ATM
2.76m2
T-00
19.36m2
T-25
9.76m2

KEY PLAN

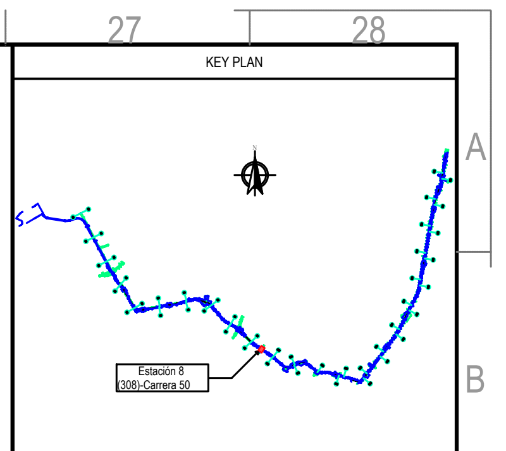
Estación 8
(308)-Carrera 50

NOTAS

1.Este plano debe revisarse junto con el informe de diseño de L1T1-5445-000-CON-ED-INS-IN-0001 y L1T1-5420-308-CON-ED-INS-PL-0001.
2.Para el listado de equipo, consulte L1T1-5445-000-CON-ED-INS-CO-0001.
3.Para el listado del cable Ethernet (incluyendo el Ethernet para los puertos de contacto seco conectados a los intercomunicadores), se incluye en los planos de los enlaces de acceso de RMS.
4.Para el listado de cables conectados a la detección de intrusos, se incluye en los planos del ACS.
5.La información de las bandejas de cables y tuberías se refiere a los planos de CNL.
6. Los criterios de denominación de las cámaras son los siguientes:
  Nivel - tipo de cámara - código de la cámara.
    Definición de nivel:
      B: como nivel del sótano;
      A: como nivel de acceso;
      I: como nivel intermedio;
      P: como nivel de plataforma.
    Definición del tipo de cámara:
      D: como cámara domo;
      F: como cámara fija;
      P: como cámara PTZ.
E.G: B-F-1 es una cámara fija con código 1 en el nivel del sótano.

CONVENCIONES

DESCRIPCIÓN DE LOS ICONOS

	Cámara de domo
	Cámara fija (tipo inteligente)
	Cámara PTZ
PAM	Monitor de vigilancia de pasajeros
DEC	Decodificador de vídeo
Intercomunicador	Intercomunicador

N.º	PLANOS DE REFERENCIA	REV.
1	L1T1-5420-308-CON-ED-INS-PL-0001	VCC

N.º	MODELO BIM DE REFERENCIA	REV.
1	L1T1-0000-308-CON-ED-ARQ-MO-0001.RVT (BL 2023-03-03)	VCC

N.º	PAQUETE DE TRABAJO DE REFERENCIA	REV.

Consorcio Consultores PMO Bogotá

CONSORCIO SUPERVISOR PLMB

Líder de Diseño Interfaz y Gerencia de Integración

DISEÑÓ: WANG KEJIA Mat.: R2022011515	APROBÓ: ZHANG YUJIE Mat.: NÚMERO DE MATRÍCULA	ING_TÉCNICO_WSP Mat.: NÚMERO DE MATRÍCULA
REVISÓ: YANG BAODONG Mat.:	MODELÓ/DIBUJÓ: WANG KEJIA Mat.:R2022011515	APRO_INTEGRACIÓN_WSP Mat.: NÚMERO DE MATRÍCULA ""Aprobada bajo el marco de los límites y condiciones establecido en la tercera sección del parágrafo del apéndice 1 sección 1 del acuerdo del contrato de diseño"

REVISIÓN N.º	FECHA	DESCRIPCIÓN	REVISÓ	APROBÓ	APROBACIÓN CLIENTE
VDD	15/10/2023	Emitido para revisión y comentarios del cliente e Interventoría - Incluye comentarios / modificado donde se indica en el control de cambios	Y.B.	Z.Y.	
VCC	15/06/2023	Emitido para revisión y comentarios del cliente e Interventoría - Incluye comentarios / modificado donde se indica en el control de cambios	Y.B.	Z.Y.	
VBB	11/10/2022	Emitido para revisión y comentarios del cliente e Interventoría	Y.B.	Z.Y.	
VA0	25/09/2022	Emitido para comentarios internos - Emisión preliminar para comentarios	Y.B.	Z.Y.	

METRO LÍNEA 1

METRO LÍNEA 1
CONTRATO DE CONCESIÓN N.º 163 DE 2019

PROYECTO PRIMERA LÍNEA DEL METRO DE BOGOTÁ - TRAMO 1

DIRECTOR INTERVENTORÍA:
JAVIER DESCARGA N.
Mat.: 25202-68697 CND

ESPECIALISTA INTERVENTORÍA:
Mat.:

FECHA: OCTUBRE 2023

SISTEMAS Y EQUIPOS

TELECOMUNICACIONES

ESTACIÓN CARRERA 50 - DISEÑO DETALLADO DEL NIVEL DE PLATAFORMA
SISTEMA CCTV
DISPOSICIÓN GENERAL

PLANCHA N.º L1T1-5445-308-CON-ED-INS-PL-0009_07_VDD
ARCHIVO: L1T1-5445-308-CON-ED-INS-PL-0009_VDD.dwg
ESCALA: 1:100
FECHA: SEPTIEMBRE 2022
REVISIÓN N.º VDD
HOJA N.º 7 DE 8

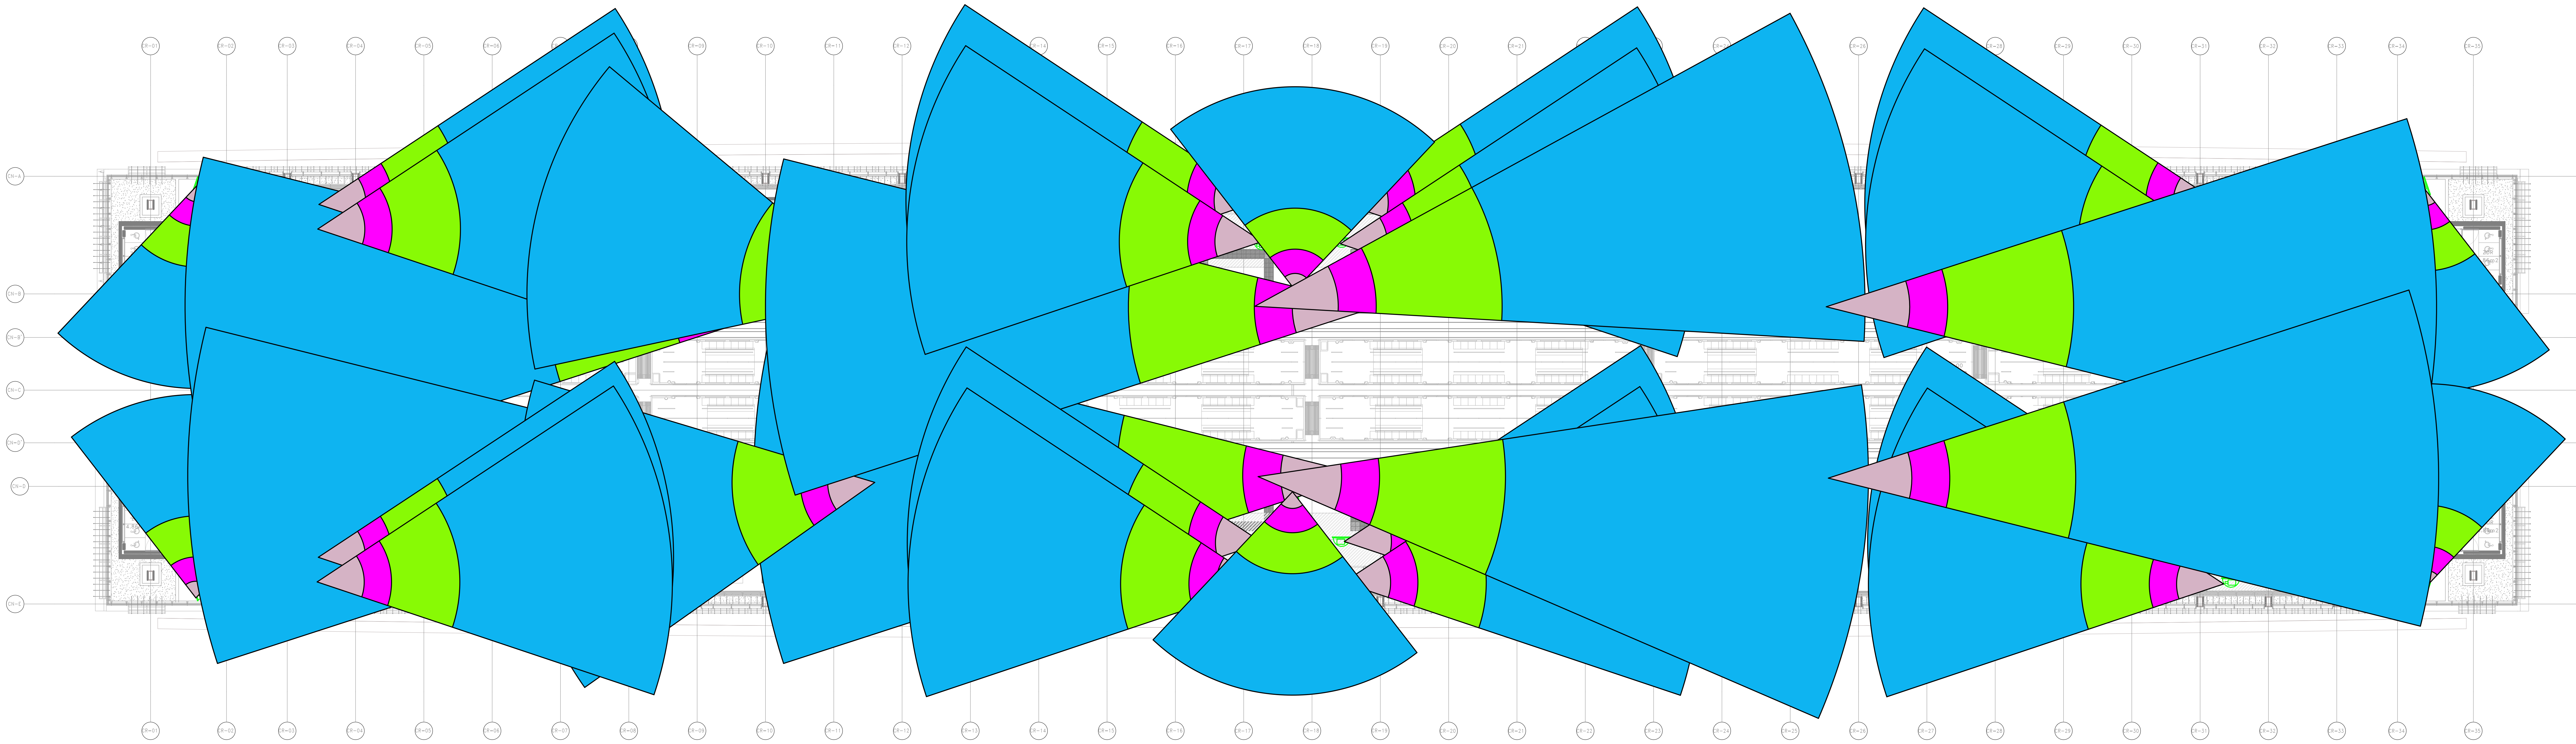

KEY PLAN

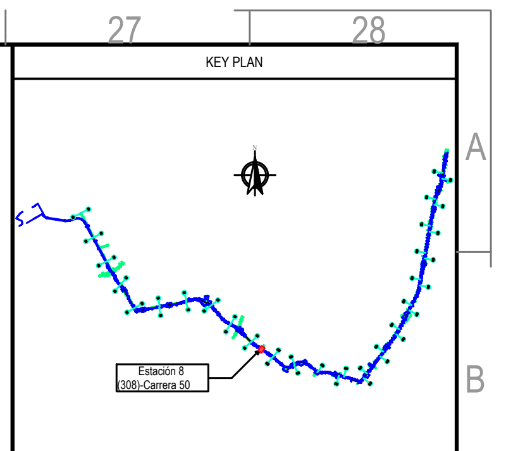

NOTAS

1.Este plano debe revisarse junto con el informe de diseño de L1T1-5445-000-CON-ED-INS-IN-0001 y L1T1-5420-308-CON-ED-INS-PL-0001.
2.Para el listado de equipo, consulte L1T1-5445-000-CON-ED-INS-CO-0001.
3.Para el listado del cable Ethernet (incluyendo el Ethernet para los puertos de contacto seco conectados a los intercomunicadores), se incluye en los planos de los enlaces de acceso de RMS.
4.Para el listado de cables conectados a la detección de intrusos, se incluye en los planos del ACS.
5.La información de las bandejas de cables y tuberías se refiere a los planos de CNL.
6. Los criterios de denominación de las cámaras son los siguientes:
   Nivel - tipo de cámara - código de la cámara.
    Definición de nivel:
      B: como nivel del sótano;
      A: como nivel de acceso;
      I: como nivel intermedio;
      P: como nivel de plataforma.
    Definición del tipo de cámara:
      D: como cámara domo;
      F: como cámara fija;
      P: como cámara PTZ.
E.G: B-F-1 es una cámara fija con código 1 en el nivel del sótano.

CONVENCIONES

DESCRIPCIÓN DE LOS ICONOS

📷	Cámara de domo
📷	Cámara fija (tipo inteligente)
◉	Cámara PTZ
PAM	Monitor de vigilancia de pasajeros
DEC	Decodificador de vídeo
Intercomunicador	Intercomunicador

N.º	PLANOS DE REFERENCIA	REV.
1	L1T1-5420-308-CON-ED-INS-PL-0001	VCC

N.º	MODELO BIM DE REFERENCIA	REV.
1	L1T1-0000-308-CON-ED-ARQ-MO-0001.RVT (BL 2023-03-03)	VCC

N.º	PAQUETE DE TRABAJO DE REFERENCIA	REV.

METRO BOGOTÁ
GCS Consorcio Consultores PMO Bogotá
CONSORCIO SUPERVISOR PLMB
wsp Líder de Diseño Interfaz y Gerencia de Integración

DISEÑÓ: WANG KEJIA Mat.: R2022011515	APROBÓ: ZHANG YUJIE Mat.: NÚMERO DE MATRÍCULA	ING_TÉCNICO_WSP Mat.: NÚMERO DE MATRÍCULA
REVISÓ: YANG BAODONG Mat.:	MODELÓ/DIBUJÓ: WANG KEJIA Mat.:R2022011515	APRO_INTEGRACIÓN_WSP Mat.: NÚMERO DE MATRÍCULA *"Aprobada bajo el marco de los límites y condiciones establecido en la tercera sección del parágrafo del apéndice 1 sección 1 del acuerdo del contrato de diseño"

REVISIÓN N.º	FECHA	DESCRIPCIÓN	REVISÓ	APROBÓ	APROBACIÓN CLIENTE
VDD	15/10/2023	Emitido para revisión y comentarios del cliente e Interventoría - Incluye comentarios / modificado donde se indica en el control de cambios	Y.B.	Z.Y.	

METRO LÍNEA 1

METRO LÍNEA 1
CONTRATO DE CONCESIÓN N.º 163 DE 2019

PROYECTO PRIMERA LÍNEA DEL METRO DE BOGOTÁ - TRAMO 1

DIRECTOR INTERVENTORÍA:
JAVIER DESCARGA N.
Mat.: 25202-68697 CND

ESPECIALISTA INTERVENTORÍA:
Mat.:

FECHA: OCTUBRE 2023

SISTEMAS Y EQUIPOS
TELECOMUNICACIONES
ESTACIÓN CARRERA 50 - DISEÑO DETALLADO DEL NIVEL DE PLATAFORMA
SISTEMA CCTV
COBERTURA

PLANCHA N.º L1T1-5445-308-CON-ED-INS-PL-0009_08_VDD
ARCHIVO: L1T1-5445-308-CON-ED-INS-PL-0009_VDD.dwg
ESCALA: 1:100
FECHA: OCTUBRE 2023
REVISIÓN N.º VDD
HOJA N.º 8 DE 8