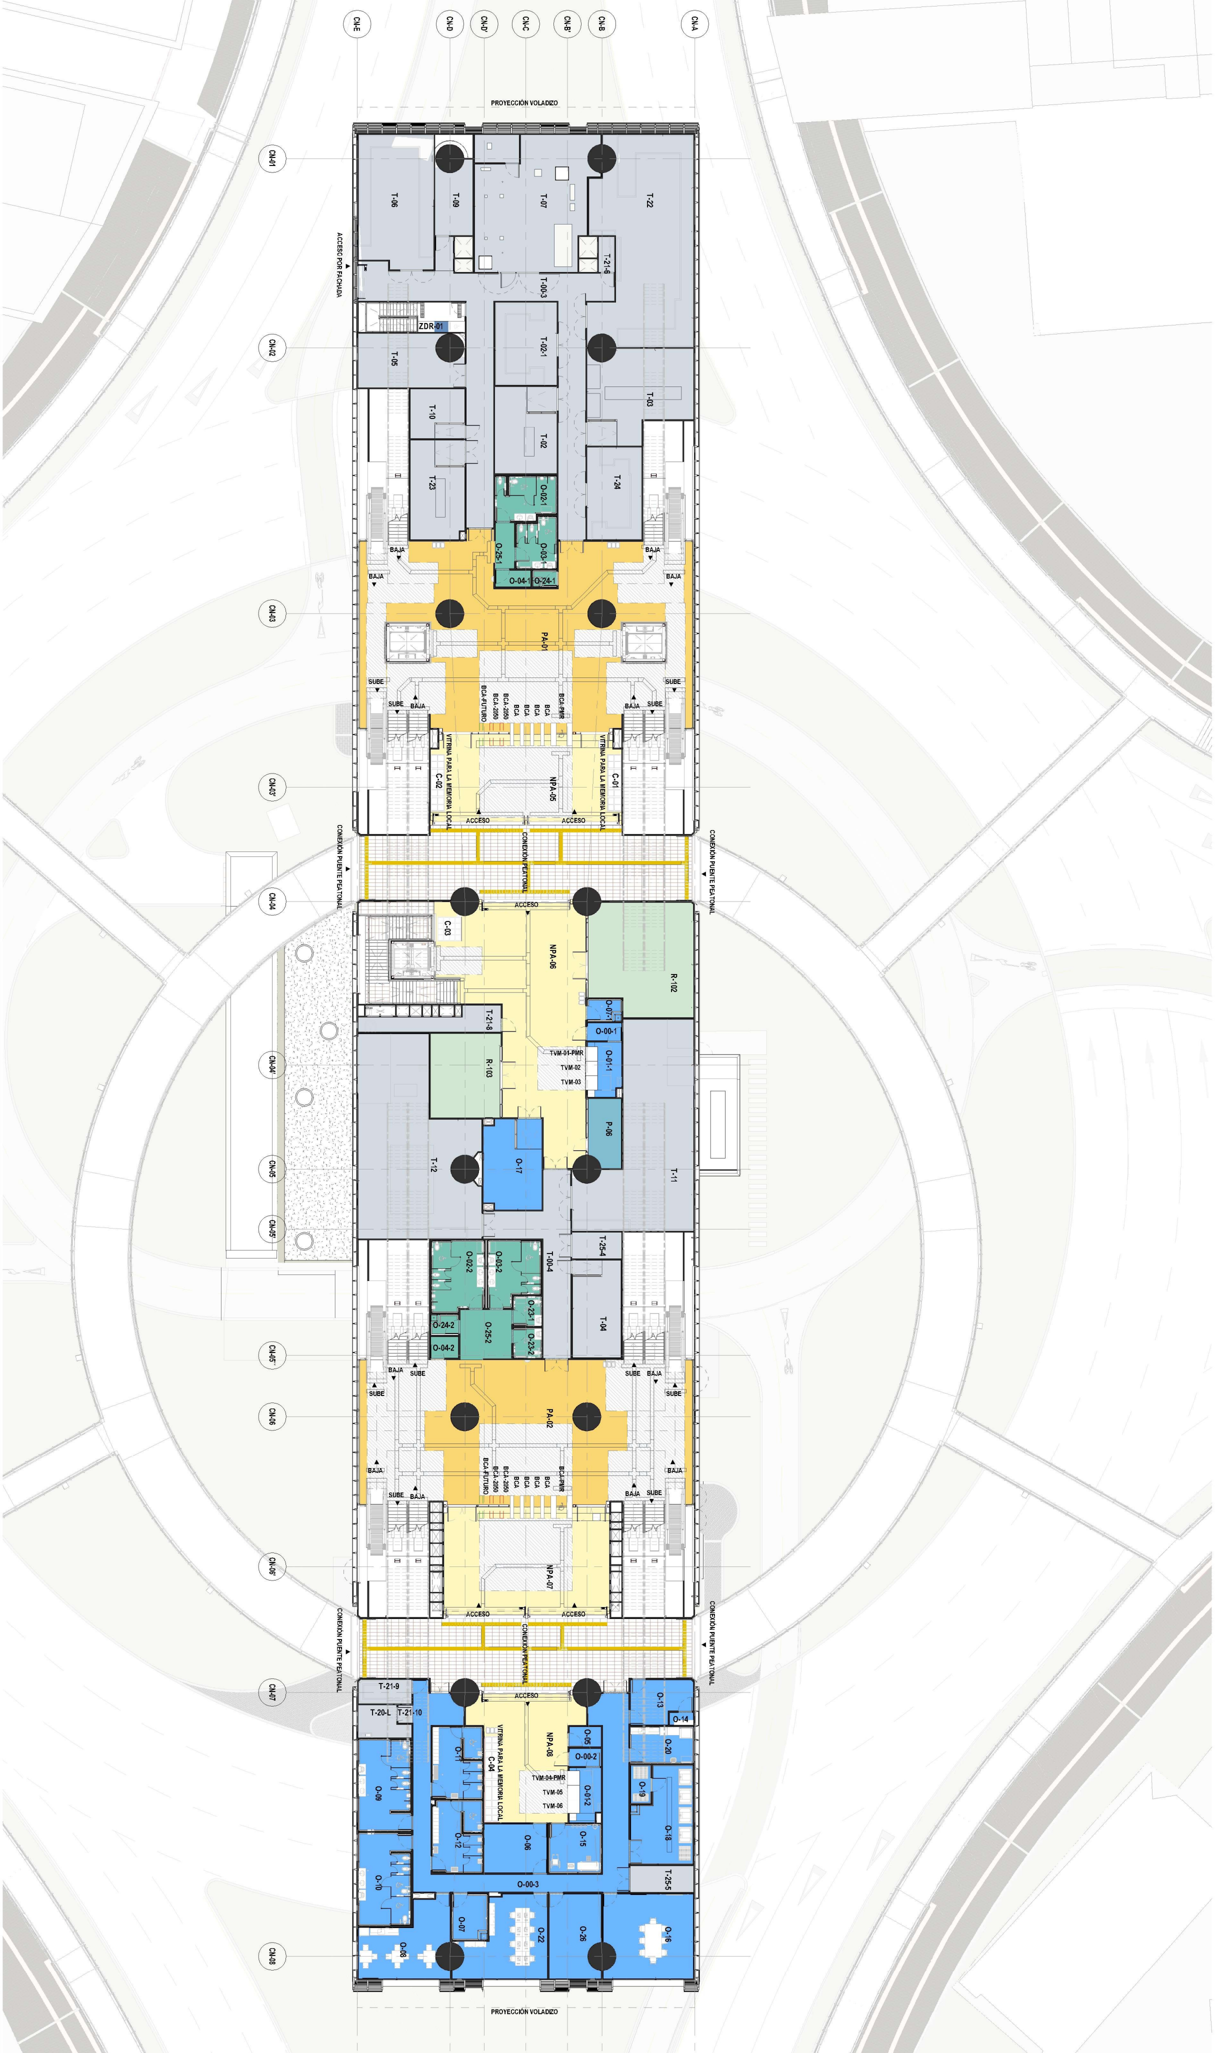
CN-E
CN-D
CN-D'
CN-C
CN-B'
CN-B
CN-A
PROYECCIÓN VOLADIZO
CN-01
CN-02
CN-03
CN-03'
CN-04
CN-04'
CN-05
CN-05'
CN-05''
CN-06
CN-06'
CN-07
CN-08
ACCESO POR FACHADA
T-06
T-09
T-07
T-22
T-21-6
T-00-3
ZDR-01
T-05
T-02-1
T-03
T-10
T-02
T-23
T-24
O-02-1
O-25-1
O-03-1
O-04-1
O-24-1
BAJA
SUBE
PA-01
BCA-FUTURO
BCA-2050
BCA-2050
BCA
BCA
BCA
BCA
BCA-PMR
VITRINA PARA LA MEMORIA LOCAL
C-02
C-01
NPA-05
ACCESO
CONEXIÓN PUENTE PEATONAL
CONEXIÓN PEATONAL
C-03
NPA-06
R-102
O-07-1
O-00-1
T-21-8
R-103
TVM-01-PMR
TVM-02
TVM-03
O-01-1
P-06
O-17
T-12
T-11
T-25-4
O-02-2
O-03-2
T-00-4
O-23-1
O-24-2
O-25-2
O-23-2
O-04-2
T-04
PA-02
NPA-07
T-21-9
T-20-L
T-21-10
O-13
O-14
O-05
O-00-2
O-20
O-11
C-04
NPA-08
TVM-04-PMR
TVM-05
TVM-06
O-01-2
O-19
O-09
O-12
O-06
O-15
O-18
O-10
O-00-3
T-25-5
O-07
O-22
O-26
O-16
O-08