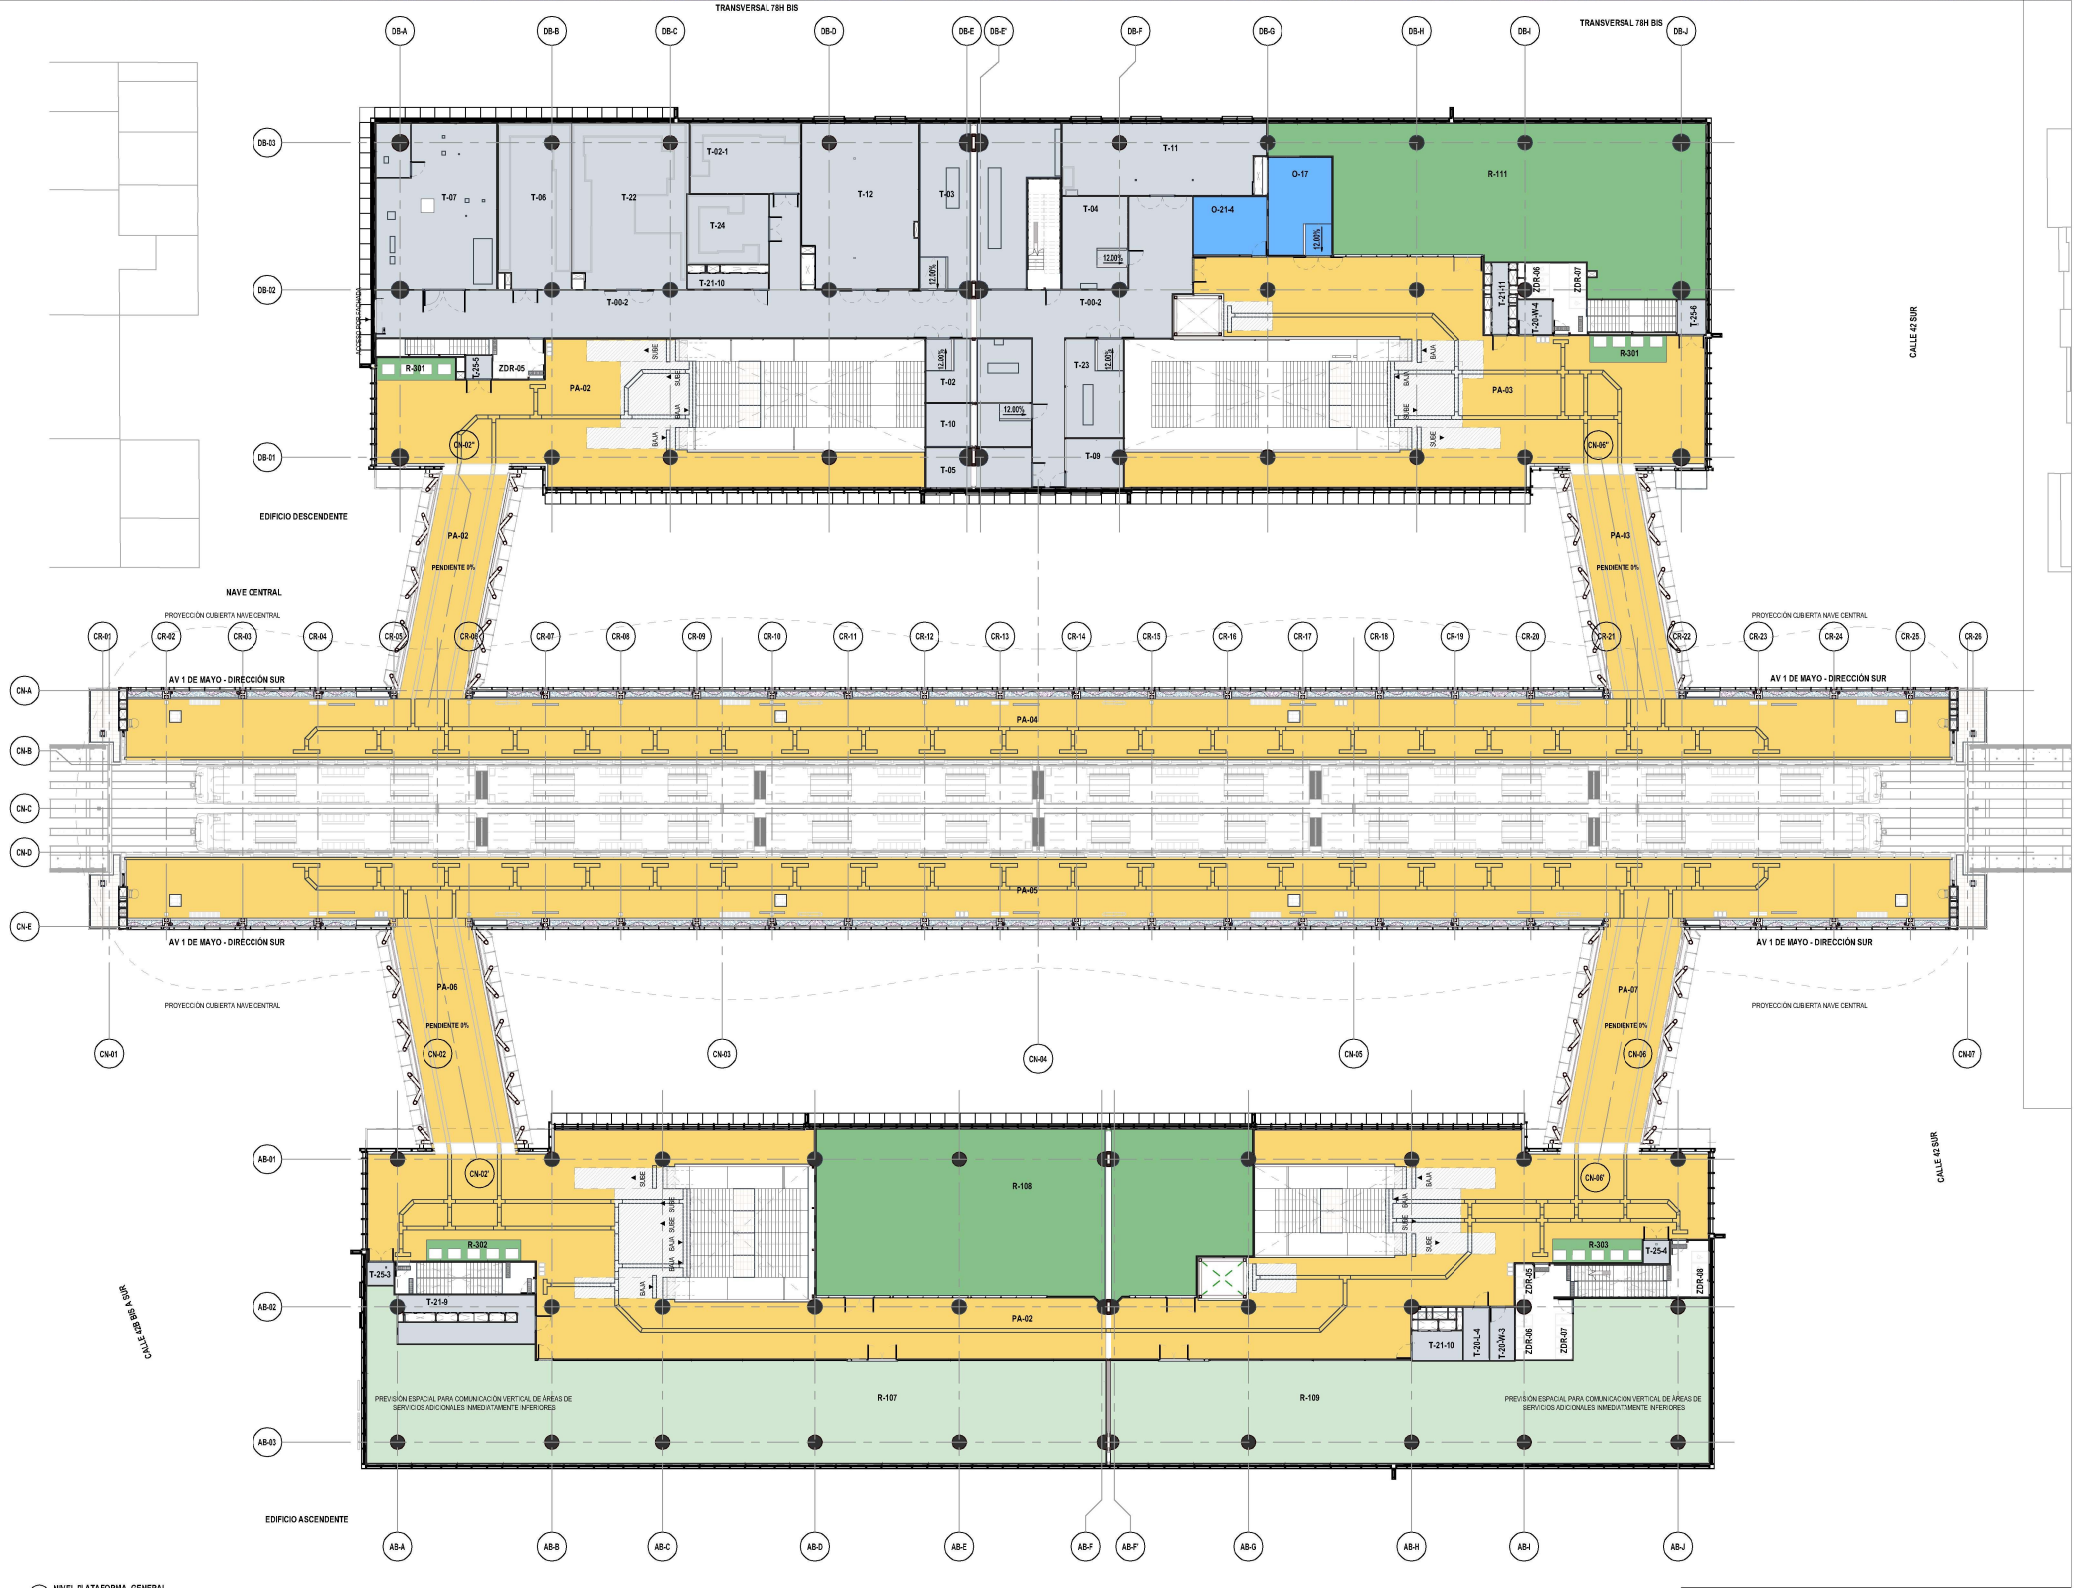

TRANSVERSAL 78H BIS
TRANSVERSAL 78H BIS
DB-A
DB-B
DB-C
DB-D
DB-E
DB-F'
DB-F
DB-G
DB-H
DB-I
DB-J
DB-03
DB-02
DB-01
T-07
T-06
T-22
T-02-1
T-24
T-12
T-03
T-11
T-04
O-17
O-21-4
R-111
T-00-2
T-21-10
T-02
T-10
T-05
T-23
T-09
R-301
T-25-5
ZDR-05
PA-02
PA-03
T-21-11
T-20-W-4
ZDR-06
ZDR-07
T-25-6
CALLE 42 SUR
EDIFICIO DESCENDENTE
NAVE CENTRAL
PROYECCIÓN CUBIERTA NAVE CENTRAL
PENDIENTE 9%
CR-01
CR-02
CR-03
CR-04
CR-05
CR-06
CR-07
CR-08
CR-09
CR-10
CR-11
CR-12
CR-13
CR-14
CR-15
CR-16
CR-17
CR-18
CR-19
CR-20
CR-21
CR-22
CR-23
CR-24
CR-25
CR-26
AV 1 DE MAYO - DIRECCIÓN SUR
CN-A
CN-B
CN-C
CN-D
CN-E
PA-04
PA-05
PA-06
PA-07
CN-01
CN-02
CN-03
CN-04
CN-05
CN-06
CN-07
AB-01
AB-02
AB-03
R-108
R-107
R-109
R-302
R-303
T-25-3
T-21-9
T-25-4
T-21-10
T-20-L-4
T-20-W-3
PREVISIÓN ESPACIAL PARA COMUNICACIÓN VERTICAL DE ÁREAS DE SERVICIOS ADICIONALES INMEDIATAMENTE INFERIORES
EDIFICIO ASCENDENTE
AB-A
AB-B
AB-C
AB-D
AB-E
AB-F
AB-F'
AB-G
AB-H
AB-I
AB-J
SUBE
BAJA