Índice

Código de plano	REV.	Nombre del plano
L1T1-5445-305-CON-ED-INS-PL-0009_01	VCC	DISEÑO DETALLADO DEL NIVEL DE SÓTANO (SISTEMA CCTV) - DISPOSICIÓN GENERAL
L1T1-5445-305-CON-ED-INS-PL-0009_02	VCC	DISEÑO DETALLADO DEL NIVEL DE SÓTANO (SISTEMA CCTV) - COBERTURA
L1T1-5445-305-CON-ED-INS-PL-0009_03	VCC	DISEÑO DETALLADO DEL NIVEL DE ACCESO (SISTEMA CCTV) - DISPOSICIÓN GENERAL (PARTE-1)
L1T1-5445-305-CON-ED-INS-PL-0009_04	VCC	DISEÑO DETALLADO DEL NIVEL DE ACCESO (SISTEMA CCTV) - COBERTURA (PARTE-1)
L1T1-5445-305-CON-ED-INS-PL-0009_05	VCC	DISEÑO DETALLADO DEL NIVEL DE ACCESO (SISTEMA CCTV) - DISPOSICIÓN GENERAL (PARTE-2)
L1T1-5445-305-CON-ED-INS-PL-0009_06	VCC	DISEÑO DETALLADO DEL NIVEL DE ACCESO (SISTEMA CCTV) - COBERTURA (PARTE-2)
L1T1-5445-305-CON-ED-INS-PL-0009_07	VCC	DISEÑO DETALLADO DEL NIVEL INTERMEDIO (SISTEMA CCTV) - DISPOSICIÓN GENERAL (PARTE-1)
L1T1-5445-305-CON-ED-INS-PL-0009_08	VCC	DISEÑO DETALLADO DEL NIVEL INTERMEDIO (SISTEMA CCTV) - COBERTURA (PARTE-1)
L1T1-5445-305-CON-ED-INS-PL-0009_09	VCC	DISEÑO DETALLADO DEL NIVEL INTERMEDIO (SISTEMA CCTV) - DISPOSICIÓN GENERAL (PARTE-2)
L1T1-5445-305-CON-ED-INS-PL-0009_10	VCC	DISEÑO DETALLADO DEL NIVEL INTERMEDIO (SISTEMA CCTV) - COBERTURA (PARTE-2)
L1T1-5445-305-CON-ED-INS-PL-0009_11	VCC	DISEÑO DETALLADO DEL NIVEL DE PLATAFORMA (SISTEMA CCTV) - DISPOSICIÓN GENERAL (PARTE-1)
L1T1-5445-305-CON-ED-INS-PL-0009_12	VCC	DISEÑO DETALLADO DEL NIVEL DE PLATAFORMA (SISTEMA CCTV) - COBERTURA (PARTE-1)
L1T1-5445-305-CON-ED-INS-PL-0009_13	VCC	DISEÑO DETALLADO DEL NIVEL DE PLATAFORMA (SISTEMA CCTV) - DISPOSICIÓN GENERAL (PARTE-2)
L1T1-5445-305-CON-ED-INS-PL-0009_14	VCC	DISEÑO DETALLADO DEL NIVEL DE PLATAFORMA (SISTEMA CCTV) - COBERTURA (PARTE-2)

KEY PLAN

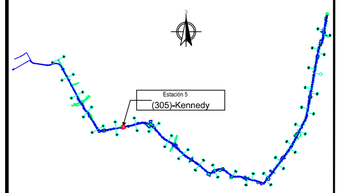

NOTAS

CONVENCIONES

No.	PLANOS DE REFERENCIA	REV.

No.	MODELO BIM DE REFERENCIA	REV.

No.	PAQUETE DE TRABAJO DE REFERENCIA	REV.

METRO BOGOTÁ | GCS Consorcio Consultores PMO Bogotá | CONSORCIO SUPERVISOR PLMB | wsp Líder de Diseño Interfaz y Gerencia de Integración

DISEÑÓ:	REVISÓ:	APROBÓ:
WANG KEJIA Mat.: R2022011515	YANG BAODONG Mat.:	ZHANG YUJIE Mat.:

ING_TÉCNICO_WSP	* APRO_INTEGRACIÓN_WSP
Mat.: NÚMERO DE MATRÍCULA	Mat.: NÚMERO DE MATRÍCULA

REVISIÓN No.	FECHA	DESCRIPCIÓN	REVISÓ	APROBÓ	APROBACIÓN CLIENTE
VCC	05/06/2023	Emitido para revisión y comentarios del cliente e Interventoría - Incluye comentarios / modificado donde se indica en el control de cambios	Y.B.	Z.Y.	
VA1	30/05/2023	Emitido para comentarios internos - Emisión preliminar para comentarios	Y.B.	Z.Y.	
VBB	11/10/2022	Emitido para revisión y comentarios del cliente e Interventoría	Y.B.	Z.Y.	
VA0	30/09/2022	Emitido para comentarios internos - Emisión preliminar para comentarios	Y.B.	Z.Y.	

METRO LÍNEA 1

METRO LÍNEA 1
CONTRATO DE CONCESIÓN N.° 163 DE 2019

PROYECTO PRIMERA LÍNEA DEL METRO DE BOGOTÁ - TRAMO 1

SISTEMAS Y EQUIPOS

TELECOMUNICACIONES

ESTACIÓN KENNEDY - DISEÑO DETALLADO
SISTEMA CCTV
TABLA DE CONTENIDO

DIRECTOR INTERVENTORÍA:	ESPECIALISTA INTERVENTORÍA:
J. DESCARGA N. Mat.: 25202-68697 CND	Mat.:

PLANCHA No.	ESCALA:	REVISIÓN No	HOJA No.
L1T1-5445-305-CON-ED-INS-PL-0009_00_VCC	GRÁFICO	VCC	0 DE 14
ARCHIVO: L1T1-5445-305-CON-ED-INS-PL-0009_VCC.dwg	FECHA: SEPTIEMBRE 2022		

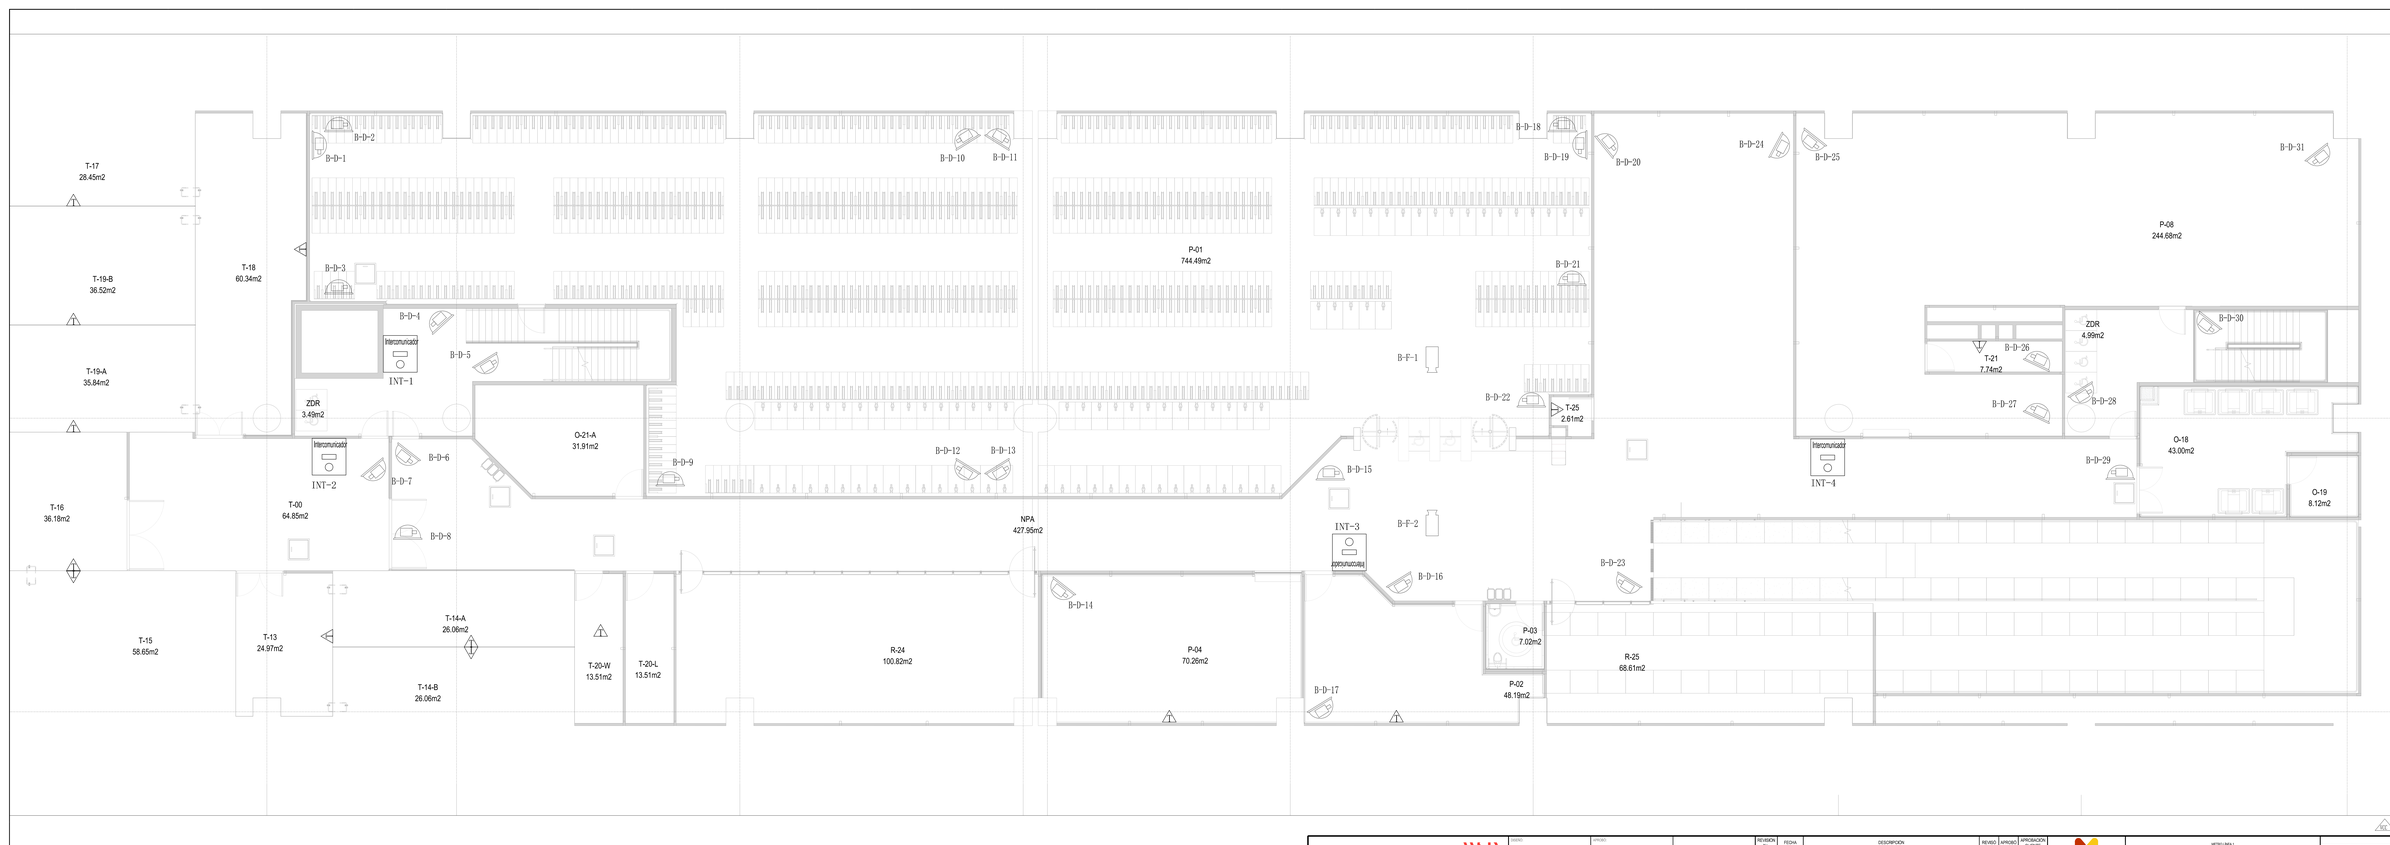

KEY PLAN

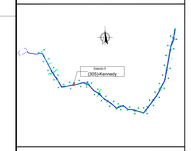

NOTAS

1.Este plano debe revisarse junto con el informe de diseño de LTT-SAAS-003-CON-ED-INS-DI-0001 y LTT-SAAS-003-CON-ED-INS-DI-0002.
2.Para efectos de equipo, consultar LTT-SAAS-003-CON-ED-INS-ES-0001.
3.Para efectos del cable Ethernet (indicando el Ethernet para los puntos de cámara sea conectados a los switches ubicados en los cuartos de telecomunicaciones), consultar el plano LTT-SAAS-003-CON-ED-INS-DI-0002.
4.Para efectos de cables conectados a la detección de intrusos, se incluye en los planos de MCS.
5.La información de las tarrojas de cables y tuberías se refiere a los planos de CIAL.
6. Los criterios de determinación de las cámaras son los siguientes.
Nivel - tipo de cámara - código de la cámara.
Definición del nivel:
B: cuarto nivel del sótano.
A: cuarto nivel de acceso.
P: primer nivel elevado.
T: cuarto nivel de plataforma.
Definición del tipo de cámara:
D: cúpula cámara domo.
F: cuerpo cámara fija.
Z: cuerpo cámara PTZ.
E.G.: B-F-1: es una cámara fija con código 1 en el nivel del sótano.

CONVENCIONES

DESCRIPCIÓN DE LOS ICONOS

	Cámara de domo
	Cámara fija (tipo inteligente)
	Cámara PTZ
PAM	Monitor de vigilancia de pasajeros
DEC	Decodificador de video
	Intercomunicador

No.	PLANOS DE REFERENCIA	REV.

No.	MODELO BIM DE REFERENCIA	REV.
1	LTT-SAAS-003-CON-ED-ARQ-M3-0001.RVT (BL 2023-R1-03)	V00

No.	PAQUETE DE TRABAJO DE REFERENCIA	REV.

REVISIÓN No.	FECHA	DESCRIPCIÓN	REVISÓ	APROBÓ	APROBACIÓN CLIENTE
VCC	09/09/2022	Emitido para revisión y comentarios del diseño a Intervensistra - Incluye comentarios / modificado dentro de indice en el control de cambios	T.B.	Z.Y.	
AAY	30/05/2022	Emitido para comentarios internos - Emisión preliminar para comentarios	T.B.	Z.Y.	
VBB	11/10/2022	Emitido para revisión y comentarios del diseño a Intervensistra	T.B.	Z.Y.	
VAC	30/09/2022	Emitido para comentarios internos - Emisión preliminar para comentarios	T.B.	Z.Y.	

DISEÑO	WANG KEJIA Mat.: R2022011915	
REVISÓ	YANG BAODONG Mat.:	
APROBÓ	ZHANG YIJIE Mat.: NÚMERO DE MATRÍCULA	
MODELO/BIM	WANG KEJIA Mat.: R2022011915	
ING_TÉCNICO_WSP Mat.: NÚMERO DE MATRÍCULA		
APRO_INTEGRACIÓN_WSP Mat.: NÚMERO DE MATRÍCULA "Declaro que he revisado el plano y/o documento con el fin de verificar la coherencia técnica y el cumplimiento de los requisitos establecidos en el marco del objeto de la consultoría" Firma:		

METRO LÍNEA 1
CONTRATO DE CONCESIÓN No.1 "GL" DE 2019
PROYECTO PRIMERA LÍNEA DEL METRO DE BOGOTÁ - TRAMO 1

DIRECTOR DE LA CONCESIÓN JAVIER ESCUDERO A. Mat.: 25202-69897 CND	SUPERVISIÓN INTERVENTORÍA Mat.:

TELECOMUNICACIONES
ESTACIÓN KENNEDY - DISEÑO DETALLADO DEL NIVEL SÓTANO
SISTEMA CCTV
DISPOSICIÓN GENERAL

FECHA JUNIO 2023	ESCALA 1:100	TAMAÑO ISO A1	HOJA 1 DE 14
NOMBRE DEL ARCHIVO LTT-SAAS-305-CON-ED-INS-PL-0009_01_VCC.dwg	REVISIÓN VCC		
FECHA DE IMPRESIÓN SEPTIEMBRE 2022			

SISTEMAS Y EQUIPOS

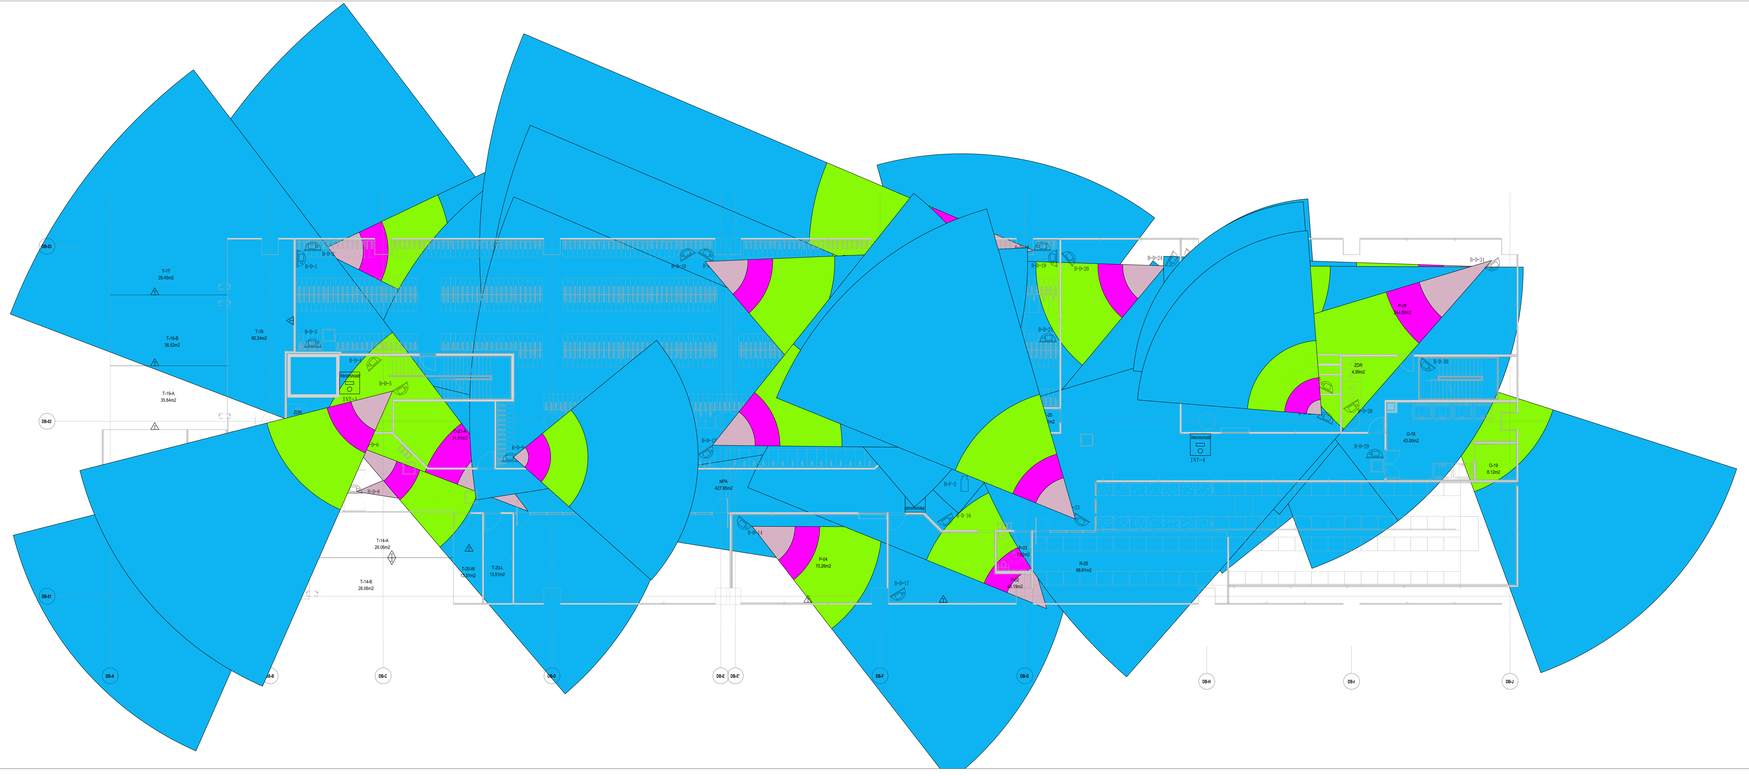

KEY PLAN

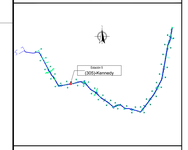

NOTAS

1.Este plano debe revisarse junto con el informe de diseño de LT17-5445-003-CON-ED-IND-RI-0001 y los planos de detalle de cámaras.
2.Para efectuar de equipo, consulte LT17-5445-003-CON-ED-ING-ZZ-0001.
3.Para efectuar del cable Ethernet (indicando el Ethernet para los puntos de cámara seco conectados a los gabinetes de cámaras), consulte el diagrama de conexión LT17-5445-003-CON-ED-ING-ZZ-0001.
4.Para efectuar los cables conectados a la detección de intrusos, se incluye en los planos del sistema de CNL.
5.La información de las bandejas de cables y tuberías se refiere a los planos de CNL.
6. Los criterios de codificación de las cámaras son los siguientes:
Nivel - tipo de cámara - código de la cámara.
Nivel de la cámara:
S: como nivel del sótano.
A: como nivel de acceso.
M: como nivel de mezzanine.
P: como nivel de plataforma.
Definición del tipo de cámara:
D: como cámara domo.
F: como cámara fija.
B: como cámara PTZ.
E.G. B-P-1: es una cámara fija con código 1 en el nivel del sótano.

CONVENCIONES

DESCRIPCIÓN DE LOS ICONOS

	Cámara de domo
	Cámara fija (tipo inteligente)
PTZ	Cámara PTZ
PAM	Monitor de vigilancia de pasajeros
DEC	Decodificador de vídeo
	Intercomunicador

No.	PLANOS DE REFERENCIA	REV.

No.	MODELO BIM DE REFERENCIA	REV.
1	LT17-5445-003-CON-ED-ARQ-MOD-RAT (R_2023-03-02)	V00

No.	PAQUETE DE TRABAJO DE REFERENCIA	REV.

DISEÑO: WANG KEJIA Mat.: R2022011915	APROBO: ZHANG YIJIE Mat.: NÚMERO DE MATRÍCULA	ING_TÉCNICO_WSP Mat.: NÚMERO DE MATRÍCULA	REVISIÓN No.	FECHA	DESCRIPCIÓN	REVISO	APROBÓ	APROBACIÓN CLIENTE
REVISO: YANG BAODONG Mat.:	MODELO BIM: WANG KEJIA Mat.: R2022011915	APRO_INTEGRACIÓN_WSP Mat.: NÚMERO DE MATRÍCULA *Cambiar de la letra A de Mat.a a Letra que corresponda a la disciplina (A=Arq, E=Elec, M=Mec, S=Estr, H=Hid) Y de acuerdo del cliente.	VCC	05/09/2023	Emitido para revisión y comentarios del diseño e interventoría. Incluye comentarios / modificado donde se indica en el control de cambios	T.B.	Z.Y.	
			VAY	30/05/2023	Emitido para comentarios internos. Emisión preliminar para comentarios	T.B.	Z.Y.	
			VBB	11/10/2022	Emitido para revisión y comentarios del diseño e Interventoría.	T.B.	Z.Y.	
			VAE	30/09/2022	Emitido para comentarios internos- Emisión preliminar para comentarios	T.B.	Z.Y.	

METRO LÍNEA 1

METRO LÍNEA 1
CONTRATO DE CONCESIÓN N.° 163 DE 2019

TELECOMUNICACIONES

PROYECTO PRIMERA LÍNEA DEL METRO DE BOGOTÁ - TRAMO 1

CONTRATISTA: JAVEN DESCANGA SL
Mat.: 2520-03-69807 CND

SUPERVISIÓN INTERVENTORÍA: Mat.:

ESCALA: 1:100

FECHA: JUNIO 2023

SISTEMAS Y EQUIPOS

TELECOMUNICACIONES

ESTACIÓN HOWIZH - DISEÑO DETALLADO DEL NIVEL SOTANO

SISTEMA CCTV

CUBIERTAN

CONTRATO No.	LT17-5445-305-CON-ED-ING-PL-0009_02_VCC		
DESCRIPCIÓN	LT17-5445-305-CON-ED-IND-PL-0009_VCC.dwg	REVISIÓN: VCC	HOJA: 2 DE 14
		EMISIÓN: SEPTIEMBRE 2022	

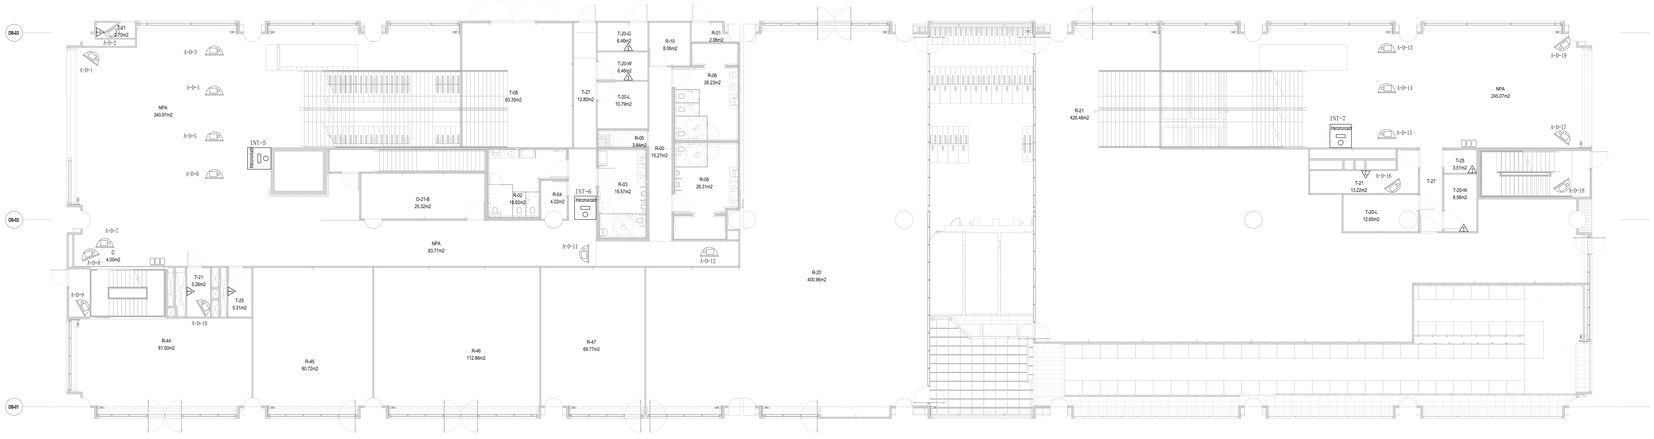

KEY PLAN

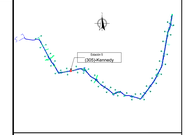

NOTAS

1.Este plano debe revisarse junto con el informe de diseño de LT1-GAAS-003-CON-ED-IND-RI-0001 y con el plano LT1-GAAS-003-CON-ED-IND-PL-0001.
2.Para efectos de equipo, consultar LT1-GAAS-003-CON-ED-IND-CO-0001.
3.Para efectos del cable Ethernet (indicando el Ethernet para los puntos de cámara seco conectados a los gabinetes de telecomunicaciones), consultar el plano LT1-GAAS-003-CON-ED-IND-PL-0002.
4.Para efectos de cables conectados a la detección de intrusos, se incluye en los planos del ACS.
5.La información de las bandejas de cables y tuberías se refiere a los planos de CNL.
6. Los criterios de determinación de las cámaras son los siguientes.
Nivel - tipo de cámara - código de la cámara.
Definición del nivel:
0 - cuarto cero/-nivel sótano.
1 - cuarto nivel de acceso.
2 - cuarto nivel mezzanine.
3 - cuarto nivel de plataforma.
Definición del tipo de cámara:
D - cámara domo tipo.
F - cámara cámara fija.
P - cámara cámara PTZ.
P.D.D. - B.P.A. es una cámara fija con código 1 en el nivel del sótano.

CONVENCIONES

DESCRIPCIÓN DE LOS ICONOS

	Cámara de domo
	Cámara fija (tipo inteligente)
	Cámara PTZ
PAM	Monitor de vigilancia de pasajeros
DEC	Decodificador de vídeo
	Intercomunicador

No.	PLANOS DE REFERENCIA	REV.

No.	MODELO BIM DE REFERENCIA	REV.
1	LT1-GAAS-003-CON-ED-ARQ-M3D-XNT (R_2023-01-02)	V00

No.	PAQUETE DE TRABAJO DE REFERENCIA	REV.

METRO BOGOTÁ	GCS Construcciones Civiles PAC Brasil	CONSORCIO SUPERVISOR PLMB	wsp Líder de Diseño Ambiental Gerencia de Proyectos	DISEÑO: WANG XEJIA Mat.: R2022011915	APROBÓ: ZHANG YUJIE Mat.: NÚMERO DE MATRÍCULA	ING_TÉCNICO_WSP Mat.: NÚMERO DE MATRÍCULA	REVISIÓN No.	FECHA	DESCRIPCIÓN	REVISÓ	APROBÓ	APROBACIÓN CLIENTE
				REVISÓ: YANG BAODONG Mat.:	MODELO/DIBUJO: WANG XEJIA Mat: R2022011915	APRO_INTEGRACIÓN_WSP Mat.: NÚMERO DE MATRÍCULA *Cumplen con lo dicho en los términos y condiciones establecidos en el contrato vigente y en el Art.7° de Ley 1581 de 2012	1.0	09/06/2023	Emitido para revisión y comentarios del diseño a Interventoría / Incluye comentarios / modificado diseño de indice en el control de sentido	T.B.	Z.Y.	
							VA1	30/05/2023	Emitido para comentarios internos - Emisión preliminar para comentarios	T.B.	Z.Y.	
							V00	11/10/2022	Emitido para revisión y comentarios del diseño a Interventoría	T.B.	Z.Y.	
							V00	09/09/2022	Emitido para comentarios internos - Emisión preliminar para comentarios	T.B.	Z.Y.	

METRO LÍNEA 1

METRO LÍNEA 1
CONTRATO DE CONCESIÓN N.° 163 DE 2019

TELECOMUNICACIONES

PROYECTO PRIMERA LÍNEA DEL METRO DE BOGOTÁ - TRAMO 1

CONTRATISTA: JAVIER DESCANSA N. Mat.: 2520245897 CND

SUPERVISIÓN INTERVENTORÍA: Mat.:

ESCALA: 1:100

FECHA: JUNIO 2023

SISTEMAS Y EQUIPOS

ESTACIÓN KENNEDY - DISEÑO DETALLADO DEL NIVEL DE ACCESO (PARTE 1)

SISTEMA CCTV

EMPOTRACIÓN GENERAL

CÓDIGO DE PLANO: LT1-GAAS-305-CON-ED-IND-PL-0009_03_VCC

NOMBRE DE ARCHIVO: LT1-GAAS-305-CON-ED-IND-PL-0009_VCC.dwg

ESCALA: 1:100

FECHA DE IMPRESIÓN: SEPTIEMBRE 2022

REVISIÓN: VCC

HOJA: 3 DE 14

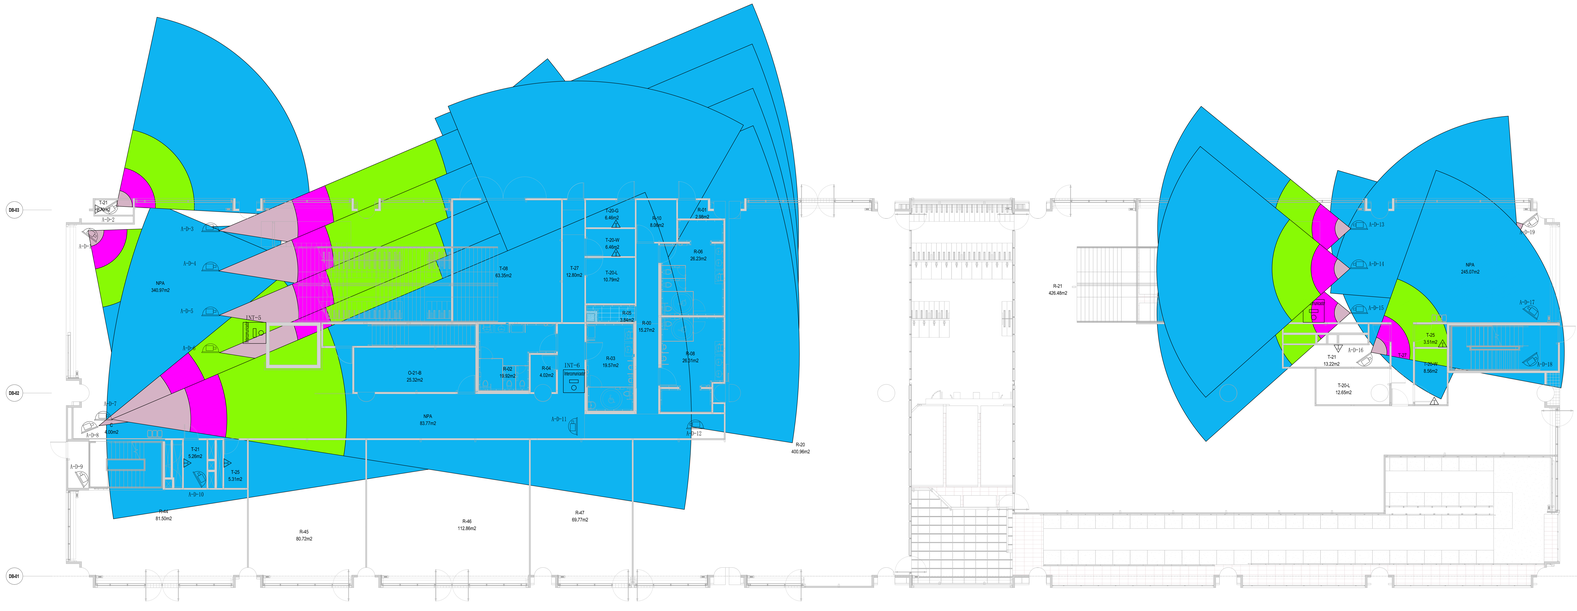

KEY PLAN

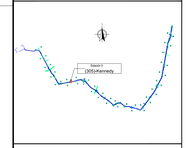

NOTAS

1.Este plano debe revisarse junto con el sistema de diseño de LTT-1-5445-000-CON-ED-IND-PL-0001 y LTT-1-5445-000-CON-ED-IND-PL-0002.
2.Para efectos de equipo, consultar LTT-1-5445-000-CON-ED-ING-CO-0001.
3.Para efectos del cable Ethernet (indicando el Ethernet para los puntos de cámara seco conectados a los gabinetes de telecomunicaciones), consultar el plano LTT-1-5445-000-CON-ED-ING-CO-0001.
4.Para efectos de cables conectados a la detección de intrusos, se incluye en los planos de red ACS.
5.La información de las bandejas de cables y tuberías se refiere a los planos de CIVIL.
6. Los criterios de codificación de las cámaras son los siguientes:
Nivel - tipo de cámara - código de la cámara.
Nivel: 01 - nivel 1
02 - cenro nivel del edificio
Ej. cenro nivel de acceso.
Tipo de cámara: 3 caracteres.
P - cenro nivel de plataforma
Definición del tipo de cámara:
D - cenro cámara domo
F - cenro cámara fija
PTZ - cenro cámara PTZ
Ej.D - 01 P - es una cenro fija con código 1 en el nivel del edificio.

CONVENCIONES

DESCRIPCIÓN DE LOS ICONOS

DOME	Cámara de domo
	Cámara fija (tipo inteligente)
PTZ	Cámara PTZ
FAB	Monitor de vigilancia de pasajeros
DEC	Decodificador de vídeo
	Intercomunicador

No.	PLANOS DE REFERENCIA	REV.

No.	MODELO BIM DE REFERENCIA	REV.
-	LTT-1-5000-000-CON-ED-ARQ-MOD-XXX* (R_2023-01-02)	V00

No.	PAQUETE DE TRABAJO DE REFERENCIA	REV.

DISEÑO:	WANG XEJIA Mat.: R2022011915	APROBÓ:	ZHANG YIJIE Mat.: NÚMERO DE MATRÍCULA	ING_TÉCNICO_WSP Mat.: NÚMERO DE MATRÍCULA	REVISIÓN No.	FECHA	DESCRIPCIÓN	REVISÓ	APROBÓ	APROBACIÓN CLIENTE
REVISÓ:	YANG BAODONG Mat.:	MODELO/BIM:	WANG XEJIA Mat.:R2022011915	APRO_INTEGRACIÓN_WSP Mat.: NÚMERO DE MATRÍCULA *Cambiar los 4 dígitos de los números consecutivos de acuerdo con el número de versión (ej. 0001), 1 de agosto de cabeza de	VCC	09/06/2023	Emitido para revisión y comentarios del diseño a tiramentario. Incluye comentarios / modificado donde se indica en el cambio de sentido.	T.B.	Z.Y.	
					VA1	30/05/2023	Emitido para comentarios internos. Emisión preliminar para comentarios	T.B.	Z.Y.	
					VB8	11/10/2022	Emitido para revisión y comentarios del diseño a tiramentario.	T.B.	Z.Y.	
					V00	30/09/2022	Emitido para comentarios internos. Emisión preliminar para comentarios	T.B.	Z.Y.	

METRO LÍNEA 1
CONTRATO DE CONCESIÓN N.° 163 DE 2019

PROYECTO PRIMERA LÍNEA DEL METRO DE BOGOTÁ - TRAMO 1

DIRECTOR DE INTERVENTORÍA:
JAVIER ESCANDA N.
Mat.: 25202-60897 CND

ESPECIALISTA INTERVENTORÍA:
Mat.:

FECHA:
JUNIO 2023

SISTEMAS Y EQUIPOS
TELECOMUNICACIONES
ESTACIÓN KENNEDY - DISEÑO DETALLADO DEL NIVEL SÓTANO
SISTEMA CCTV
CUBIERTAS

CONTRATO No.	ESCALA:	FORMATO:	
LTT-5445-305-CON-ED-IND-PL-0009_04_VCC	1:100	ISO A1	
NOMBRE DEL ARCHIVO:	FECHA:	REVISIÓN:	HOJA:
LTT-5445-305-CON-ED-IND-PL-0009_VCC.dwg	SEPTIEMBRE 2022	VCC	4 DE 14

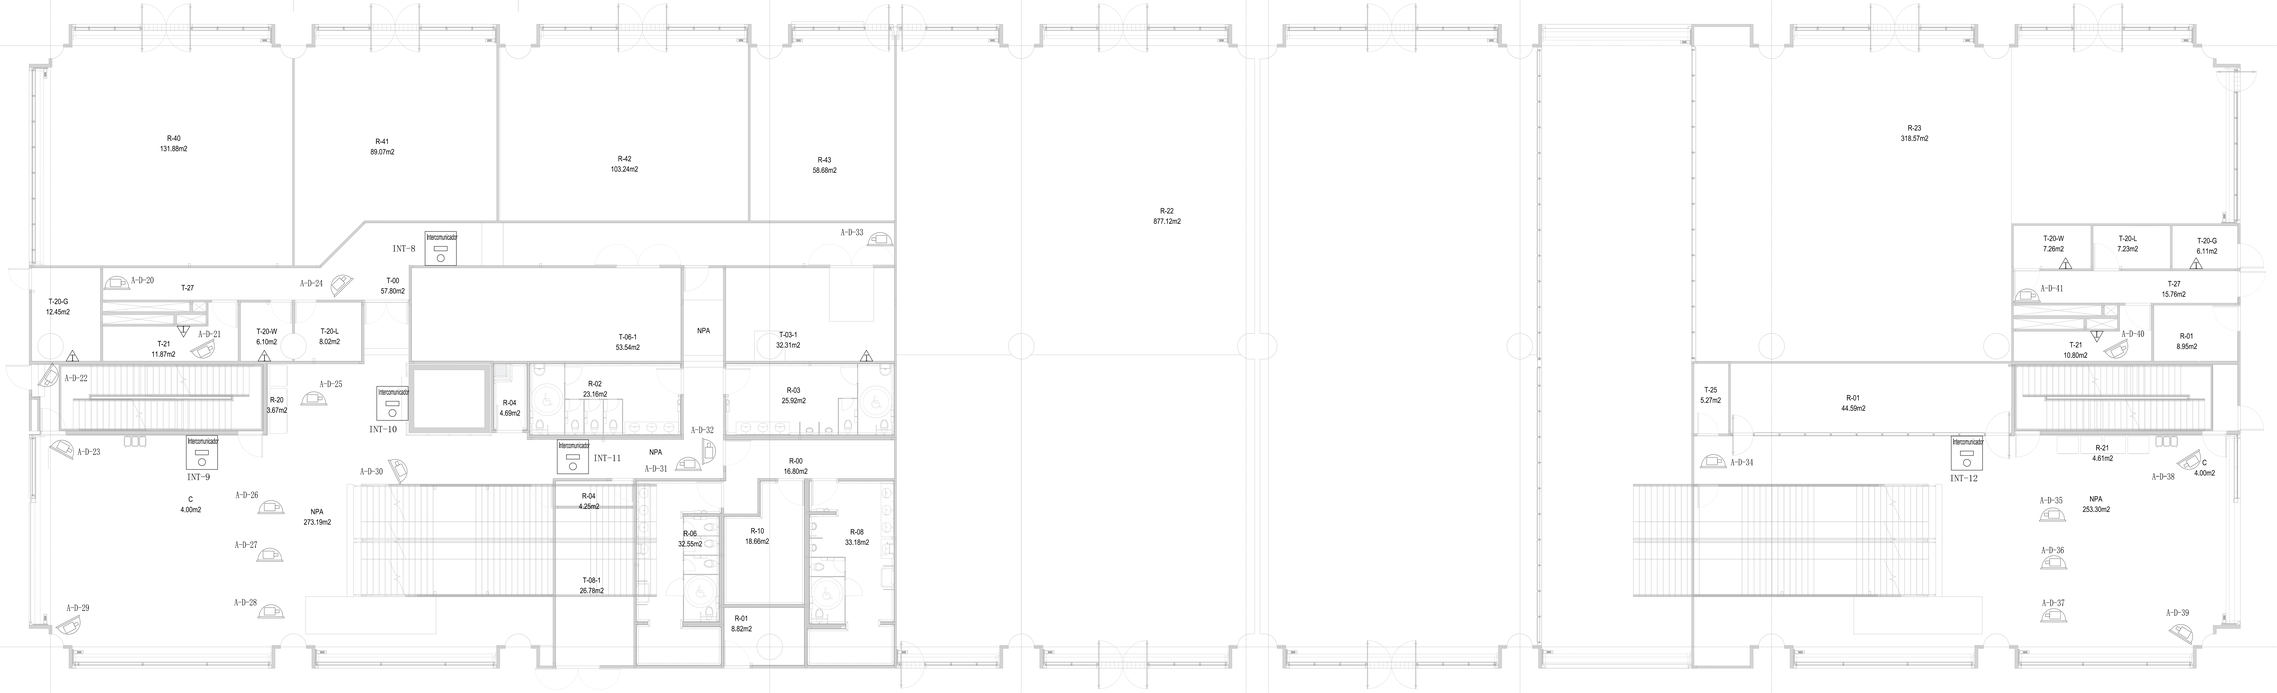

KEY PLAN

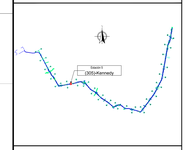

NOTAS

1.Este plano debe revisarse junto con el informe de diseño de LT1-5445-003-CON-ED-IND-PL-0001 y LT1-5445-003-CON-ED-IND-PL-0002.
2.Para efectos de equipo, consulte LT1-5445-003-ESP-IND-CO-0001.
3.Para efectos del cable Ethernet (indicando el Ethernet para los puntos de cámara seco conectados a los gabinetes de telecomunicaciones), consulte LT1-5445-003-ESP-IND-CO-0001.
4.Para efectos de cables conectados a la detección de intrusos, se indican en los planos del ACS.
5.La información de las bandejas de cables y tuberías se refiere a los planos de CNL.
6. Los criterios de determinación de las cámaras son los siguientes.
Nivel: tipo de cámara - código de la cámara.
Definición del nivel:
B: como nivel del sótano.
A: como nivel de acceso.
1: como nivel 1.
P: como nivel de plataforma.
Definición del tipo de cámara:
D: como cámara domo.
F: como cámara fija.
PTZ: como cámara PTZ.
P.D.: B-P-1: es una cámara fija con código 1 en el nivel del sótano.

CONVENCIONES

DESCRIPCIÓN DE LOS ICONOS

	Cámara de domo
	Cámara fija (tipo inteligente)
	Cámara PTZ
PAB	Monitor de vigilancia de pasajeros
DEC	Decodificador de video
	Intercomunicador

No.	PLANOS DE REFERENCIA	REV.

No.	MODELO BIM DE REFERENCIA	REV.
-	LT1-5445-003-CON-ED-ARQUMOD-RAT (EL 2023-03-02)	V00

No.	PAQUETE DE TRABAJO DE REFERENCIA	REV.

METRO LÍNEA 1	GCS Gestión Consultoría PMO Bogotá	CONSORCIO SUPERVISOR PLMB	wsp Línea 1 Metro de Bogotá Gerencia de Integración	DISEÑO: WANG KEJIA Mat.: R2022011915	APROBÓ: ZHANG YUJIE Mat.: NÚMERO DE MATRÍCULA	ING_TÉCNICO_WSP Mat.: NÚMERO DE MATRÍCULA	REVISIÓN No.	FECHA	DESCRIPCIÓN	REVISÓ	APROBÓ	APROBACIÓN CLIENTE
				REVISÓ: YANG BAODONG Mat.:	MODELO BIM: WANG KEJIA Mat.: R2022011915	APRO_INTEGRACIÓN_WSP Mat.: NÚMERO DE MATRÍCULA "Declaro que la obra de la referencia cumple con lo establecido en la NSR-10 y demás normas vigentes y en especial, en cuanto se refiere a la información contenida en este plano."	00	09/06/2023	Emitido para revisión y comentarios del diseño e interventoría - Incluye comentarios / modificado diseño de tubos en el control de cambios	T.B.	Z.Y.	
							001	30/06/2023	Emitido para comentarios internos - Emisión preliminar para comentarios	T.B.	Z.Y.	
							188	11/10/2023	Emitido para revisión y comentarios del diseño e interventoría	T.B.	Z.Y.	
							140	30/05/2023	Emitido para comentarios internos - Emisión preliminar para comentarios	T.B.	Z.Y.	

METRO LÍNEA 1

DIRECTOR DE PROYECTO: JAVIER ESCAMILLA N. Mat.: 25202-68697 CND

METRO LÍNEA 1
CONTRATO DE CONCESIÓN N.° 163 DE 2019
PROYECTO PRIMERA LÍNEA DEL METRO DE BOGOTÁ - TRAMO 1

DIBUJADO/APROBADO POR: Mat.:

FECHA: JUNIO 2023

SISTEMAS Y EQUIPOS
TELECOMUNICACIONES
ESTACIÓN KENNEDY - DISEÑO DETALLADO DEL NIVEL DE ACCESO (PARTE-2)
SISTEMA CCTV
DISPOSICIÓN GENERAL

NÚMERO DE PLANO: LT1-5445-305-CON-ED-IND-PL-0009_05_VCC

NOMBRE DEL ARCHIVO: LT1-5445-305-CON-ED-IND-PL-0009_VCC.dwg

ESCALA: 1:100

FECHA DE EMISIÓN: SEPTIEMBRE 2022

REVISIÓN: VCC

HOJA: 5 DE 14

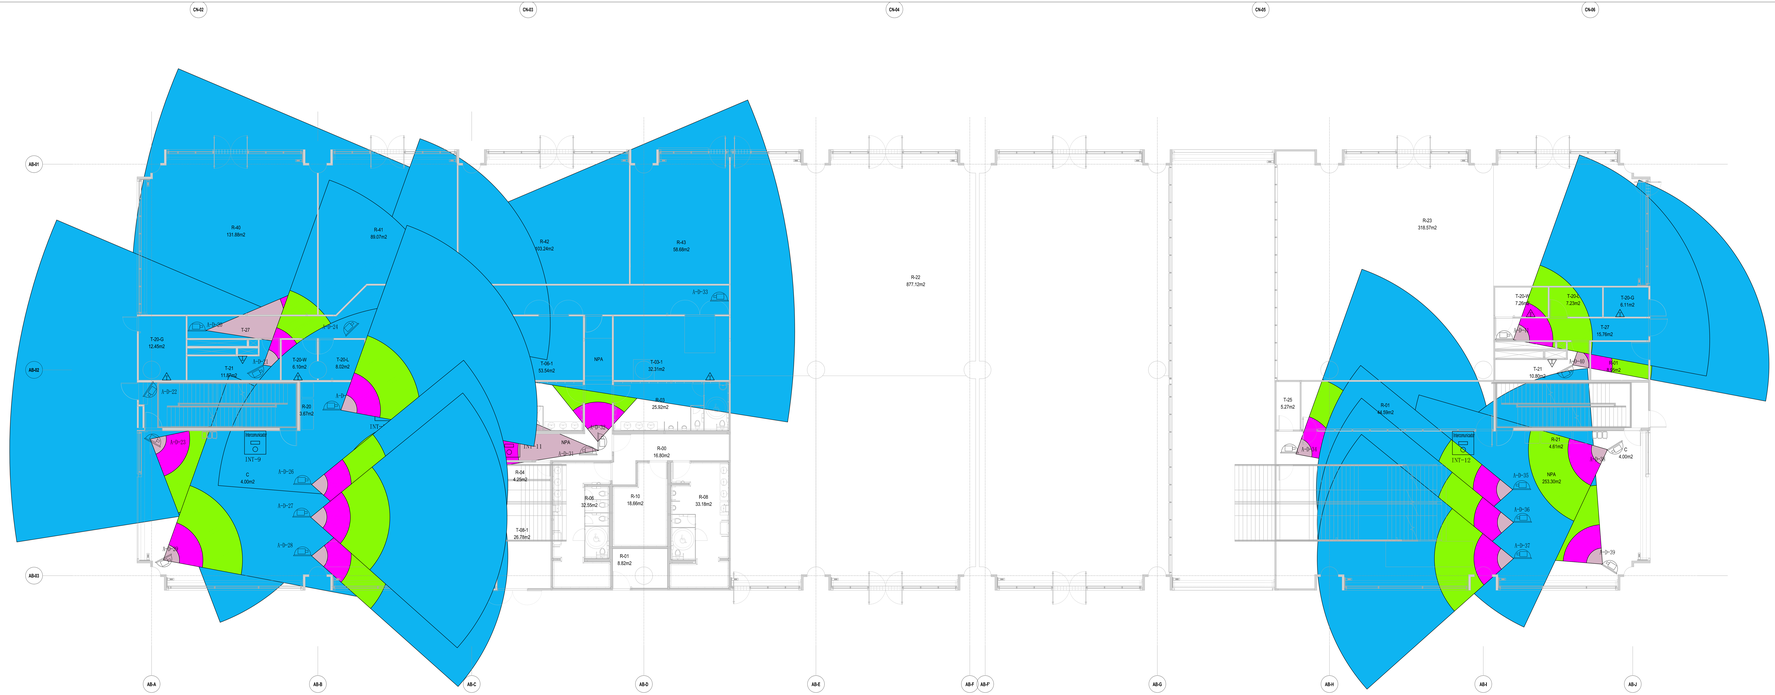

KEY PLAN

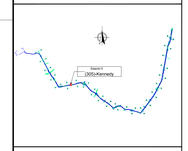

NOTAS

1.Este plano debe revisarse junto con el informe de diseño de LTT-SAAS-003-CON-ED-INS-RI-0001 y los planos de detalle de cámaras.
2.Para efectos de equipo, consulte LTT-SAAS-003-CON-ED-ING-CO-0001.
3.Para efectos del cable Ethernet (indicando el Ethernet para los puntos de cámara seco conectados a los gabinetes de telecomunicaciones), consulte el plano LTT-SAAS-003-CON-ED-ING-DI-0001.
4.Para efectos de cables conectados a la detección de intrusos, se incluye en los planos del ACS.
5.La información de las bandejas de cables y tuberías se refiere a los planos de CIVIL.
6. Los criterios de codificación de las cámaras son los siguientes:
Nivel - tipo de cámara - código de la cámara.
Nivel: B1 = sótano 1
B = sótano
1 = sótano nivel del sótano
A = zona nivel de acceso
Tipo de cámara: Domo/Fija.
F = zona nivel de plataforma
Definición del tipo de cámara:
D = zona cámara domo
F = zona cámara fija
P = zona cámara PTZ
E.G.: B1F = es una cámara fija con código 1 en el nivel del sótano.

CONVENCIONES

DESCRIPCIÓN DE LOS ICONOS

	Cámara de domo
	Cámara fija (tipo inteligente)
PTZ	Cámara PTZ
FAB	Monitor de vigilancia de pasajeros
DEC	Decodificador de video
	Intercomunicador

No.	PLANOS DE REFERENCIA	REV.

No.	MODELO BIM DE REFERENCIA	REV.
1	LTT-SAAS-003-CON-ED-ARQ-MOD-0001.RVT (R_2023-01-02)	V00

No.	PAQUETE DE TRABAJO DE REFERENCIA	REV.

METRO MOVILIDAD	GCS Gestores Ciudadanos PRC Bogotá	CONSORCIO SUPERVISOR PLMB	wsp Línea 3 Metro Ingeniería Gerencia de Proyectos	DISEÑO	WANG KEJIA Mat.: R2022011015	APROBO	ZHANG YIJIE Mat.: NUMERO DE MATRICULA	ING_TÉCNICO_WSP Mat.: NUMERO DE MATRICULA	REVISIÓN No.	FECHA	DESCRIPCIÓN	REVISO	APROBÓ	APROBACIÓN CLIENTE
				REVISO	YANG BAODONG Mat.:	MODELO/DIBUJO	WANG KEJIA Mat.: R2022011015	APRO_INTEGRACIÓN_WSP Mat.: NUMERO DE MATRICULA *Declaro que la obra se ha ejecutado conforme a los diseños y especificaciones técnicas, ajustes y ensayos de calidad, de acuerdo con los requisitos establecidos en el contrato de obra*	VCC	05/09/2023	Emitido para revisión y comentarios del diseño e interventoría- incluye comentarios- modificado donde se indica en el control de cambios	Y.B.	Z.Y.	
									UVI	30/05/2023	Emitido para comentarios internos- Emisión preliminar para comentarios	Y.B.	Z.Y.	
									VBB	11/10/2022	Emitido para revisión y comentarios del diseño e Interventoría	Y.B.	Z.Y.	
									VNO	30/09/2022	Emitido para comentarios internos- Emisión preliminar para comentarios	Y.B.	Z.Y.	

METRO LÍNEA 1

METRO LÍNEA 1
CONTRATO DE CONCESIÓN N.° 163 DE 2019

PROYECTO PRIMERA LÍNEA DEL METRO DE BOGOTÁ - TRAMO 1

CONTRATISTA: JAVEIR DISCARGA N. Mat.: 2520248807 CND

ESPECIALISTA INTERVENTORÍA: Mat.:

ESCALA: 1:100

FECHA: JUNIO 2023

SISTEMAS Y EQUIPOS
TELECOMUNICACIONES
ESTACIÓN KENNEDY - DISEÑO DETALLADO DEL NIVEL SÓTANO
SISTEMA CCTV
CUBIERTAS

NOMENCLATURA: LTT-SAAS-305-CON-ED-INS-PL-0009_06_VCC
NOMENCLATURA: LTT-SAAS-305-CON-ED-INS-PL-0009_VCC.dwg

ESCALA: 1:100
FECHA: SEPTIEMBRE 2022
REVISIÓN: VCC
HOJA: 6 DE 14

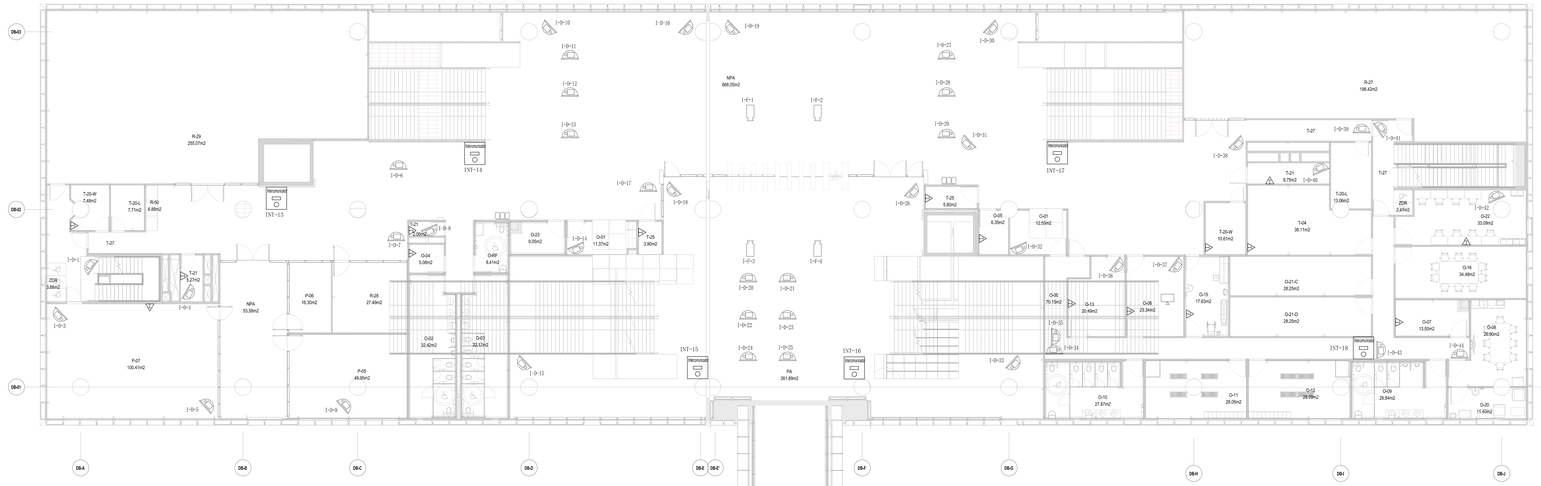

KEY PLAN

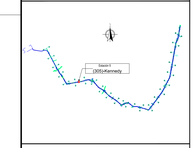

NOTAS

1.Este plano debe revisarse junto con el informe de diseño de LT-T-5445-003-CON-ED-IND-PL-0001 y el plano de convenciones de CNL.
2.Para el diseño de equipo, consultar LT-T-5445-003-CN-ED-IND-CO-0001.
3.Para efectos del cable Ethernet (indicando el Ethernet para los puntos de cámara seis) consultarlo a los especialistas de telecomunicaciones y de sistemas de seguridad electrónica.
4.Para efectos de cables conectados a la detección de intrusos, se indica en los planos ver ACS.
5.La información de las tipologías de cables y tuberías se refiere a los planos de CNL.
6. Los criterios de denominación de las cámaras son los siguientes.
Nivel - tipo de cámara - código de la cámara.
Nivel: Ejemplo: -1
0 como nivel del sótano.
1 como nivel de acceso.
2 como nivel mezanine.
3 como nivel de plataforma.
Definición del tipo de cámara
D como cámara domo.
F como cámara fija.
PTZ como cámara PTZ.
E.G: B-F-1 es una cámara fija con código 1 en el nivel del sótano.

CONVENCIONES

DESCRIPCIÓN DE LOS ICONOS

DOME	Cámara de domo
	Cámara fija (tipo inteligente)
PTZ	Cámara PTZ
FAB	Monitor de vigilancia de pasajeros
DEC	Decodificador de video
INT	Intercomunicador

No.	PLANOS DE REFERENCIA	REV.

No.	MODELO BIM DE REFERENCIA	REV.
1	LT-T-5000-005-CON-ED-ARQ-MOD-XXX* (R_ED-XX-XX)	V00

No.	PAQUETE DE TRABAJO DE REFERENCIA	REV.

REVISIÓN No.	FECHA	DESCRIPCIÓN	REVISÓ	APROBÓ	APROBACIÓN CLIENTE
VCC	05/09/2023	Emitido para revisión y comentarios del diseño e Interventoría- Incluye comentarios- modificado donde se indica en el control de cambios	Y.B.	Z.Y.	
VA1	30/06/2023	Emitido para comentarios internos- Emisión preliminar para comentarios	Y.B.	Z.Y.	
V00	11/10/2022	Emitido para revisión y comentarios del diseño e Interventoría	Y.B.	Z.Y.	
V00	30/09/2022	Emitido para comentarios internos- Emisión preliminar para comentarios	Y.B.	Z.Y.	

METRO LÍNEA 1
CONTRATO DE CONCESIÓN N.° 02 DE 2019

TELECOMUNICACIONES

ESTACIÓN KENNEDY - DISEÑO DETALLADO DEL NIVEL INTERMEDIO (PARTE 1)

SISTEMA CCTV

DISPOSICIÓN GENERAL

NOMBRE DEL ARCHIVO: LT-T-5445-305-CON-ED-IND-PL-0009_ST_VCC.dwg	ESCALA: 1:100	TAMAÑO: ISO A1	HOJA: 1 DE 14
FECHA: SEPTIEMBRE 2022	REVISIÓN: VCC		

DISEÑO: WANG KEJIA
Mat.: R2022011015

DIBUJO: YANG BAODONG
Mat.:

APROBÓ: ZHANG YIJIE
Mat.: NÚMERO DE MATRÍCULA

MODELO/BIM: WANG KEJIA
Mat.: R2022011015

ING_TÉCNICO_WSP
Mat.: NÚMERO DE MATRÍCULA

APRO_INTEGRACIÓN_WSP
Mat.: NÚMERO DE MATRÍCULA
"Declaro que he leído y he tenido en cuenta los comentarios de la revisión anterior y emito mi visto bueno de diseño de sistemas"

METRO LÍNEA 1
JAVIER ESCAMILLA N.
Mat.: 2520248897 CND

Mat.:

JUNIO 2023

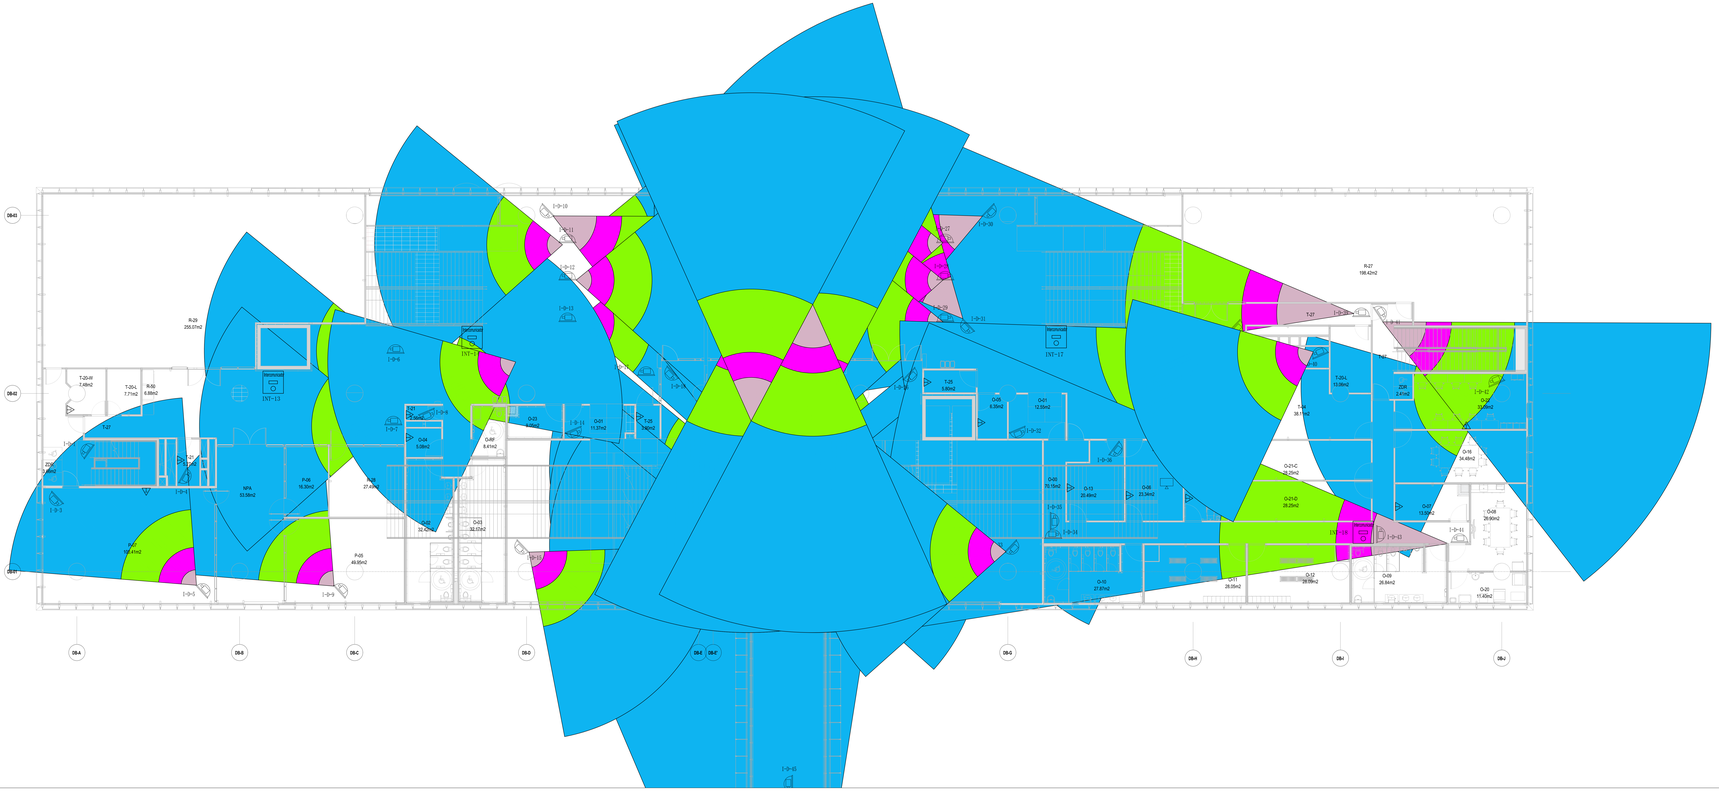

KEY PLAN

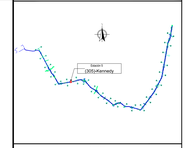

NOTAS

1.Este plano debe revisarse junto con el sistema de diseño de LTT-1-5445-005-CON-ED-IND-PL-0001 y LTT-1-5445-005-CON-ED-IND-PL-0002.
2.Para efectos de equipo, consultar LTT-5445-005-CON-ED-ING-CO-0001.
3.Para efectos del cable Ethernet (indicando el Ethernet para los puntos de cámara seco conectados a los gabinetes de telecomunicaciones), consultar LTT-5445-005-CON-ED-ING-CO-0001.
4.Para efectos de cables conectados a la detección de intrusos, se incluye en los planos del ACS.
5.La información de las bandejas de cables y tuberías se refiere a los planos de CNL.
6. Los criterios de codificación de las cámaras son los siguientes:
Nivel - tipo de cámara - código de la cámara.
Nivel: 1 como nivel 1.
B como nivel del sótano.
a, como nivel de acceso.
M como nivel de mezzanine.
P como nivel de plataforma.
Definición del tipo de cámara
D como cámara domo.
F como cámara fija.
PTZ como cámara PTZ.
E.G. B-F-1 es una cámara fija con código 1 en el nivel del sótano.

CONVENCIONES

DESCRIPCIÓN DE LOS ICONOS

DOME	Cámara de domo
	Cámara fija (tipo inteligente)
PTZ	Cámara PTZ
PAM	Monitor de vigilancia de pasajeros
DEC	Decodificador de video
	Intercomunicador

No.	PLANOS DE REFERENCIA	REV.

No.	MODELO BIM DE REFERENCIA	REV.
1	LTT-1-5000-005-CON-ED-ARQ-MOD-0007 (R_2023-01-02)	V00

No.	PAQUETE DE TRABAJO DE REFERENCIA	REV.

METRO DE BOGOTÁ	GCS Gestión Consultoría PMO Mcp®	CONSORCIO SUPERVISOR PLMB	wsp Línea de Diseño Asesoría y Gerencia de Proyectos	DIBUJO: WANG KEJIA Mat.: R2022011915	REVISO: YANG BAODONG Mat.:	APROBO: ZHANG YIJIE Mat.: NÚMERO DE MATRÍCULA	MODELO BIM: WANG KEJIA Mat.: R2022011915	ING_TÉCNICO_WSP Mat.: NÚMERO DE MATRÍCULA	APRO_INTEGRACIÓN_WSP Mat.: NÚMERO DE MATRÍCULA *Cumplen los roles de los firmas y cargos establecidos en el Plan de Gestión de la Calidad, apartado 5. ROLES Y RESPONSABILIDADES, numeral 5.1. ROLES DEL EQUIPO DE TRABAJO	REVISIÓN No.	FECHA	DESCRIPCIÓN	REVISO	APROBÓ	APROBACIÓN CLIENTE
									VCC	05/09/2023	Emitido para revisión y comentarios del cliente e interventoría - Incluye comentarios / modificado donde se indica en el control de cambios	T.B.	Z.Y.	
									UAI	30/06/2023	Emitido para comentarios internos - Emisión preliminar para comentarios	T.B.	Z.Y.	
									VBB	11/10/2022	Emitido para revisión y comentarios del cliente e Interventoría	T.B.	Z.Y.	
									VAC	30/09/2022	Emitido para comentarios internos - Emisión preliminar para comentarios	T.B.	Z.Y.	

METRO LÍNEA 1

METRO LÍNEA 1
CONTRATO DE CONCESIÓN N.° 163 DE 2019

TELECOMUNICACIONES

PROYECTO PRIMERA LÍNEA DEL METRO DE BOGOTÁ - TRAMO 1

CONTRATISTA:	JAVIER DESCANSA N.
Mat.:	2520245897 CND
ESPECIALISTA ESTRUCTURAS:	
Mat.:	
ESCALA:	1:100
FECHA:	JUNIO 2023

SISTEMAS Y EQUIPOS

ESTACIÓN KENNEDY - DISEÑO DETALLADO DEL NIVEL SÓTANO

SISTEMA CCTV

CUBIERTAS

CONTRATO No.	LTT-5445-005-CON-ED-IND-PL-0009_08_VCC	REVISIÓN:	VCC
DESCRIPCIÓN:	LTT-5445-005-CON-ED-IND-PL-0009_VCC.dwg	FECHA:	SEPTIEMBRE 2022

HOJA: 8 DE 14

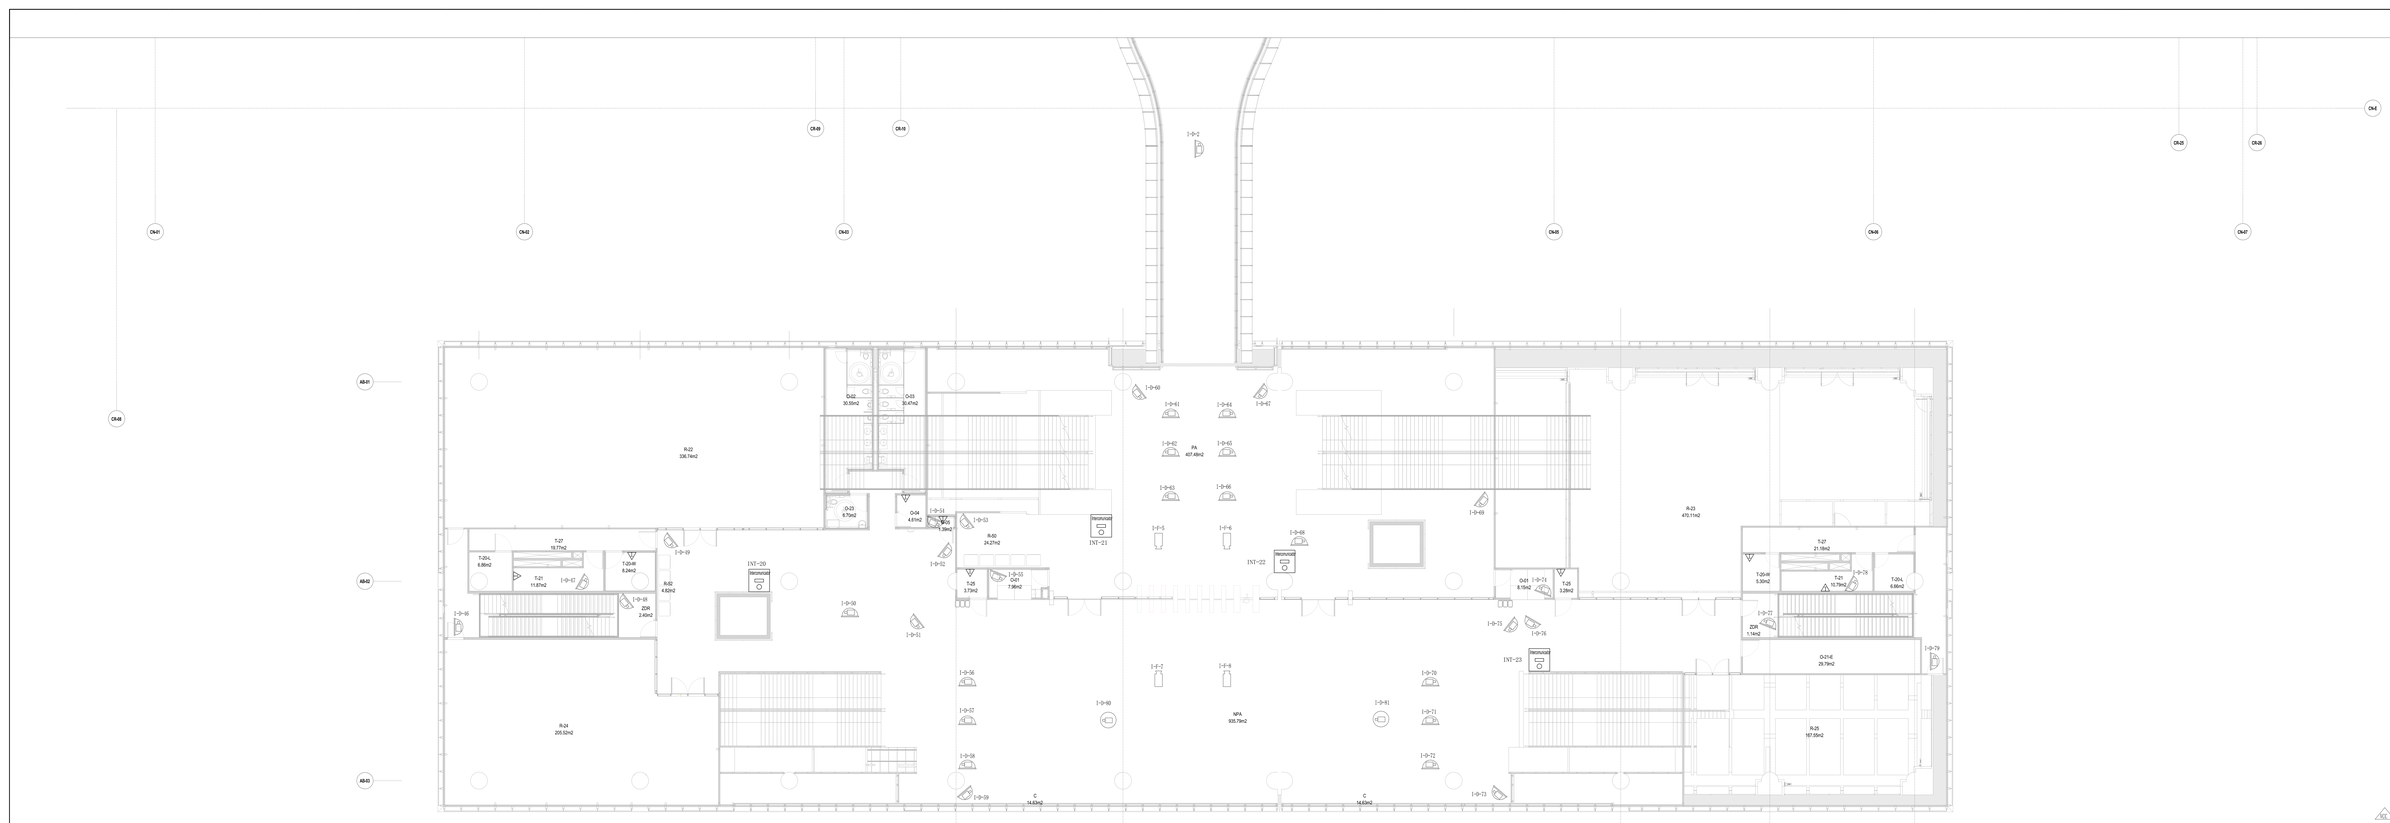

KEY PLAN

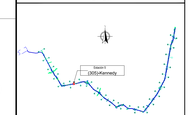

NOTAS

1.Este plano debe revisarse junto con el informe de diseño de LT1-1-0445-000-CON-ED-IND-RI-0001 y con el plano LT1-1-0445-000-CON-ED-IND-PL-0001.
2.Para efectuar las sujeción, consultar LT1-1-0445-000-CON-ED-IND-CO-0001.
3.Para efectuar del cable Ethernet (indicando el Ethernet para los puntos de cámara seco conectados a los switches) consultar el plano LT1-1-0445-000-CON-ED-IND-PL-0002 y LT1-1-0445-000-CON-ED-IND-CO-0001.
4.Para efectuar los cables conectados a la detección de intrusos, se incluye en los planos del ACS.
5.La información de las bandejas de cables y tuberías se refiere a los planos de CNL.
6. Los criterios de denominación de las cámaras son los siguientes.
Nivel - tipo de cámara - código de la cámara.
Definición del nivel:
E: como nivel del exterior.
A: como nivel de acceso.
M: como nivel mezzanine.
P: como nivel de plataforma.
Definición del tipo de cámara:
D: como cámara domo.
F: como cámara fija.
PTZ: como cámara PTZ.
E.G. B-P-1 es una cámara fija con código 1 en el nivel del exterior.

CONVENCIONES

DESCRIPCIÓN DE LOS ICONOS

	Cámara de domo
	Cámara fija (tipo inteligente)
PTZ	Cámara PTZ
FAB	Monitor de vigilancia de pasajeros
DEC	Decodificador de video
	Intercomunicador

No.	PLANOS DE REFERENCIA	REV.

No.	MODELO BIM DE REFERENCIA	REV.
1	LT1-1-0000-000-CON-ED-ARQ-MOD-XXX* (R_2023-01-02)	V00

No.	PAQUETE DE TRABAJO DE REFERENCIA	REV.

REVISIÓN No.	FECHA	DESCRIPCIÓN	REVISÓ	APROBÓ	APROBACIÓN CLIENTE
VCC	05/08/2023	Emitido para revisión y comentarios del diseño e Interventoría- Incluye comentarios / modificado donde se indica en el control de cambios	T.B.	Z.Y.	
UAV	30/05/2023	Emitido para comentarios internos - Emisión preliminar para comentarios	T.B.	Z.Y.	
VBB	11/10/2022	Emitido para revisión y comentarios del diseño e Interventoría	T.B.	Z.Y.	
VNG	30/09/2022	Emitido para comentarios internos- Emisión preliminar para comentarios	T.B.	Z.Y.	

DISEÑO: WANG KEJIA Mat.: R2022011915
REVISÓ: YANG BAODONG Mat.:
APROBÓ: ZHANG YIJIE Mat.: NÚMERO DE MATRÍCULA
MODELO BIM: WANG KEJIA Mat.: R2022011915
ING_TÉCNICO_WSP Mat.: NÚMERO DE MATRÍCULA
APRO_INTEGRACIÓN_WSP Mat.: NÚMERO DE MATRÍCULA
"Declaro que he leído y he dado el correcto cumplimiento a lo establecido en el Manual de Estándares y en LT1- 1- 0445- 001-GEN-IN-0001 y que el plano se encuentra en el nivel de madurez requerido para la fase"

METRO LÍNEA 1
CONTRATO DE CONCESIÓN N.° 163 DE 2019
TELECOMUNICACIONES
PROYECTO PRIMERA LÍNEA DEL METRO DE BOGOTÁ - TRAMO 1
JAVIER ESCOBOZA N.
Mat.: 25202-69897 CND

SISTEMAS Y EQUIPOS
TELECOMUNICACIONES
ESTACIÓN KENNEDY - DISEÑO DETALLADO DEL NIVEL INTERMEDIO (PARTE 2)
SISTEMA CCTV
EMPOTRADOR GENERAL

CONTRATO No.	ESCALA	FORMATO	HOJA No.
LT1-1-0445-305-CON-ED-IND-PL-0009_09_VCC	1:100	A1	9 DE 14
NOMBRE DEL ARCHIVO: LT1-1-0445-305-CON-ED-IND-PL-0009_VCC.dwg	FECHA: SEPTIEMBRE 2022	REVISIÓN: VCC	

Empresa Consultora PMO Bogotá
Línea de Diseño Asistido y Gerencia de Proyectos
CONSORCIO SUPERVISOR PLMB

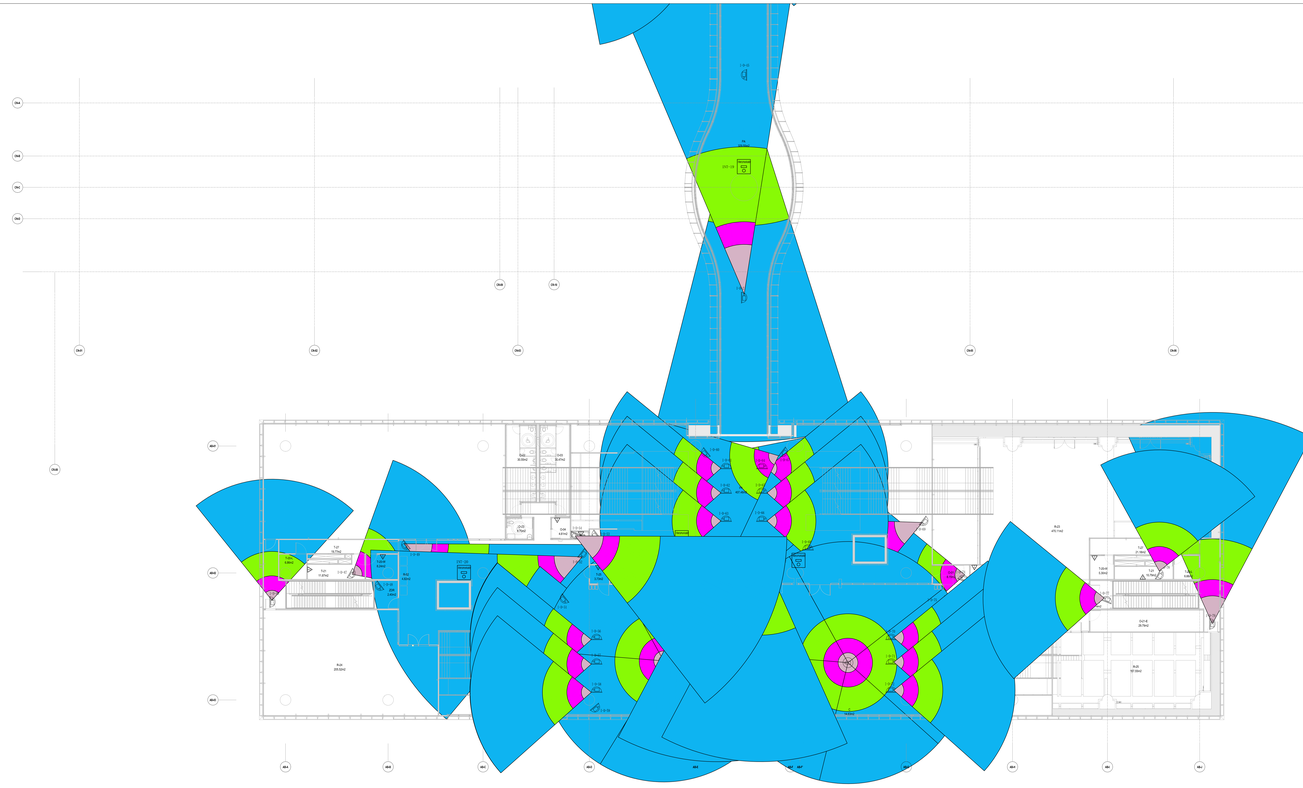

KEY PLAN

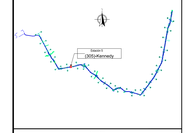

NOTAS

1.Este plano debe revisarse junto con el informe de diseño (ls LT1-5445-000-CON-ED-IND-PL-0001 y LT1-5445-000-CON-ED-IND-PL-0002).
2.Para el diseño de equipo, consulte LT1-5445-000-CON-ED-IND-ZZ-0001.
3.Para el diseño del cable Ethernet (incluyendo el Ethernet para los puertos de cámara) vea conectados a los switches de comunicación, consulte LT1-5445-000-CON-ED-IND-ZZ-0001 y LT1-5445-000-CON-ED-IND-ZZ-0002.
4.Para el diseño de cables conectados a la detección de intrusos, se incluye en los planos del ACS.
5.La información de las bandejas de cables y tuberías se refiere a los planos de CNL.
6. Los criterios de codificación de las cámaras son los siguientes.
Nivel - tipo de cámara - código de la cámara.
Nivel de cámara:
S: cuarto nivel del sótano.
a: cuarto nivel de acceso.
1: primer nivel de mezzanine.
P: cuarto nivel de plataforma.
Definición del tipo de cámara
D: cúpula cámara domo
F: cuarto cámara fija
P: cuarto cámara PTZ
E.G.: S-F-1: es una cámara fija con código 1 en el nivel del sótano.

CONVENCIONES

DESCRIPCIÓN DE LOS ICONOS

	Cámara de domo
	Cámara fija (tipo inteligente)
	Cámara PTZ
FAB	Monitor de vigilancia de pasajeros
DEC	Decodificador de vídeo
	Intercomunicador

No.	PLANOS DE REFERENCIA	REV.

No.	MODELO BIM DE REFERENCIA	REV.
-	LT1-5445-000-CON-ED-ARQ-MOD-XXX* (RL 2023-01-02)	V00

No.	PAQUETE DE TRABAJO DE REFERENCIA	REV.

DISEÑO: WANG KEJIA Mat.: R2022011915	APROBÓ: ZHANG YIJIE Mat.: NÚMERO DE MATRÍCULA	ING_TÉCNICO_WSP Mat.: NÚMERO DE MATRÍCULA	REVISIÓN No.	FECHA	DESCRIPCIÓN	REVISÓ	APROBÓ	APROBACIÓN CLIENTE	METRO LÍNEA 1 CONTRATO DE CONCESIÓN N.° 163 DE 2019 PROYECTO PRIMERA LÍNEA DEL METRO DE BOGOTÁ - TRAMO 1
REVISÓ: YANG BAODONG Mat.:	ACEPTACIÓN CLIENTE: WANG KEJIA Mat.: R2022011915	APRO_INTEGRACIÓN_WSP Mat.: NÚMERO DE MATRÍCULA *Cumplir con lo dicho en las normas y procedimientos de la Gerencia de Integración vigentes y escribir el nombre del cargado de aprobar el documento	VCC	05/09/2023	Emitido para revisión y comentarios del diseño a Interventoría - incluye comentarios / modificado diseño de rutas en el control de centros	Y.B.	Z.Y.		METRO LÍNEA 1
			UVI	30/06/2023	Emitido para comentarios internos - Emisión preliminar para comentarios	Y.B.	Z.Y.		
			VBB	11/10/2022	Emitido para revisión y comentarios del diseño a Interventoría	Y.B.	Z.Y.		
			VAC	30/09/2022	Emitido para comentarios internos - Emisión preliminar para comentarios	Y.B.	Z.Y.		

DIRECTOR DE CONSTRUCCIÓN: JAVIER ESCAMILLA N. Mat.: 25202-60897 CND	ESPECIALISTA INTERVENTORÍA: Mat.:	ESCALA:	FECHA: JUNIO 2023

SISTEMAS Y EQUIPOS			
TELECOMUNICACIONES			
ESTACIÓN KENNEDY - DISEÑO DETALLADO DEL NIVEL SÓTANO			
SISTEMA CCTV			
CUBIERTAS			
CONTRATO: LT1-5445-305-CON-ED-IND-PL-0009_10_VCC	ESCALA: 1:100	TAMAÑO: ISO A1	REVISIÓN: VCC
NOMBRE DEL ARCHIVO: LT1-5445-305-CON-ED-IND-PL-0009_VCC.dwg	FECHA: SEPTIEMBRE 2022	HOJA: 19 DE 141	

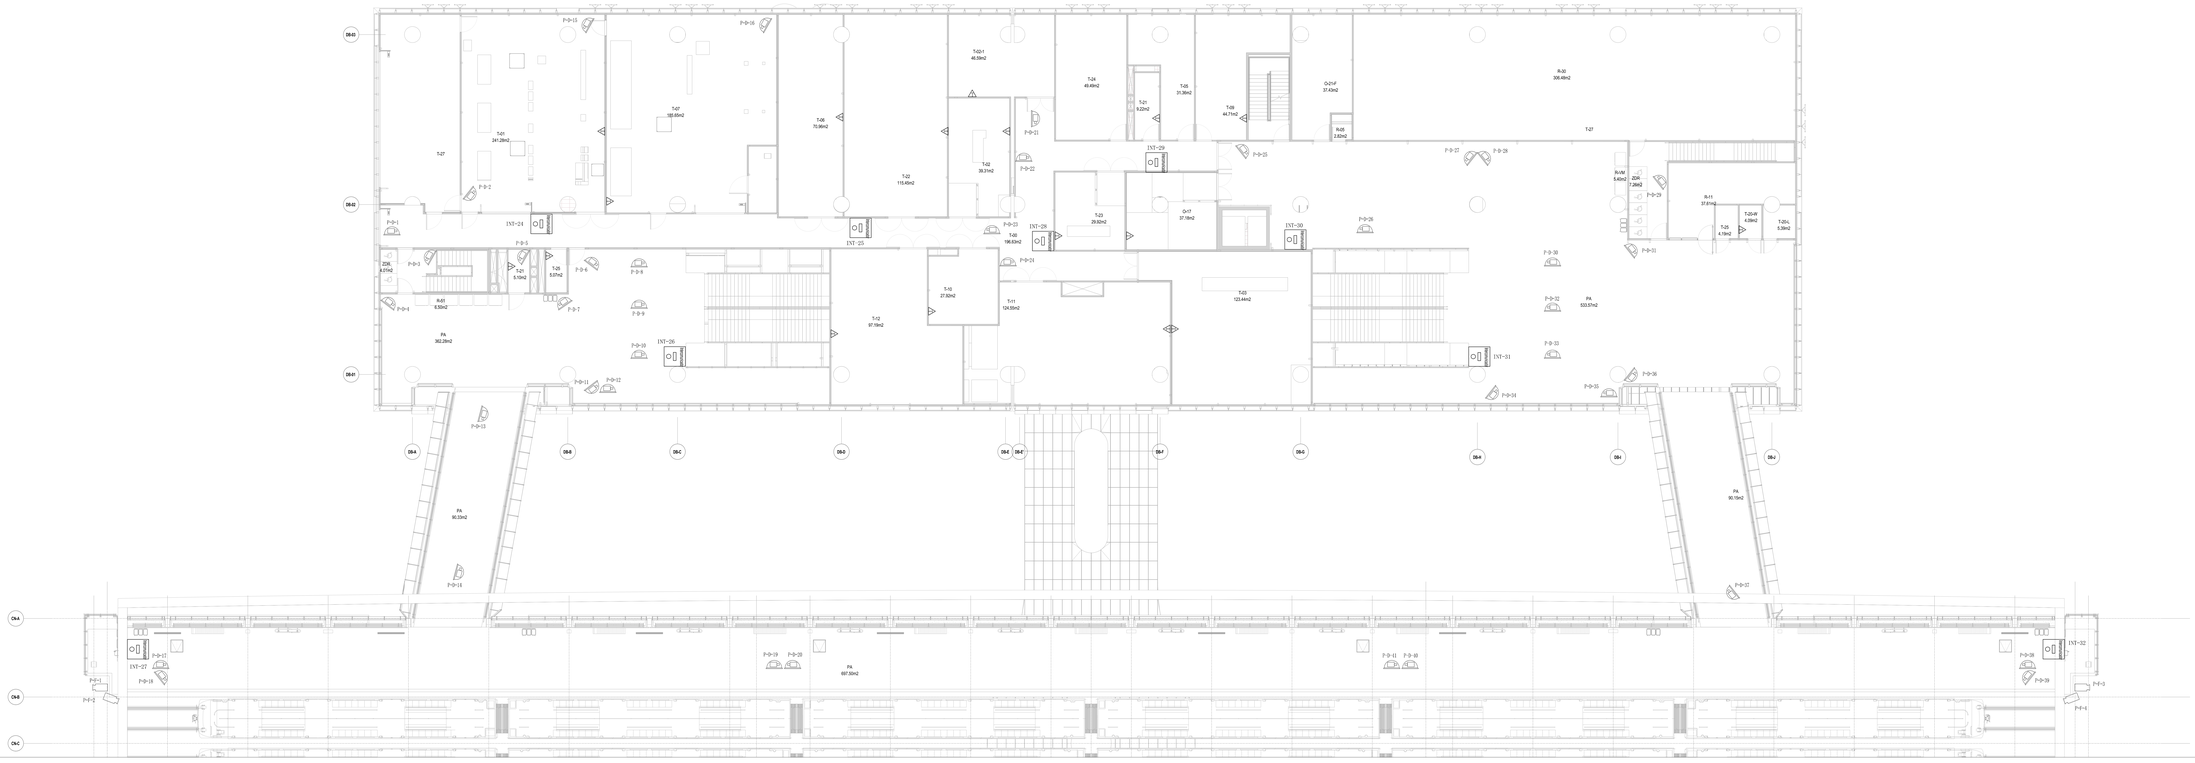

KEY PLAN

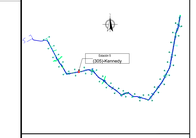

NOTAS

1.Este plano debe revisarse junto con el informe de diseño (n.1771-5445-003-CON-ED-IND-RI-0001 y n.1771-5445-003-CON-ED-IND-RI-0002).
2.Para ubicación de equipo, consultar (1771-5445-003-CON-ED-IND-DU-0001).
3.Para ubicación del cable Ethernet (indicando el Ethernet para los puntos de cámara seco conectados a los gabinetes de telecomunicaciones), consultar (1771-5445-003-CON-ED-IND-DU-0001).
4.Para ubicación de cables conectados a la detección de intrusos, se incluye en los planos de red ACS.
5.La información de las bandejas de cables y tuberías se refiere a los planos de CNL.
6. Los criterios de denominación de las cámaras son los siguientes.
Nivel - tipo de cámara - código de la cámara.
Nivel: Ejemplo: D8
D: zona nivel del edificio
8: zona nivel de acceso
E: zona nivel de plataforma
F: zona nivel de plataforma
Definición del tipo de cámara:
D: zona cámara domo
F: zona cámara fija
PTZ: zona cámara PTZ
P.D.: B.P.A. es una cámara fija con código 1 en el nivel del edificio.

CONVENCIONES

DESCRIPCIÓN DE LOS ICONOS

	Cámara de domo
	Cámara fija (tipo inteligente)
PTZ	Cámara PTZ
FAB	Monitor de vigilancia de pasajeros
DEC	Decodificador de vídeo
INT	Intercomunicador

No.	PLANOS DE REFERENCIA	REV.

No.	MODELO BIM DE REFERENCIA	REV.
-	L171-5445-003-CON-ED-ARQ-MOD-XXX.rvt (BL 2023-0102)	V00

No.	PAQUETE DE TRABAJO DE REFERENCIA	REV.

DISEÑO: WANG KEJIA Mat.: R2022011815
REVISÓ: YANG BAODONG Mat.:
APROBÓ: ZHANG YIJIE Mat.: NÚMERO DE MATRÍCULA
MODELO BIM: WANG KEJIA Mat.: R2022011815
ING_TÉCNICO_WSP Mat.: NÚMERO DE MATRÍCULA
APRO_INTEGRACIÓN_WSP Mat.: NÚMERO DE MATRÍCULA

REVISIÓN No.	FECHA	DESCRIPCIÓN	REVISÓ	APROBÓ	APROBACIÓN CLIENTE
VCC	05/09/2023	Emitido para revisión y comentarios del diseño e Interventoría - Incluye comentarios / modificado donde se indica en el control de cambios	Y.B.	Z.Y.	
VA1	30/06/2023	Emitido para comentarios internos - Emisión preliminar para comentarios	Y.B.	Z.Y.	
VB8	11/10/2022	Emitido para revisión y contemplas del diseño e Interventoría	Y.B.	Z.Y.	
VA0	30/09/2022	Emitido para comentarios internos - Emisión preliminar para comentarios	Y.B.	Z.Y.	

METRO LÍNEA 1
CONTRATO DE CONCESIÓN N.° 163 DE 2019
TELECOMUNICACIONES
PROYECTO PRIMERA LÍNEA DEL METRO DE BOGOTÁ - TRAMO 1
DIRECTOR DE CONCESIÓN: JAVIER ESCAMILLA N. Mat.: 25202-60897 CND
ESPECIALISTA INTERVENTORÍA: Mat.:
FECHA: JUNIO 2023

SISTEMAS Y EQUIPOS
TELECOMUNICACIONES
ESTACIÓN KENNEDY - DISEÑO DETALLADO DEL NIVEL DE PLATAFORMA (PARTE 1)
SISTEMA CCTV
DISPOSICIÓN GENERAL
CONTRATO No.: L171-5445-3DS-CON-ED-IND-PL-0009_11_VCC
DOCUMENTO No.: L171-5445-3DS-CON-ED-IND-PL-0009_VCC.dwg
ESCALA: 1:100
FECHA: SEPTIEMBRE 2022
REVISIÓN: VCC
HOJA: 11 DE 14

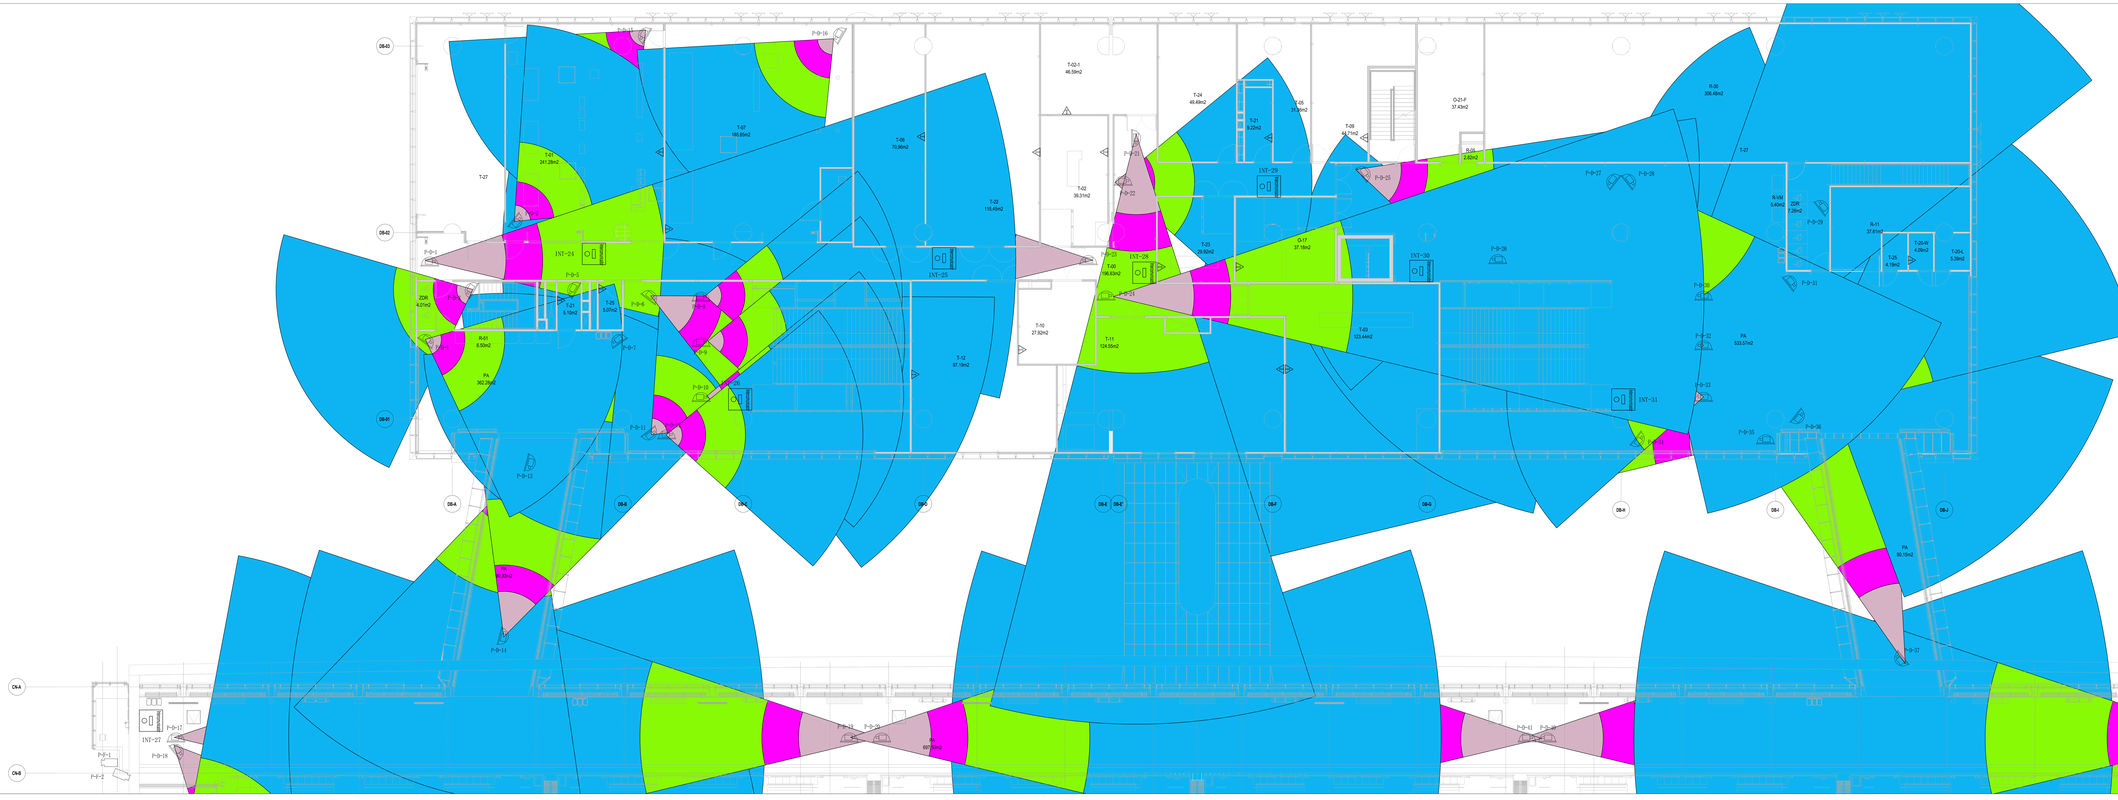
DB-D
DB-E
DB-1
DB-A
DB-B
DB-C
DB-F
DB-G
DB-H
DB-I
DB-J
DA-A
DA-B
INT-24
INT-25
INT-26
INT-27
INT-28
INT-29
INT-30
INT-31
INT-32
T-01 180.65m2
T-02 115.45m2
T-03 241.28m2
T-04 70.99m2
T-05 39.31m2
T-06 49.42m2
T-07 124.00m2
T-08 46.71m2
T-09 37.43m2
T-10 27.92m2
T-11 124.00m2
T-12 87.19m2
T-13 46.59m2
T-14 45.49m2
T-15 37.43m2
T-16 37.18m2
T-17 123.44m2
T-18 124.00m2
T-19 124.00m2
T-20 123.44m2
T-21 5.10m2
T-22 1.22m2
T-23 28.92m2
T-24 45.49m2
T-25 1.05m2
R-01 6.50m2
R-02 6.50m2
R-03 6.50m2
R-04 6.50m2
R-05 37.43m2
R-06 37.18m2
R-07 123.44m2
R-08 124.00m2
R-09 124.00m2
R-10 123.44m2
R-11 37.81m2
R-12 37.81m2
R-13 37.81m2
R-14 37.81m2
R-15 37.81m2
R-16 37.81m2
R-17 37.81m2
R-18 37.81m2
R-19 37.81m2
R-20 37.81m2
R-21 37.81m2
R-22 37.81m2
R-23 37.81m2
R-24 37.81m2
R-25 37.81m2
R-26 37.81m2
R-27 37.81m2
R-28 37.81m2
R-29 37.81m2
R-30 306.48m2
R-31 37.81m2
R-32 37.81m2
R-33 37.81m2
R-34 37.81m2
R-35 37.81m2
R-36 37.81m2
R-37 37.81m2
R-38 37.81m2
R-39 37.81m2
R-40 37.81m2
R-41 37.81m2
R-42 37.81m2
R-43 37.81m2
R-44 37.81m2
R-45 37.81m2
R-46 37.81m2
R-47 37.81m2
R-48 37.81m2
R-49 37.81m2
R-50 37.81m2

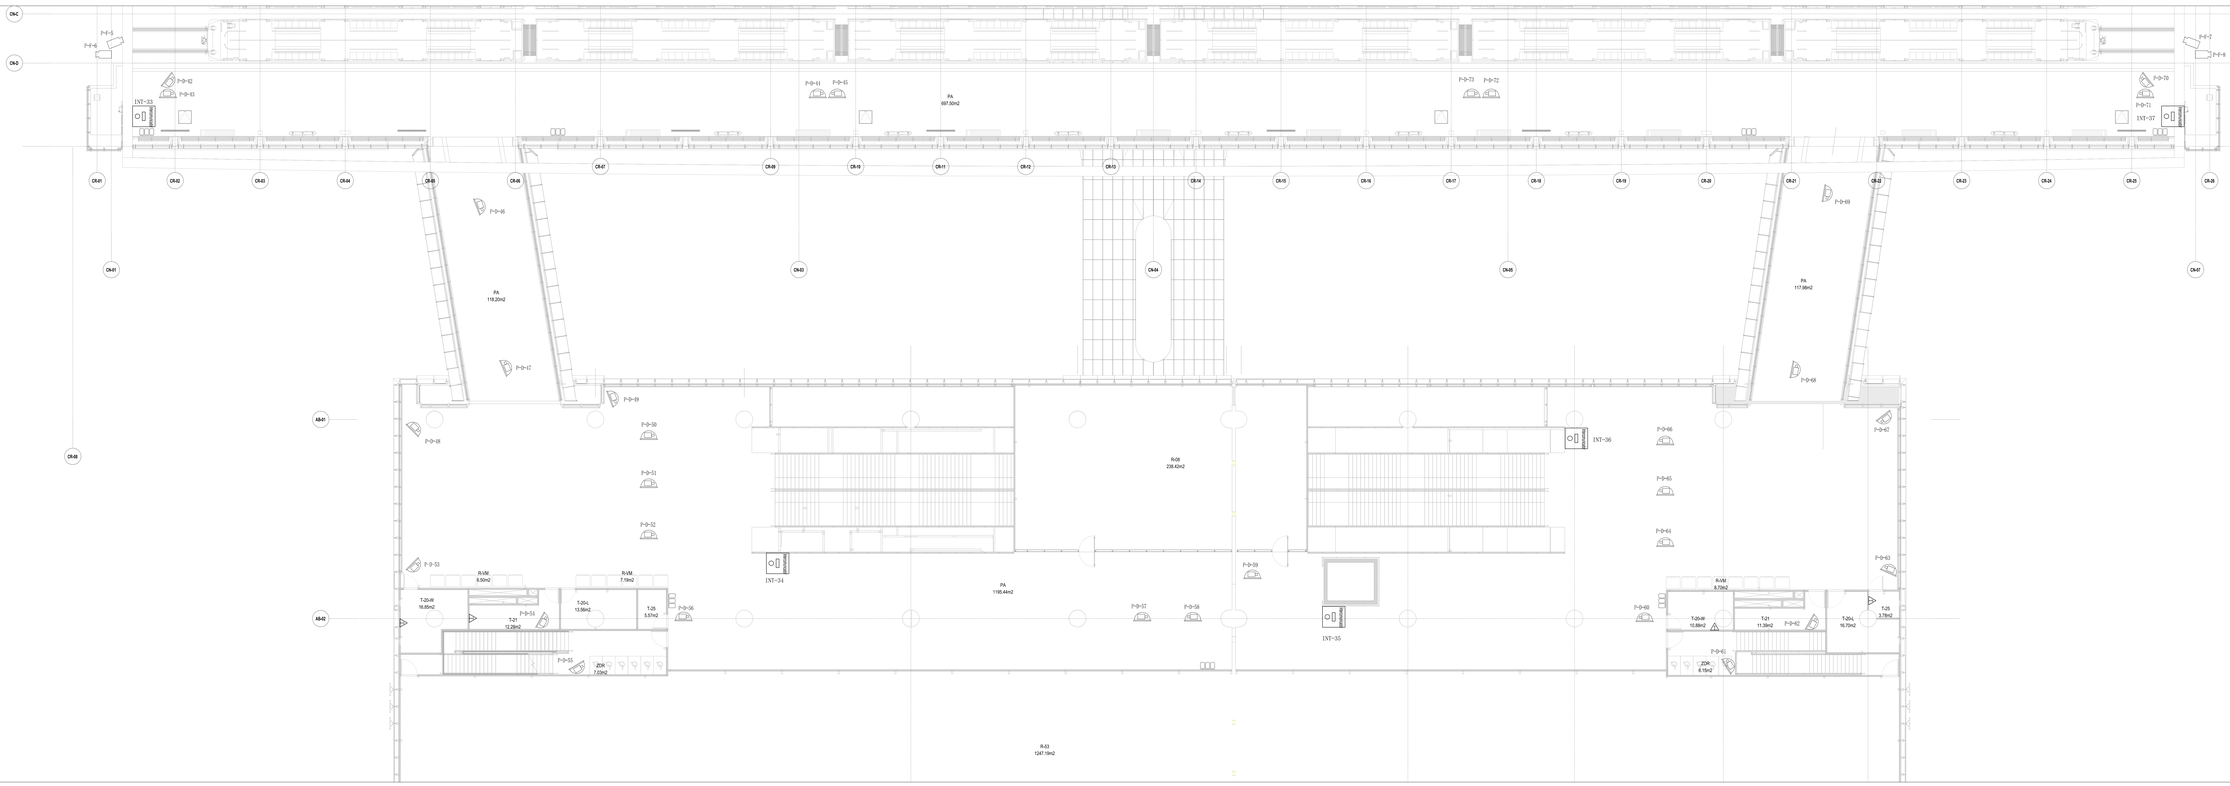

KEY PLAN

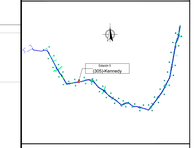

NOTAS

1.Este plano debe revisarse junto con el informe de diseño de LTT-GAS-003-CON-ED-INS-RI-0001 y los planos de detalle de cámaras.
2.Para el diseño de equipo, consulte LTT-GAS-003-CN-ED-INS-DC-0001.
3.Para el diseño del cable Ethernet (indicando el Ethernet para los puntos de cámara seco conectados a los gabinetes de telecomunicaciones), consulte el diagrama de red LTT-GAS-003-CN-ED-INS-DR-0001.
4.Para el diseño de cables conectados a la detección de intrusos, se incluye en los planos del AICS.
5.La información de las bandejas de cables y tuberías se refiere a los planos de CNL.
6. Los criterios de denominación de las cámaras son los siguientes.
Nivel - tipo de cámara - código de la cámara.
Definición del nivel:
B: como nivel del sótano.
A: como nivel de acceso.
M: como nivel medio.
P: como nivel de plataforma.
Definición del tipo de cámara:
D: como cámara domo.
F: como cámara fija.
T: como cámara PTZ.
E.G.: B-F-1: es una cámara fija con código 1 en el nivel del sótano.

CONVENCIONES

DESCRIPCIÓN DE LOS ICONOS

	Cámara de domo
	Cámara fija (tipo inteligente)
PTZ	Cámara PTZ
PAB	Monitor de vigilancia de pasajeros
DEC	Decodificador de vídeo
INT	Intercomunicador

No.	PLANOS DE REFERENCIA	REV.

No.	MODELO BIM DE REFERENCIA	REV.
1	LTT-GAS-003-CON-ED-ARQ-MOD-XXY (R_ED-XX-XX)	V00

No.	PAQUETE DE TRABAJO DE REFERENCIA	REV.

METRO MADRID | GCS Grandes Consultores PRC Bright | CONSORCIO SUPERVISOR PLMB | wsp Líder de Diseño Ferroviario Ingeniería de Pedigrotti

DISEÑO: WANG KEJIA Mat.: R2022011915	APROBÓ: ZHANG YUJIE Mat.: NÚMERO DE MATRÍCULA	ING_TÉCNICO_WSP Mat.: NÚMERO DE MATRÍCULA	
REVISÓ: YANG BAODONG Mat.:	MODELO/DIBUJO: WANG KEJIA Mat.: R2022011915	APRO_INTEGRACIÓN_WSP Mat.: NÚMERO DE MATRÍCULA "Declaro que he visto a los efectos y conocimiento de mi firma, el presente plano y doy mi conformidad a su contenido, emitido a efectos de validez de aprobación"	

REVISIÓN No.	FECHA	DESCRIPCIÓN	REVISÓ	APROBÓ	APROBACIÓN CLIENTE
VCC	05/09/2023	Emitido para revisión y comentarios del diseño e interventoría. Incluye comentarios / modificado donde se indica en el comité de sambos	Y.B.	Z.Y.	
V01	30/05/2023	Emitido para comentarios internos. Emisión preliminar para comentarios	Y.B.	Z.Y.	
V00	11/10/2022	Emitido para revisión y comentarios del diseño e Interventoría.	Y.B.	Z.Y.	
V00	30/09/2022	Emitido para comentarios internos. Emisión preliminar para comentarios	Y.B.	Z.Y.	

METRO LÍNEA 1

DIRECTOR DE PROYECTO: JAVIER ESCAMILLA N. Mat.: 25202-69897 CND	ESPECIALISTA INTERVENTORÍA: Mat.:

METRO LÍNEA 1
CONTRATO DE CONCESIÓN N.° 163 DE 2019
TELECOMUNICACIONES
PROYECTO PRIMERA LÍNEA DEL METRO DE BOGOTÁ - TRAMO 1

SISTEMAS Y EQUIPOS	
ESTACIÓN KENNEDY - DISEÑO DETALLADO DEL NIVEL DE PLATAFORMA (PARTE 2)	
SISTEMA CCTV	
DISPOSICIÓN GENERAL	
FORMATO: A1	ESCALA: 1:100
NOMBRE DEL ARCHIVO: LTT-GAS-305-CON-ED-INS-PL-0009_13_VCC.dwg	
FECHA: JUNIO 2023	
FECHA DE IMPRESIÓN: SEPTIEMBRE 2022	REVISIÓN: VCC
HOJA No.: 13 DE 14	

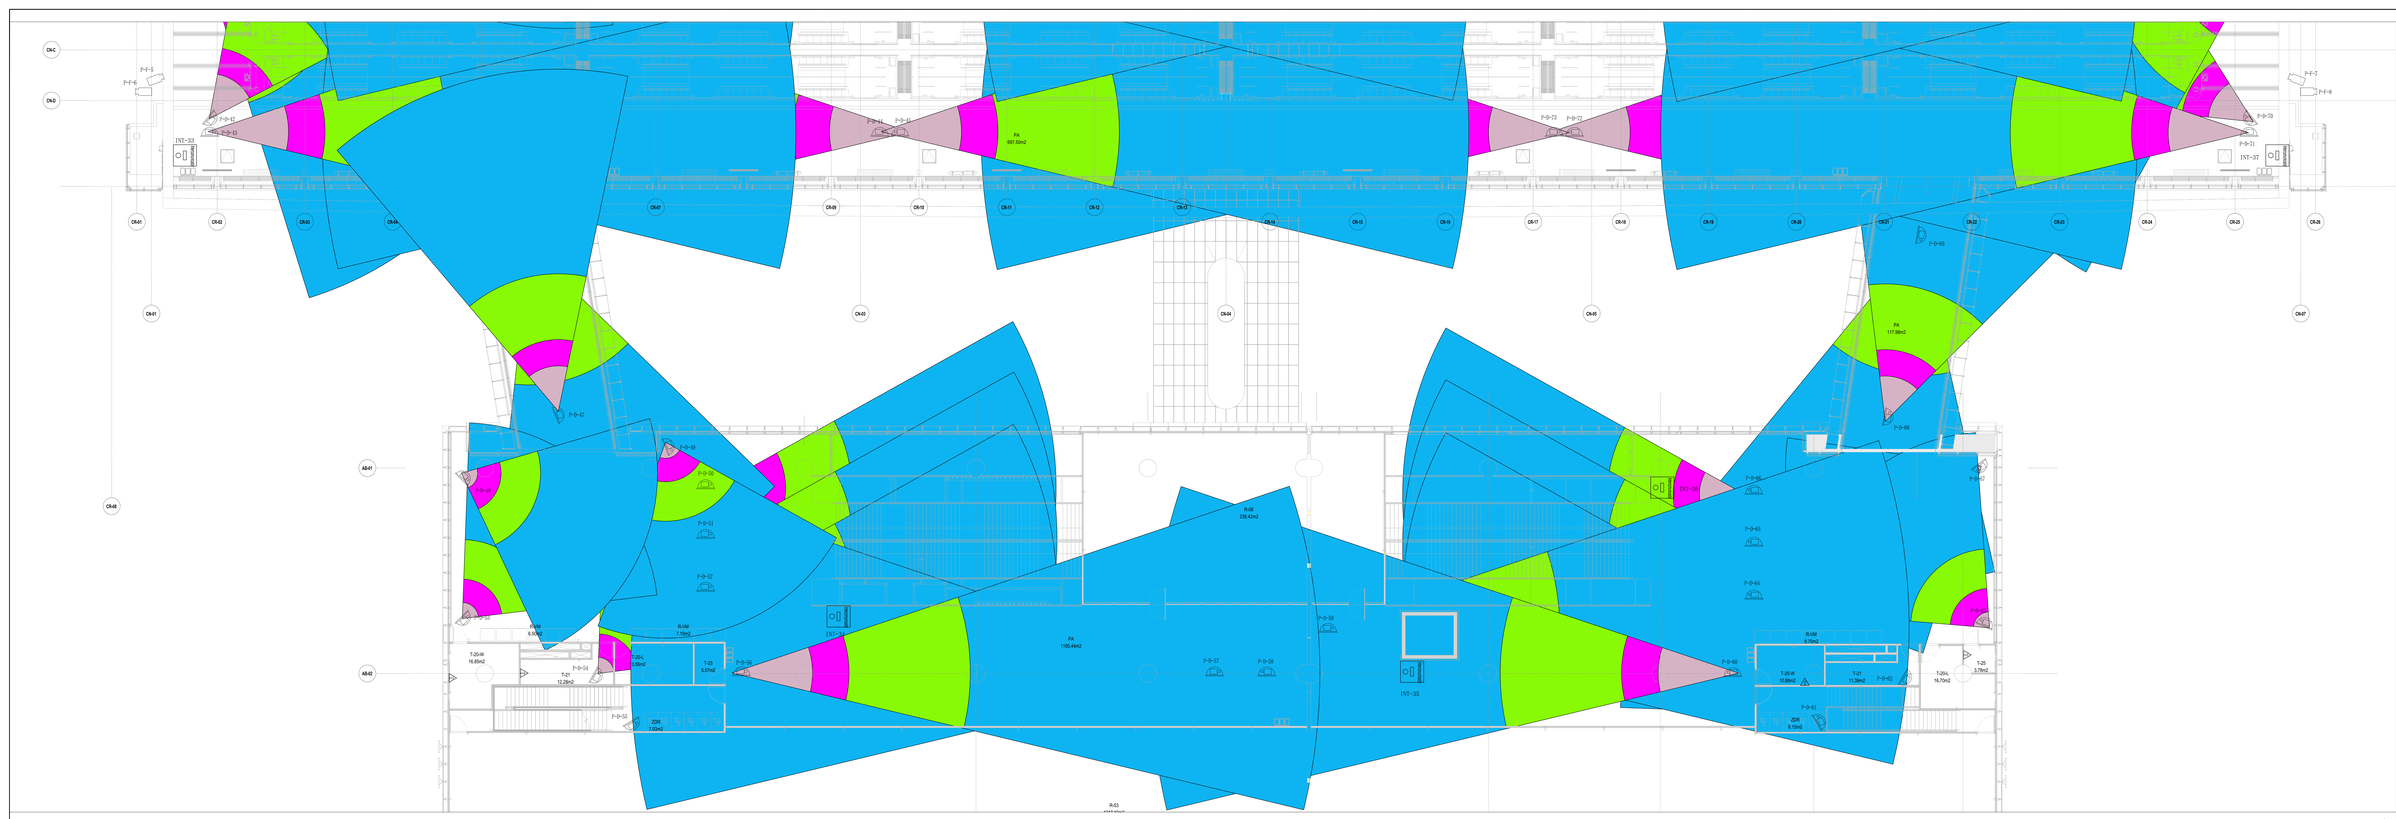

KEY PLAN

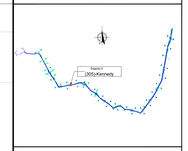

NOTAS

1.Con datos data nocturna pulir con el sistema de dueño de L-TT-1-5445-003-CON-ED-IND-IN-0001 y L-TT-1-5445-003-CON-ED-IND-IN-0002.
2.Para efectuar de equipo, consulte L-TT-1-5445-003-CON-ED-IND-ES-0001.
3.Para efectuar del cable Ethernet (indiquelo el Ethernet para los puntos de cimiento seco conectados a los equipos de cableado estructurado, consulte L-TT-1-5445-003-CON-ED-IND-ES-0001.
4.Para efectuar los cables conectados a la detección de intrusos, se incluye en los planos del ACS.
5.La información de las bandejas de cables y tuberías se refiere a los planos de CNL.
6.Los criterios de codificación de las cámaras son los siguientes.
Nivel - tipo de cámara - código de la cámara.
Nivel: Ej: P-I-01
P: como nivel del edificio.
A: como nivel de acceso.
Tipo de cámara: Ej: (Domo)
P: como nivel de plataforma.
Definición del tipo de cámara
D: como cámara domo.
F: como cámara fija.
PTZ: como cámara PTZ.
Ej:D - B1F: es una cámara fija con código 1 en el nivel del edificio.

CONVENCIONES

DESCRIPCIÓN DE LOS ICONOS

	Cámara de domo
	Cámara fija (tipo inteligente)
PTZ	Cámara PTZ
PAM	Monitor de vigilancia de pasajeros
DEC	Decodificador de vídeo
	Intercomunicador

No.	PLANOS DE REFERENCIA	REV.

No.	MODELO BIM DE REFERENCIA	REV.
1	L-TT-1-5445-003-CON-ED-ARQ-MOD-XXX7 (R) 2023-03-03	V00

No.	PAQUETE DE TRABAJO DE REFERENCIA	REV.

DISEÑO		DIBUJO		APROBÓ	
WANG KEJIA Mat.: R2022011915		ZHANG YIJIE Mat.: NÚMERO DE MATRÍCULA		ING_TÉCNICO_WSP Mat.: NÚMERO DE MATRÍCULA	
REVISÓ		MODELO BIM LID		APRO_INTEGRACIÓN_WSP	
YANG BAODONG Mat.:		WANG KEJIA Mat: R2022011915		Mat.: NÚMERO DE MATRÍCULA "Declaro que he leído y de mi entera conformidad, acepto el contenido de este documento, además, doy fe de que he cumplido con todos los requisitos establecidos en el manual de calidad de WSP"	

REVISIÓN No.	FECHA	DESCRIPCIÓN	REVISÓ	APROBÓ	APROBACIÓN CLIENTE
VCC	09/09/2022	Emitido para revisión y comentarios del diseño e Interventoría. Incluye comentarios / modificado donde se indica en el comité de semilla	T.B.	Z.Y.	
1A1	30/05/2023	Emitido para comentarios internos. Emisión preliminar para comentarios	T.B.	Z.Y.	
V00	11/10/2022	Emitido para revisión y comentarios del diseño e Interventoría	T.B.	Z.Y.	
V00	30/05/2022	Emitido para comentarios internos. Emisión preliminar para comentarios	T.B.	Z.Y.	

METRO LÍNEA 1
CONTRATO DE CONCESIÓN N.° 163 DE 2019

TELECOMUNICACIONES

PROYECTO PRIMERA LÍNEA DEL METRO DE BOGOTÁ - TRAMO 1

DIRECTOR DE INTERVENTORÍA
JAVIER ESCAMILLA N.
Mat.: 25202-69897 CND

ESPECIALISTA INTERVENTORÍA
Mat.:

FECHA
JUNIO 2023

SISTEMAS Y EQUIPOS

ESTACIÓN KENNEDY - DISEÑO DETALLADO DEL NIVEL SÓTANO

SISTEMA CCTV

CUBIERTA/N

CONTRATO No.	ESCALA	FORMATO
L-TT-1-5445-003-CON-ED-IND-PL-0009_14_VCC.dwg	1:100	ARCH D
NOMBRE DEL ARCHIVO	FECHA	REVISIÓN
L-TT-1-5445-003-CON-ED-IND-PL-0009_VCC.dwg	SEPTIEMBRE 2022	VCC

HOJA No.	DE No.
14	14