L1T1-CON-CAL-FR-0120 - B1 : 1000x707mm

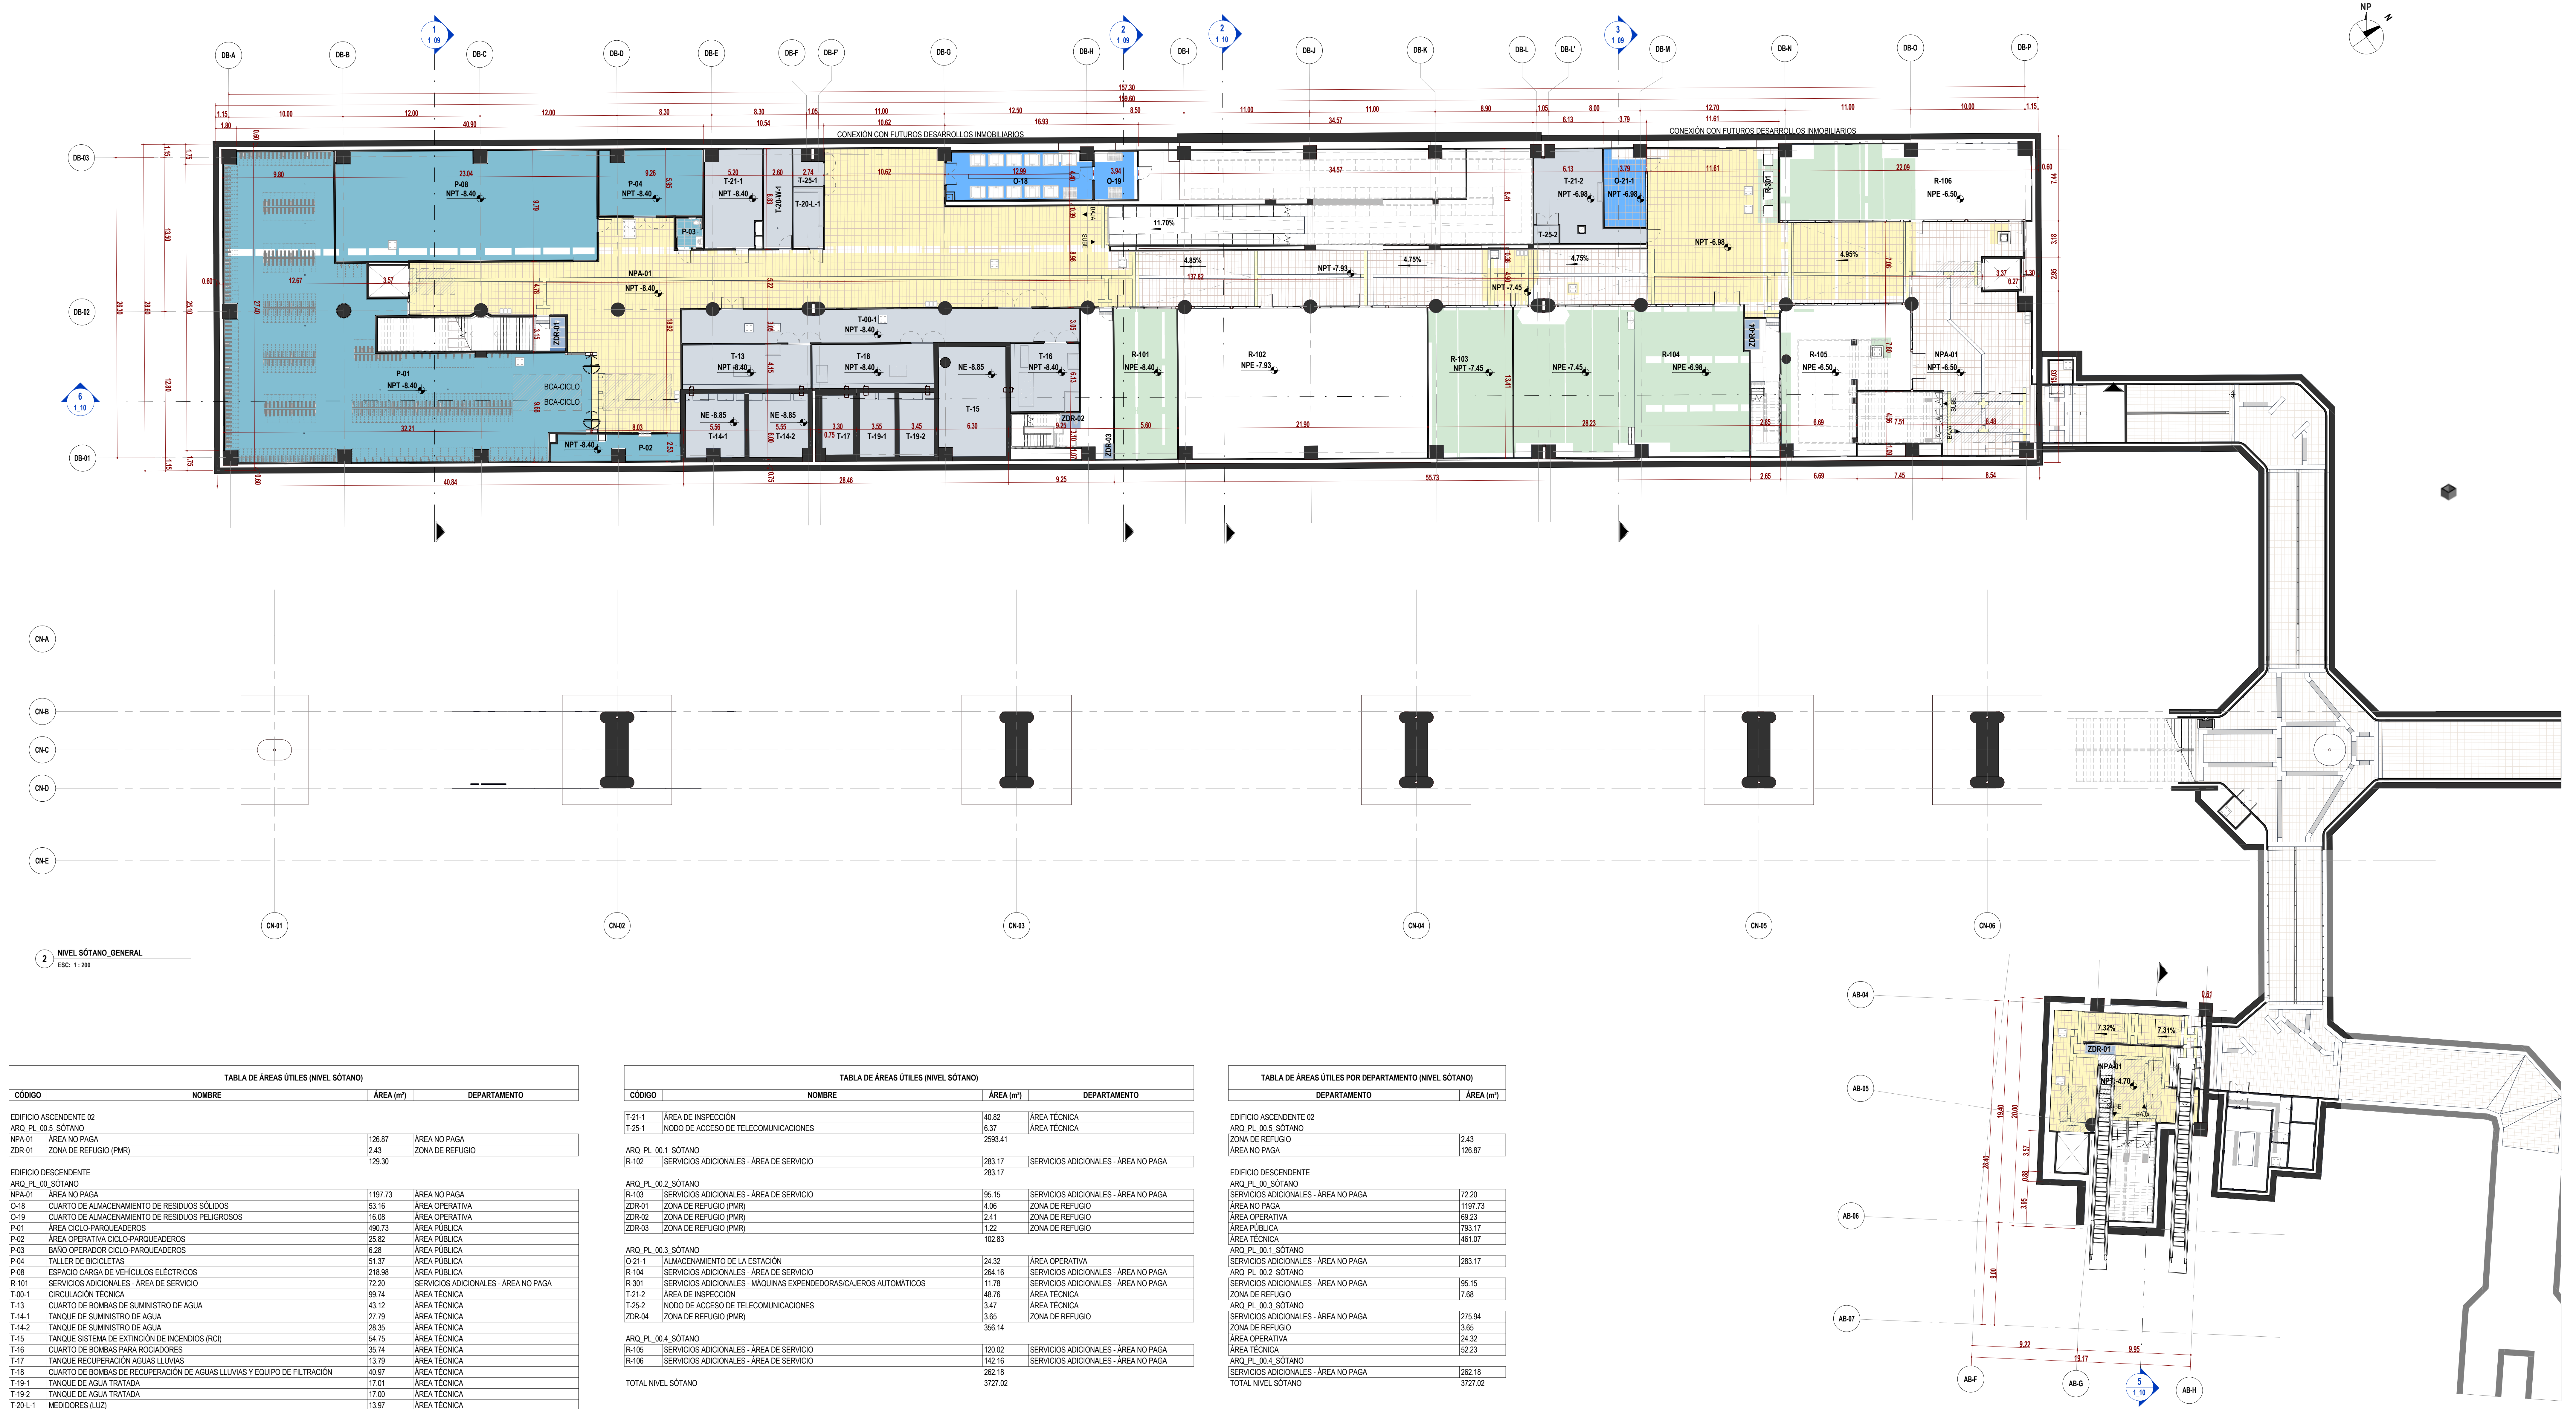
CONEXIÓN CON FUTUROS DESARROLLOS INMOBILIARIOS
CONEXIÓN CON FUTUROS DESARROLLOS INMOBILIARIOS
SCA-CICLO
NPA-01
CN-A
CN-B
CN-C
CN-D
CN-E
CN-01
AB-F
AB-G
AB-H

2 NIVEL SÓTANO_GENERAL
ESC: 1 : 200

TABLA DE ÁREAS ÚTILES (NIVEL SÓTANO)

CÓDIGO	NOMBRE	ÁREA (m²)	DEPARTAMENTO
EDIFICIO ASCENDENTE 02			
ARQ_PL_00.5_SÓTANO			
NPA-01	ÁREA NO PAGA	126.87	ÁREA NO PAGA
ZDR-01	ZONA DE REFUGIO (PMR)	2.43	ZONA DE REFUGIO
		129.30	
EDIFICIO DESCENDENTE			
ARQ_PL_00_SÓTANO			
NPA-01	ÁREA NO PAGA	1197.73	ÁREA NO PAGA
O-18	CUARTO DE ALMACENAMIENTO DE RESIDUOS SÓLIDOS	53.16	ÁREA OPERATIVA
O-19	CUARTO DE ALMACENAMIENTO DE RESIDUOS PELIGROSOS	16.08	ÁREA OPERATIVA
P-01	ÁREA CICLO-PARQUEADEROS	490.73	ÁREA PÚBLICA
P-02	ÁREA OPERATIVA CICLO-PARQUEADEROS	25.82	ÁREA PÚBLICA
P-03	BAÑO OPERADOR CICLO-PARQUEADEROS	6.28	ÁREA PÚBLICA
P-04	TALLER DE BICICLETAS	51.37	ÁREA PÚBLICA
P-08	ESPACIO CARGA DE VEHÍCULOS ELÉCTRICOS	218.98	ÁREA PÚBLICA
R-101	SERVICIOS ADICIONALES - ÁREA DE SERVICIO	72.20	SERVICIOS ADICIONALES - ÁREA NO PAGA
T-00-1	CIRCULACIÓN TÉCNICA	99.74	ÁREA TÉCNICA
T-13	CUARTO DE BOMBAS DE SUMINISTRO DE AGUA	43.12	ÁREA TÉCNICA
T-14-1	TANQUE DE SUMINISTRO DE AGUA	27.79	ÁREA TÉCNICA
T-14-2	TANQUE DE SUMINISTRO DE AGUA	28.35	ÁREA TÉCNICA
T-15	TANQUE SISTEMA DE EXTINCIÓN DE INCENDIOS (RCI)	54.75	ÁREA TÉCNICA
T-16	CUARTO DE BOMBAS PARA ROCIADORES	35.74	ÁREA TÉCNICA
T-17	TANQUE RECUPERACIÓN AGUAS LLUVIAS	13.79	ÁREA TÉCNICA
T-18	CUARTO DE BOMBAS DE RECUPERACIÓN DE AGUAS LLUVIAS Y EQUIPO DE FILTRACIÓN	40.97	ÁREA TÉCNICA
T-19-1	TANQUE DE AGUA TRATADA	17.01	ÁREA TÉCNICA
T-19-2	TANQUE DE AGUA TRATADA	17.00	ÁREA TÉCNICA
T-20-L-1	MEDIDORES (LUZ)	13.97	ÁREA TÉCNICA
T-20-W-1	MEDIDORES (AGUA)	21.66	ÁREA TÉCNICA
T-21-1	ÁREA DE INSPECCIÓN	40.82	ÁREA TÉCNICA
T-25-1	NODO DE ACCESO DE TELECOMUNICACIONES	6.37	ÁREA TÉCNICA
		2593.41	
ARQ_PL_00.1_SÓTANO			
R-102	SERVICIOS ADICIONALES - ÁREA DE SERVICIO	283.17	SERVICIOS ADICIONALES - ÁREA NO PAGA
		283.17	
ARQ_PL_00.2_SÓTANO			
R-103	SERVICIOS ADICIONALES - ÁREA DE SERVICIO	95.15	SERVICIOS ADICIONALES - ÁREA NO PAGA
ZDR-01	ZONA DE REFUGIO (PMR)	4.06	ZONA DE REFUGIO
ZDR-02	ZONA DE REFUGIO (PMR)	2.41	ZONA DE REFUGIO
ZDR-03	ZONA DE REFUGIO (PMR)	1.22	ZONA DE REFUGIO
		102.83	
ARQ_PL_00.3_SÓTANO			
O-21-1	ALMACENAMIENTO DE LA ESTACIÓN	24.32	ÁREA OPERATIVA
R-104	SERVICIOS ADICIONALES - ÁREA DE SERVICIO	264.16	SERVICIOS ADICIONALES - ÁREA NO PAGA
R-301	SERVICIOS ADICIONALES - MÁQUINAS EXPENDEDORAS/CAJEROS AUTOMÁTICOS	11.78	SERVICIOS ADICIONALES - ÁREA NO PAGA
T-21-2	ÁREA DE INSPECCIÓN	48.76	ÁREA TÉCNICA
T-25-2	NODO DE ACCESO DE TELECOMUNICACIONES	3.47	ÁREA TÉCNICA
ZDR-04	ZONA DE REFUGIO (PMR)	3.65	ZONA DE REFUGIO
		356.14	
ARQ_PL_00.4_SÓTANO			
R-105	SERVICIOS ADICIONALES - ÁREA DE SERVICIO	120.02	SERVICIOS ADICIONALES - ÁREA NO PAGA
R-106	SERVICIOS ADICIONALES - ÁREA DE SERVICIO	142.16	SERVICIOS ADICIONALES - ÁREA NO PAGA
		262.18	
TOTAL NIVEL SÓTANO		3727.02	

TABLA DE ÁREAS ÚTILES POR DEPARTAMENTO (NIVEL SÓTANO)

DEPARTAMENTO	ÁREA (m²)
EDIFICIO ASCENDENTE 02	
ARQ_PL_00.5_SÓTANO	
ZONA DE REFUGIO	2.43
ÁREA NO PAGA	126.87
EDIFICIO DESCENDENTE	
ARQ_PL_00_SÓTANO	
SERVICIOS ADICIONALES - ÁREA NO PAGA	72.20
ÁREA NO PAGA	1197.73
ÁREA OPERATIVA	69.23
ÁREA PÚBLICA	793.17
ÁREA TÉCNICA	461.07
ARQ_PL_00.1_SÓTANO	
SERVICIOS ADICIONALES - ÁREA NO PAGA	283.17
ARQ_PL_00.2_SÓTANO	
SERVICIOS ADICIONALES - ÁREA NO PAGA	95.15
ZONA DE REFUGIO	7.68
ARQ_PL_00.3_SÓTANO	
SERVICIOS ADICIONALES - ÁREA NO PAGA	275.94
ZONA DE REFUGIO	3.65
ÁREA OPERATIVA	24.32
ÁREA TÉCNICA	52.23
ARQ_PL_00.4_SÓTANO	
SERVICIOS ADICIONALES - ÁREA NO PAGA	262.18
TOTAL NIVEL SÓTANO	3727.02

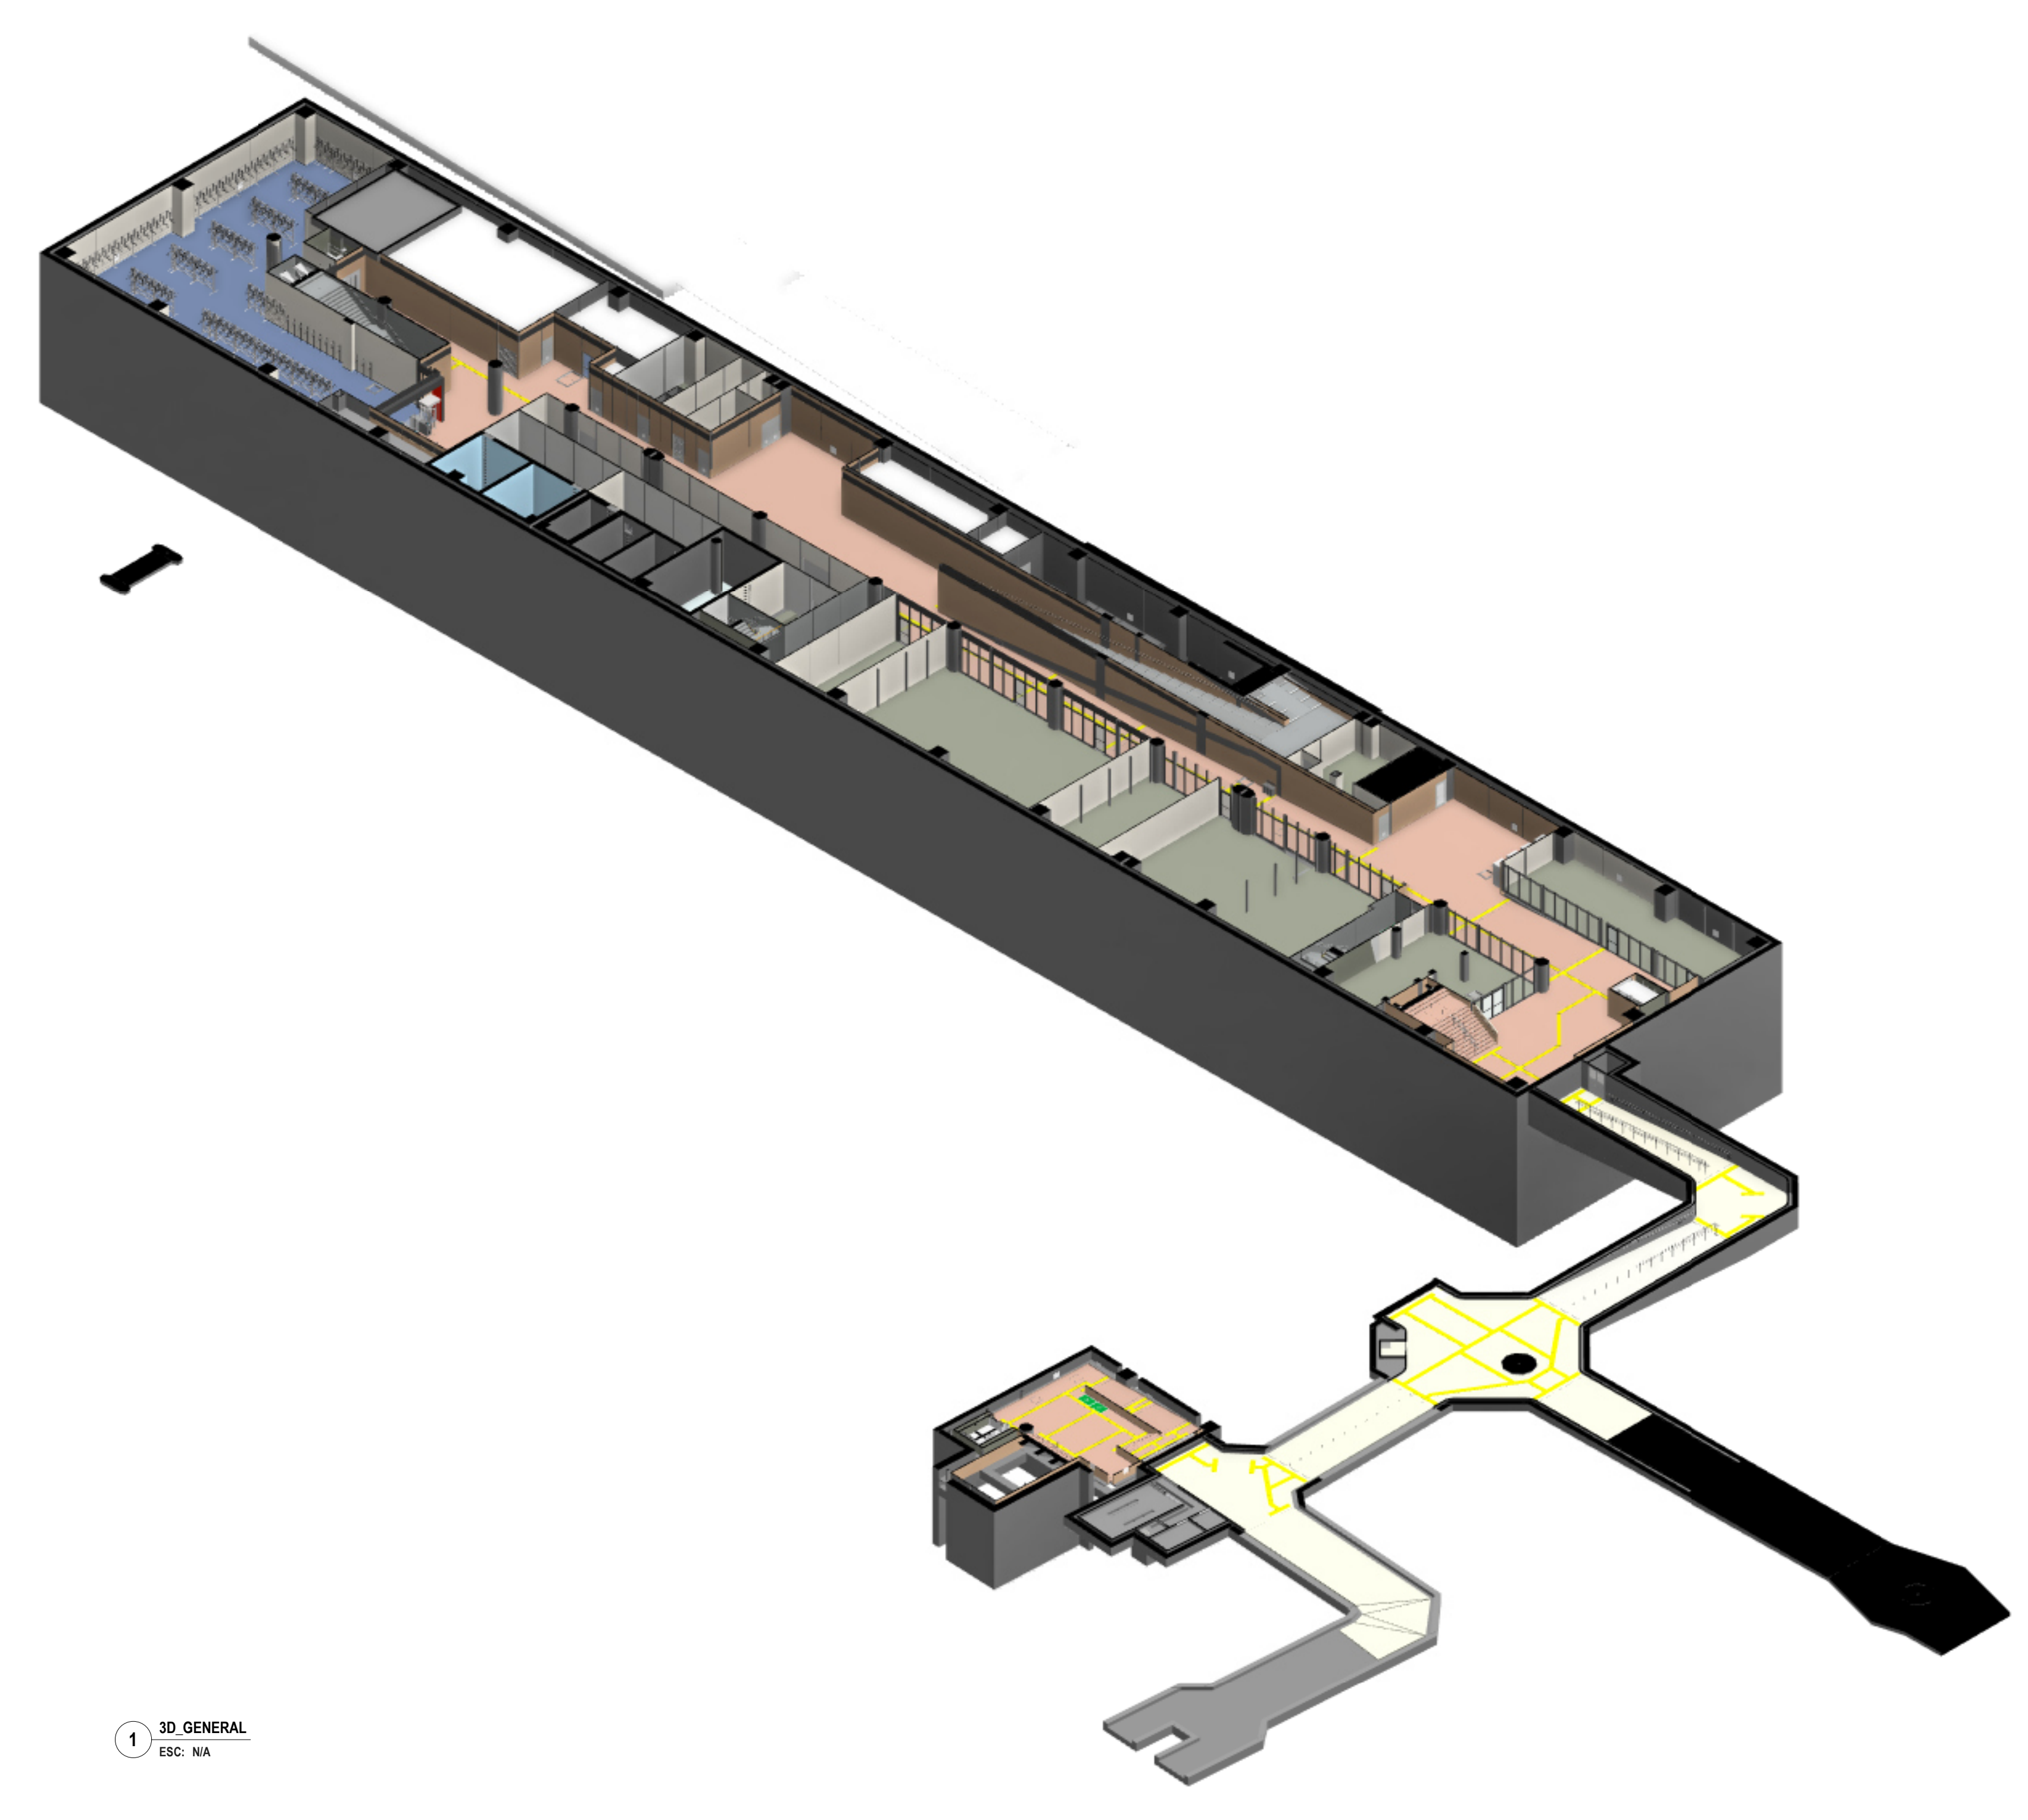

1 3D_GENERAL
ESC: N/A

TABLA DE CICLO-PARQUEADEROS ESPECÍFICA

DESCRIPCIÓN	CANTIDAD (und)	USUARIOS
ARQ_PL_00_SÓTANO		
BICIPARQUEADERO ASISTIDO EN ACERO INOXIDABLE ASTM A240, a=0.70m X l=1.20m, h=1.70m.	1	EMPLEADOS
BICIPARQUEADERO DE COLGAR, 2 PUESTOS, a=1.20m X l=0.70m, h=2.40m. ACABADO EN PINTURA ELECTROSTÁTICA COLOR RAL9005 "NEGRO INTENSO".	4	EMPLEADOS
EMPLEADOS	5	
BICIPARQUEADERO ASISTIDO EN ACERO INOXIDABLE ASTM A240, a=0.70m X l=1.20m, h=1.70m.	36	VISITANTE
BICIPARQUEADERO DE COLGAR DE 6 PUESTOS EN ACERO, a=1.20m X l=2.10m, h=2.40m. ACABADO EN PINTURA ELECTROSTÁTICA COLOR RAL9005 "NEGRO INTENSO".	306	VISITANTE
BICIPARQUEADERO DE COLGAR, 1 PUESTO, a=1.20m X l=0.70m, h=2.40m. ACABADO EN PINTURA ELECTROSTÁTICA COLOR RAL9005 "NEGRO INTENSO".	12	VISITANTE
BICIPARQUEADERO DE COLGAR, 2 PUESTOS, a=1.20m X l=0.70m, h=2.40m. ACABADO EN PINTURA ELECTROSTÁTICA COLOR RAL9005 "NEGRO INTENSO".	18	VISITANTE
VISITANTE	372	
TOTAL CUPOS	377	

LOCALIZACIÓN

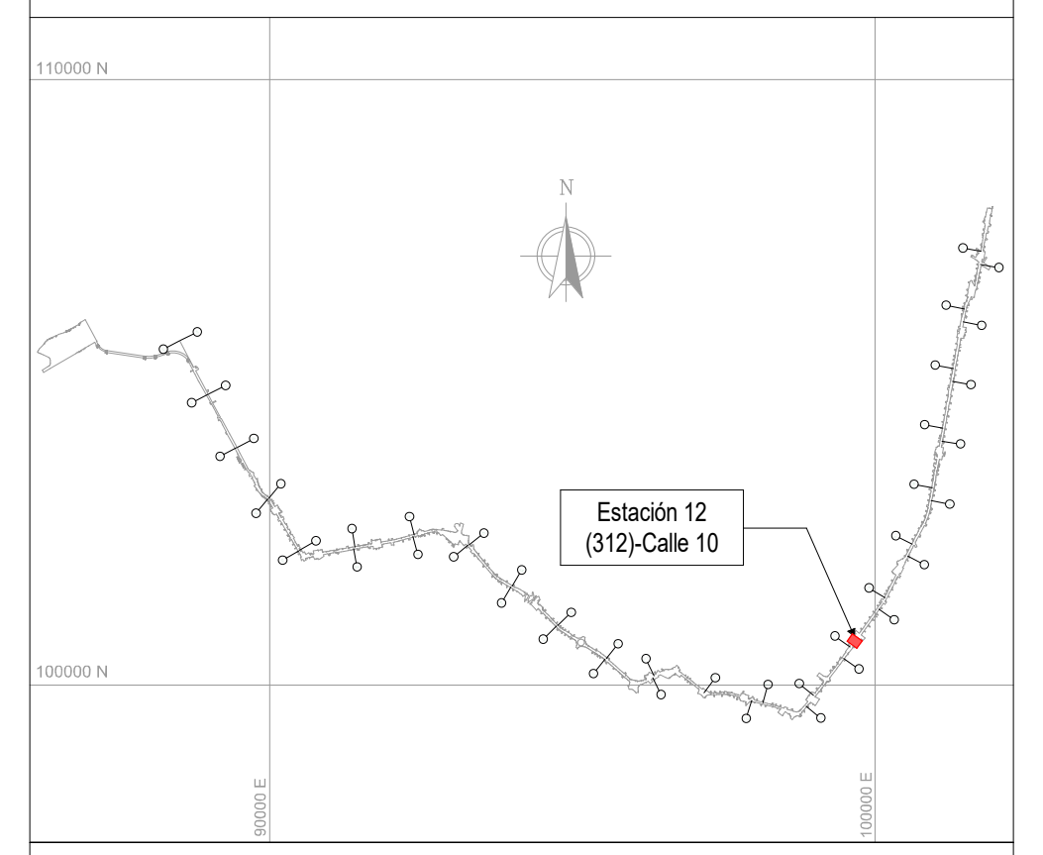

NOTAS

01 TODAS LAS DIMENSIONES ESTÁN CONFIGURADAS EN METROS A MENOS QUE SE INDIQUE UNA UNIDAD DE MEDIDA DIFERENTE.

02 TODAS LAS MEDIDAS, UBICACIÓN Y NIVELES DEBEN VERIFICARSE EN EL LUGAR DE CONSTRUCCIÓN.

03 EL NIVEL DE ACCESO AL EDIFICIO PL 01 CORRESPONDE AL +0,00 DE LA ESTACIÓN Y REFERENCIA AL NIVEL 2589.25 M.S.N.M.

04 LOS NOMBRES ESPECÍFICOS DE LAS ÁREAS PUEDEN SER CONSULTADAS EN EL PLANO NO. 3 Ó EN LAS VISTAS EN PLANTA.

05 LOS COLORES QUE SE MUESTRAN EN LOS PLANOS COMO PROYECCIÓN DE ELEMENTOS ARQUITECTÓNICOS COMO CUBIERTAS FACHADAS MUROS ETC. NO REPRESENTAN LA MATERIALIDAD Y REALIDAD DE ACABADOS DEL PROYECTO, SOLO SON INDICATIVOS PARA REALIZAR UNA CORRECTA LECTURA DE LA PLANIMETRÍA.

06 SE DEBEN REVISAR LOS NIVELES ESTRUCTURALES PARA NIVEL DE ACCESO PL_01 Y SUBNIVELES, PL_02 (INTERMEDIO), PL_03 (PLATAFORMA) CON LA PLANIMETRÍA DE PLACAS ESTRUCTURALES EN LOS ENTREGABLES L1T1-1300-412-CON-ED-EST-PL-0045, 86, 88, 129, 130, 131, 134, 135, 136, RESPECTIVAMENTE. EL NIVEL ESTRUCTURAL (NE) REFERENCIA LOS ESPACIOS DONDE SE DEBE ACONDICIONAR EL ACABADO DE PISO SEGÚN CORRESPONDA, CON LOS NIVELES DE PISO TERMINADO (NPT). LOS NIVELES PROYECTADOS DE EMPATE (NPE) EN LAS ÁREAS DE SERVICIOS ADICIONALES, REFERENCIAN LA ADECUACIÓN DE LOS DESNIVELES EN ESTAS ÁREAS; QUEDA COMO RESPONSABILIDAD DEL LOCATARIO DEFINIR Y ACONDICIONAR ESTE ACABADO DE PISO (NPE) EN LÍNEA CON EL NIVEL (NPT) DE ESPACIOS COLINDANTES. EL NIVEL ESTRUCTURAL (NE) SE ENCUENTRA A (- 0.10M) POR DEBAJO DE LOS NIVELES DE PISO TERMINADO (NPT) Y LOS NIVELES PROYECTADOS DE EMPATE (NPE) MARCADOS EN LA PLANIMETRÍA.

07 RESPECTO A LAS ÁREAS CONSTRUIDAS Y DE ACUERDO CON LA COMUNICACIÓN EXTS22-0002544 DE EMB, SE IDENTIFICA QUE EL CONCESIONARIO SE ENCUENTRA BUSCANDO ESTRATEGIAS PARA MEJORAR EL DISEÑO CON EL PROGRAMA ARQUITECTÓNICO, UNA DE ESTAS ESTRATEGIAS ES MEJORAR EL FUNCIONAMIENTO DEL DISEÑO URBANO Y BRINDAR UNA SOLUCIÓN INTEGRAL RESPECTO A LOS INMUEBLES DE INTERÉS CULTURAL. DE ACUERDO CON LO ANTERIOR, PARA LA EMB, ESTAS ACTIVIDADES OBEDECEN AL PROCESO NATURAL DE LOS ESTUDIOS Y DISEÑOS DEFINITIVOS QUE DEBE DESARROLLAR METRO LÍNEA 1.

- ARQ_PL_00 = SÓTANO / NPT -8.40m
- ARQ_PL_00.1 = SÓTANO / NPT -7.93m
- ARQ_PL_00.2 = SÓTANO / NPT -7.45m
- ARQ_PL_00.3 = SÓTANO / NPT -6.98m
- ARQ_PL_00.4 = SÓTANO / NPT -6.50m
- ARQ_PL_00.5 = SÓTANO / NPT -4.70m
- ARQ_PL_00.1 = ACCESO / NPT -2.40m
- ARQ_PL_00.2 = ACCESO / NPT -2.10m
- ARQ_PL_00.3 = ACCESO / NPT -1.85m
- ARQ_PL_00.4 = ACCESO / NPT -1.65m
- ARQ_PL_00.5 = ACCESO / NPT -1.45m
- ARQ_PL_00.6 = ACCESO / NPT -1.25m
- ARQ_PL_00.7 = ACCESO / NPT -0.85m
- ARQ_PL_00.8 = ACCESO / NPT -0.45m
- ARQ_PL_00.9 = ACCESO / NPT -0.20m
- ARQ_PL_00.10 = ACCESO / NPT -0.15m
- ARQ_PL_01 = ACCESO / NPT 0.00m
- ARQ_PL_01.1 = ACCESO / NPT 0.97m
- ARQ_PL_02 = INTERMEDIO / NPT 6.75m
- ARQ_PL_02.2 = TOPE DE RIEL (TOR) / NPT 14.35m
- ARQ_PL_03 = PLATAFORMA / NPT 15.49m
- ARQ_PL_04 = CUBIERTA EDIFICACIONES / NPT 22.09m
- ARQ_PL_05 = CUBIERTA NAVE CENTRAL / NPT 24.75m

CONVENCIONES

🟩	SERVICIOS ADICIONALES ÁREA NO PAGA	🟨	ÁREA NO PAGA
🟩	SERVICIOS ADICIONALES ÁREA PAGA	🟦	ÁREA OPERATIVA
🟩	SERVICIO PÚBLICO	🟧	ÁREA PAGA
🟦	ZONA DE REFUGIO	🟦	ÁREA PÚBLICA
🟥	ÁREA CULTURAL	⬜	ÁREA TÉCNICA
🟩	CADE		

No.	PLANOS DE REFERENCIA	REV.

No.	MODELO BIM DE REFERENCIA	REV.
1	L1T1-1100-212-CON-ED-EST-MO-0001.rvt	V00
2	L1T1-1100-213-CON-ED-EST-MO-0001.rvt	V00
3	L1T1-1100-312-CON-ED-EST-MO-0001.rvt	V00
4	L1T1-1150-212-CON-ED-EST-MO-0001.rvt	V00
5	L1T1-1150-213-CON-ED-EST-MO-0001.rvt	V00
6	L1T1-1150-312-CON-ED-EST-MO-0001.rvt	V00
7	L1T1-1200-312-CON-ED-EST-MO-0001.rvt	V00
8	L1T1-1300-412-CON-ED-EST-MO-0001.rvt	V00
9	L1T1-1300-412-CON-ED-EST-MO-0002.rvt	V00
10	L1T1-1300-412-CON-ED-EST-MO-0003.rvt	V00
11	L1T1-1310-412-CON-ED-EST-MO-0001.rvt	V00
12	L1T1-1410-312-CON-ED-MEC-MO-0001.rvt	V00
13	L1T1-1420-312-CON-ED-MEC-MO-0001.rvt	V00
14	L1T1-2320-584-CON-ED-EST-MO-0001.rvt	V00
15	L1T1-2330-584-CON-ED-ARQ-MO-0001.rvt	V00
16	L1T1-2430-551-CON-ED-ARQ-MO-0001.rvt	V00
17	L1T1-2430-551-CON-ED-EST-MO-0001.rvt	V00
18	L1T1-5160-312-CON-ED-ARQ-MO-0001.rvt	V00
19	L1T1-5160-312-CON-ED-EST-MO-0001.rvt	V00
20	L1T1-5300-312-CON-ED-MEC-MO-0001.rvt	V00
21	L1T1-5600-312-CON-ED-INS-MO-0001.rvt	V00
22	L1T1-1330-412-CON-ED-ARQ-MO-0011.rvt	V00
23	L1T1-1330-412-CON-ED-ARQ-MO-0012.rvt	V00
24	L1T1-1330-412-CON-ED-ARQ-MO-0013.rvt	V00

No.	PAQUETE DE TRABAJO DE REFERENCIA	REV.
1	XREF-URBANISM_CONTEXT_ST12.rvt	
2	XREF-SECONDARY-STRUCTURE-ST12.rvt	

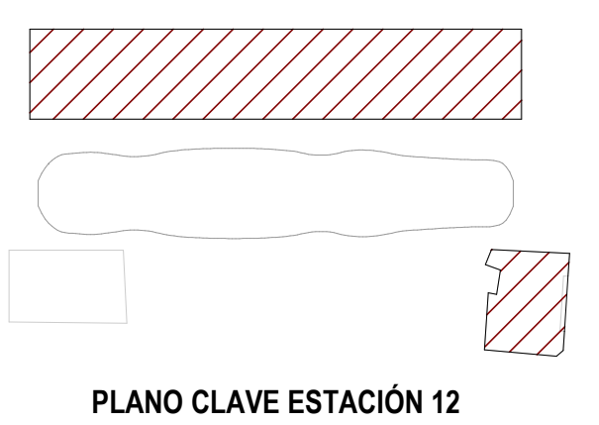

PLANO CLAVE ESTACIÓN 12

0 2 10m
1:200

VÁLIDO PARA CONSTRUCCIÓN
31-03-26

METRO BOGOTÁ
GCS Consorcio Consultores PMO Bogotá
CONSORCIO SUPERVISOR PLMB
CHEC

DISEÑÓ:
REN ZHENHUA
Licencia de Arq.nivel I (China): 1101735-614

APROBÓ:
DIEGO ERNESTO DUEÑAS
Mat.: 25202-53876 CND

REVISÓ:
CARLOS MAURICIO BARRETO BARBOSA
Mat.: A4012012-14139353

DIBUJÓ:
EQUIPO CHEC

REVISIÓN No.	FECHA	DESCRIPCIÓN	REVISÓ	APROBÓ	APROBACIÓN CLIENTE
V02	31/03/2026	EMITIDO PARA CONSTRUCCIÓN	C.M.B.B	D.E.D	
V01	16/07/2025	REVISIÓN NO OBJETADA - EMITIDO PARA CONSTRUCCIÓN	F.B.R	M.M.R	
VB1	20/03/2025	EMITIDO PARA REVISIÓN Y COMENTARIOS DEL CLIENTE E INTERVENTORÍA	F.B.R	E.O.M	
V00	13/02/2025	REVISIÓN NO OBJETADA - EMITIDO PARA CONSTRUCCIÓN	F.B.R	E.O.M	
VGG	18/10/2024	EMITIDO PARA REVISIÓN Y COMENTARIOS DEL CLIENTE E INTERVENTORÍA - INCLUYE COMENTARIOS /(AJUSTES V2)	F.B.R	E.O.M	
VFF	21/05/2024	EMITIDO PARA REVISIÓN Y COMENTARIOS DEL CLIENTE E INTERVENTORÍA - INCLUYE COMENTARIOS /(AJUSTES)	F.B.R	E.O.M	
VEE	25/01/2023	EMITIDO PARA REVISIÓN Y COMENTARIOS DEL CLIENTE E INTERVENTORÍA - INCLUYE COMENTARIOS /(90% ACCESOS)	J.E.M	M.B.M	
VDD	18/12/2022	EMITIDO PARA REVISIÓN Y COMENTARIOS DEL CLIENTE E INTERVENTORÍA - INCLUYE COMENTARIOS /(NAVE CENTRAL)	J.E.M	M.B.M	
VCC	22/08/2022	EMITIDO PARA REVISIÓN Y COMENTARIOS DEL CLIENTE E INTERVENTORÍA - INCLUYE COMENTARIOS /(ENTREGA 90%)	J.E.M	M.B.M	
VBB	06/12/2021	EMITIDO PARA REVISIÓN Y COMENTARIOS DEL CLIENTE E INTERVENTORÍA	J.E.M	M.B.M	

METRO LÍNEA 1

DIRECTOR DE INTERVENTORÍA:
JAVIER DESCARGA N.
Mat.:25202-68697 CND

ESPECIALISTA INTERVENTORÍA:
CARLOS ALBERTO HOYOS SOTO
Mat.:A25072000-14251682

FECHA:
MARZO 2026

METRO LÍNEA 1
CONTRATO DE CONCESIÓN No. 163 DE 2019

PROYECTO PRIMERA LÍNEA DEL METRO DE BOGOTÁ - TRAMO 1

INFRAESTRUCTURA VIAL

ARQUITECTURA

ESTACIÓN METRO 12 - (CALLE 10)
EDIFICIO DESCENDENTE
VISTA EN PLANTA Y 3D - NIVEL SÓTANO

PLANCHA No: L1T1-0000-312-CON-ED-ARQ-PL-0001_04_V02
ARCHIVO: L1T1-0000-312-CON-ED-ARQ-MO-0001_V01.rvt
ESCALA: INDICADA
FECHA: JUNIO 2021
REVISIÓN No. V02
PLANO No. 04 DE 100