L1T1-CON-CAL-FR-0120 - B1 : 1000x707mm

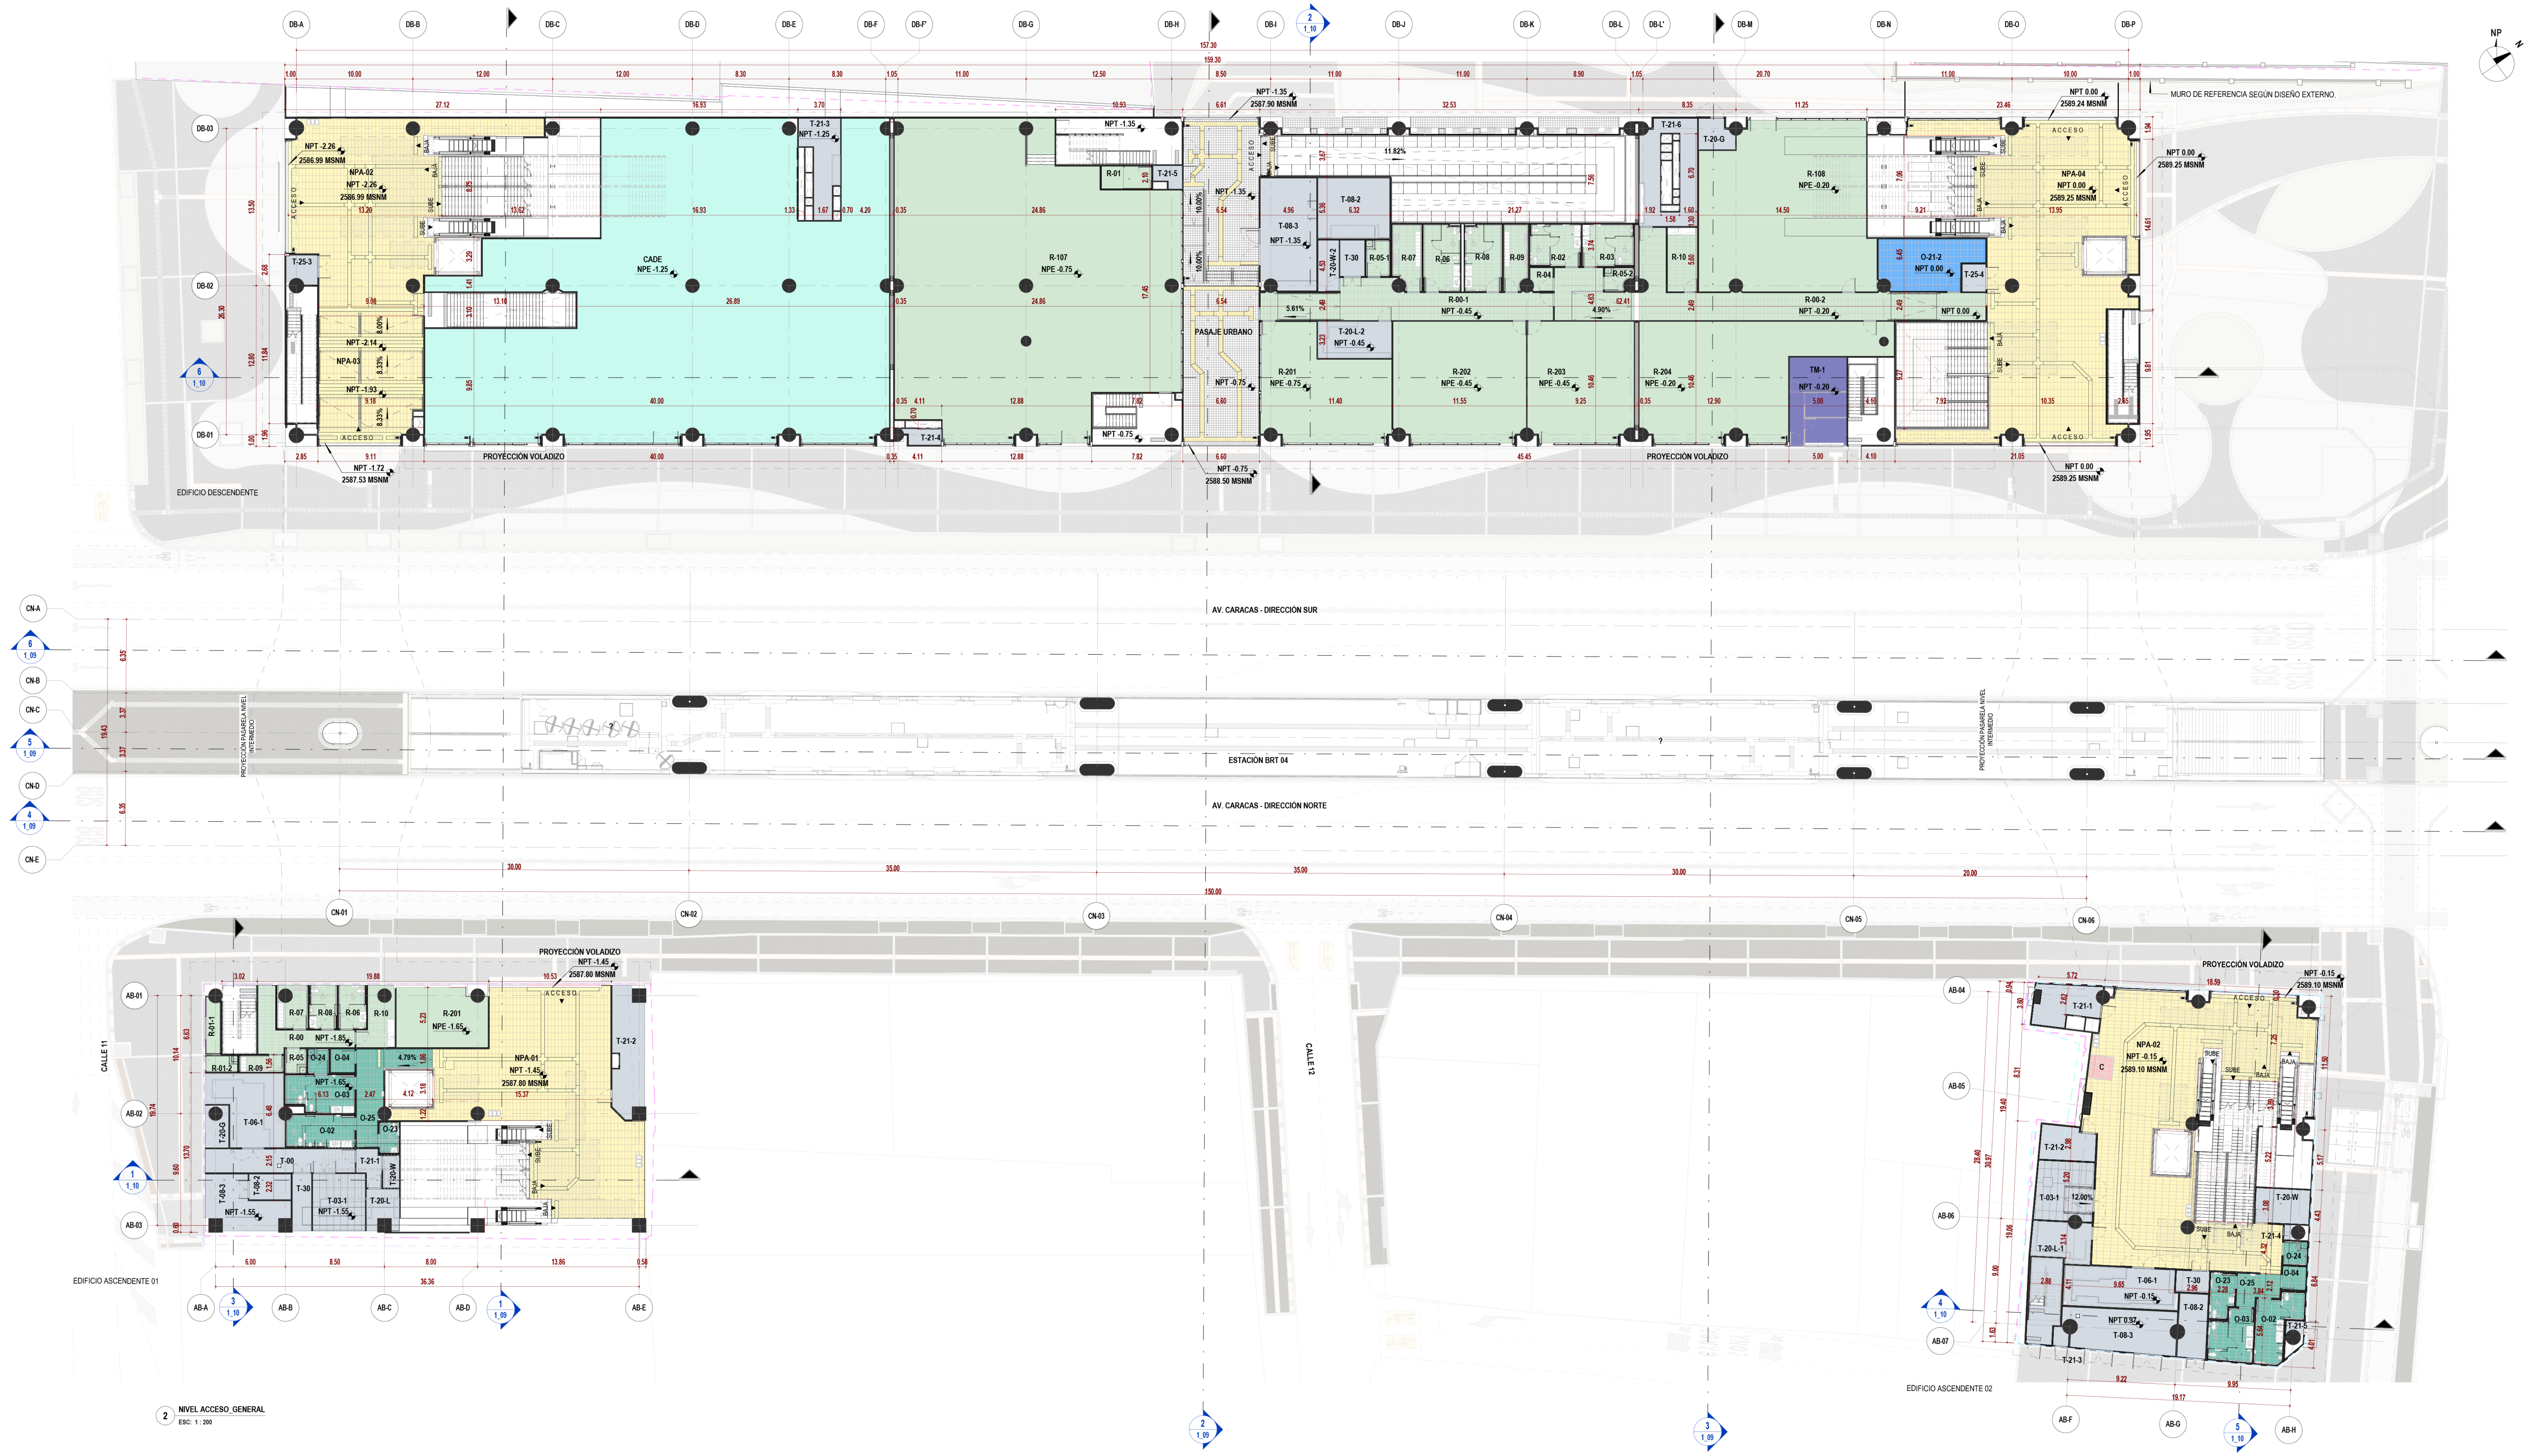
DB-A
DB-B
DB-C
DB-D
DB-E
DB-F
DB-F'
DB-G
DB-H
DB-I
DB-J
DB-K
DB-L
DB-L'
DB-M
DB-N
DB-O
DB-P
DB-01
DB-02
DB-03
157.30
159.30
MURO DE REFERENCIA SEGÚN DISEÑO EXTERNO.
NPT -2.26 2586.99 MSNM
NPA-02 NPT -2.26 2586.99 MSNM
ACCESO
BAJA
SUBE
T-25-3
NPT -2.14
NPA-03
NPT -1.93
8.00%
8.33%
NPT -1.72 2587.53 MSNM
CADE NPE -1.25
T-21-3 NPT -1.25
R-107 NPE -0.75
NPT -1.35
R-01
T-21-5
T-21-4
NPT -0.75
PASAJE URBANO
NPT -0.75 2588.50 MSNM
NPT -1.35 2587.90 MSNM
11.82%
T-08-2
T-08-3 NPT -1.35
T-20-W-2
T-30
R-05-1
R-07
R-06
R-08
R-09
R-02
R-03
R-04
R-05-2
R-00-1 NPT -0.45
5.61%
4.90%
T-20-L-2 NPT -0.45
R-201 NPE -0.75
R-202 NPE -0.45
R-203 NPE -0.45
R-204 NPE -0.20
T-21-6
T-20-G
R-10
R-108 NPE -0.20
R-00-2 NPT -0.20
TM-1 NPT -0.20
NPT 0.00 2589.24 MSNM
NPA-04 NPT 0.00 2589.25 MSNM
NPT 0.00 2589.25 MSNM
O-21-2 NPT 0.00
T-25-4
NPT 0.00
PROYECCIÓN VOLADIZO
EDIFICIO DESCENDENTE
AV. CARACAS - DIRECCIÓN SUR
ESTACIÓN BRT 04
AV. CARACAS - DIRECCIÓN NORTE
PROYECCIÓN PASARELA NIVEL INTERMEDIO
CN-A
CN-B
CN-C
CN-D
CN-E
CN-01
CN-02
CN-03
CN-04
CN-05
CN-06
30.00
35.00
35.00
150.00
30.00
20.00
CALLE 11
CALLE 12
AB-01
AB-02
AB-03
AB-04
AB-05
AB-06
AB-07
AB-A
AB-B
AB-C
AB-D
AB-E
AB-F
AB-G
AB-H
PROYECCIÓN VOLADIZO NPT -1.45 2587.80 MSNM
R-01-1
R-01-2
R-09
R-00 NPT -1.85
R-07
R-08
R-06
R-10
R-201 NPE -1.65
R-05
O-24
O-04
4.79%
NPT -1.65
O-03
O-25
O-02
O-23
NPA-01 NPT -1.45 2587.80 MSNM
T-21-2
T-20-G
T-06-1
T-00
T-21-1
T-20-W
T-08-3
T-08-2
T-30
T-03-1
T-20-L
NPT -1.55
NPT -1.55
36.36
EDIFICIO ASCENDENTE 01
PROYECCIÓN VOLADIZO
NPT -0.15 2589.10 MSNM
T-21-1
NPA-02 NPT -0.15 2589.10 MSNM
C
T-21-2
T-03-1
12.00%
T-20-L-1
T-06-1 NPT -0.15
T-30
T-08-2
NPT 0.97
T-08-3
T-21-3
O-23
O-25
O-03
O-02
O-24
O-04
T-20-W
T-21-4
T-21-5
19.17
EDIFICIO ASCENDENTE 02

2 NIVEL ACCESO_GENERAL
ESC: 1 : 200

TABLA ÁREAS ÚTILES (NIVEL ACCESO)			
CÓDIGO	NOMBRE	ÁREA (m²)	DEPARTAMENTO
EDIFICIO ASCENDENTE 01			
ARQ_PL_00.3_ACCESO			
R-00	SERVICIOS ADICIONALES - CORREDOR OPERATIVO	19.44	SERVICIOS ADICIONALES - ÁREA NO PAGA
R-01-1	SERVICIOS ADICIONALES - CUARTO DE BASURAS PARA METRO	6.02	SERVICIOS ADICIONALES - ÁREA NO PAGA
R-01-2	SERVICIOS ADICIONALES - CUARTO DE BASURAS PARA METRO	4.04	SERVICIOS ADICIONALES - ÁREA NO PAGA
R-05	SERVICIOS ADICIONALES - CUARTO DE LIMPIEZA	3.75	SERVICIOS ADICIONALES - ÁREA NO PAGA
R-06	SERVICIOS ADICIONALES - BAÑOS EMPLEADOS MUJERES	8.61	SERVICIOS ADICIONALES - ÁREA NO PAGA
R-07	SERVICIOS ADICIONALES - VESTIDORES EMPLEADOS MUJERES	8.45	SERVICIOS ADICIONALES - ÁREA NO PAGA
R-08	SERVICIOS ADICIONALES - BAÑOS EMPLEADOS HOMBRES	8.51	SERVICIOS ADICIONALES - ÁREA NO PAGA
R-09	SERVICIOS ADICIONALES - VESTIDORES EMPLEADOS HOMBRES	5.28	SERVICIOS ADICIONALES - ÁREA NO PAGA
R-10	SERVICIOS ADICIONALES - SALA DE EMPLEADOS	14.00	SERVICIOS ADICIONALES - ÁREA NO PAGA
		78.09	
ARQ_PL_00.4_ACCESO			
O-02	BAÑOS PÚBLICOS DE HOMBRES	15.76	SERVICIO PÚBLICO
O-03	BAÑOS PÚBLICOS DE MUJERES	17.92	SERVICIO PÚBLICO
O-04	CONTROL DE ACCESO BAÑOS PÚBLICOS	4.28	SERVICIO PÚBLICO
O-23	BAÑO PÚBLICO - FAMILIAR	4.42	SERVICIO PÚBLICO
O-24	CUARTO DE LIMPIEZA DE BAÑOS PÚBLICOS	3.75	SERVICIO PÚBLICO
O-25	BAÑO PÚBLICO - CORREDOR OPERACIONAL	25.71	SERVICIO PÚBLICO
R-201	SERVICIOS ADICIONALES - ÁREA DE COMIDAS	38.64	SERVICIOS ADICIONALES - ÁREA NO PAGA
T-00	CIRCULACIÓN TÉCNICA	26.26	ÁREA TÉCNICA
T-03-1	LOCAL SECUNDARIO DE TELECOMUNICACIONES	22.17	ÁREA TÉCNICA
T-06-1	LOCAL SECUNDARIO DE TABLEROS	34.97	ÁREA TÉCNICA
T-08-2	CENTRO DE TRANSFORMACIÓN ENEL-CODENSA (CT)_CUARTO BAJA TENSIÓN	7.92	ÁREA TÉCNICA
T-08-3	CENTRO DE TRANSFORMACIÓN ENEL-CODENSA (CT)_CUARTO MEDIA TENSIÓN	24.95	ÁREA TÉCNICA
T-20-G	MEDIDORES (GAS)	5.90	ÁREA TÉCNICA
T-20-L	MEDIDORES (LUZ)	8.88	ÁREA TÉCNICA
T-20-W	MEDIDORES (AGUA)	3.93	ÁREA TÉCNICA
T-21-1	ÁREA DE INSPECCIÓN	5.99	ÁREA TÉCNICA
T-30	SISTEMA PROTECCIÓN CONTRA INCENDIO ENEL	7.87	ÁREA TÉCNICA
		259.34	
ARQ_PL_00.5_ACCESO			
NPA-01	ÁREA NO PAGA	229.73	ÁREA NO PAGA
T-21-2	ÁREA DE INSPECCIÓN	27.55	ÁREA TÉCNICA
		257.28	
EDIFICIO ASCENDENTE 02			
ARQ_PL_00.10_ACCESO			
NPA-02	ÁREA NO PAGA	283.21	ÁREA NO PAGA
O-02	BAÑOS PÚBLICOS DE HOMBRES	17.44	SERVICIO PÚBLICO
O-03	BAÑOS PÚBLICOS DE MUJERES	15.32	SERVICIO PÚBLICO
O-04	CONTROL DE ACCESO BAÑOS PÚBLICOS	4.14	SERVICIO PÚBLICO
O-23	BAÑO PÚBLICO - FAMILIAR	7.64	SERVICIO PÚBLICO
O-24	CUARTO DE LIMPIEZA DE BAÑOS PÚBLICOS	4.01	SERVICIO PÚBLICO
O-25	BAÑO PÚBLICO - CORREDOR OPERACIONAL	9.00	SERVICIO PÚBLICO
T-03-1	LOCAL SECUNDARIO DE TELECOMUNICACIONES	25.84	ÁREA TÉCNICA
T-06-1	LOCAL SECUNDARIO DE TABLEROS	107.59	ÁREA TÉCNICA
T-20-L-1	MEDIDORES (LUZ)	16.13	ÁREA TÉCNICA
T-20-W	MEDIDORES (AGUA)	13.68	ÁREA TÉCNICA
T-21-1	ÁREA DE INSPECCIÓN	16.72	ÁREA TÉCNICA
T-21-2	ÁREA DE INSPECCIÓN	13.02	ÁREA TÉCNICA
T-21-4	ÁREA DE INSPECCIÓN	0.85	ÁREA TÉCNICA
T-30	SISTEMA PROTECCIÓN CONTRA INCENDIO ENEL	5.20	ÁREA TÉCNICA
		539.78	
ARQ_PL_01_ACCESO			
C	ÁREAS DE USO CULTURAL	4.00	ÁREA CULTURAL
		4.00	
ARQ_PL_01.1_ACCESO			
T-08-2	CENTRO DE TRANSFORMACIÓN ENEL-CODENSA (CT)_CUARTO BAJA TENSIÓN	12.76	ÁREA TÉCNICA
T-08-3	CENTRO DE TRANSFORMACIÓN ENEL-CODENSA (CT)_CUARTO MEDIA TENSIÓN	32.52	ÁREA TÉCNICA
T-21-3	ÁREA DE INSPECCIÓN	1.93	ÁREA TÉCNICA
T-21-5	ÁREA DE INSPECCIÓN	1.43	ÁREA TÉCNICA
		48.64	
EDIFICIO DESCENDENTE			
ARQ_PL_00.1_ACCESO			
NPA-02	ÁREA NO PAGA	202.89	ÁREA NO PAGA
NPA-03	ÁREA NO PAGA	93.86	ÁREA NO PAGA
T-25-3	NODO DE ACCESO DE TELECOMUNICACIONES	6.55	ÁREA TÉCNICA
		303.30	
ARQ_PL_00.5_ACCESO			
R-01	SERVICIOS ADICIONALES - CUARTO DE BASURAS PARA METRO	8.51	SERVICIOS ADICIONALES - ÁREA NO PAGA
T-08-2	CENTRO DE TRANSFORMACIÓN ENEL-CODENSA (CT)_CUARTO BAJA TENSIÓN	31.56	ÁREA TÉCNICA
T-08-3	CENTRO DE TRANSFORMACIÓN ENEL-CODENSA (CT)_CUARTO MEDIA TENSIÓN	44.56	ÁREA TÉCNICA
T-21-5	ÁREA DE INSPECCIÓN	4.02	ÁREA TÉCNICA
		88.66	
ARQ_PL_00.6_ACCESO			
CADE	CADE	847.35	CADE
T-21-3	ÁREA DE INSPECCIÓN	20.87	ÁREA TÉCNICA
		868.22	
ARQ_PL_00.7_ACCESO			
R-00-1	SERVICIOS ADICIONALES - CORREDOR OPERATIVO	66.00	SERVICIOS ADICIONALES - ÁREA NO PAGA
R-107	SERVICIOS ADICIONALES - ÁREA DE SERVICIO	576.88	SERVICIOS ADICIONALES - ÁREA NO PAGA
R-201	SERVICIOS ADICIONALES - ÁREA DE COMIDAS	93.92	SERVICIOS ADICIONALES - ÁREA NO PAGA
T-21-4	ÁREA DE INSPECCIÓN	4.06	ÁREA TÉCNICA
		740.87	
ARQ_PL_00.8_ACCESO			
R-00-2	SERVICIOS ADICIONALES - CORREDOR OPERATIVO	109.28	SERVICIOS ADICIONALES - ÁREA NO PAGA
R-02	SERVICIOS ADICIONALES - BAÑO PÚBLICO DE MUJERES	15.18	SERVICIOS ADICIONALES - ÁREA NO PAGA
R-03	SERVICIOS ADICIONALES - BAÑO PÚBLICO DE HOMBRES	15.46	SERVICIOS ADICIONALES - ÁREA NO PAGA
R-04	SERVICIOS ADICIONALES - CONTROL DE ACCESO BAÑOS PÚBLICOS	3.79	SERVICIOS ADICIONALES - ÁREA NO PAGA
R-05-1	SERVICIOS ADICIONALES - CUARTO DE LIMPIEZA	6.26	SERVICIOS ADICIONALES - ÁREA NO PAGA
R-05-2	SERVICIOS ADICIONALES - CUARTO DE LIMPIEZA	4.13	SERVICIOS ADICIONALES - ÁREA NO PAGA
R-06	SERVICIOS ADICIONALES - BAÑOS EMPLEADOS MUJERES	17.73	SERVICIOS ADICIONALES - ÁREA NO PAGA
R-07	SERVICIOS ADICIONALES - VESTIDORES EMPLEADOS MUJERES	13.19	SERVICIOS ADICIONALES - ÁREA NO PAGA
R-08	SERVICIOS ADICIONALES - BAÑOS EMPLEADOS HOMBRES	17.73	SERVICIOS ADICIONALES - ÁREA NO PAGA
R-09	SERVICIOS ADICIONALES - VESTIDORES EMPLEADOS HOMBRES	11.50	SERVICIOS ADICIONALES - ÁREA NO PAGA
R-202	SERVICIOS ADICIONALES - ÁREA DE COMIDAS	116.51	SERVICIOS ADICIONALES - ÁREA NO PAGA
R-203	SERVICIOS ADICIONALES - ÁREA DE COMIDAS	92.79	SERVICIOS ADICIONALES - ÁREA NO PAGA
T-20-L-2	MEDIDORES (LUZ)	19.75	ÁREA TÉCNICA
T-20-W-2	MEDIDORES (AGUA)	7.89	ÁREA TÉCNICA
T-30	SISTEMA PROTECCIÓN CONTRA INCENDIO ENEL	6.49	ÁREA TÉCNICA
		457.70	
ARQ_PL_00.9_ACCESO			
R-10	SERVICIOS ADICIONALES - SALA DE EMPLEADOS	14.19	SERVICIOS ADICIONALES - ÁREA NO PAGA
R-108	SERVICIOS ADICIONALES - ÁREA DE SERVICIO	204.82	SERVICIOS ADICIONALES - ÁREA NO PAGA
R-204	SERVICIOS ADICIONALES - ÁREA DE COMIDAS	156.76	SERVICIOS ADICIONALES - ÁREA NO PAGA
T-20-G	MEDIDORES (GAS)	7.27	ÁREA TÉCNICA
T-21-6	ÁREA DE INSPECCIÓN	33.24	ÁREA TÉCNICA
TM-1	ÁREA DE TAQUILLAS BRT	37.45	ÁREA DE TAQUILLAS BRT
		453.72	
ARQ_PL_01_ACCESO			
NPA-04	ÁREA NO PAGA	328.59	ÁREA NO PAGA
O-21-2	ALMACENAMIENTO DE LA ESTACIÓN	35.43	ÁREA OPERATIVA
T-25-4	NODO DE ACCESO DE TELECOMUNICACIONES	4.58	ÁREA TÉCNICA
		368.60	
TOTAL NIVEL ACCESO		4468.19	

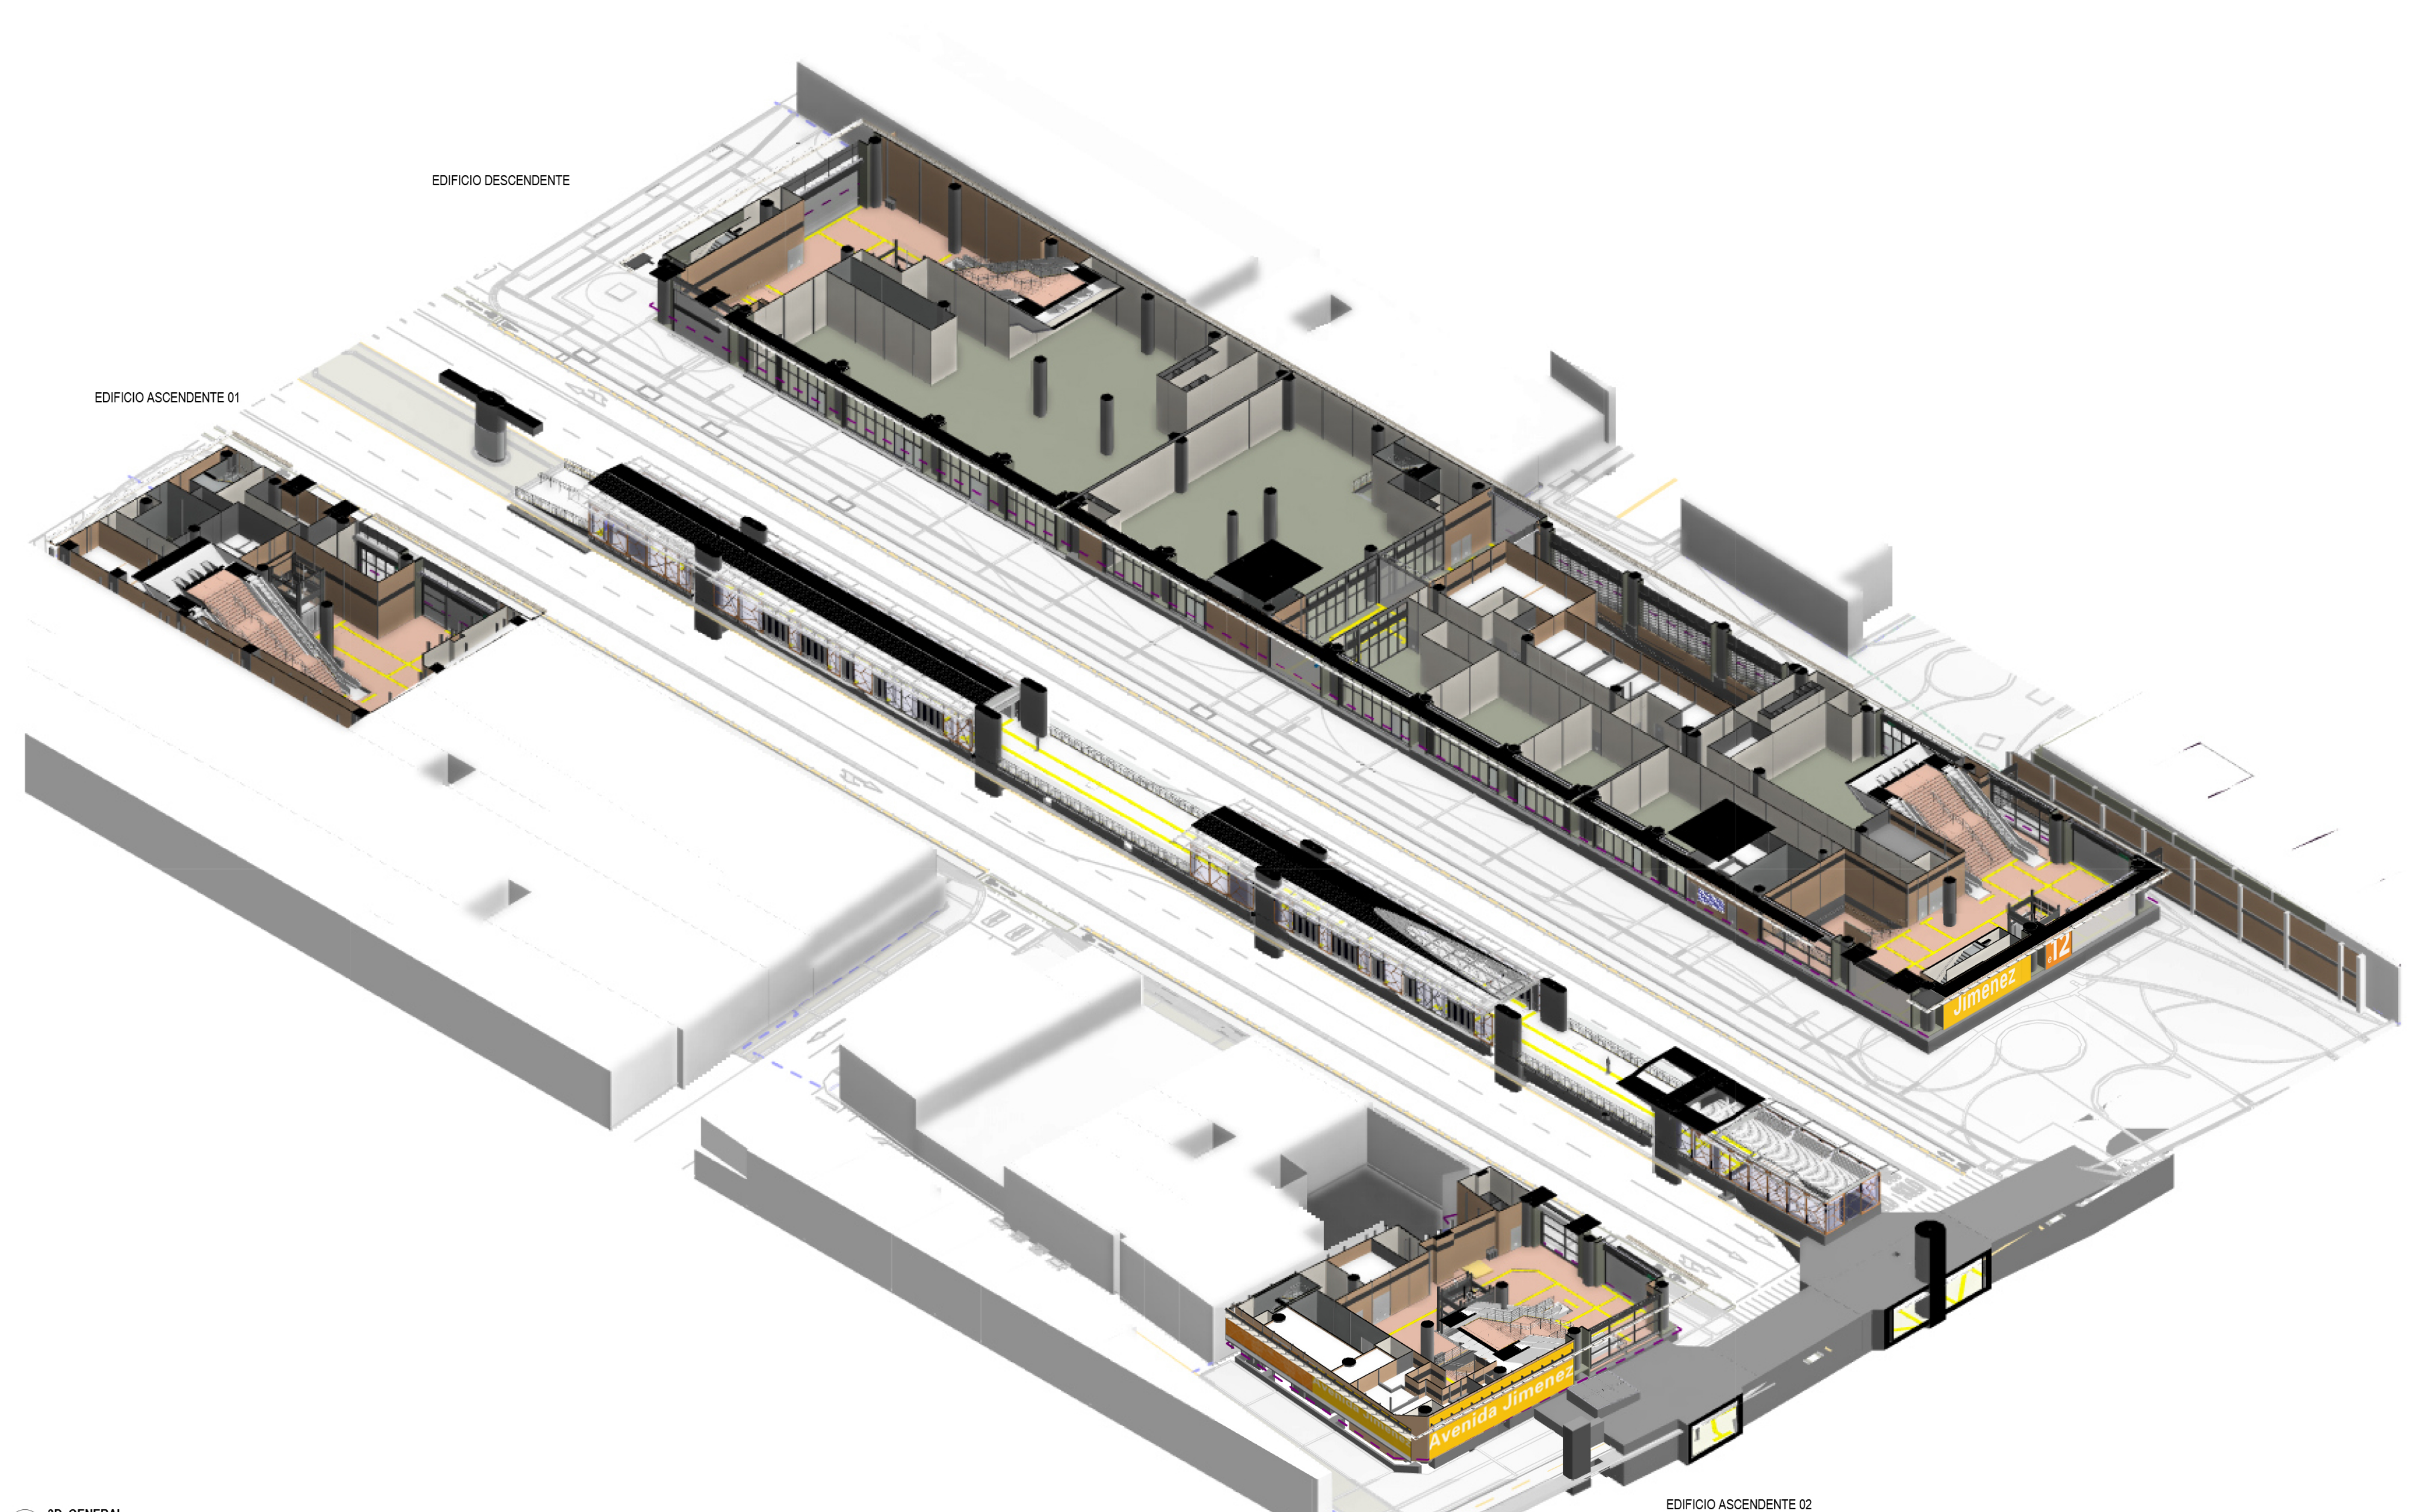
EDIFICIO DESCENDENTE
EDIFICIO ASCENDENTE 01
EDIFICIO ASCENDENTE 02
Jiménez
12
Avenida Jiménez

1 3D_GENERAL
ESC: N/A

TABLA ÁREAS ÚTILES POR DEPARTAMENTO (NIVEL ACCESO)	
DEPARTAMENTO	ÁREA (m²)
EDIFICIO ASCENDENTE 01	
ARQ_PL_00.3_ACCESO	
SERVICIOS ADICIONALES - ÁREA NO PAGA	78.09
ARQ_PL_00.4_ACCESO	
SERVICIO PÚBLICO	71.85
SERVICIOS ADICIONALES - ÁREA NO PAGA	38.64
ÁREA TÉCNICA	148.84
ARQ_PL_00.5_ACCESO	
ÁREA NO PAGA	229.73
ÁREA TÉCNICA	27.55
EDIFICIO ASCENDENTE 02	
ARQ_PL_00.10_ACCESO	
SERVICIO PÚBLICO	57.55
ÁREA NO PAGA	283.21
ÁREA TÉCNICA	199.01
ARQ_PL_01_ACCESO	
ÁREA CULTURAL	4.00
ARQ_PL_01.1_ACCESO	
ÁREA TÉCNICA	48.64

TABLA ÁREAS ÚTILES POR DEPARTAMENTO (NIVEL ACCESO)	
DEPARTAMENTO	ÁREA (m²)
EDIFICIO DESCENDENTE	
ARQ_PL_00.1_ACCESO	
ÁREA NO PAGA	296.75
ÁREA TÉCNICA	6.55
ARQ_PL_00.5_ACCESO	
SERVICIOS ADICIONALES - ÁREA NO PAGA	8.51
ÁREA TÉCNICA	80.14
ARQ_PL_00.6_ACCESO	
CADE	847.35
ÁREA TÉCNICA	20.87
ARQ_PL_00.7_ACCESO	
SERVICIOS ADICIONALES - ÁREA NO PAGA	736.81
ÁREA TÉCNICA	4.06
ARQ_PL_00.8_ACCESO	
SERVICIOS ADICIONALES - ÁREA NO PAGA	423.56
ÁREA TÉCNICA	34.14
ARQ_PL_00.9_ACCESO	
SERVICIOS ADICIONALES - ÁREA NO PAGA	375.77
ÁREA DE TAQUILLAS BRT	37.45
ÁREA TÉCNICA	40.51
ARQ_PL_01_ACCESO	
ÁREA NO PAGA	328.59
ÁREA OPERATIVA	35.43
ÁREA TÉCNICA	4.58
TOTAL NIVEL ACCESO	4468.19

TABLA GENERAL DE NIVELES		
NOMBRE	NIVEL	ELEVACIÓN (m)
ARQ_PL_05_CUB_NVC	CUBIERTA NAVE CENTRAL	24.75
ARQ_PL_04_CUB_EDIFICACIONES	CUBIERTA EDIFICACIONES	22.09
ARQ_PL_02.2_TOR	TOPE DE RIEL	14.35
ARQ_PL_03_PLATAFORMA	PLATAFORMA	15.49
ARQ_PL_02_INTERMEDIO	INTERMEDIO	6.75
ARQ_PL_00.1_ACCESO	ACCESO	-2.40
ARQ_PL_00.2_ACCESO	ACCESO	-2.10
ARQ_PL_00.3_ACCESO	ACCESO	-1.85
ARQ_PL_00.4_ACCESO	ACCESO	-1.65
ARQ_PL_00.5_ACCESO	ACCESO	-1.45
ARQ_PL_00.6_ACCESO	ACCESO	-1.25
ARQ_PL_00.7_ACCESO	ACCESO	-0.85
ARQ_PL_00.8_ACCESO	ACCESO	-0.45
ARQ_PL_00.9_ACCESO	ACCESO	-0.20
ARQ_PL_00.10_ACCESO	ACCESO	-0.15
ARQ_PL_01.1_ACCESO	ACCESO	0.97
ARQ_PL_01_ACCESO	ACCESO*	2589.25
ARQ_PL_00.1_SÓTANO	SÓTANO	-7.93
ARQ_PL_00.2_SÓTANO	SÓTANO	-7.45
ARQ_PL_00.3_SÓTANO	SÓTANO	-6.98
ARQ_PL_00.4_SÓTANO	SÓTANO	-6.50
ARQ_PL_00.5_SÓTANO	SÓTANO	-4.70
ARQ_PL_00_SÓTANO	SÓTANO	-8.40

M.S.N.M / 0.00

LOCALIZACIÓN

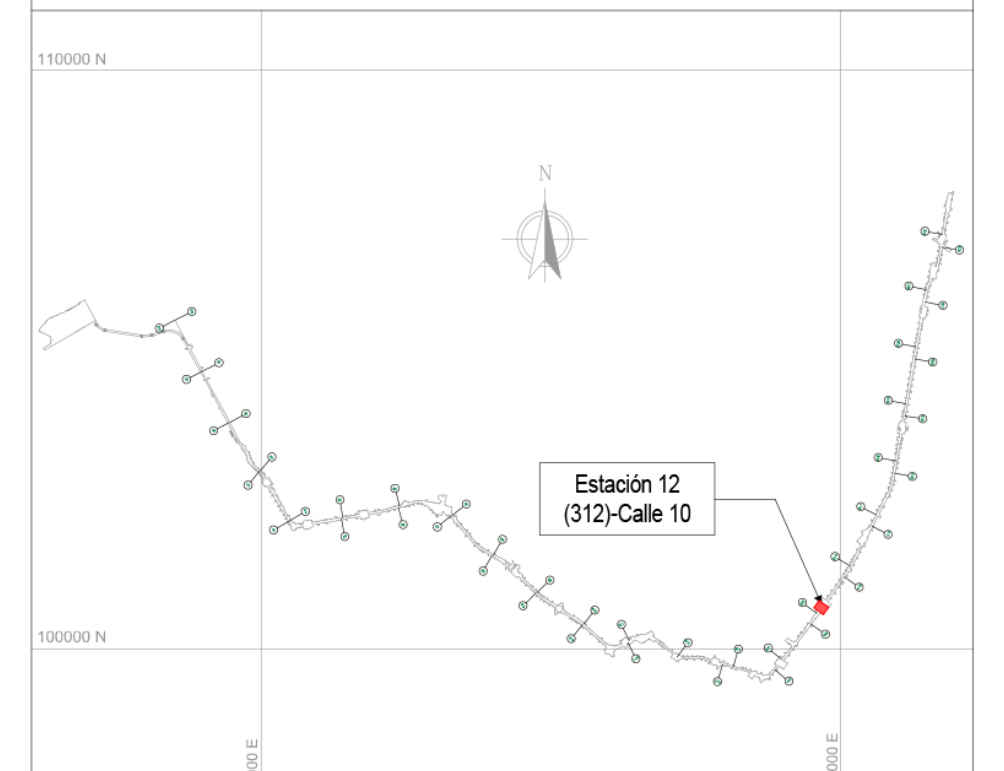
110000 N
100000 N
90000 E
100000 E
N
Estación 12
(312)-Calle 10

NOTAS

01 TODAS LAS DIMENSIONES ESTÁN CONFIGURADAS EN METROS A MENOS QUE SE INDIQUE UNA UNIDAD DE MEDIDA DIFERENTE.

02 TODAS LAS MEDIDAS, UBICACIÓN Y NIVELES DEBEN VERIFICARSE EN EL LUGAR DE CONSTRUCCIÓN.

03 EL NIVEL DE ACCESO AL EDIFICIO PL 01 CORRESPONDE AL +0,00 DE LA ESTACIÓN Y REFERENCIA AL NIVEL 2589.25 M.S.N.M.

04 LOS NOMBRES ESPECÍFICOS DE LAS ÁREAS PUEDEN SER CONSULTADAS EN EL PLANO NO. 3 Ó EN LAS VISTAS EN PLANTA.

05 LOS COLORES QUE SE MUESTRAN EN LOS PLANOS COMO PROYECCIÓN DE ELEMENTOS ARQUITECTÓNICOS COMO CUBIERTAS FACHADAS MUROS ETC. NO REPRESENTAN LA MATERIALIDAD Y REALIDAD DE ACABADOS DEL PROYECTO, SOLO SON INDICATIVOS PARA REALIZAR UNA CORRECTA LECTURA DE LA PLANIMETRÍA.

06 LAS ESCALERAS ELÉCTRICAS INDICAN SU SENTIDO CON LA SIGUIENTE NOMENCLATURA: "SUBE" Y "BAJA".

07 SE DEBEN REVISAR LOS NIVELES ESTRUCTURALES PARA NIVEL DE ACCESO PL_01 Y SUBNIVELES, PL_02 (INTERMEDIO), PL_03 (PLATAFORMA) CON LA PLANIMETRÍA DE PLACAS ESTRUCTURALES EN LOS ENTREGABLES L1T1-1300-412-CON-ED-EST-PL-0045, 86, 88, 129, 130, 131, 134, 135, 136, RESPECTIVAMENTE. EL NIVEL ESTRUCTURAL (NE) REFERENCIA LOS ESPACIOS DONDE SE DEBE ACONDICIONAR EL ACABADO DE PISO SEGÚN CORRESPONDA, CON LOS NIVELES DE PISO TERMINADO (NPT). LOS NIVELES PROYECTADOS DE EMPATE (NPE) EN LAS ÁREAS DE SERVICIOS ADICIONALES, REFERENCIAN LA ADECUACIÓN DE LOS DESNIVELES EN ESTAS ÁREAS, QUEDA COMO RESPONSABILIDAD DEL LOCATARIO DEFINIR Y ACONDICIONAR ESTE ACABADO DE PISO (NPE) EN LÍNEA CON EL NIVEL (NPT) DE ESPACIOS COLINDANTES. EL NIVEL ESTRUCTURAL (NE) SE ENCUENTRA A (- 0.10M) POR DEBAJO DE LOS NIVELES DE PISO TERMINADO (NPT) Y LOS NIVELES PROYECTADOS DE EMPATE (NPE) MARCADOS EN LA PLANIMETRÍA.

08 RESPECTO A LAS ÁREAS CONSTRUIDAS Y DE ACUERDO CON LA COMUNICACIÓN EXTS22-0002544 DE EMB, SE IDENTIFICA QUE EL CONCESIONARIO SE ENCUENTRA BUSCANDO ESTRATEGIAS PARA MEJORAR EL DISEÑO CON EL PROGRAMA ARQUITECTÓNICO, UNA DE ESTAS ESTRATEGIAS ES MEJORAR EL FUNCIONAMIENTO DEL DISEÑO URBANO Y BRINDAR UNA SOLUCIÓN INTEGRAL RESPECTO A LOS INMUEBLES DE INTERÉS CULTURAL. DE ACUERDO CON LO ANTERIOR, PARA LA EMB, ESTAS ACTIVIDADES OBEDECEN AL PROCESO NATURAL DE LOS ESTUDIOS Y DISEÑOS DEFINITIVOS QUE DEBE DESARROLLAR METRO LÍNEA 1.

CONVENCIONES

- LÍMITE DE INTERVENCIÓN
- HUELLA APÉNDICE TÉCNICO
- HUELLA LÍMITE LEVANTAMIENTO TOPOGRÁFICO
- MURO DIVISORIO
- PROYECCIÓN NIVEL SUPERIOR

🟩	SERVICIOS ADICIONALES ÁREA NO PAGA	🟨	ÁREA NO PAGA
🟩	SERVICIOS ADICIONALES ÁREA PAGA	🟦	ÁREA OPERATIVA
🟩	SERVICIO PÚBLICO	🟨	ÁREA PAGA
🟦	ZONA DE REFUGIO	🟦	ÁREA PÚBLICA
🟥	ÁREA CULTURAL	⬜	ÁREA TÉCNICA
🟩	CADE		

No.	PLANOS DE REFERENCIA	REV.

No.	MODELO BIM DE REFERENCIA	REV.
1	L1T1-1100-212-CON-ED-EST-MO-0001.rvt	V00
2	L1T1-1100-213-CON-ED-EST-MO-0001.rvt	V00
3	L1T1-1100-312-CON-ED-EST-MO-0001.rvt	V00
4	L1T1-1150-212-CON-ED-EST-MO-0001.rvt	V00
5	L1T1-1150-213-CON-ED-EST-MO-0001.rvt	V00
6	L1T1-1150-312-CON-ED-EST-MO-0001.rvt	V00
7	L1T1-1200-312-CON-ED-EST-MO-0001.rvt	V00
8	L1T1-1300-412-CON-ED-EST-MO-0001.rvt	V00
9	L1T1-1300-412-CON-ED-EST-MO-0002.rvt	V00
10	L1T1-1300-412-CON-ED-EST-MO-0003.rvt	V00
11	L1T1-1310-412-CON-ED-EST-MO-0001.rvt	V00
12	L1T1-1410-312-CON-ED-MEC-MO-0001.rvt	V00
13	L1T1-1420-312-CON-ED-MEC-MO-0001.rvt	V00
14	L1T1-2320-584-CON-ED-EST-MO-0001.rvt	V00
15	L1T1-2330-584-CON-ED-ARQ-MO-0001.rvt	V00
16	L1T1-2430-551-CON-ED-ARQ-MO-0001.rvt	V00
17	L1T1-2430-551-CON-ED-EST-MO-0001.rvt	V00
18	L1T1-5160-312-CON-ED-ARQ-MO-0001.rvt	V00
19	L1T1-5160-312-CON-ED-EST-MO-0001.rvt	V00
20	L1T1-5300-312-CON-ED-MEC-MO-0001.rvt	V00
21	L1T1-5600-312-CON-ED-INS-MO-0001.rvt	V00
22	L1T1-1330-412-CON-ED-ARQ-MO-0011.rvt	V00
23	L1T1-1330-412-CON-ED-ARQ-MO-0012.rvt	V00
24	L1T1-1330-412-CON-ED-ARQ-MO-0013.rvt	V00

No.	PAQUETE DE TRABAJO DE REFERENCIA	REV.
1	XREF-URBANISM_CONTEXT_ST12.rvt	
2	XREF-SECONDARY-STRUCTURE-ST12.rvt	

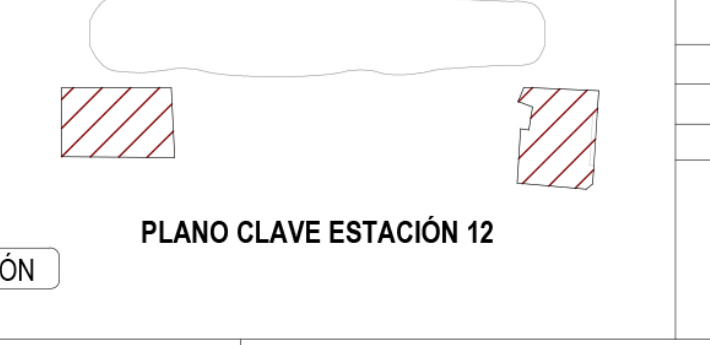

PLANO CLAVE ESTACIÓN 12

0 2 10m
1:200

VÁLIDO PARA CONSTRUCCIÓN
31-03-26

METRO BOGOTÁ — GCS Consorcio Consultores PMO Bogotá — CONSORCIO SUPERVISOR PLMB — CHEC

DISEÑO:
REN ZHENHUA
Licencia de Arq.nivel I (China): 1101735-614

REVISÓ:
CARLOS MAURICIO BARRETO BARBOSA
Mat.: A4012012-14139353

APROBÓ:
DIEGO ERNESTO DUEÑAS
Mat.: 25202-53876 CND

DIBUJÓ:
EQUIPO CHEC

REVISIÓN No.	FECHA	DESCRIPCIÓN	REVISÓ	APROBÓ	APROBACIÓN CLIENTE
V02	31/03/2026	EMITIDO PARA CONSTRUCCIÓN	C.M.B.B	D.E.D	
V01	16/07/2025	REVISIÓN NO OBJETADA - EMITIDO PARA CONSTRUCCIÓN	F.B.R	M.M.R	
VB1	20/03/2025	EMITIDO PARA REVISIÓN Y COMENTARIOS DEL CLIENTE E INTERVENTORÍA	F.B.R	E.O.M	
V00	13/02/2025	REVISIÓN NO OBJETADA - EMITIDO PARA CONSTRUCCIÓN	F.B.R	E.O.M	
VGG	18/10/2024	EMITIDO PARA REVISIÓN Y COMENTARIOS DEL CLIENTE E INTERVENTORÍA - INCLUYE COMENTARIOS //(AJUSTES V2)	F.B.R	E.O.M	
VFF	21/05/2024	EMITIDO PARA REVISIÓN Y COMENTARIOS DEL CLIENTE E INTERVENTORÍA - INCLUYE COMENTARIOS //(AJUSTES)	F.B.R	E.O.M	
VEE	25/01/2023	EMITIDO PARA REVISIÓN Y COMENTARIOS DEL CLIENTE E INTERVENTORÍA - INCLUYE COMENTARIOS //(90% ACCESOS)	J.E.M	M.B.M	
VDD	18/12/2022	EMITIDO PARA REVISIÓN Y COMENTARIOS DEL CLIENTE E INTERVENTORÍA - INCLUYE COMENTARIOS //(NAVE CENTRAL)	J.E.M	M.B.M	
VCC	22/08/2022	EMITIDO PARA REVISIÓN Y COMENTARIOS DEL CLIENTE E INTERVENTORÍA - INCLUYE COMENTARIOS //(ENTREGA 90%)	J.E.M	M.B.M	
VBB	06/12/2021	EMITIDO PARA REVISIÓN Y COMENTARIOS DEL CLIENTE E INTERVENTORÍA	J.E.M	M.B.M	

METRO LÍNEA 1

METRO LÍNEA 1
CONTRATO DE CONCESIÓN No. 163 DE 2019

PROYECTO PRIMERA LÍNEA DEL METRO DE BOGOTÁ - TRAMO 1

DIRECTOR DE INTERVENTORÍA:
JAVIER DESCARGA N.
Mat.:25202-68697 CND

ESPECIALISTA INTERVENTORÍA:
CARLOS ALBERTO HOYOS SOTO
Mat.:A25072000-14251682

FECHA:
MARZO 2026

INFRAESTRUCTURA VIAL

ARQUITECTURA

ESTACIÓN METRO 12 - (CALLE 10)
NAVE CENTRAL - EDIFICIO ASCENDENTE 01 - EDIFICIO ASCENDENTE 02 - EDIFICIO DESCENDENTE
VISTA EN PLANTA Y 3D - NIVEL ACCESO

PLANCHA No: L1T1-0000-312-CON-ED-ARQ-PL-0001_05_V02
ARCHIVO: L1T1-0000-312-CON-ED-ARQ-MO-0001_V01.rvt
ESCALA: INDICADA
FECHA: JUNIO 2021
REVISIÓN No. V02
PLANO No. 05 DE 100