L1T1-CON-CAL-FR-0120 - B1 : 1000x707mm

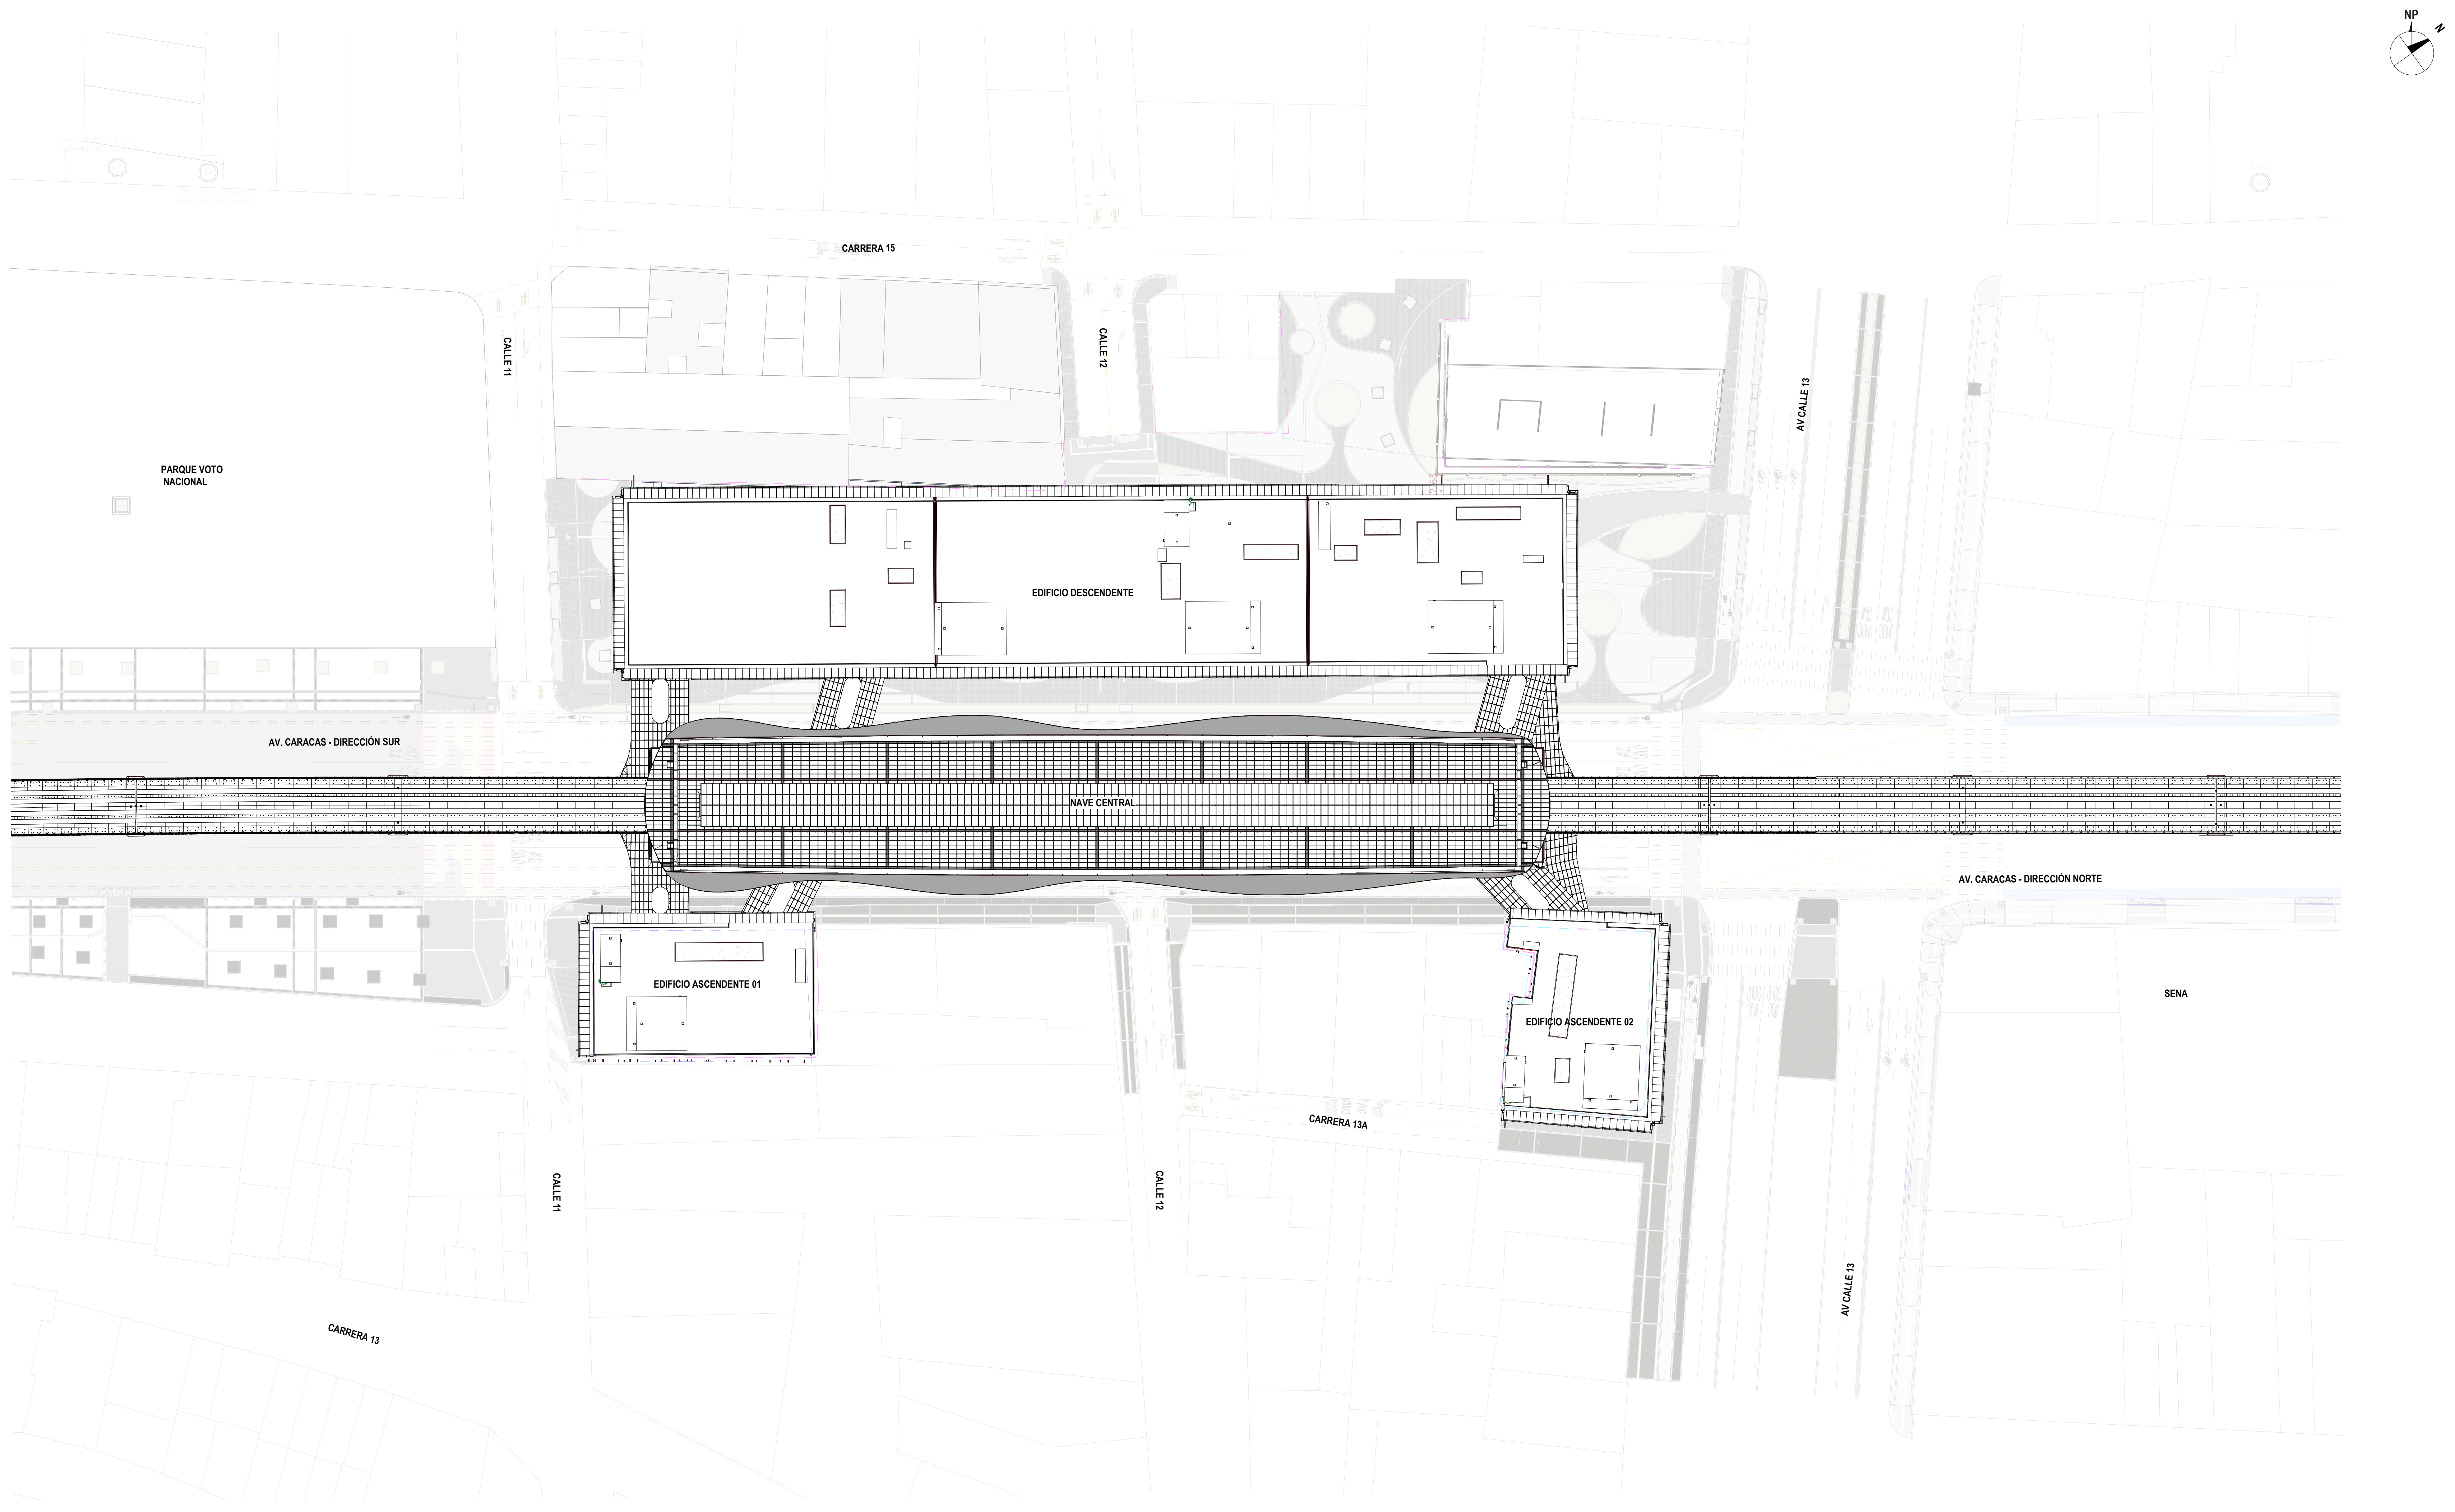

2 **NIVEL CUBIERTA_GENERAL**
ESC.: 1 : 500

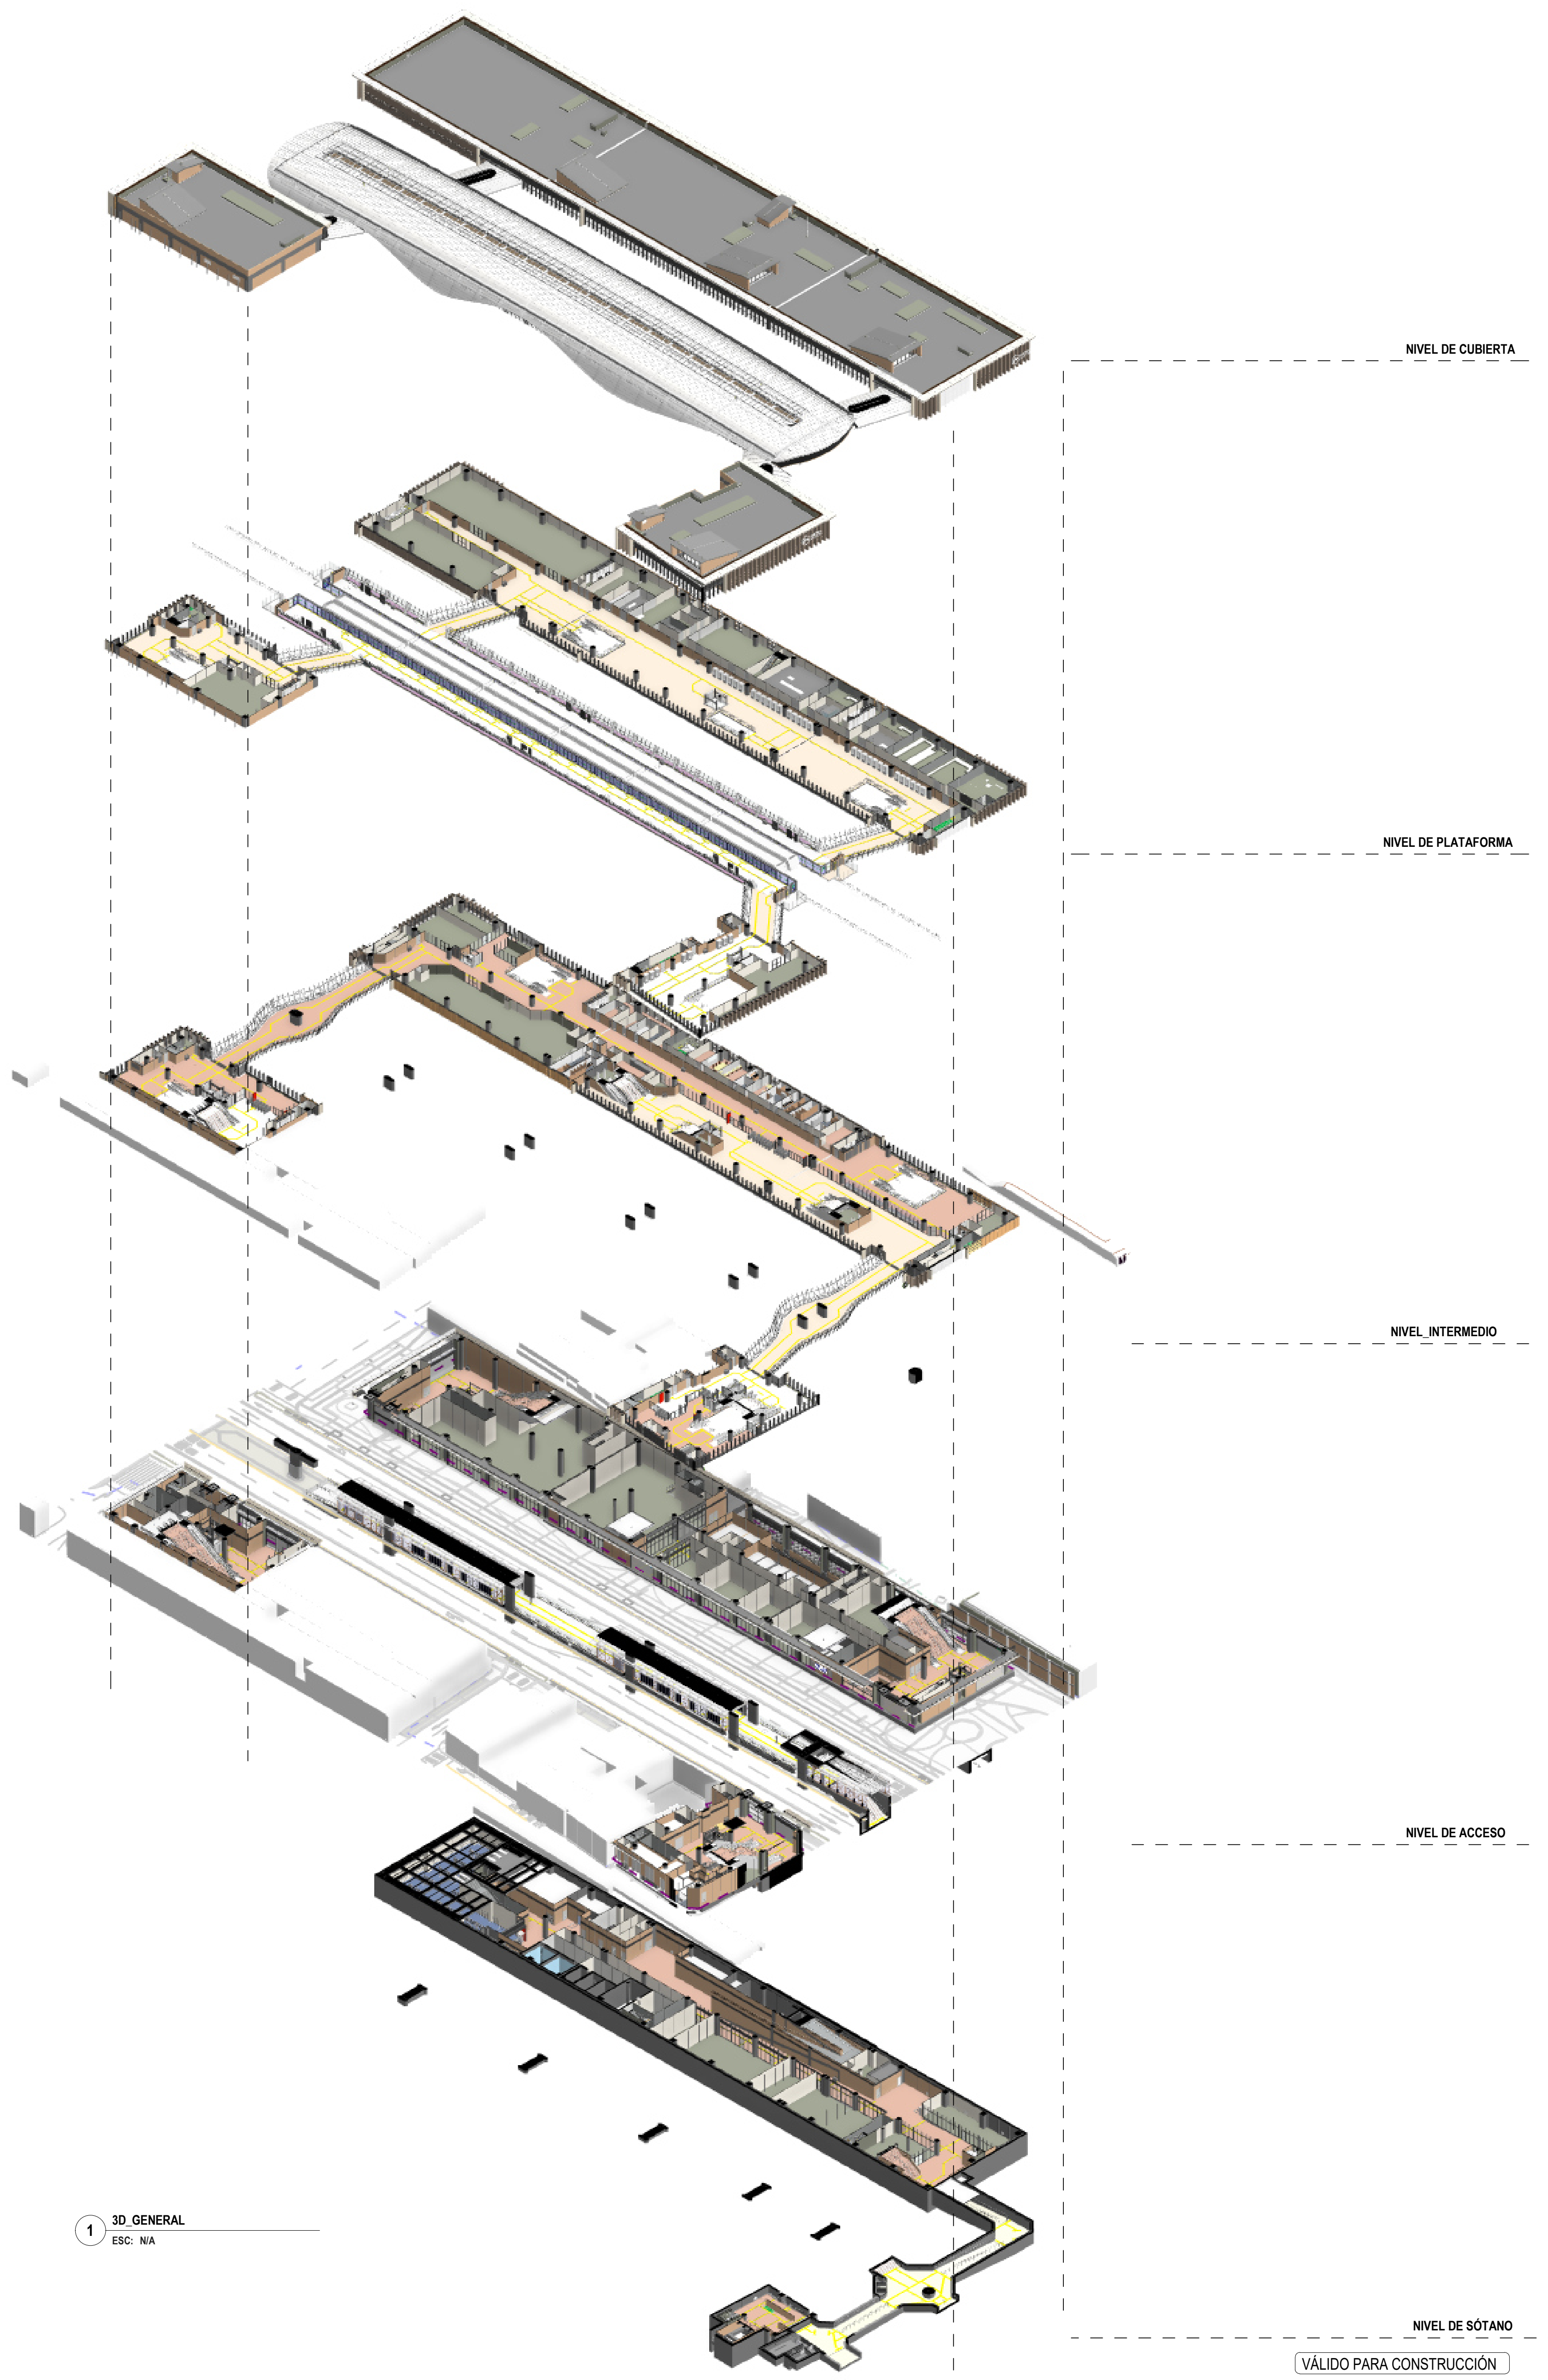

1 **3D_GENERAL**
ESC: N/A

VÁLIDO PARA CONSTRUCCIÓN
31-03-26

LOCALIZACIÓN

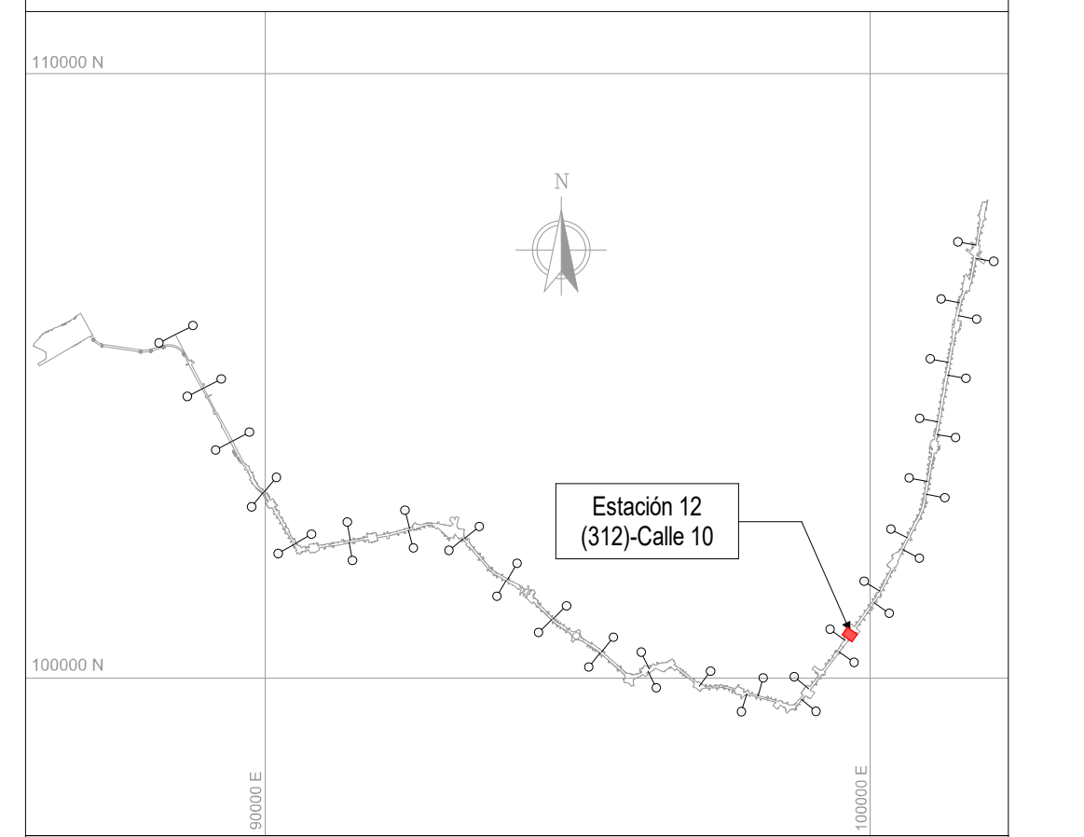

NOTAS

01 TODAS LAS DIMENSIONES ESTÁN CONFIGURADAS EN METROS A MENOS QUE SE INDIQUE UNA UNIDAD DE MEDIDA DIFERENTE.

02 TODAS LAS MEDIDAS, UBICACIÓN Y NIVELES DEBEN VERIFICARSE EN EL LUGAR DE CONSTRUCCIÓN.

03 EL NIVEL DE ACCESO AL EDIFICIO PL 01 CORRESPONDE AL +0,00 DE LA ESTACIÓN Y REFERENCIA AL NIVEL 2589.25 M.S.N.M.

04 LOS EJES DEBEN VERIFICARSE EN LA VISTA EN PLANTA DE LOS PLANOS ARQUITECTÓNICOS.

05 LOS COLORES QUE SE MUESTRAN EN LOS PLANOS COMO PROYECCIÓN DE ELEMENTOS ARQUITECTÓNICOS COMO CUBIERTAS FACHADAS MUROS ETC. NO REPRESENTAN LA MATERIALIDAD Y REALIDAD DE ACABADOS DEL PROYECTO, SOLO SON INDICATIVOS PARA REALIZAR UNA CORRECTA LECTURA DE LA PLANIMETRÍA.

06 VER LOS PLANOS DE LAS ESPECIALIDADES ESPECÍFICAS PARA EL DISEÑO DE LAS ZONAS EXTERIORES DE LAS ESTACIONES METRO EN LA QUE SE ENCUENTRAN DETALLES DE URBANISMO, PAISAJISMO, PASOS PEATONALES Y VÍAS.

- ARQ_PL_00 = SÓTANO / NPT -8.40m
- ARQ_PL_00.1 = SÓTANO / NPT -7.93m
- ARQ_PL_00.2 = SÓTANO / NPT -7.45m
- ARQ_PL_00.3 = SÓTANO / NPT -6.98m
- ARQ_PL_00.4 = SÓTANO / NPT -6.50m
- ARQ_PL_00.5 = SÓTANO / NPT -4.70m
- ARQ_PL_00.1 = ACCESO / NPT -2.40m
- ARQ_PL_00.2 = ACCESO / NPT -2.10m
- ARQ_PL_00.3 = ACCESO / NPT -1.85m
- ARQ_PL_00.4 = ACCESO / NPT -1.65m
- ARQ_PL_00.5 = ACCESO / NPT -1.45m
- ARQ_PL_00.6 = ACCESO / NPT -1.25m
- ARQ_PL_00.7 = ACCESO / NPT -0.85m
- ARQ_PL_00.8 = ACCESO / NPT -0.45m
- ARQ_PL_00.9 = ACCESO / NPT -0.20m
- ARQ_PL_00.10 = ACCESO / NPT -0.15m
- ARQ_PL_01 = ACCESO / NPT 0.00m
- ARQ_PL_01.1 = ACCESO / NPT 0.97m
- ARQ_PL_02 = INTERMEDIO / NPT 6.75m
- ARQ_PL_02.2 = TOPE DE RIEL (TOR) / NPT 14.35m
- ARQ_PL_03 = PLATAFORMA / NPT 15.49m
- ARQ_PL_04 = CUBIERTA EDIFICACIONES / NPT 22.09m
- ARQ_PL_05 = CUBIERTA NAVE CENTRAL / NPT 24.75m

CONVENCIONES

▬ ▬ ▬	LÍMITE DE INTERVENCIÓN
▬ ▬ ▬	HUELLA APÉNDICE TÉCNICO
▬ ▬ ▬	HUELLA LÍMITE LEVANTAMIENTO TOPOGRÁFICO
■	MURO DIVISORIO
▬ ▬ ▬	PROYECCIÓN NIVEL SUPERIOR

No.	PLANOS DE REFERENCIA	REV.

No.	MODELO BIM DE REFERENCIA	REV.
1	L1T1-1100-212-CON-ED-EST-MO-0001.rvt	V00
2	L1T1-1100-213-CON-ED-EST-MO-0001.rvt	V00
3	L1T1-1100-312-CON-ED-EST-MO-0001.rvt	V00
4	L1T1-1150-212-CON-ED-EST-MO-0001.rvt	V00
5	L1T1-1150-213-CON-ED-EST-MO-0001.rvt	V00
6	L1T1-1150-312-CON-ED-EST-MO-0001.rvt	V00
7	L1T1-1200-312-CON-ED-EST-MO-0001.rvt	V00
8	L1T1-1300-412-CON-ED-EST-MO-0001.rvt	V00
9	L1T1-1300-412-CON-ED-EST-MO-0002.rvt	V00
10	L1T1-1300-412-CON-ED-EST-MO-0003.rvt	V00
11	L1T1-1310-412-CON-ED-EST-MO-0001.rvt	V00
12	L1T1-1410-312-CON-ED-MEC-MO-0001.rvt	V00
13	L1T1-1420-312-CON-ED-MEC-MO-0001.rvt	V00
14	L1T1-2320-584-CON-ED-EST-MO-0001.rvt	V00
15	L1T1-2330-584-CON-ED-ARQ-MO-0001.rvt	V00
16	L1T1-2430-551-CON-ED-ARQ-MO-0001.rvt	V00
17	L1T1-2430-551-CON-ED-EST-MO-0001.rvt	V00
18	L1T1-5160-312-CON-ED-ARQ-MO-0001.rvt	V00
19	L1T1-5160-312-CON-ED-EST-MO-0001.rvt	V00
20	L1T1-5300-312-CON-ED-MEC-MO-0001.rvt	V00
21	L1T1-5600-312-CON-ED-INS-MO-0001.rvt	V00
22	L1T1-1330-412-CON-ED-ARQ-MO-0011.rvt	V00
23	L1T1-1330-412-CON-ED-ARQ-MO-0012.rvt	V00
24	L1T1-1330-412-CON-ED-ARQ-MO-0013.rvt	V00

No.	PAQUETE DE TRABAJO DE REFERENCIA	REV.
1	XREF-URBANISM_CONTEXT_ST12.rvt	
2	XREF-SECONDARY-STRUCTURE-ST12.rvt	

0 5 25m
1:500

METRO BOGOTÁ
GCS Consorcio Consultores PMO Bogotá
CONSORCIO SUPERVISOR PLMB
CHEC

DISEÑÓ:	REN ZHENHUA Licencia de Arq.nivel I (China): 1101735-614
APROBÓ:	DIEGO ERNESTO DUEÑAS Mat.: 25202-53876 CND
REVISÓ:	CARLOS MAURICIO BARRETO BARBOSA Mat.: A4012012-14139353
DIBUJÓ:	EQUIPO CHEC

REVISIÓN No.	FECHA	DESCRIPCIÓN	REVISÓ	APROBÓ	APROBACIÓN CLIENTE
V02	31/03/2026	EMITIDO PARA CONSTRUCCIÓN	C.M.B.B	D.E.D	
V01	16/07/2025	REVISIÓN NO OBJETADA - EMITIDO PARA CONSTRUCCIÓN	F.B.R	M.M.R	
VB1	20/03/2025	EMITIDO PARA REVISIÓN Y COMENTARIOS DEL CLIENTE E INTERVENTORÍA	F.B.R	E.O.M	
V00	13/02/2025	REVISIÓN NO OBJETADA - EMITIDO PARA CONSTRUCCIÓN	F.B.R	E.O.M	
VGG	18/10/2024	EMITIDO PARA REVISIÓN Y COMENTARIOS DEL CLIENTE E INTERVENTORÍA - INCLUYE COMENTARIOS /(AJUSTES V2)	F.B.R	E.O.M	
VFF	21/05/2024	EMITIDO PARA REVISIÓN Y COMENTARIOS DEL CLIENTE E INTERVENTORÍA - INCLUYE COMENTARIOS /(AJUSTES)	F.B.R	E.O.M	
VEE	25/01/2023	EMITIDO PARA REVISIÓN Y COMENTARIOS DEL CLIENTE E INTERVENTORÍA - INCLUYE COMENTARIOS /(90% ACCESOS)	J.E.M	M.B.M	
VDD	18/12/2022	EMITIDO PARA REVISIÓN Y COMENTARIOS DEL CLIENTE E INTERVENTORÍA - INCLUYE COMENTARIOS /(NAVE CENTRAL)	J.E.M	M.B.M	
VCC	22/08/2022	EMITIDO PARA REVISIÓN Y COMENTARIOS DEL CLIENTE E INTERVENTORÍA - INCLUYE COMENTARIOS /(ENTREGA 90%)	J.E.M	M.B.M	
VBB	06/12/2021	EMITIDO PARA REVISIÓN Y COMENTARIOS DEL CLIENTE E INTERVENTORÍA	J.E.M	M.B.M	

METRO LÍNEA 1

METRO LÍNEA 1
CONTRATO DE CONCESIÓN No. 163 DE 2019

PROYECTO PRIMERA LÍNEA DEL METRO DE BOGOTÁ - TRAMO 1

DIRECTOR DE INTERVENTORÍA:	ESPECIALISTA INTERVENTORÍA:	FECHA:
JAVIER DESCARGA N. Mat.:25202-68697 CND	CARLOS ALBERTO HOYOS SOTO Mat.:A25072000-14251682	MARZO 2026

INFRAESTRUCTURA VIAL

ARQUITECTURA

ESTACIÓN METRO 12 - (CALLE 10)
NAVE CENTRAL - EDIFICIO ASCENDENTE 01 - EDIFICIO ASCENDENTE 02 - EDIFICIO DESCENDENTE
VISTA EN PLANTA - NIVEL DE CUBIERTA - AXONOMETRÍA GENERAL

PLANCHA No:	L1T1-0000-312-CON-ED-ARQ-PL-0001_08_V02	ESCALA: INDICADA	REVISIÓN No.	PLANO No.	
ARCHIVO:	L1T1-0000-312-CON-ED-ARQ-MO-0001_V01.rvt	FECHA: DICIEMBRE 2021	V02	08 DE 100	