KEY PLAN

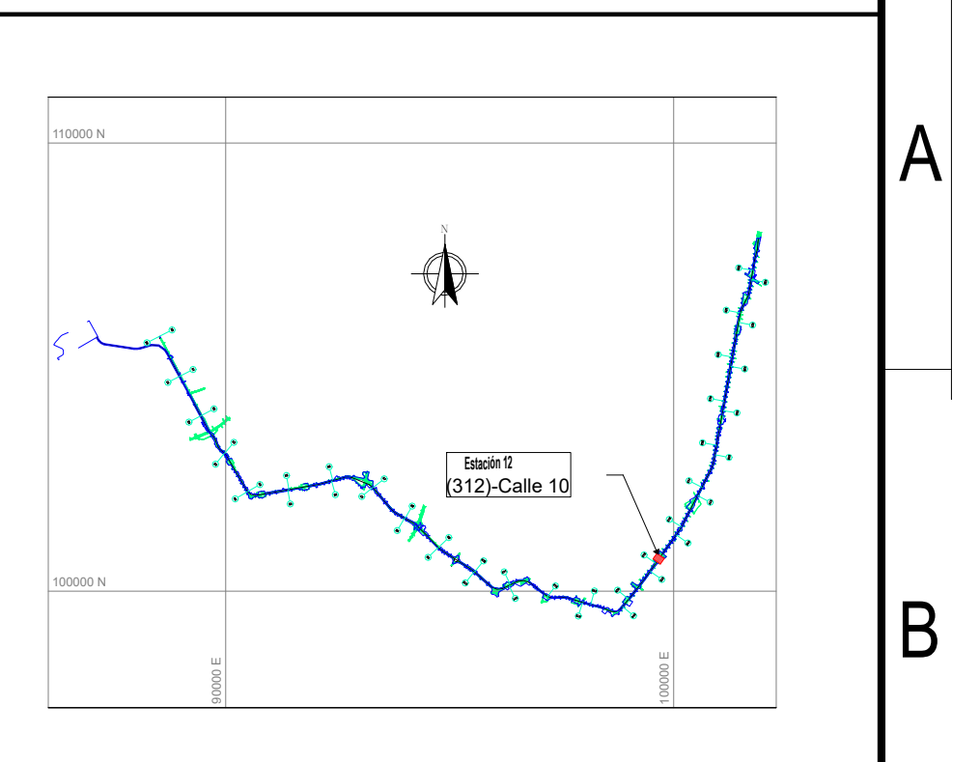

NOTAS

1.Este plano debe revisarse junto con el informe de diseño de L1T1-5445-000-CON-ED-INS-IN-0001 y L1T1-5420-312-CON-ED-INS-PL-0001.

2.Para el listado de equipo, consulte L1T1-5445-000-CON-ED-INS-CO-0001.

3.Para el listado del cable Ethernet (incluyendo el Ethernet para los puertos de contacto seco conectados a los intercomunicadores), se incluye en los planos de los enlaces de acceso de RMS.

4.Para el listado de cables conectados a la detección de intrusos, se incluye en los planos del ACS.

5.La información de las bandejas de cables y tuberías se refiere a los planos de CNL.

6. Los criterios de denominación de las cámaras son los siguientes:

Nivel - tipo de cámara - código de la cámara.

Definición de nivel:

B: como nivel del sótano;
A: como nivel de acceso;
I: como nivel intermedio;
P: como nivel de plataforma.

Definición del tipo de cámara:

D: como cámara domo;
F: como cámara fija;
P: como cámara PTZ.

E.G: B-F-1 es una cámara fija con código 1 en el nivel del sótano.

CONVENCIONES

DESCRIPCIÓN DE LOS ICONOS

	Cámara de domo
	Cámara fija (tipo inteligente)
	Cámara PTZ
PAM	Monitor de vigilancia de pasajeros
DEC	Decodificador de vídeo
Intercomunicador	Intercomunicador

No.	PLANOS DE REFERENCIA	REV.
1	L1T1-5420-312-CON-ED-INS-PL-0001	VDD

No.	MODELO BIM DE REFERENCIA	REV.
1	L1T1-0000-312-CON-ED-ARQ-MO-0001	VDD

No.	PAQUETE DE TRABAJO DE REFERENCIA	REV.

METRO BOGOTÁ

Consorcio Consultores PMO Bogotá

CONSORCIO SUPERVISOR PLMB

Líder de Diseño
Interfaz y
Gerencia de Integración

DISEÑÓ:
WANG KEJIA
Mat.: R2022011515

APROBÓ:
ZHANG YUJIE
Mat.: NÚMERO DE MATRÍCULA

ING_TÉCNICO_WSP
Mat.: NÚMERO DE MATRÍCULA

REVISÓ:
YANG BAODONG
Mat.:

MODELÓ/DIBUJÓ:
WANG KEJIA
Mat.:R2022011515

APRO_INTEGRACIÓN_WSP
Mat.: NÚMERO DE MATRÍCULA
*"Aprobada bajo el marco de los límites y condiciones establecido en la tercera sección del parágrafo del apéndice 1 sección 1 del acuerdo del contrato de diseño"

REVISIÓN No.	FECHA	DESCRIPCIÓN	REVISÓ	APROBÓ	APROBACIÓN CLIENTE
VDD	05/06/2023	Emitido para revisión y comentarios del cliente e Interventoría - Incluye comentarios / modificado donde se indica en el control de cambios	Y.B.	Z.Y.	
VCC	11/10/2022	Emitido para revisión y comentarios del cliente e Interventoría - Incluye comentarios / modificado donde se indica en el control de cambios	Y.B.	Z.Y.	
VBB	09/12/2021	Emitido para revisión y comentarios del cliente e Interventoría	Y.B.	Z.Y.	
VA0	08/12/2021	Emitido para comentarios internos - Emisión preliminar para comentarios	Y.B.	Z.Y.	

METRO LÍNEA 1

METRO LÍNEA 1
CONTRATO DE CONCESIÓN N.º 163 DE 2019

PROYECTO PRIMERA LÍNEA DEL METRO DE BOGOTÁ - TRAMO 1

DIRECTOR INTERVENTORÍA:
JAVIER DESCARGA N.
Mat.: 25202-68697 CND

ESPECIALISTA INTERVENTORÍA:
Mat.:

FECHA:
JUNIO 2023

SISTEMAS Y EQUIPOS
TELECOMUNICACIONES

ESTACIÓN CALLE 10 - DISEÑO DETALLADO DEL NIVEL DE ACCESO (PARTE DESCENDENTE)
SISTEMA CCTV
DISPOSICIÓN GENERAL

PLANCHA No.: L1T1-5445-312-CON-ED-INS-PL-0009_03_VDD
ARCHIVO: L1T1-5445-312-CON-ED-INS-PL-0009_VDD.dwg
ESCALA: 1:100
FECHA: DICIEMBRE 2021
REVISIÓN No.: VDD
HOJA No.: 3 DE 14