DB-D
DB-E
DB-F
DB-J
DB-K
DB-L
DB-L'
DB-M
DB-N
DB-03
DB-02
DB-01
Intercomunicador
T-08
T-21
R-104
229.80m2
R-202
118.28m2

KEY PLAN

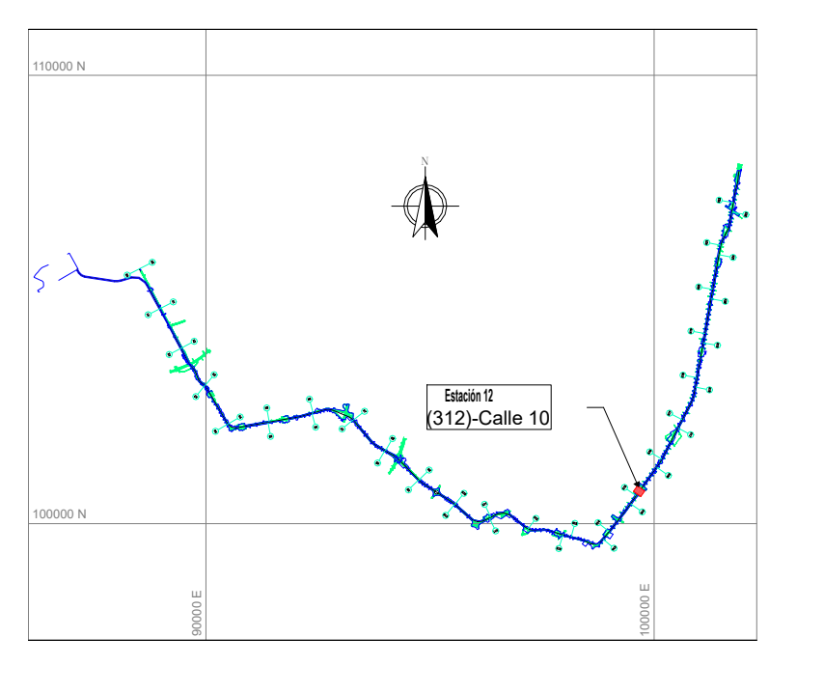

NOTAS

1.Este plano debe revisarse junto con el informe de diseño de L1T1-5445-000-CON-ED-INS-IN-0001 y L1T1-5420-312-CON-ED-INS-PL-0001.

2.Para el listado de equipo, consulte L1T1-5445-000-CON-ED-INS-CO-0001.

3.Para el listado del cable Ethernet (incluyendo el Ethernet para los puertos de contacto seco conectados a los intercomunicadores), se incluye en los planos de los enlaces de acceso de RMS.

4.Para el listado de cables conectados a la detección de intrusos, se incluye en los planos del ACS.

5.La información de las bandejas de cables y tuberías se refiere a los planos de CNL.

6. Los criterios de denominación de las cámaras son los siguientes:

Nivel - tipo de cámara - código de la cámara.

Definición de nivel:

- B: como nivel del sótano;
- A: como nivel de acceso;
- I: como nivel intermedio;
- P: como nivel de plataforma.

Definición del tipo de cámara:

- D: como cámara domo;
- F: como cámara fija;
- P: como cámara PTZ.

E.G: B-F-1 es una cámara fija con código 1 en el nivel del sótano.

CONVENCIONES

DESCRIPCIÓN DE LOS ICONOS

⌓	Cámara de domo
▭	Cámara fija (tipo inteligente)
◎	Cámara PTZ
PAM	Monitor de vigilancia de pasajeros
DEC	Decodificador de vídeo
Intercomunicador	Intercomunicador

No.	PLANOS DE REFERENCIA	REV.
1	L1T1-5420-312-CON-ED-INS-PL-0001	VDD

No.	MODELO BIM DE REFERENCIA	REV.
1	L1T1-0000-312-CON-ED-ARQ-MO-0001	VDD

No.	PAQUETE DE TRABAJO DE REFERENCIA	REV.

VDD

METRO BOGOTÁ

Consorcio Consultores PMO Bogotá

CONSORCIO SUPERVISOR PLMB

wsp
Líder de Diseño
Interfaz y
Gerencia de Integración

DISEÑÓ: WANG KEJIA Mat.: R2022011515	APROBÓ: ZHANG YUJIE Mat.: NÚMERO DE MATRÍCULA	ING_TÉCNICO_WSP Mat.: NÚMERO DE MATRÍCULA
REVISÓ: YANG BAODONG Mat.:	MODELÓ/DIBUJÓ: WANG KEJIA Mat.:R2022011515	APRO_INTEGRACIÓN_WSP Mat.: NÚMERO DE MATRÍCULA *"Aprobada bajo el marco de los límites y condiciones establecido en la tercera sección del parágrafo del apéndice 1 sección 1 del acuerdo del contrato de diseño"

REVISIÓN No.	FECHA	DESCRIPCIÓN	REVISÓ	APROBÓ	APROBACIÓN CLIENTE
VDD	05/06/2023	Emitido para revisión y comentarios del cliente e Interventoría - Incluye comentarios / modificado donde se indica en el control de cambios	Y.B.	Z.Y.	
VCC	11/10/2022	Emitido para revisión y comentarios del cliente e Interventoría - Incluye comentarios / modificado donde se indica en el control de cambios	Y.B.	Z.Y.	
VBB	09/12/2021	Emitido para revisión y comentarios del cliente e Interventoría	Y.B.	Z.Y.	
VA0	08/12/2021	Emitido para comentarios internos - Emisión preliminar para comentarios	Y.B.	Z.Y.	

METRO LÍNEA 1

METRO LÍNEA 1
CONTRATO DE CONCESIÓN N.º 163 DE 2019

PROYECTO PRIMERA LÍNEA DEL METRO DE BOGOTÁ - TRAMO 1

DIRECTOR INTERVENTORÍA: JAVIER DESCARGA N. Mat.: 25202-68697 CND	ESPECIALISTA INTERVENTORÍA: Mat.:	FECHA: JUNIO 2023

SISTEMAS Y EQUIPOS

TELECOMUNICACIONES

ESTACIÓN CALLE 10 - DISEÑO DETALLADO DEL NIVEL DE ACCESO (PARTE DESCENDENTE)
SISTEMA CCTV
COBERTURA

PLANCHA No. L1T1-5445-312-CON-ED-INS-PL-0009_04_VDD	ESCALA: 1:100	REVISIÓN No. VDD	HOJA No. 4 DE 14
ARCHIVO: L1T1-5445-312-CON-ED-INS-PL-0009_VDD.dwg	FECHA: DICIEMBRE 2021		