L1T1-CON-CAL-FR-0120 -81:1680x720mm

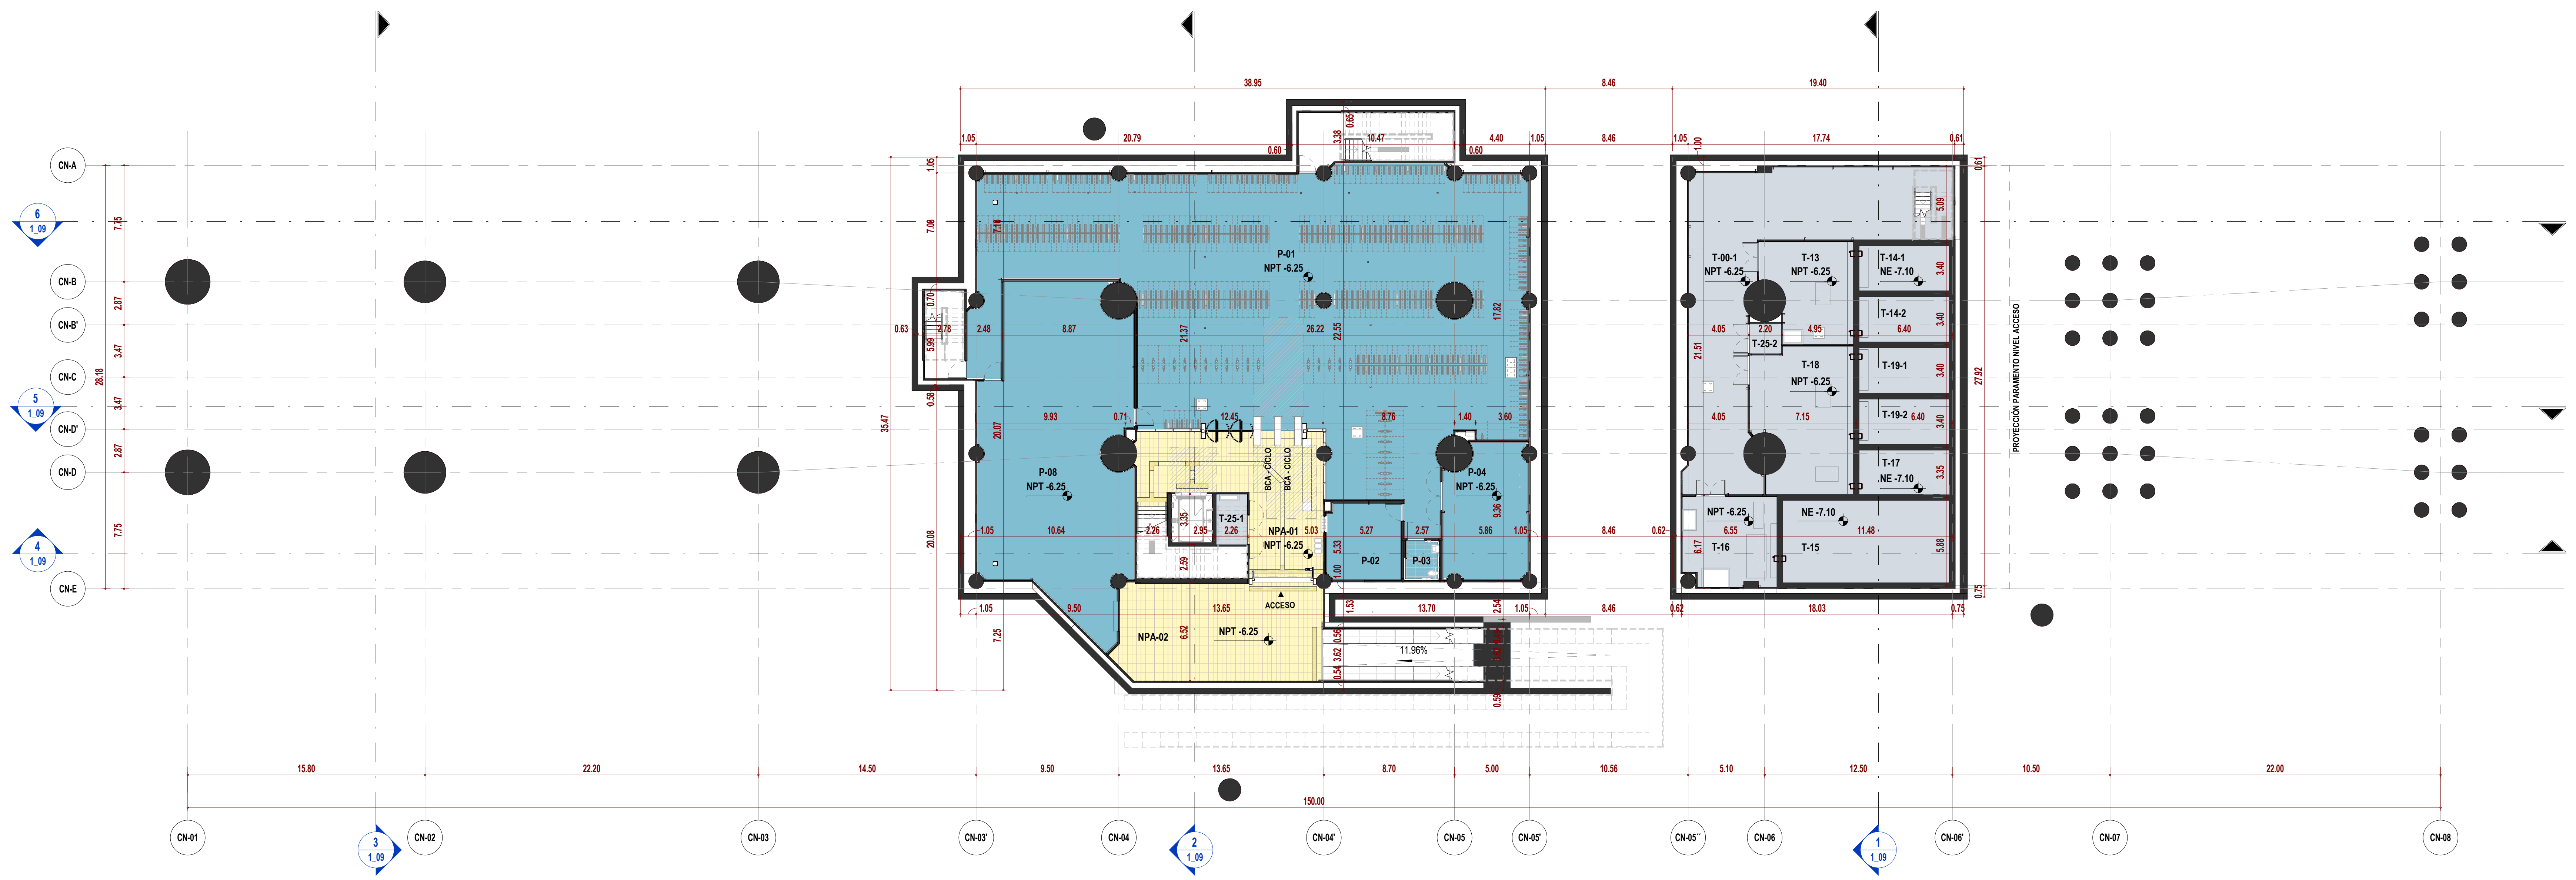

2 **NIVEL SÓTANO / ACCESO BICIUSUARIOS_NAVE CENTRAL**
ESC: 1 : 200

TABLA DE CICLO-PARQUEADEROS ESPECÍFICA		
DESCRIPCIÓN	**CANTIDAD**	**USUARIO**
BICIPARQUEADERO ASISTIDO EN ACERO INOXIDABLE ASTM A240, a=0.70m X l=1.20m, h=1.70m.	1	EMPLEADOS
BICIPARQUEADERO DE COLGAR, 2 PUESTOS, a=1.20m X l=0.70m, h=2.40m. ACABADO EN PINTURA ELECTROSTÁTICA COLOR RAL9005 "NEGRO INTENSO".	4	EMPLEADOS
EMPLEADOS	5	
BICIPARQUEADERO ASISTIDO EN ACERO INOXIDABLE ASTM A240, a=0.70m X l=1.20m, h=1.70m.	50	VISITANTE
BICIPARQUEADERO DE COLGAR, 1 PUESTO, a=1.20m X l=0.70m, h=2.40m. ACABADO EN PINTURA ELECTROSTÁTICA COLOR RAL9005 "NEGRO INTENSO".	24	VISITANTE
BICIPARQUEADERO DE COLGAR, 2 PUESTOS, a=1.20m X l=0.70m, h=2.40m. ACABADO EN PINTURA ELECTROSTÁTICA COLOR RAL9005 "NEGRO INTENSO".	70	VISITANTE
BICIPARQUEADERO DE COLGAR DE 6 PUESTOS EN ACERO, a=1.20m X l=2.10m, h=2.40m. ACABADO EN PINTURA ELECTROSTÁTICA COLOR RAL9005 "NEGRO INTENSO".	354	VISITANTE
VISITANTE	498	
TOTAL CUPOS	503	

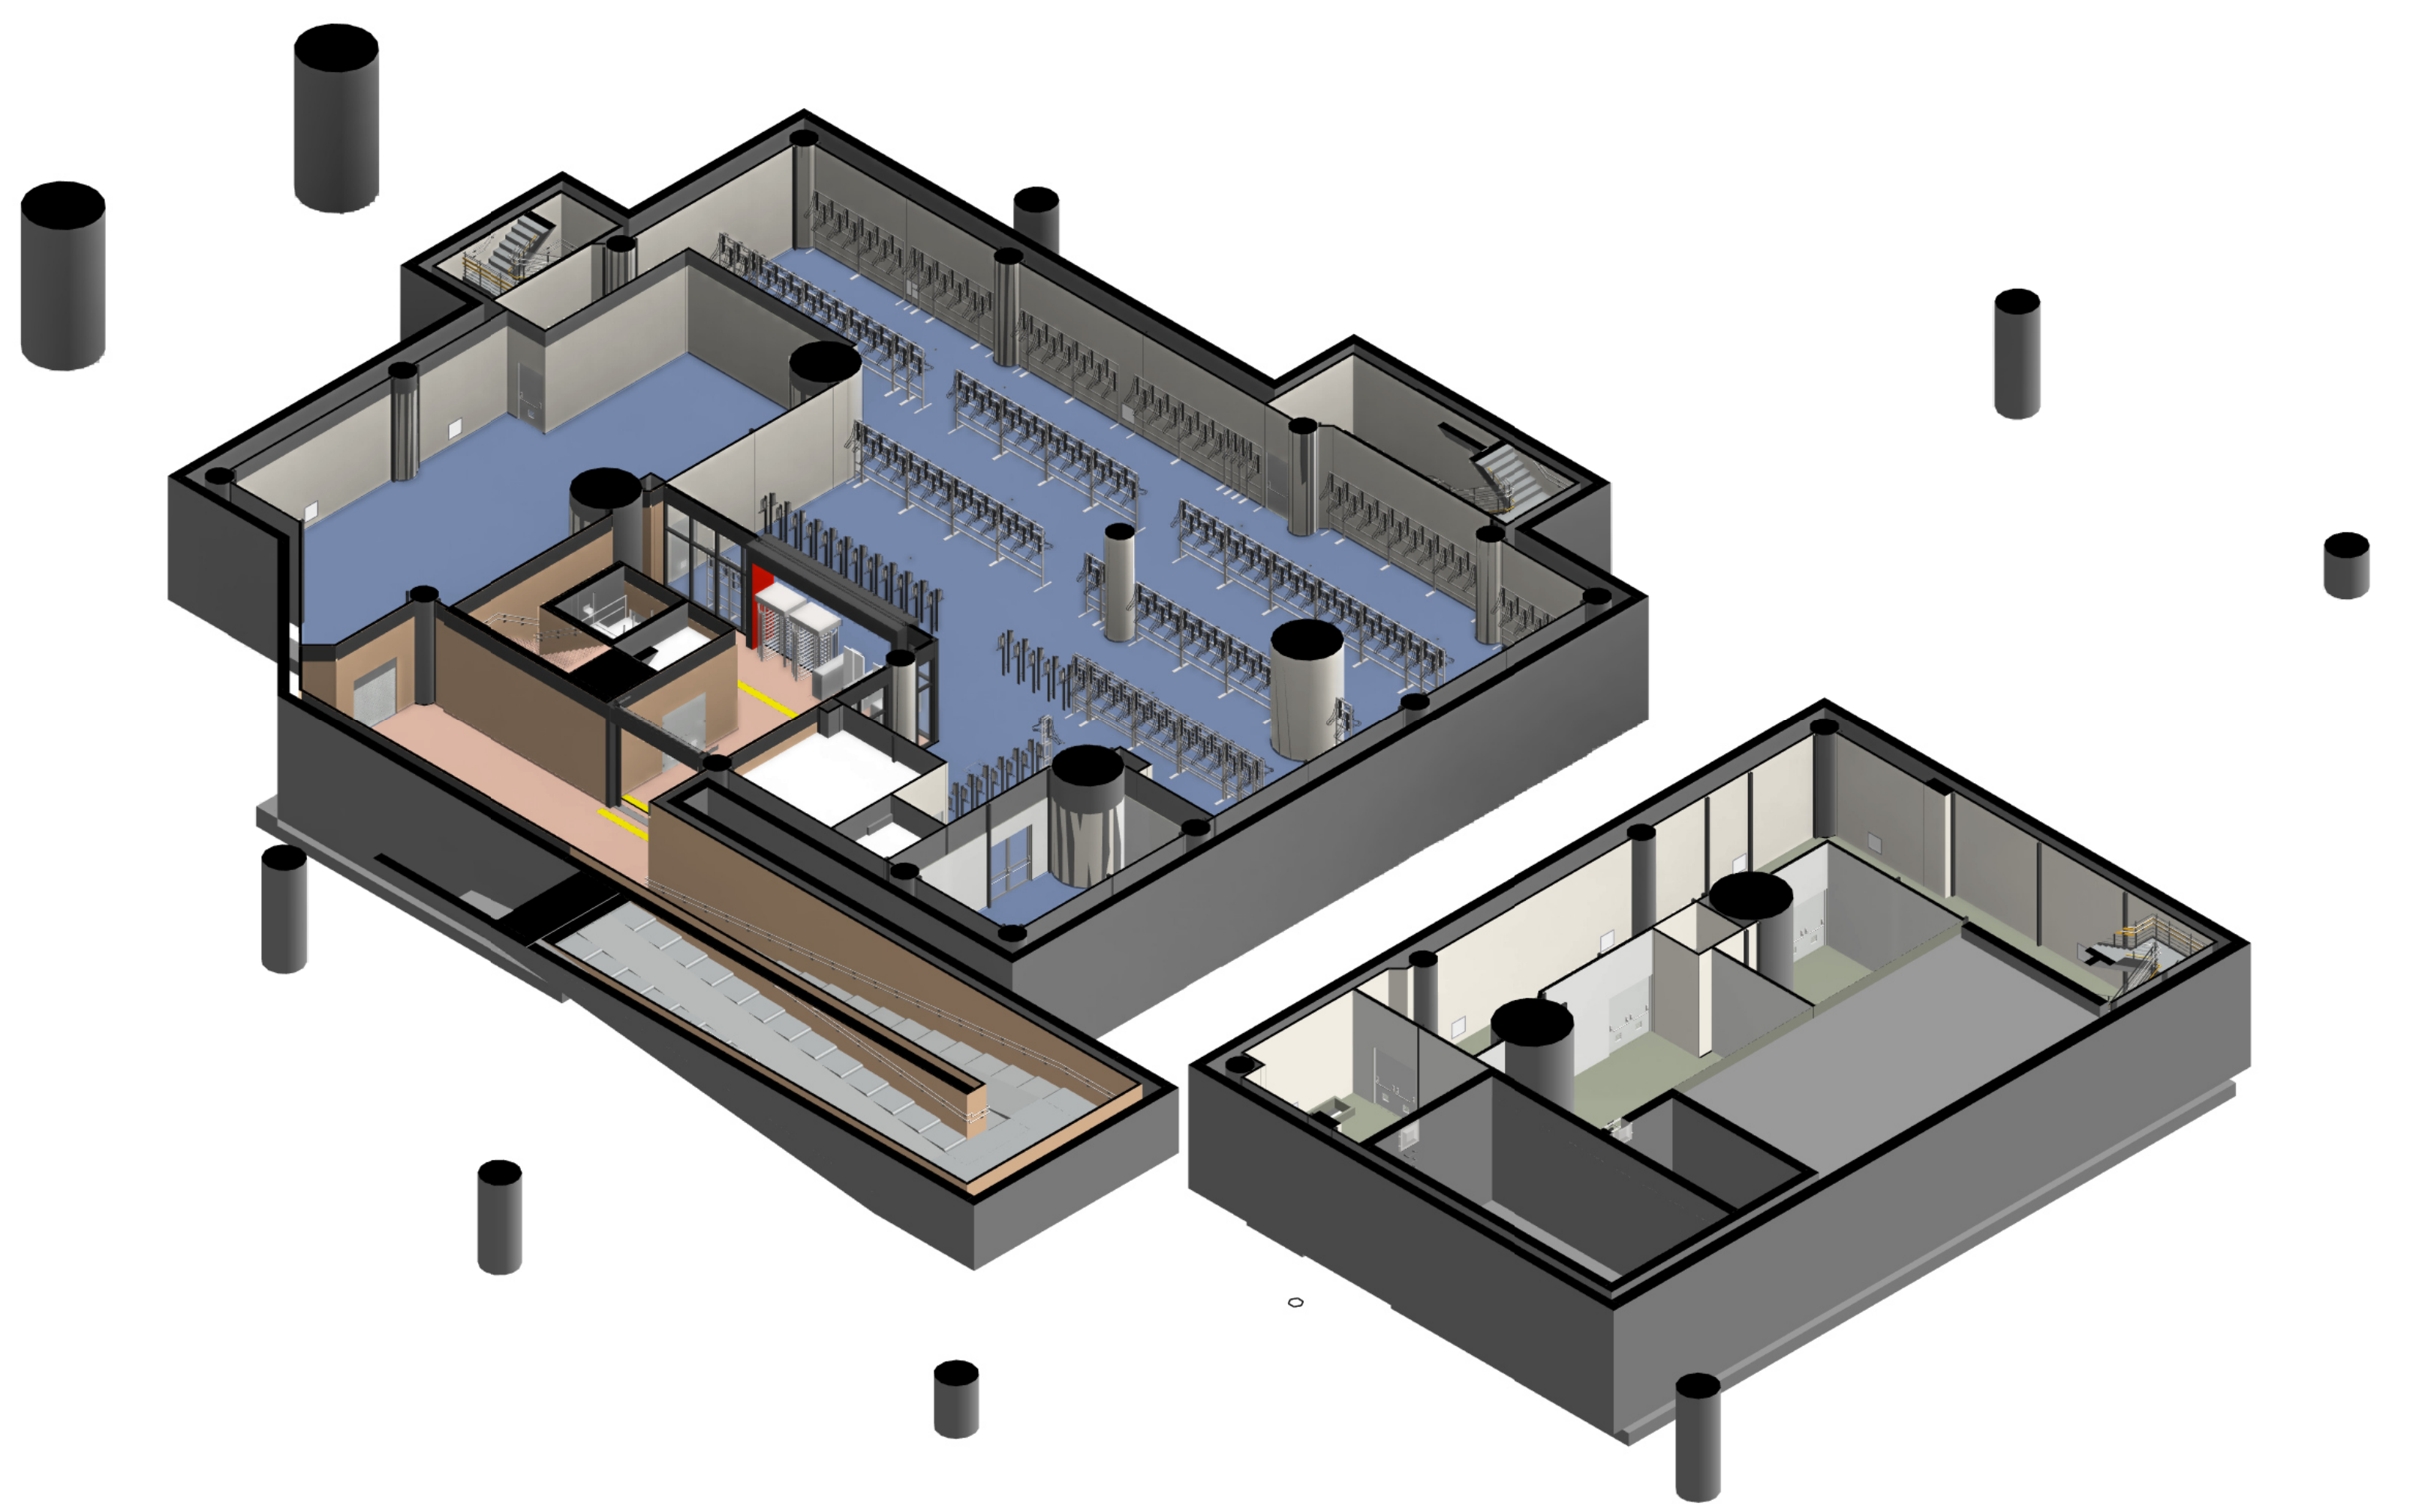

1 **3D_NIVEL SÓTANO / ACCESO BICIUSUARIOS_NAVE CENTRAL**
ESC: N/A

TABLA DE ÁREAS ÚTILES (NIVEL SÓTANO / ACCESO BICIUSUARIOS_NAVE CENTRAL)			
CÓDIGO	**NOMBRE**	**ÁREA (m²)**	**DEPARTAMENTO**
NAVE CENTRAL			
ARQ_PL_00_SÓTANO / ACCESO BICIUSUARIOS			
NPA-01	ÁREA NO PAGA	78.47	ÁREA NO PAGA
NPA-02	ÁREA NO PAGA	90.84	ÁREA NO PAGA
P-01	ÁREA CICLO-PARQUEADEROS	576.89	ÁREA PÚBLICA
P-02	ÁREA OPERATIVA CICLO-PARQUEADEROS	25.83	ÁREA PÚBLICA
P-03	BAÑO OPERADOR CICLO-PARQUEADEROS	6.19	ÁREA PÚBLICA
P-04	TALLER DE BICICLETAS	48.24	ÁREA PÚBLICA
P-08	ESPACIO CARGA DE VEHÍCULOS ELÉCTRICOS	202.14	ÁREA PÚBLICA
T-00-1	CIRCULACIÓN TÉCNICA	152.43	ÁREA TÉCNICA
T-13	CUARTO DE BOMBAS DE SUMINISTRO DE AGUA	35.80	ÁREA TÉCNICA
T-14-1	TANQUE DE SUMINISTRO DE AGUA	17.91	ÁREA TÉCNICA
T-14-2	TANQUE DE SUMINISTRO DE AGUA	17.91	ÁREA TÉCNICA
T-15	TANQUE SISTEMA DE EXTINCIÓN DE INCENDIOS (RCI)	60.57	ÁREA TÉCNICA
T-16	CUARTO DE BOMBAS PARA ROCIADORES	36.47	ÁREA TÉCNICA
T-17	TANQUE RECUPERACIÓN AGUAS LLUVIAS	17.62	ÁREA TÉCNICA
T-18	CUARTO DE BOMBAS DE RECUPERACIÓN DE AGUAS LLUVIAS Y EQUIPO DE FILTRACIÓN	65.30	ÁREA TÉCNICA
T-19-1	TANQUE DE AGUA TRATADA	17.92	ÁREA TÉCNICA
T-19-2	TANQUE DE AGUA TRATADA	17.92	ÁREA TÉCNICA
T-25-1	NODO DE ACCESO DE TELECOMUNICACIONES	6.93	ÁREA TÉCNICA
T-25-2	NODO DE ACCESO DE TELECOMUNICACIONES	4.16	ÁREA TÉCNICA
TOTAL NIVEL SÓTANO / ACCESO BICIUSUARIOS		1479.53	

TABLA DE ÁREAS ÚTILES POR DEPARTAMENTO (NIVEL SÓTANO / ACCESO BICIUSUARIOS)	
DEPARTAMENTO	**ÁREA (m²)**
ÁREA NO PAGA	169.31
ÁREA PÚBLICA	859.29
ÁREA TÉCNICA	450.94
TOTAL NIVEL SÓTANO / ACCESO BICIUSUARIOS	1479.53

LOCALIZACIÓN

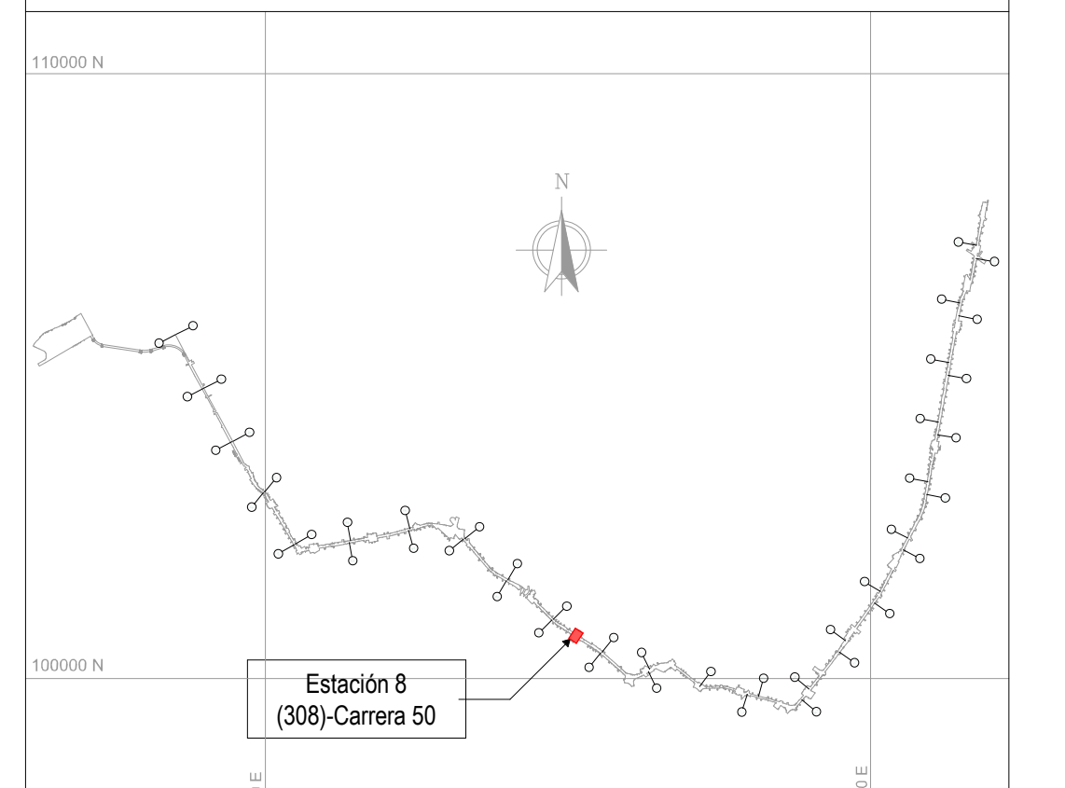

NOTAS

01 TODAS LAS DIMENSIONES ESTÁN CONFIGURADAS EN METROS A MENOS QUE SE INDIQUE UNA UNIDAD DE MEDIDA DIFERENTE.

02 TODAS LAS MEDIDAS, UBICACIÓN Y NIVELES DEBEN VERIFICARSE EN EL LUGAR DE CONSTRUCCIÓN.

03 EL NIVEL DE ACCESO AL EDIFICIO PL 01 CORRESPONDE AL +0,00 DE LA ESTACIÓN Y REFERENCIA AL NIVEL 2555.65 M.S.N.M

04 LOS NOMBRES ESPECÍFICOS DE LAS ÁREAS PUEDEN SER CONSULTADAS EN EL PLANO NO. 3 Ó EN LAS VISTAS EN PLANTA.

05 LOS COLORES QUE SE MUESTRAN EN LOS PLANOS COMO PROYECCIÓN DE ELEMENTOS ARQUITECTÓNICOS COMO CUBIERTAS FACHADAS MUROS ETC. NO REPRESENTAN LA MATERIALIDAD Y REALIDAD DE ACABADOS DEL PROYECTO, SOLO SON INDICATIVOS PARA REALIZAR UNA CORRECTA LECTURA DE LA PLANIMETRÍA.

06 SE DEBEN REVISAR LOS NIVELES ESTRUCTURALES PARA NIVEL DE ACCESO PL_01 Y SUBNIVELES, PL_02 (INTERMEDIO), PL_03 (PLATAFORMA) CON LA PLANIMETRÍA DE PLACAS ESTRUCTURALES EN LOS ENTREGABLES L1T1-1200-308-CON-ED-EST-PL-0068, 69, RESPECTIVAMENTE. EL NIVEL ESTRUCTURAL (NE) REFERENCIA LOS ESPACIOS DONDE SE DEBE ACONDICIONAR EL ACABADO DE PISO SEGÚN CORRESPONDA, CON LOS NIVELES DE PISO TERMINADO (NPT). LOS NIVELES PROYECTADOS DE EMPATE (NPE) EN LAS ÁREAS DE SERVICIOS ADICIONALES, REFERENCIAN LA ADECUACIÓN DE LOS DESNIVELES EN ESTAS ÁREAS; QUEDA COMO RESPONSABILIDAD DEL LOCATARIO DEFINIR Y ACONDICIONAR ESTE ACABADO DE PISO (NPE) EN LÍNEA CON EL NIVEL (NPT) DE ESPACIOS COLINDANTES. EL NIVEL ESTRUCTURAL (NE) SE ENCUENTRA A (- 0.10M) POR DEBAJO DE LOS NIVELES DE PISO TERMINADO (NPT) Y LOS NIVELES PROYECTADOS DE EMPATE (NPE) MARCADOS EN LA PLANIMETRÍA.

- ARC_PL_00 = SÓTANO / ACCESO BICIUSUARIOS	/ NPT -6.25
- ARC_PL_01 = ACCESO TÉCNICO	/ NPT 0.00
- ARC_PL_02 = INTERMEDIO / ACCESO PEATONAL	/ NPT 7.60
- ARC_PL_02.1 = PLACA INFERIOR VIGA CAJÓN	/ NPT 13.82
- ARC_PL_02.2 = TOPE DE RIEL (TOR)	/ NPT 15.95
- ARC_PL_03 = PLATAFORMA	/ NPT 17.09
- ARC_PL_05 = CUBIERTA NAVE CENTRAL	/ NPT 26.42

CONVENCIONES

🟩	SERVICIOS ADICIONALES - ÁREA NO PAGA	🟨	ÁREA NO PAGA
🟩	SERVICIOS ADICIONALES - ÁREA PAGA	🟦	ÁREA OPERATIVA
🟩	SERVICIO PÚBLICO	🟨	ÁREA PAGA
🟦	ZONA DE REFUGIO	🟦	ÁREA PÚBLICA
🟥	ÁREA CULTURAL	⬜	ÁREA TÉCNICA
🟪	ÁREA DE TAQUILLAS BRT		

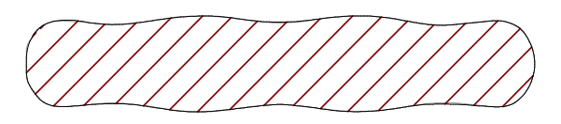

PLANO CLAVE ESTACIÓN 8

VÁLIDO PARA CONSTRUCCIÓN
12/12/2025

No.	PLANOS DE REFERENCIA	REV.

No.	MODELO BIM DE REFERENCIA	REV.
1	L1T1-1100-208-CON-ED-EST-MO-0001.rvt	V00
2	L1T1-1100-209-CON-ED-EST-MO-0001.rvt	V00
3	L1T1-1100-308-CON-ED-EST-MO-0001.rvt	V00
4	L1T1-1150-208-CON-ED-EST-MO-0001.rvt	V00
5	L1T1-1150-209-CON-ED-EST-MO-0001.rvt	V00
6	L1T1-1150-308-CON-ED-EST-MO-0001.rvt	V00
7	L1T1-1200-308-CON-ED-EST-MO-0001.rvt	V00
8	L1T1-1410-308-CON-ED-MEC-MO-0001.rvt	V00
9	L1T1-1420-308-CON-ED-MEC-MO-0001.rvt	V00
10	L1T1-2420-561-CON-ED-EST-MO-0001.rvt	V00
11	L1T1-5160-308-CON-ED-EST-MO-0001.rvt	V00
12	L1T1-5160-308-CON-ED-ARQ-MO-0001.rvt	V00
13	L1T1-5300-308-CON-ED-MEC-MO-0001.rvt	V00

No.	PAQUETE DE TRABAJO DE REFERENCIA	REV.
1	XREF-URBANISM_CONTEXT_ST08.rvt	
2	XREF-SECONDARY-STRUCTURE-ST08.rvt	

0 2 10m
1:200

METRO BOGOTÁ
Consorcio Consultores PMO Bogotá
CONSORCIO SUPERVISOR PLMB
wsp

DISEÑÓ: Santiago A. David G.
SANTIAGO ANDRES DAVID GUZMÁN
Mat.: A413202011-1010176190

APROBÓ: Firmado digitalmente por MAURICIO MEJIA RESTREPO Fecha: 2026.01.26 15:49:31 -05'00'
MAURICIO MEJÍA RESTREPO
Mat.: 25202-72411 CND

REVISÓ: Digitally signed by Bautista Rondón, Freddy (COFB100240)
FREDDY BAUTISTA R.
Mat.:25202-092831 CND

DIBUJÓ:
EQUIPO WSP

REVISIÓN No.	FECHA	DESCRIPCIÓN	REVISÓ	APROBÓ	APROBACIÓN CLIENTE
V00	12/12/2025	REVISIÓN NO OBJETADA - EMITIDO PARA CONSTRUCCIÓN	F.B.R	M.M.R	
VCC	01/10/2025	EMITIDO PARA REVISIÓN Y COMENTARIOS DEL CLIENTE E INTERVENTORÍA - INCLUYE COMENTARIOS /(AJUSTE)	F.B.R	M.M.R	
VBB	15/07/2025	EMITIDO PARA REVISIÓN Y COMENTARIOS DEL CLIENTE E INTERVENTORÍA	F.B.R	M.M.R	
VA0	04/07/2025	EMITIDO PARA COMENTARIOS INTERNOS - EMISIÓN PRELIMINAR PARA COMENTARIOS	F.B.R	M.M.R	

METRO LÍNEA 1

DIRECTOR DE INTERVENTORÍA:
JAVIER DESCARGA N.
Mat.:25202-68697 CND
Firmado digitalmente por JAVIER DESCARGA NAPOLES
DN: cn=JAVIER DESCARGA NAPOLES, c=CO, o=CONSORCIO SUPERVISOR PLMB, ou=DIRECCION GENERAL, email=jdescarga@ayesa.com
Motivo: Estoy de acuerdo con las partes indicadas de este documento
Fecha: 2026.04.23 14:44:30 -05'00'

ESPECIALISTA INTERVENTORÍA:
MARIA AUXILIADORA SANCHEZ HERMOSIN
INT: PAH138382-RES.NO.34 DE 2021
Firmado digitalmente por Maria Auxiliadora Sánchez Hermosin
DN: cn=Maria Auxiliadora Sánchez Hermosin, c=CO Colombia, o=Consorcio Supervisor PLMB, ou=Especialista Arquitectura, email=masanchezh@ayesa.com
Motivo: Estoy de acuerdo con las partes indicadas de este documento
Fecha: 2026.04.23 14:17:10 -05'00'

FECHA:
DICIEMBRE 2025

METRO LÍNEA 1
CONTRATO DE CONCESIÓN No. 163 DE 2019

PROYECTO PRIMERA LÍNEA DEL METRO DE BOGOTÁ - TRAMO 1

INFRAESTRUCTURA VIAL

ARQUITECTURA

ESTACIÓN METRO 8 (CARRERA 50)
NAVE CENTRAL
VISTA EN PLANTA Y 3D - NIVEL SÓTANO / ACCESO BICIUSUARIOS

PLANCHA No: L1T1-0000-308-CON-ED-ARQ-PL-0022_04_V00	ESCALA: INDICADA	REVISIÓN No.	PLANO No.
ARCHIVO: L1T1-0000-308-CON-ED-ARQ-MO-0002_V00.rvt	FECHA: JULIO 2025	V00	04 DE 47