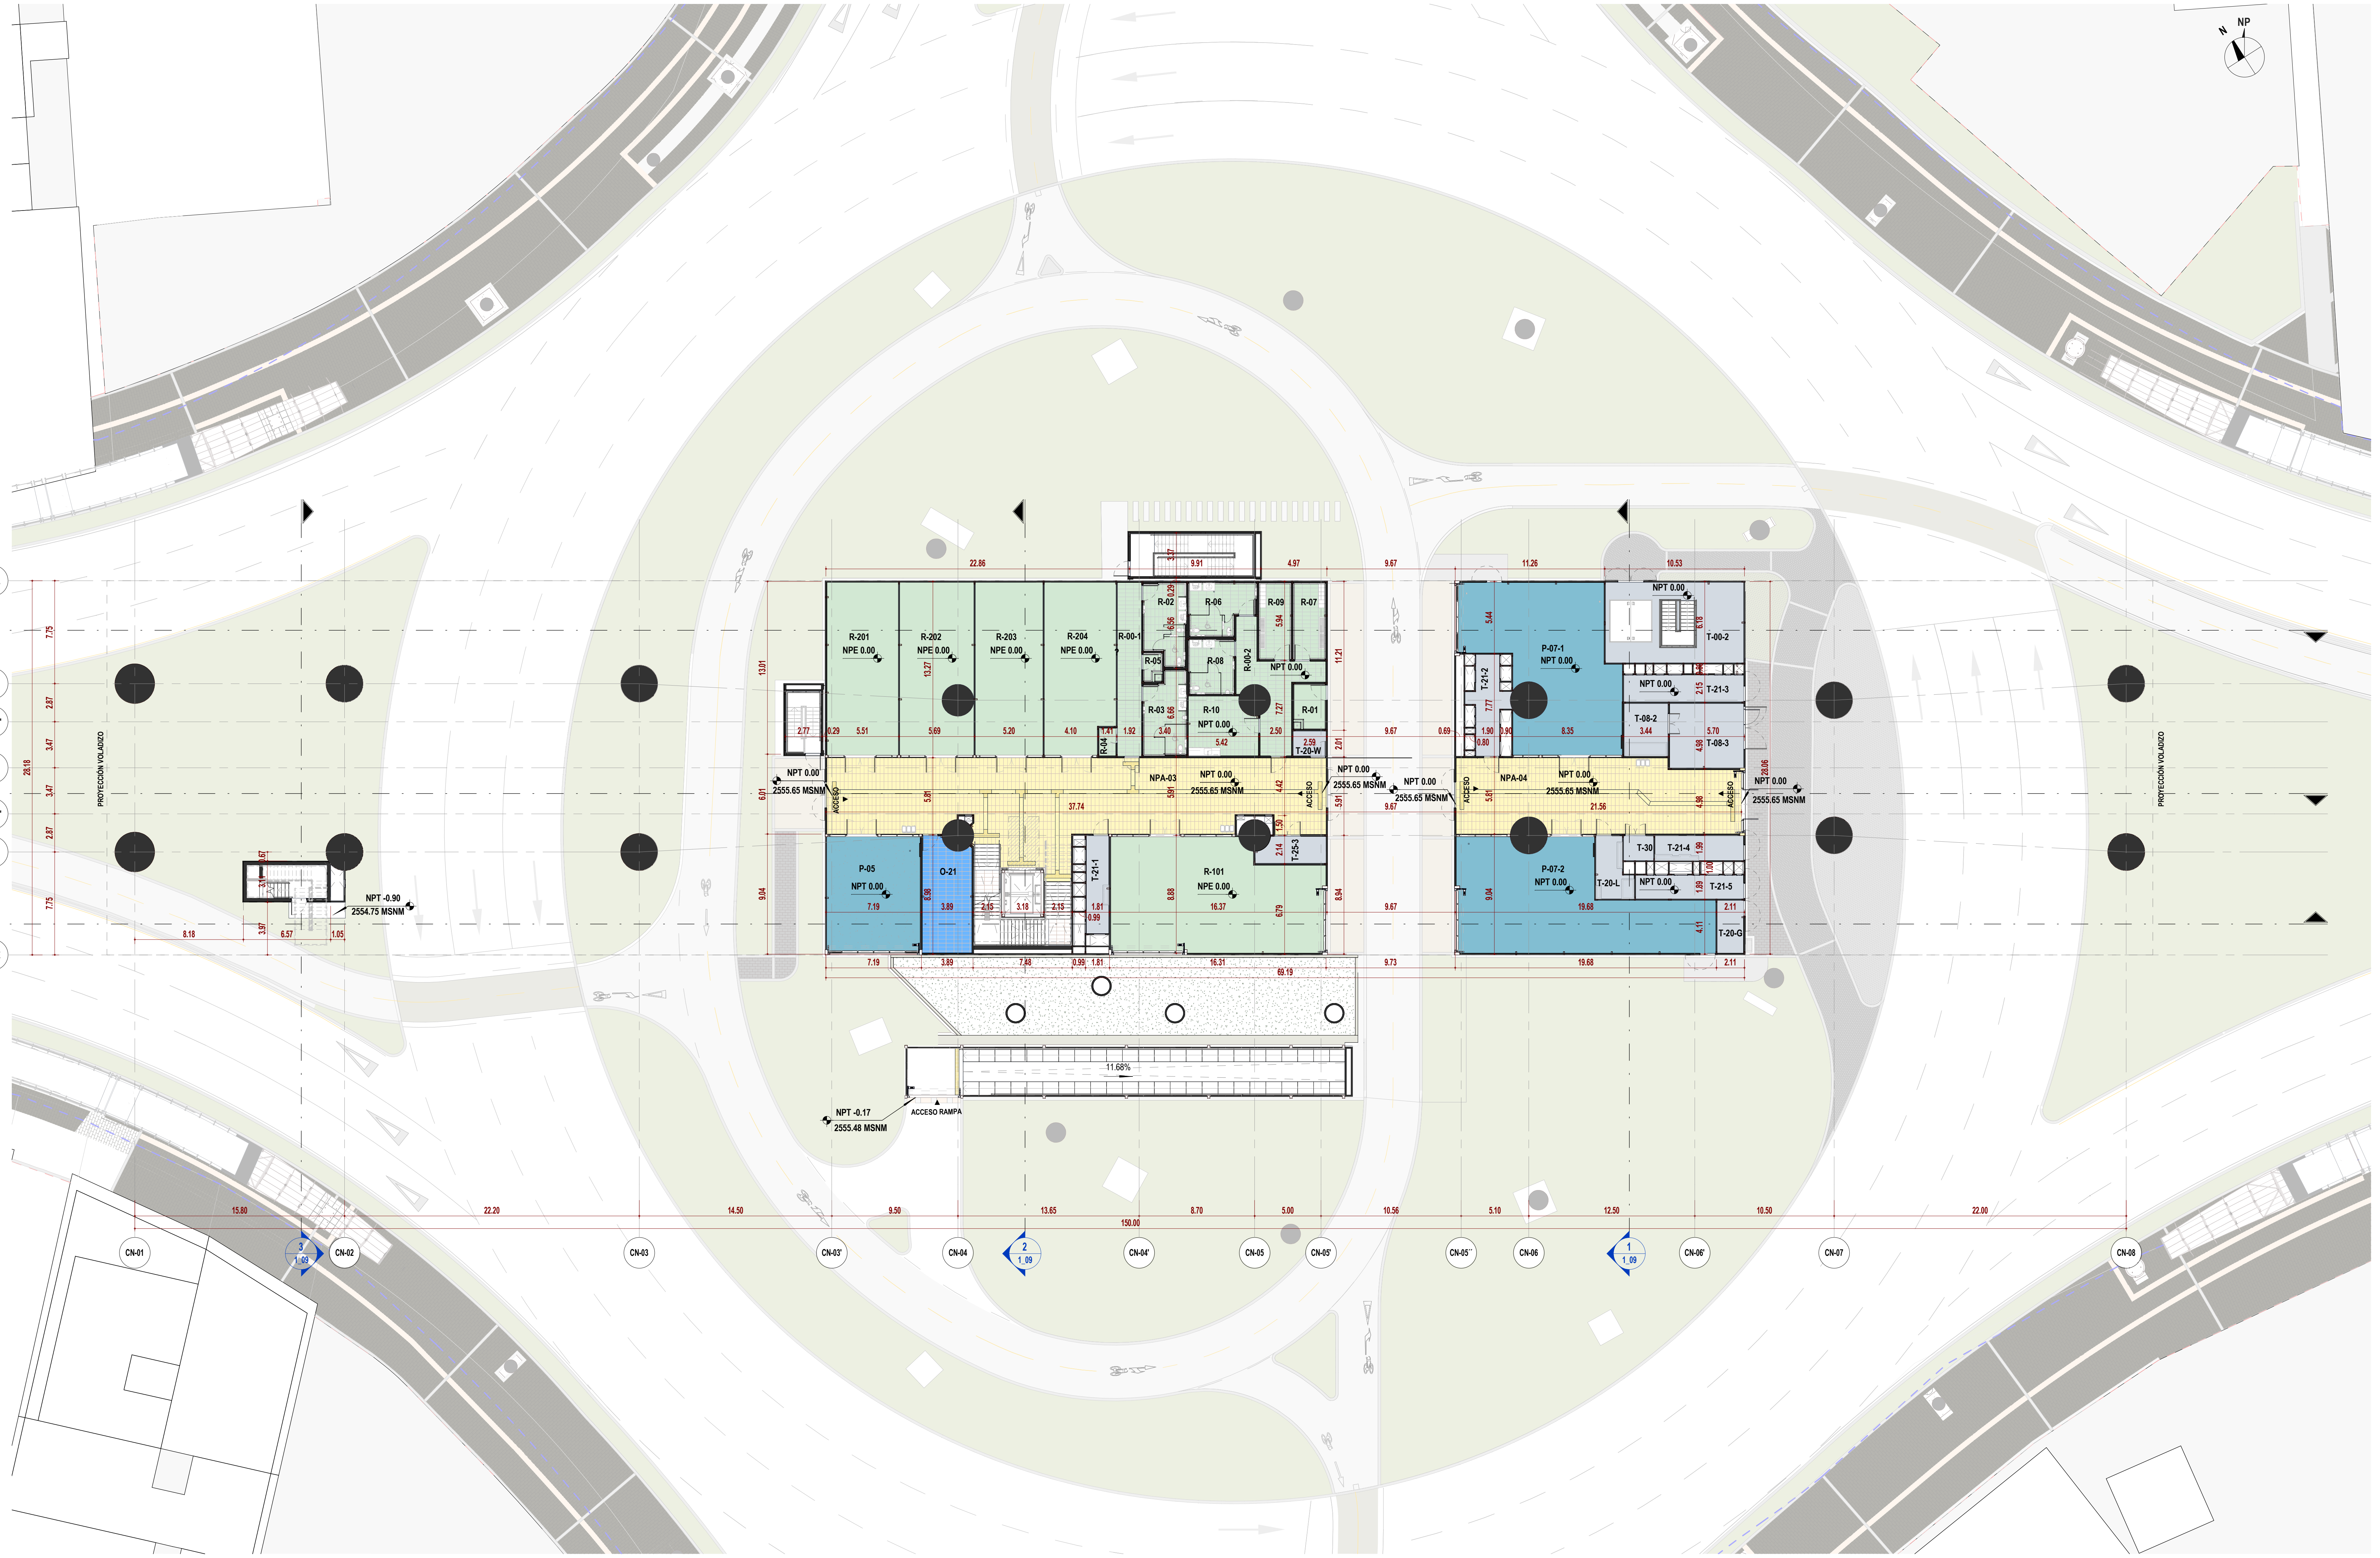

2 **NIVEL ACCESO TÉCNICO_NAVE CENTRAL**
ESC: 1 : 200

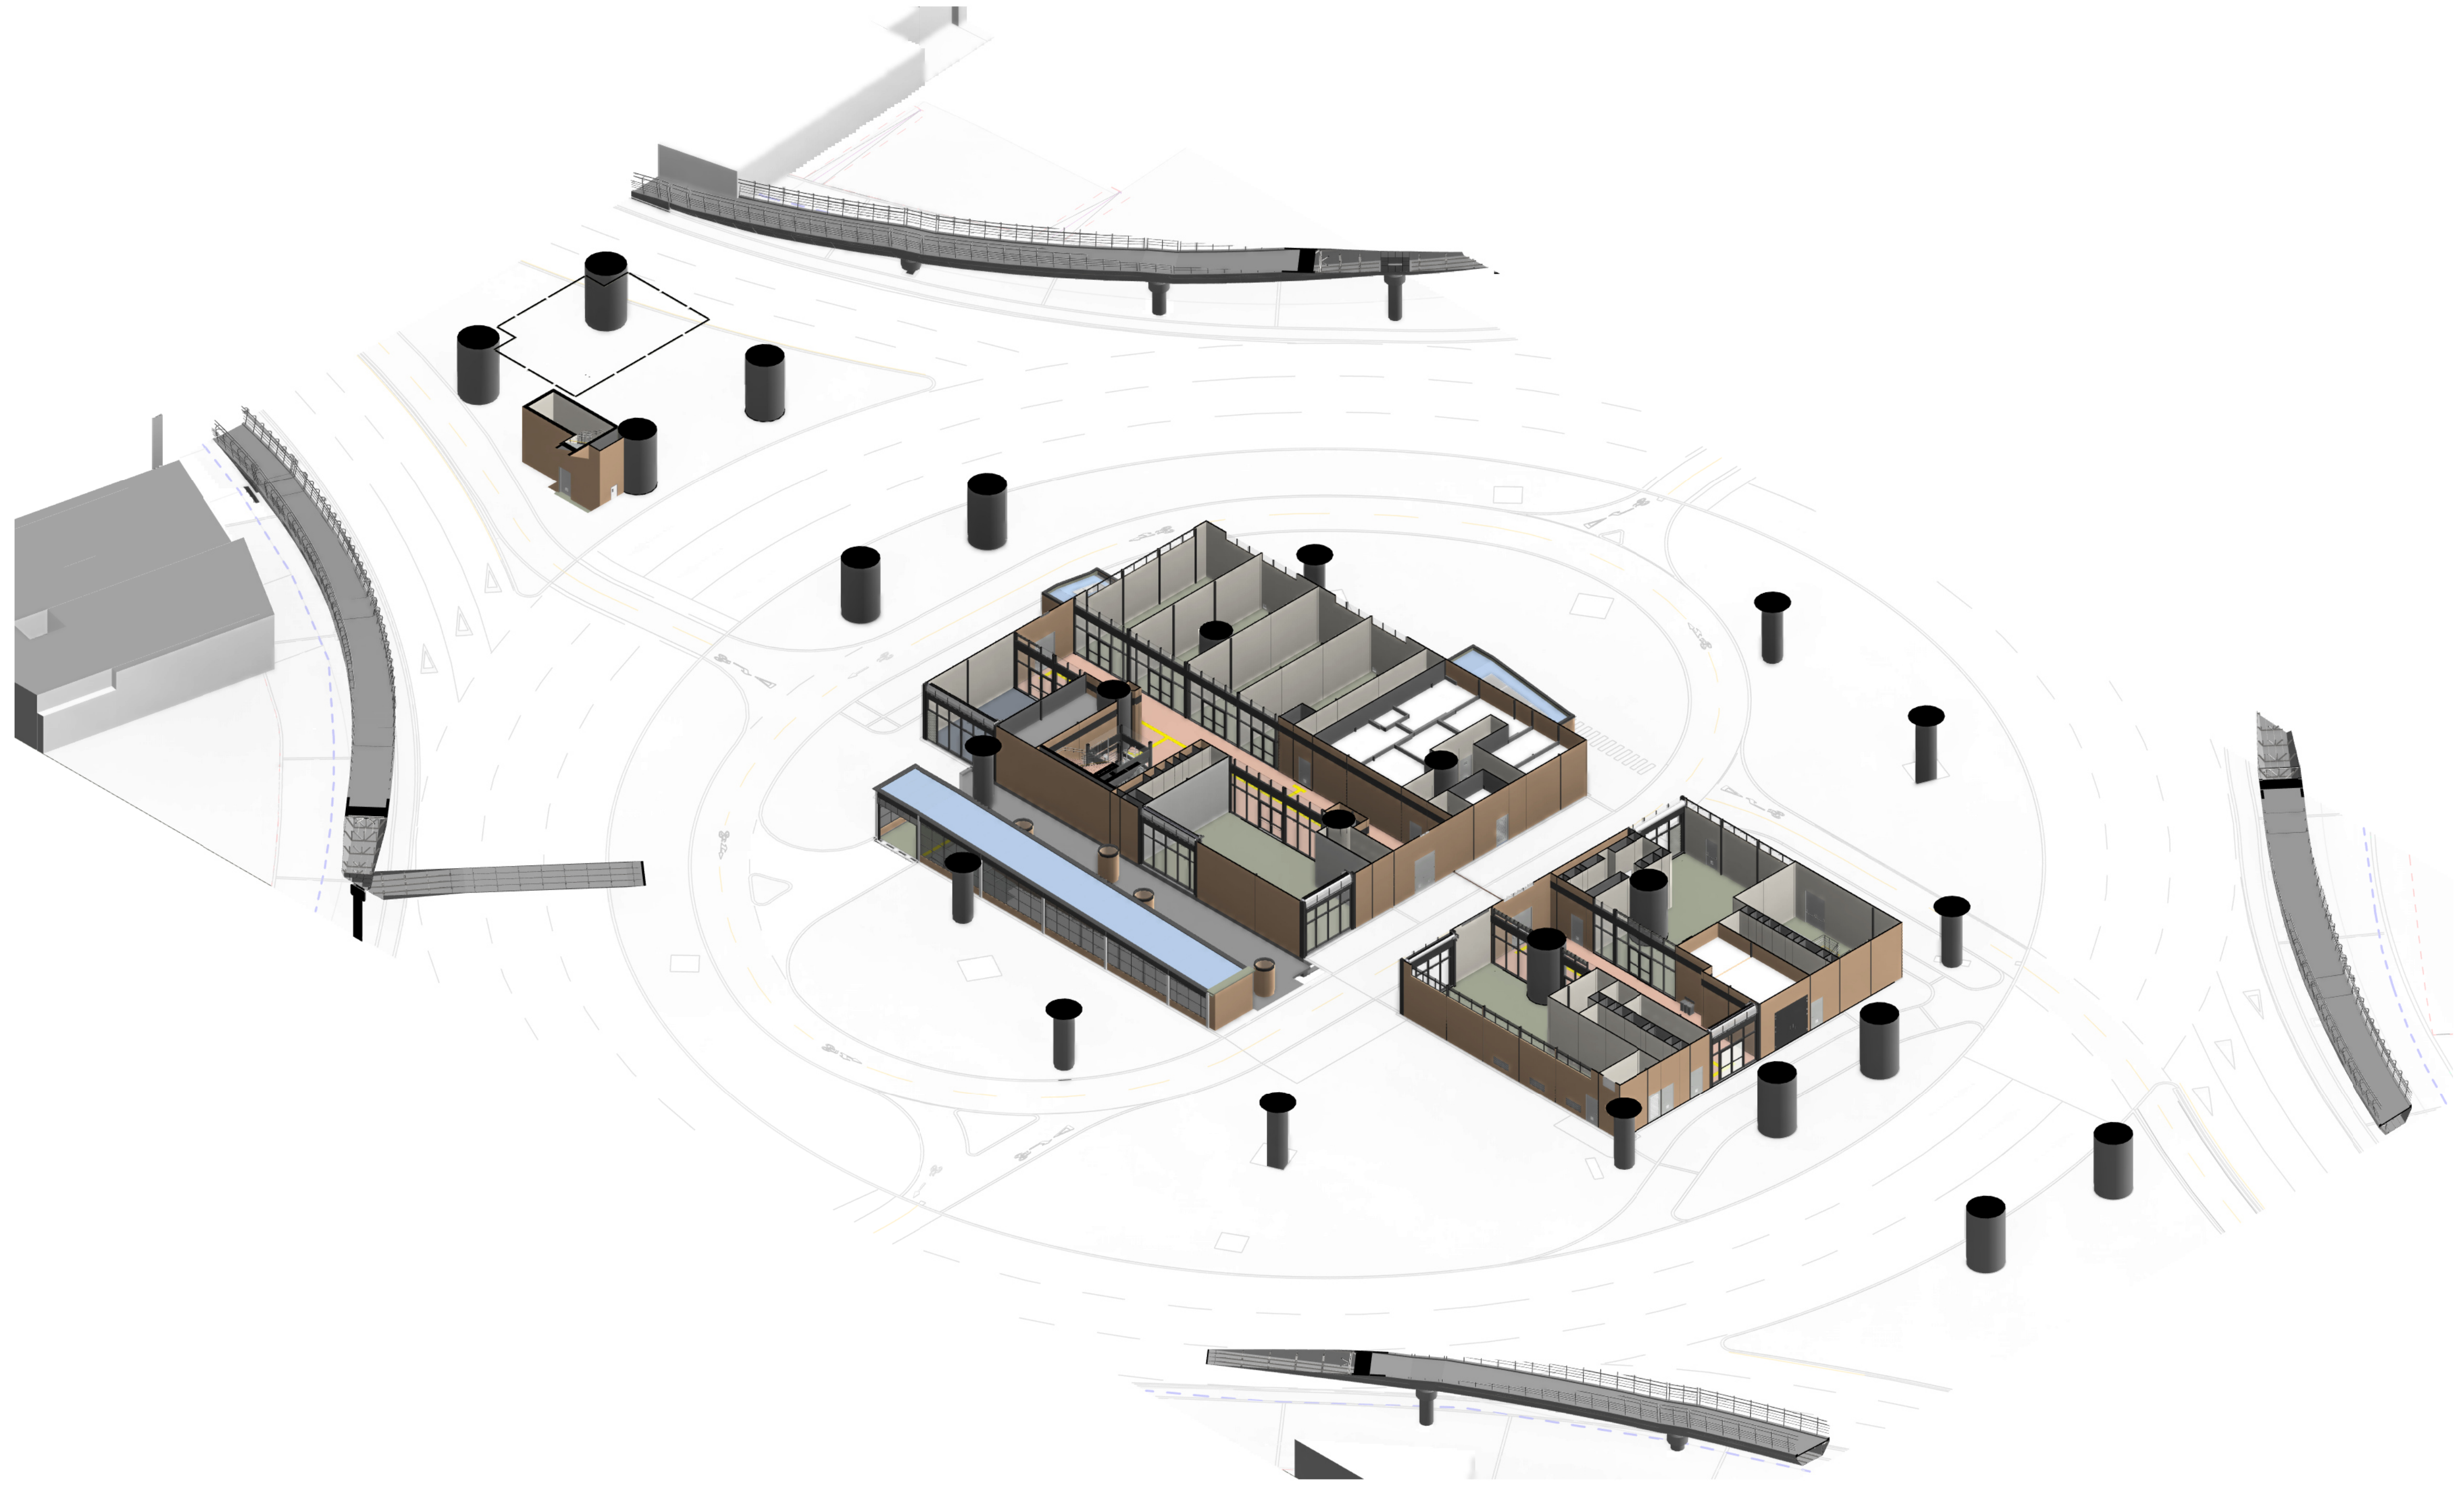

1 **3D_NIVEL ACCESO TÉCNICO_NAVE CENTRAL**
ESC: N/A

TABLA DE AREAS ÚTILES (NIVEL ACCESO TÉCNICO NAVE CENTRAL)			
CÓDIGO	**NOMBRE**	**ÁREA (m²)**	**DEPARTAMENTO**
NAVE CENTRAL			
ARQ_PL_01_ACCESO TÉCNICO			
NPA-03	ÁREA NO PAGA	228.01	ÁREA NO PAGA
NPA-04	ÁREA NO PAGA	116.92	ÁREA NO PAGA
O-21	ALMACENAMIENTO DE LA ESTACIÓN	31.11	ÁREA OPERATIVA
P-05	BIBLIOMETRO	60.37	ÁREA PÚBLICA
P-07-1	SALÓN MÚLTIPLE EMB	114.35	ÁREA PÚBLICA
P-07-2	SALÓN MÚLTIPLE EMB	124.15	ÁREA PÚBLICA
R-00-1	SERVICIOS ADICIONALES - CORREDOR OPERATIVO	23.69	SERVICIOS ADICIONALES - ÁREA NO PAGA
R-00-2	SERVICIOS ADICIONALES - CORREDOR OPERATIVO	28.87	SERVICIOS ADICIONALES - ÁREA NO PAGA
R-01	SERVICIOS ADICIONALES - CUARTO DE BASURAS PARA METRO	8.26	SERVICIOS ADICIONALES - ÁREA NO PAGA
R-02	SERVICIOS ADICIONALES - BAÑO PÚBLICO DE MUJERES	18.30	SERVICIOS ADICIONALES - ÁREA NO PAGA
R-03	SERVICIOS ADICIONALES - BAÑO PÚBLICO DE HOMBRES	19.13	SERVICIOS ADICIONALES - ÁREA NO PAGA
R-04	SERVICIOS ADICIONALES - CONTROL DE ACCESO BAÑOS PÚBLICOS	2.78	SERVICIOS ADICIONALES - ÁREA NO PAGA
R-05	SERVICIOS ADICIONALES - CUARTO DE LIMPIEZA	3.10	SERVICIOS ADICIONALES - ÁREA NO PAGA
R-06	SERVICIOS ADICIONALES - BAÑOS EMPLEADOS MUJERES	17.74	SERVICIOS ADICIONALES - ÁREA NO PAGA
R-07	SERVICIOS ADICIONALES - VESTIDORES EMPLEADOS MUJERES	14.06	SERVICIOS ADICIONALES - ÁREA NO PAGA
R-08	SERVICIOS ADICIONALES - BAÑOS EMPLEADOS HOMBRES	13.97	SERVICIOS ADICIONALES - ÁREA NO PAGA
R-09	SERVICIOS ADICIONALES - VESTIDORES EMPLEADOS HOMBRES	14.12	SERVICIOS ADICIONALES - ÁREA NO PAGA
R-10	SERVICIOS ADICIONALES - SALA DE EMPLEADOS	22.00	SERVICIOS ADICIONALES - ÁREA NO PAGA
R-101	SERVICIOS ADICIONALES - ÁREA DE SERVICIO	127.81	SERVICIOS ADICIONALES - ÁREA NO PAGA
R-201	SERVICIOS ADICIONALES - ÁREA DE COMIDAS	68.31	SERVICIOS ADICIONALES - ÁREA NO PAGA
R-202	SERVICIOS ADICIONALES - ÁREA DE COMIDAS	68.02	SERVICIOS ADICIONALES - ÁREA NO PAGA
R-203	SERVICIOS ADICIONALES - ÁREA DE COMIDAS	66.17	SERVICIOS ADICIONALES - ÁREA NO PAGA
R-204	SERVICIOS ADICIONALES - ÁREA DE COMIDAS	67.09	SERVICIOS ADICIONALES - ÁREA NO PAGA
T-00-2	CIRCULACIÓN TÉCNICA	62.96	ÁREA TÉCNICA
T-08-2	CENTRO DE TRANSFORMACIÓN ENEL-CODENSA (CT)_CUARTO BAJA TENSIÓN	13.00	ÁREA TÉCNICA
T-08-3	CENTRO DE TRANSFORMACIÓN ENEL-CODENSA (CT)_CUARTO MEDIA TENSIÓN	26.86	ÁREA TÉCNICA
T-20-G	MEDIDORES (GAS)	7.88	ÁREA TÉCNICA
T-20-L	MEDIDORES (LUZ)	11.03	ÁREA TÉCNICA
T-20-W	MEDIDORES (AGUA)	4.63	ÁREA TÉCNICA
T-21-1	ÁREA DE INSPECCIÓN	12.52	ÁREA TÉCNICA

TABLA DE AREAS ÚTILES (NIVEL ACCESO TÉCNICO NAVE CENTRAL)			
CÓDIGO	**NOMBRE**	**ÁREA (m²)**	**DEPARTAMENTO**
T-21-2	ÁREA DE INSPECCIÓN	15.55	ÁREA TÉCNICA
T-21-3	ÁREA DE INSPECCIÓN	18.21	ÁREA TÉCNICA
T-21-4	ÁREA DE INSPECCIÓN	12.38	ÁREA TÉCNICA
T-21-5	ÁREA DE INSPECCIÓN	14.45	ÁREA TÉCNICA
T-25-3	NODO DE ACCESO DE TELECOMUNICACIONES	9.76	ÁREA TÉCNICA
T-30	SISTEMA PROTECCIÓN CONTRA INCENDIO ENEL	4.18	ÁREA TÉCNICA
TOTAL NIVEL ACCESO TÉCNICO		1471.72	

TABLA DE ÁREAS ÚTILES POR DEPARTAMENTO (NIVEL ACCESO TÉCNICO)	
DEPARTAMENTO	**ÁREA (m²)**
SERVICIOS ADICIONALES - ÁREA NO PAGA	583.41
ÁREA NO PAGA	344.92
ÁREA OPERATIVA	31.11
ÁREA PÚBLICA	298.87
ÁREA TÉCNICA	213.41
TOTAL NIVEL ACCESO TÉCNICO	1471.72

LOCALIZACIÓN

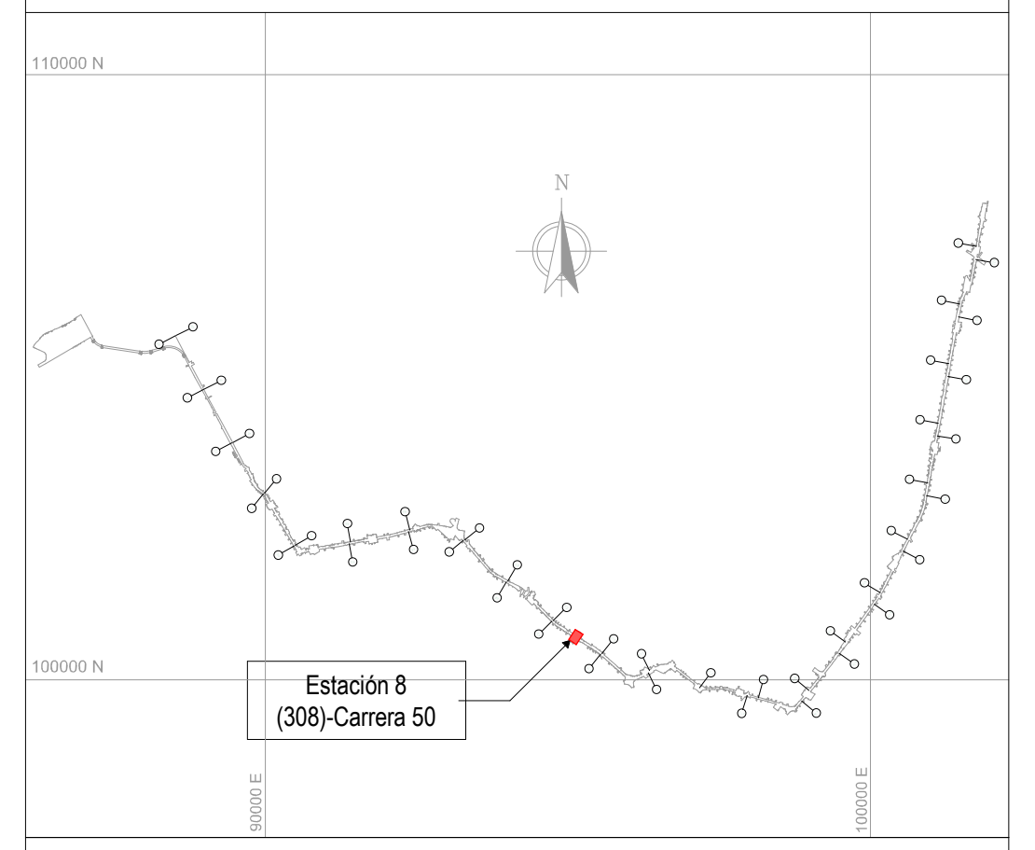

NOTAS

01 TODAS LAS DIMENSIONES ESTÁN CONFIGURADAS EN METROS A MENOS QUE SE INDIQUE UNA UNIDAD DE MEDIDA DIFERENTE.

02 TODAS LAS MEDIDAS, UBICACIÓN Y NIVELES DEBEN VERIFICARSE EN EL LUGAR DE CONSTRUCCIÓN.

03 EL NIVEL DE ACCESO AL EDIFICIO PL 01 CORRESPONDE AL +0,00 DE LA ESTACIÓN Y REFERENCIA AL NIVEL 2555.65 M.S.N.M

04 LOS NOMBRES ESPECÍFICOS DE LAS ÁREAS PUEDEN SER CONSULTADAS EN EL PLANO NO. 3 Ó EN LAS VISTAS EN PLANTA.

05 LOS COLORES QUE SE MUESTRAN EN LOS PLANOS COMO PROYECCIÓN DE ELEMENTOS ARQUITECTÓNICOS COMO CUBIERTAS FACHADAS MUROS ETC. NO REPRESENTAN LA MATERIALIDAD Y REALIDAD DE ACABADOS DEL PROYECTO, SOLO SON INDICATIVOS PARA REALIZAR UNA CORRECTA LECTURA DE LA PLANIMETRÍA.

06 LAS ESCALERAS ELÉCTRICAS INDICAN SU SENTIDO CON LA SIGUIENTE NOMENCLATURA: "SUBE" Y "BAJA".

07 SE DEBEN REVISAR LOS NIVELES ESTRUCTURALES PARA NIVEL DE ACCESO PL_01 Y SUBNIVELES, PL_02 (INTERMEDIO), PL_03 (PLATAFORMA) CON LA PLANIMETRÍA DE PLACAS ESTRUCTURALES EN LOS ENTREGABLES L1T1-1200-308-CON-ED-EST-PL-0068, 69, RESPECTIVAMENTE. EL NIVEL ESTRUCTURAL (NE) REFERENCIA LOS ESPACIOS DONDE SE DEBE ACONDICIONAR EL ACABADO DE PISO SEGÚN CORRESPONDA, CON LOS NIVELES DE PISO TERMINADO (NPT). LOS NIVELES PROYECTADOS DE EMPATE (NPE) EN LAS ÁREAS DE SERVICIOS ADICIONALES, REFERENCIAN LA ADECUACIÓN DE LOS DESNIVELES EN ESTAS ÁREAS; QUEDA COMO RESPONSABILIDAD DEL LOCATARIO DEFINIR Y ACONDICIONAR ESTE ACABADO DE PISO (NPE) EN LÍNEA CON EL NIVEL (NPT) DE ESPACIOS COLINDANTES. EL NIVEL ESTRUCTURAL (NE) SE ENCUENTRA A (- 0.10M) POR DEBAJO DE LOS NIVELES DE PISO TERMINADO (NPT) Y LOS NIVELES PROYECTADOS DE EMPATE (NPE) MARCADOS EN LA PLANIMETRÍA.

- ARC_PL_00 = SÓTANO / ACCESO BICIUSUARIOS	/ NPT -6.25
- ARC_PL_01 = ACCESO TÉCNICO	/ NPT 0.00
- ARC_PL_02 = INTERMEDIO / ACCESO PEATONAL	/ NPT 7.60
- ARC_PL_02.1 = PLACA INFERIOR VIGA CAJÓN	/ NPT 13.82
- ARC_PL_02.2 = TOPE DE RIEL (TOR)	/ NPT 15.95
- ARC_PL_03 = PLATAFORMA	/ NPT 17.09
- ARC_PL_05 = CUBIERTA NAVE CENTRAL	/ NPT 26.42

CONVENCIONES

🟩	SERVICIOS ADICIONALES - ÁREA NO PAGA	🟨	ÁREA NO PAGA
🟩	SERVICIOS ADICIONALES - ÁREA PAGA	🟦	ÁREA OPERATIVA
🟩	SERVICIO PÚBLICO	🟧	ÁREA PAGA
🟦	ZONA DE REFUGIO	🟦	ÁREA PÚBLICA
🟥	ÁREA CULTURAL	⬜	ÁREA TÉCNICA
🟪	ÁREA DE TAQUILLAS BRT		

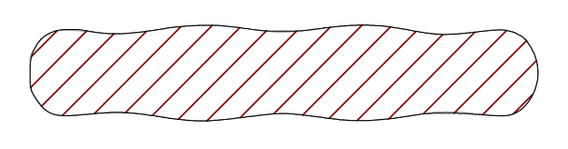

PLANO CLAVE ESTACIÓN 8

VÁLIDO PARA CONSTRUCCIÓN
12/12/2025

No.	**PLANOS DE REFERENCIA**	**REV.**
No.	**MODELO BIM DE REFERENCIA**	**REV.**
1	L1T1-1100-208-CON-ED-EST-MO-0001.rvt	V00
2	L1T1-1100-209-CON-ED-EST-MO-0001.rvt	V00
3	L1T1-1100-308-CON-ED-EST-MO-0001.rvt	V00
4	L1T1-1150-208-CON-ED-EST-MO-0001.rvt	V00
5	L1T1-1150-209-CON-ED-EST-MO-0001.rvt	V00
6	L1T1-1150-308-CON-ED-EST-MO-0001.rvt	V00
7	L1T1-1200-308-CON-ED-EST-MO-0001.rvt	V00
8	L1T1-1410-308-CON-ED-MEC-MO-0001.rvt	V00
9	L1T1-1420-308-CON-ED-MEC-MO-0001.rvt	V00
10	L1T1-2420-561-CON-ED-EST-MO-0001.rvt	V00
11	L1T1-5160-308-CON-ED-EST-MO-0001.rvt	V00
12	L1T1-5160-308-CON-ED-ARQ-MO-0001.rvt	V00
13	L1T1-5300-308-CON-ED-MEC-MO-0001.rvt	V00
No.	**PAQUETE DE TRABAJO DE REFERENCIA**	**REV.**
1	XREF-URBANISM_CONTEXT_ST08.rvt	
2	XREF-SECONDARY-STRUCTURE-ST08.rvt	

0 2 10m
1:200

METRO BOGOTÁ
Consorcio Consultores PMO Bogotá
CONSORCIO SUPERVISOR PLMB

DISEÑÓ:
SANTIAGO ANDRES DAVID GUZMÁN
Mat.: A413202011-1010176190

APROBÓ:
Firmado digitalmente por MAURICIO MEJIA RESTREPO
Fecha: 2026.01.26 15:49:51 -05'00'
MAURICIO MEJÍA RESTREPO
Mat.: 25202-72411 CND

REVISÓ:
Digitally signed by Bautista Rondón, Freddy (COFB100240)
FREDDY BAUTISTA R.
Mat.:25202-092831 CND

DIBUJÓ:
EQUIPO WSP

REVISIÓN No.	FECHA	DESCRIPCIÓN	REVISÓ	APROBÓ	APROBACIÓN CLIENTE
V00	12/12/2025	REVISIÓN NO OBJETADA - EMITIDO PARA CONSTRUCCIÓN	F.B.R	M.M.R	
VCC	01/10/2025	EMITIDO PARA REVISIÓN Y COMENTARIOS DEL CLIENTE E INTERVENTORÍA - INCLUYE COMENTARIOS /(AJUSTE)	F.B.R	M.M.R	
VBB	15/07/2025	EMITIDO PARA REVISIÓN Y COMENTARIOS DEL CLIENTE E INTERVENTORÍA	F.B.R	M.M.R	
VA0	04/07/2025	EMITIDO PARA COMENTARIOS INTERNOS - EMISIÓN PRELIMINAR PARA COMENTARIOS	F.B.R	M.M.R	

METRO LÍNEA 1

METRO LÍNEA 1
CONTRATO DE CONCESIÓN No. 163 DE 2019

PROYECTO PRIMERA LÍNEA DEL METRO DE BOGOTÁ - TRAMO 1

DIRECTOR DE INTERVENTORÍA:
JAVIER DESCARGA N.
Mat.:25202-68697 CND
Firmado digitalmente por JAVIER DESCARGA NAPOLES
DN: cn=JAVIER DESCARGA NAPOLES, c=CO, o=CONSORCIO SUPERVISOR PLMB, ou=DIRECCION GENERAL, email=jdescarga@ayesa.com
Motivo: Estoy de acuerdo con las partes indicadas de este documento
Fecha: 2026.04.23 14:45:22 -05'00'

ESPECIALISTA INTERVENTORÍA:
MARIA AUXILIADORA SANCHEZ HERMOSIN
INT: PAH138382-RES.NO.34 DE 2021
Firmado digitalmente por Maria Auxiliadora Sánchez Hermosin
DN: cn=Maria Auxiliadora Sánchez Hermosin, c=CO Colombia, o=Consorcio Supervisor PLMB, ou=Especialista Arquitectura, email=masanchezh@ayesa.com
Motivo: Estoy de acuerdo con las partes indicadas de este documento
Fecha: 2026.04.23 14:17:19 -05'00'

FECHA:
DICIEMBRE 2025

INFRAESTRUCTURA VIAL

ARQUITECTURA

ESTACIÓN METRO 8 (CARRERA 50)
NAVE CENTRAL
VISTA EN PLANTA Y 3D - NIVEL ACCESO TÉCNICO

PLANCHA No: L1T1-0000-308-CON-ED-ARQ-PL-0022_05_V00
ARCHIVO: L1T1-0000-308-CON-ED-ARQ-MO-0002_V00.rvt
ESCALA: INDICADA
FECHA: JULIO 2025
REVISIÓN No. V00
PLANO No. 05 DE 47