L1T1-CON-CAL-FR-0120 -81:18890x720mm

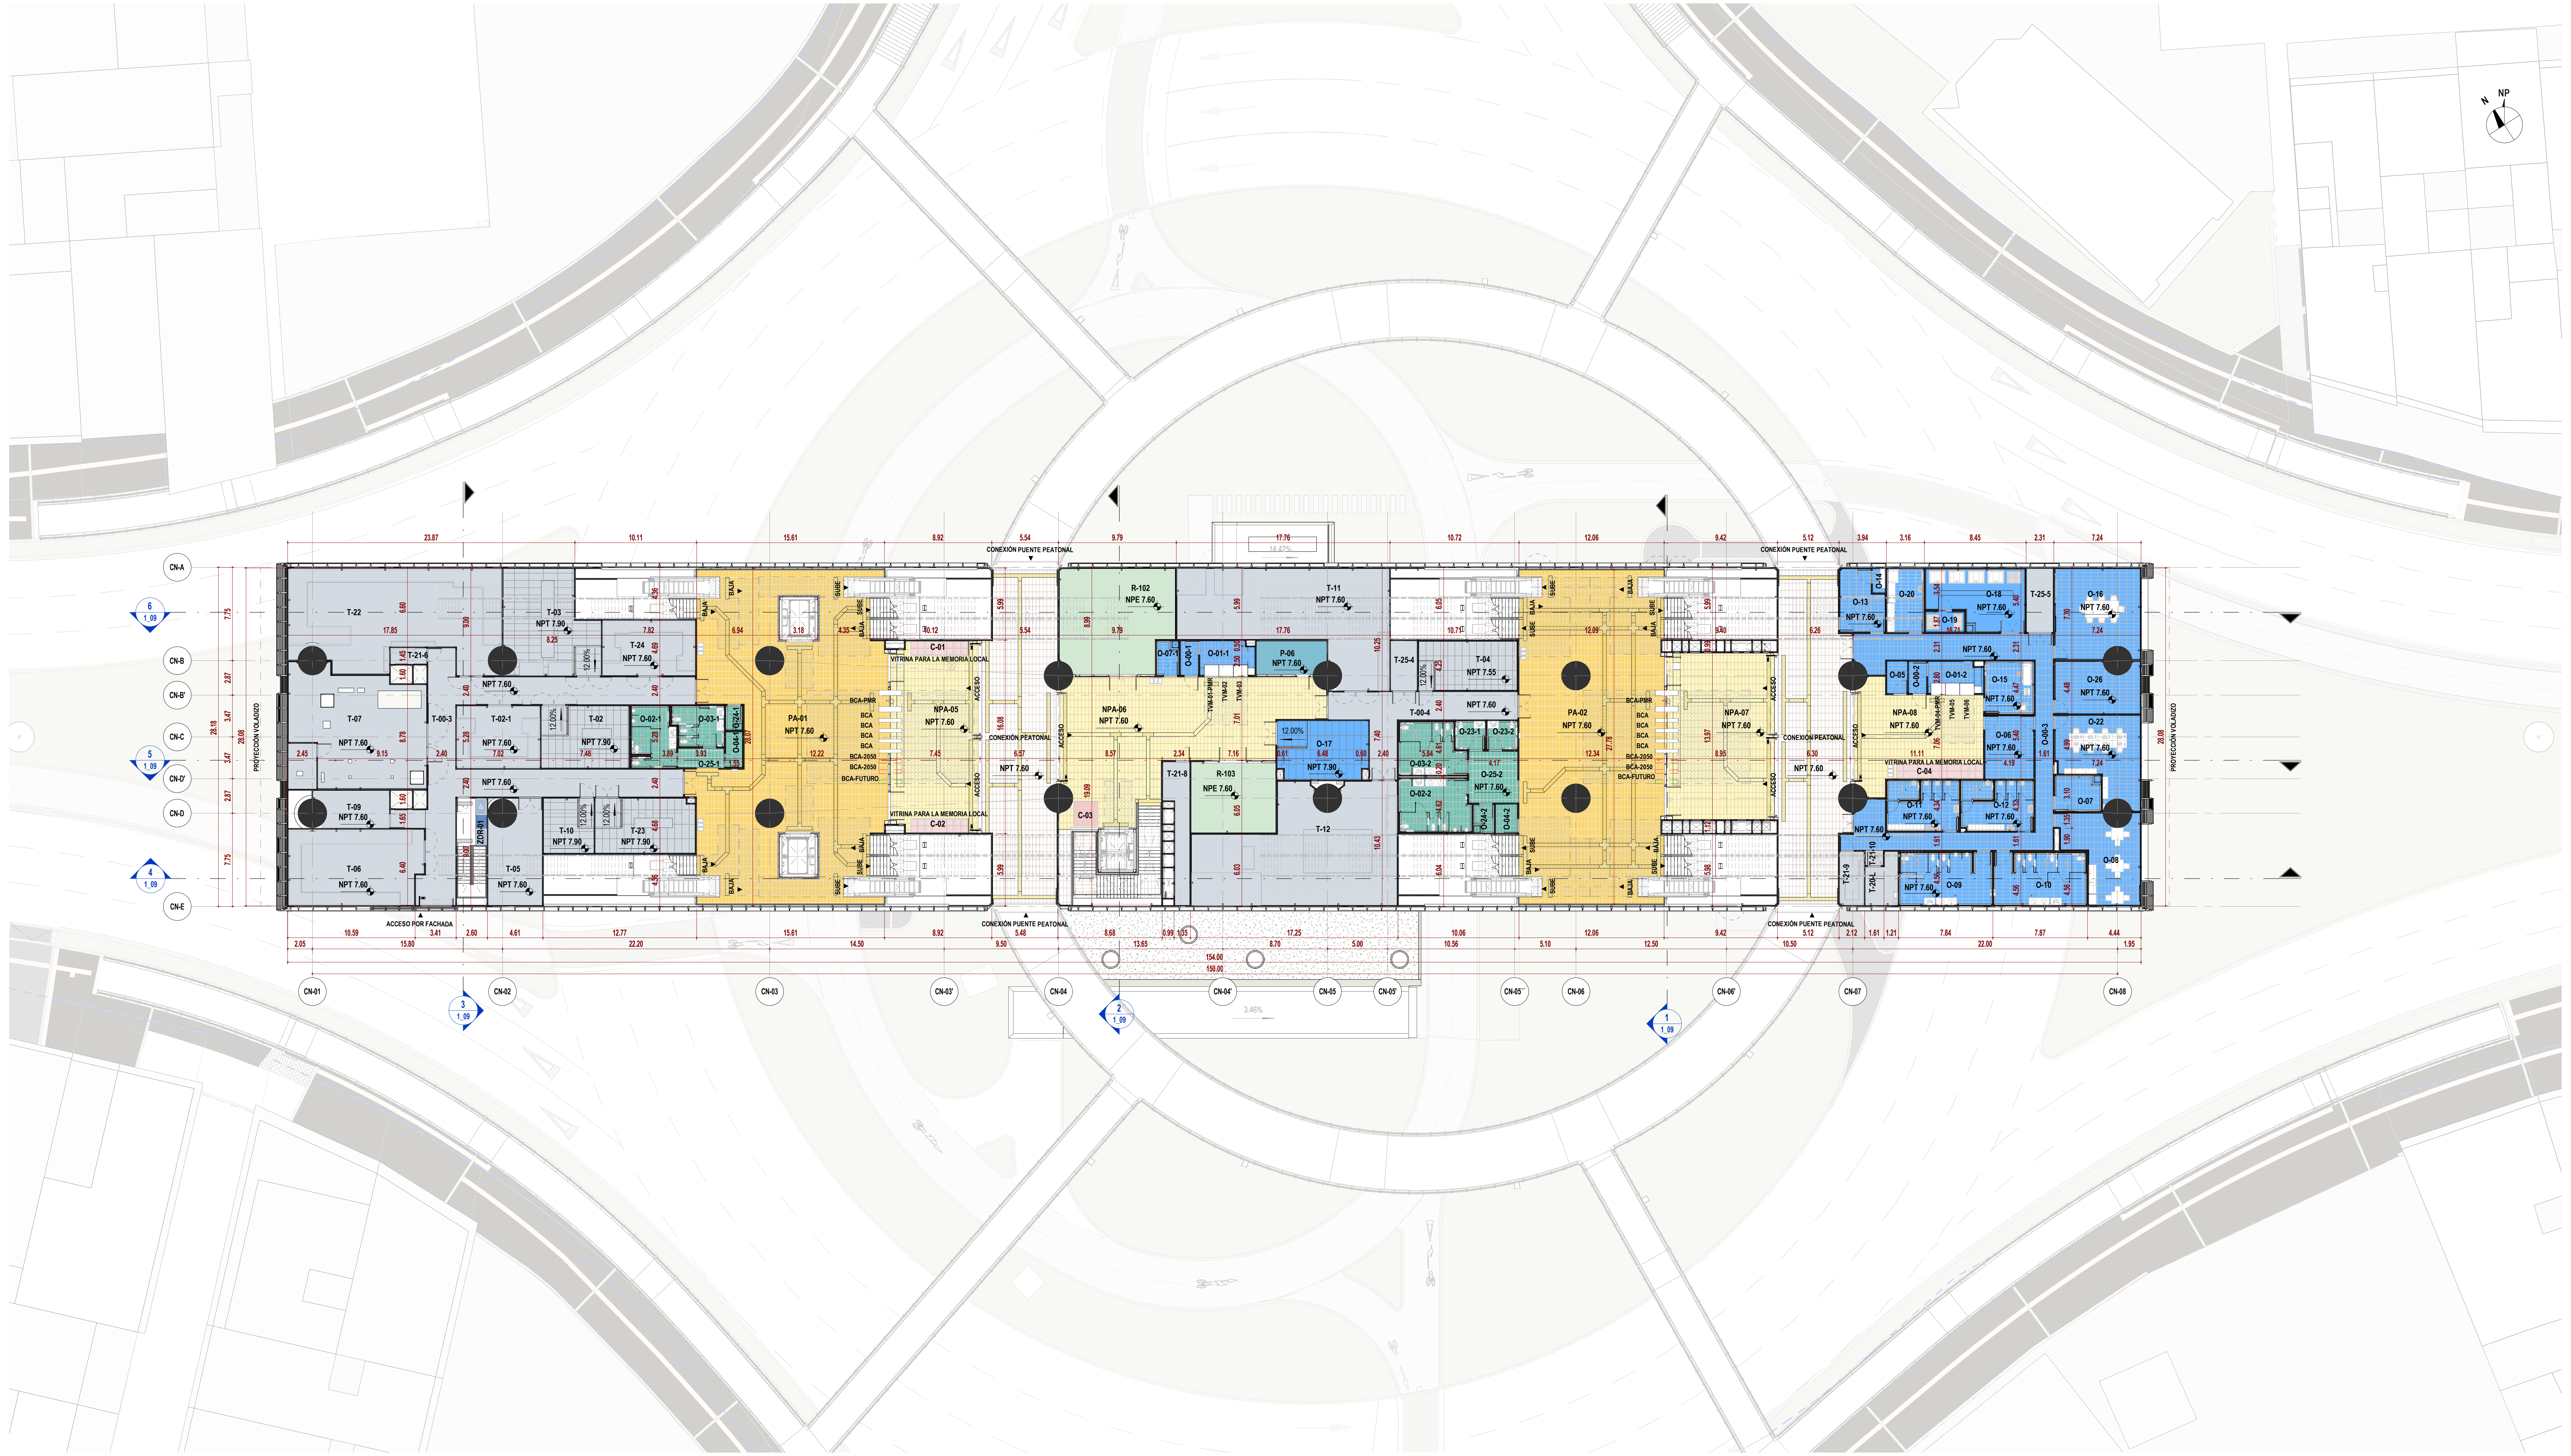

2 NIVEL INTERMEDIO / ACCESO PEATONAL_NAVE CENTRAL
ESC: 1 : 200

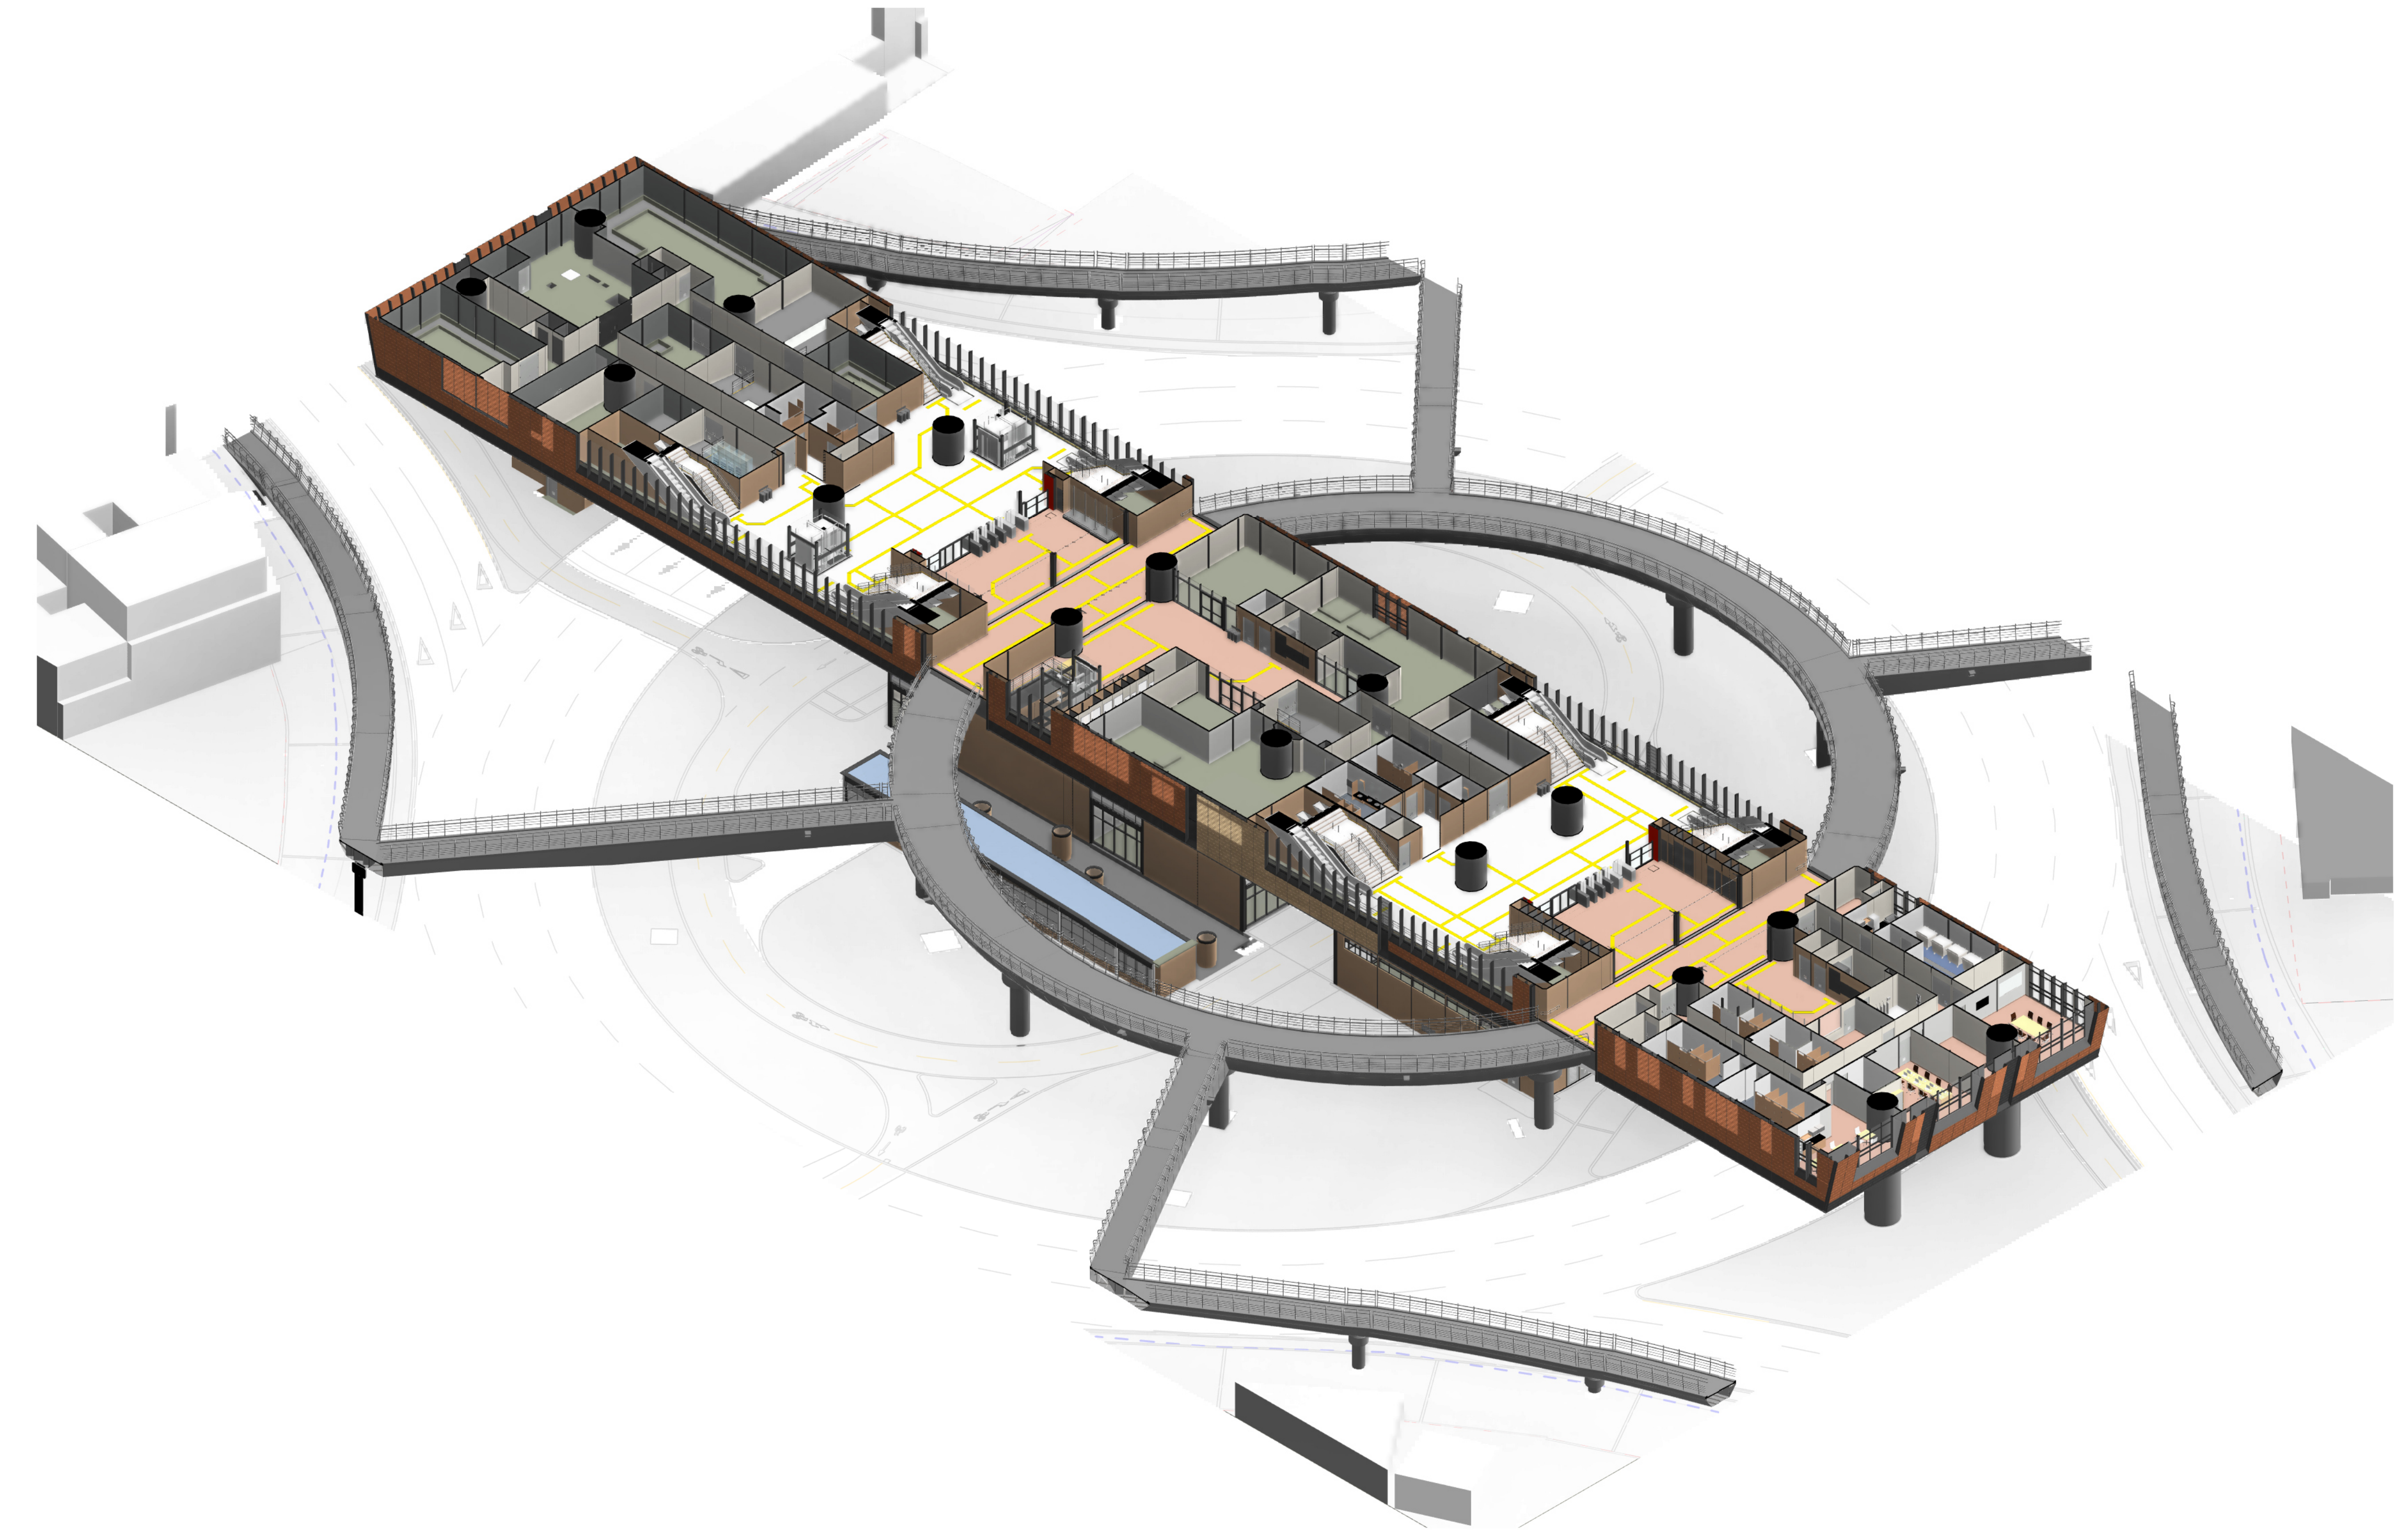

1 3D_NIVEL INTERMEDIO / ACCESO PEATONAL_NAVE CENTRAL
ESC: N/A

TABLA DE AREAS ÚTILES (NIVEL INTERMEDIO / ACCESO PEATONAL NAVE CENTRAL)

CÓDIGO	NOMBRE	ÁREA (m²)	DEPARTAMENTO
NAVE CENTRAL			
ARQ_PL_02_INTERMEDIO / ACCESO PEATONAL			
C-01	ÁREAS DE USO CULTURAL	5.76	ÁREA CULTURAL
C-02	ÁREAS DE USO CULTURAL	5.76	ÁREA CULTURAL
C-03	ÁREAS DE USO CULTURAL	4.00	ÁREA CULTURAL
C-04	ÁREAS DE USO CULTURAL	8.96	ÁREA CULTURAL
NPA-05	ÁREA NO PAGA	107.66	ÁREA NO PAGA
NPA-06	ÁREA NO PAGA	179.25	ÁREA NO PAGA
NPA-07	ÁREA NO PAGA	123.82	ÁREA NO PAGA
NPA-08	ÁREA NO PAGA	71.87	ÁREA NO PAGA
O-00-1	CIRCULACIÓN ÁREAS OPERATIVAS	4.31	ÁREA OPERATIVA
O-00-2	CIRCULACIÓN ÁREAS OPERATIVAS	4.01	ÁREA OPERATIVA
O-00-3	CIRCULACIÓN ÁREAS OPERATIVAS	92.95	ÁREA OPERATIVA
O-01-1	VENTA AUTOMÁTICA DE BOLETOS	12.82	ÁREA OPERATIVA
O-01-2	VENTA AUTOMÁTICA DE BOLETOS	11.92	ÁREA OPERATIVA
O-02-1	BAÑOS PÚBLICOS DE HOMBRES	17.66	SERVICIO PÚBLICO
O-02-2	BAÑOS PÚBLICOS DE HOMBRES	25.47	SERVICIO PÚBLICO
O-03-1	BAÑOS PÚBLICOS DE MUJERES	13.40	SERVICIO PÚBLICO
O-03-2	BAÑOS PÚBLICOS DE MUJERES	21.91	SERVICIO PÚBLICO
O-04-1	CONTROL DE ACCESO BAÑOS PÚBLICOS	4.19	SERVICIO PÚBLICO
O-04-2	CONTROL DE ACCESO BAÑOS PÚBLICOS	4.23	SERVICIO PÚBLICO
O-05	LOCAL DE INFORMACIÓN	4.53	ÁREA OPERATIVA
O-06	OFICINA DEL SUPERVISOR DE LA ESTACIÓN	21.36	ÁREA OPERATIVA
O-07	CUARTO DE LIMPIEZA	11.44	ÁREA OPERATIVA
O-07-1	CUARTO DE LIMPIEZA COMPLEMENTARIO	5.26	ÁREA OPERATIVA
O-08	SALA DE DESCANSO PARA EMPLEADOS	38.31	ÁREA OPERATIVA
O-09	BAÑOS EMPLEADOS HOMBRES	33.55	ÁREA OPERATIVA
O-10	BAÑOS EMPLEADOS MUJERES	33.58	ÁREA OPERATIVA
O-11	VESTIDORES EMPLEADOS HOMBRES	25.35	ÁREA OPERATIVA
O-12	VESTIDORES EMPLEADOS MUJERES	25.40	ÁREA OPERATIVA
O-13	LOCAL DE POLICÍA	17.39	ÁREA OPERATIVA
O-14	CALABOZO	2.12	ÁREA OPERATIVA
O-15	LOCAL PRIMEROS AUXILIOS	17.64	ÁREA OPERATIVA
O-16	SALA DE REUNIONES	51.49	ÁREA OPERATIVA
O-17	OPERADORES TELECOMUNICACIONES EXTERIORES	35.84	ÁREA OPERATIVA
O-18	CUARTO DE ALMACENAMIENTO DE RESIDUOS SÓLIDOS	37.20	ÁREA OPERATIVA
O-19	CUARTO DE ALMACENAMIENTO DE RESIDUOS PELIGROSOS	5.55	ÁREA OPERATIVA
O-20	SALA DE LACTANCIA	16.13	ÁREA OPERATIVA
O-22	OFICINA DE MANTENIMIENTO	42.09	ÁREA OPERATIVA
O-23-1	BAÑO PÚBLICO - FAMILIAR	5.74	SERVICIO PÚBLICO
O-23-2	BAÑO PÚBLICO - FAMILIAR	5.85	SERVICIO PÚBLICO
O-24-1	CUARTO DE LIMPIEZA DE BAÑOS PÚBLICOS	2.79	SERVICIO PÚBLICO
O-24-2	CUARTO DE LIMPIEZA DE BAÑOS PÚBLICOS	3.98	SERVICIO PÚBLICO
O-25-1	BAÑO PÚBLICO - CORREDOR OPERACIONAL	6.20	SERVICIO PÚBLICO
O-25-2	BAÑO PÚBLICO - CORREDOR OPERACIONAL	17.66	SERVICIO PÚBLICO
O-26	ALMACENAMIENTO DE BASURAS METRO	28.86	ÁREA OPERATIVA
P-06	ESPACIO IPES (INSTITUTO PARA LA ECONOMÍA SOCIAL)	15.22	ÁREA PÚBLICA
PA-01	ÁREA PAGA	395.95	ÁREA PAGA
PA-02	ÁREA PAGA	333.00	ÁREA PAGA
R-102	SERVICIOS ADICIONALES - ÁREA DE SERVICIO	78.81	SERVICIOS ADICIONALES - ÁREA NO PAGA
R-103	SERVICIOS ADICIONALES - ÁREA DE SERVICIO	40.91	SERVICIOS ADICIONALES - ÁREA NO PAGA
T-00-3	CIRCULACIÓN TÉCNICA	141.48	ÁREA TÉCNICA
T-00-4	CIRCULACIÓN TÉCNICA	47.41	ÁREA TÉCNICA
T-02	LOCAL DE CONDUCCIÓN AUTOMÁTICA (CBTC)	37.64	ÁREA TÉCNICA
T-02-1	UPS DEDICADA (CBTC)	35.48	ÁREA TÉCNICA
T-03	TELECOMUNICACIONES ESTACIÓN - CORRIENTE DÉBIL	62.79	ÁREA TÉCNICA
T-04	EQUIPO BOLETERÍA	32.64	ÁREA TÉCNICA
T-05	ALMACÉN PARA MANTENIMIENTO	34.95	ÁREA TÉCNICA
T-06	SALA DE TABLEROS	68.53	ÁREA TÉCNICA
T-07	CENTRO DE TRANSFORMACIÓN (CT)	110.83	ÁREA TÉCNICA
T-09	ALMACÉN EQUIPO ELÉCTRICO	17.68	ÁREA TÉCNICA
T-10	CUARTO DE EQUIPO ELECTROMECÁNICO	18.71	ÁREA TÉCNICA
T-11	CUARTO DE VENTILACIÓN	123.25	ÁREA TÉCNICA
T-12	PLANTA DE REFRIGERACIÓN PARA LA CLIMATIZACIÓN	138.54	ÁREA TÉCNICA
T-20-L	MEDIDORES (LUZ)	10.02	ÁREA TÉCNICA
T-21-6	ÁREA DE INSPECCIÓN	4.01	ÁREA TÉCNICA
T-21-7	ÁREA DE INSPECCIÓN	4.42	ÁREA TÉCNICA
T-21-8	ÁREA DE INSPECCIÓN	17.86	ÁREA TÉCNICA
T-21-9	ÁREA DE INSPECCIÓN	8.82	ÁREA TÉCNICA
T-21-10	ÁREA DE INSPECCIÓN	1.89	ÁREA TÉCNICA
T-22	CUARTO DE UPS	136.63	ÁREA TÉCNICA
T-23	CUARTO PDAP	37.19	ÁREA TÉCNICA
T-24	TETRA UPS	35.12	ÁREA TÉCNICA
T-25-4	NODO DE ACCESO DE TELECOMUNICACIONES	9.03	ÁREA TÉCNICA
T-25-5	NODO DE ACCESO DE TELECOMUNICACIONES	11.64	ÁREA TÉCNICA
ZDR-01	ZONA DE REFUGIO (PMR)	3.54	ZONA DE REFUGIO
TOTAL NIVEL INTERMEDIO / ACCESO PEATONAL		3229.26	

TABLA DE ÁREAS ÚTILES POR DEPARTAMENTO (NIVEL INTERMEDIO / ACCESO PEATONAL)

DEPARTAMENTO	ÁREA (m²)
SERVICIO PÚBLICO	129.08
SERVICIOS ADICIONALES - ÁREA NO PAGA	119.72
ZONA DE REFUGIO	3.54
ÁREA CULTURAL	24.48
ÁREA NO PAGA	482.60
ÁREA OPERATIVA	579.11
ÁREA PAGA	728.95
ÁREA PÚBLICA	15.22
ÁREA TÉCNICA	1146.57
TOTAL NIVEL INTERMEDIO	3229.26

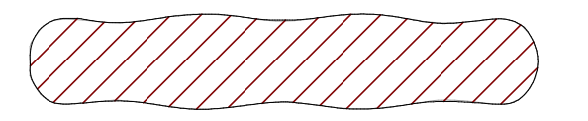

PLANO CLAVE ESTACIÓN 8

VÁLIDO PARA CONSTRUCCIÓN
12/12/2025

LOCALIZACIÓN

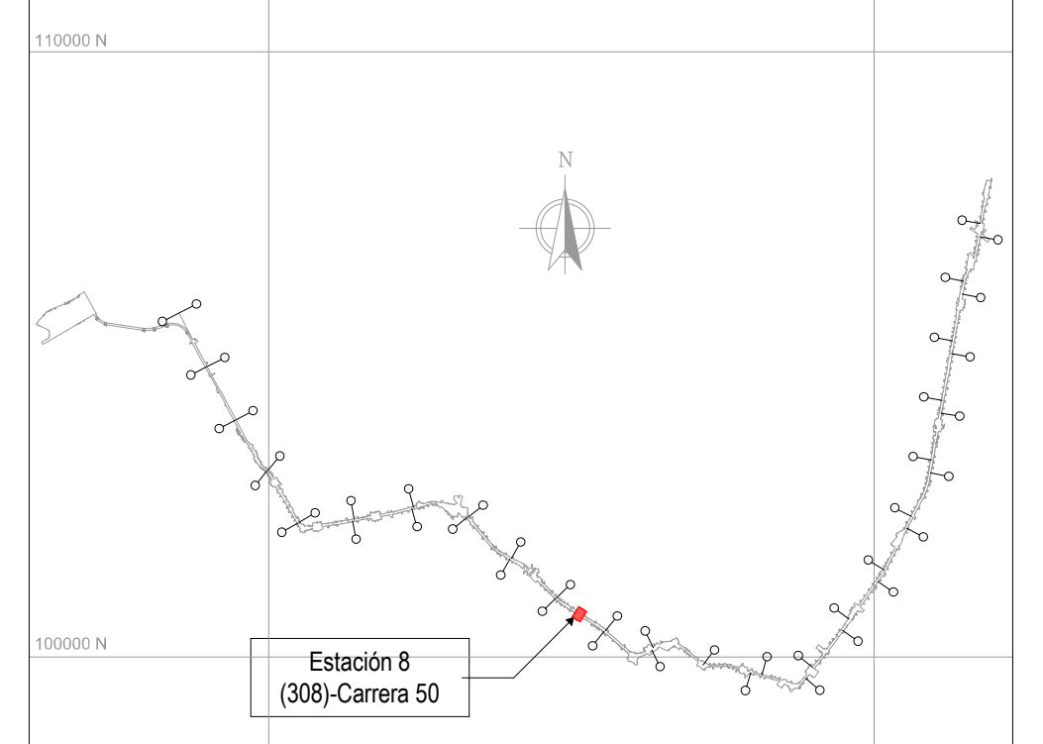

NOTAS

01 TODAS LAS DIMENSIONES ESTÁN CONFIGURADAS EN METROS A MENOS QUE SE INDIQUE UNA UNIDAD DE MEDIDA DIFERENTE.

02 TODAS LAS MEDIDAS, UBICACIÓN Y NIVELES DEBEN VERIFICARSE EN EL LUGAR DE CONSTRUCCIÓN.

03 EL NIVEL DE ACCESO AL EDIFICIO PL 01 CORRESPONDE AL +0,00 DE LA ESTACIÓN Y REFERENCIA AL NIVEL 2555.65 M.S.N.M

04 LOS NOMBRES ESPECÍFICOS DE LAS ÁREAS PUEDEN SER CONSULTADAS EN EL PLANO NO. 3 Ó EN LAS VISTAS EN PLANTA.

05 LOS COLORES QUE SE MUESTRAN EN LOS PLANOS COMO PROYECCIÓN DE ELEMENTOS ARQUITECTÓNICOS COMO CUBIERTAS FACHADAS MUROS ETC. NO REPRESENTAN LA MATERIALIDAD Y REALIDAD DE ACABADOS DEL PROYECTO, SOLO SON INDICATIVOS PARA REALIZAR UNA CORRECTA LECTURA DE LA PLANIMETRÍA.

06 LAS ESCALERAS ELÉCTRICAS INDICAN SU SENTIDO CON LA SIGUIENTE NOMENCLATURA: "SUBE" Y "BAJA".

07 SE DEBEN REVISAR LOS NIVELES ESTRUCTURALES PARA NIVEL DE ACCESO PL_01 Y SUBNIVELES, PL_02 (INTERMEDIO), PL_03 (PLATAFORMA) CON LA PLANIMETRÍA DE PLACAS ESTRUCTURALES EN LOS ENTREGABLES L1T1-1200-308-CON-ED-EST-PL-0068, 69, RESPECTIVAMENTE. EL NIVEL ESTRUCTURAL (NE) REFERENCIA LOS ESPACIOS DONDE SE DEBE ACONDICIONAR EL ACABADO DE PISO SEGÚN CORRESPONDA, CON LOS NIVELES DE PISO TERMINADO (NPT). LOS NIVELES PROYECTADOS DE EMPATE (NPE) EN LAS ÁREAS DE SERVICIOS ADICIONALES, REFERENCIAN LA ADECUACIÓN DE LOS DESNIVELES EN ESTAS ÁREAS; QUEDA COMO RESPONSABILIDAD DEL LOCATARIO DEFINIR Y ACONDICIONAR ESTE ACABADO DE PISO (NPE) EN LÍNEA CON EL NIVEL (NPT) DE ESPACIOS COLINDANTES. EL NIVEL ESTRUCTURAL (NE) SE ENCUENTRA A (- 0.10M) POR DEBAJO DE LOS NIVELES DE PISO TERMINADO (NPT) Y LOS NIVELES PROYECTADOS DE EMPATE (NPE) MARCADOS EN LA PLANIMETRÍA.

- ARC_PL_00 = SÓTANO / ACCESO BICIUSUARIOS	/ NPT -6.25
- ARC_PL_01 = ACCESO TÉCNICO	/ NPT 0.00
- ARC_PL_02 = INTERMEDIO / ACCESO PEATONAL	/ NPT 7.60
- ARC_PL_02.1 = PLACA INFERIOR VIGA CAJÓN	/ NPT 13.82
- ARC_PL_02.2 = TOPE DE RIEL (TOR)	/ NPT 15.95
- ARC_PL_03 = PLATAFORMA	/ NPT 17.09
- ARC_PL_05 = CUBIERTA NAVE CENTRAL	/ NPT 26.42

CONVENCIONES

🟩	SERVICIOS ADICIONALES - ÁREA NO PAGA	🟨	ÁREA NO PAGA
🟩	SERVICIOS ADICIONALES - ÁREA PAGA	🟦	ÁREA OPERATIVA
🟩	SERVICIO PÚBLICO	🟨	ÁREA PAGA
🟦	ZONA DE REFUGIO	🟦	ÁREA PÚBLICA
🟥	ÁREA CULTURAL	⬜	ÁREA TÉCNICA
🟪	ÁREA DE TAQUILLAS BRT		

No.	PLANOS DE REFERENCIA	REV.

No.	MODELO BIM DE REFERENCIA	REV.
1	L1T1-1100-208-CON-ED-EST-MO-0001.rvt	V00
2	L1T1-1100-209-CON-ED-EST-MO-0001.rvt	V00
3	L1T1-1100-308-CON-ED-EST-MO-0001.rvt	V00
4	L1T1-1150-208-CON-ED-EST-MO-0001.rvt	V00
5	L1T1-1150-209-CON-ED-EST-MO-0001.rvt	V00
6	L1T1-1150-308-CON-ED-EST-MO-0001.rvt	V00
7	L1T1-1200-308-CON-ED-EST-MO-0001.rvt	V00
8	L1T1-1410-308-CON-ED-MEC-MO-0001.rvt	V00
9	L1T1-1420-308-CON-ED-MEC-MO-0001.rvt	V00
10	L1T1-2420-561-CON-ED-EST-MO-0001.rvt	V00
11	L1T1-5160-308-CON-ED-EST-MO-0001.rvt	V00
12	L1T1-5160-308-CON-ED-ARQ-MO-0001.rvt	V00
13	L1T1-5300-308-CON-ED-MEC-MO-0001.rvt	V00

No.	PAQUETE DE TRABAJO DE REFERENCIA	REV.
1	XREF-URBANISM_CONTEXT_ST08.rvt	
2	XREF-SECONDARY-STRUCTURE-ST08.rvt	

0 2 10m
1:200

METRO BOGOTÁ
GCS Consorcio Consultores PMO Bogotá
CONSORCIO SUPERVISOR PLMB
wsp

DISEÑÓ: SANTIAGO ANDRES DAVID GUZMÁN
Mat.: A413202011-1010176190

APROBÓ: MAURICIO MEJÍA RESTREPO
Mat.: 25202-72411 CND
Firmado digitalmente por MAURICIO MEJIA RESTREPO
Fecha: 2026.01.26 15:50:13 -05'00'

REVISÓ: FREDDY BAUTISTA R.
Mat.:25202-092831 CND
Digitally signed by Bautista Rondón, Freddy (COFB100240)

DIBUJÓ: EQUIPO WSP

REVISIÓN No.	FECHA	DESCRIPCIÓN	REVISÓ	APROBÓ	APROBACIÓN CLIENTE
V00	12/12/2025	REVISIÓN NO OBJETADA - EMITIDO PARA CONSTRUCCIÓN	F.B.R	M.M.R	
VCC	01/10/2025	EMITIDO PARA REVISIÓN Y COMENTARIOS DEL CLIENTE E INTERVENTORÍA - INCLUYE COMENTARIOS /(AJUSTE)	F.B.R	M.M.R	
VBB	15/07/2025	EMITIDO PARA REVISIÓN Y COMENTARIOS DEL CLIENTE E INTERVENTORÍA	F.B.R	M.M.R	
VA0	04/07/2025	EMITIDO PARA COMENTARIOS INTERNOS - EMISIÓN PRELIMINAR PARA COMENTARIOS	F.B.R	M.M.R	

METRO LÍNEA 1

METRO LÍNEA 1
CONTRATO DE CONCESIÓN No. 163 DE 2019

PROYECTO PRIMERA LÍNEA DEL METRO DE BOGOTÁ - TRAMO 1

DIRECTOR DE INTERVENTORÍA:
JAVIER DESCARGA N.
Mat.:25202-68697 CND
Firmado digitalmente por JAVIER DESCARGA NAPOLES
DN: cn=JAVIER DESCARGA NAPOLES, c=CO, o=CONSORCIO SUPERVISOR PLMB, ou=DIRECCION GENERAL, email=jdescarga@ayesa.com
Motivo: Estoy de acuerdo con las partes indicadas de este documento
Fecha: 2026.04.23 14:45:47 -05'00'

ESPECIALISTA INTERVENTORÍA:
MARIA AUXILIADORA SANCHEZ HERMOSIN
INT: PAH138382-RES.NO.34 DE 2021
Firmado digitalmente por Maria Auxiliadora Sánchez Hermosin
DN: cn=Maria Auxiliadora Sánchez Hermosin, c=CO Colombia, o=Consorcio Supervisor PLMB, ou=Especialista Arquitectura, email=masanchezh@ayesa.com
Motivo: Estoy de acuerdo con las partes indicadas de este documento
Fecha: 2026.04.23 14:18:04 -05'00'

FECHA: DICIEMBRE 2025

INFRAESTRUCTURA VIAL

ARQUITECTURA

ESTACIÓN METRO 8 (CARRERA 50)
NAVE CENTRAL
VISTA EN PLANTA Y 3D - NIVEL INTERMEDIO / ACCESO PEATONAL

PLANCHA No: L1T1-0000-308-CON-ED-ARQ-PL-0022_06_V00
ARCHIVO: L1T1-0000-308-CON-ED-ARQ-MO-0002_V00.rvt
ESCALA: INDICADA
FECHA: JULIO 2025
REVISIÓN No. V00
PLANO No. 06 DE 47