L1T1-CON-CAL-FR-0120 -B1 1680x720mm

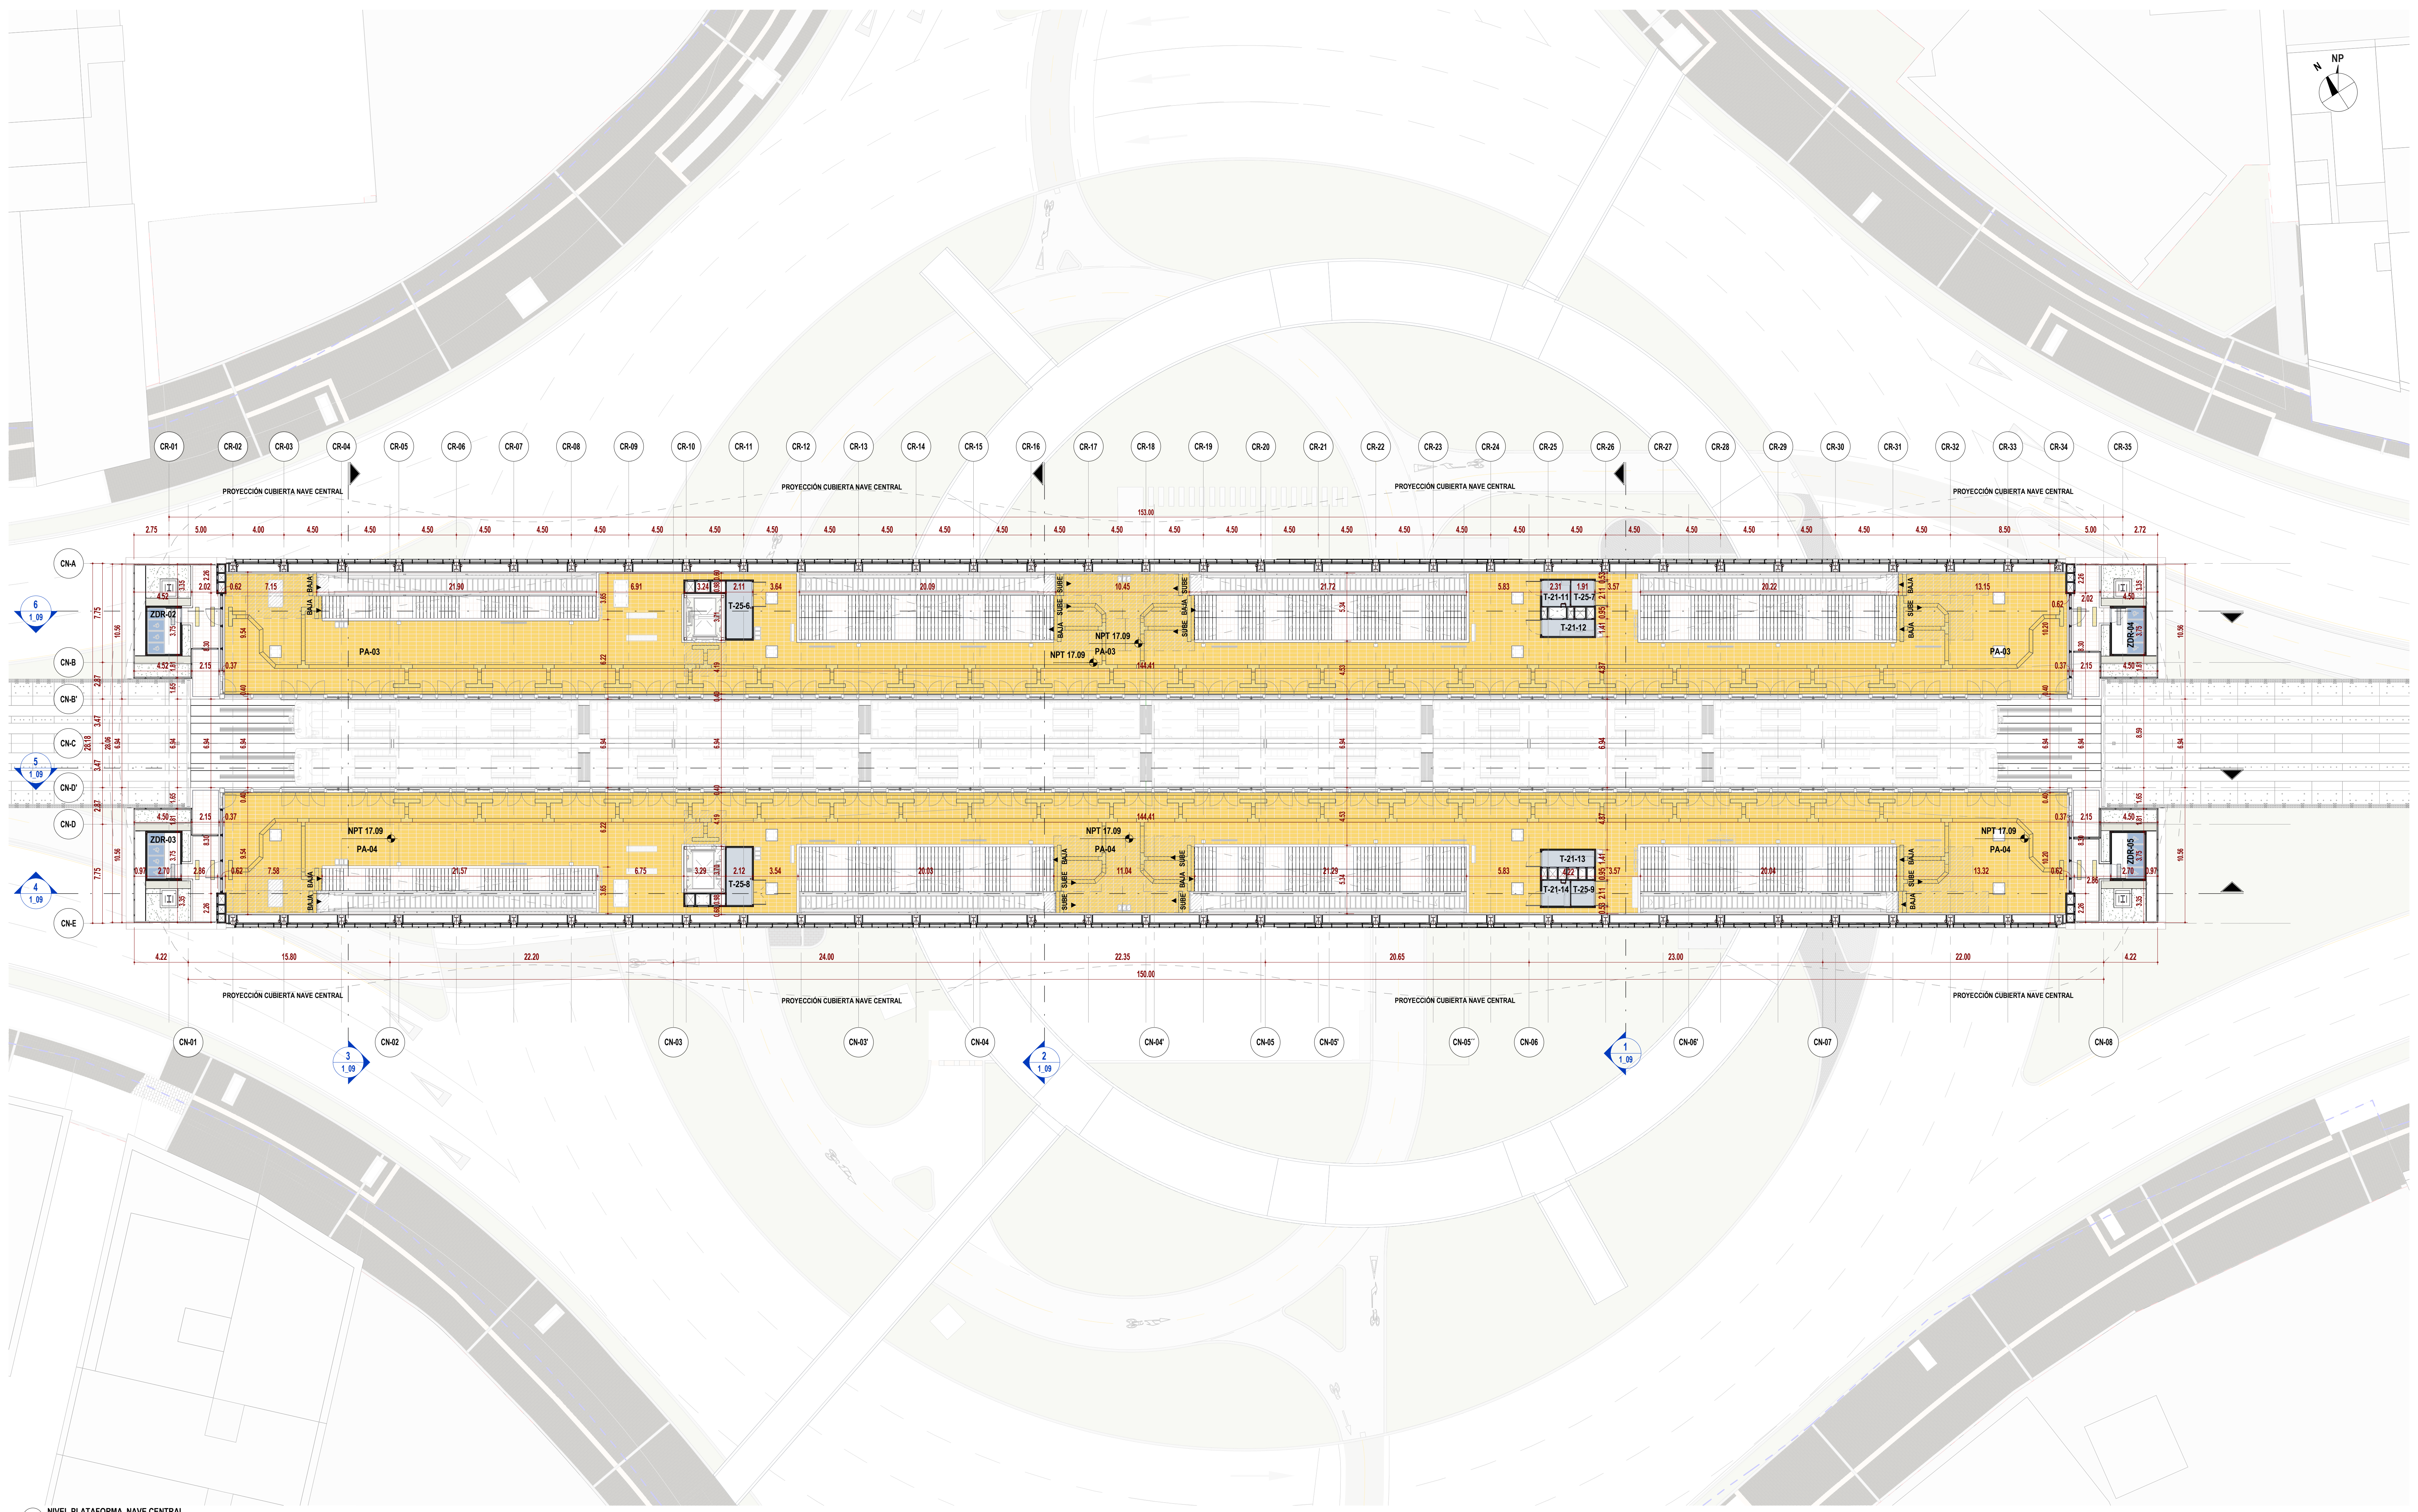

2 NIVEL PLATAFORMA_NAVE CENTRAL
ESC: 1 : 200

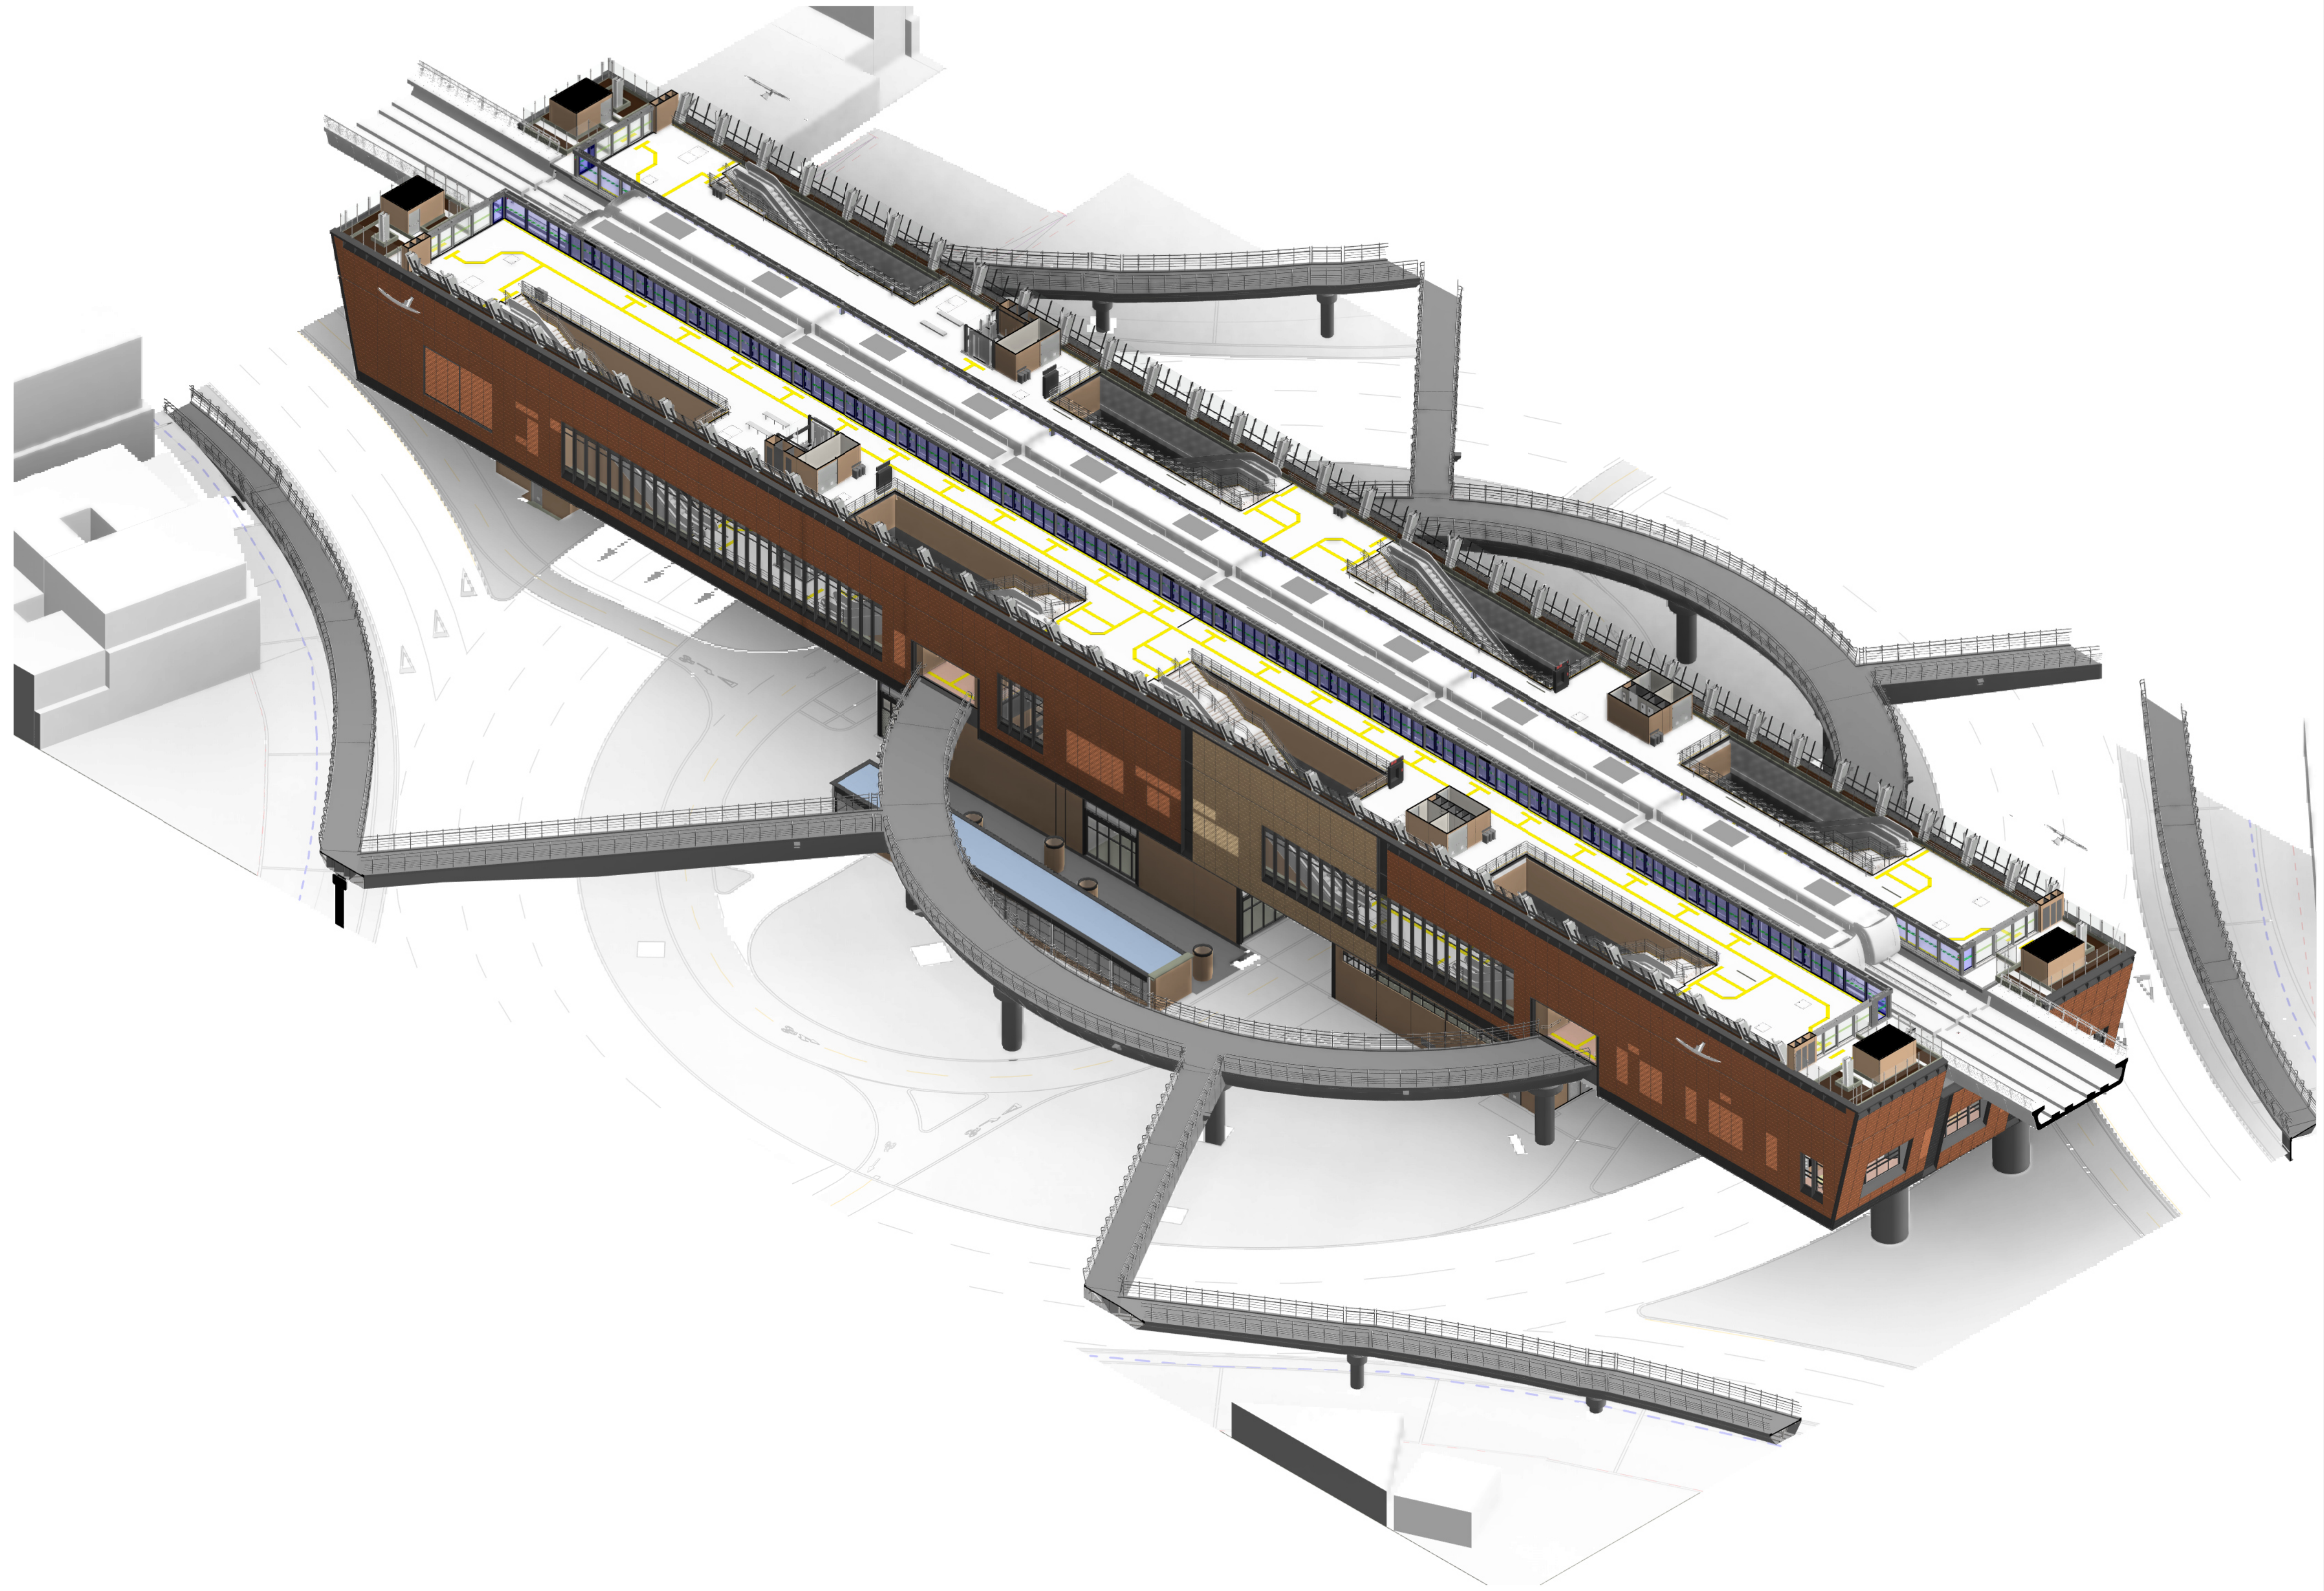

1 3D_NIVEL PLATAFORMA_NAVE CENTRAL
ESC: N/A

TABLA DE ÁREAS ÚTILES (NIVEL PLATAFORMA_NAVE CENTRAL)

CÓDIGO	NOMBRE	ÁREA (m²)	DEPARTAMENTO
NAVE CENTRAL			
ARQ_PL_03_PLATAFORMA			
J-01	JARDÍN	24.02	ÁREA JARDIN
J-02	JARDÍN	23.99	ÁREA JARDIN
J-03	JARDÍN	23.80	ÁREA JARDIN
J-04	JARDÍN	24.23	ÁREA JARDIN
PA-03	ÁREA PAGA	926.30	ÁREA PAGA
PA-04	ÁREA PAGA	920.14	ÁREA PAGA
T-21-11	ÁREA DE INSPECCIÓN	4.32	ÁREA TÉCNICA
T-21-12	ÁREA DE INSPECCIÓN	5.21	ÁREA TÉCNICA
T-21-13	ÁREA DE INSPECCIÓN	5.21	ÁREA TÉCNICA
T-21-14	ÁREA DE INSPECCIÓN	4.32	ÁREA TÉCNICA
T-25-6	NODO DE ACCESO DE TELECOMUNICACIONES	8.82	ÁREA TÉCNICA
T-25-7	NODO DE ACCESO DE TELECOMUNICACIONES	3.52	ÁREA TÉCNICA
T-25-8	NODO DE ACCESO DE TELECOMUNICACIONES	8.83	ÁREA TÉCNICA
T-25-9	NODO DE ACCESO DE TELECOMUNICACIONES	3.52	ÁREA TÉCNICA
ZDR-02	ZONA DE REFUGIO (PMR)	4.86	ZONA DE REFUGIO
ZDR-03	ZONA DE REFUGIO (PMR)	4.81	ZONA DE REFUGIO
ZDR-04	ZONA DE REFUGIO (PMR)	4.81	ZONA DE REFUGIO
ZDR-05	ZONA DE REFUGIO (PMR)	4.81	ZONA DE REFUGIO
TOTAL NIVEL PLATAFORMA		2005.50	

TABLA DE ÁREAS ÚTILES POR DEPARTAMENTO (NIVEL PLATAFORMA)

DEPARTAMENTO	ÁREA (m²)
ZONA DE REFUGIO	19.28
ÁREA JARDIN	96.04
ÁREA PAGA	1846.44
ÁREA TÉCNICA	43.74
TOTAL NIVEL PLATAFORMA	2005.50

LOCALIZACIÓN

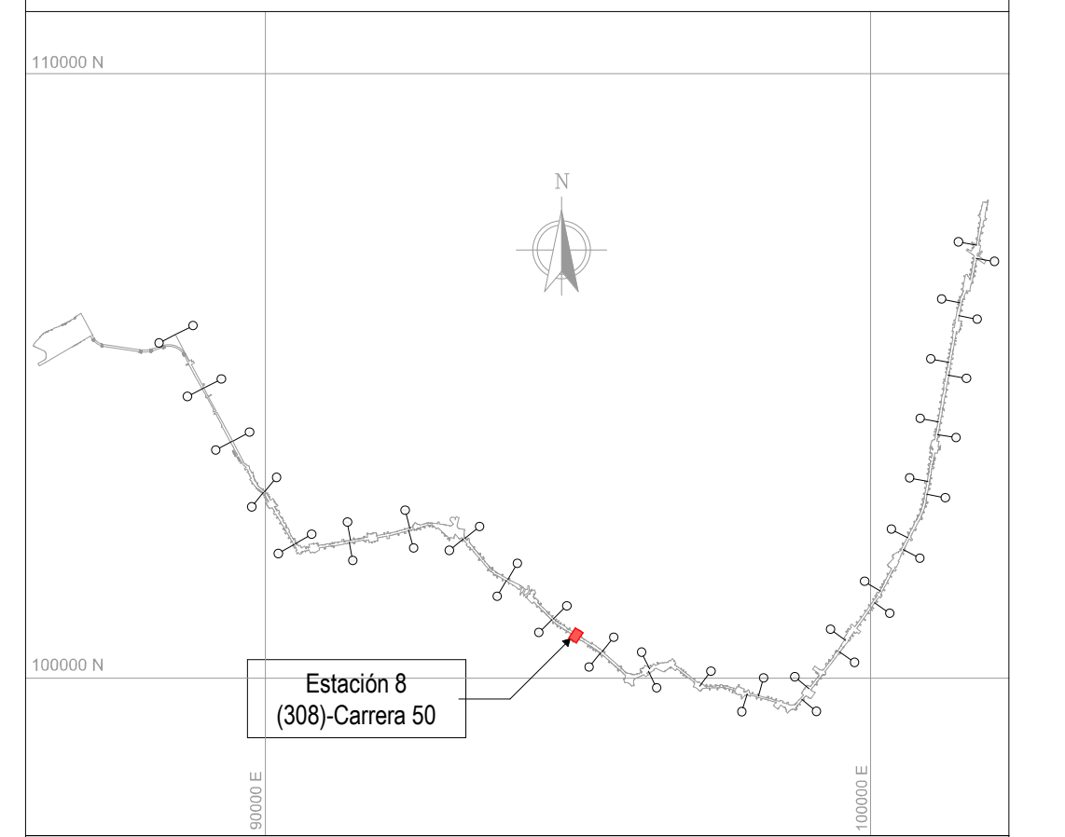

NOTAS

01 TODAS LAS DIMENSIONES ESTÁN CONFIGURADAS EN METROS A MENOS QUE SE INDIQUE UNA UNIDAD DE MEDIDA DIFERENTE.

02 TODAS LAS MEDIDAS, UBICACIÓN Y NIVELES DEBEN VERIFICARSE EN EL LUGAR DE CONSTRUCCIÓN.

03 EL NIVEL DE ACCESO AL EDIFICIO PL 01 CORRESPONDE AL +0,00 DE LA ESTACIÓN Y REFERENCIA AL NIVEL 2555.65 M.S.N.M

04 LOS NOMBRES ESPECÍFICOS DE LAS ÁREAS PUEDEN SER CONSULTADAS EN EL PLANO NO. 3 Ó EN LAS VISTAS EN PLANTA.

05 LOS COLORES QUE SE MUESTRAN EN LOS PLANOS COMO PROYECCIÓN DE ELEMENTOS ARQUITECTÓNICOS COMO CUBIERTAS FACHADAS MUROS ETC. NO REPRESENTAN LA MATERIALIDAD Y REALIDAD DE ACABADOS DEL PROYECTO, SOLO SON INDICATIVOS PARA REALIZAR UNA CORRECTA LECTURA DE LA PLANIMETRÍA.

06 LAS ESCALERAS ELÉCTRICAS INDICAN SU SENTIDO CON LA SIGUIENTE NOMENCLATURA: “SUBE” Y “BAJA”.

07 SE DEBEN REVISAR LOS NIVELES ESTRUCTURALES PARA NIVEL DE ACCESO PL_01 Y SUBNIVELES, PL_02 (INTERMEDIO), PL_03 (PLATAFORMA) CON LA PLANIMETRÍA DE PLACAS ESTRUCTURALES EN LOS ENTREGABLES L1T1-1200-308-CON-ED-EST-PL-0068, 69, RESPECTIVAMENTE. EL NIVEL ESTRUCTURAL (NE) REFERENCIA LOS ESPACIOS DONDE SE DEBE ACONDICIONAR EL ACABADO DE PISO SEGÚN CORRESPONDA, CON LOS NIVELES DE PISO TERMINADO (NPT). LOS NIVELES PROYECTADOS DE EMPATE (NPE) EN LAS ÁREAS DE SERVICIOS ADICIONALES, REFERENCIAN LA ADECUACIÓN DE LOS DESNIVELES EN ESTAS ÁREAS; QUEDA COMO RESPONSABILIDAD DEL LOCATARIO DEFINIR Y ACONDICIONAR ESTE ACABADO DE PISO (NPE) EN LÍNEA CON EL NIVEL (NPT) DE ESPACIOS COLINDANTES. EL NIVEL ESTRUCTURAL (NE) SE ENCUENTRA A (- 0.10M) POR DEBAJO DE LOS NIVELES DE PISO TERMINADO (NPT) Y LOS NIVELES PROYECTADOS DE EMPATE (NPE) MARCADOS EN LA PLANIMETRÍA.

- ARC_PL_00 = SÓTANO / ACCESO BICIUSUARIOS	/ NPT -6.25
- ARC_PL_01 = ACCESO TÉCNICO	/ NPT 0.00
- ARC_PL_02 = INTERMEDIO / ACCESO PEATONAL	/ NPT 7.60
- ARC_PL_02.1 = PLACA INFERIOR VIGA CAJÓN	/ NPT 13.82
- ARC_PL_02.2 = TOPE DE RIEL (TOR)	/ NPT 15.95
- ARC_PL_03 = PLATAFORMA	/ NPT 17.09
- ARC_PL_05 = CUBIERTA NAVE CENTRAL	/ NPT 26.42

CONVENCIONES

🟩	SERVICIOS ADICIONALES - ÁREA NO PAGA	🟨	ÁREA NO PAGA
🟩	SERVICIOS ADICIONALES - ÁREA PAGA	🟦	ÁREA OPERATIVA
🟩	SERVICIO PÚBLICO	🟧	ÁREA PAGA
🟦	ZONA DE REFUGIO	🟦	ÁREA PÚBLICA
🟥	ÁREA CULTURAL	⬜	ÁREA TÉCNICA
🟪	ÁREA DE TAQUILLAS BRT		

No.	PLANOS DE REFERENCIA	REV.

No.	MODELO BIM DE REFERENCIA	REV.
1	L1T1-1100-208-CON-ED-EST-MO-0001.rvt	V00
2	L1T1-1100-209-CON-ED-EST-MO-0001.rvt	V00
3	L1T1-1100-308-CON-ED-EST-MO-0001.rvt	V00
4	L1T1-1150-208-CON-ED-EST-MO-0001.rvt	V00
5	L1T1-1150-209-CON-ED-EST-MO-0001.rvt	V00
6	L1T1-1150-308-CON-ED-EST-MO-0001.rvt	V00
7	L1T1-1200-308-CON-ED-EST-MO-0001.rvt	V00
8	L1T1-1410-308-CON-ED-MEC-MO-0001.rvt	V00
9	L1T1-1420-308-CON-ED-MEC-MO-0001.rvt	V00
10	L1T1-2420-561-CON-ED-EST-MO-0001.rvt	V00
11	L1T1-5160-308-CON-ED-EST-MO-0001.rvt	V00
12	L1T1-5160-308-CON-ED-ARQ-MO-0001.rvt	V00
13	L1T1-5300-308-CON-ED-MEC-MO-0001.rvt	V00

No.	PAQUETE DE TRABAJO DE REFERENCIA	REV.
1	XREF-URBANISM_CONTEXT_ST08.rvt	
2	XREF-SECONDARY-STRUCTURE-ST08.rvt	

VÁLIDO PARA CONSTRUCCIÓN
12/12/2025

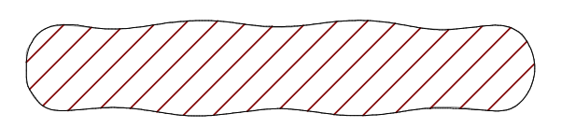

PLANO CLAVE ESTACIÓN 8

0 2 10m
1:200

METRO BOGOTÁ
GCS Consorcio Consultores PMO Bogotá
CONSORCIO SUPERVISOR PLMB
wsp

DISEÑÓ: Santiago A. David G.
SANTIAGO ANDRES DAVID GUZMÁN
Mat.: A413202011-1010176190

APROBÓ:
Firmado digitalmente por MAURICIO MEJIA RESTREPO
Fecha: 2026.01.26 15:50:34 -05'00'
MAURICIO MEJÍA RESTREPO
Mat.: 25202-72411 CND

REVISÓ:
Digitally signed by Bautista Rondón, Freddy (COFB100240)
FREDDY BAUTISTA R.
Mat.:25202-092831 CND

DIBUJÓ:
EQUIPO WSP

REVISIÓN No.	FECHA	DESCRIPCIÓN	REVISÓ	APROBÓ	APROBACIÓN CLIENTE
V00	12/12/2025	REVISIÓN NO OBJETADA - EMITIDO PARA CONSTRUCCIÓN	F.B.R	M.M.R	
VCC	01/10/2025	EMITIDO PARA REVISIÓN Y COMENTARIOS DEL CLIENTE E INTERVENTORÍA - INCLUYE COMENTARIOS /(AJUSTE)	F.B.R	M.M.R	
VBB	15/07/2025	EMITIDO PARA REVISIÓN Y COMENTARIOS DEL CLIENTE E INTERVENTORÍA	F.B.R	M.M.R	
VA0	04/07/2025	EMITIDO PARA COMENTARIOS INTERNOS - EMISIÓN PRELIMINAR PARA COMENTARIOS	F.B.R	M.M.R	

METRO LÍNEA 1

METRO LÍNEA 1
CONTRATO DE CONCESIÓN No. 163 DE 2019

PROYECTO PRIMERA LÍNEA DEL METRO DE BOGOTÁ - TRAMO 1

DIRECTOR DE INTERVENTORÍA:
Firmado digitalmente por JAVIER DESCARGA NAPOLES
DN: cn=JAVIER DESCARGA NAPOLES, c=CO, o=CONSORCIO SUPERVISOR PLMB, ou=DIRECCION GENERAL, email=jdescarga@ayesa.com
Motivo: Estoy de acuerdo con las partes indicadas de este documento
Fecha: 2026.04.23 14:46:03 -05'00'
JAVIER DESCARGA N.
Mat.:25202-68697 CND

ESPECIALISTA INTERVENTORÍA:
Firmado digitalmente por Maria Auxiliadora Sánchez Hermosin
DN: cn=Maria Auxiliadora Sánchez Hermosin, c=CO Colombia, [illegible] quitectura, email=masanchezh@ayesa.com
Motivo: Estoy de acuerdo con las partes indicadas de este documento
Fecha: 2026.04.23 14:18:26 -05'00'
MARIA AUXILIADORA SANCHEZ HERMOSIN
INT: PAH138382-RES.NO.34 DE 2021

FECHA:
DICIEMBRE 2025

INFRAESTRUCTURA VIAL

ARQUITECTURA

ESTACIÓN METRO 8 (CARRERA 50)
NAVE CENTRAL
VISTA EN PLANTA Y 3D - NIVEL PLATAFORMA

PLANCHA No: L1T1-0000-308-CON-ED-ARQ-PL-0022_07_V00
ARCHIVO: L1T1-0000-308-CON-ED-ARQ-MO-0002_V00.rvt
ESCALA: INDICADA
FECHA: JULIO 2025
REVISIÓN No. V00
PLANO No. 07 DE 47