L1T1-CON-CAL-FR-0120 -B1:1471x720mm

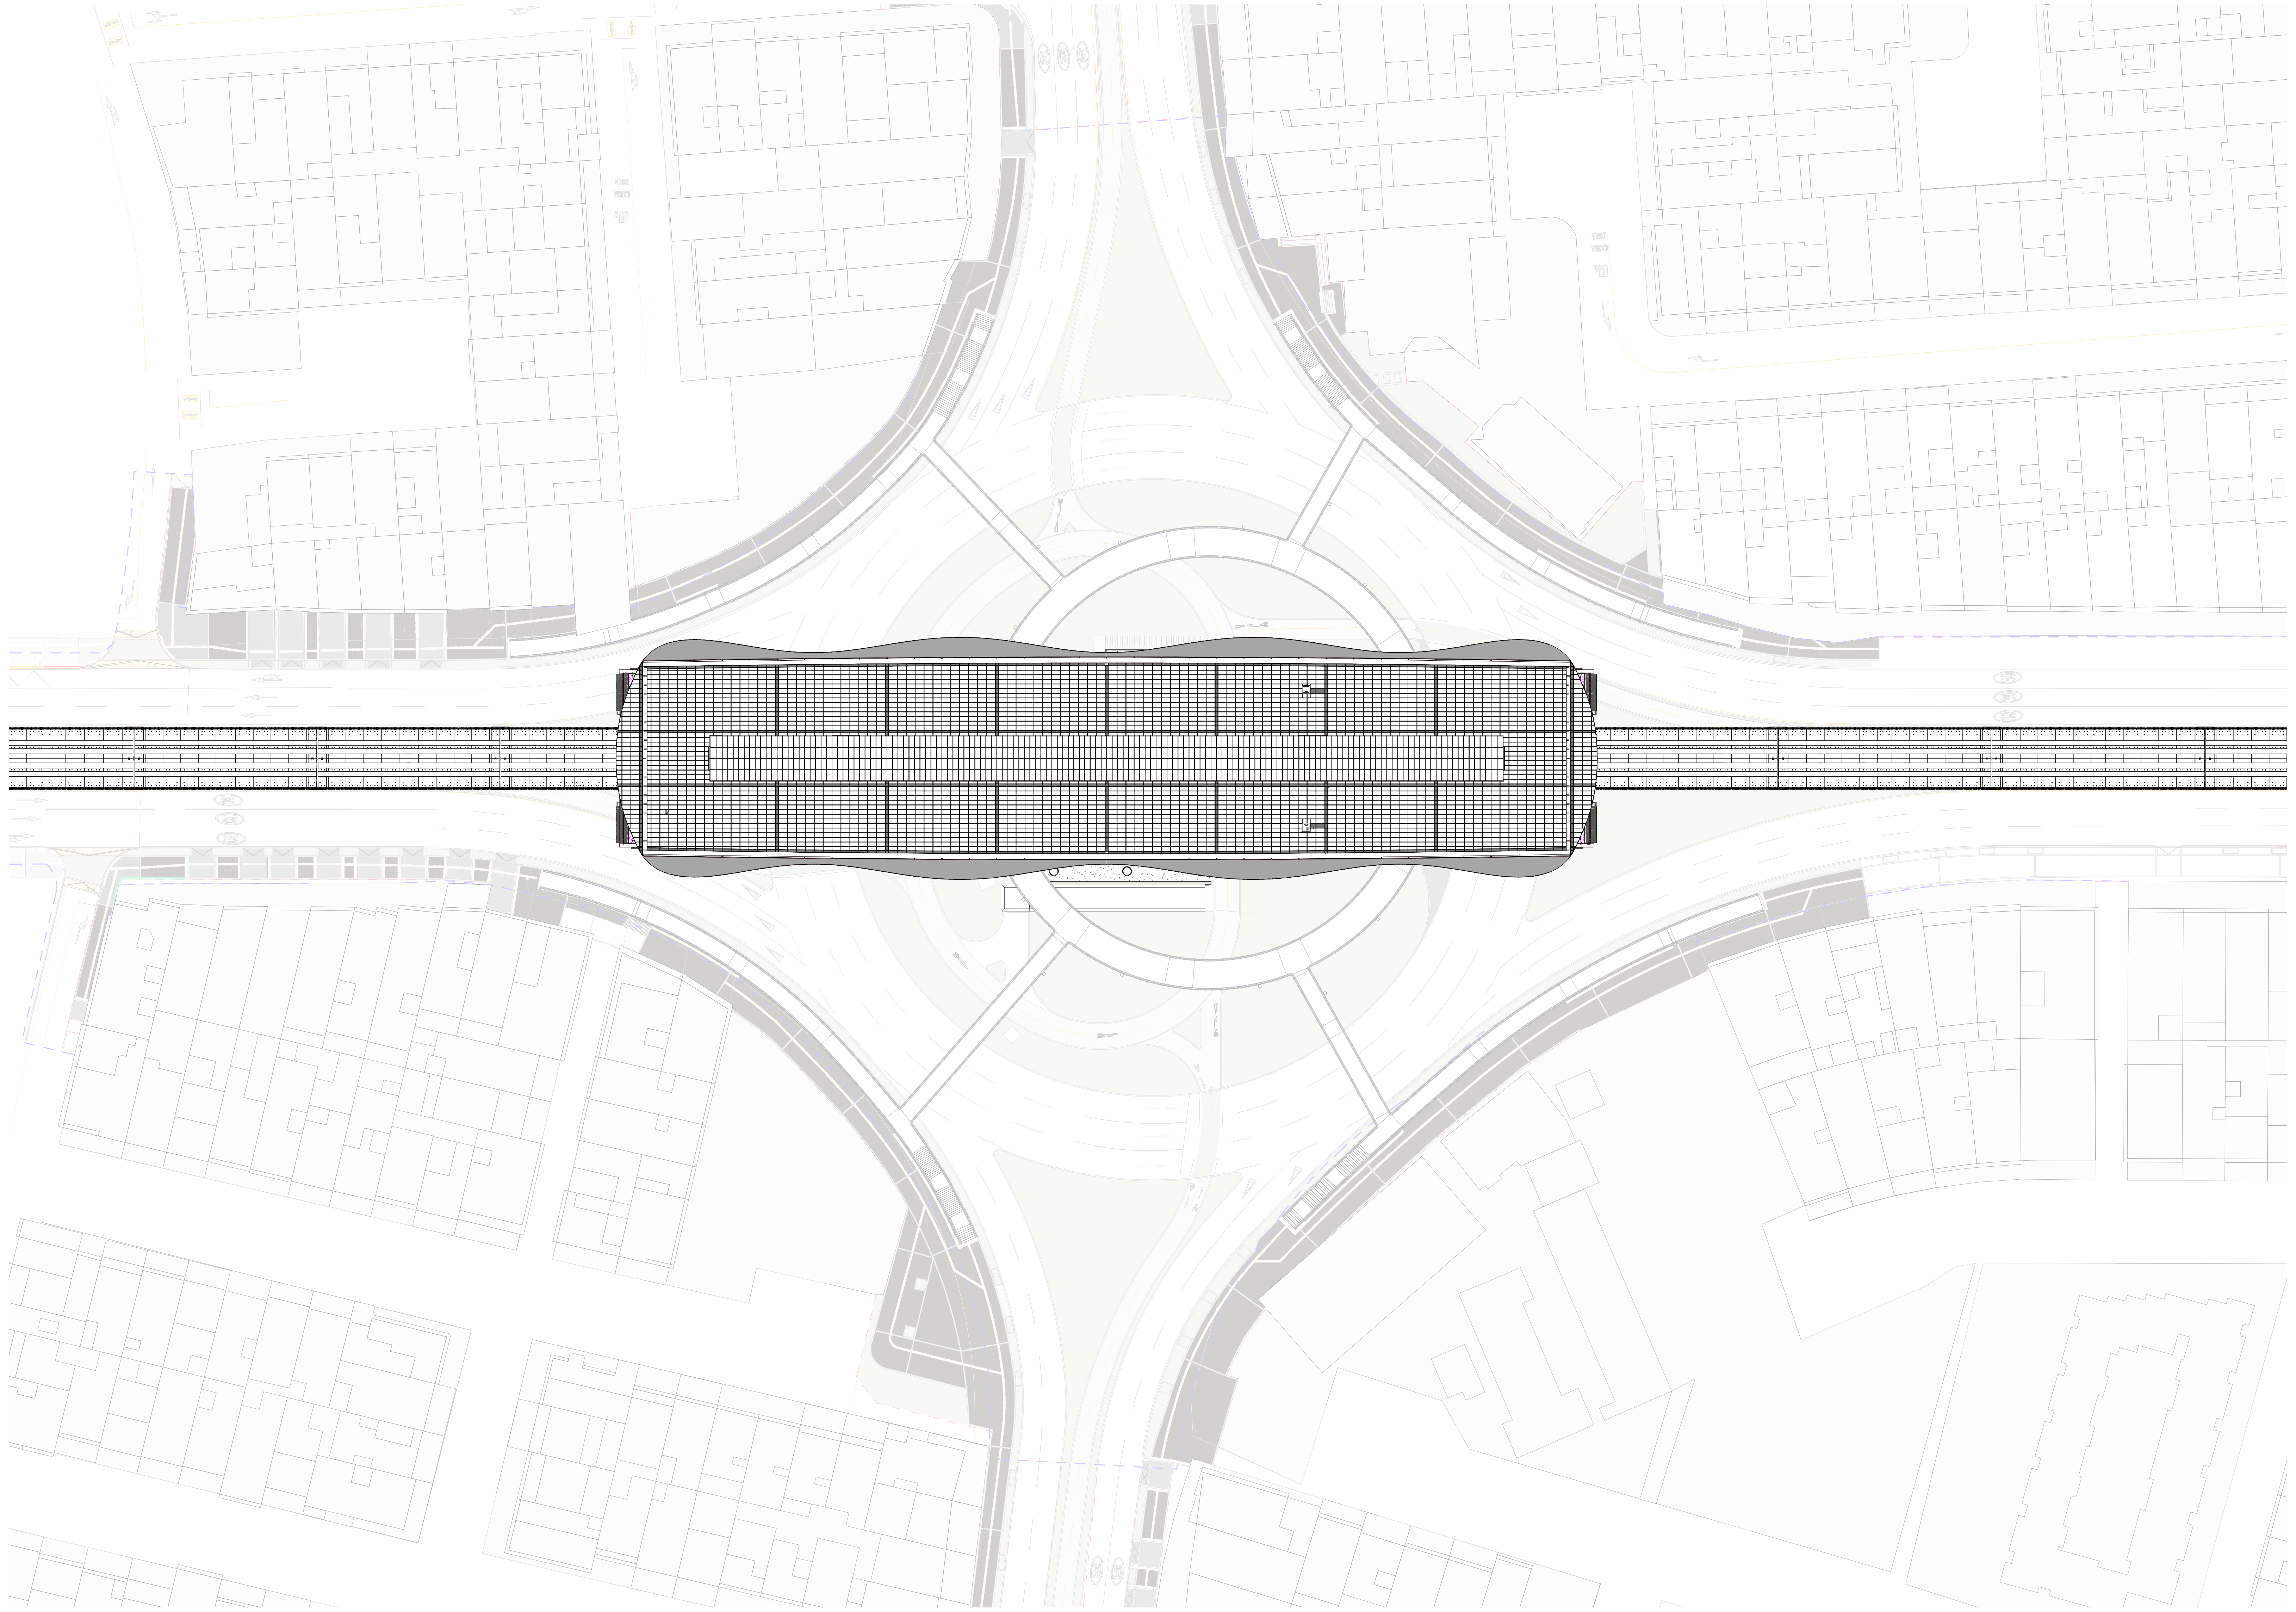

2 **NIVEL CUBIERTA_NAVE CENTRAL**
ESC: 1 : 500

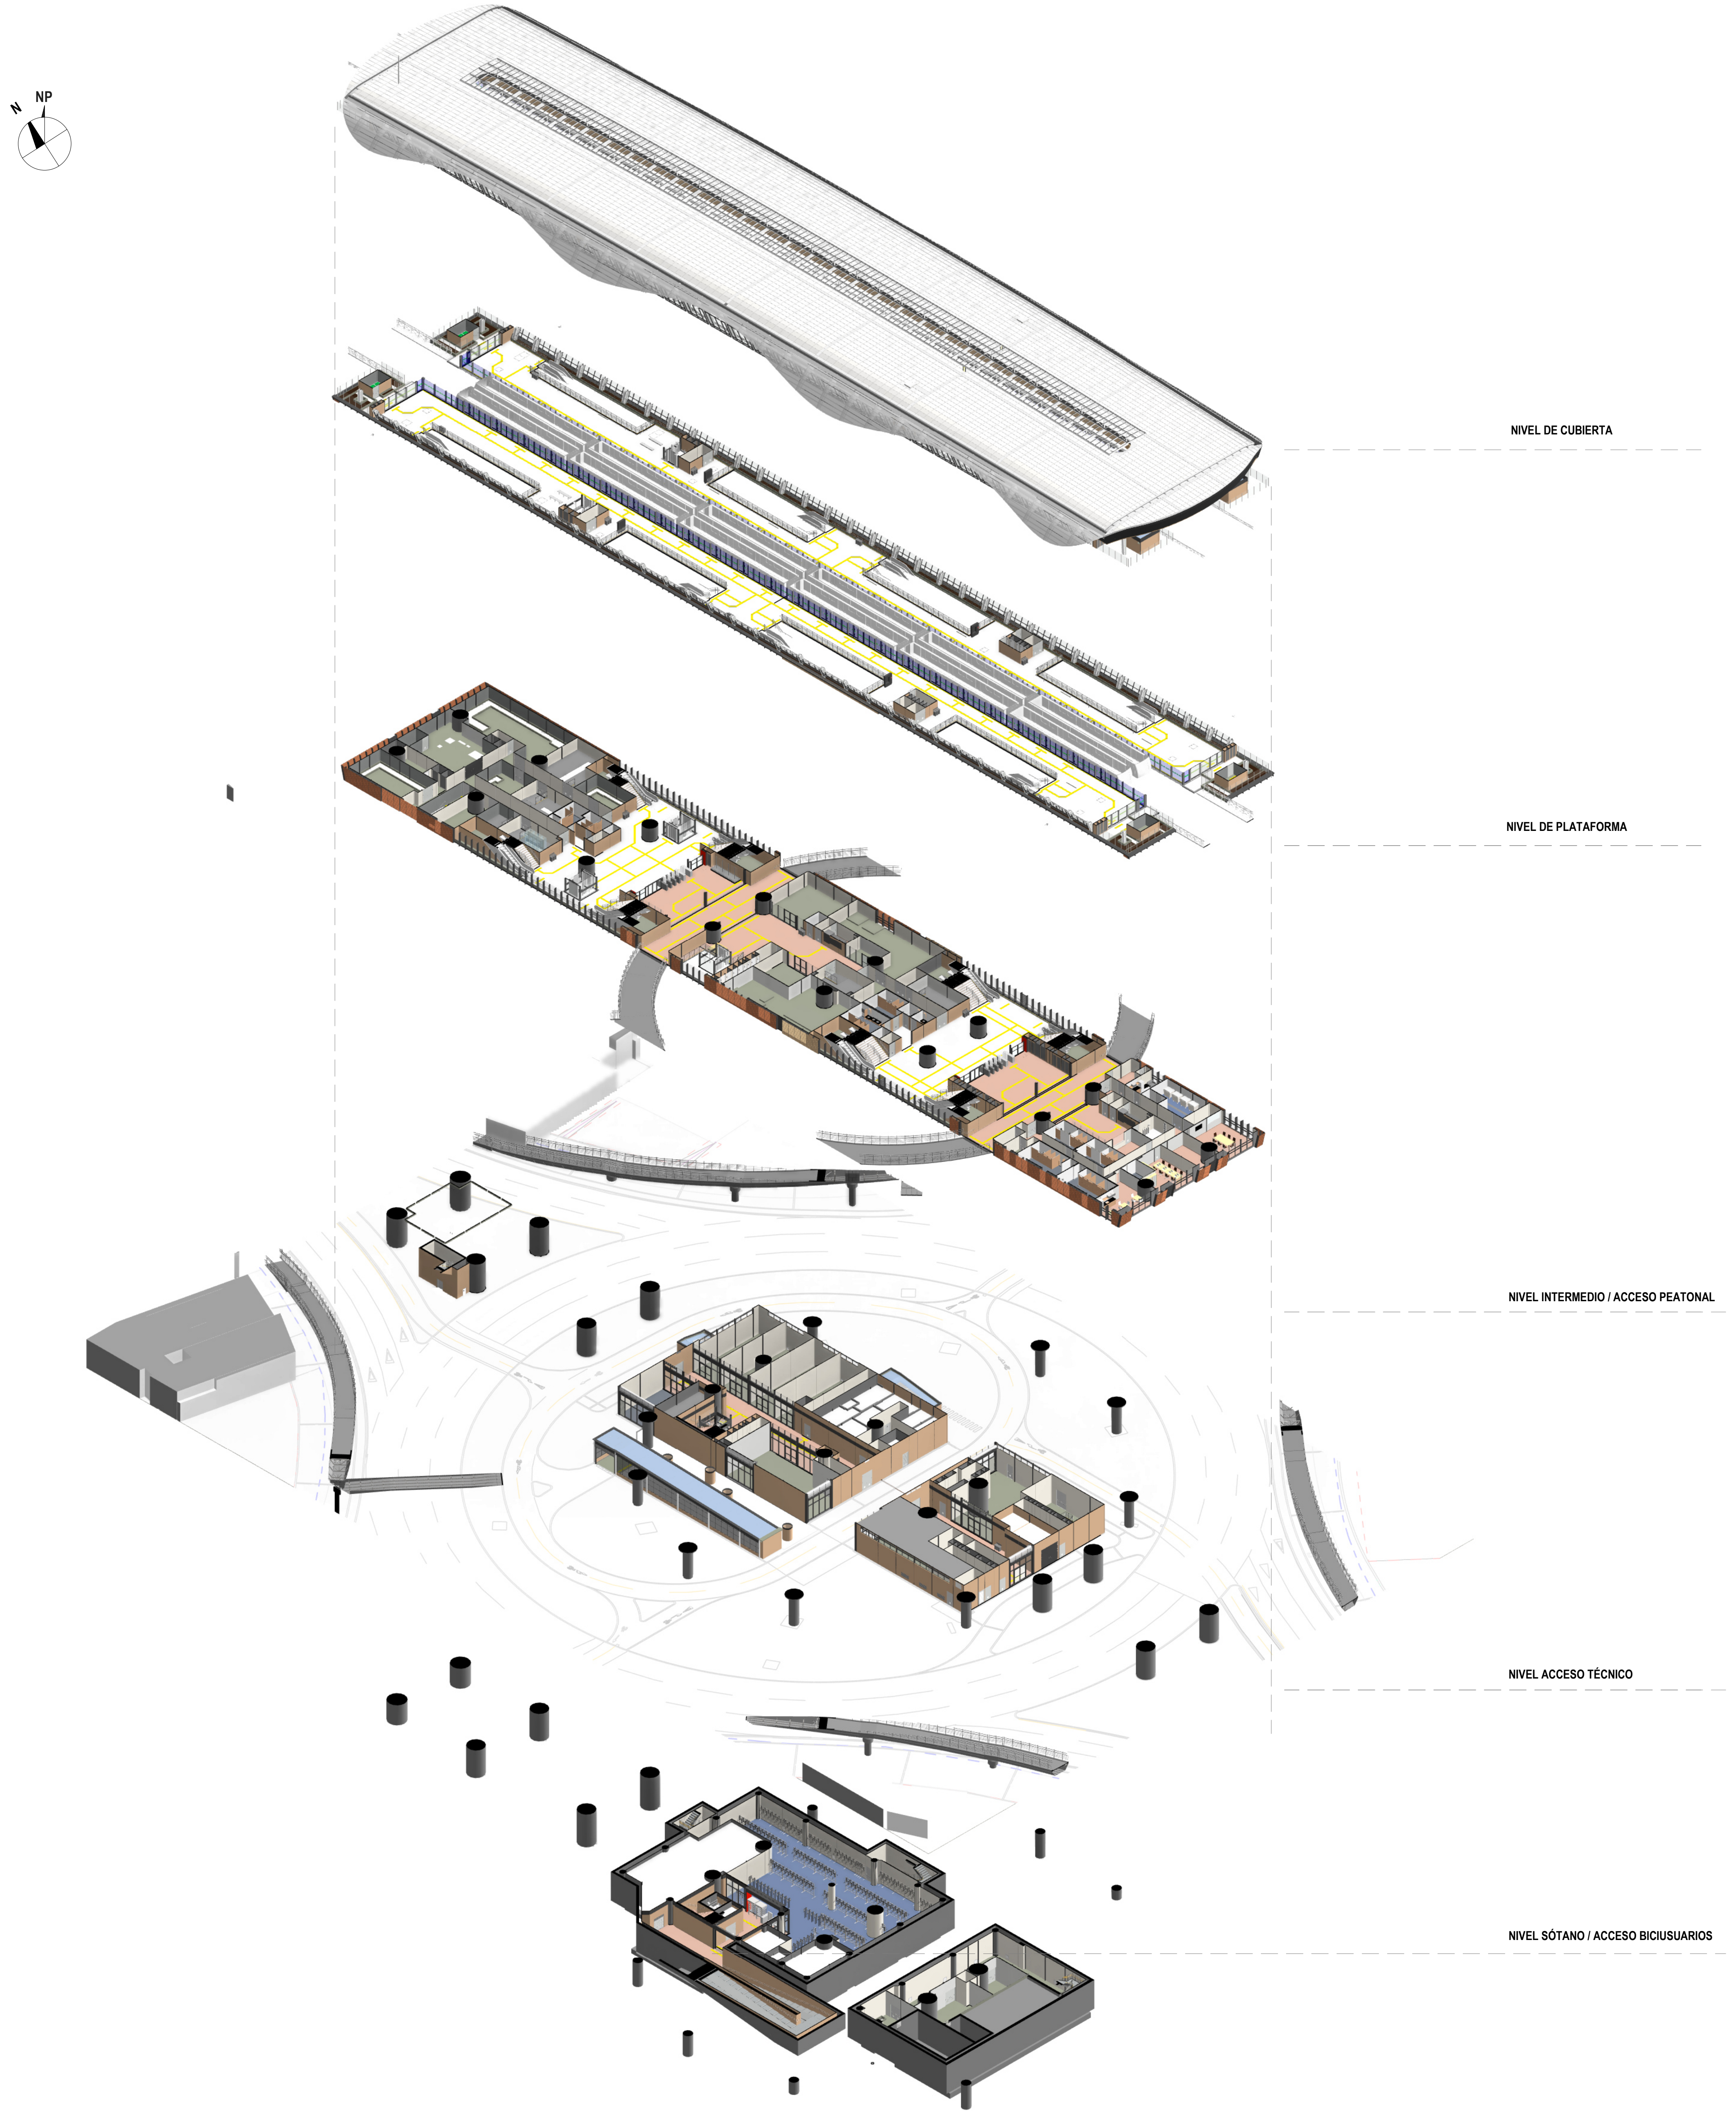
N
NP
NIVEL DE CUBIERTA
NIVEL DE PLATAFORMA
NIVEL INTERMEDIO / ACCESO PEATONAL
NIVEL ACCESO TÉCNICO
NIVEL SÓTANO / ACCESO BICIUSUARIOS

1 **3D_SUBDIVISIÓN POR NIVELES**
ESC: N/A

LOCALIZACIÓN

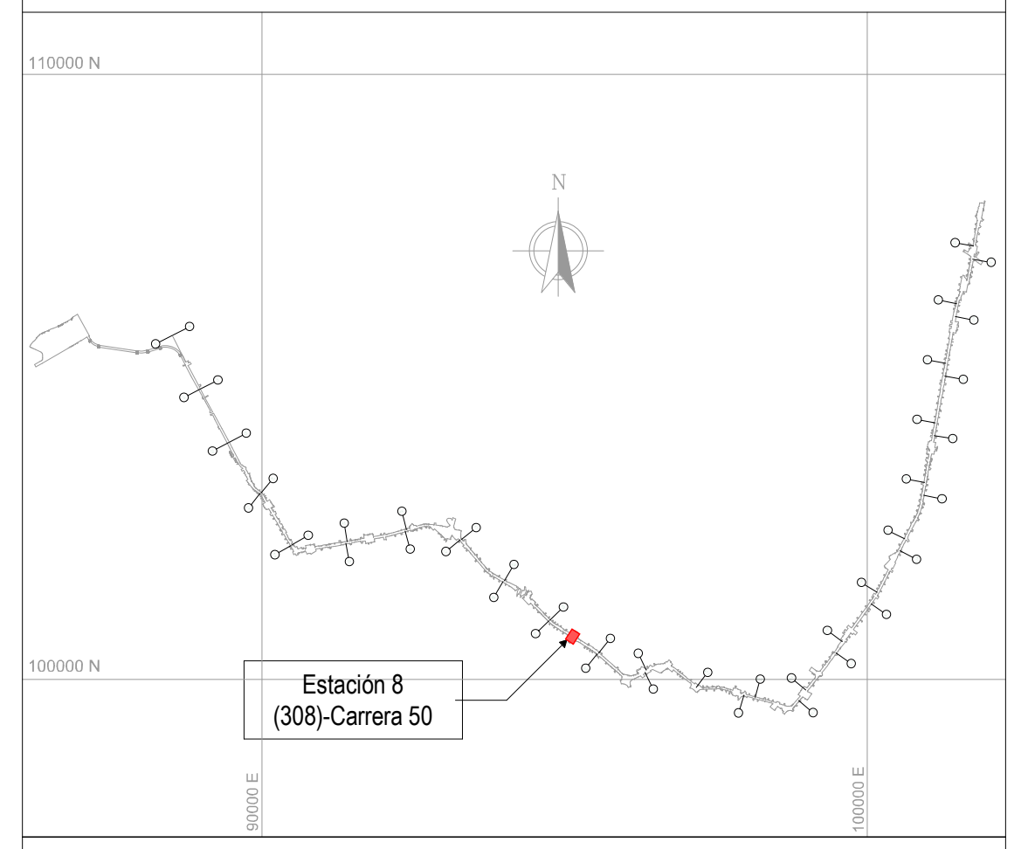

NOTAS

01 TODAS LAS DIMENSIONES ESTÁN CONFIGURADAS EN METROS A MENOS QUE SE INDIQUE UNA UNIDAD DE MEDIDA DIFERENTE.

02 TODAS LAS MEDIDAS, UBICACIÓN Y NIVELES DEBEN VERIFICARSE EN EL LUGAR DE CONSTRUCCIÓN.

03 EL NIVEL DE ACCESO AL EDIFICIO PL 01 CORRESPONDE AL +0,00 DE LA ESTACIÓN Y REFERENCIA AL NIVEL 2555.65 M.S.N.M

04 LOS EJES DEBEN VERIFICARSE EN LA VISTA EN PLANTA DE LOS PLANOS ARQUITECTÓNICOS.

05 LOS COLORES QUE SE MUESTRAN EN LOS PLANOS COMO PROYECCIÓN DE ELEMENTOS ARQUITECTÓNICOS COMO CUBIERTAS FACHADAS MUROS ETC. NO REPRESENTAN LA MATERIALIDAD Y REALIDAD DE ACABADOS DEL PROYECTO, SOLO SON INDICATIVOS PARA REALIZAR UNA CORRECTA LECTURA DE LA PLANIMETRÍA.

06 VER LOS PLANOS DE LAS ESPECIALIDADES ESPECÍFICAS PARA EL DISEÑO DE LAS ZONAS EXTERIORES DE LAS ESTACIONES METRO EN LOS QUE SE ENCUENTRAN DETALLES DE URBANISMO, PAISAJISMO, PASOS PEATONALES Y VÍAS.

- ARC_PL_00 = SÓTANO / ACCESO BICIUSUARIOS	/ NPT -6.25
- ARC_PL_01 = ACCESO TÉCNICO	/ NPT 0.00
- ARC_PL_02 = INTERMEDIO / ACCESO PEATONAL	/ NPT 7.60
- ARC_PL_02.1 = PLACA INFERIOR VIGA CAJÓN	/ NPT 13.82
- ARC_PL_02.2 = TOPE DE RIEL (TOR)	/ NPT 15.95
- ARC_PL_03 = PLATAFORMA	/ NPT 17.09
- ARC_PL_05 = CUBIERTA NAVE CENTRAL	/ NPT 26.42

CONVENCIONES

▬ ▬ ▬	LÍMITE DE INTERVENCIÓN
‒ ‒ ‒	HUELLA APÉNDICE TÉCNICO
■	MURO DIVISORIO
— — —	PROYECCIÓN NIVEL SUPERIOR

No.	PLANOS DE REFERENCIA	REV.

No.	MODELO BIM DE REFERENCIA	REV.
1	L1T1-1100-208-CON-ED-EST-MO-0001.rvt	V00
2	L1T1-1100-209-CON-ED-EST-MO-0001.rvt	V00
3	L1T1-1100-308-CON-ED-EST-MO-0001.rvt	V00
4	L1T1-1150-208-CON-ED-EST-MO-0001.rvt	V00
5	L1T1-1150-209-CON-ED-EST-MO-0001.rvt	V00
6	L1T1-1150-308-CON-ED-EST-MO-0001.rvt	V00
7	L1T1-1200-308-CON-ED-EST-MO-0001.rvt	V00
8	L1T1-1410-308-CON-ED-MEC-MO-0001.rvt	V00
9	L1T1-1420-308-CON-ED-MEC-MO-0001.rvt	V00
10	L1T1-2420-561-CON-ED-EST-MO-0001.rvt	V00
11	L1T1-5160-308-CON-ED-EST-MO-0001.rvt	V00
12	L1T1-5160-308-CON-ED-ARQ-MO-0001.rvt	V00
13	L1T1-5300-308-CON-ED-MEC-MO-0001.rvt	V00

No.	PAQUETE DE TRABAJO DE REFERENCIA	REV.
1	XREF-URBANISM_CONTEXT_ST08.rvt	
2	XREF-SECONDARY-STRUCTURE-ST08.rvt	

0 5 25m
1:500

VÁLIDO PARA CONSTRUCCIÓN
12/12/2025

METRO BOGOTÁ
GCS Consorcio Consultores PMO Bogotá
CONSORCIO SUPERVISOR PLMB
wsp

DISEÑÓ: Santiago A. David G.
SANTIAGO ANDRES DAVID GUZMÁN
Mat.: A413202011-1010176190

REVISÓ:
Digitally signed by Bautista Rondón, Freddy (COFB100240)
FREDDY BAUTISTA R.
Mat.:25202-092831 CND

APROBÓ:
Firmado digitalmente por MAURICIO MEJIA RESTREPO
Fecha: 2026.01.26 15:50:54 -05'00'
MAURICIO MEJÍA RESTREPO
Mat.: 25202-72411 CND

DIBUJÓ:
EQUIPO WSP

REVISIÓN No.	FECHA	DESCRIPCIÓN	REVISÓ	APROBÓ	APROBACIÓN CLIENTE
V00	12/12/2025	REVISIÓN NO OBJETADA - EMITIDO PARA CONSTRUCCIÓN	F.B.R	M.M.R	
VCC	01/10/2025	EMITIDO PARA REVISIÓN Y COMENTARIOS DEL CLIENTE E INTERVENTORÍA - INCLUYE COMENTARIOS /(AJUSTE)	F.B.R	M.M.R	
VBB	15/07/2025	EMITIDO PARA REVISIÓN Y COMENTARIOS DEL CLIENTE E INTERVENTORÍA	F.B.R	M.M.R	
VA0	04/07/2025	EMITIDO PARA COMENTARIOS INTERNOS - EMISIÓN PRELIMINAR PARA COMENTARIOS	F.B.R	M.M.R	

METRO LÍNEA 1

METRO LÍNEA 1
CONTRATO DE CONCESIÓN No. 163 DE 2019

PROYECTO PRIMERA LÍNEA DEL METRO DE BOGOTÁ - TRAMO 1

DIRECTOR DE INTERVENTORÍA:
Firmado digitalmente por JAVIER DESCARGA NAPOLES
DN: cn=JAVIER DESCARGA NAPOLES, c=CO, o=CONSORCIO SUPERVISOR PLMB, ou=DIRECCION GENERAL, email=jdescarga@ayesa.com
Motivo: Estoy de acuerdo con las partes indicadas de este documento
Fecha: 2026.04.23 14:46:39 -05'00'
JAVIER DESCARGA N.
Mat.:25202-68697 CND

ESPECIALISTA INTERVENTORÍA:
Firmado digitalmente por Maria Auxiliadora Sánchez Hermosin
DN: cn=Maria Auxiliadora Sánchez Hermosin, c=CO Colombia, [illegible] Arquitectura, email=masanchez@ayesa.com
Motivo: Estoy de acuerdo con las partes indicadas de este documento
Fecha: 2026.04.23 14:18:45 -05'00'
MARIA AUXILIADORA SÁNCHEZ HERMOSIN
INT: PAH138382-RES.NO.34 DE 2021

FECHA:
DICIEMBRE 2025

INFRAESTRUCTURA VIAL
ARQUITECTURA
ESTACIÓN METRO 8 (CARRERA 50)
NAVE CENTRAL
VISTA EN PLANTA - NIVEL CUBIERTA - AXONOMETRÍA GENERAL

PLANCHA No: L1T1-0000-308-CON-ED-ARQ-PL-0022_08_V00
ARCHIVO: L1T1-0000-308-CON-ED-ARQ-MO-0002_V00.rvt
ESCALA: INDICADA
FECHA: JULIO 2025
REVISIÓN No. V00
PLANO No. 08 DE 47