
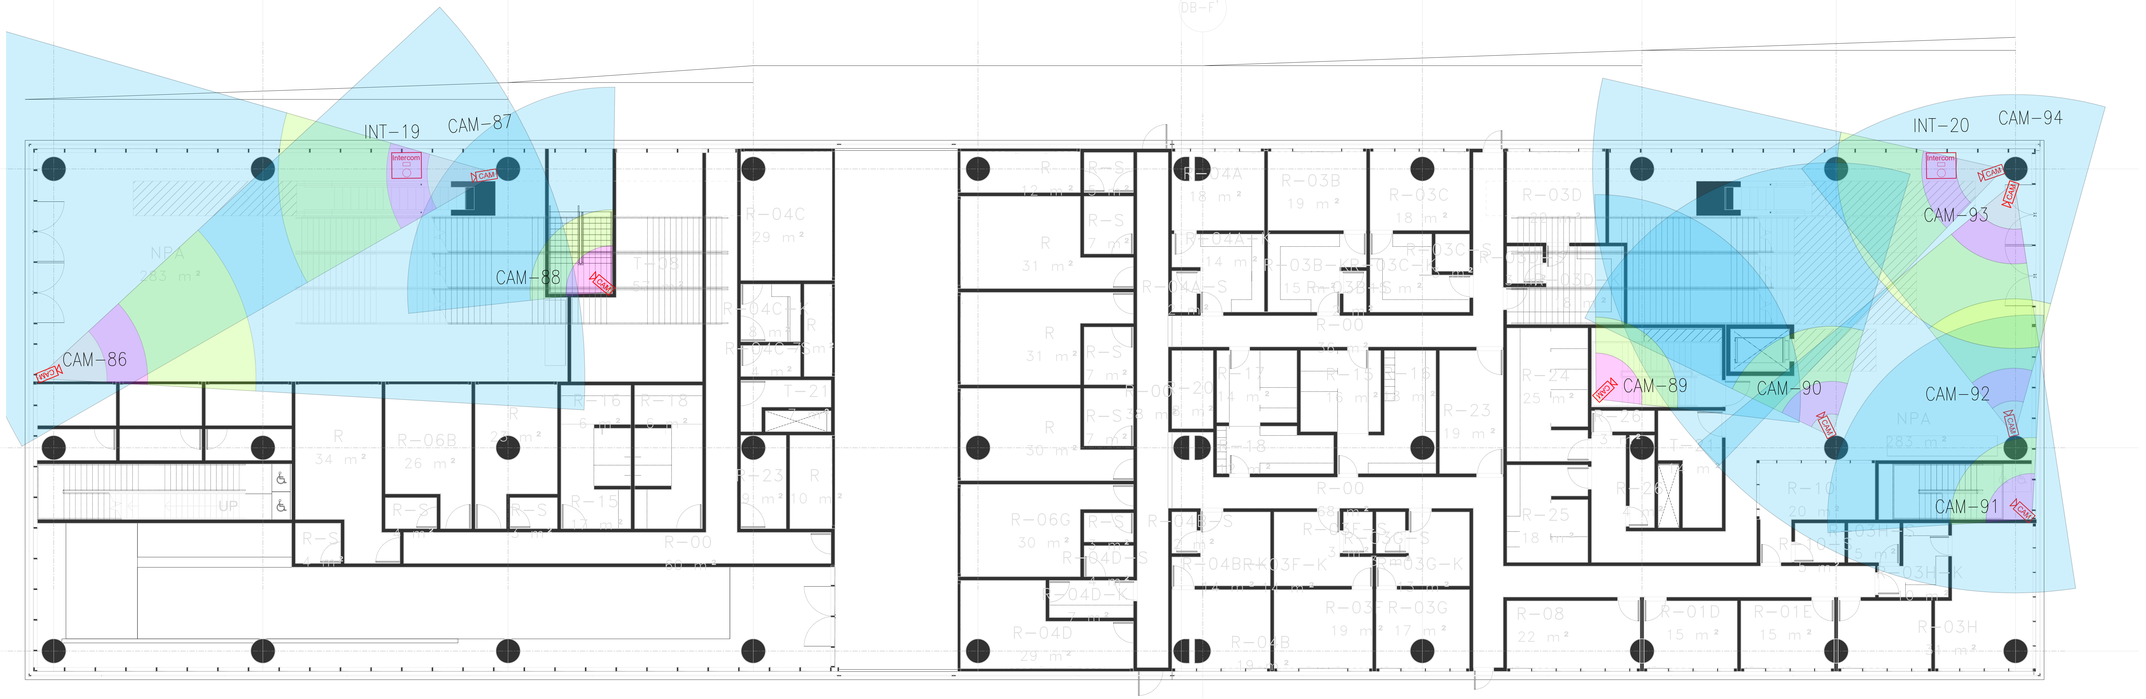


LOCALIZACIÓN

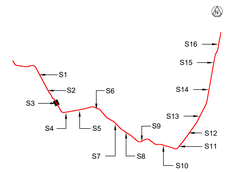

S- ESTACIÓN

NOTAS

1. ESTE PLANO DEBE IMPRIMIRSE EN COLOR.

2. NO SE DEBE ESCALAR A PARTIR DE ESTE PLANO.

3. ESTE PLANO DEBE SER REVISADO JUNTO CON EL INFORME DE TELECOMUNICACIONES .


4. EL LISTADO DE LOS EQUIPOS Y LOS CABLES, CONSULTE L1T1-5400-303-CON-ED-INS-CO-0001 Y L1T1-5400-303-CON-ED-INS-CO-0002 RESPECTIVAMENTE.

5. LOS TIPOS DE SWITCHES SE CONFIRMARÁN EN LA FASE DE DISEÑO DETALLADO.

6. LOS PUNTOS DE TERMINACIÓN SE SITUARÁN JUNTO A LOS ACTIVOS DE CAMPO DE LAS TELECOMUNICACIONES, LO QUE PERMITIRÁ LA DESCONEXIÓN LOCAL DE LA RED.

CONVENCIONES

CAM	Circuito Cerrado de Televisión
CAM PTZ	Cámara PTZ
Intercom	Intercomunicador

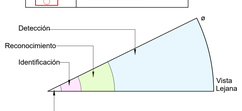

Campo de Visión de la Cámara del CCTV

No.	PLANOS DE REFERENCIA	REV.

No.	MODELO BIM DE REFERENCIA	REV.

No.	PAQUETE DE TRABAJO DE REFERENCIA	REV.

NOTAS:
"De acuerdo con el apartado 7.1 (c) del Anexo Técnico 3 del Contrato de Concesión, se declara que el presente documento no ha sido producido a partir de los modelos BIM".

METRO BOGOTÁ | GCS Consorcio Consultores PMO Bogotá | CONSORCIO SUPERVISOR PLMB | wsp

DISEÑO: ARANI MUKHERJEE Mat.: N/A
APROBÓ: FERNANDO Y. MOSQUEDA I. Céd. Extranjería: 983533 MX.
REVISÓ: JAIME ZAMLUNG Céd. Extranjería: 597/6199
MODELÓ/DIBUJÓ: EQUIPO WSP Mat.: N/A

REVISIÓN No.	FECHA	DESCRIPCIÓN	REVISÓ	APROBÓ	APROBACIÓN CLIENTE
VBB	30/11/2021	Emitido para revisión y comentarios del cliente e interventoría.	J.Z.	F.M.	
VAO	29/11/2021	Emitido para Comentarios internos	A.M	P.B.	

METRO LÍNEA 1

METRO LÍNEA 1
CONTRATO DE CONCESIÓN No. 163 DE 2019

PRIMERA LÍNEA DEL METRO DE BOGOTÁ - TRAMO 1

REVISÓ: SANTIAGO PERILLA | APROBÓ: HAO WANG | FECHA: NOVIEMBRE 2021

SISTEMAS Y EQUIPOS
TELECOMUNICACIONES
DISEÑO PRELIMINAR - ESTACIÓN CARRERA 80 - PLANTA 1
COBERTURA CCTV
DISPOSICIÓN GENERAL

PLANO No.: L1T1-5445-303-CON-ED-INS-PL-0002_VBB
ESCALA: 1:100
REVISIÓN No.: VBB
PLANO No.: 1 DE 2
ARCHIVO: L1T1-5445-303-CON-ED-INS-PL-0002_VBB.dwg
FECHA: NOVIEMBRE 2021