
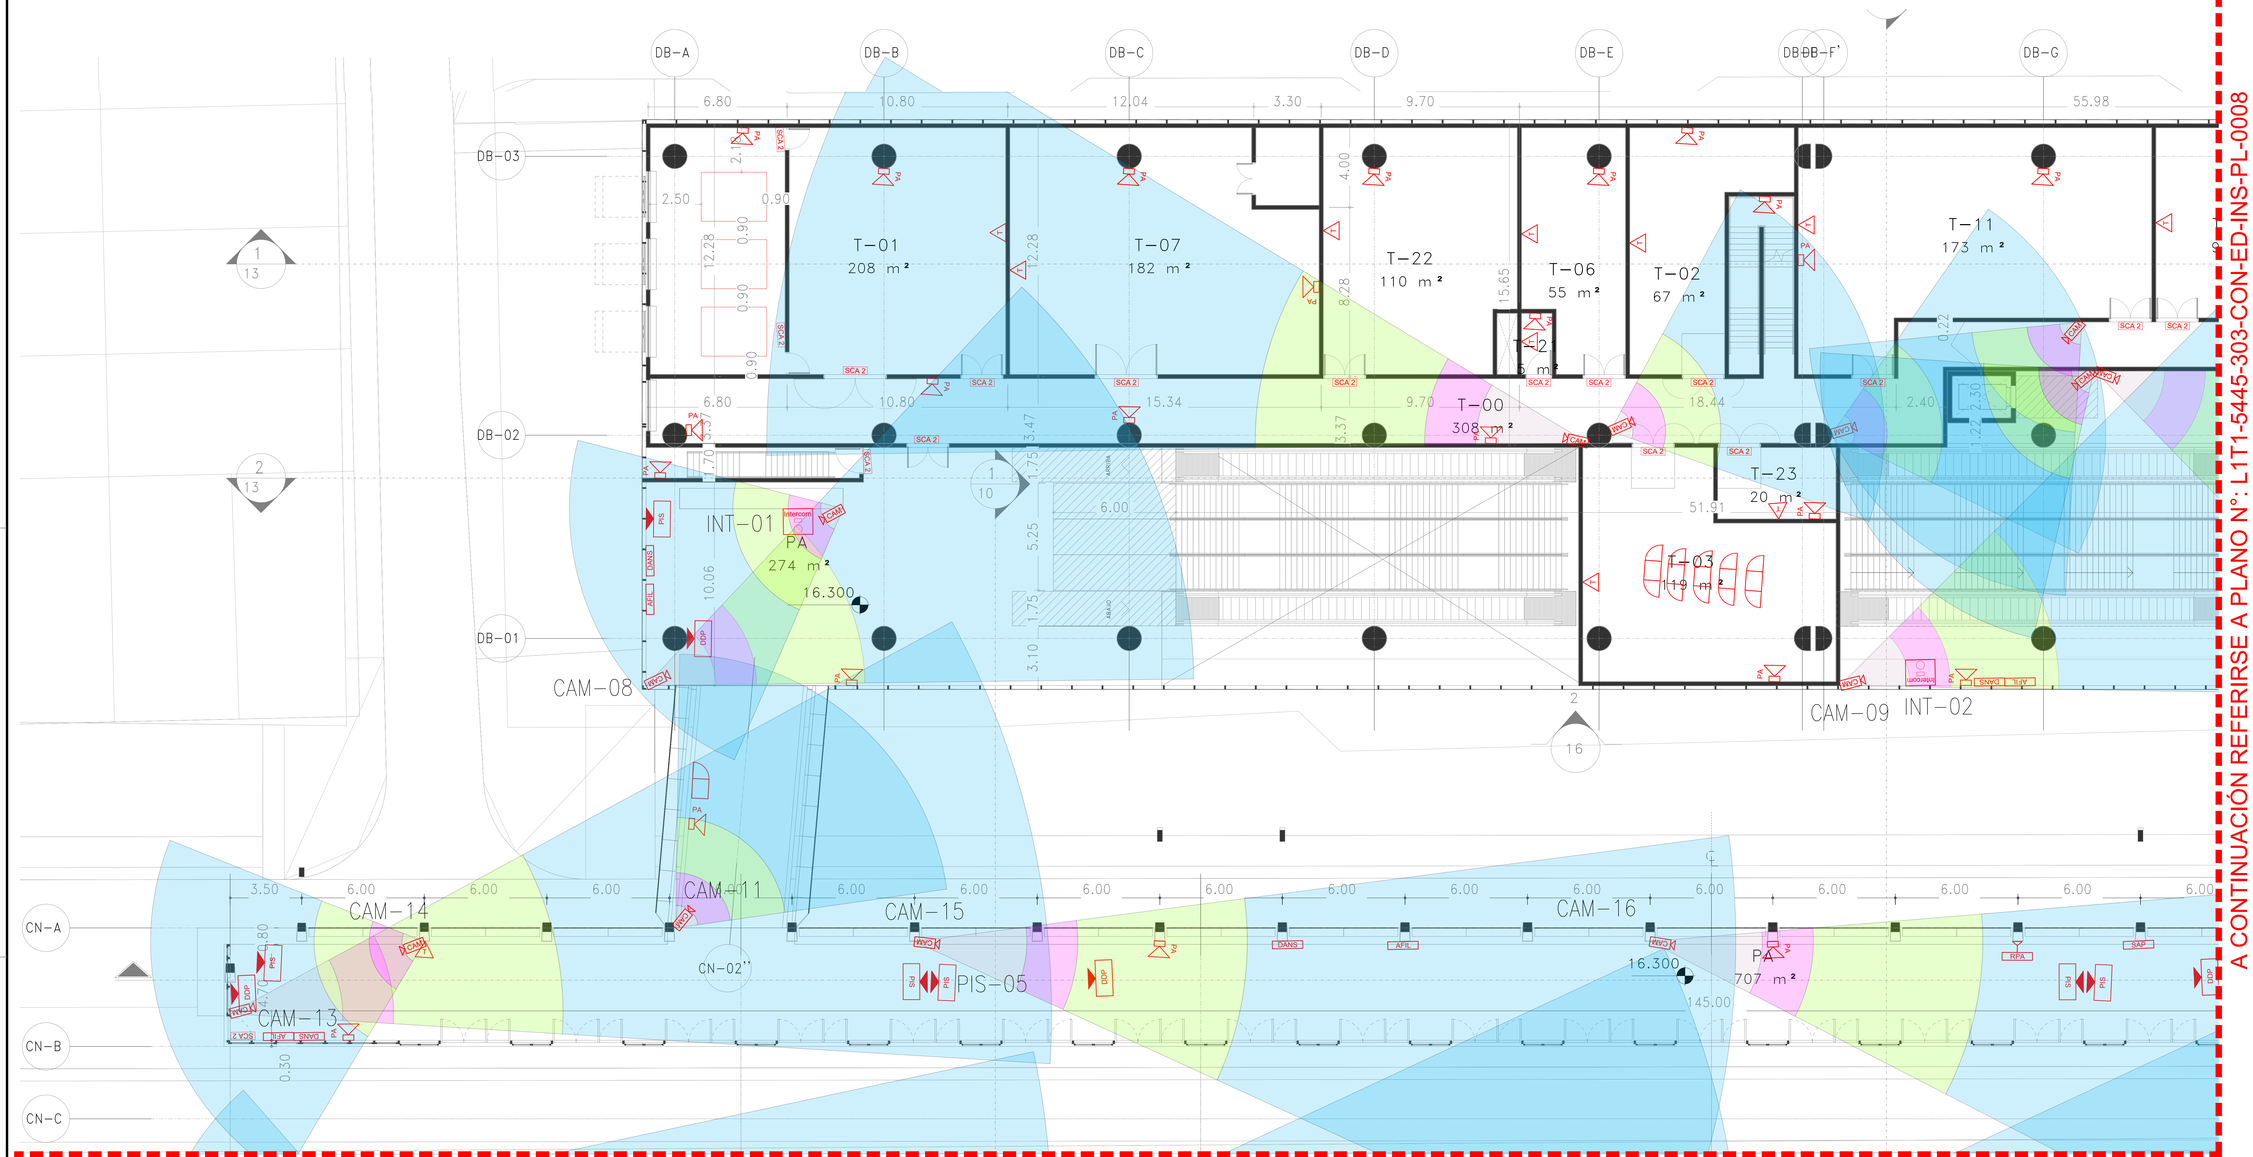


LOCALIZACIÓN

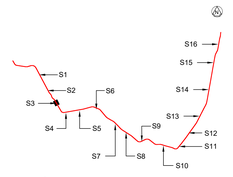


S- ESTACIÓN

NOTAS

1. ESTE PLANO DEBE IMPRIMIRSE EN COLOR.
2. NO SE DEBE ESCALAR A PARTIR DE ESTE PLANO
3. ESTE PLANO DEBE SER REVISADO JUNTO CON EL INFORME DE TELECOMUNICACIONES.
4. PARA EL LISTADO DE EQUIPOS Y CABLEADO, CONSULTE L1T1-5400-303-CON-ED-INS-CO-0001 Y L1T1-5400-303-CON-ED-INS-CO-0002 RESPECTIVAMENTE.
5. LOS TIPOS DE SWITCHES SE CONFIRMARÁN EN LA FASE DE DISEÑO DETALLADO.
6. LOS PUNTOS TERMINALES SE SITUARÁN JUNTO A LOS ACTIVOS DE CAMPO DE TELECOMUNICACIONES, PERMITIENDO LA DESCONEXIÓN LOCAL DE LA RED.

CONVENCIONES

CAM	Circuito Cerrado de Televisión
CAM	Cámara PTZ
Intercom DDP	Intercomunicador

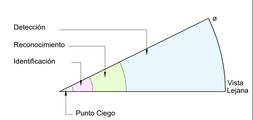

Campo de Visión de la cámara de CCTV

No.	PLANOS DE REFERENCIA	REV.

No.	MODELO BIM DE REFERENCIA	REV.

No.	PAQUETE DE TRABAJO DE REFERENCIA	REV.

NOTAS:
"De acuerdo con el apartado 7.1 (c) del Anexo Técnico 3 del Contrato de Concesión, se declara que el presente documento no ha sido producido a partir de los modelos BIM".

DISEÑO:	APROBÓ:
ARANI MUKHERJEE Mat.: N/A	FERNANDO Y. MOSQUEDA I. Céd. Extranjería: 983533 MX.
REVISÓ:	MODELÓ/DIBUJÓ
JAIME ZAMLUNG Céd. Extranjería: 597/6199	EQUIPO WSP Mat.: N/A

REVISIÓN No.	FECHA	DESCRIPCIÓN	REVISÓ	APROBÓ	APROBACIÓN CLIENTE
VBB	30/11/2021	Emitido para revisión y comentarios del cliente e interventoría.	J.Z	F.M	
VA0	29/11/2021	Emitido para Comentarios Internos.	A.M	P.B	

METRO LÍNEA 1
CONTRATO DE CONCESIÓN NO. 163 DE 2019

PROYECTO PRIMERA LÍNEA DEL METRO DE BOGOTÁ - TRAMO 1

REVISÓ:	APROBÓ:	FECHA:
SANTIAGO PERILLA	HAO WANG	NOVIEMBRE 2021

SISTEMAS Y EQUIPOS
TELECOMUNICACIONES
DISEÑO PRELIMINAR - ESTACIÓN CARRERA 80- PLANTA 3
COBERTURA CCTV
DISPOSICIÓN GENERAL

PLANO/IA No.:	ESCALA:	REVISIÓN No.:	PLANO No.:
L1T1-5445-303-CON-ED-INS-PL-0006_VBB	1:100	VBB	1 DE 3
ARCHIVO: L1T1-5445-303-CON-ED-INS-PL-0006_VBB.dwg	FECHA: NOVIEMBRE 2021		