

A CONTINUACIÓN REFERIRSE A PLANO N°: L1T1-5445-304-CON-ED-INS-PL-0004

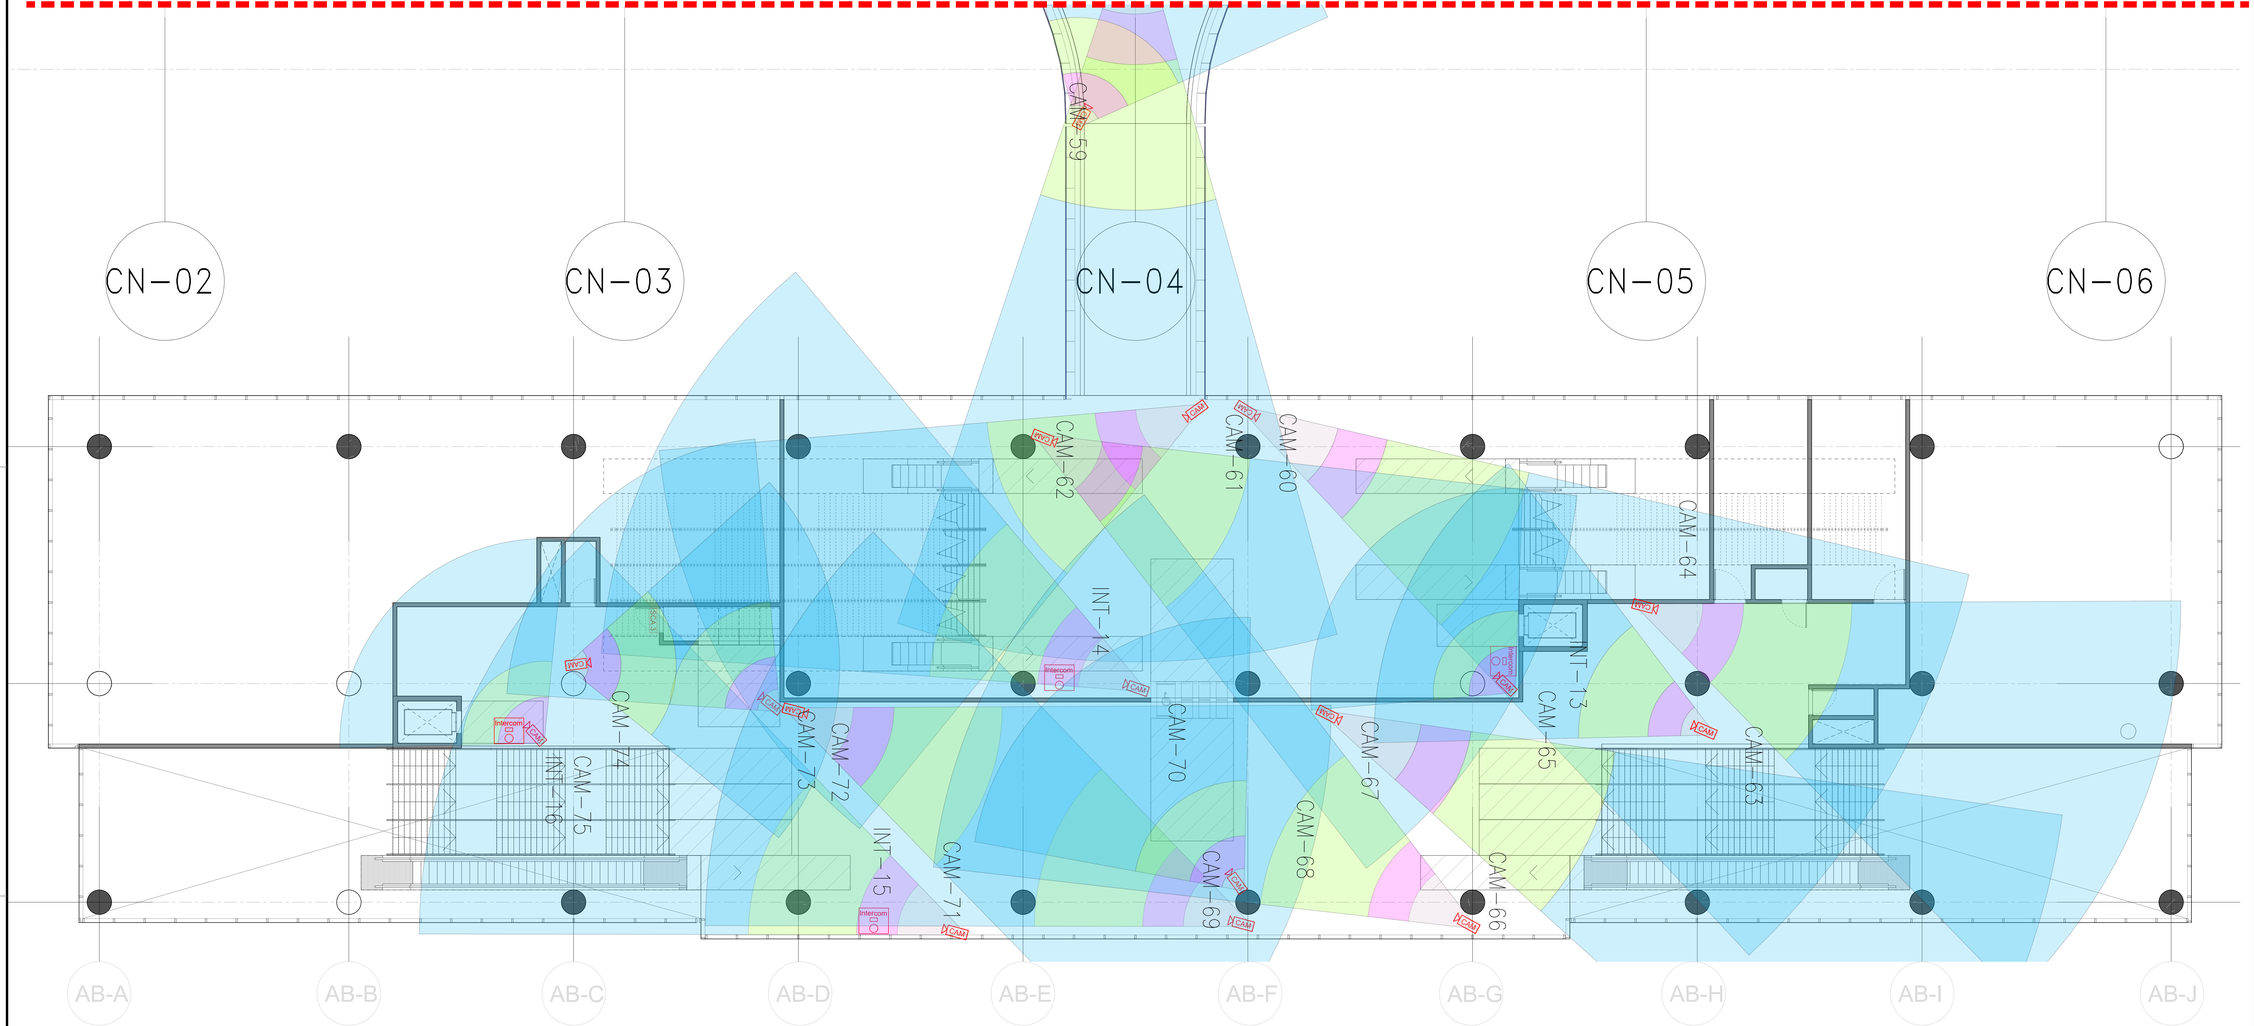

LOCALIZACIÓN

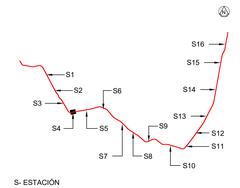

S- ESTACIÓN

NOTAS

1. ESTE PLANO DEBE IMPRIMIRSE EN COLOR.
2. NO SE DEBE ESCALAR A PARTIR DE ESTE PLANO.
3. ESTE PLANO DEBE SER REVISADO JUNTO CON EL INFORME DE TELECOMUNICACIONES.
4. PARA EL LISTADO DE EQUIPOS Y CABLEADO, CONSULTE L1T1-5400-304-CON-ED-INS-CO-0001 Y L1T1-5400-304-CON-ED-INS-CO-0002 RESPECTIVAMENTE.
5. LOS TIPOS DE SWITCH SE CONFIRMARÁN EN LA FASE DE DISEÑO DETALLADO.
6. LOS PUNTOS TERMINALES SE SITUARÁN JUNTO A LOS ACTIVOS DE CAMPO DE TELECOMUNICACIONES, PERMITIENDO LA DESCONEXIÓN LOCAL DE LA RED.

CONVENCIONES

CAM	Circuito Cerrado de Televisión
CAM	Cámara PTZ
Intercom	Intercomunicador



Campo de Visión de la cámara de CCTV

No.	PLANOS DE REFERENCIA	REV.

No.	MODELO BIM DE REFERENCIA	REV.

No.	PAQUETE DE TRABAJO DE REFERENCIA	REV.

NOTAS:
"De acuerdo con el apartado 7.1 (c) del Anexo Técnico 3 del Contrato de Concesión, se declara que el presente documento no ha sido producido a partir de los modelos BIM".

METRO BOGOTÁ | GCS Consorcio Consultores PMO Bogotá | CONSORCIO SUPERVISOR PLMB | wsp

DISEÑO: ARANI MUKHERJEE Mat.: N/A
APROBÓ: FERNANDO Y. MOSQUEDA I. Céd. Extranjería: 983533 MX.
REVISÓ: JAIME ZAMLUNG Céd. Extranjería: 5976199
MODELÓ/DIBUJÓ: EQUIPO WSP Mat.: N/A

REVISIÓN No.	FECHA	DESCRIPCIÓN	REVISÓ	APROBÓ	APROBACIÓN CLIENTE
VBB	20/11/2021	Emitido para revisión y comentarios del cliente e interventoría.	J.Z	F.M	
VAO	19/11/2021	Emitido para Comentarios Internos.	A.M	P.B	

METRO LÍNEA 1

METRO LÍNEA 1
CONTRATO DE CONCESIÓN NO. 163 DE 2019

PROYECTO PRIMERA LÍNEA DEL METRO DE BOGOTÁ - TRAMO 1

REVISÓ: SANTIAGO PERILLA | APROBÓ: HAO WANG | FECHA: NOVIEMBRE 2021

SISTEMAS Y EQUIPOS
TELECOMUNICACIONES
DISEÑO PRELIMINAR - ESTACIÓN CALLE 42 SUR - PLANTA 2
COBERTURA CCTV
DISPOSICIÓN GENERAL

PLANO No.: L1T1-5445-304-CON-ED-INS-PL-0005_VBB
ARCHIVO: L1T1-5445-304-CON-ED-INS-PL-0005_VBB.dwg
ESCALA: 1:100
FECHA: NOVIEMBRE 2021
REVISIÓN No.: VBB
PLANO No.: 2 DE 2