L1T1-CON-CAL-FR-0120 - B1 : 1000x707mm

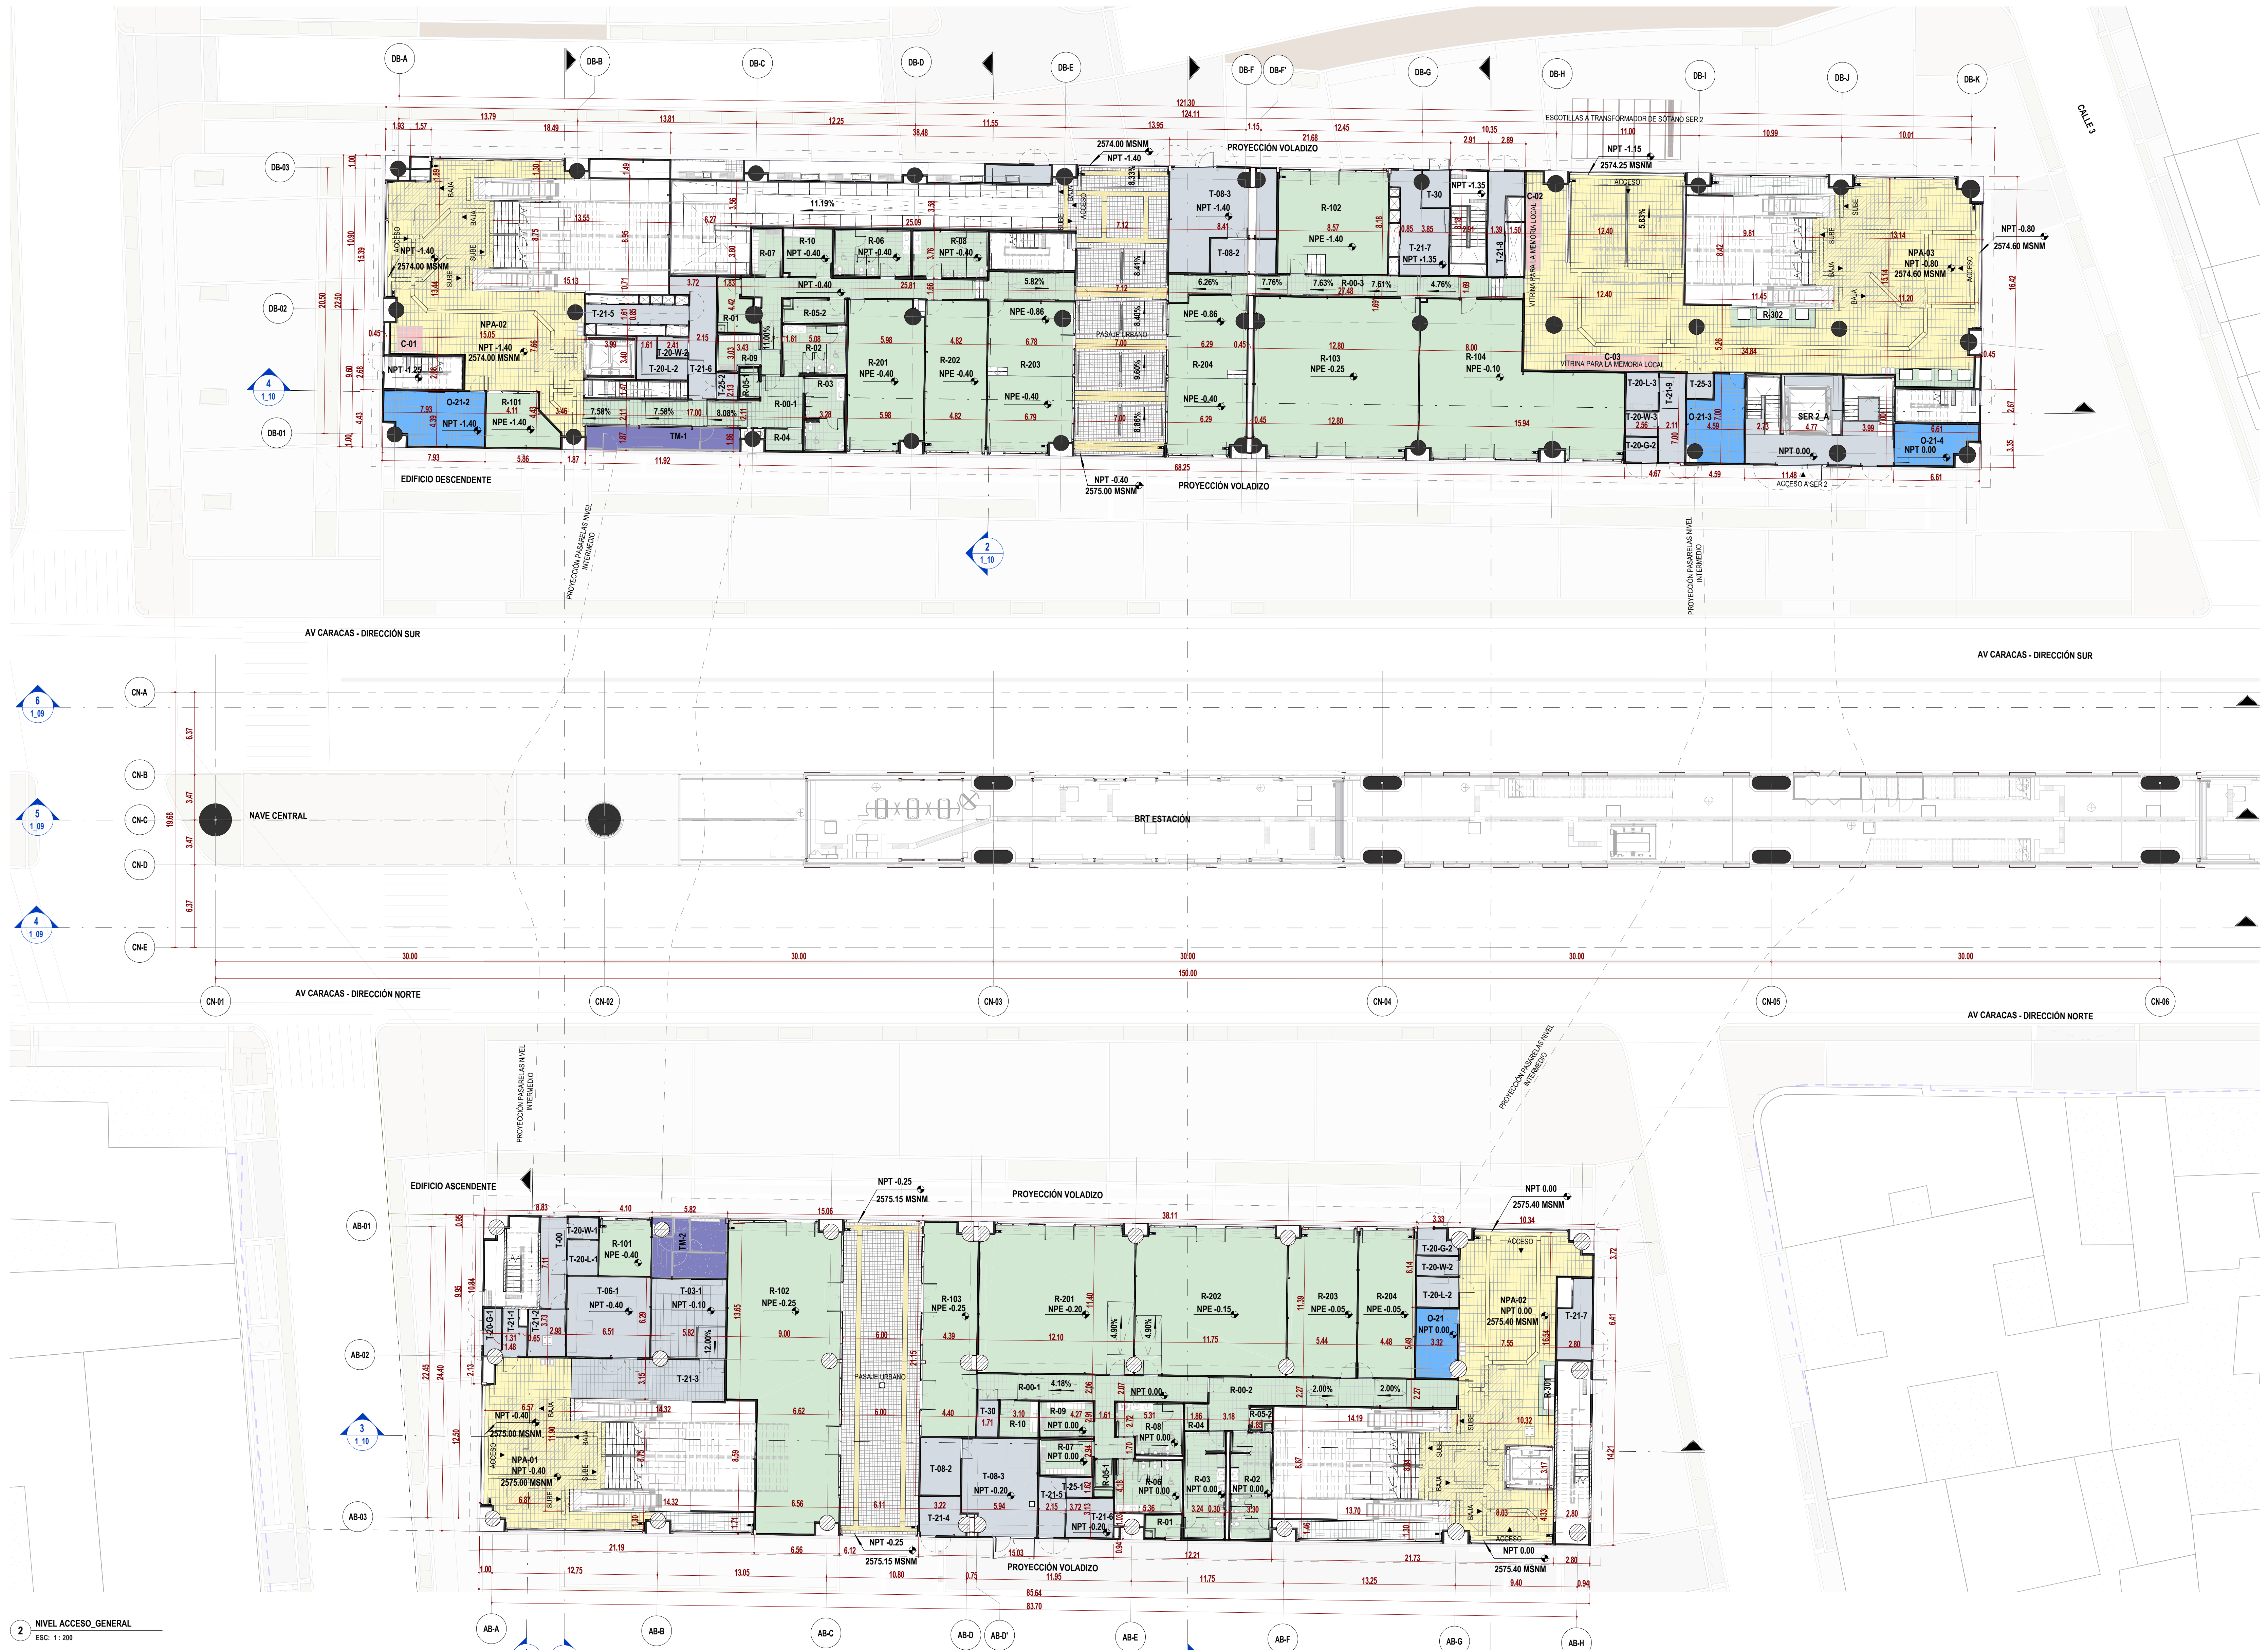

2 NIVEL ACCESO_GENERAL
ESC: 1 : 200

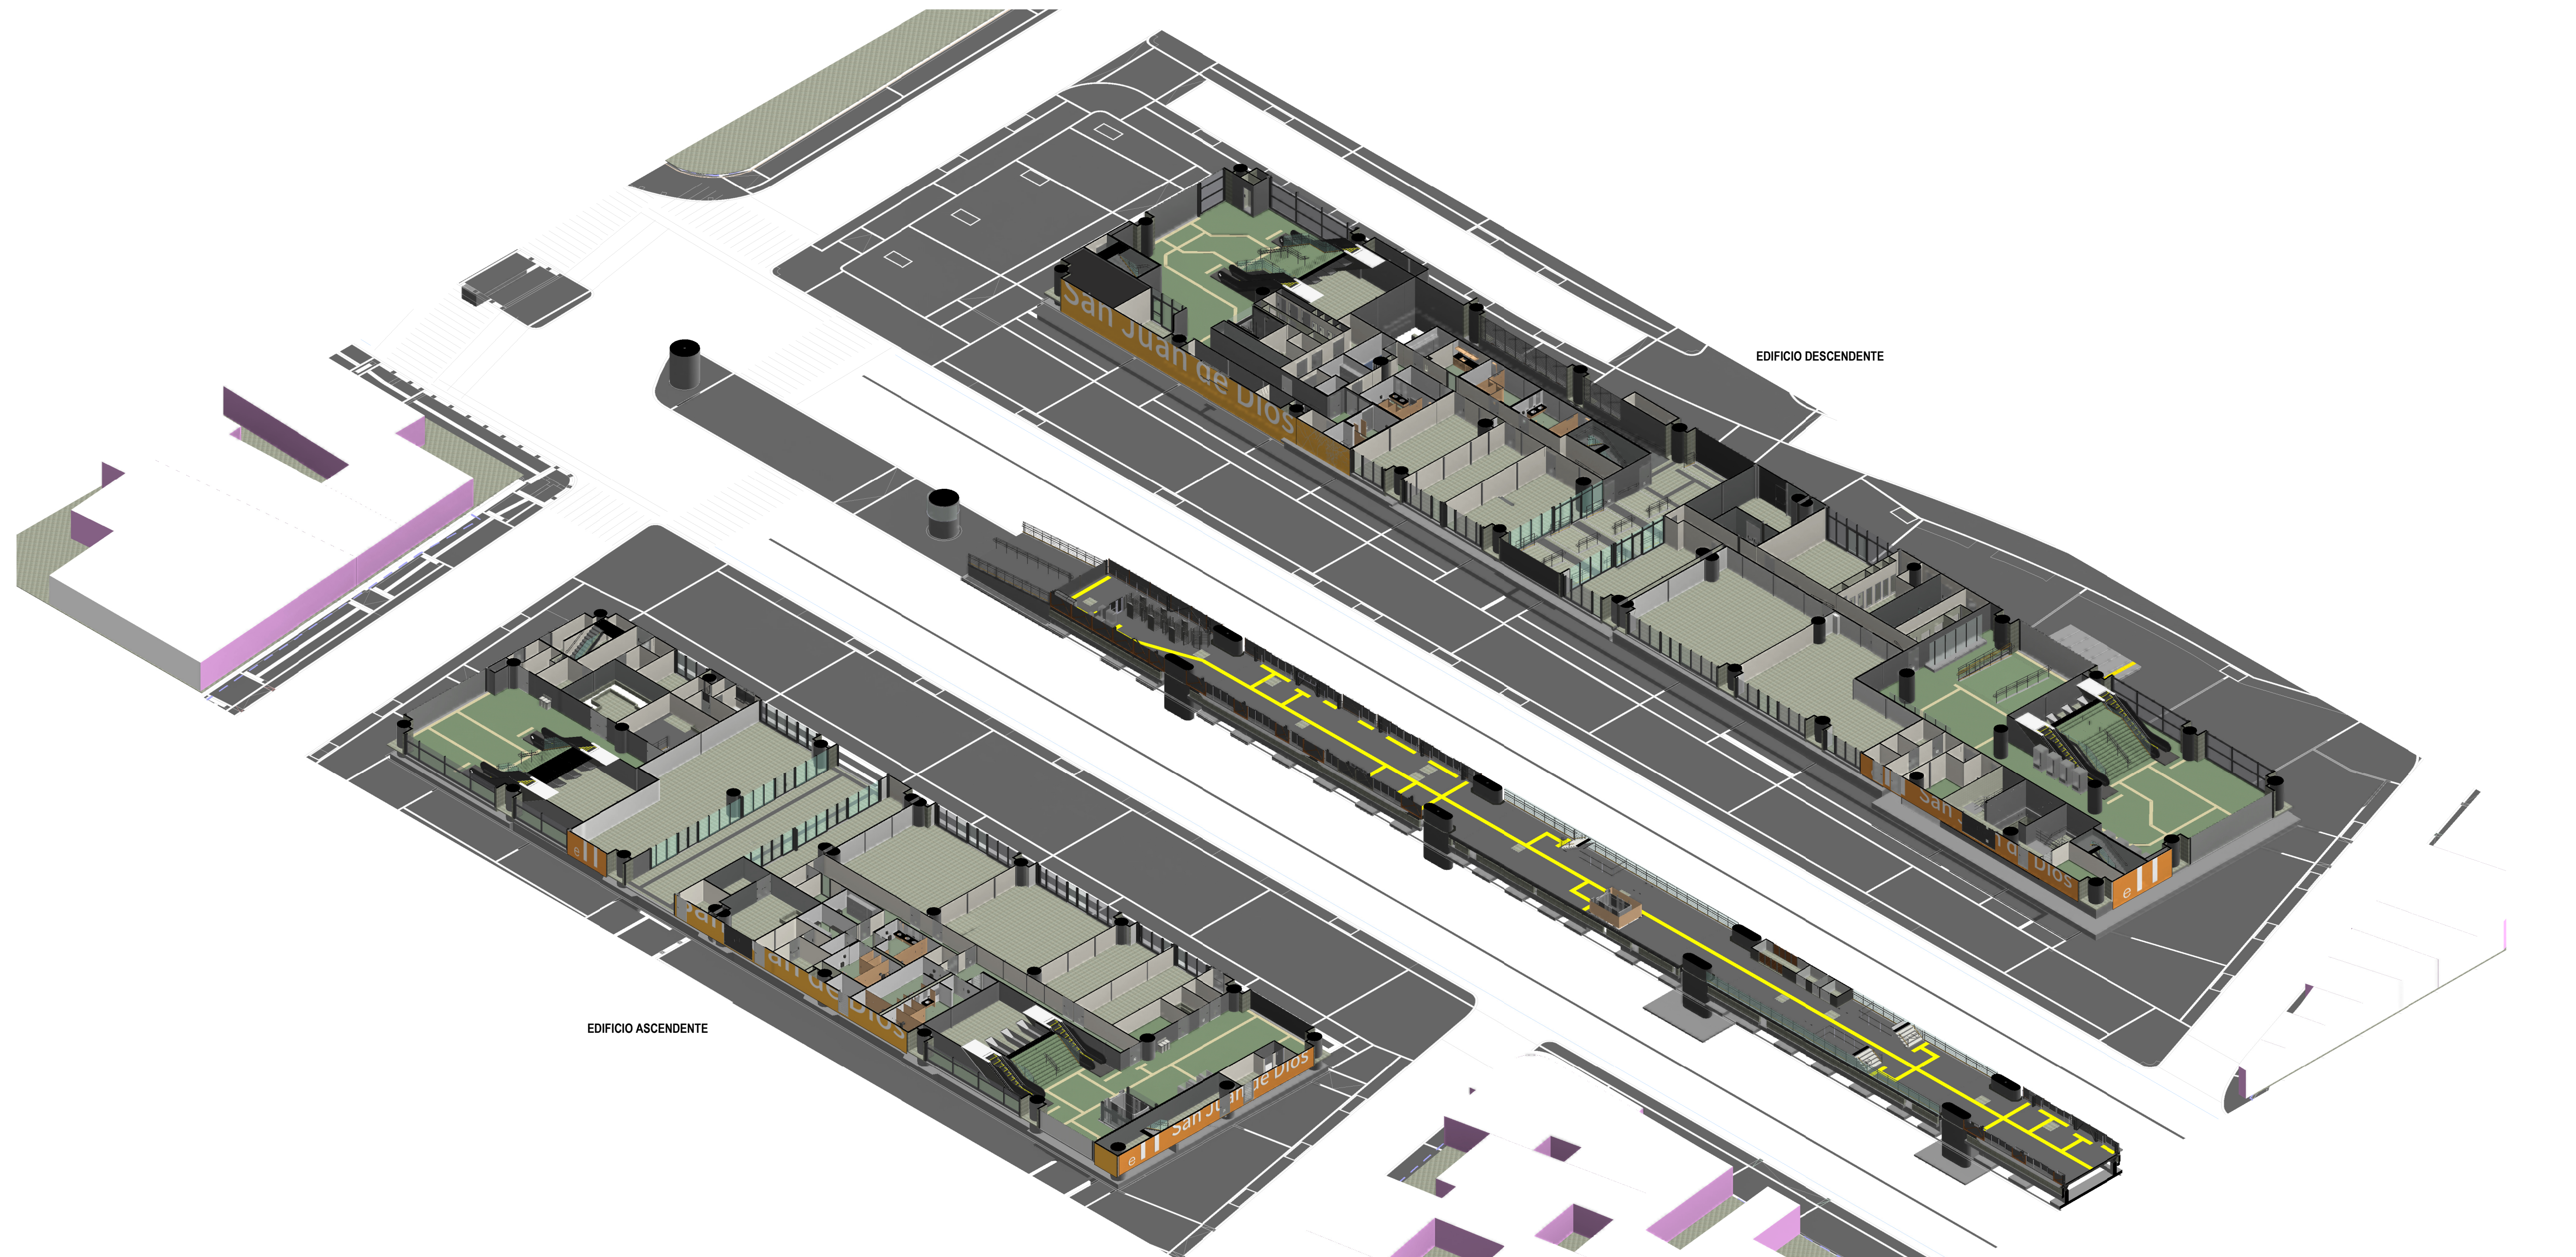

1 3D_NIVEL ACCESO_GENERAL
ESC: N/A

TABLA DE ÁREAS ÚTILES (NIVEL ACCESO)

CÓDIGO	NOMBRE	ÁREA (m²)	DEPARTAMENTO
EDIFICIO ASCENDENTE			
ARQ_PL_00.6_ACCESO			
NPA-01	ÁREA NO PAGA	107.75	ÁREA NO PAGA
R-101	SERVICIOS ADICIONALES - ÁREA DE SERVICIO	16.99	SERVICIOS ADICIONALES - ÁREA NO PAGA
T-00	CIRCULACIÓN TÉCNICA	13.99	ÁREA TÉCNICA
T-03-1	LOCAL SECUNDARIO DE TELECOMUNICACIONES	34.14	ÁREA TÉCNICA
T-06-1	LOCAL SECUNDARIO DE TABLEROS	39.23	ÁREA TÉCNICA
T-20-G-1	MEDIDORES (GAS)	4.41	ÁREA TÉCNICA
T-20-L-1	MEDIDORES (LUZ)	6.21	ÁREA TÉCNICA
T-20-W-1	MEDIDORES (AGUA)	3.72	ÁREA TÉCNICA
T-21-1	ÁREA DE INSPECCIÓN	5.79	ÁREA TÉCNICA
T-21-2	ÁREA DE INSPECCIÓN	10.35	ÁREA TÉCNICA
T-21-3	ÁREA DE INSPECCIÓN	36.68	ÁREA TÉCNICA
TM-2	ÁREA DE TAQUILLAS BRT	25.44	ÁREA DE TAQUILLAS BRT
		304.71	
ARQ_PL_00.7_ACCESO			
R-00-1	SERVICIOS ADICIONALES - CORREDOR OPERATIVO	43.97	SERVICIOS ADICIONALES - ÁREA NO PAGA
R-10	SERVICIOS ADICIONALES - SALA DE EMPLEADOS	8.30	SERVICIOS ADICIONALES - ÁREA NO PAGA
R-102	SERVICIOS ADICIONALES - ÁREA DE SERVICIO	180.69	SERVICIOS ADICIONALES - ÁREA NO PAGA
R-103	SERVICIOS ADICIONALES - ÁREA DE SERVICIO	64.78	SERVICIOS ADICIONALES - ÁREA NO PAGA
T-21-4	ÁREA DE INSPECCIÓN	9.40	ÁREA TÉCNICA
T-30	SISTEMA PROTECCIÓN CONTRA INCENDIO ENEL	4.47	ÁREA TÉCNICA
		311.62	
ARQ_PL_00.8_ACCESO			
R-01	SERVICIOS ADICIONALES - CUARTO DE BASURAS PARA METRO	5.20	SERVICIOS ADICIONALES - ÁREA NO PAGA
R-201	SERVICIOS ADICIONALES - ÁREA DE COMIDAS	136.05	SERVICIOS ADICIONALES - ÁREA NO PAGA
R-202	SERVICIOS ADICIONALES - ÁREA DE COMIDAS	130.36	SERVICIOS ADICIONALES - ÁREA NO PAGA
T-08-2	CENTRO DE TRANSFORMACIÓN ENEL-CODENSA (CT)_CUARTO BAJA TENSIÓN	13.50	ÁREA TÉCNICA
T-08-3	CENTRO DE TRANSFORMACIÓN ENEL-CODENSA (CT)_CUARTO MEDIA TENSIÓN	40.71	ÁREA TÉCNICA
T-21-5	ÁREA DE INSPECCIÓN	9.32	ÁREA TÉCNICA
T-21-6	ÁREA DE INSPECCIÓN	10.83	ÁREA TÉCNICA
T-25-1	NODO DE ACCESO DE TELECOMUNICACIONES	3.01	ÁREA TÉCNICA
		348.98	
ARQ_PL_00.9_ACCESO			
R-00-2	SERVICIOS ADICIONALES - CORREDOR OPERATIVO	47.42	SERVICIOS ADICIONALES - ÁREA NO PAGA
R-203	SERVICIOS ADICIONALES - ÁREA DE COMIDAS	59.10	SERVICIOS ADICIONALES - ÁREA NO PAGA
R-204	SERVICIOS ADICIONALES - ÁREA DE COMIDAS	49.69	SERVICIOS ADICIONALES - ÁREA NO PAGA
T-21-7	ÁREA DE INSPECCIÓN	13.98	ÁREA TÉCNICA
		170.19	
ARQ_PL_01_ACCESO			
NPA-02	ÁREA NO PAGA	184.20	ÁREA NO PAGA
O-21	ALMACENAMIENTO DE LA ESTACIÓN	16.54	ÁREA OPERATIVA
R-02	SERVICIOS ADICIONALES - BAÑO PÚBLICO DE MUJERES	25.57	SERVICIOS ADICIONALES - ÁREA NO PAGA
R-03	SERVICIOS ADICIONALES - BAÑO PÚBLICO DE HOMBRES	25.62	SERVICIOS ADICIONALES - ÁREA NO PAGA
R-04	SERVICIOS ADICIONALES - CONTROL DE ACCESO BAÑOS PÚBLICOS	3.61	SERVICIOS ADICIONALES - ÁREA NO PAGA
R-05-1	SERVICIOS ADICIONALES - CUARTO DE LIMPIEZA	4.19	SERVICIOS ADICIONALES - ÁREA NO PAGA
R-05-2	SERVICIOS ADICIONALES - CUARTO DE LIMPIEZA	2.90	SERVICIOS ADICIONALES - ÁREA NO PAGA
R-06	SERVICIOS ADICIONALES - BAÑOS EMPLEADOS MUJERES	20.67	SERVICIOS ADICIONALES - ÁREA NO PAGA
R-07	SERVICIOS ADICIONALES - VESTIDORES EMPLEADOS MUJERES	11.38	SERVICIOS ADICIONALES - ÁREA NO PAGA
R-08	SERVICIOS ADICIONALES - BAÑOS EMPLEADOS HOMBRES	18.17	SERVICIOS ADICIONALES - ÁREA NO PAGA
R-09	SERVICIOS ADICIONALES - VESTIDORES EMPLEADOS HOMBRES	11.33	SERVICIOS ADICIONALES - ÁREA NO PAGA
R-301	SERVICIOS ADICIONALES - MÁQUINAS EXPENDEDORAS/CAJEROS AUTOMÁTICOS	5.28	SERVICIOS ADICIONALES - ÁREA NO PAGA
T-20-G-2	MEDIDORES (GAS)	5.28	ÁREA TÉCNICA
T-20-L-2	MEDIDORES (LUZ)	7.36	ÁREA TÉCNICA
T-20-W-2	MEDIDORES (AGUA)	4.79	ÁREA TÉCNICA
		346.88	
EDIFICIO ASCENDENTE		1482.38	
EDIFICIO DESCENDENTE			
ARQ_PL_00.1_ACCESO			
C-01	ÁREAS DE USO CULTURAL	4.00	ÁREA CULTURAL
NPA-02	ÁREA NO PAGA	178.99	ÁREA NO PAGA
O-21-2	ALMACENAMIENTO DE LA ESTACIÓN	30.23	ÁREA OPERATIVA
R-101	SERVICIOS ADICIONALES - ÁREA DE SERVICIO	20.00	SERVICIOS ADICIONALES - ÁREA NO PAGA
R-102	SERVICIOS ADICIONALES - ÁREA DE SERVICIO	66.56	SERVICIOS ADICIONALES - ÁREA NO PAGA
T-08-2	CENTRO DE TRANSFORMACIÓN ENEL-CODENSA (CT)_CUARTO BAJA TENSIÓN	13.03	ÁREA TÉCNICA
T-08-3	CENTRO DE TRANSFORMACIÓN ENEL-CODENSA (CT)_CUARTO MEDIA TENSIÓN	49.81	ÁREA TÉCNICA
T-21-7	ÁREA DE INSPECCIÓN	24.35	ÁREA TÉCNICA
T-21-8	ÁREA DE INSPECCIÓN	13.09	ÁREA TÉCNICA
T-30	SISTEMA PROTECCIÓN CONTRA INCENDIO ENEL	5.41	ÁREA TÉCNICA
		405.47	
ARQ_PL_00.2_ACCESO			
R-00-2	SERVICIOS ADICIONALES - CORREDOR OPERATIVO	52.30	SERVICIOS ADICIONALES - ÁREA NO PAGA
T-20-G-1	MEDIDORES (GAS)	6.71	ÁREA TÉCNICA
		59.00	
ARQ_PL_00.3_ACCESO			
R-00-3	SERVICIOS ADICIONALES - CORREDOR OPERATIVO	43.83	SERVICIOS ADICIONALES - ÁREA NO PAGA
R-203	SERVICIOS ADICIONALES - ÁREA DE COMIDAS	72.20	SERVICIOS ADICIONALES - ÁREA NO PAGA
R-204	SERVICIOS ADICIONALES - ÁREA DE COMIDAS	70.61	SERVICIOS ADICIONALES - ÁREA NO PAGA
T-20-L-2	MEDIDORES (LUZ)	8.77	ÁREA TÉCNICA
T-20-W-2	MEDIDORES (AGUA)	3.66	ÁREA TÉCNICA
T-21-5	ÁREA DE INSPECCIÓN	11.82	ÁREA TÉCNICA
T-21-6	ÁREA DE INSPECCIÓN	21.39	ÁREA TÉCNICA
T-25-2	NODO DE ACCESO DE TELECOMUNICACIONES	3.28	ÁREA TÉCNICA
		235.57	
ARQ_PL_00.4_ACCESO			
C-02	ÁREAS DE USO CULTURAL	7.18	ÁREA CULTURAL
C-03	ÁREAS DE USO CULTURAL	8.63	ÁREA CULTURAL
NPA-03	ÁREA NO PAGA	381.84	ÁREA NO PAGA
O-21-3	ALMACENAMIENTO DE LA ESTACIÓN	24.92	ÁREA OPERATIVA
R-302	SERVICIOS ADICIONALES - MÁQUINAS EXPENDEDORAS/CAJEROS AUTOMÁTICOS	9.75	SERVICIOS ADICIONALES - ÁREA NO PAGA
R-303	SERVICIOS ADICIONALES - MÁQUINAS EXPENDEDORAS/CAJEROS AUTOMÁTICOS	7.84	SERVICIOS ADICIONALES - ÁREA NO PAGA
T-25-3	NODO DE ACCESO DE TELECOMUNICACIONES	3.81	ÁREA TÉCNICA
		443.96	
ARQ_PL_00.5_ACCESO			
R-00-1	SERVICIOS ADICIONALES - CORREDOR OPERATIVO	40.07	SERVICIOS ADICIONALES - ÁREA NO PAGA
R-02	SERVICIOS ADICIONALES - BAÑO PÚBLICO DE MUJERES	18.40	SERVICIOS ADICIONALES - ÁREA NO PAGA
R-03	SERVICIOS ADICIONALES - BAÑO PÚBLICO DE HOMBRES	17.10	SERVICIOS ADICIONALES - ÁREA NO PAGA
R-04	SERVICIOS ADICIONALES - CONTROL DE ACCESO BAÑOS PÚBLICOS	4.70	SERVICIOS ADICIONALES - ÁREA NO PAGA
R-05-1	SERVICIOS ADICIONALES - CUARTO DE LIMPIEZA	3.47	SERVICIOS ADICIONALES - ÁREA NO PAGA
R-09	SERVICIOS ADICIONALES - VESTIDORES EMPLEADOS HOMBRES	8.63	SERVICIOS ADICIONALES - ÁREA NO PAGA
		92.37	
ARQ_PL_00.6_ACCESO			
R-01	SERVICIOS ADICIONALES - CUARTO DE BASURAS PARA METRO	9.80	SERVICIOS ADICIONALES - ÁREA NO PAGA
R-05-2	SERVICIOS ADICIONALES - CUARTO DE LIMPIEZA	8.97	SERVICIOS ADICIONALES - ÁREA NO PAGA
R-06	SERVICIOS ADICIONALES - BAÑOS EMPLEADOS MUJERES	20.71	SERVICIOS ADICIONALES - ÁREA NO PAGA
R-07	SERVICIOS ADICIONALES - VESTIDORES EMPLEADOS MUJERES	8.47	SERVICIOS ADICIONALES - ÁREA NO PAGA
R-08	SERVICIOS ADICIONALES - BAÑOS EMPLEADOS HOMBRES	20.33	SERVICIOS ADICIONALES - ÁREA NO PAGA
R-10	SERVICIOS ADICIONALES - SALA DE EMPLEADOS	13.64	SERVICIOS ADICIONALES - ÁREA NO PAGA
R-201	SERVICIOS ADICIONALES - ÁREA DE COMIDAS	63.70	SERVICIOS ADICIONALES - ÁREA NO PAGA
R-202	SERVICIOS ADICIONALES - ÁREA DE COMIDAS	54.44	SERVICIOS ADICIONALES - ÁREA NO PAGA
TM-1	ÁREA DE TAQUILLAS BRT	21.32	ÁREA DE TAQUILLAS BRT
		221.37	
ARQ_PL_00.7_ACCESO			
R-103	SERVICIOS ADICIONALES - ÁREA DE SERVICIO	150.77	SERVICIOS ADICIONALES - ÁREA NO PAGA
		150.77	
ARQ_PL_00.9_ACCESO			
R-104	SERVICIOS ADICIONALES - ÁREA DE SERVICIO	144.45	SERVICIOS ADICIONALES - ÁREA NO PAGA
T-20-G-2	MEDIDORES (GAS)	4.61	ÁREA TÉCNICA
T-20-L-3	MEDIDORES (LUZ)	7.00	ÁREA TÉCNICA
T-20-W-3	MEDIDORES (AGUA)	4.62	ÁREA TÉCNICA
T-21-9	ÁREA DE INSPECCIÓN	13.73	ÁREA TÉCNICA
		174.42	
ARQ_PL_01_ACCESO			
O-21-4	ALMACENAMIENTO DE LA ESTACIÓN	17.73	ÁREA OPERATIVA
SER 2_A	ACCESO SER 2	77.18	ÁREA TÉCNICA
		94.91	
EDIFICIO DESCENDENTE		1877.84	
TOTAL NIVEL ACCESO		3360.22	

TABLA DE ÁREAS ÚTILES POR DEPARTAMENTO (NIVEL ACCESO)

DEPARTAMENTO	ÁREA (m²)
SERVICIOS ADICIONALES - ÁREA NO PAGA	1802.00
ÁREA CULTURAL	19.80
ÁREA DE TAQUILLAS BRT	46.76
ÁREA NO PAGA	852.78
ÁREA OPERATIVA	89.42
ÁREA TÉCNICA	549.45
TOTAL NIVEL ACCESO	3360.22

VÁLIDO PARA CONSTRUCCIÓN
20-03-26

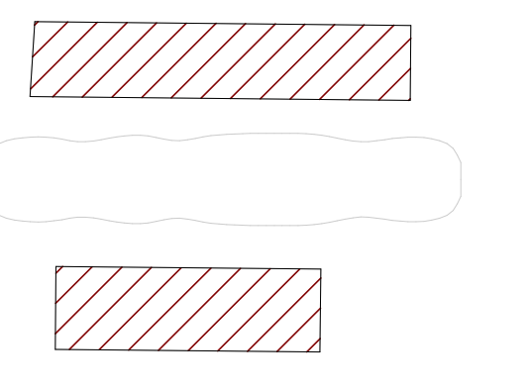

PLANO CLAVE ESTACIÓN 11

LOCALIZACIÓN

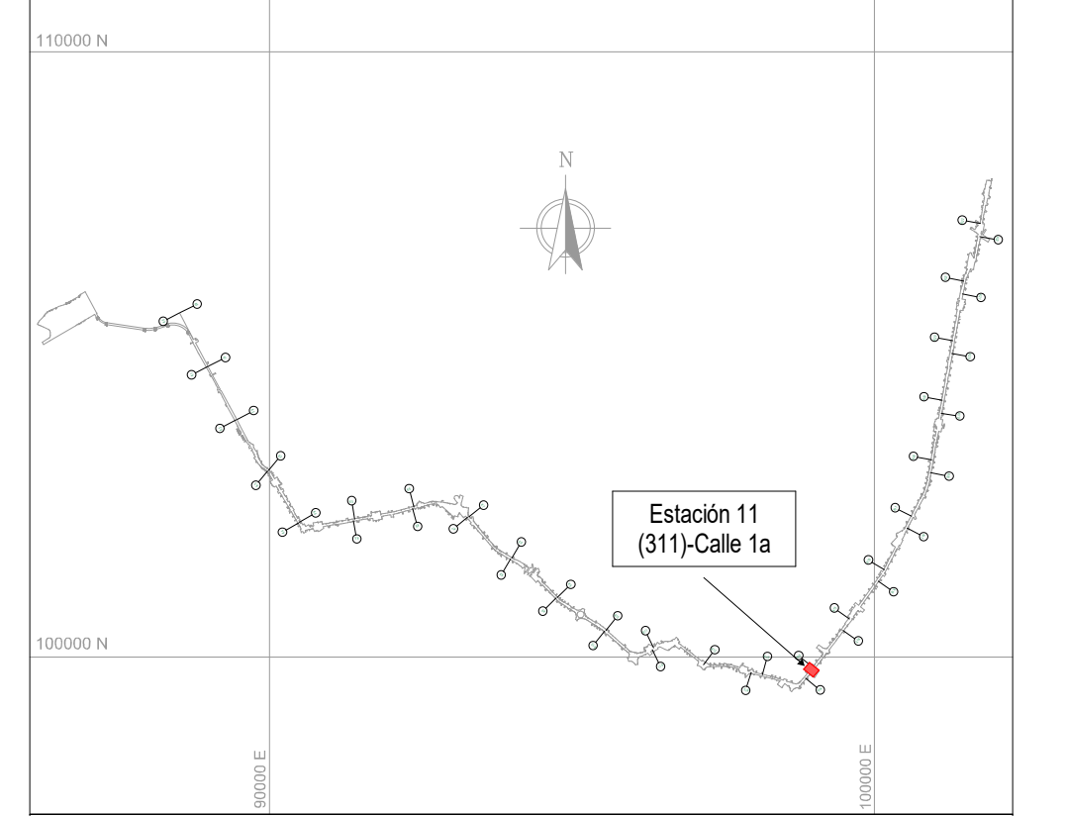

NOTAS

01. TODAS LAS DIMENSIONES ESTÁN CONFIGURADAS EN METROS A MENOS QUE SE INDIQUE UNA UNIDAD DE MEDIDA DIFERENTE.
02. TODAS LAS MEDIDAS, UBICACIÓN Y NIVELES DEBEN VERIFICARSE EN EL LUGAR DE CONSTRUCCIÓN.
03. EL NIVEL DE ACCESO AL EDIFICIO PL 01 CORRESPONDE AL +0,00 DE LA ESTACIÓN Y REFERENCIA AL NIVEL 2575.40 M.S.N.M.
04. LOS NOMBRES ESPECÍFICOS DE LAS ÁREAS PUEDEN SER CONSULTADAS EN EL PLANO NO. 3 Ó EN LAS VISTAS EN PLANTA.
05. LOS COLORES QUE SE MUESTRAN EN LOS PLANOS COMO PROYECCIÓN DE ELEMENTOS ARQUITECTÓNICOS COMO CUBIERTAS, FACHADAS, MUROS, ETC. NO REPRESENTAN LA MATERIALIDAD Y REALIDAD DE ACABADOS DEL PROYECTO, SOLO SON INDICATIVOS PARA REALIZAR UNA CORRECTA LECTURA DE LA PLANIMETRÍA.
06. LAS ESCALERAS ELÉCTRICAS INDICAN SU SENTIDO CON LA SIGUIENTE NOMENCLATURA: "SUBE" Y "BAJA".
07. SE DEBEN REVISAR LOS NIVELES ESTRUCTURALES PARA NIVEL DE ACCESO PL_01 Y SUBNIVELES, PL_02 (INTERMEDIO), PL_03 (PLATAFORMA) CON LA PLANIMETRÍA DE PLACAS ESTRUCTURALES EN LOS ENTREGABLES L1T1-1300-411-CON-ED-EST-PL-0070, 71, 72, 73, 99, 100, 101, 102, 103, 104, 105, 125, 126, RESPECTIVAMENTE. EL NIVEL ESTRUCTURAL (NE) REFERENCIA LOS ESPACIOS DONDE SE DEBE ACONDICIONAR EL ACABADO DE PISO SEGÚN CORRESPONDA, CON LOS NIVELES DE PISO TERMINADO (NPT). LOS NIVELES PROYECTADOS DE EMPATE (NPE) EN LAS ÁREAS DE SERVICIOS ADICIONALES, REFERENCIAN LA ADECUACIÓN DE LOS DESNIVELES EN ESTAS ÁREAS; QUEDA COMO RESPONSABILIDAD DEL LOCATARIO DEFINIR Y ACONDICIONAR ESTE ACABADO DE PISO (NPE) EN LÍNEA CON EL NIVEL (NPT) DE ESPACIOS COLINDANTES. EL NIVEL ESTRUCTURAL (NE) SE ENCUENTRA A (- 0.10M) POR DEBAJO DE LOS NIVELES DE PISO TERMINADO (NPT) Y LOS NIVELES PROYECTADOS DE EMPATE (NPE) MARCADOS EN LA PLANIMETRÍA.

- ARQ_PL_-00.1 = SER-2	/ NPT -12.00	- ARQ_PL_00.8 = ACCESO	/ NPT -0.20
- ARQ_PL_00 = SÓTANO	/ NPT -7.70	- ARQ_PL_00.9 = ACCESO	/ NPT -0.10
- ARQ_PL_00.1 = ACCESO	/ NPT -1.40	- ARQ_PL_01 = ACCESO	/ NPT 0.00
- ARQ_PL_00.2 = ACCESO	/ NPT -1.25	- ARQ_PL_02 = INTERMEDIO	/ NPT 6.60
- ARQ_PL_00.3 = ACCESO	/ NPT -0.90	- ARQ_PL_02.2 = TOPE DE RIEL (TOR)	/ NPT 14.20
- ARQ_PL_00.4 = ACCESO	/ NPT -0.80	- ARQ_PL_03 = PLATAFORMA	/ NPT 15.34
- ARQ_PL_00.5 = ACCESO	/ NPT -0.65	- ARQ_PL_04 = CUBIERTA EDIFICACIONES	/ NPT 21.94
- ARQ_PL_00.6 = ACCESO	/ NPT -0.40	- ARQ_PL_05 = CUBIERTA NAVE CENTRAL	/ NPT 24.60
- ARQ_PL_00.7 = ACCESO	/ NPT -0.25		

CONVENCIONES

- - - -	LÍMITE DE NIVEL ARQUITECTÓNICO
- - - -	HUELLA APÉNDICE TÉCNICO
▬	MURO DIVISORIO
— — —	PROYECCIÓN NIVEL SUPERIOR

🟩	SERVICIOS ADICIONALES - ÁREA NO PAGA	🟨	ÁREA NO PAGA
🟩	SERVICIOS ADICIONALES - ÁREA PAGA	🟦	ÁREA OPERATIVA
🟩	SERVICIO PÚBLICO	🟨	ÁREA PAGA
🟦	ZONA DE REFUGIO	🟦	ÁREA PÚBLICA
🟥	ÁREA CULTURAL	⬜	ÁREA TÉCNICA
🟪	ÁREA DE TAQUILLAS BRT	🟧	ÁREA BRT

No.	PLANOS DE REFERENCIA	REV.

No.	MODELO BIM DE REFERENCIA	REV.
1	L1T1-1100-211-CON-ED-EST-MO-0001.rvt	V00
2	L1T1-1100-212-CON-ED-EST-MO-0001.rvt	V00
3	L1T1-1100-311-CON-ED-EST-MO-0001.rvt	V00
4	L1T1-1150-211-CON-ED-EST-MO-0001.rvt	V00
5	L1T1-1150-212-CON-ED-EST-MO-0001.rvt	V00
6	L1T1-1150-311-CON-ED-EST-MO-0001.rvt	V00
7	L1T1-1200-311-CON-ED-EST-MO-0001.rvt	V00
8	L1T1-1300-411-CON-ED-EST-MO-0001.rvt	V00
9	L1T1-1300-411-CON-ED-EST-MO-0002.rvt	V00
10	L1T1-1310-411-CON-ED-EST-MO-0001.rvt	V00
11	L1T1-1410-311-CON-ED-MEC-MO-0001.rvt	V00
12	L1T1-1420-311-CON-ED-MEC-MO-0001.rvt	V00
13	L1T1-2320-582-CON-ED-EST-MO-0001.rvt	V00
14	L1T1-2330-582-CON-ED-ARQ-MO-0001.rvt	V00
15	L1T1-5110-571-CON-ED-EST-MO-0001.rvt	V00
16	L1T1-5160-311-CON-ED-EST-MO-0001.rvt	V00
17	L1T1-5160-311-CON-ED-ARQ-MO-0001.rvt	V00
18	L1T1-5300-311-CON-ED-MEC-MO-0001.rvt	V00
19	L1T1-5600-311-CON-ED-INS-MO-0001.rvt	V00
20	L1T1-1330-411-CON-ED-ARQ-MO-0011.rvt	V00
21	L1T1-1330-411-CON-ED-ARQ-MO-0012.rvt	V00

No.	PAQUETE DE TRABAJO DE REFERENCIA	REV.
1	XREF-URBANISM_CONTEXT_ST11.rvt	
2	XREF-SECONDARY-STRUCTURE-ST11.rvt	

0 2 10m
1:200

METRO BOGOTÁ
GCS Consorcio Consultores PMO Bogotá
CONSORCIO SUPERVISOR PLMB
HEC

DISEÑÓ:
REN ZHENHUA
Licencia de Arq.nivel I (China): 1101735-614

APROBÓ:
DIEGO ERNESTO DUEÑAS
Mat.: 25202-53876 CND

REVISÓ:
CARLOS MAURICIO BARRETO BARBOSA
Mat.: A4012012-14139353

DIBUJÓ:
EQUIPO CHEC

REVISIÓN No.	FECHA	DESCRIPCIÓN	REVISÓ	APROBÓ	APROBACIÓN CLIENTE
V01	20/03/2026	EMITIDO PARA CONSTRUCCIÓN	C.M.B.B	D.E.D	
V00	31/03/2025	REVISIÓN NO OBJETADA - EMITIDO PARA CONSTRUCCIÓN	F.B.R	E.O.M	
VII	22/07/2024	EMITIDO PARA REVISIÓN Y COMENTARIOS DEL CLIENTE E INTERVENTORÍA - INCLUYE COMENTARIOS /(AJUSTES V4)	F.B.R	E.O.M	
VHH	26/04/2024	EMITIDO PARA REVISIÓN Y COMENTARIOS DEL CLIENTE E INTERVENTORÍA - INCLUYE COMENTARIOS /(AJUSTES V3)	F.B.R	E.O.M	
VGG	30/10/2023	EMITIDO PARA REVISIÓN Y COMENTARIOS DEL CLIENTE E INTERVENTORÍA - INCLUYE COMENTARIOS /(AJUSTES V2)	J.E.M	M.B.M	
VFF	20/04/2023	EMITIDO PARA REVISIÓN Y COMENTARIOS DEL CLIENTE E INTERVENTORÍA - INCLUYE COMENTARIOS /(AJUSTES)	J.E.M	M.B.M	
VEE	18/12/2022	EMITIDO PARA REVISIÓN Y COMENTARIOS DEL CLIENTE E INTERVENTORÍA - INCLUYE COMENTARIOS /(NO APLICA)	J.E.M	M.B.M	
VDD	11/11/2022	EMITIDO PARA REVISIÓN Y COMENTARIOS DEL CLIENTE E INTERVENTORÍA - INCLUYE COMENTARIOS /(90% ACCESOS)	J.E.M	M.B.M	
VCC	22/08/2022	EMITIDO PARA REVISIÓN Y COMENTARIOS DEL CLIENTE E INTERVENTORÍA - INCLUYE COMENTARIOS /(NO APLICA)	J.E.M	M.B.M	
VBB	06/12/2021	EMITIDO PARA REVISIÓN Y COMENTARIOS DEL CLIENTE E INTERVENTORÍA	J.E.M	M.B.M	

METRO LÍNEA 1

METRO LÍNEA 1
CONTRATO DE CONCESIÓN No. 163 DE 2019

PROYECTO PRIMERA LÍNEA DEL METRO DE BOGOTÁ - TRAMO 1

DIRECTOR DE INTERVENTORÍA:
JAVIER DESCARGA N.
Mat.:25202-68697 CND

ESPECIALISTA INTERVENTORÍA:
CARLOS ALBERTO HOYOS SOTO
Mat.:A25072000-14251682

FECHA: MARZO 2026

INFRAESTRUCTURA VIAL

ARQUITECTURA

ESTACIÓN METRO 11 (CALLE 1)
GENERAL
VISTA EN PLANTA Y 3D - NIVEL ACCESO

PLANCHA No: L1T1-0000-311-CON-ED-ARQ-PL-0001_05_V01
ARCHIVO: L1T1-0000-311-CON-ED-ARQ-MO-0001_V00.rvt
ESCALA: INDICADA
FECHA: DICIEMBRE 2021
REVISIÓN No.: V01
PLANO No.: 05 DE 97