L1T1-CON-CAL-FR-0120 - B1 : 1000x707mm

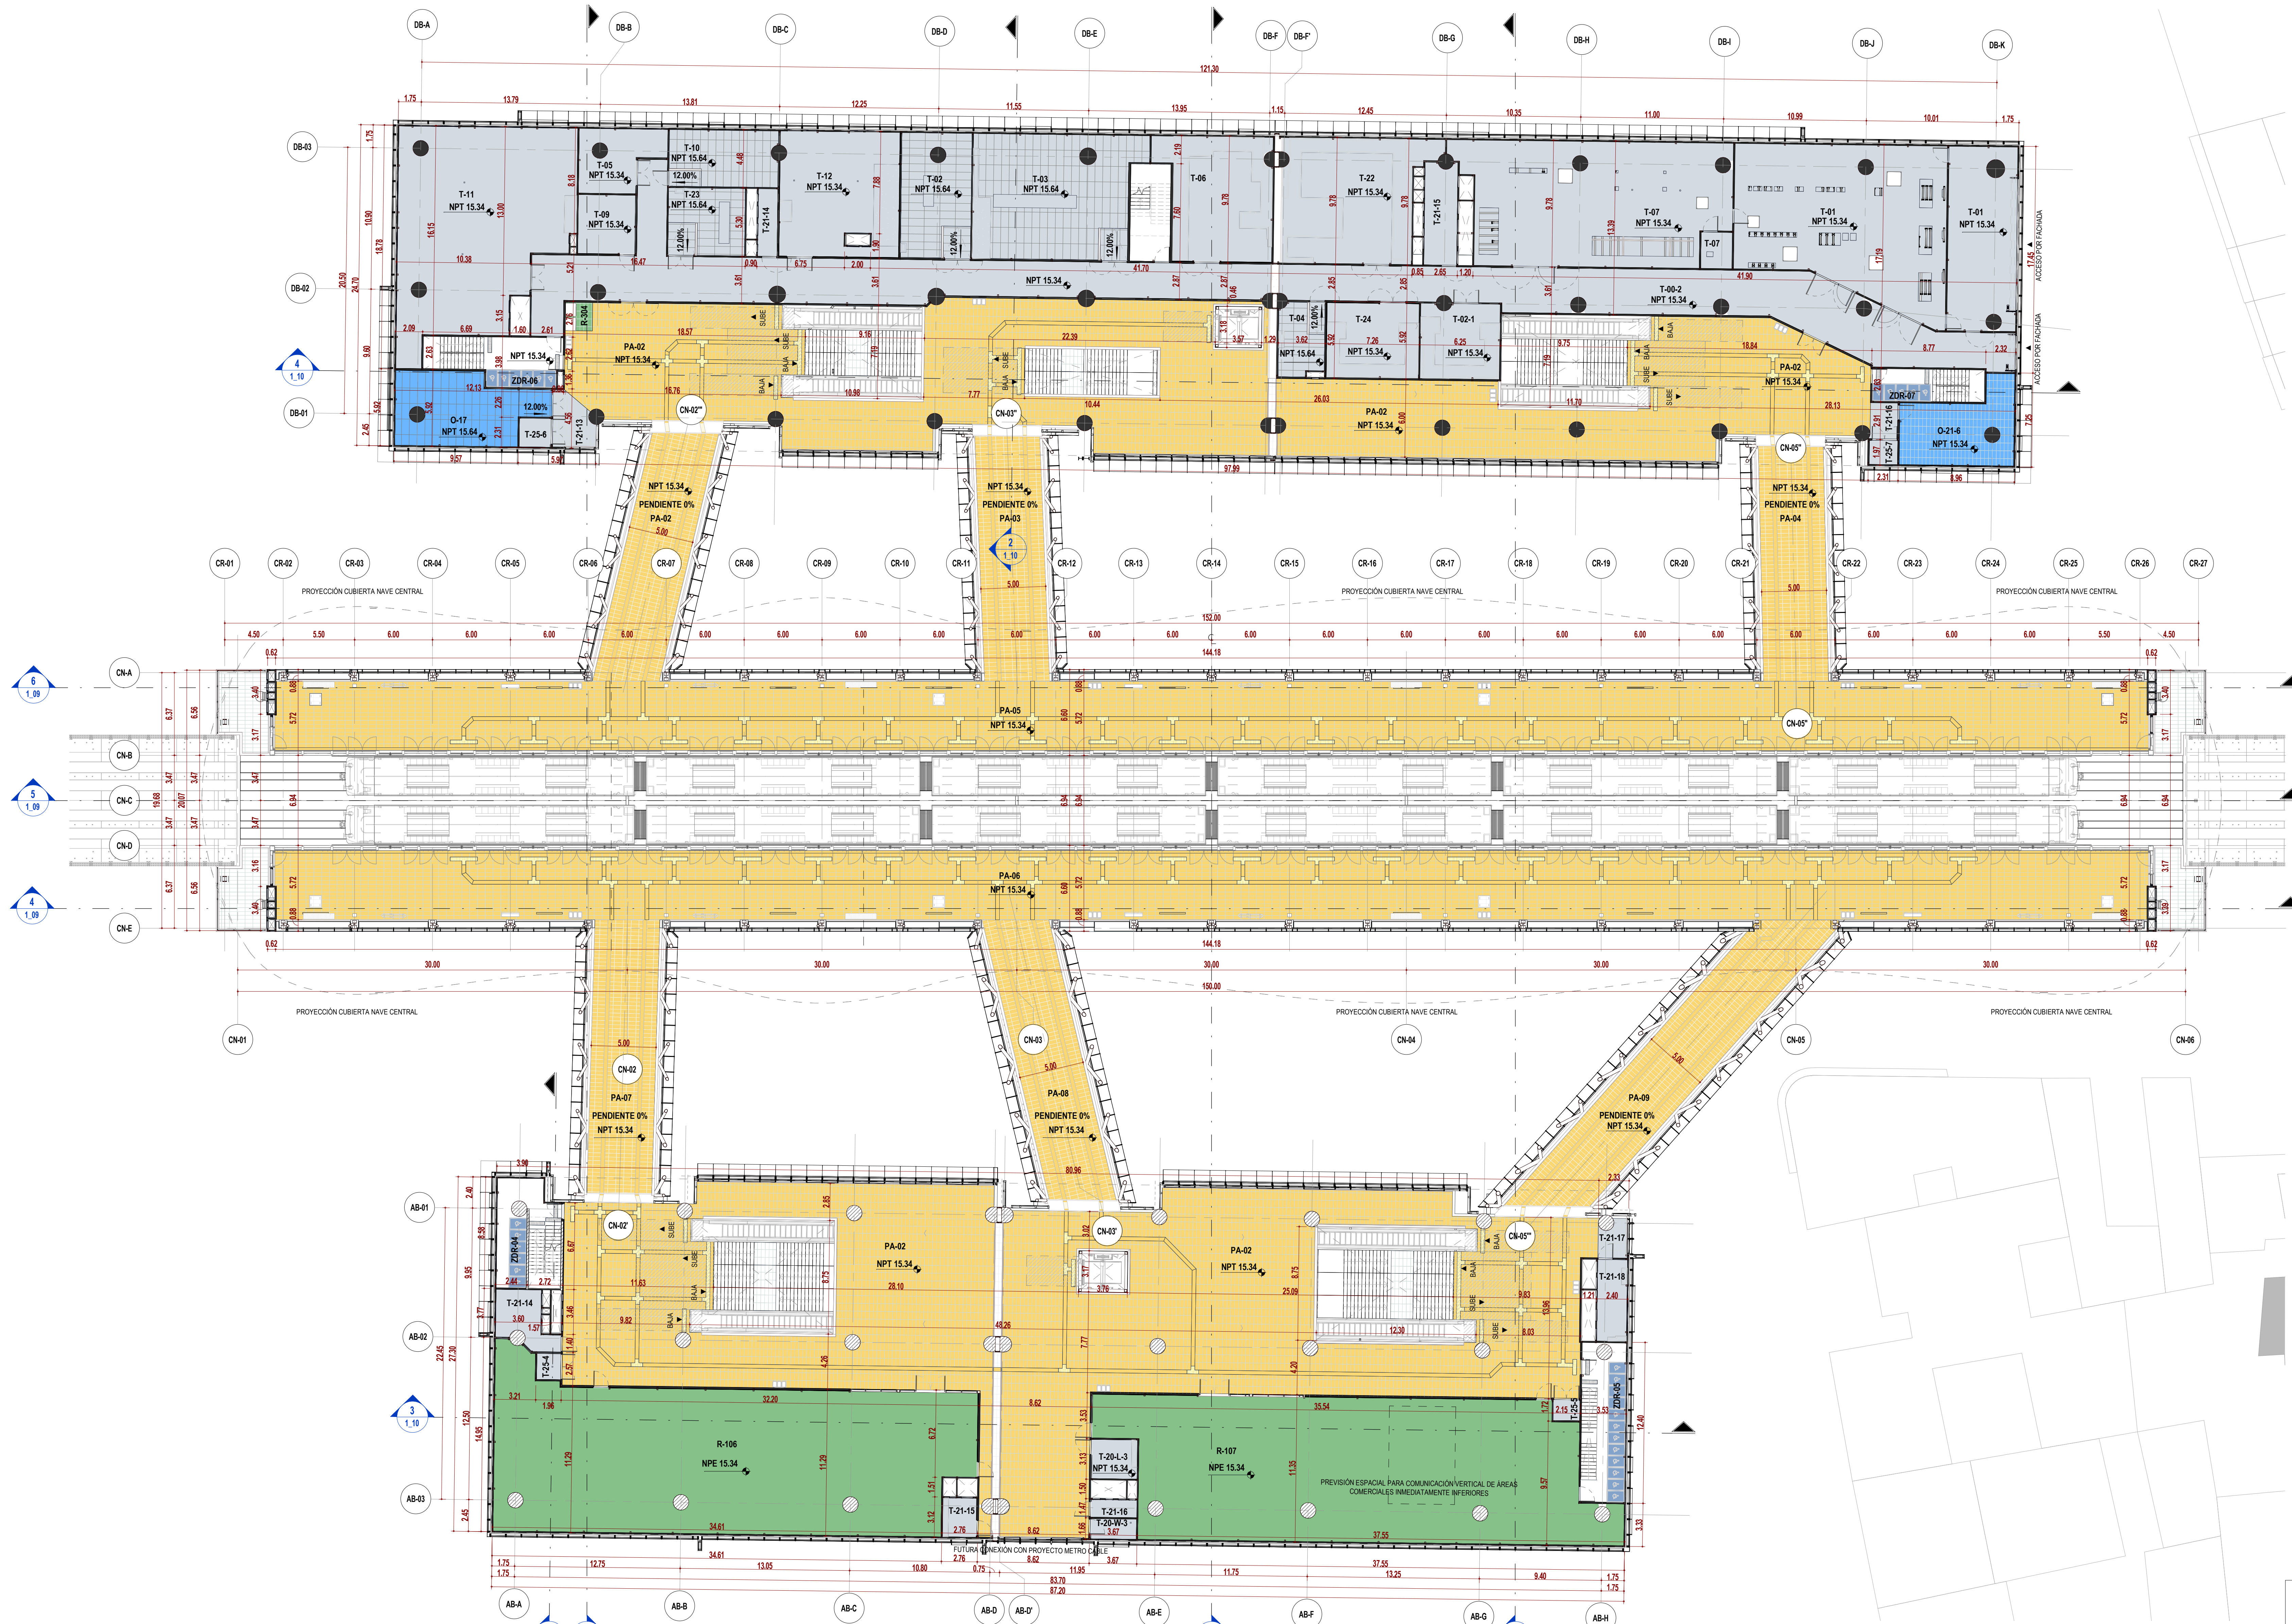
PA-02
NPT 15.34
PA-03
PA-04
PA-05
PA-06
PA-07
PA-08
PA-09
PENDIENTE 0%
R-106
NPE 15.34
R-107
PROYECCIÓN CUBIERTA NAVE CENTRAL
PROYECCIÓN ESPACIAL PARA COMUNICACIÓN VERTICAL DE ÁREAS COMERCIALES (MANTENIMIENTO MAYOR)

2 **NIVEL PLATAFORMA_GENERAL**
ESC: 1 : 200

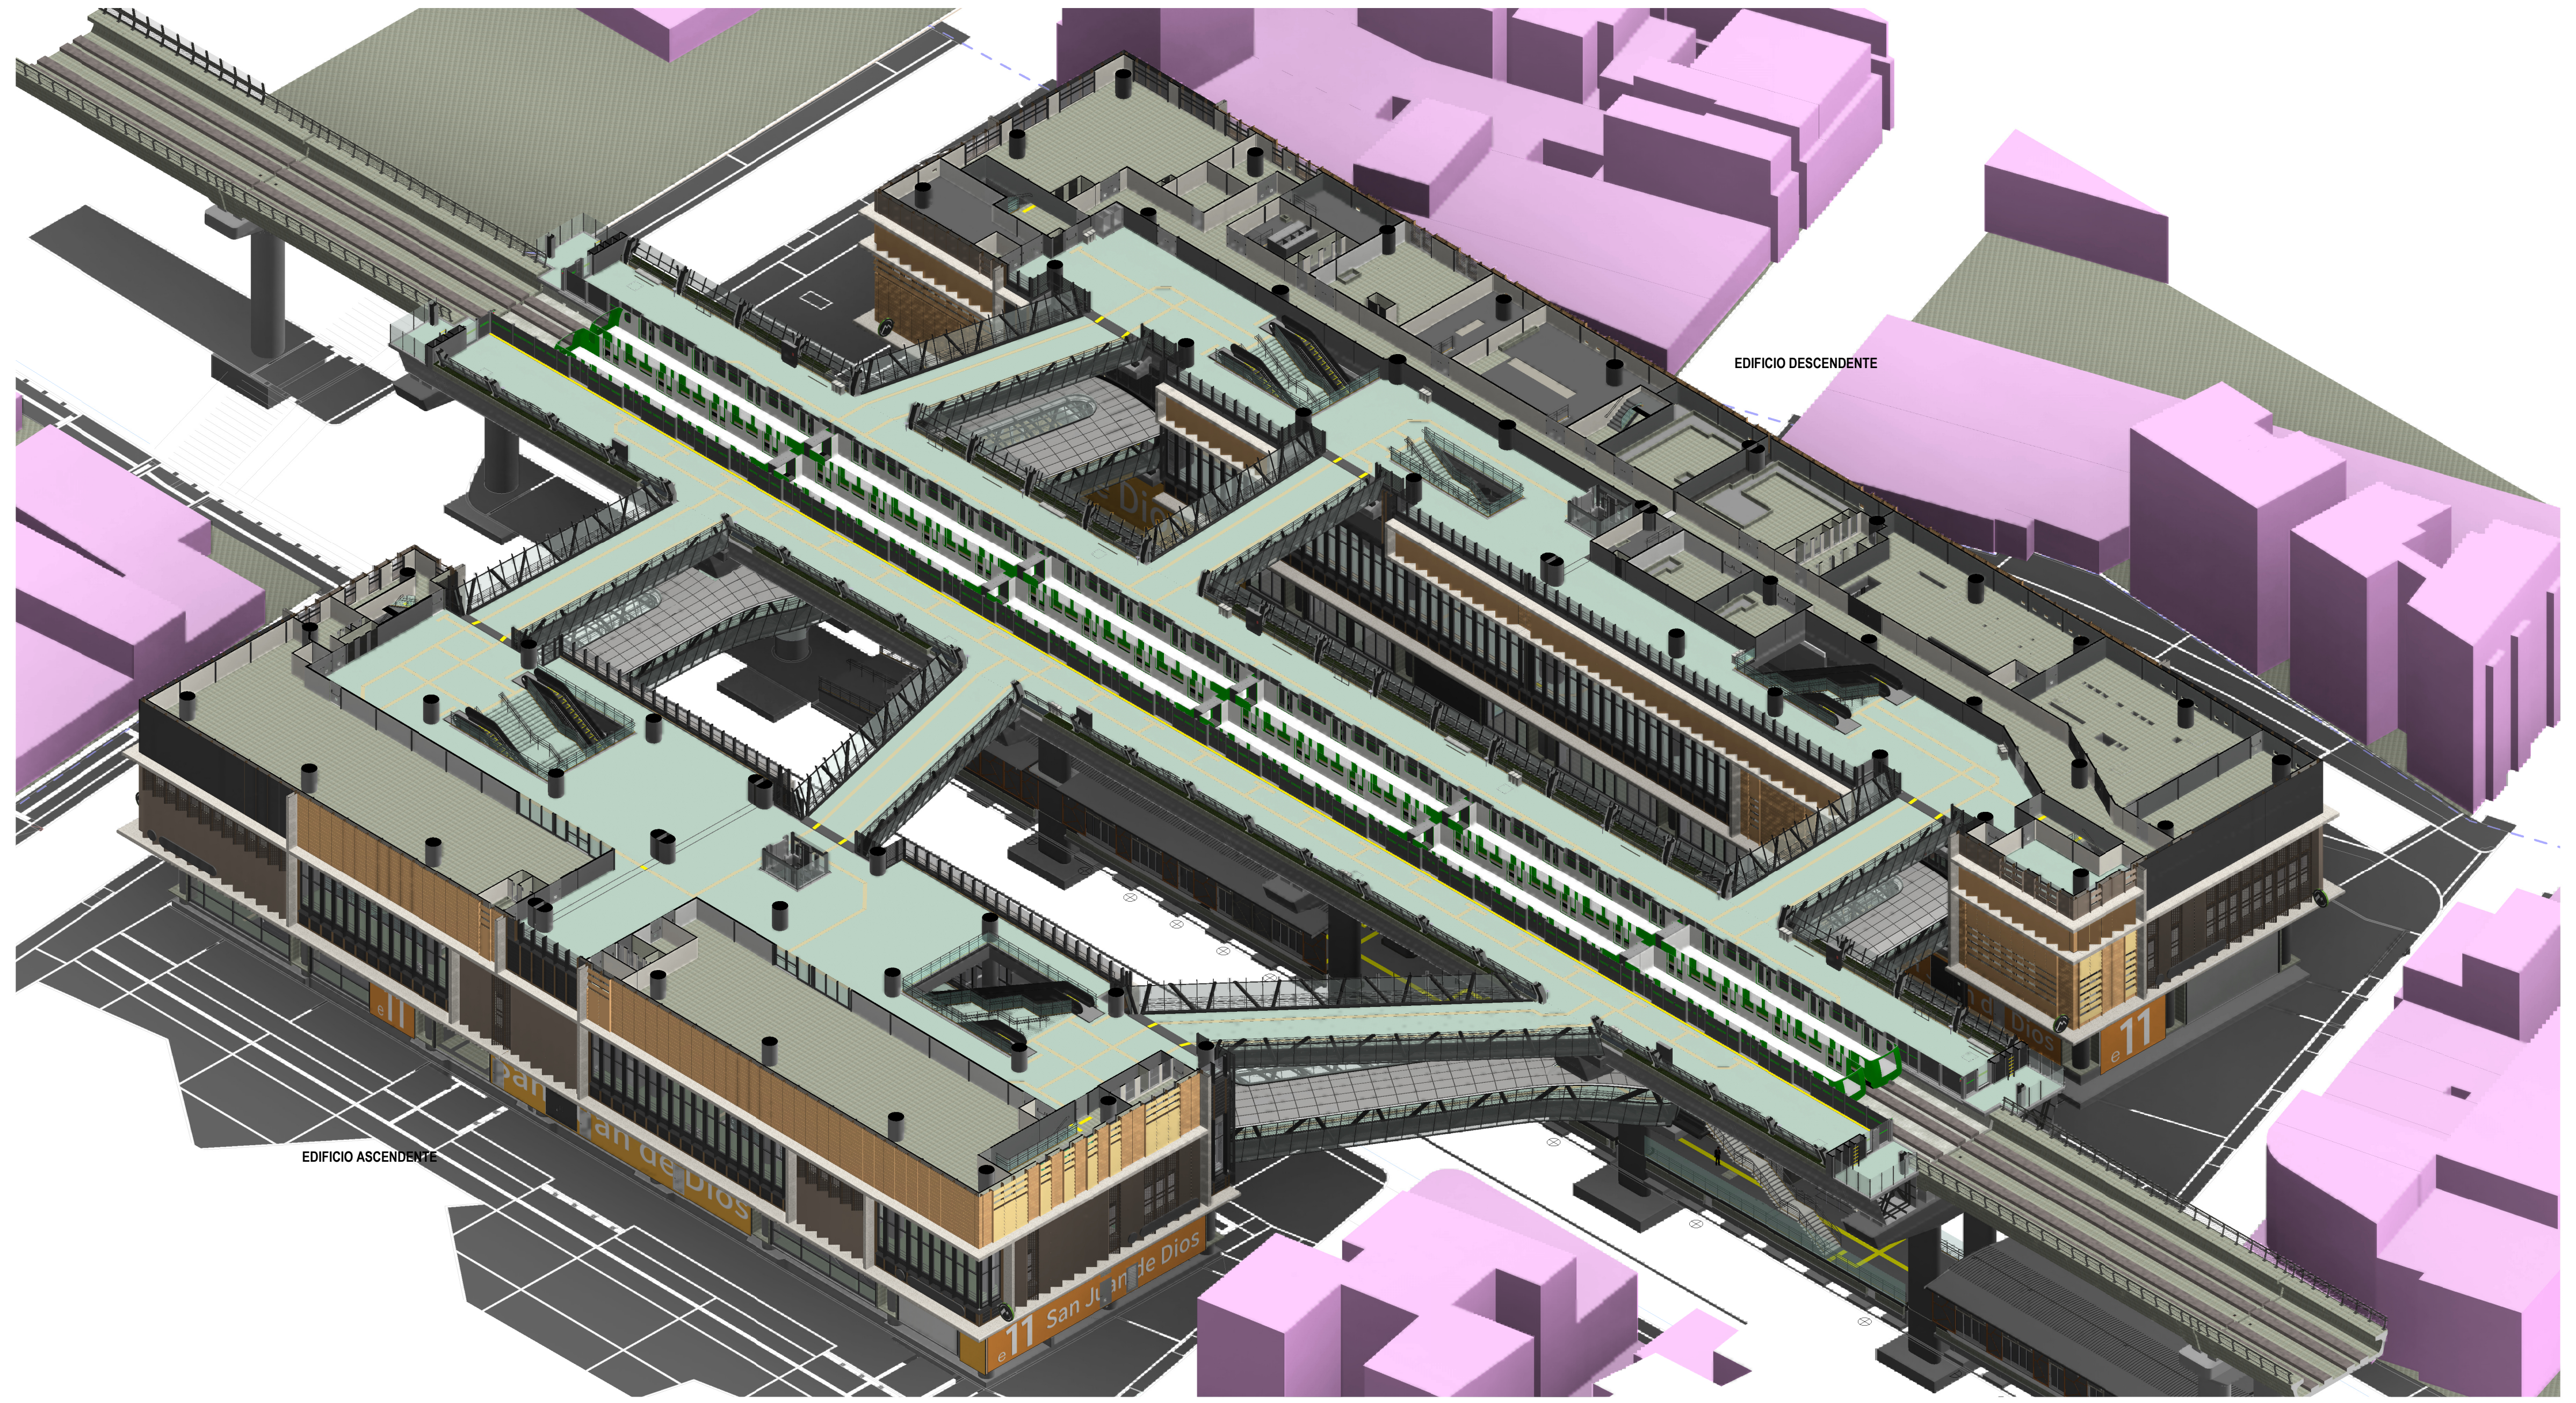

1 **3D_NIVEL PLATAFORMA_GENERAL**
ESC: N/A

TABLA DE ÁREAS ÚTILES (NIVEL PLATAFORMA)

CÓDIGO	NOMBRE	ÁREA (m²)	DEPARTAMENTO
EDIFICIO ASCENDENTE			
ARQ_PL_03_PLATAFORMA			
R-106	SERVICIOS ADICIONALES - ÁREA DE SERVICIO	408.72	SERVICIOS ADICIONALES - ÁREA PAGA
T-21-16	ÁREA DE INSPECCIÓN	4.76	ÁREA TÉCNICA
T-21-14	ÁREA DE INSPECCIÓN	15.48	ÁREA TÉCNICA
T-21-18	ÁREA DE INSPECCIÓN	14.40	ÁREA TÉCNICA
ZDR-05	ZONA DE REFUGIO (PMR)	14.58	ZONA DE REFUGIO
ZDR-04	ZONA DE REFUGIO (PMR)	7.29	ZONA DE REFUGIO
T-20-W-3	MEDIDORES (AGUA)	5.44	ÁREA TÉCNICA
T-20-L-3	MEDIDORES (LUZ)	10.56	ÁREA TÉCNICA
PA-02	ÁREA PAGA	1072.83	ÁREA PAGA
R-107	SERVICIOS ADICIONALES - ÁREA DE SERVICIO	392.30	SERVICIOS ADICIONALES - ÁREA PAGA
T-21-15	ÁREA DE INSPECCIÓN	7.81	ÁREA TÉCNICA
T-25-4	NODO DE ACCESO DE TELECOMUNICACIONES	3.68	ÁREA TÉCNICA
T-25-5	NODO DE ACCESO DE TELECOMUNICACIONES	3.18	ÁREA TÉCNICA
T-21-17	ÁREA DE INSPECCIÓN	5.76	ÁREA TÉCNICA
EDIFICIO ASCENDENTE		1966.78	
EDIFICIO DESCENDENTE			
ARQ_PL_03_PLATAFORMA			
PA-02	ÁREA PAGA	749.16	ÁREA PAGA
T-07	CENTRO DE TRANSFORMACIÓN (CT)	193.94	ÁREA TÉCNICA
T-12	PLANTA DE REFRIGERACIÓN PARA LA CLIMATIZACIÓN	85.93	ÁREA TÉCNICA
T-02	LOCAL DE CONDUCCIÓN AUTOMÁTICA (CBTC)	51.11	ÁREA TÉCNICA
T-03	TELECOMUNICACIONES ESTACIÓN - CORRIENTE DÉBIL	118.16	ÁREA TÉCNICA
T-11	CUARTO DE VENTILACIÓN	195.38	ÁREA TÉCNICA
T-04	EQUIPO BOLETERÍA	19.50	ÁREA TÉCNICA
O-21-6	ALMACENAMIENTO DE LA ESTACIÓN	46.36	ÁREA OPERATIVA
T-01	SUBESTACIÓN DE TRACCIÓN (SET)	256.58	ÁREA TÉCNICA
T-21-15	ÁREA DE INSPECCIÓN	19.62	ÁREA TÉCNICA
T-00-2	CIRCULACIÓN TÉCNICA	387.43	ÁREA TÉCNICA
T-21-14	ÁREA DE INSPECCIÓN	7.73	ÁREA TÉCNICA
ZDR-07	ZONA DE REFUGIO (PMR)	6.07	ZONA DE REFUGIO
O-17	OPERADORES TELECOMUNICACIONES EXTERIORES	55.30	ÁREA OPERATIVA
ZDR-06	ZONA DE REFUGIO (PMR)	7.29	ZONA DE REFUGIO

TABLA DE ÁREAS ÚTILES (NIVEL PLATAFORMA)

CÓDIGO	NOMBRE	ÁREA (m²)	DEPARTAMENTO
T-10	CUARTO DE EQUIPO ELECTROMECÁNICO	36.13	ÁREA TÉCNICA
T-05	ALMACÉN PARA MANTENIMIENTO	26.12	ÁREA TÉCNICA
T-09	ALMACÉN EQUIPO ELÉCTRICO	19.93	ÁREA TÉCNICA
T-23	CUARTO PDAP	30.70	ÁREA TÉCNICA
R-304	SERVICIOS ADICIONALES - MÁQUINAS EXPENDEDORAS/CAJEROS AUTOMÁTICOS	4.62	SERVICIOS ADICIONALES - ÁREA PAGA
T-25-6	NODO DE ACCESO DE TELECOMUNICACIONES	5.28	ÁREA TÉCNICA
T-25-7	NODO DE ACCESO DE TELECOMUNICACIONES	4.02	ÁREA TÉCNICA
T-06	SALA DE TABLEROS	76.47	ÁREA TÉCNICA
T-22	CUARTO DE UPS	105.51	ÁREA TÉCNICA
T-02-1	UPS DEDICADA (CBTC)	34.86	ÁREA TÉCNICA
T-24	TETRA UPS	40.71	ÁREA TÉCNICA
T-21-13	ÁREA DE INSPECCIÓN	11.74	ÁREA TÉCNICA
T-21-16	ÁREA DE INSPECCIÓN	5.93	ÁREA TÉCNICA
EDIFICIO DESCENDENTE		2601.59	
NAVE CENTRAL			
ARQ_PL_03_PLATAFORMA			
PA-05	ÁREA PAGA	769.76	ÁREA PAGA
PA-02	ÁREA PAGA	98.79	ÁREA PAGA
PA-03	ÁREA PAGA	95.09	ÁREA PAGA
PA-04	ÁREA PAGA	91.10	ÁREA PAGA
PA-06	ÁREA PAGA	769.76	ÁREA PAGA
PA-09	ÁREA PAGA	148.55	ÁREA PAGA
PA-08	ÁREA PAGA	111.93	ÁREA PAGA
PA-07	ÁREA PAGA	106.33	ÁREA PAGA
NAVE CENTRAL		2191.29	
TOTAL NIVEL PLATAFORMA		6759.66	

TABLA DE ÁREAS ÚTILES POR DEPARTAMENTO (NIVEL PLATAFORMA)

DEPARTAMENTO	ÁREA (m²)
SERVICIOS ADICIONALES - ÁREA PAGA	805.64
ZONA DE REFUGIO	35.23
ÁREA OPERATIVA	101.66
ÁREA PAGA	4013.29
ÁREA TÉCNICA	1803.84
TOTAL NIVEL PLATAFORMA	6759.66

LOCALIZACIÓN

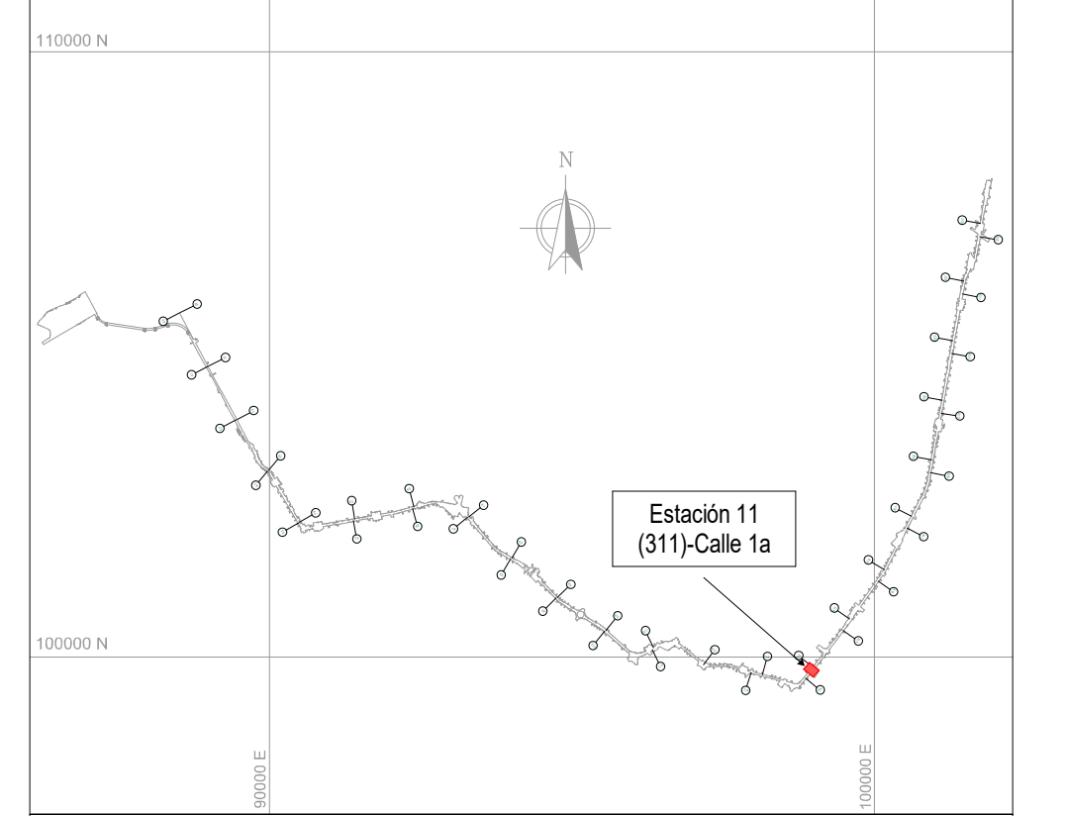

NOTAS

01 TODAS LAS DIMENSIONES ESTÁN CONFIGURADAS EN METROS A MENOS QUE SE INDIQUE UNA UNIDAD DE MEDIDA DIFERENTE.

02 TODAS LAS MEDIDAS, UBICACIÓN Y NIVELES DEBEN VERIFICARSE EN EL LUGAR DE CONSTRUCCIÓN.

03 EL NIVEL DE ACCESO AL EDIFICIO PL 01 CORRESPONDE AL +0,00 DE LA ESTACIÓN Y REFERENCIA AL NIVEL 2575.40 M.S.N.M.

04 LOS NOMBRES ESPECÍFICOS DE LAS ÁREAS PUEDEN SER CONSULTADAS EN EL PLANO NO. 3 Ó EN LAS VISTAS EN PLANTA.

05 LOS COLORES QUE SE MUESTRAN EN LOS PLANOS COMO PROYECCIÓN DE ELEMENTOS ARQUITECTÓNICOS COMO CUBIERTAS, FACHADAS, MUROS, ETC. NO REPRESENTAN LA MATERIALIDAD Y REALIDAD DE ACABADOS DEL PROYECTO, SOLO SON INDICATIVOS PARA REALIZAR UNA CORRECTA LECTURA DE LA PLANIMETRÍA.

06 LAS ESCALERAS ELÉCTRICAS INDICAN SU SENTIDO CON LA SIGUIENTE NOMENCLATURA: "SUBE" Y "BAJA".

07 SE DEBEN REVISAR LOS NIVELES ESTRUCTURALES PARA NIVEL DE ACCESO PL_01 Y SUBNIVELES, PL_02 (INTERMEDIO), PL_03 (PLATAFORMA) CON LA PLANIMETRÍA DE PLACAS ESTRUCTURALES EN LOS ENTREGABLES L1T1-1300-411-CON-ED-EST-PL-0070, 71, 72, 73, 99, 100, 101, 102, 103, 104, 105, 125, 126, RESPECTIVAMENTE. EL NIVEL ESTRUCTURAL (NE) REFERENCIA LOS ESPACIOS DONDE SE DEBE ACONDICIONAR EL ACABADO DE PISO SEGÚN CORRESPONDA, CON LOS NIVELES DE PISO TERMINADO (NPT). LOS NIVELES PROYECTADOS DE EMPATE (NPE) EN LAS ÁREAS DE SERVICIOS ADICIONALES, REFERENCIAN LA ADECUACIÓN DE LOS DESNIVELES EN ESTAS ÁREAS; QUEDA COMO RESPONSABILIDAD DEL LOCATARIO DEFINIR Y ACONDICIONAR ESTE ACABADO DE PISO (NPE) EN LÍNEA CON EL NIVEL (NPT) DE ESPACIOS COLINDANTES. EL NIVEL ESTRUCTURAL (NE) SE ENCUENTRA A (- 0.10M) POR DEBAJO DE LOS NIVELES DE PISO TERMINADO (NPT) Y LOS NIVELES PROYECTADOS DE EMPATE (NPE) MARCADOS EN LA PLANIMETRÍA.

- ARQ_PL_-00.1 = SER-2 / NPT -12.00
- ARQ_PL_00 = SÓTANO / NPT -7.70
- ARQ_PL_00.1 = ACCESO / NPT -1.40
- ARQ_PL_00.2 = ACCESO / NPT -1.25
- ARQ_PL_00.3 = ACCESO / NPT -0.90
- ARQ_PL_00.4 = ACCESO / NPT -0.80
- ARQ_PL_00.5 = ACCESO / NPT -0.65
- ARQ_PL_00.6 = ACCESO / NPT -0.40
- ARQ_PL_00.7 = ACCESO / NPT -0.25
- ARQ_PL_00.8 = ACCESO / NPT -0.20
- ARQ_PL_00.9 = ACCESO / NPT -0.10
- ARQ_PL_01 = ACCESO / NPT 0.00
- ARQ_PL_02 = INTERMEDIO / NPT 6.60
- ARQ_PL_02.2 = TOPE DE RIEL (TOR) / NPT 14.20
- ARQ_PL_03 = PLATAFORMA / NPT 15.34
- ARQ_PL_04 = CUBIERTA EDIFICACIONES / NPT 21.94
- ARQ_PL_05 = CUBIERTA NAVE CENTRAL / NPT 24.60

CONVENCIONES

- - - - LÍMITE DE NIVEL ARQUITECTÓNICO
- - - - HUELLA APÉNDICE TÉCNICO
▬ MURO DIVISORIO
— — — PROYECCIÓN NIVEL SUPERIOR

🟩	SERVICIOS ADICIONALES - ÁREA NO PAGA	🟨	ÁREA NO PAGA
🟩	SERVICIOS ADICIONALES - ÁREA PAGA	🟦	ÁREA OPERATIVA
🟩	SERVICIO PÚBLICO	🟨	ÁREA PAGA
🟦	ZONA DE REFUGIO	🟦	ÁREA PÚBLICA
🟥	ÁREA CULTURAL	⬜	ÁREA TÉCNICA
🟪	ÁREA DE TAQUILLAS BRT	🟧	ÁREA BRT

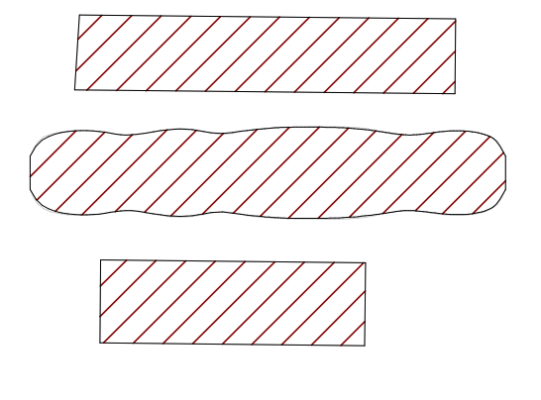

PLANO CLAVE ESTACIÓN 11

No.	PLANOS DE REFERENCIA	REV.

No.	MODELO BIM DE REFERENCIA	REV.
1	L1T1-1100-211-CON-ED-EST-MO-0001.rvt	V00
2	L1T1-1100-212-CON-ED-EST-MO-0001.rvt	V00
3	L1T1-1100-311-CON-ED-EST-MO-0001.rvt	V00
4	L1T1-1150-211-CON-ED-EST-MO-0001.rvt	V00
5	L1T1-1150-212-CON-ED-EST-MO-0001.rvt	V00
6	L1T1-1150-311-CON-ED-EST-MO-0001.rvt	V00
7	L1T1-1200-311-CON-ED-EST-MO-0001.rvt	V00
8	L1T1-1300-411-CON-ED-EST-MO-0001.rvt	V00
9	L1T1-1300-411-CON-ED-EST-MO-0002.rvt	V00
10	L1T1-1310-411-CON-ED-EST-MO-0001.rvt	V00
11	L1T1-1410-311-CON-ED-MEC-MO-0001.rvt	V00
12	L1T1-1420-311-CON-ED-MEC-MO-0001.rvt	V00
13	L1T1-2320-582-CON-ED-EST-MO-0001.rvt	V00
14	L1T1-2330-582-CON-ED-ARQ-MO-0001.rvt	V00
15	L1T1-5110-571-CON-ED-EST-MO-0001.rvt	V00
16	L1T1-5160-311-CON-ED-EST-MO-0001.rvt	V00
17	L1T1-5160-311-CON-ED-ARQ-MO-0001.rvt	V00
18	L1T1-5300-311-CON-ED-MEC-MO-0001.rvt	V00
19	L1T1-5600-311-CON-ED-INS-MO-0001.rvt	V00
20	L1T1-1330-411-CON-ED-ARQ-MO-0011.rvt	V00
21	L1T1-1330-411-CON-ED-ARQ-MO-0012.rvt	V00

No.	PAQUETE DE TRABAJO DE REFERENCIA	REV.
1	XREF-URBANISM_CONTEXT_ST11.rvt	
2	XREF-SECONDARY-STRUCTURE-ST11.rvt	

0 2 10m
1:200

VÁLIDO PARA CONSTRUCCIÓN
20-03-26

METRO BOGOTÁ
GCS Consorcio Consultores PMO Bogotá
CONSORCIO SUPERVISOR PLMB
CHEC

DISEÑÓ:
REN ZHENHUA
Licencia de Arq.nivel I (China): 1101735-614

APROBÓ:
DIEGO ERNESTO DUEÑAS
Mat.: 25202-53876 CND

REVISÓ:
CARLOS MAURICIO BARRETO BARBOSA
Mat.: A4012012-14139353

DIBUJÓ:
EQUIPO CHEC

REVISIÓN No.	FECHA	DESCRIPCIÓN	REVISÓ	APROBÓ	APROBACIÓN CLIENTE
V01	20/03/2026	EMITIDO PARA CONSTRUCCIÓN	C.M.B.B	D.E.D	
V00	31/03/2025	REVISIÓN NO OBJETADA - EMITIDO PARA CONSTRUCCIÓN	F.B.R	E.O.M	
VII	22/07/2024	EMITIDO PARA REVISIÓN Y COMENTARIOS DEL CLIENTE E INTERVENTORÍA - INCLUYE COMENTARIOS /(AJUSTES V4)	F.B.R	E.O.M	
VHH	26/04/2024	EMITIDO PARA REVISIÓN Y COMENTARIOS DEL CLIENTE E INTERVENTORÍA - INCLUYE COMENTARIOS /(AJUSTES V3)	F.B.R	E.O.M	
VGG	30/10/2023	EMITIDO PARA REVISIÓN Y COMENTARIOS DEL CLIENTE E INTERVENTORÍA - INCLUYE COMENTARIOS /(AJUSTES V2)	J.E.M	M.B.M	
VFF	20/04/2023	EMITIDO PARA REVISIÓN Y COMENTARIOS DEL CLIENTE E INTERVENTORÍA - INCLUYE COMENTARIOS /(AJUSTES)	J.E.M	M.B.M	
VEE	18/12/2022	EMITIDO PARA REVISIÓN Y COMENTARIOS DEL CLIENTE E INTERVENTORÍA - INCLUYE COMENTARIOS /(NAVE CENTRAL)	J.E.M	M.B.M	
VDD	11/11/2022	EMITIDO PARA REVISIÓN Y COMENTARIOS DEL CLIENTE E INTERVENTORÍA - INCLUYE COMENTARIOS /(90% ACCESOS)	J.E.M	M.B.M	
VCC	22/08/2022	EMITIDO PARA REVISIÓN Y COMENTARIOS DEL CLIENTE E INTERVENTORÍA - INCLUYE COMENTARIOS /(ENTREGA 90%)	J.E.M	M.B.M	
VBB	06/12/2021	EMITIDO PARA REVISIÓN Y COMENTARIOS DEL CLIENTE E INTERVENTORÍA	J.E.M	M.B.M	

METRO LÍNEA 1

METRO LÍNEA 1
CONTRATO DE CONCESIÓN No. 163 DE 2019

PROYECTO PRIMERA LÍNEA DEL METRO DE BOGOTÁ - TRAMO 1

DIRECTOR DE INTERVENTORÍA:
JAVIER DESCARGA N.
Mat.:25202-68697 CND

ESPECIALISTA INTERVENTORÍA:
CARLOS ALBERTO HOYOS SOTO
Mat.:A25072000-14251682

FECHA:
MARZO 2026

INFRAESTRUCTURA VIAL
ARQUITECTURA
ESTACIÓN METRO 11 (CALLE 1)
GENERAL
VISTA EN PLANTA Y 3D - NIVEL PLATAFORMA

PLANCHA No: L1T1-0000-311-CON-ED-ARQ-PL-0001_07_V01
ARCHIVO: L1T1-0000-311-CON-ED-ARQ-MO-0001_V00.rvt
ESCALA: INDICADA
FECHA: DICIEMBRE 2021
REVISIÓN No. V01
PLANO No. 07 DE 97