L1T1-CON-CAL-FR-0120 - B1 : 1000x707mm

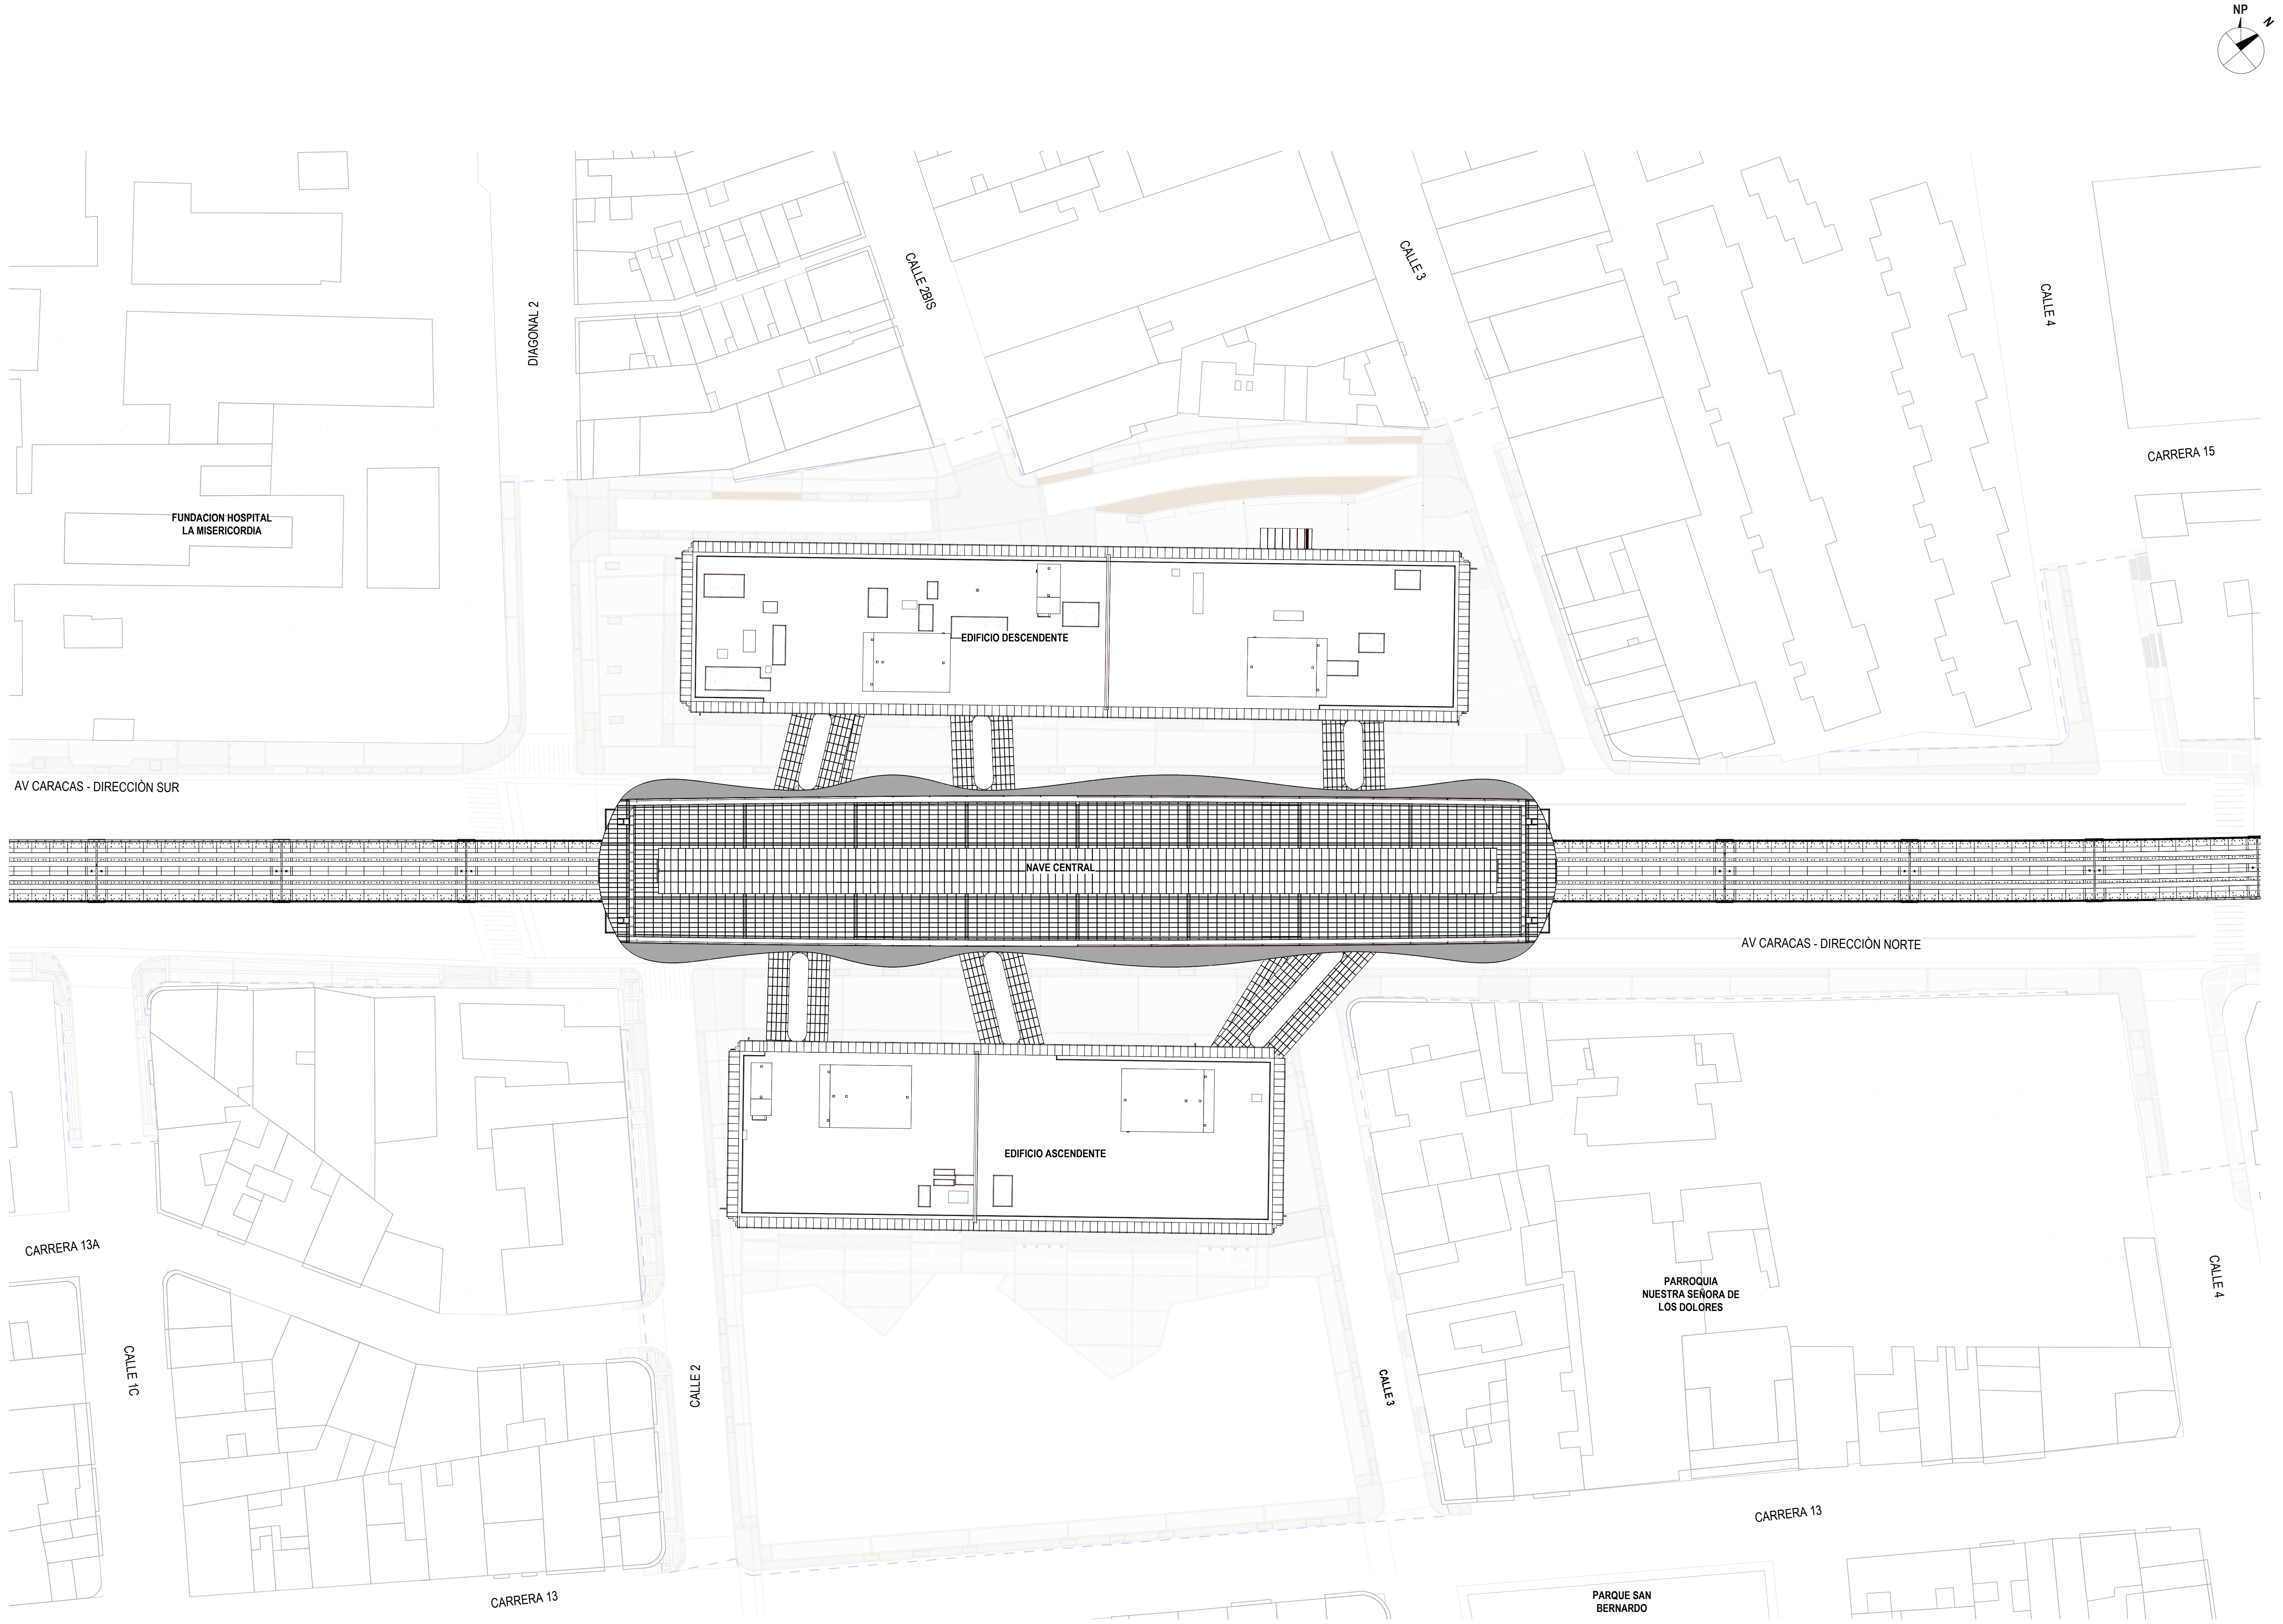

2 NIVEL CUBIERTA_GENERAL
ESC: 1 : 500

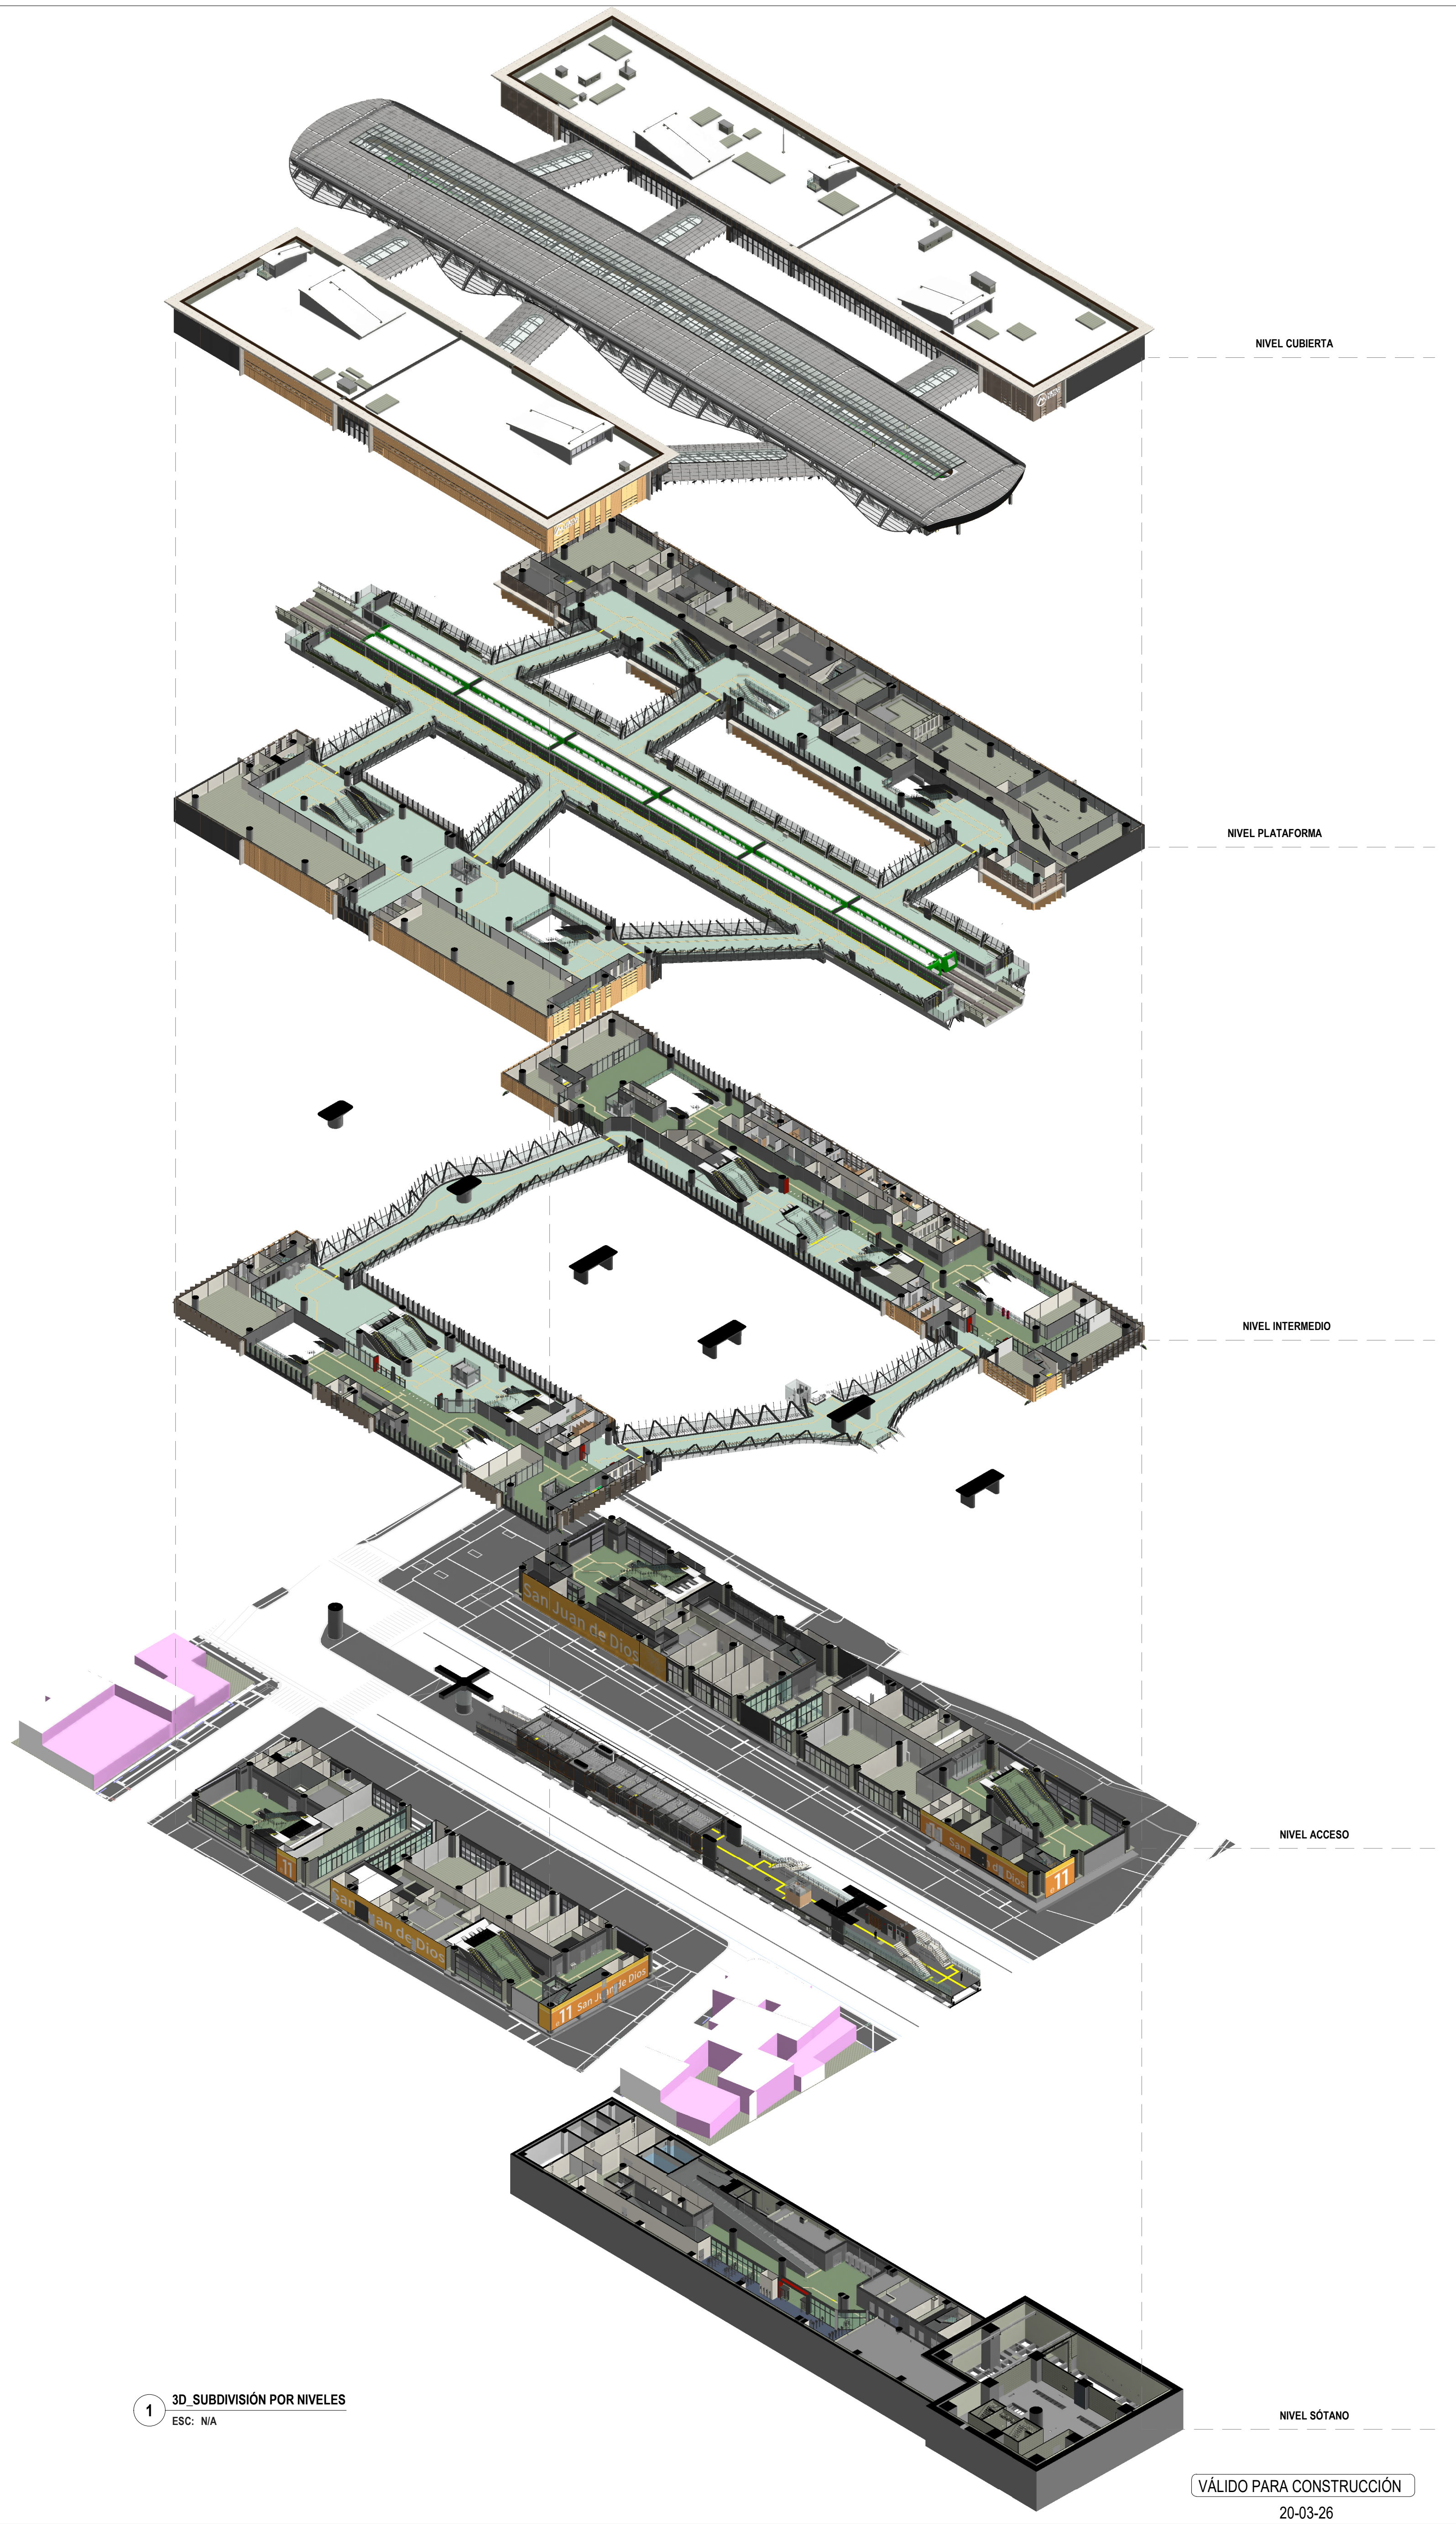

1 3D_SUBDIVISIÓN POR NIVELES
ESC: N/A

VÁLIDO PARA CONSTRUCCIÓN
20-03-26

LOCALIZACIÓN

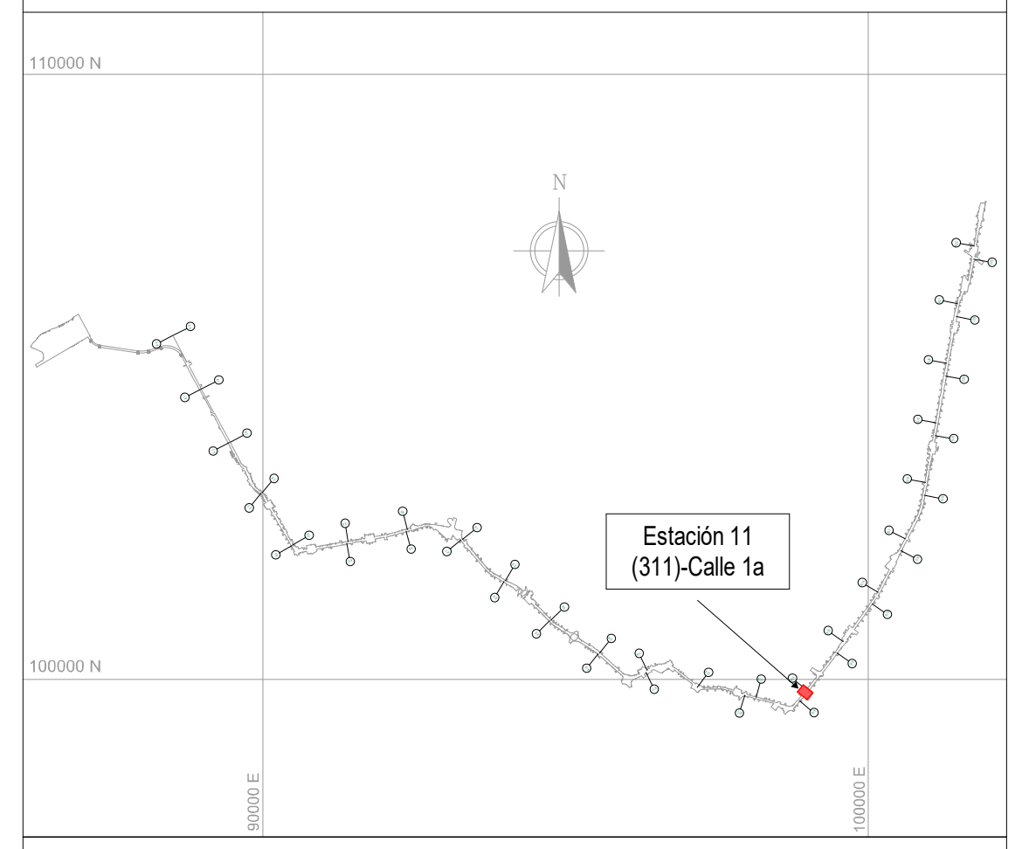

NOTAS

01 TODAS LAS DIMENSIONES ESTÁN CONFIGURADAS EN METROS A MENOS QUE SE INDIQUE UNA UNIDAD DE MEDIDA DIFERENTE.

02 TODAS LAS MEDIDAS, UBICACIÓN Y NIVELES DEBEN VERIFICARSE EN EL LUGAR DE CONSTRUCCIÓN.

03 EL NIVEL DE ACCESO AL EDIFICIO PL 01 CORRESPONDE AL +0,00 DE LA ESTACIÓN Y REFERENCIA AL NIVEL 2575.40 M.S.N.M

04 LOS EJES DEBEN VERIFICARSE EN LA VISTA EN PLANTA DE LOS PLANOS ARQUITECTÓNICOS.

05 LOS COLORES QUE SE MUESTRAN EN LOS PLANOS COMO PROYECCIÓN DE ELEMENTOS ARQUITECTÓNICOS COMO CUBIERTAS, FACHADAS, MUROS, ETC. NO REPRESENTAN LA MATERIALIDAD Y REALIDAD DE ACABADOS DEL PROYECTO, SOLO SON INDICATIVOS PARA REALIZAR UNA CORRECTA LECTURA DE LA PLANIMETRÍA.

06 VER LOS PLANOS DE LAS ESPECIALIDADES ESPECÍFICAS PARA EL DISEÑO DE LAS ZONAS EXTERIORES DE LAS ESTACIONES METRO EN LA QUE SE ENCUENTRAN DETALLES DE URBANISMO, PAISAJISMO, PASOS PEATONALES Y VÍAS.

- ARQ_PL_-00.1 = SER-2 / NPT -12.00
- ARQ_PL_00 = SÓTANO / NPT -7.70
- ARQ_PL_00.1 = ACCESO / NPT -1.40
- ARQ_PL_00.2 = ACCESO / NPT -1.25
- ARQ_PL_00.3 = ACCESO / NPT -0.90
- ARQ_PL_00.4 = ACCESO / NPT -0.80
- ARQ_PL_00.5 = ACCESO / NPT -0.65
- ARQ_PL_00.6 = ACCESO / NPT -0.40
- ARQ_PL_00.7 = ACCESO / NPT -0.25
- ARQ_PL_00.8 = ACCESO / NPT -0.20
- ARQ_PL_00.9 = ACCESO / NPT -0.10
- ARQ_PL_01 = ACCESO / NPT 0.00
- ARQ_PL_02 = INTERMEDIO / NPT 6.60
- ARQ_PL_02.2 = TOPE DE RIEL (TOR) / NPT 14.20
- ARQ_PL_03 = PLATAFORMA / NPT 15.34
- ARQ_PL_04 = CUBIERTA EDIFICACIONES / NPT 21.94
- ARQ_PL_05 = CUBIERTA NAVE CENTRAL / NPT 24.60

CONVENCIONES

- - - -	LÍMITE DE NIVEL ARQUITECTÓNICO
- - - -	HUELLA APÉNDICE TÉCNICO
▬	MURO DIVISORIO
— — —	PROYECCIÓN NIVEL SUPERIOR

No.	PLANOS DE REFERENCIA	REV.
No.	**MODELO BIM DE REFERENCIA**	**REV.**
1	L1T1-1100-211-CON-ED-EST-MO-0001.rvt	V00
2	L1T1-1100-212-CON-ED-EST-MO-0001.rvt	V00
3	L1T1-1100-311-CON-ED-EST-MO-0001.rvt	V00
4	L1T1-1150-211-CON-ED-EST-MO-0001.rvt	V00
5	L1T1-1150-212-CON-ED-EST-MO-0001.rvt	V00
6	L1T1-1150-311-CON-ED-EST-MO-0001.rvt	V00
7	L1T1-1200-311-CON-ED-EST-MO-0001.rvt	V00
8	L1T1-1300-411-CON-ED-EST-MO-0001.rvt	V00
9	L1T1-1300-411-CON-ED-EST-MO-0002.rvt	V00
10	L1T1-1310-411-CON-ED-EST-MO-0001.rvt	V00
11	L1T1-1410-311-CON-ED-MEC-MO-0001.rvt	V00
12	L1T1-1420-311-CON-ED-MEC-MO-0001.rvt	V00
13	L1T1-2320-582-CON-ED-EST-MO-0001.rvt	V00
14	L1T1-2330-582-CON-ED-ARQ-MO-0001.rvt	V00
15	L1T1-5110-571-CON-ED-EST-MO-0001.rvt	V00
16	L1T1-5160-311-CON-ED-EST-MO-0001.rvt	V00
17	L1T1-5160-311-CON-ED-ARQ-MO-0001.rvt	V00
18	L1T1-5300-311-CON-ED-MEC-MO-0001.rvt	V00
19	L1T1-5600-311-CON-ED-INS-MO-0001.rvt	V00
20	L1T1-1330-411-CON-ED-ARQ-MO-0011.rvt	V00
21	L1T1-1330-411-CON-ED-ARQ-MO-0012.rvt	V00
No.	**PAQUETE DE TRABAJO DE REFERENCIA**	**REV.**
1	XREF-URBANISM_CONTEXT_ST11.rvt	
2	XREF-SECONDARY-STRUCTURE-ST11.rvt	

0 5 25m
1:500

METRO BOGOTÁ
GCS Consorcio Consultores PMO Bogotá
CONSORCIO SUPERVISOR PLMB
HEC

DISEÑÓ: REN ZHENHUA Licencia de Arq.nivel I (China): 1101735-614	APROBÓ: DIEGO ERNESTO DUEÑAS Mat.: 25202-53876 CND
REVISÓ: CARLOS MAURICIO BARRETO BARBOSA Mat.: A4012012-14139353	DIBUJÓ: EQUIPO CHEC

REVISIÓN No.	FECHA	DESCRIPCIÓN	REVISÓ	APROBÓ	APROBACIÓN CLIENTE
V01	20/03/2026	EMITIDO PARA CONSTRUCCIÓN	C.M.B.B	D.E.D	
V00	31/03/2025	REVISIÓN NO OBJETADA - EMITIDO PARA CONSTRUCCIÓN	F.B.R	E.O.M	
VII	22/07/2024	EMITIDO PARA REVISIÓN Y COMENTARIOS DEL CLIENTE E INTERVENTORÍA - INCLUYE COMENTARIOS /(AJUSTES V4)	F.B.R	E.O.M	
VHH	26/04/2024	EMITIDO PARA REVISIÓN Y COMENTARIOS DEL CLIENTE E INTERVENTORÍA - INCLUYE COMENTARIOS /(AJUSTES V3)	F.B.R	E.O.M	
VGG	30/10/2023	EMITIDO PARA REVISIÓN Y COMENTARIOS DEL CLIENTE E INTERVENTORÍA - INCLUYE COMENTARIOS /(AJUSTES V2)	J.E.M	M.B.M	
VFF	20/04/2023	EMITIDO PARA REVISIÓN Y COMENTARIOS DEL CLIENTE E INTERVENTORÍA - INCLUYE COMENTARIOS /(AJUSTES)	J.E.M	M.B.M	
VEE	18/12/2022	EMITIDO PARA REVISIÓN Y COMENTARIOS DEL CLIENTE E INTERVENTORÍA - INCLUYE COMENTARIOS /(NAVE CENTRAL)	J.E.M	M.B.M	
VDD	11/11/2022	EMITIDO PARA REVISIÓN Y COMENTARIOS DEL CLIENTE E INTERVENTORÍA - INCLUYE COMENTARIOS /(90% ACCESOS)	J.E.M	M.B.M	
VCC	22/08/2022	EMITIDO PARA REVISIÓN Y COMENTARIOS DEL CLIENTE E INTERVENTORÍA - INCLUYE COMENTARIOS /(ENTREGA 90%)	J.E.M	M.B.M	
VBB	06/12/2021	EMITIDO PARA REVISIÓN Y COMENTARIOS DEL CLIENTE E INTERVENTORÍA	J.E.M	M.B.M	

METRO LÍNEA 1

METRO LÍNEA 1
CONTRATO DE CONCESIÓN No. 163 DE 2019

PROYECTO PRIMERA LÍNEA DEL METRO DE BOGOTÁ - TRAMO 1

DIRECTOR DE INTERVENTORÍA: JAVIER DESCARGA N.
Mat.:25202-68697 CND

ESPECIALISTA INTERVENTORÍA: CARLOS ALBERTO HOYOS SOTO
Mat.:A25072000-14251682

FECHA: MARZO 2026

INFRAESTRUCTURA VIAL

ARQUITECTURA

ESTACIÓN METRO 11 (CALLE 1)
GENERAL
VISTA EN PLANTA - NIVEL CUBIERTA - AXONOMETRÍA GENERAL

PLANCHA No: L1T1-0000-311-CON-ED-ARQ-PL-0001_08_V01
ARCHIVO: L1T1-0000-311-CON-ED-ARQ-MO-0001_V00.rvt
ESCALA: INDICADA
FECHA: DICIEMBRE 2021
REVISIÓN No. V01
PLANO No. 08 DE 97