L1T1-CON-CAL-FR-0120 - B1 : 1000x707mm

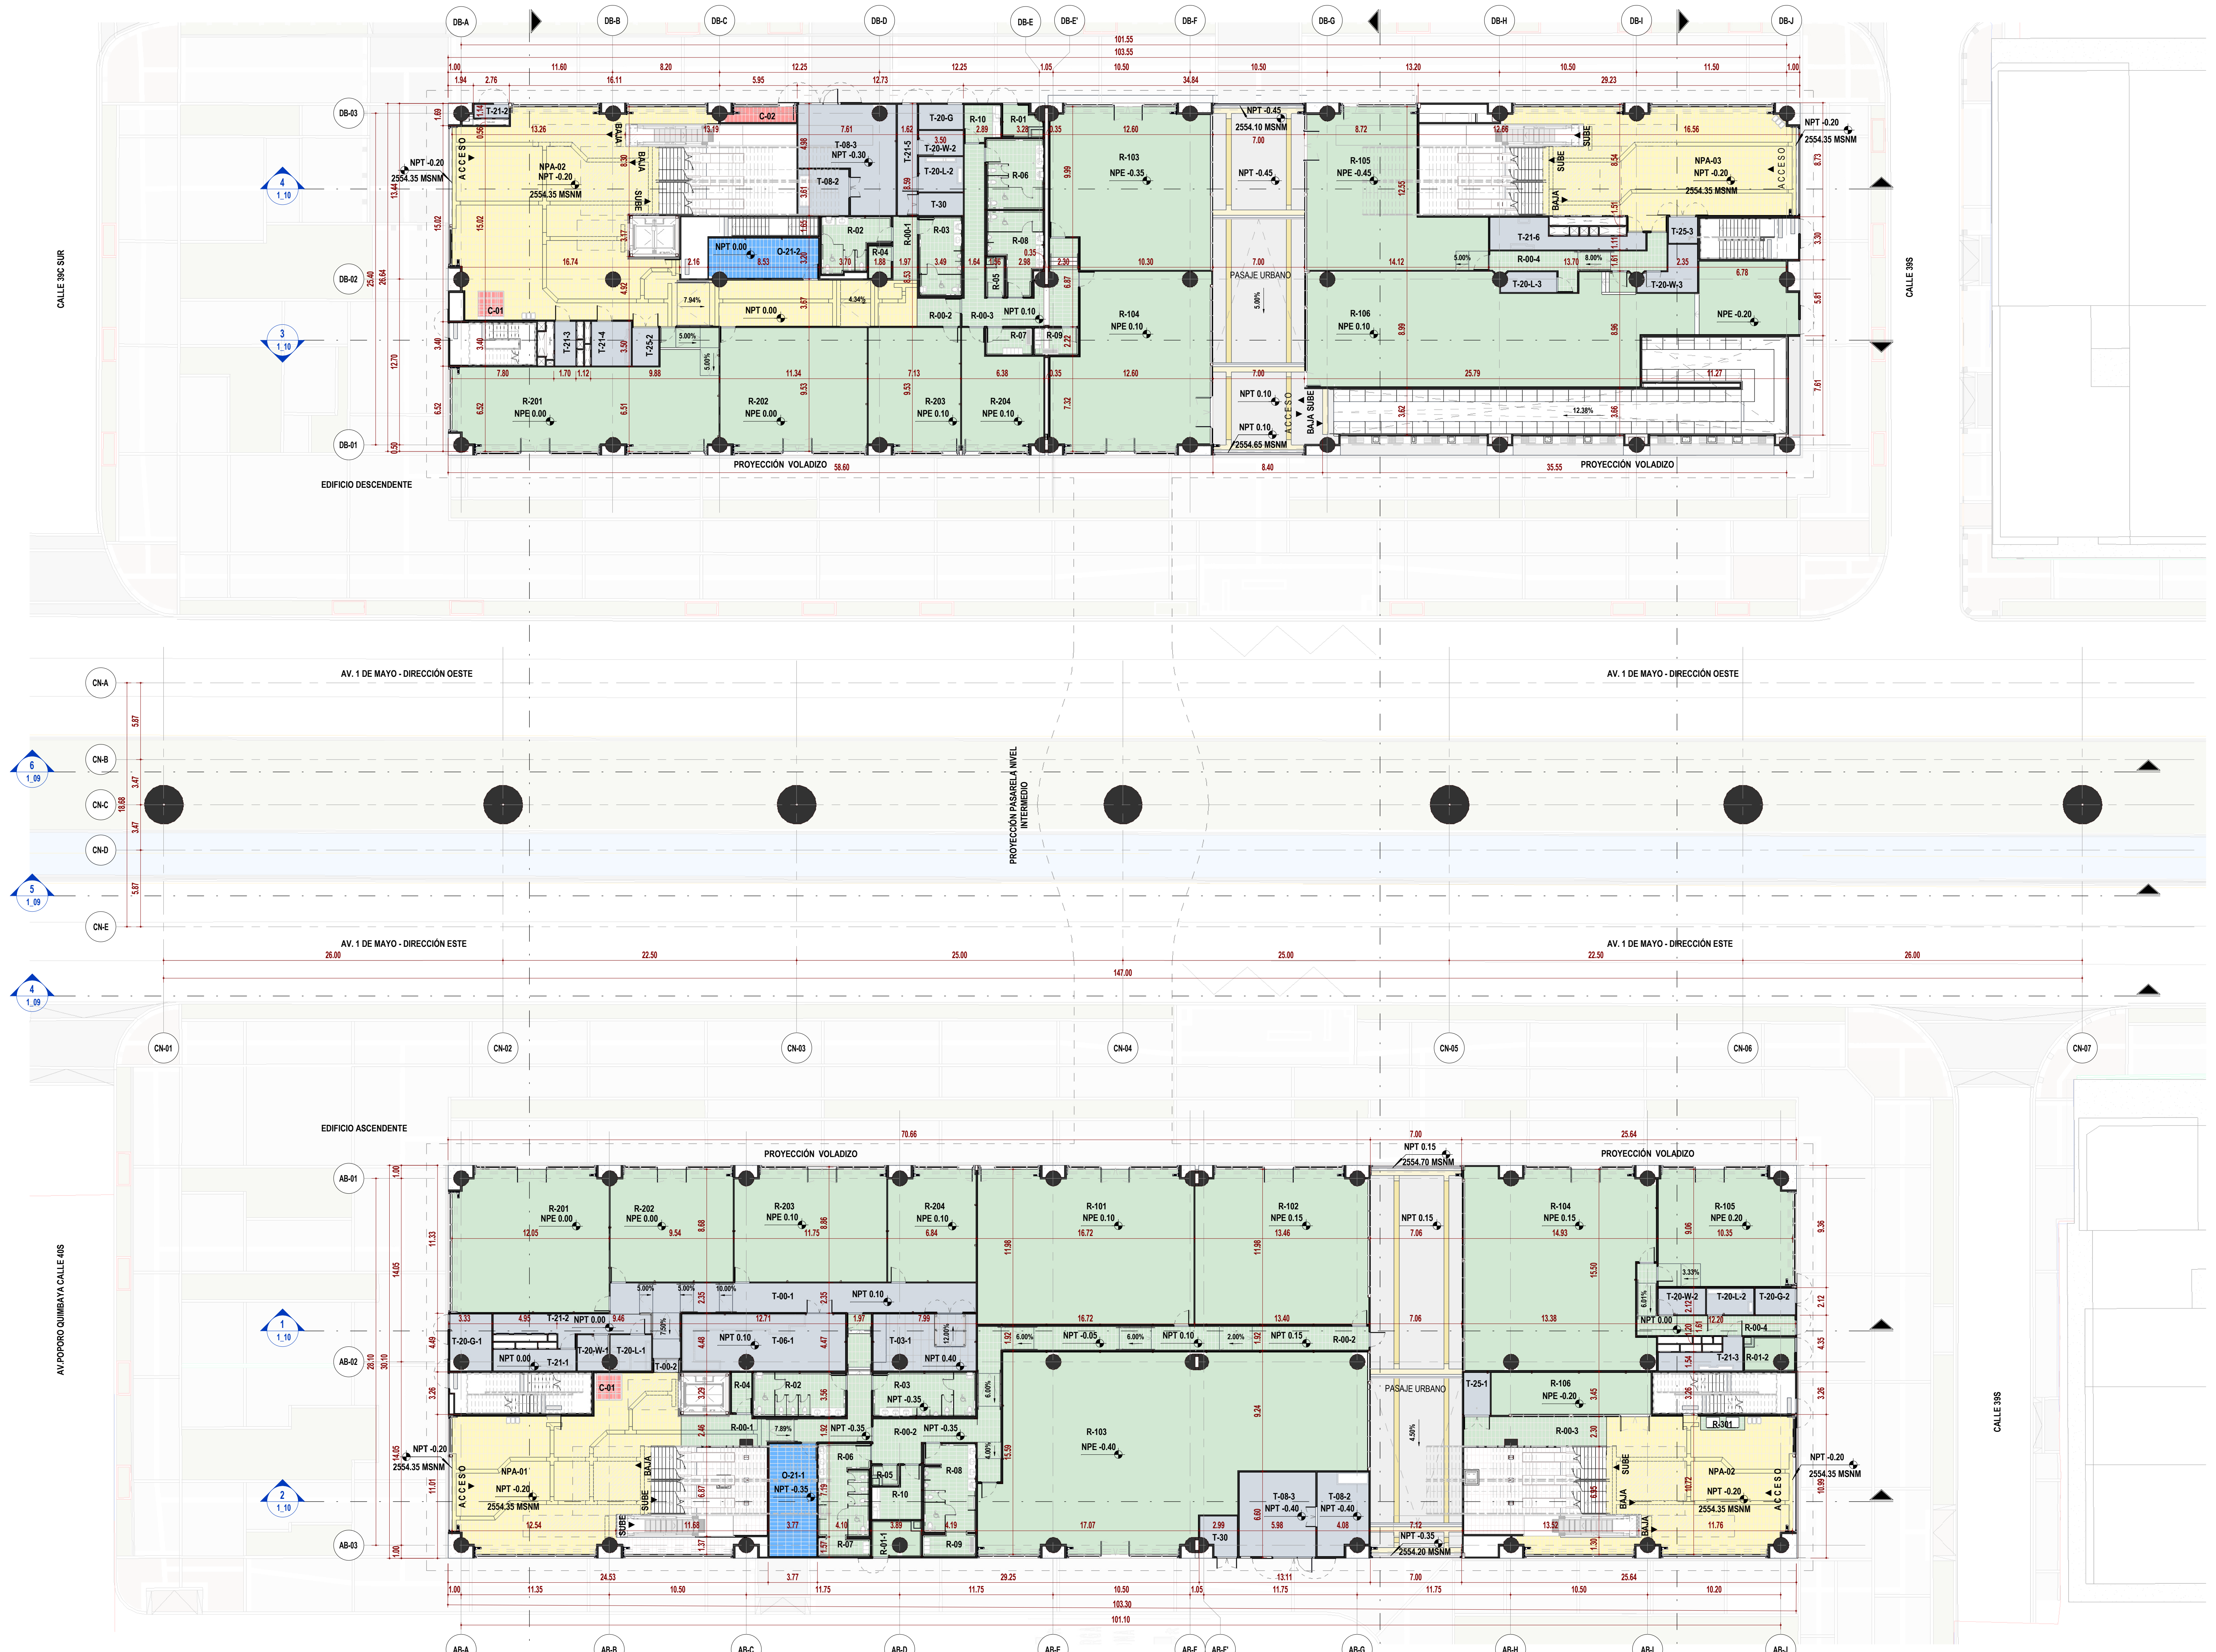

2 NIVEL ACCESO_GENERAL
ESC : 1 : 200

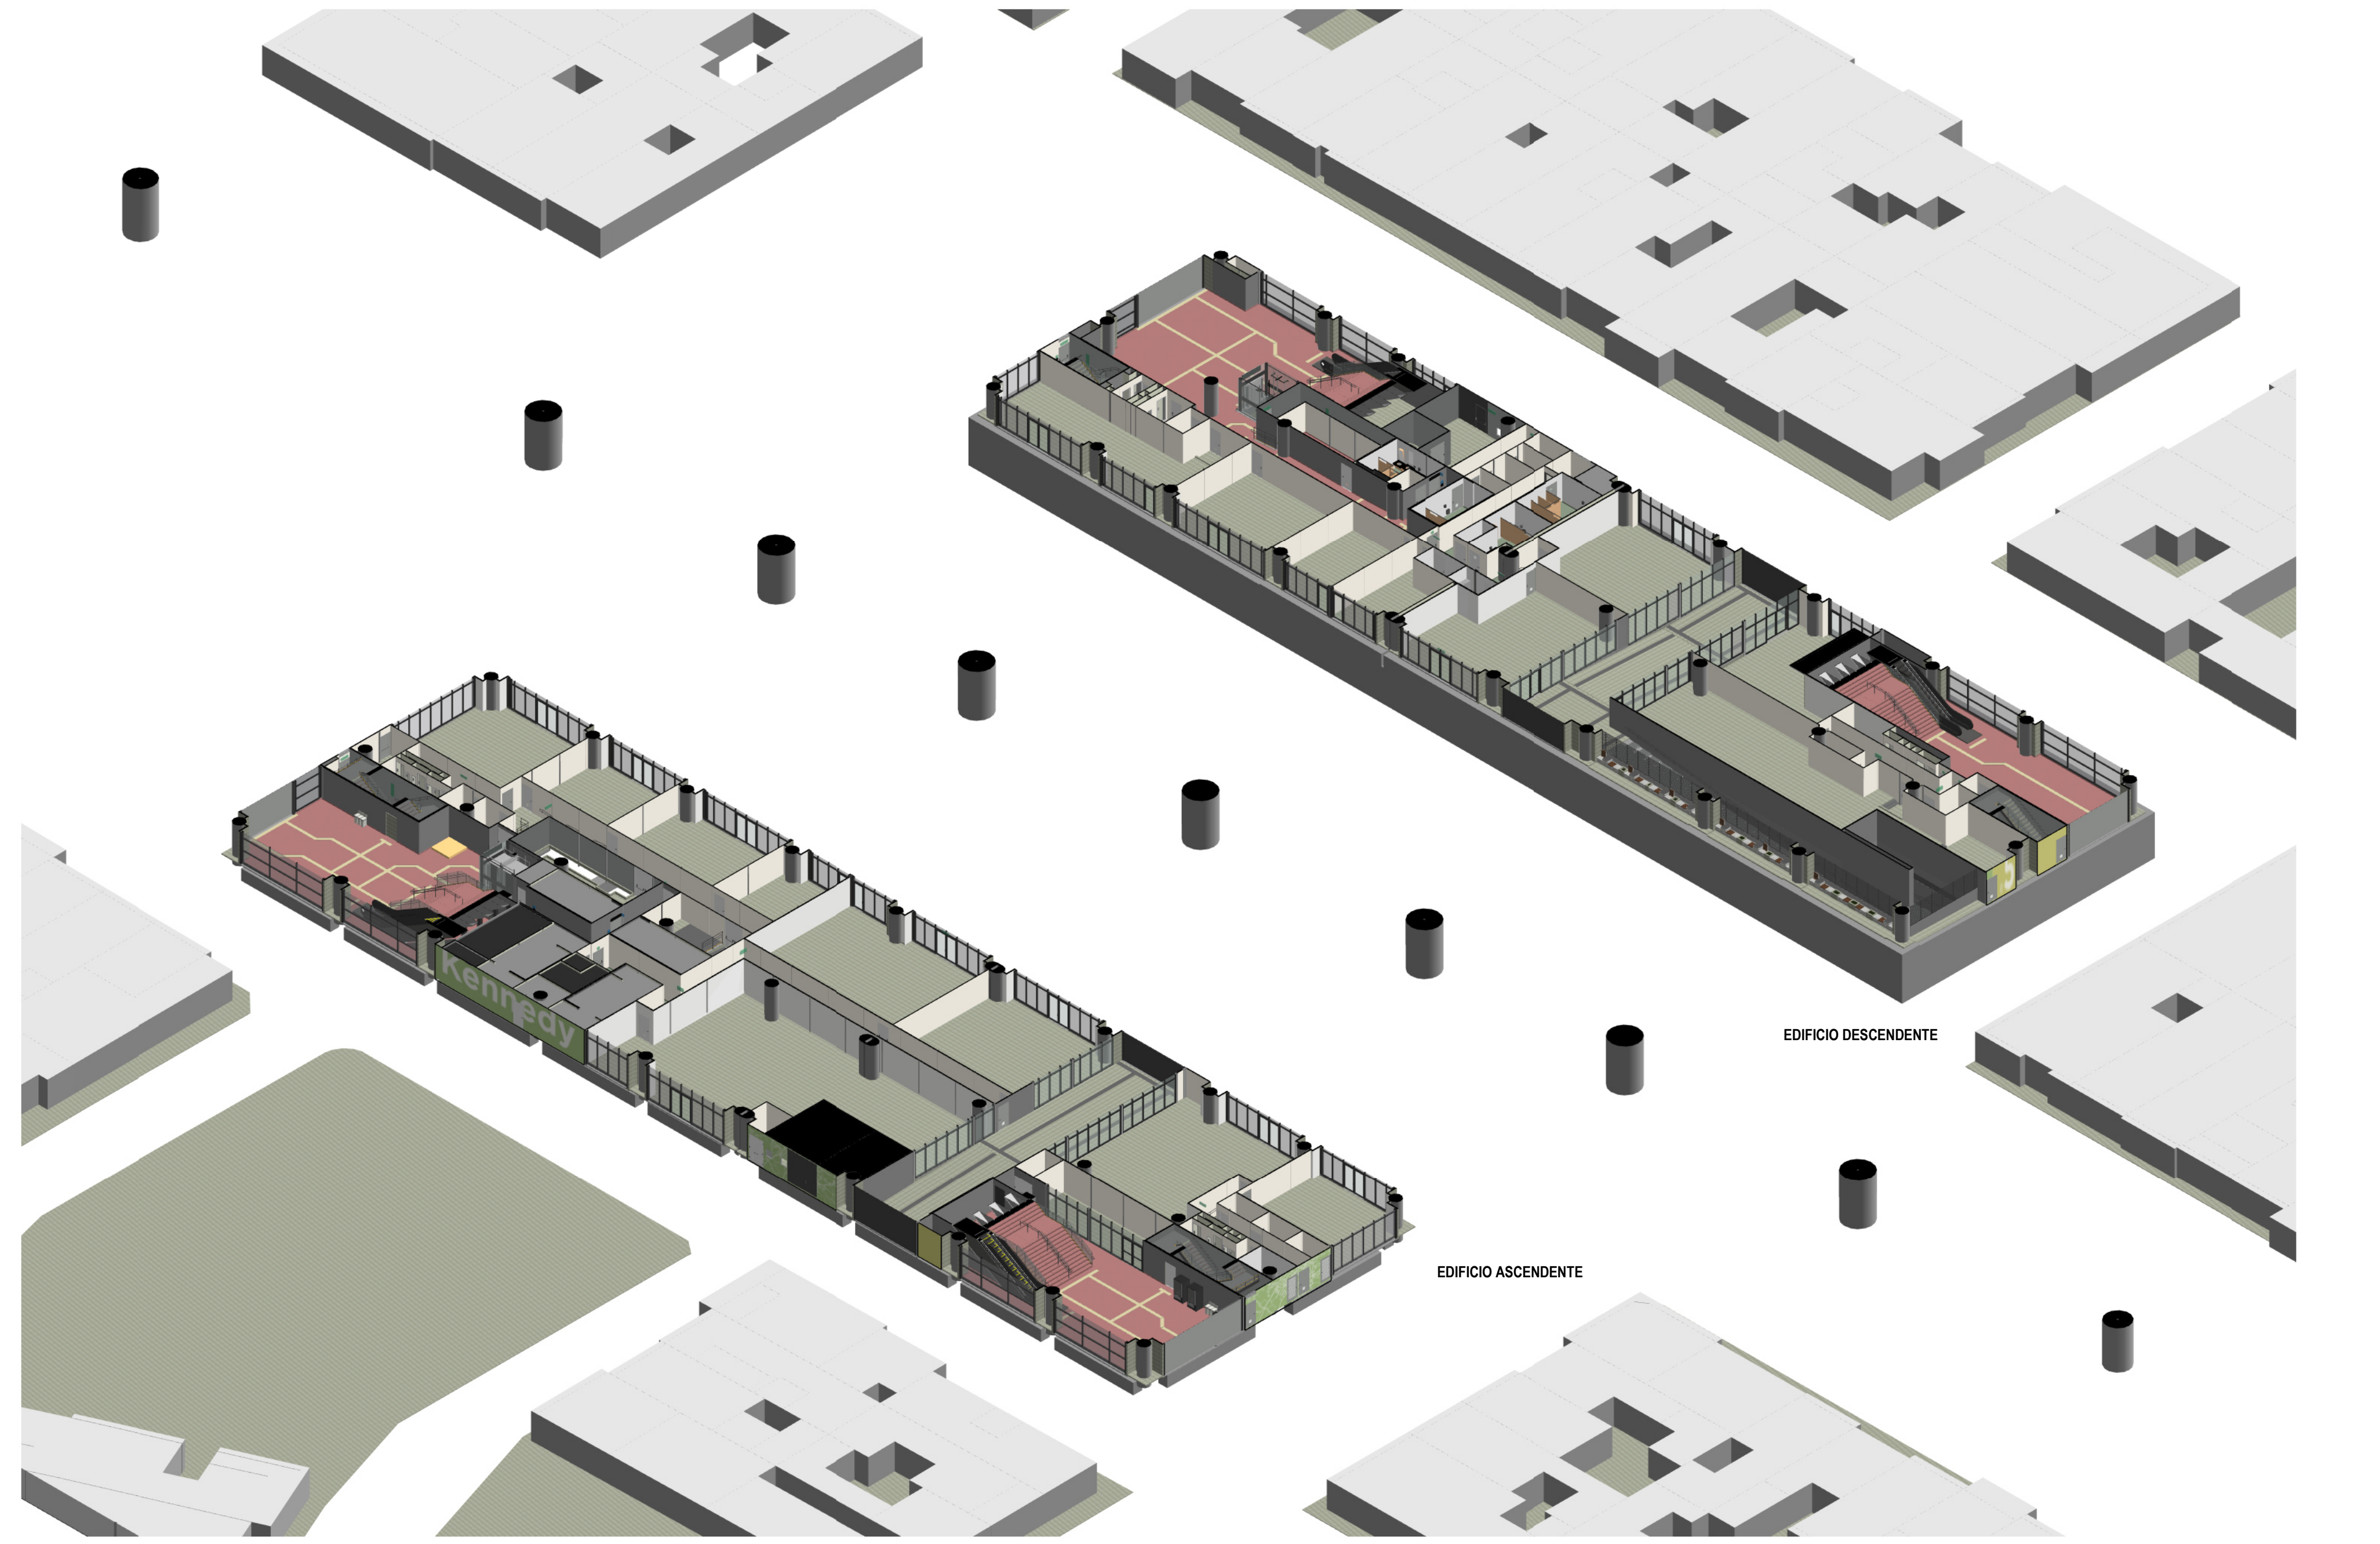

1 3D_NIVEL ACCESO_GENERAL
ESC : N/A

TABLA DE ÁREAS ÚTILES (NIVEL ACCESO)			
CÓDIGO	NOMBRE	ÁREA (m²)	DEPARTAMENTO
EDIFICIO ASCENDENTE			
ARQ_PL_00.1_ACCESO			
R-103	SERVICIOS ADICIONALES - ÁREA DE SERVICIO	362.25	SERVICIOS ADICIONALES - ÁREA NO PAGA
T-08-2	CENTRO DE TRANSFORMACIÓN ENEL-CODENSA (CT)_CUARTO BAJA TENSIÓN	23.12	ÁREA TÉCNICA
T-08-3	CENTRO DE TRANSFORMACIÓN ENEL-CODENSA (CT)_CUARTO MEDIA TENSIÓN	37.84	ÁREA TÉCNICA
T-30	SISTEMA PROTECCIÓN CONTRA INCENDIO ENEL	7.59	ÁREA TÉCNICA
		430.80	
ARQ_PL_00.2_ACCESO			
O-21-1	ALMACENAMIENTO DE LA ESTACIÓN	31.47	ÁREA OPERATIVA
R-00-2	SERVICIOS ADICIONALES - CORREDOR OPERATIVO	93.66	SERVICIOS ADICIONALES - ÁREA NO PAGA
R-01-1	SERVICIOS ADICIONALES - CUARTO DE BASURAS PARA METRO	8.86	SERVICIOS ADICIONALES - ÁREA NO PAGA
R-02	SERVICIOS ADICIONALES - BAÑO PÚBLICO DE MUJERES	23.12	SERVICIOS ADICIONALES - ÁREA NO PAGA
R-03	SERVICIOS ADICIONALES - BAÑO PÚBLICO DE HOMBRES	25.82	SERVICIOS ADICIONALES - ÁREA NO PAGA
R-05	SERVICIOS ADICIONALES - CUARTO DE LIMPIEZA	3.15	SERVICIOS ADICIONALES - ÁREA NO PAGA
R-06	SERVICIOS ADICIONALES - BAÑOS EMPLEADOS MUJERES	26.96	SERVICIOS ADICIONALES - ÁREA NO PAGA
R-07	SERVICIOS ADICIONALES - VESTIDORES EMPLEADOS MUJERES	5.61	SERVICIOS ADICIONALES - ÁREA NO PAGA
R-08	SERVICIOS ADICIONALES - BAÑOS EMPLEADOS HOMBRES	26.33	SERVICIOS ADICIONALES - ÁREA NO PAGA
R-09	SERVICIOS ADICIONALES - VESTIDORES EMPLEADOS HOMBRES	6.97	SERVICIOS ADICIONALES - ÁREA NO PAGA
R-10	SERVICIOS ADICIONALES - SALA DE EMPLEADOS	11.94	SERVICIOS ADICIONALES - ÁREA NO PAGA
		263.88	
ARQ_PL_00.4_ACCESO			
C-01	ÁREAS DE USO CULTURAL	4.00	ÁREA CULTURAL
NPA-01	ÁREA NO PAGA	174.81	ÁREA NO PAGA
NPA-02	ÁREA NO PAGA	147.12	ÁREA NO PAGA
R-00-1	SERVICIOS ADICIONALES - CORREDOR OPERATIVO	44.20	SERVICIOS ADICIONALES - ÁREA NO PAGA
R-00-3	SERVICIOS ADICIONALES - CORREDOR OPERATIVO	24.12	SERVICIOS ADICIONALES - ÁREA NO PAGA
R-04	SERVICIOS ADICIONALES - CONTROL DE ACCESO BAÑOS PÚBLICOS	4.87	SERVICIOS ADICIONALES - ÁREA NO PAGA
R-106	SERVICIOS ADICIONALES - ÁREA DE SERVICIO	39.21	SERVICIOS ADICIONALES - ÁREA NO PAGA
R-301	SERVICIOS ADICIONALES - MÁQUINAS EXPENDEDORAS/CAJEROS AUTOMÁTICOS	3.65	SERVICIOS ADICIONALES - ÁREA NO PAGA
T-00-2	CIRCULACIÓN TÉCNICA	2.06	ÁREA TÉCNICA
T-25-1	NODO DE ACCESO DE TELECOMUNICACIONES	6.52	ÁREA TÉCNICA
		450.55	
ARQ_PL_00.5_ACCESO			
T-00-1	CIRCULACIÓN TÉCNICA	70.52	ÁREA TÉCNICA
		70.52	
ARQ_PL_01_ACCESO			
R-00-4	SERVICIOS ADICIONALES - CORREDOR OPERATIVO	24.14	SERVICIOS ADICIONALES - ÁREA NO PAGA
R-01-2	SERVICIOS ADICIONALES - CUARTO DE BASURAS PARA METRO	8.69	SERVICIOS ADICIONALES - ÁREA NO PAGA
R-201	SERVICIOS ADICIONALES - ÁREA DE COMIDAS	128.42	SERVICIOS ADICIONALES - ÁREA NO PAGA
R-202	SERVICIOS ADICIONALES - ÁREA DE COMIDAS	80.38	SERVICIOS ADICIONALES - ÁREA NO PAGA
T-20-G-1	MEDIDORES (GAS)	12.40	ÁREA TÉCNICA
T-20-G-2	MEDIDORES (GAS)	6.10	ÁREA TÉCNICA
T-20-L-1	MEDIDORES (LUZ)	8.04	ÁREA TÉCNICA
T-20-L-2	MEDIDORES (LUZ)	7.22	ÁREA TÉCNICA
T-20-W-1	MEDIDORES (AGUA)	6.09	ÁREA TÉCNICA
T-20-W-2	MEDIDORES (AGUA)	7.22	ÁREA TÉCNICA
T-21-1	ÁREA DE INSPECCIÓN	10.30	ÁREA TÉCNICA
T-21-2	ÁREA DE INSPECCIÓN	19.84	ÁREA TÉCNICA
T-21-3	ÁREA DE INSPECCIÓN	10.85	ÁREA TÉCNICA
		329.70	
ARQ_PL_01.1_ACCESO			
R-101	SERVICIOS ADICIONALES - ÁREA DE SERVICIO	193.90	SERVICIOS ADICIONALES - ÁREA NO PAGA
R-203	SERVICIOS ADICIONALES - ÁREA DE COMIDAS	98.42	SERVICIOS ADICIONALES - ÁREA NO PAGA
R-204	SERVICIOS ADICIONALES - ÁREA DE COMIDAS	56.03	SERVICIOS ADICIONALES - ÁREA NO PAGA
T-03-1	LOCAL SECUNDARIO DE TELECOMUNICACIONES	32.40	ÁREA TÉCNICA
T-06-1	LOCAL SECUNDARIO DE TABLEROS	53.31	ÁREA TÉCNICA
		434.07	
ARQ_PL_01.2_ACCESO			
R-102	SERVICIOS ADICIONALES - ÁREA DE SERVICIO	153.61	SERVICIOS ADICIONALES - ÁREA NO PAGA
R-104	SERVICIOS ADICIONALES - ÁREA DE SERVICIO	211.00	SERVICIOS ADICIONALES - ÁREA NO PAGA
		364.61	
ARQ_PL_01.3_ACCESO			
R-105	SERVICIOS ADICIONALES - ÁREA DE SERVICIO	89.58	SERVICIOS ADICIONALES - ÁREA NO PAGA
		89.58	
EDIFICIO DESCENDENTE			
ARQ_PL_00.1_ACCESO			
R-00-4	SERVICIOS ADICIONALES - CORREDOR OPERATIVO	25.38	SERVICIOS ADICIONALES - ÁREA NO PAGA
R-105	SERVICIOS ADICIONALES - ÁREA DE SERVICIO	125.09	SERVICIOS ADICIONALES - ÁREA NO PAGA
T-20-L-3	MEDIDORES (LUZ)	6.21	ÁREA TÉCNICA
		156.67	
ARQ_PL_00.2_ACCESO			
R-00-3	SERVICIOS ADICIONALES - CORREDOR OPERATIVO	48.17	SERVICIOS ADICIONALES - ÁREA NO PAGA
R-103	SERVICIOS ADICIONALES - ÁREA DE SERVICIO	144.95	SERVICIOS ADICIONALES - ÁREA NO PAGA
		193.12	
ARQ_PL_00.3_ACCESO			
C-02	ÁREAS DE USO CULTURAL	6.11	ÁREA CULTURAL
T-08-2	CENTRO DE TRANSFORMACIÓN ENEL-CODENSA (CT)_CUARTO BAJA TENSIÓN	13.37	ÁREA TÉCNICA
T-08-3	CENTRO DE TRANSFORMACIÓN ENEL-CODENSA (CT)_CUARTO MEDIA TENSIÓN	47.37	ÁREA TÉCNICA
T-20-G	MEDIDORES (GAS)	6.37	ÁREA TÉCNICA
T-20-L-2	MEDIDORES (LUZ)	9.04	ÁREA TÉCNICA
T-20-W-2	MEDIDORES (AGUA)	6.41	ÁREA TÉCNICA
T-21-5	ÁREA DE INSPECCIÓN	12.67	ÁREA TÉCNICA
T-30	SISTEMA PROTECCIÓN CONTRA INCENDIO ENEL	5.73	ÁREA TÉCNICA
		107.06	
ARQ_PL_00.4_ACCESO			
C-01	ÁREAS DE USO CULTURAL	4.00	ÁREA CULTURAL
NPA-02	ÁREA NO PAGA	303.38	ÁREA NO PAGA
NPA-03	ÁREA NO PAGA	162.96	ÁREA NO PAGA
R-01	SERVICIOS ADICIONALES - CUARTO DE BASURAS PARA METRO	6.56	SERVICIOS ADICIONALES - ÁREA NO PAGA
R-106	SERVICIOS ADICIONALES - ÁREA DE SERVICIO	264.99	SERVICIOS ADICIONALES - ÁREA NO PAGA
T-20-W-3	MEDIDORES (AGUA)	11.32	ÁREA TÉCNICA
T-21-2	ÁREA DE INSPECCIÓN	2.66	ÁREA TÉCNICA
T-21-3	ÁREA DE INSPECCIÓN	5.34	ÁREA TÉCNICA
T-21-4	ÁREA DE INSPECCIÓN	10.10	ÁREA TÉCNICA
T-21-6	ÁREA DE INSPECCIÓN	18.90	ÁREA TÉCNICA
T-25-2	NODO DE ACCESO DE TELECOMUNICACIONES	5.81	ÁREA TÉCNICA
T-25-3	NODO DE ACCESO DE TELECOMUNICACIONES	4.46	ÁREA TÉCNICA
		800.48	
ARQ_PL_01_ACCESO			
O-21-2	ALMACENAMIENTO DE LA ESTACIÓN	25.38	ÁREA OPERATIVA
R-201	SERVICIOS ADICIONALES - ÁREA DE COMIDAS	140.76	SERVICIOS ADICIONALES - ÁREA NO PAGA
R-202	SERVICIOS ADICIONALES - ÁREA DE COMIDAS	105.42	SERVICIOS ADICIONALES - ÁREA NO PAGA
		271.56	
ARQ_PL_01.1_ACCESO			
R-00-1	SERVICIOS ADICIONALES - CORREDOR OPERATIVO	9.01	SERVICIOS ADICIONALES - ÁREA NO PAGA
R-00-2	SERVICIOS ADICIONALES - CORREDOR OPERATIVO	7.08	SERVICIOS ADICIONALES - ÁREA NO PAGA
R-02	SERVICIOS ADICIONALES - BAÑO PÚBLICO DE MUJERES	18.34	SERVICIOS ADICIONALES - ÁREA NO PAGA
R-03	SERVICIOS ADICIONALES - BAÑO PÚBLICO DE HOMBRES	19.15	SERVICIOS ADICIONALES - ÁREA NO PAGA
R-04	SERVICIOS ADICIONALES - CONTROL DE ACCESO BAÑOS PÚBLICOS	3.86	SERVICIOS ADICIONALES - ÁREA NO PAGA
R-05	SERVICIOS ADICIONALES - CUARTO DE LIMPIEZA	4.21	SERVICIOS ADICIONALES - ÁREA NO PAGA
R-06	SERVICIOS ADICIONALES - BAÑOS EMPLEADOS MUJERES	23.05	SERVICIOS ADICIONALES - ÁREA NO PAGA
R-07	SERVICIOS ADICIONALES - VESTIDORES EMPLEADOS MUJERES	7.24	SERVICIOS ADICIONALES - ÁREA NO PAGA
R-08	SERVICIOS ADICIONALES - BAÑOS EMPLEADOS HOMBRES	21.63	SERVICIOS ADICIONALES - ÁREA NO PAGA
R-09	SERVICIOS ADICIONALES - VESTIDORES EMPLEADOS HOMBRES	6.89	SERVICIOS ADICIONALES - ÁREA NO PAGA
R-10	SERVICIOS ADICIONALES - SALA DE EMPLEADOS	7.42	SERVICIOS ADICIONALES - ÁREA NO PAGA
R-104	SERVICIOS ADICIONALES - ÁREA DE SERVICIO	151.00	SERVICIOS ADICIONALES - ÁREA NO PAGA
R-203	SERVICIOS ADICIONALES - ÁREA DE COMIDAS	64.85	SERVICIOS ADICIONALES - ÁREA NO PAGA
R-204	SERVICIOS ADICIONALES - ÁREA DE COMIDAS	48.39	SERVICIOS ADICIONALES - ÁREA NO PAGA
		392.12	
TOTAL NIVEL ACCESO		4354.72	

TABLA DE ÁREAS ÚTILES POR DEPARTAMENTO (NIVEL ACCESO)	
DEPARTAMENTO	ÁREA (m²)
EDIFICIO ASCENDENTE	
ARQ_PL_00.1_ACCESO	
SERVICIOS ADICIONALES - ÁREA NO PAGA	362.25
ÁREA TÉCNICA	68.55
ARQ_PL_00.2_ACCESO	
SERVICIOS ADICIONALES - ÁREA NO PAGA	232.41
ÁREA OPERATIVA	31.47
ARQ_PL_00.4_ACCESO	
SERVICIOS ADICIONALES - ÁREA NO PAGA	116.04
ÁREA CULTURAL	4.00
ÁREA NO PAGA	321.94
ÁREA TÉCNICA	8.58
ARQ_PL_00.5_ACCESO	
ÁREA TÉCNICA	70.52
ARQ_PL_01_ACCESO	
SERVICIOS ADICIONALES - ÁREA NO PAGA	241.64
ÁREA TÉCNICA	88.06
ARQ_PL_01.1_ACCESO	
SERVICIOS ADICIONALES - ÁREA NO PAGA	348.35
ÁREA TÉCNICA	85.72
ARQ_PL_01.2_ACCESO	
SERVICIOS ADICIONALES - ÁREA NO PAGA	364.61
ARQ_PL_01.3_ACCESO	
SERVICIOS ADICIONALES - ÁREA NO PAGA	89.58
EDIFICIO DESCENDENTE	
ARQ_PL_00.1_ACCESO	
SERVICIOS ADICIONALES - ÁREA NO PAGA	150.46
ÁREA TÉCNICA	6.21
ARQ_PL_00.2_ACCESO	
SERVICIOS ADICIONALES - ÁREA NO PAGA	193.12
ARQ_PL_00.3_ACCESO	
ÁREA CULTURAL	6.11
ÁREA TÉCNICA	100.95
ARQ_PL_00.4_ACCESO	
SERVICIOS ADICIONALES - ÁREA NO PAGA	271.55
ÁREA CULTURAL	4.00
ÁREA NO PAGA	466.34
ÁREA TÉCNICA	58.59
ARQ_PL_01_ACCESO	
SERVICIOS ADICIONALES - ÁREA NO PAGA	246.18
ÁREA OPERATIVA	25.38
ARQ_PL_01.1_ACCESO	
SERVICIOS ADICIONALES - ÁREA NO PAGA	392.12
TOTAL NIVEL ACCESO	4354.72

LOCALIZACIÓN

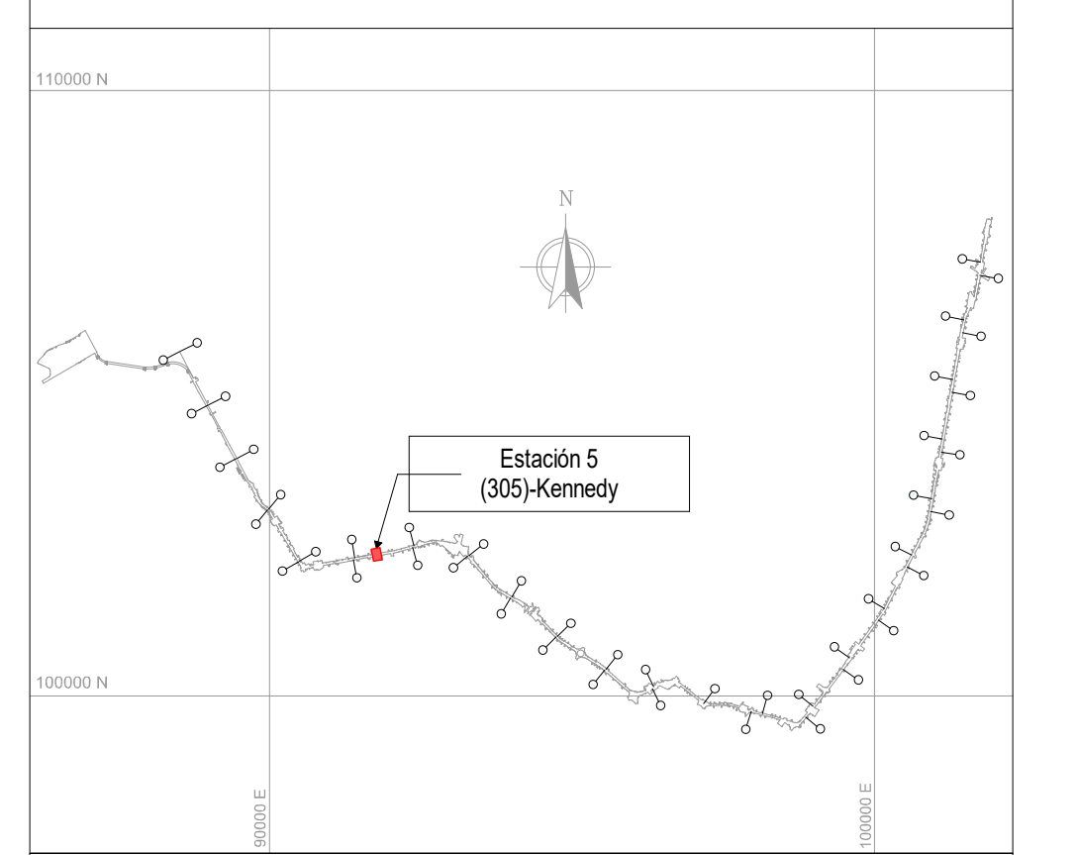

NOTAS

01 TODAS LAS DIMENSIONES ESTÁN CONFIGURADAS EN METROS A MENOS QUE SE INDIQUE UNA UNIDAD DE MEDIDA DIFERENTE.

02 TODAS LAS MEDIDAS, UBICACIÓN Y NIVELES DEBEN VERIFICARSE EN EL LUGAR DE CONSTRUCCIÓN.

03 EL NIVEL DE ACCESO AL EDIFICIO PL 01 CORRESPONDE AL +0,00 DE LA ESTACIÓN Y REFERENCIA AL NIVEL 2554.55 M.S.N.M

04 LOS NOMBRES ESPECIFICOS DE LAS ÁREAS PUEDEN SER CONSULTADAS EN EL PLANO NO. 3 Ó EN LAS VISTAS EN PLANTA.

05 LOS COLORES QUE SE MUESTRAN EN LOS PLANOS COMO PROYECCIÓN DE ELEMENTOS ARQUITECTÓNICOS COMO CUBIERTAS FACHADAS MUROS ETC. NO REPRESENTAN LA MATERIALIDAD Y REALIDAD DE ACABADOS DEL PROYECTO, SOLO SON INDICATIVOS PARA REALIZAR UNA CORRECTA LECTURA DE LA PLANIMETRÍA.

06 LAS ESCALERAS ELÉCTRICAS INDICAN SU SENTIDO CON LA SIGUIENTE NOMENCLATURA: "SUBE" Y "BAJA".

07 SE DEBEN REVISAR LOS NIVELES ESTRUCTURALES PARA NIVEL DE ACCESO PL_01 Y SUBNIVELES, PL_02 (INTERMEDIO), PL_03 (PLATAFORMA) CON LA PLANIMETRÍA DE PLACAS ESTRUCTURALES EN LOS ENTREGABLES L1T1-1300-405-CON-ED-EST-PL-0170, 0139, 0156, 0140, 0171, 0181, RESPECTIVAMENTE. EL NIVEL ESTRUCTURAL (NE) REFERENCIA LOS ESPACIOS DONDE SE DEBE ACONDICIONAR EL ACABADO DE PISO SEGÚN CORRESPONDA, CON LOS NIVELES DE PISO TERMINADO (NPT). LOS NIVELES PROYECTADOS DE EMPATE (NPE) EN LAS ÁREAS DE SERVICIOS ADICIONALES, REFERENCIAN LA ADECUACIÓN DE LOS DESNIVELES EN ESTAS ÁREAS; QUEDA COMO RESPONSABILIDAD DEL LOCATARIO DEFINIR Y ACONDICIONAR ESTE ACABADO DE PISO (NPE) EN LÍNEA CON EL NIVEL (NPT) DE ESPACIOS COLINDANTES. EL NIVEL ESTRUCTURAL (NE) SE ENCUENTRA A (- 0.10M) POR DEBAJO DE LOS NIVELES DE PISO TERMINADO (NPT) Y LOS NIVELES PROYECTADOS DE EMPATE (NPE) MARCADOS EN LA PLANIMETRÍA.

- ARQ_PL_00 = SÓTANO / NPT -6.75
- ARQ_PL_00.1 = ACCESO / NPT -0.45
- ARQ_PL_00.2 = ACCESO / NPT -0.35
- ARQ_PL_00.3 = ACCESO / NPT -0.30
- ARQ_PL_00.4 = ACCESO / NPT -0.20
- ARQ_PL_00.5 = ACCESO / NPT -0.10
- ARQ_PL_01 = ACCESO / NPT 0.00
- ARQ_PL_01.1 = ACCESO / NPT 0.10
- ARQ_PL_01.2 = ACCESS / NPT 0.15
- ARQ_PL_01.3 = ACCESS / NPT 0.20
- ARQ_PL_02 = INTERMEDIO / NPT 6.60
- ARQ_PL_02.2 = TOPE DE RIEL / NPT 14.20
- ARQ_PL_03 = PLATAFORMA / NPT 15.34
- ARQ_PL_04 = CUBIERTA EDIFICACIONES / NPT 21.94
- ARQ_PL_05 = CUBIERTA NAVE CENTRAL / NPT 24.59

CONVENCIONES

- - - -	LIMITE DE INTERVENCIÓN
- - - -	HUELLA APÉNDICE TÉCNICO
▬	MURO DIVISORIO
— — —	PROYECCIÓN NIVEL SUPERIOR
🟩	SERVICIOS ADICIONALES - ÁREA NO PAGA
🟩	SERVICIOS ADICIONALES - ÁREA PAGA
🟩	SERVICIO PÚBLICO
🟦	ZONA DE REFUGIO
🟥	ÁREA CULTURAL
🟪	ÁREA DE TAQUILLA BRT
🟨	ÁREA NO PAGA
🟦	ÁREA OPERATIVA
🟧	ÁREA PAGA
🟦	ÁREA PÚBLICA
⬜	ÁREA TÉCNICA

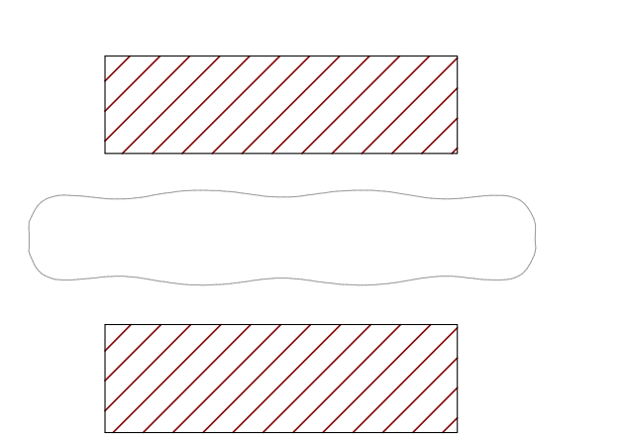

PLANO CLAVE ESTACIÓN 5

VÁLIDO PARA CONSTRUCCIÓN
20-03-26

No.	PLANOS DE REFERENCIA	REV.

No.	MODELO BIM DE REFERENCIA	REV.
1	L1T1-1100-205-CON-ED-EST-MO-0001.rvt	V00
2	L1T1-1100-206-CON-ED-EST-MO-0001.rvt	V00
3	L1T1-1100-305-CON-ED-EST-MO-0001.rvt	V00
4	L1T1-1150-205-CON-ED-EST-MO-0001.rvt	V00
5	L1T1-1150-206-CON-ED-EST-MO-0001.rvt	V00
6	L1T1-1150-305-CON-ED-EST-MO-0001.rvt	V00
7	L1T1-1200-305-CON-ED-EST-MO-0001.rvt	V00
8	L1T1-1300-405-CON-ED-EST-MO-0001.rvt	V00
9	L1T1-1300-405-CON-ED-EST-MO-0002.rvt	V00
10	L1T1-1310-405-CON-ED-EST-MO-0001.rvt	V00
11	L1T1-1410-305-CON-ED-MEC-MO-0001.rvt	V00
12	L1T1-1420-305-CON-ED-MEC-MO-0001.rvt	V00
13	L1T1-5160-305-CON-ED-EST-MO-0001.rvt	V00
14	L1T1-5160-305-CON-ED-ARC-MO-0001.rvt	V00
15	L1T1-5300-305-CON-ED-MEC-MO-0001.rvt	V00
16	L1T1-5600-305-CON-ED-INS-MO-0001.rvt	V00
17	L1T1-1330-405-CON-ED-ARQ-MO-0011.rvt	V00
18	L1T1-1330-405-CON-ED-ARQ-MO-0012.rvt	V00

No.	PAQUETE DE TRABAJO DE REFERENCIA	REV.
1	XREF-URBANISM_CONTEXT_ST05.rvt	
2	XREF-SECONDARY-STRUCTURE-ST05.rvt	

0 2 10m
1:200

METRO BOGOTÁ
Consorcio Consultores PMO Bogotá
CONSORCIO SUPERVISOR PLMB

DISEÑÓ:	REN ZHENHUA Licencia de Arq.nivel I (China): 1101735-614
APROBÓ:	DIEGO ERNESTO DUEÑAS Mat.: 25202-53876 CND
REVISÓ:	CARLOS MAURICIO BARRETO BARBOSA Mat.: A4012012-14139353
DIBUJÓ:	EQUIPO CHEC

REVISIÓN No.	FECHA	DESCRIPCIÓN	REVISÓ	APROBÓ	APROBACIÓN CLIENTE
V01	20/03/2026	EMITIDO PARA CONSTRUCCIÓN	C.M.B.B	D.E.D	
V00	07/04/2025	REVISIÓN NO OBJETADA - EMITIDO PARA CONSTRUCCIÓN	F.B.R	E.O.M	
VHH	20/09/2024	EMITIDO PARA REVISIÓN Y COMENTARIOS DEL CLIENTE E INTERVENTORÍA - INCLUYE COMENTARIOS /(AJUSTES V3)	F.B.R	E.O.M	
VGG	23/05/2024	EMITIDO PARA REVISIÓN Y COMENTARIOS DEL CLIENTE E INTERVENTORÍA - INCLUYE COMENTARIOS /(AJUSTES V2)	F.B.R	E.O.M	
VFF	03/05/2023	EMITIDO PARA REVISIÓN Y COMENTARIOS DEL CLIENTE E INTERVENTORÍA - INCLUYE COMENTARIOS /(AJUSTES)	J.E.M	M.B.M	
VEE	18/12/2022	EMITIDO PARA REVISIÓN Y COMENTARIOS DEL CLIENTE E INTERVENTORÍA - INCLUYE COMENTARIOS /(NO APLICA)	J.E.M	M.B.M	
VDD	11/11/2022	EMITIDO PARA REVISIÓN Y COMENTARIOS DEL CLIENTE E INTERVENTORÍA - INCLUYE COMENTARIOS /(90% ACCESOS)	J.E.M	M.B.M	
VCC	22/08/2022	EMITIDO PARA REVISIÓN Y COMENTARIOS DEL CLIENTE E INTERVENTORÍA - INCLUYE COMENTARIOS /(NO APLICA)	J.E.M	M.B.M	
VBB	06/12/2021	EMITIDO PARA REVISIÓN Y COMENTARIOS DEL CLIENTE E INTERVENTORÍA	J.E.M	M.B.M	
VA0	05/12/2021	EMITIDO PARA COMENTARIOS INTERNOS - EMISIÓN PRELIMINAR PARA COMENTARIOS	J.E.M	M.B.M	

METRO LÍNEA 1

METRO LÍNEA 1
CONTRATO DE CONCESIÓN No. 163 DE 2019

PROYECTO PRIMERA LÍNEA DEL METRO DE BOGOTÁ - TRAMO 1

DIRECTOR DE INTERVENTORÍA:
JAVIER DESCARGA N.
Mat.:25202-68697 CND

ESPECIALISTA INTERVENTORÍA:
CARLOS ALBERTO HOYOS SOTO
Mat.:A25072000-14251682

FECHA: MARZO 2026

INFRAESTRUCTURA VIAL

ARQUITECTURA

ESTACIÓN METRO 5 (KENNEDY)
GENERAL
VISTA EN PLANTA Y 3D - NIVEL ACCESO

PLANCHA No: L1T1-0000-305-CON-ED-ARQ-PL-0001_05_V01	ESCALA: INDICADA	REVISIÓN No.	PLANO No.
ARCHIVO: L1T1-0000-305-CON-ED-ARQ-MO-0001_V00.rvt	FECHA: DICIEMBRE 2021	V01	05 DE 96