L1T1-CON-CAL-FR-0120 - B1 : 1000x707mm

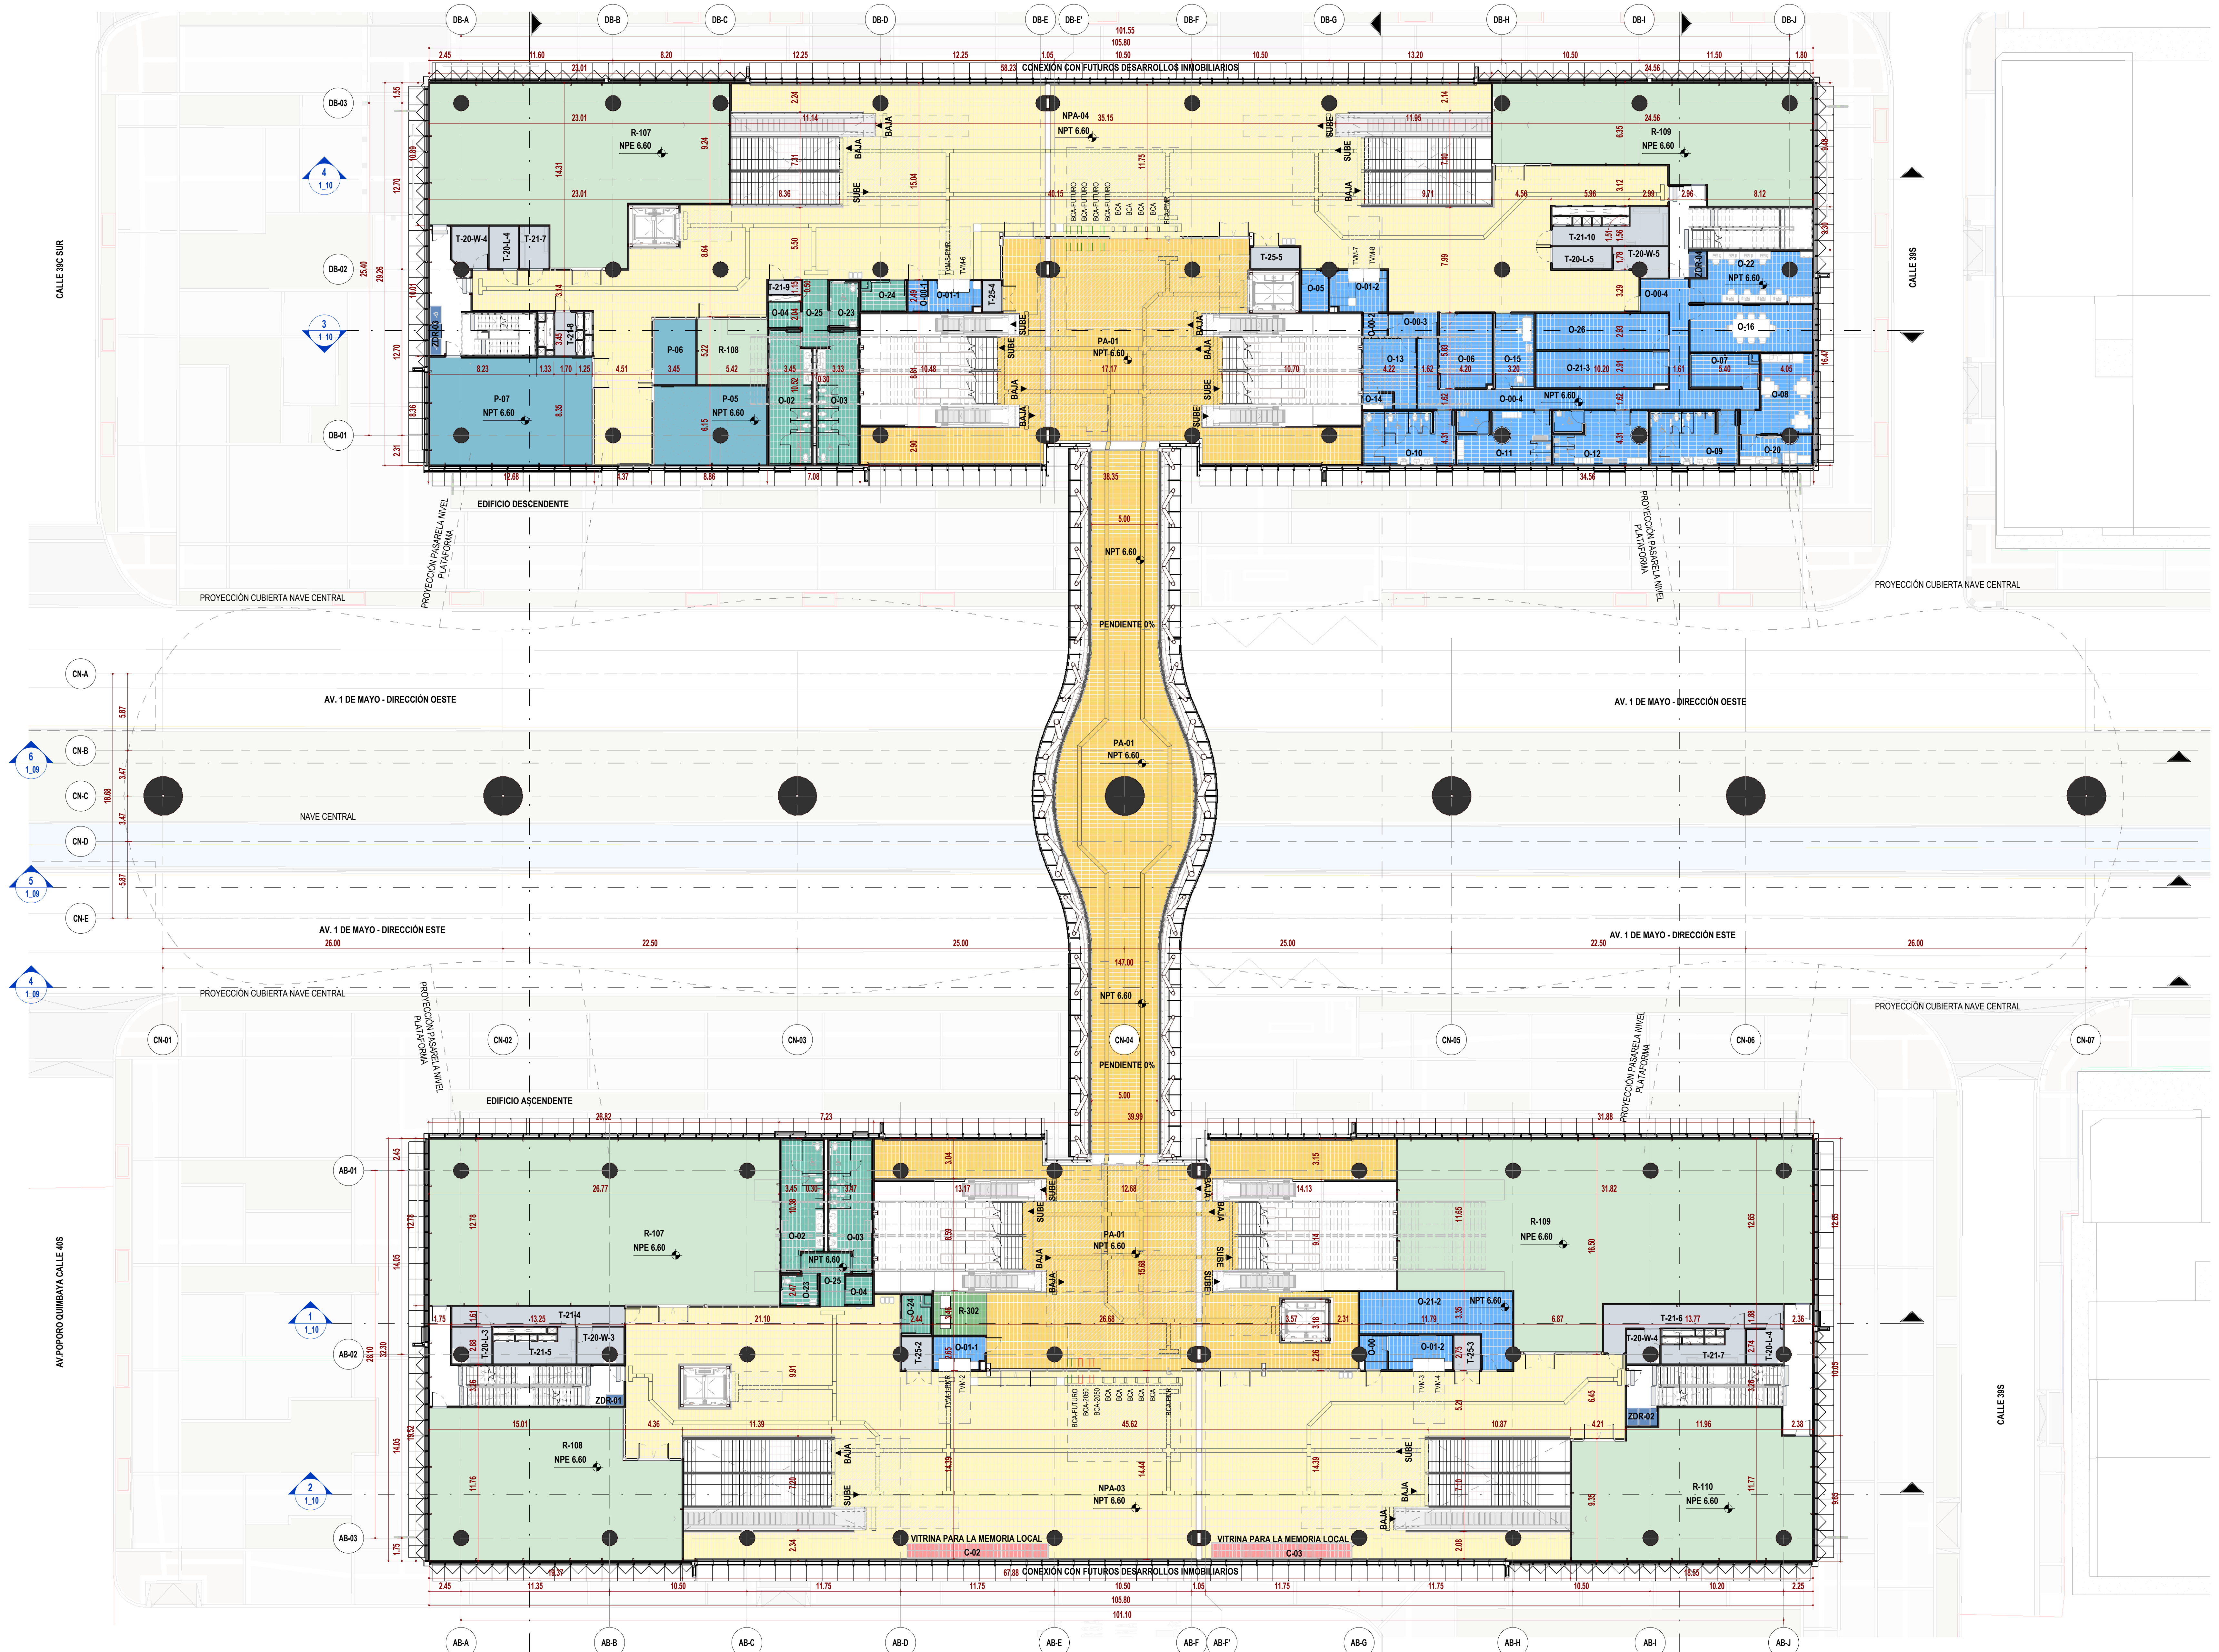
CONEXIÓN CON FUTUROS DESARROLLOS INMOBILIARIOS
CALLE 39C SUR
CALLE 39S
AV. POPORO QUIMBAYA CALLE 40S
R-107 NPE 6.60
R-108 NPE 6.60
R-109 NPE 6.60
R-110 NPE 6.60
NPA-04 NPT 6.60
NPA-03 NPT 6.60
PA-01 NPT 6.60
EDIFICIO DESCENDENTE
EDIFICIO ASCENDENTE
PROYECCIÓN CUBIERTA NAVE CENTRAL
AV. 1 DE MAYO - DIRECCIÓN OESTE
AV. 1 DE MAYO - DIRECCIÓN ESTE
NAVE CENTRAL
PENDIENTE 0%
SUBE
BAJA
VITRINA PARA LA MEMORIA LOCAL

② NIVEL INTERMEDIO_GENERAL
ESC : 1 : 200

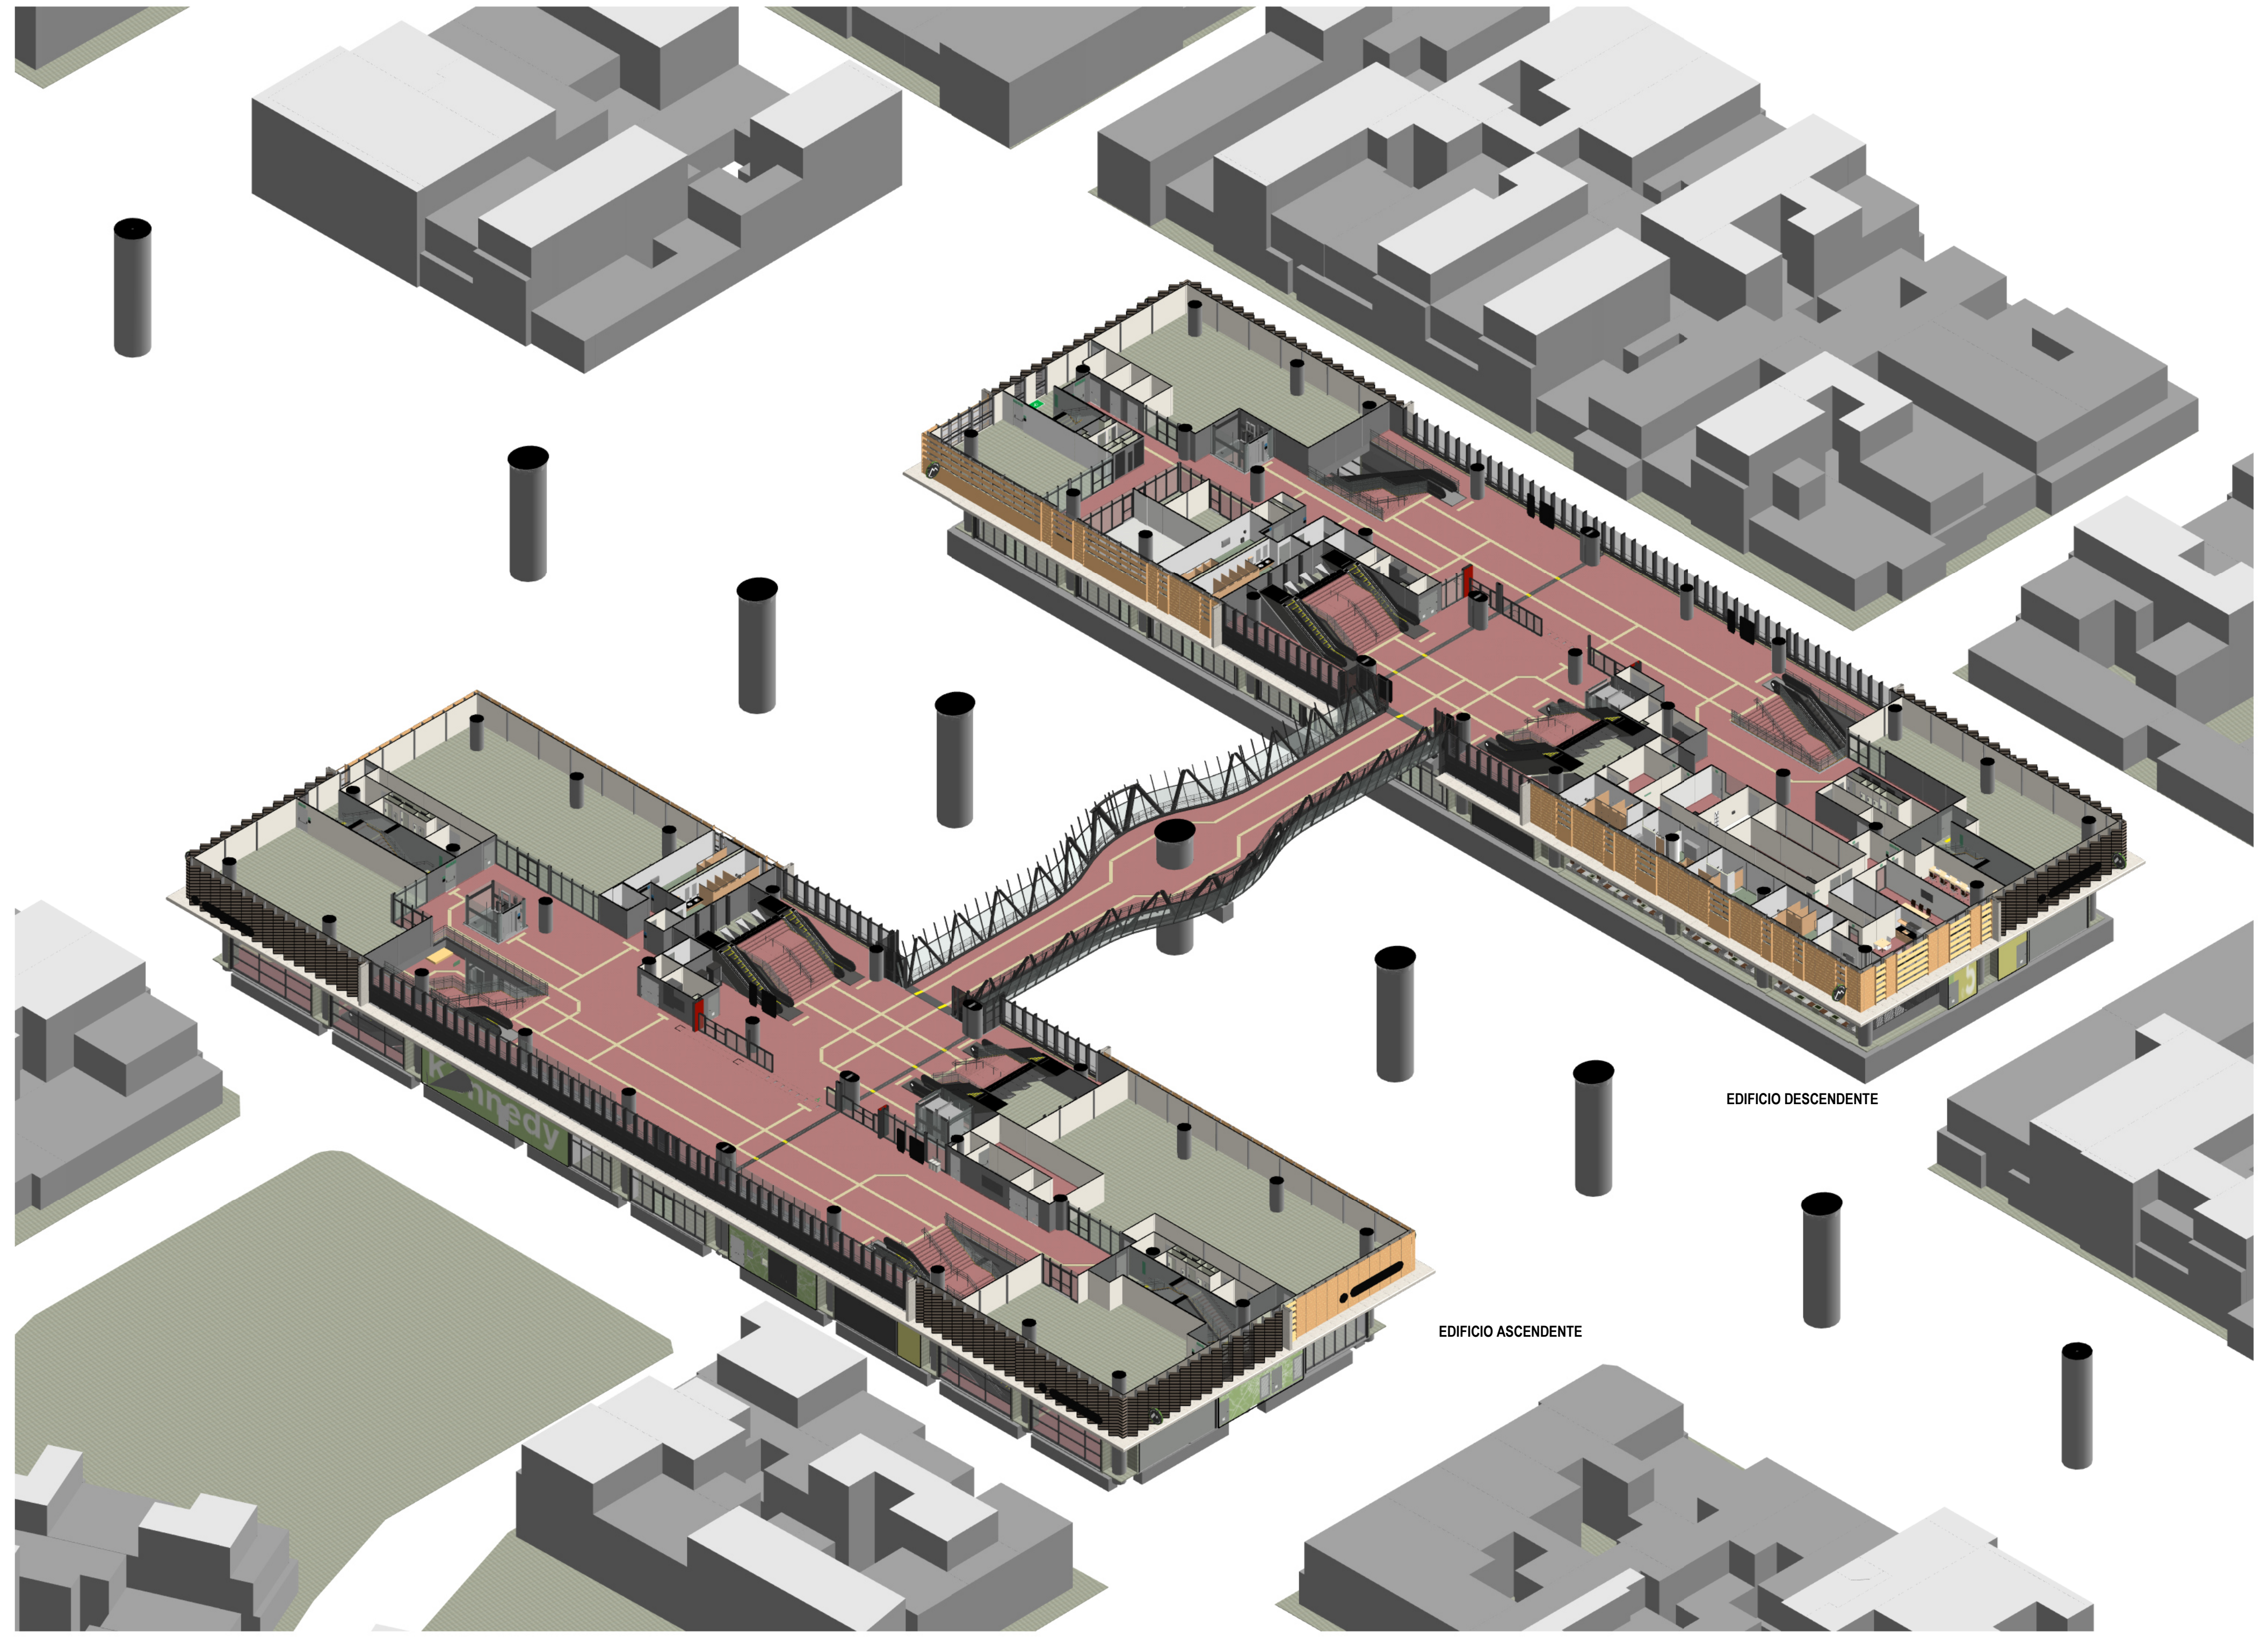

① 3D_NIVEL INTERMEDIO_GENERAL
ESC : N/A

TABLA DE ÁREAS ÚTILES (NIVEL INTERMEDIO)

CÓDIGO	NOMBRE	ÁREA (m²)	DEPARTAMENTO
EDIFICIO ASCENDENTE			
ARQ_PL_02_INTERMEDIO			
C-02	ÁREAS DE USO CULTURAL	12.78	ÁREA CULTURAL
C-03	ÁREAS DE USO CULTURAL	12.79	ÁREA CULTURAL
NPA-03	ÁREA NO PAGA	919.07	ÁREA NO PAGA
O-00	CIRCULACIÓN ÁREAS OPERATIVAS	4.62	ÁREA OPERATIVA
O-01-1	VENTA AUTOMÁTICA DE BOLETOS	9.52	ÁREA OPERATIVA
O-01-2	VENTA AUTOMÁTICA DE BOLETOS	12.92	ÁREA OPERATIVA
O-02	BAÑOS PÚBLICOS DE HOMBRES	30.42	SERVICIO PÚBLICO
O-03	BAÑOS PÚBLICOS DE MUJERES	30.54	SERVICIO PÚBLICO
O-04	CONTROL DE ACCESO BAÑOS PÚBLICOS	4.44	SERVICIO PÚBLICO
O-21-2	ALMACENAMIENTO DE LA ESTACIÓN	43.67	ÁREA OPERATIVA
O-23	BAÑO PÚBLICO - FAMILIAR	6.70	SERVICIO PÚBLICO
O-24	CUARTO DE LIMPIEZA DE BAÑOS PÚBLICOS	6.88	SERVICIO PÚBLICO
O-25	BAÑO PÚBLICO - CORREDOR OPERACIONAL	10.32	SERVICIO PÚBLICO
PA-01	ÁREA PAGA	372.36	ÁREA PAGA
R-107	SERVICIOS ADICIONALES - ÁREA DE SERVICIO	334.06	SERVICIOS ADICIONALES - ÁREA NO PAGA
R-108	SERVICIOS ADICIONALES - ÁREA DE SERVICIO	203.57	SERVICIOS ADICIONALES - ÁREA NO PAGA
R-109	SERVICIOS ADICIONALES - ÁREA DE SERVICIO	410.16	SERVICIOS ADICIONALES - ÁREA NO PAGA
R-110	SERVICIOS ADICIONALES - ÁREA DE SERVICIO	192.59	SERVICIOS ADICIONALES - ÁREA NO PAGA
R-302	SERVICIOS ADICIONALES - MÁQUINAS EXPENDEDORAS/CAJEROS AUTOMÁTICOS	13.43	SERVICIOS ADICIONALES - ÁREA PAGA
T-20-L-3	MEDIDORES (LUZ)	6.86	ÁREA TÉCNICA
T-20-L-4	MEDIDORES (LUZ)	6.70	ÁREA TÉCNICA
T-20-W-3	MEDIDORES (AGUA)	8.50	ÁREA TÉCNICA
T-20-W-4	MEDIDORES (AGUA)	6.34	ÁREA TÉCNICA
T-21-4	ÁREA DE INSPECCIÓN	19.70	ÁREA TÉCNICA
T-21-5	ÁREA DE INSPECCIÓN	11.84	ÁREA TÉCNICA
T-21-6	ÁREA DE INSPECCIÓN	27.46	ÁREA TÉCNICA
T-21-7	ÁREA DE INSPECCIÓN	10.85	ÁREA TÉCNICA
T-25-2	NODO DE ACCESO DE TELECOMUNICACIONES	5.33	ÁREA TÉCNICA
T-25-3	NODO DE ACCESO DE TELECOMUNICACIONES	5.21	ÁREA TÉCNICA
ZDR-01	ZONA DE REFUGIO (PMR)	1.22	ZONA DE REFUGIO
ZDR-02	ZONA DE REFUGIO (PMR)	3.16	ZONA DE REFUGIO
EDIFICIO DESCENDENTE			
ARQ_PL_02_INTERMEDIO			
NPA-04	ÁREA NO PAGA	909.40	ÁREA NO PAGA
O-00-1	CIRCULACIÓN ÁREAS OPERATIVAS	3.52	ÁREA OPERATIVA
O-00-2	CIRCULACIÓN ÁREAS OPERATIVAS	3.33	ÁREA OPERATIVA
O-00-3	CIRCULACIÓN ÁREAS OPERATIVAS	6.72	ÁREA OPERATIVA
O-00-4	CIRCULACIÓN ÁREAS OPERATIVAS	63.47	ÁREA OPERATIVA
O-01-1	VENTA AUTOMÁTICA DE BOLETOS	9.02	ÁREA OPERATIVA
O-01-2	VENTA AUTOMÁTICA DE BOLETOS	13.19	ÁREA OPERATIVA
O-02	BAÑOS PÚBLICOS DE HOMBRES	32.66	SERVICIO PÚBLICO
O-03	BAÑOS PÚBLICOS DE MUJERES	30.89	SERVICIO PÚBLICO
O-04	CONTROL DE ACCESO BAÑOS PÚBLICOS	4.80	SERVICIO PÚBLICO
O-05	LOCAL DE INFORMACIÓN	6.35	ÁREA OPERATIVA
O-06	OFICINA DEL SUPERVISOR DE LA ESTACIÓN	22.71	ÁREA OPERATIVA
O-07	CUARTO DE LIMPIEZA	13.50	ÁREA OPERATIVA
O-08	SALA DE DESCANSO PARA EMPLEADOS	26.53	ÁREA OPERATIVA
O-09	BAÑOS EMPLEADOS HOMBRES	26.86	ÁREA OPERATIVA
O-10	BAÑOS EMPLEADOS MUJERES	27.93	ÁREA OPERATIVA
O-11	VESTIDORES EMPLEADOS HOMBRES	27.86	ÁREA OPERATIVA
O-12	VESTIDORES EMPLEADOS MUJERES	27.99	ÁREA OPERATIVA
O-13	LOCAL DE POLICÍA	18.96	ÁREA OPERATIVA
O-14	CALABOZO	2.75	ÁREA OPERATIVA
O-15	LOCAL PRIMEROS AUXILIOS	17.63	ÁREA OPERATIVA
O-16	SALA DE REUNIONES	33.75	ÁREA OPERATIVA
O-20	SALA DE LACTANCIA	11.74	ÁREA OPERATIVA
O-21-3	ALMACENAMIENTO DE LA ESTACIÓN	27.91	ÁREA OPERATIVA
O-22	OFICINA DE MANTENIMIENTO	32.78	ÁREA OPERATIVA
O-23	BAÑO PÚBLICO - FAMILIAR	7.64	SERVICIO PÚBLICO
O-24	CUARTO DE LIMPIEZA DE BAÑOS PÚBLICOS	8.00	SERVICIO PÚBLICO
O-25	BAÑO PÚBLICO - CORREDOR OPERACIONAL	10.13	SERVICIO PÚBLICO
O-26	ALMACENAMIENTO DE BASURAS METRO	28.27	ÁREA OPERATIVA
P-05	BIBLIOMETRO	50.24	ÁREA PÚBLICA
P-06	ESPACIO IPES (INSTITUTO PARA LA ECONOMÍA SOCIAL)	15.66	ÁREA PÚBLICA
P-07	SALÓN MÚLTIPLE EMB	100.11	ÁREA PÚBLICA
PA-01	ÁREA PAGA	327.76	ÁREA PAGA
R-107	SERVICIOS ADICIONALES - ÁREA DE SERVICIO	248.99	SERVICIOS ADICIONALES - ÁREA NO PAGA
R-108	SERVICIOS ADICIONALES - ÁREA DE SERVICIO	26.35	SERVICIOS ADICIONALES - ÁREA NO PAGA
R-109	SERVICIOS ADICIONALES - ÁREA DE SERVICIO	176.77	SERVICIOS ADICIONALES - ÁREA NO PAGA
T-20-L-4	MEDIDORES (LUZ)	7.10	ÁREA TÉCNICA
T-20-L-5	MEDIDORES (LUZ)	7.46	ÁREA TÉCNICA
T-20-W-4	MEDIDORES (AGUA)	8.28	ÁREA TÉCNICA
T-20-W-5	MEDIDORES (AGUA)	7.64	ÁREA TÉCNICA
T-21-7	ÁREA DE INSPECCIÓN	7.18	ÁREA TÉCNICA
T-21-8	ÁREA DE INSPECCIÓN	5.27	ÁREA TÉCNICA
T-21-9	ÁREA DE INSPECCIÓN	2.54	ÁREA TÉCNICA
T-21-10	ÁREA DE INSPECCIÓN	17.11	ÁREA TÉCNICA
T-25-4	NODO DE ACCESO DE TELECOMUNICACIONES	3.33	ÁREA TÉCNICA
T-25-5	NODO DE ACCESO DE TELECOMUNICACIONES	5.92	ÁREA TÉCNICA
ZDR-03	ZONA DE REFUGIO (PMR)	3.42	ZONA DE REFUGIO
ZDR-04	ZONA DE REFUGIO (PMR)	2.71	ZONA DE REFUGIO
NAVE CENTRAL			
ARQ_PL_02_INTERMEDIO			
PA-01	ÁREA PAGA	329.55	ÁREA PAGA
TOTAL NIVEL INTERMEDIO		5553.68	

TABLA DE ÁREAS ÚTILES POR DEPARTAMENTO (NIVEL INTERMEDIO)

DEPARTAMENTO	ÁREA (m²)
EDIFICIO ASCENDENTE	
ARQ_PL_02_INTERMEDIO	
SERVICIO PÚBLICO	89.29
SERVICIOS ADICIONALES - ÁREA NO PAGA	1140.37
SERVICIOS ADICIONALES - ÁREA PAGA	13.43
ZONA DE REFUGIO	4.38
ÁREA CULTURAL	25.57
ÁREA NO PAGA	919.07
ÁREA OPERATIVA	70.73
ÁREA PAGA	372.36
ÁREA TÉCNICA	108.79
EDIFICIO DESCENDENTE	
ARQ_PL_02_INTERMEDIO	
SERVICIO PÚBLICO	94.13
SERVICIOS ADICIONALES - ÁREA NO PAGA	452.11
ZONA DE REFUGIO	6.13
ÁREA NO PAGA	909.40
ÁREA OPERATIVA	452.78
ÁREA PAGA	327.76
ÁREA PÚBLICA	166.01
ÁREA TÉCNICA	71.83
NAVE CENTRAL	
ARQ_PL_02_INTERMEDIO	
ÁREA PAGA	329.55
TOTAL NIVEL INTERMEDIO	5553.68

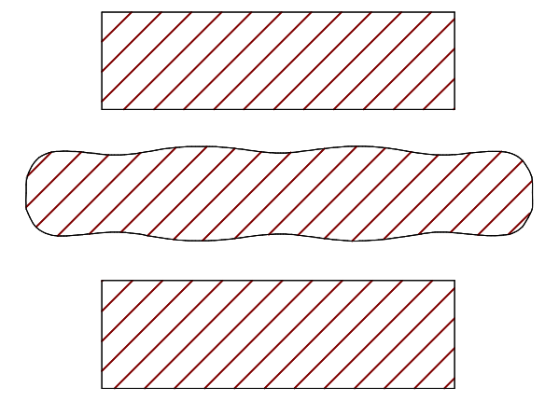

PLANO CLAVE ESTACIÓN 5
VÁLIDO PARA CONSTRUCCIÓN
20-03-26

LOCALIZACIÓN

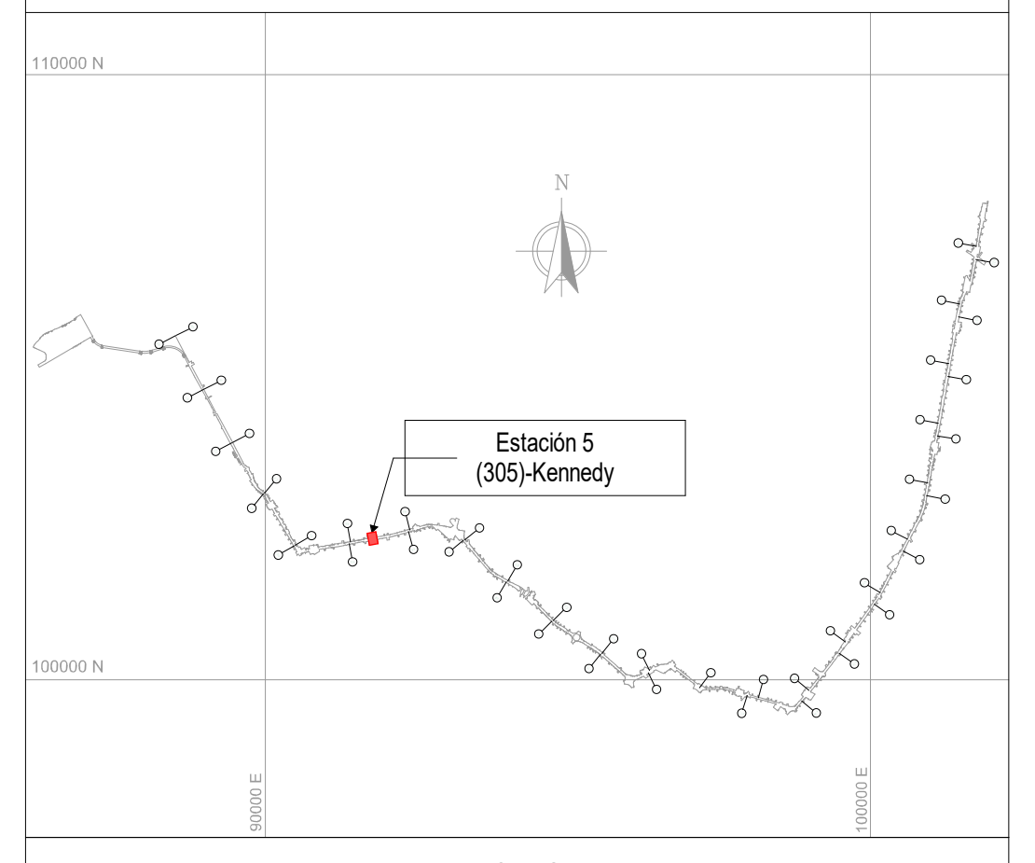

NOTAS

01. TODAS LAS DIMENSIONES ESTÁN CONFIGURADAS EN METROS A MENOS QUE SE INDIQUE UNA UNIDAD DE MEDIDA DIFERENTE.
02. TODAS LAS MEDIDAS, UBICACIÓN Y NIVELES DEBEN VERIFICARSE EN EL LUGAR DE CONSTRUCCIÓN.
03. EL NIVEL DE ACCESO AL EDIFICIO PL 01 CORRESPONDE AL +0,00 DE LA ESTACIÓN Y REFERENCIA AL NIVEL 2554.55 M.S.N.M
04. LOS NOMBRES ESPECIFICOS DE LAS ÁREAS PUEDEN SER CONSULTADAS EN EL PLANO NO. 3 Ó EN LAS VISTAS EN PLANTA.
05. LOS COLORES QUE SE MUESTRAN EN LOS PLANOS COMO PROYECCIÓN DE ELEMENTOS ARQUITECTÓNICOS COMO CUBIERTAS FACHADAS MUROS ETC. NO REPRESENTAN LA MATERIALIDAD Y REALIDAD DE ACABADOS DEL PROYECTO, SOLO SON INDICATIVOS PARA REALIZAR UNA CORRECTA LECTURA DE LA PLANIMETRÍA.
06. LAS ESCALERAS ELÉCTRICAS INDICAN SU SENTIDO CON LA SIGUIENTE NOMENCLATURA: "SUBE" Y "BAJA".
07. SE DEBEN REVISAR LOS NIVELES ESTRUCTURALES PARA NIVEL DE ACCESO PL_01 Y SUBNIVELES, PL_02 (INTERMEDIO), PL_03 (PLATAFORMA) CON LA PLANIMETRÍA DE PLACAS ESTRUCTURALES EN LOS ENTREGABLES L1T1-1300-405-CON-ED-EST-PL-0170, 0139, 0156, 0140, 0171, 0181, RESPECTIVAMENTE. EL NIVEL ESTRUCTURAL (NE) REFERENCIA LOS ESPACIOS DONDE SE DEBE ACONDICIONAR EL ACABADO DE PISO SEGÚN CORRESPONDA, CON LOS NIVELES DE PISO TERMINADO (NPT). LOS NIVELES PROYECTADOS DE EMPATE (NPE) EN LAS ÁREAS DE SERVICIOS ADICIONALES, REFERENCIAN LA ADECUACIÓN DE LOS DESNIVELES EN ESTAS ÁREAS; QUEDA COMO RESPONSABILIDAD DEL LOCATARIO DEFINIR Y ACONDICIONAR ESTE ACABADO DE PISO (NPE) EN LÍNEA CON EL NIVEL (NPT) DE ESPACIOS COLINDANTES. EL NIVEL ESTRUCTURAL (NE) SE ENCUENTRA A (- 0.10M) POR DEBAJO DE LOS NIVELES DE PISO TERMINADO (NPT) Y LOS NIVELES PROYECTADOS DE EMPATE (NPE) MARCADOS EN LA PLANIMETRÍA.

- ARQ_PL_00 = SÓTANO / NPT -6.75
- ARQ_PL_00.1 = ACCESO / NPT -0.45
- ARQ_PL_00.2 = ACCESO / NPT -0.35
- ARQ_PL_00.3 = ACCESO / NPT -0.30
- ARQ_PL_00.4 = ACCESO / NPT -0.20
- ARQ_PL_00.5 = ACCESO / NPT -0.10
- ARQ_PL_01 = ACCESO / NPT 0.00
- ARQ_PL_01.1 = ACCESO / NPT 0.10
- ARQ_PL_01.2 = ACCESS / NPT 0.15
- ARQ_PL_01.3 = ACCESS / NPT 0.20
- ARQ_PL_02 = INTERMEDIO / NPT 6.60
- ARQ_PL_02.2 = TOPE DE RIEL / NPT 14.20
- ARQ_PL_03 = PLATAFORMA / NPT 15.34
- ARQ_PL_04 = CUBIERTA EDIFICACIONES / NPT 21.94
- ARQ_PL_05 = CUBIERTA NAVE CENTRAL / NPT 24.59

CONVENCIONES

▬ ▬ ▬	LIMITE DE INTERVENCIÓN
‒ ‒ ‒	HUELLA APÉNDICE TÉCNICO
■	MURO DIVISORIO
— — —	PROYECCIÓN NIVEL SUPERIOR
🟩	SERVICIOS ADICIONALES - ÁREA NO PAGA
🟩	SERVICIOS ADICIONALES - ÁREA PAGA
🟩	SERVICIO PÚBLICO
🟦	ZONA DE REFUGIO
🟥	ÁREA CULTURAL
🟪	ÁREA DE TAQUILLA BRT
🟨	ÁREA NO PAGA
🟦	ÁREA OPERATIVA
🟧	ÁREA PAGA
🟦	ÁREA PÚBLICA
⬜	ÁREA TÉCNICA

No.	PLANOS DE REFERENCIA	REV.

No.	MODELO BIM DE REFERENCIA	REV.
1	L1T1-1100-205-CON-ED-EST-MO-0001.rvt	V00
2	L1T1-1100-206-CON-ED-EST-MO-0001.rvt	V00
3	L1T1-1100-305-CON-ED-EST-MO-0001.rvt	V00
4	L1T1-1150-205-CON-ED-EST-MO-0001.rvt	V00
5	L1T1-1150-206-CON-ED-EST-MO-0001.rvt	V00
6	L1T1-1150-305-CON-ED-EST-MO-0001.rvt	V00
7	L1T1-1200-305-CON-ED-EST-MO-0001.rvt	V00
8	L1T1-1300-405-CON-ED-EST-MO-0001.rvt	V00
9	L1T1-1300-405-CON-ED-EST-MO-0002.rvt	V00
10	L1T1-1310-405-CON-ED-EST-MO-0001.rvt	V00
11	L1T1-1410-305-CON-ED-MEC-MO-0001.rvt	V00
12	L1T1-1420-305-CON-ED-MEC-MO-0001.rvt	V00
13	L1T1-5160-305-CON-ED-EST-MO-0001.rvt	V00
14	L1T1-5160-305-CON-ED-ARC-MO-0001.rvt	V00
15	L1T1-5300-305-CON-ED-MEC-MO-0001.rvt	V00
16	L1T1-5600-305-CON-ED-INS-MO-0001.rvt	V00
17	L1T1-1330-405-CON-ED-ARQ-MO-0011.rvt	V00
18	L1T1-1330-405-CON-ED-ARQ-MO-0012.rvt	V00

No.	PAQUETE DE TRABAJO DE REFERENCIA	REV.
1	XREF-URBANISM_CONTEXT_ST05.rvt	
2	XREF-SECONDARY-STRUCTURE-ST05.rvt	

0 2 10m
1:200

METRO
GCS Consorcio Constructor PMB Bogotá
CONSORCIO SUPERVISOR PLMB
HEC

DISEÑÓ:
REN ZHENHUA
Licencia de Arq.nivel I (China): 1101735-614

REVISÓ:
CARLOS MAURICIO BARRETO BARBOSA
Mat.: A4012012-14139353

APROBÓ:
DIEGO ERNESTO DUEÑAS
Mat.: 25202-53876 CND

DIBUJÓ:
EQUIPO CHEC

REVISIÓN No.	FECHA	DESCRIPCIÓN	REVISÓ	APROBÓ	APROBACIÓN CLIENTE
V01	20/03/2026	EMITIDO PARA CONSTRUCCIÓN	C.M.B.B	D.E.D	
V00	07/04/2025	REVISIÓN NO OBJETADA - EMITIDO PARA CONSTRUCCIÓN	F.B.R	E.O.M	
VHH	20/09/2024	EMITIDO PARA REVISIÓN Y COMENTARIOS DEL CLIENTE E INTERVENTORÍA - INCLUYE COMENTARIOS /(AJUSTES V3)	F.B.R	E.O.M	
VGG	23/05/2024	EMITIDO PARA REVISIÓN Y COMENTARIOS DEL CLIENTE E INTERVENTORÍA - INCLUYE COMENTARIOS /(AJUSTES V2)	F.B.R	E.O.M	
VFF	03/05/2023	EMITIDO PARA REVISIÓN Y COMENTARIOS DEL CLIENTE E INTERVENTORÍA - INCLUYE COMENTARIOS /(AJUSTES)	J.E.M	M.B.M	
VEE	18/12/2022	EMITIDO PARA REVISIÓN Y COMENTARIOS DEL CLIENTE E INTERVENTORÍA - INCLUYE COMENTARIOS /(NO APLICA)	J.E.M	M.B.M	
VDD	11/11/2022	EMITIDO PARA REVISIÓN Y COMENTARIOS DEL CLIENTE E INTERVENTORÍA - INCLUYE COMENTARIOS /(90% ACCESOS)	J.E.M	M.B.M	
VCC	22/08/2022	EMITIDO PARA REVISIÓN Y COMENTARIOS DEL CLIENTE E INTERVENTORÍA - INCLUYE COMENTARIOS /(NO APLICA)	J.E.M	M.B.M	
VBB	06/12/2021	EMITIDO PARA REVISIÓN Y COMENTARIOS DEL CLIENTE E INTERVENTORÍA	J.E.M	M.B.M	
VA0	05/12/2021	EMITIDO PARA COMENTARIOS INTERNOS - EMISIÓN PRELIMINAR PARA COMENTARIOS	J.E.M	M.B.M	

METRO LÍNEA 1

METRO LÍNEA 1
CONTRATO DE CONCESIÓN No. 163 DE 2019

PROYECTO PRIMERA LÍNEA DEL METRO DE BOGOTÁ - TRAMO 1

DIRECTOR DE INTERVENTORÍA:
JAVIER DESCARGA N.
Mat.:25202-68697 CND

ESPECIALISTA INTERVENTORÍA:
CARLOS ALBERTO HOYOS SOTO
Mat.:A25072000-14251682

FECHA:
MARZO 2026

INFRAESTRUCTURA VIAL
ARQUITECTURA
ESTACIÓN METRO 5 (KENNEDY)
GENERAL
VISTA EN PLANTA Y 3D - NIVEL INTERMEDIO

PLANCHA No: L1T1-0000-305-CON-ED-ARQ-PL-0001_06_V01
ARCHIVO: L1T1-0000-305-CON-ED-ARQ-MO-0001_V00.rvt
ESCALA: INDICADA
FECHA: DICIEMBRE 2021
REVISIÓN No. V01
PLANO No. 06 DE 96