L1T1-CON-CAL-FR-0120 - B1 : 1000x707mm

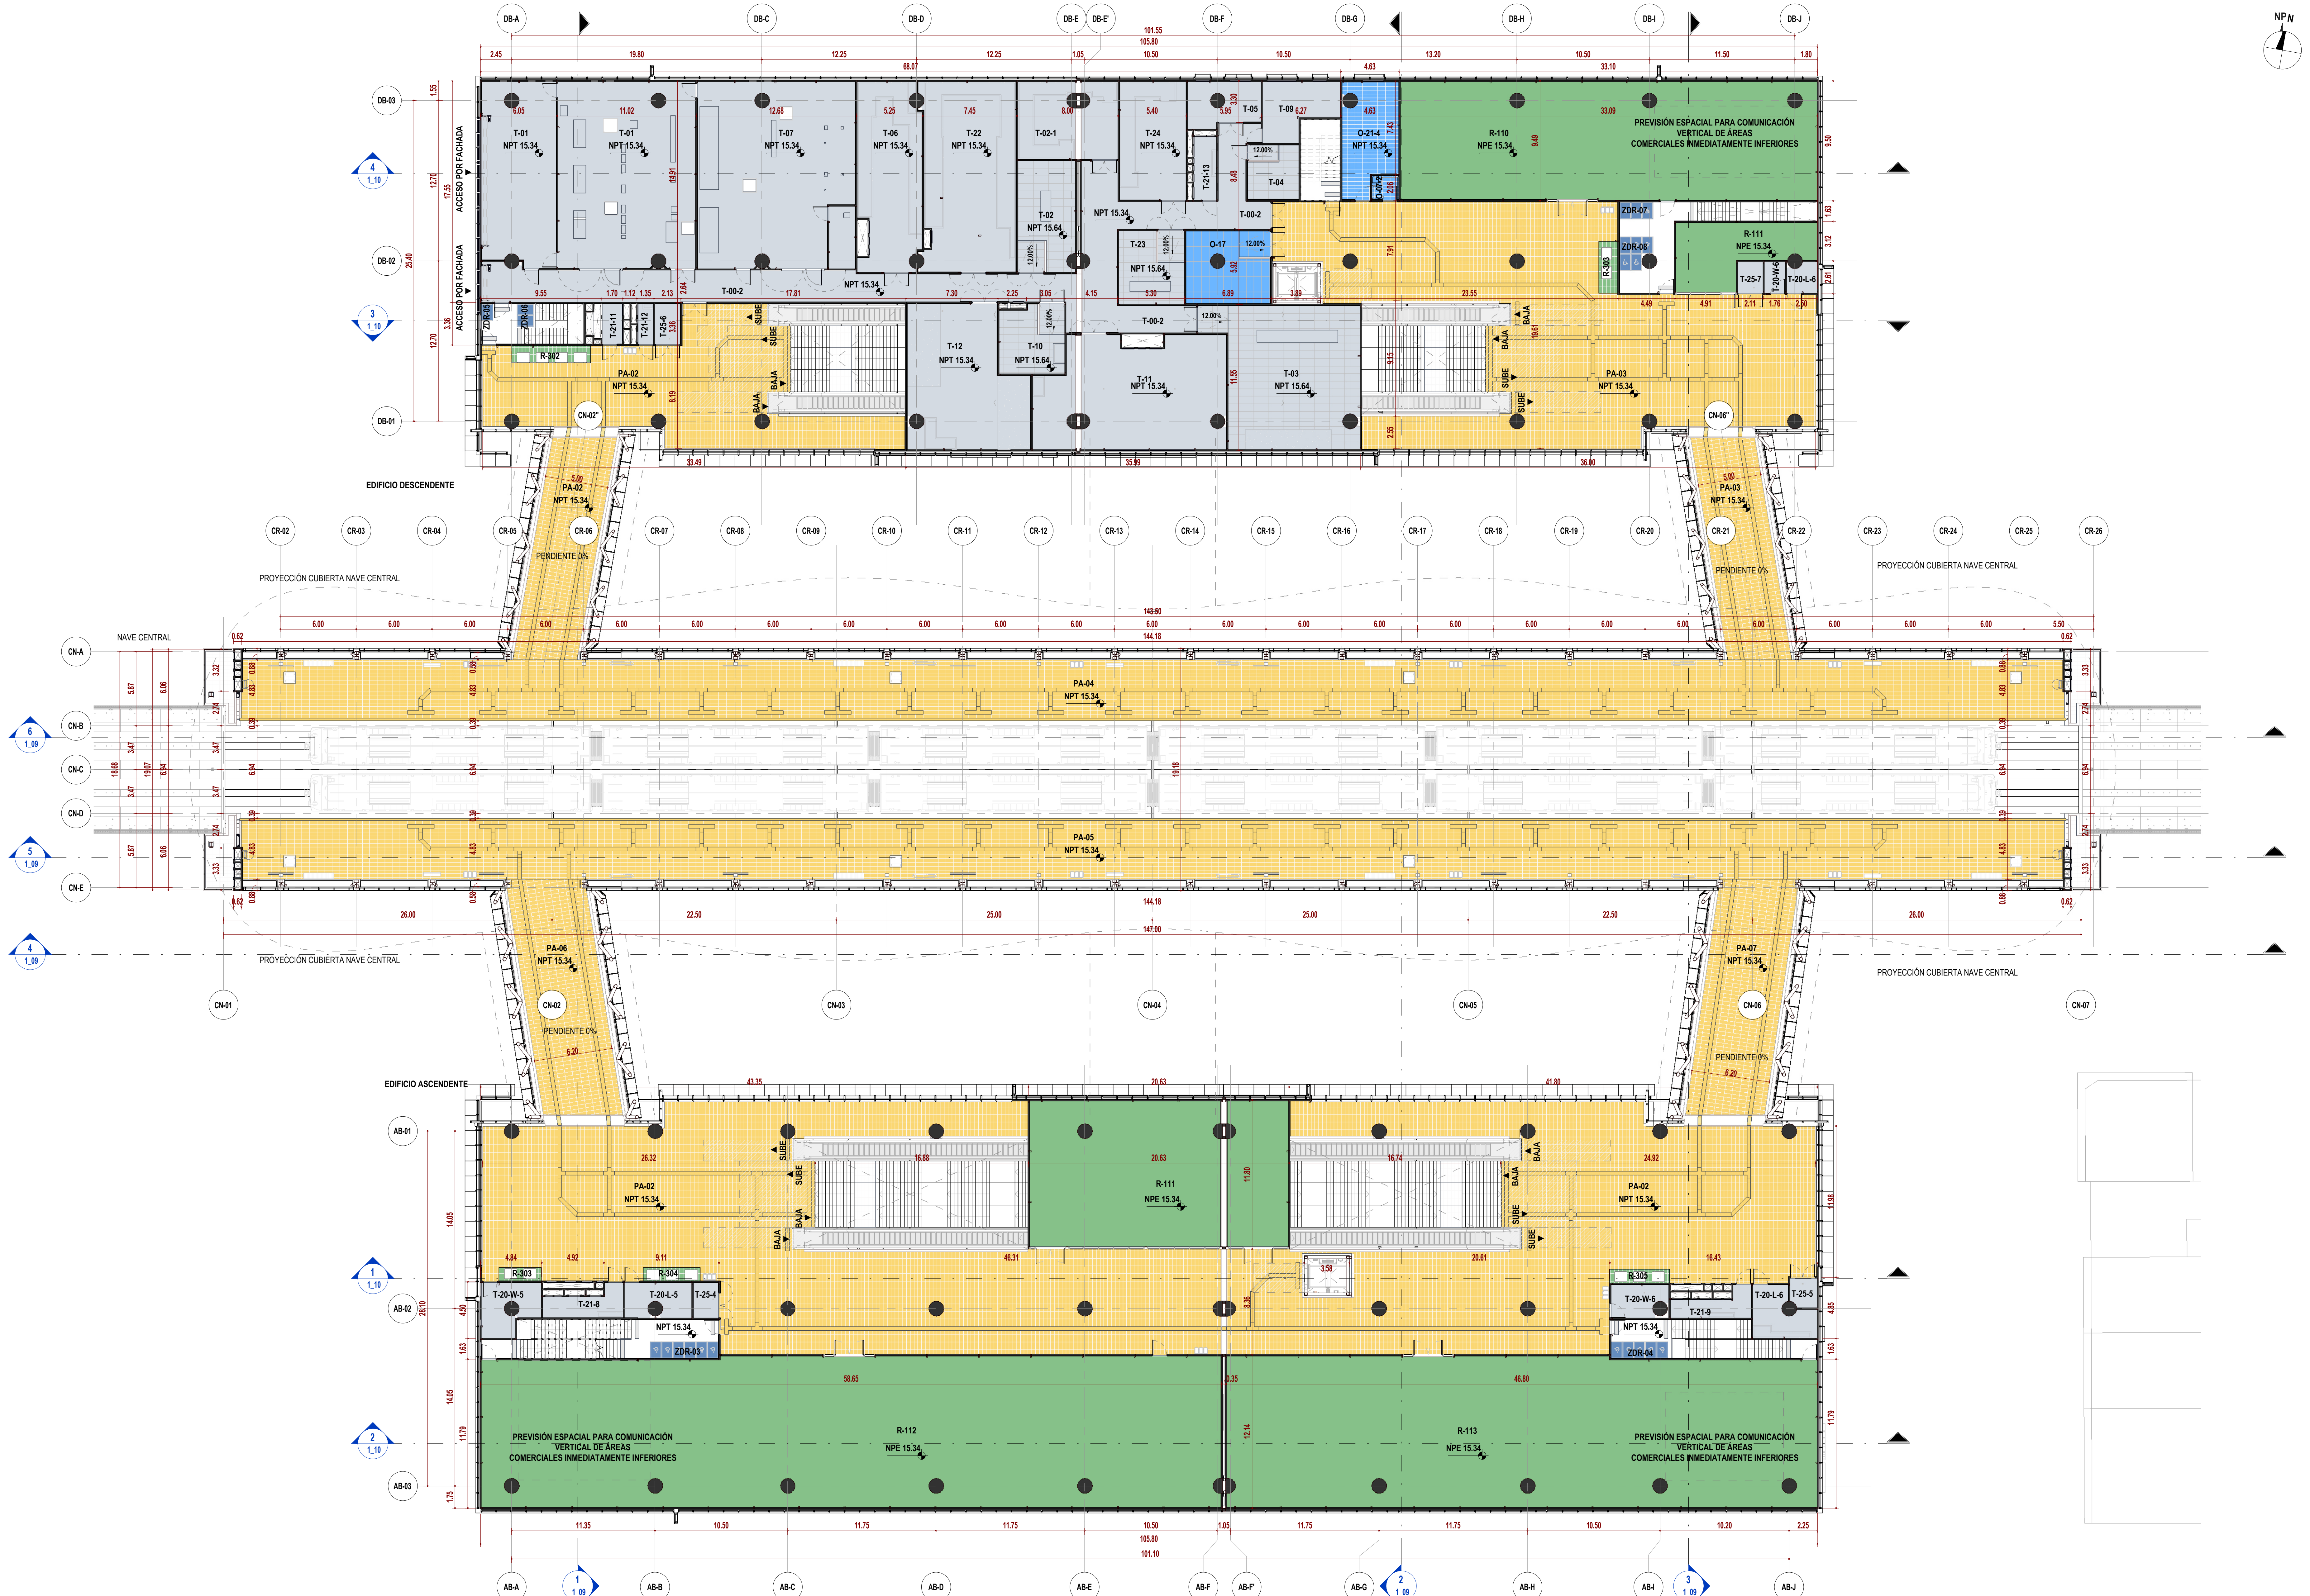

2 **NIVEL PLATAFORMA_GENERAL**
ESC : 1 : 200

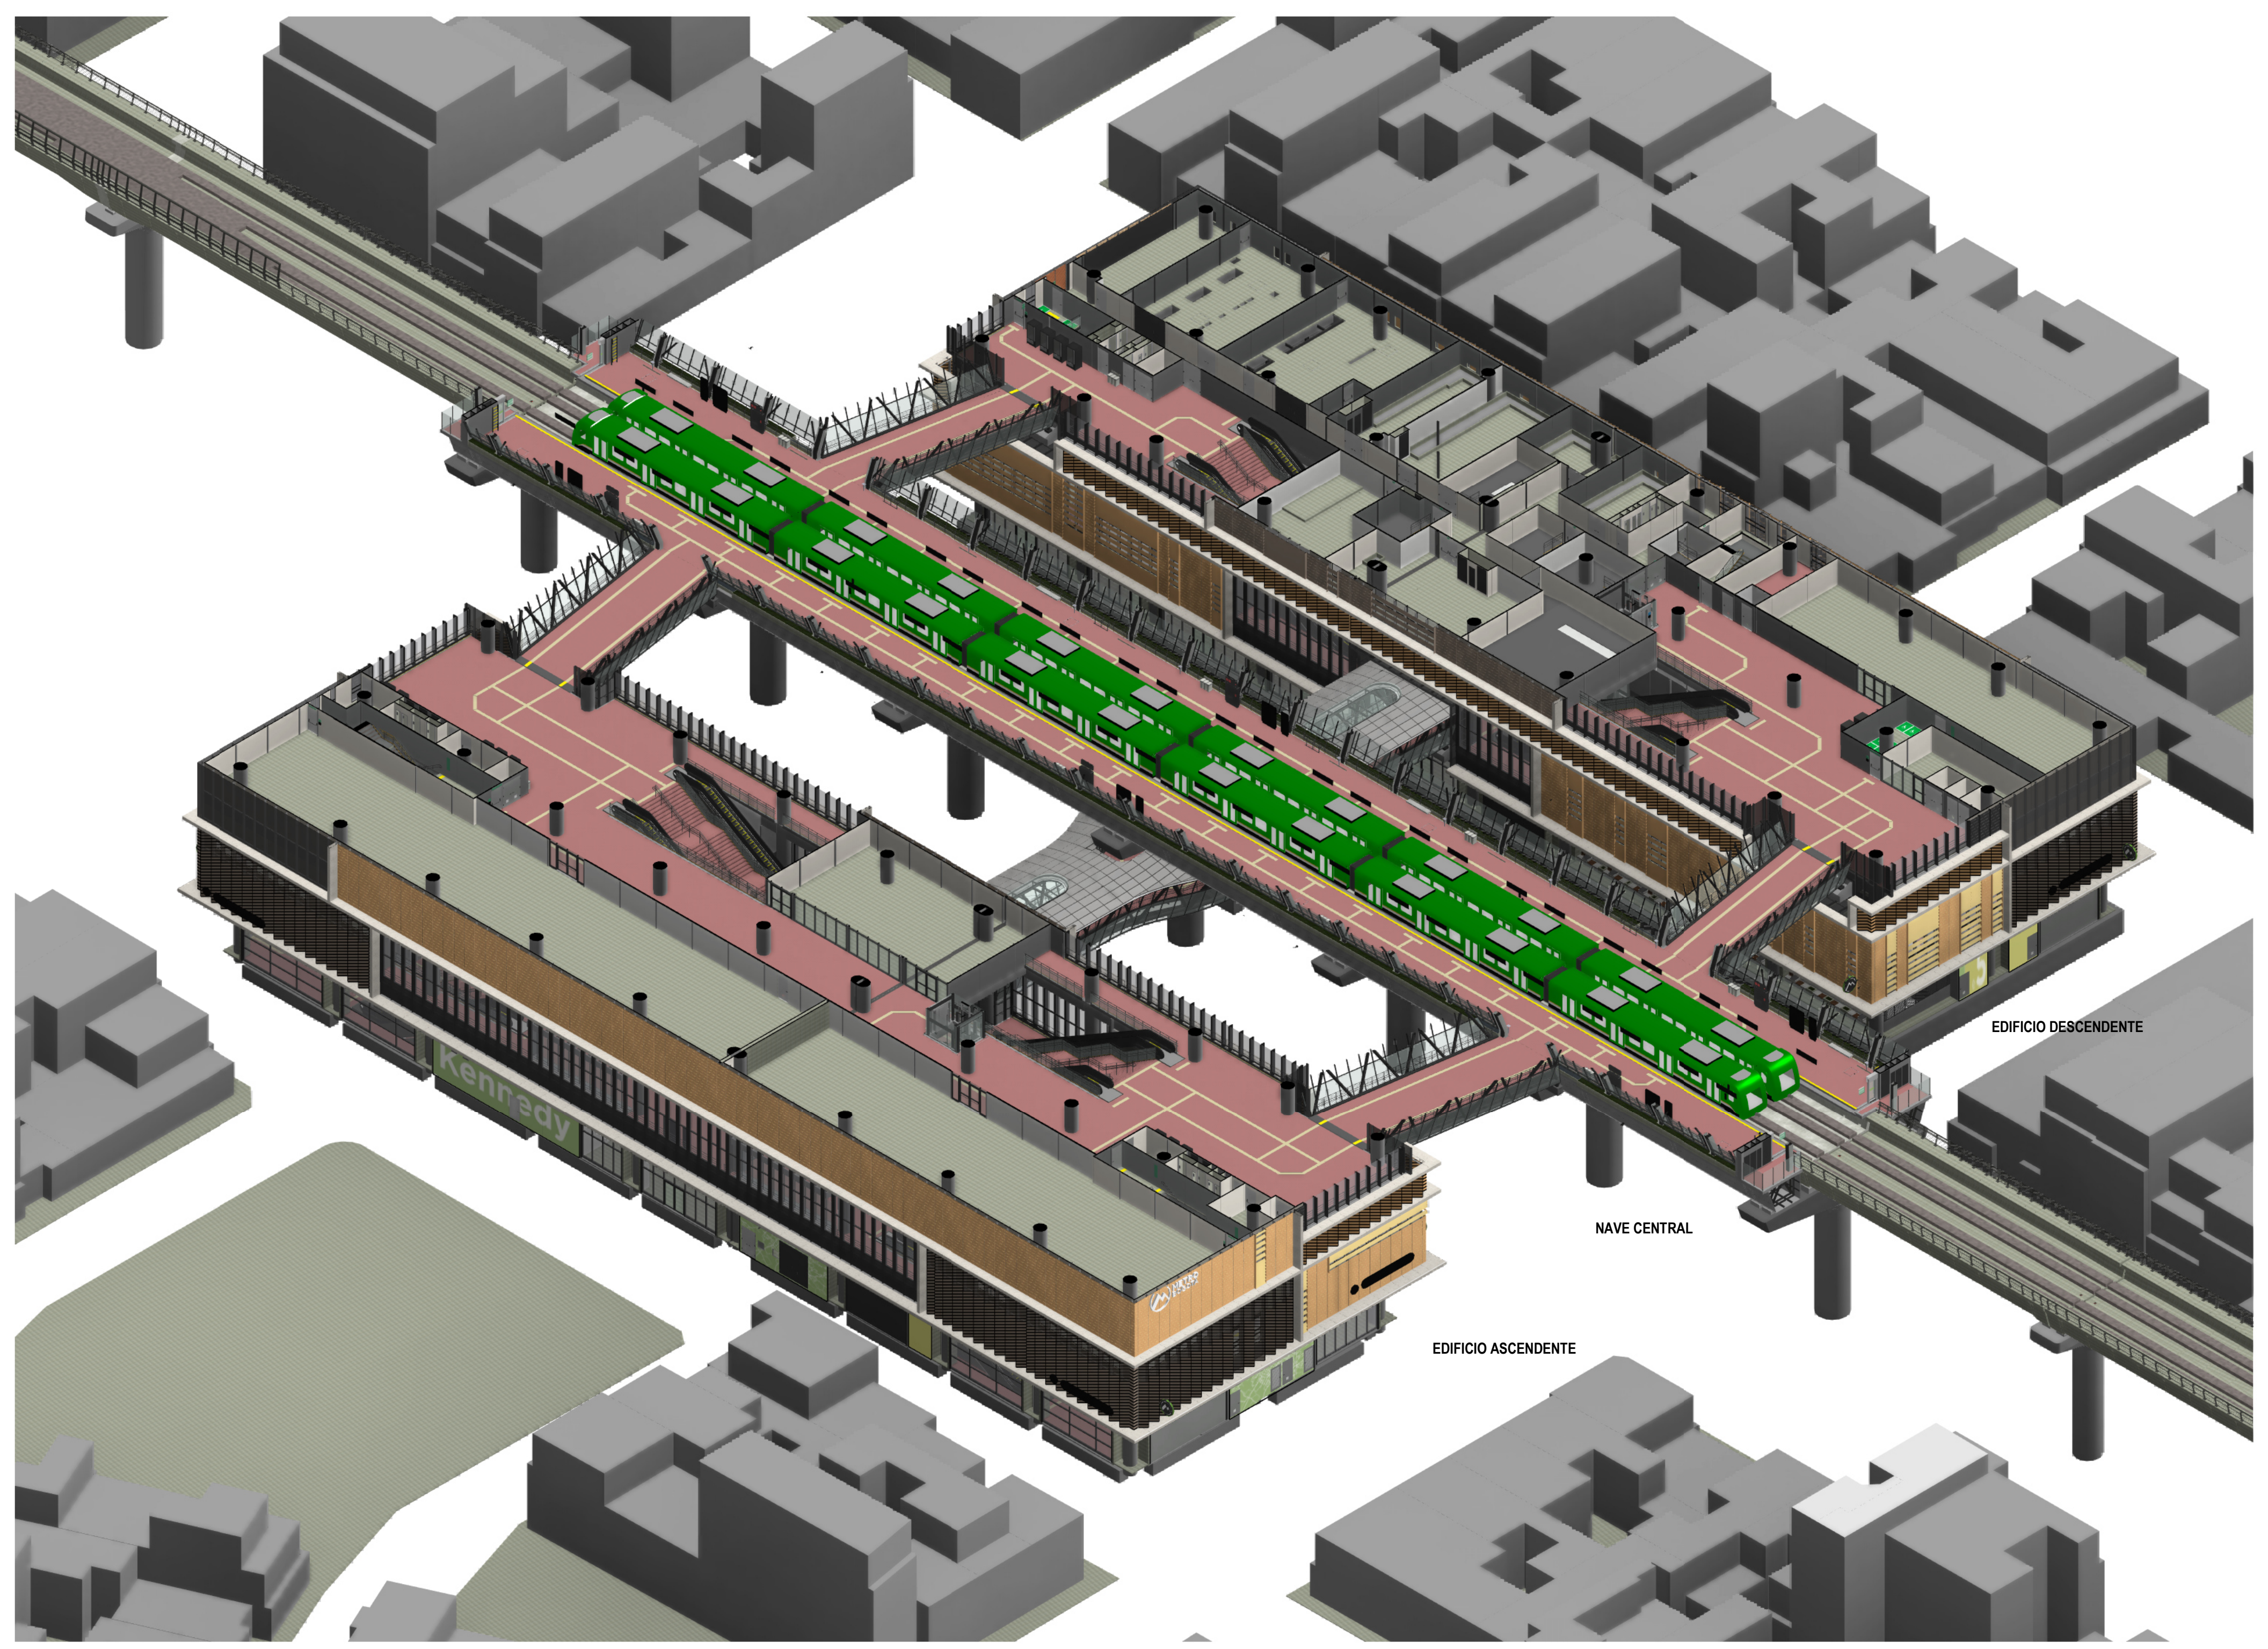

1 **3D_NIVEL PLATAFORMA_GENERAL**
ESC : N/A

TABLA DE ÁREAS ÚTILES (NIVEL PLATAFORMA)			
CÓDIGO	**NOMBRE**	**ÁREA (m²)**	**DEPARTAMENTO**
EDIFICIO ASCENDENTE			
ARQ_PL_03_PLATAFORMA			
PA-02	ÁREA PAGA	1255.26	ÁREA PAGA
R-111	SERVICIOS ADICIONALES - ÁREA DE SERVICIO	233.52	SERVICIOS ADICIONALES - ÁREA PAGA
R-112	SERVICIOS ADICIONALES - ÁREA DE SERVICIO	688.56	SERVICIOS ADICIONALES - ÁREA PAGA
R-113	SERVICIOS ADICIONALES - ÁREA DE SERVICIO	548.98	SERVICIOS ADICIONALES - ÁREA PAGA
R-303	SERVICIOS ADICIONALES - MÁQUINAS EXPENDEDORAS/CAJEROS AUTOMÁTICOS	3.60	SERVICIOS ADICIONALES - ÁREA PAGA
R-304	SERVICIOS ADICIONALES - MÁQUINAS EXPENDEDORAS/CAJEROS AUTOMÁTICOS	4.91	SERVICIOS ADICIONALES - ÁREA PAGA
R-305	SERVICIOS ADICIONALES - MÁQUINAS EXPENDEDORAS/CAJEROS AUTOMÁTICOS	5.26	SERVICIOS ADICIONALES - ÁREA PAGA
T-20-L-5	MEDIDORES (LUZ)	13.55	ÁREA TÉCNICA
T-20-L-6	MEDIDORES (LUZ)	16.33	ÁREA TÉCNICA
T-20-W-5	MEDIDORES (AGUA)	16.20	ÁREA TÉCNICA
T-20-W-6	MEDIDORES (AGUA)	10.68	ÁREA TÉCNICA
T-21-8	ÁREA DE INSPECCIÓN	11.94	ÁREA TÉCNICA
T-21-9	ÁREA DE INSPECCIÓN	11.02	ÁREA TÉCNICA
T-25-4	NODO DE ACCESO DE TELECOMUNICACIONES	5.57	ÁREA TÉCNICA
T-25-5	NODO DE ACCESO DE TELECOMUNICACIONES	4.78	ÁREA TÉCNICA
ZDR-03	ZONA DE REFUGIO (PMR)	7.29	ZONA DE REFUGIO
ZDR-04	ZONA DE REFUGIO (PMR)	6.09	ZONA DE REFUGIO
EDIFICIO DESCENDENTE			
ARQ_PL_03_PLATAFORMA			
O-07-2	CUARTO DE LIMPIEZA COMPLEMENTARIO	3.91	ÁREA OPERATIVA
O-17	OPERADORES TELECOMUNICACIONES EXTERIORES	36.84	ÁREA OPERATIVA
O-21-4	ALMACENAMIENTO DE LA ESTACIÓN	36.12	ÁREA OPERATIVA
PA-02	ÁREA PAGA	210.31	ÁREA PAGA
PA-03	ÁREA PAGA	500.38	ÁREA PAGA
R-110	SERVICIOS ADICIONALES - ÁREA DE SERVICIO	305.25	SERVICIOS ADICIONALES - ÁREA PAGA
R-111	SERVICIOS ADICIONALES - ÁREA DE SERVICIO	45.18	SERVICIOS ADICIONALES - ÁREA PAGA
R-302	SERVICIOS ADICIONALES - MÁQUINAS EXPENDEDORAS/CAJEROS AUTOMÁTICOS	8.23	SERVICIOS ADICIONALES - ÁREA PAGA
R-303	SERVICIOS ADICIONALES - MÁQUINAS EXPENDEDORAS/CAJEROS AUTOMÁTICOS	6.31	SERVICIOS ADICIONALES - ÁREA PAGA
T-00-2	CIRCULACIÓN TÉCNICA	212.73	ÁREA TÉCNICA
T-01	SUBESTACIÓN DE TRACCIÓN (SET)	243.34	ÁREA TÉCNICA
T-02	LOCAL DE CONDUCCIÓN AUTOMÁTICA (CBTC)	39.08	ÁREA TÉCNICA
T-02-1	UPS DEDICADA (CBTC)	46.29	ÁREA TÉCNICA
T-03	TELECOMUNICACIONES ESTACIÓN - CORRIENTE DÉBIL	123.39	ÁREA TÉCNICA
T-04	EQUIPO BOLETERÍA	17.15	ÁREA TÉCNICA

TABLA DE ÁREAS ÚTILES (NIVEL PLATAFORMA)			
CÓDIGO	**NOMBRE**	**ÁREA (m²)**	**DEPARTAMENTO**
T-05	ALMACÉN PARA MANTENIMIENTO	18.82	ÁREA TÉCNICA
T-06	SALA DE TABLEROS	71.04	ÁREA TÉCNICA
T-07	CENTRO DE TRANSFORMACIÓN (CT)	182.61	ÁREA TÉCNICA
T-09	ALMACÉN EQUIPO ELÉCTRICO	23.41	ÁREA TÉCNICA
T-10	CUARTO DE EQUIPO ELECTROMECÁNICO	27.47	ÁREA TÉCNICA
T-11	CUARTO DE VENTILACIÓN	123.92	ÁREA TÉCNICA
T-12	PLANTA DE REFRIGERACIÓN PARA LA CLIMATIZACIÓN	96.35	ÁREA TÉCNICA
T-20-L-6	MEDIDORES (LUZ)	5.39	ÁREA TÉCNICA
T-20-W-6	MEDIDORES (AGUA)	4.09	ÁREA TÉCNICA
T-21-11	ÁREA DE INSPECCIÓN	5.12	ÁREA TÉCNICA
T-21-12	ÁREA DE INSPECCIÓN	4.00	ÁREA TÉCNICA
T-21-13	ÁREA DE INSPECCIÓN	9.22	ÁREA TÉCNICA
T-22	CUARTO DE UPS	108.69	ÁREA TÉCNICA
T-23	CUARTO PDAP	29.80	ÁREA TÉCNICA
T-24	TETRA UPS	49.20	ÁREA TÉCNICA
T-25-6	NODO DE ACCESO DE TELECOMUNICACIONES	6.46	ÁREA TÉCNICA
T-25-7	NODO DE ACCESO DE TELECOMUNICACIONES	4.95	ÁREA TÉCNICA
ZDR-05	ZONA DE REFUGIO (PMR)	1.21	ZONA DE REFUGIO
ZDR-06	ZONA DE REFUGIO (PMR)	2.43	ZONA DE REFUGIO
ZDR-07	ZONA DE REFUGIO (PMR)	3.65	ZONA DE REFUGIO
ZDR-08	ZONA DE REFUGIO (PMR)	6.08	ZONA DE REFUGIO
NAVE CENTRAL			
ARQ_PL_03_PLATAFORMA			
PA-02	ÁREA PAGA	90.33	ÁREA PAGA
PA-03	ÁREA PAGA	90.89	ÁREA PAGA
PA-04	ÁREA PAGA	697.51	ÁREA PAGA
PA-05	ÁREA PAGA	697.51	ÁREA PAGA
PA-06	ÁREA PAGA	118.32	ÁREA PAGA
PA-07	ÁREA PAGA	112.93	ÁREA PAGA
TOTAL NIVEL PLATAFORMA		7269.42	

TABLA DE ÁREAS ÚTILES POR DEPARTAMENTO (NIVEL PLATAFORMA)	
DEPARTAMENTO	**ÁREA (m²)**
EDIFICIO ASCENDENTE	
ARQ_PL_03_PLATAFORMA	
SERVICIOS ADICIONALES - ÁREA PAGA	1484.82
ZONA DE REFUGIO	13.38
ÁREA PAGA	1255.26
ÁREA TÉCNICA	90.07
EDIFICIO DESCENDENTE	
ARQ_PL_03_PLATAFORMA	
SERVICIOS ADICIONALES - ÁREA PAGA	364.96
ZONA DE REFUGIO	13.36
ÁREA OPERATIVA	76.88
ÁREA PAGA	710.69
ÁREA TÉCNICA	1452.51
NAVE CENTRAL	
ARQ_PL_03_PLATAFORMA	
ÁREA PAGA	1807.51
TOTAL NIVEL PLATAFORMA	7269.42

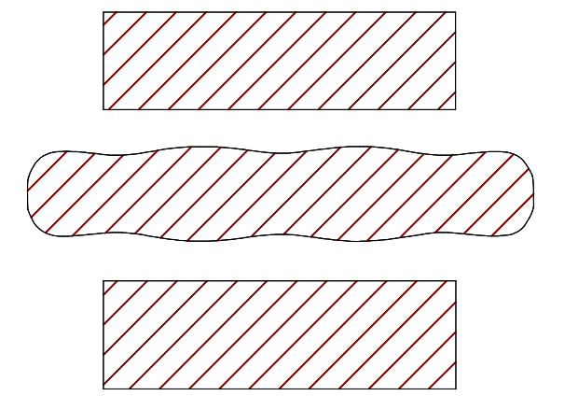

PLANO CLAVE ESTACIÓN 5
VÁLIDO PARA CONSTRUCCIÓN
20-03-26

LOCALIZACIÓN

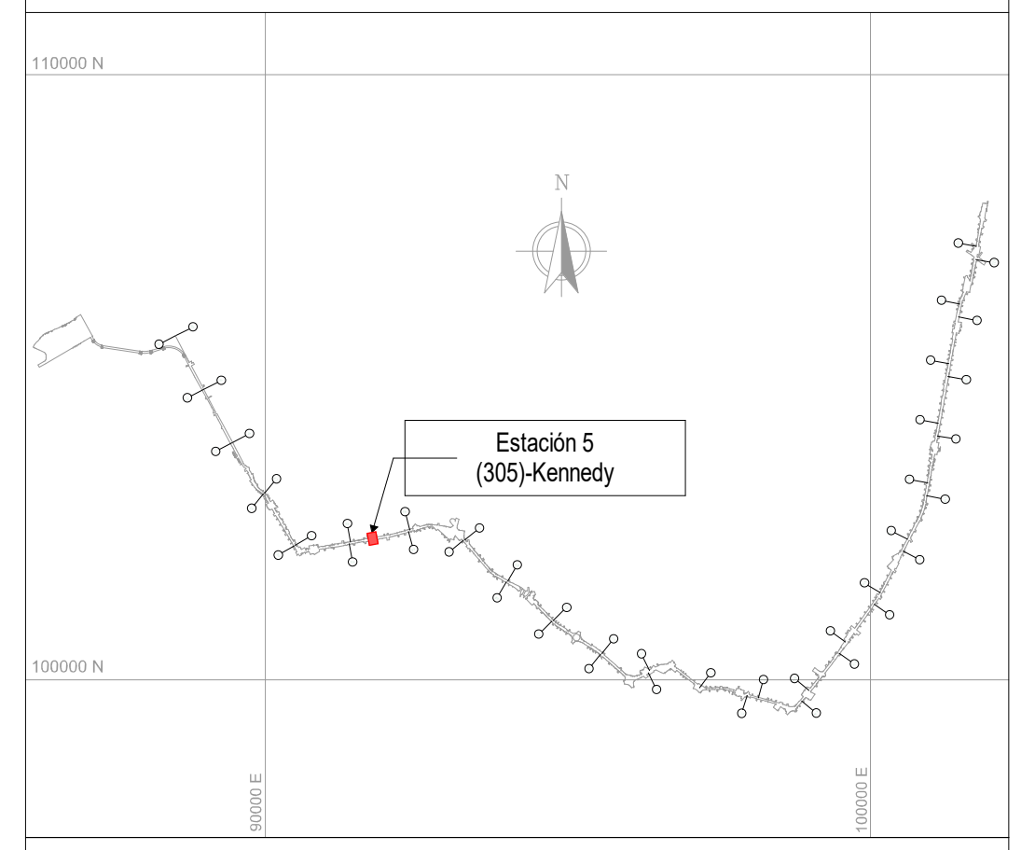

NOTAS

01 TODAS LAS DIMENSIONES ESTÁN CONFIGURADAS EN METROS A MENOS QUE SE INDIQUE UNA UNIDAD DE MEDIDA DIFERENTE.

02 TODAS LAS MEDIDAS, UBICACIÓN Y NIVELES DEBEN VERIFICARSE EN EL LUGAR DE CONSTRUCCIÓN.

03 EL NIVEL DE ACCESO AL EDIFICIO PL 01 CORRESPONDE AL +0,00 DE LA ESTACIÓN Y REFERENCIA AL NIVEL 2554.55 M.S.N.M

04 LOS NOMBRES ESPECIFICOS DE LAS ÁREAS PUEDEN SER CONSULTADAS EN EL PLANO NO. 3 Ó EN LAS VISTAS EN PLANTA.

05 LOS COLORES QUE SE MUESTRAN EN LOS PLANOS COMO PROYECCIÓN DE ELEMENTOS ARQUITECTÓNICOS COMO CUBIERTAS FACHADAS MUROS ETC. NO REPRESENTAN LA MATERIALIDAD Y REALIDAD DE ACABADOS DEL PROYECTO, SOLO SON INDICATIVOS PARA REALIZAR UNA CORRECTA LECTURA DE LA PLANIMETRÍA.

06 LAS ESCALERAS ELÉCTRICAS INDICAN SU SENTIDO CON LA SIGUIENTE NOMENCLATURA: "SUBE" Y "BAJA".

07 SE DEBEN REVISAR LOS NIVELES ESTRUCTURALES PARA NIVEL DE ACCESO PL_01 Y SUBNIVELES, PL_02 (INTERMEDIO), PL_03 (PLATAFORMA) CON LA PLANIMETRÍA DE PLACAS ESTRUCTURALES EN LOS ENTREGABLES L1T1-1300-405-CON-ED-EST-PL-0170, 0139, 0156, 0140, 0171, 0181, RESPECTIVAMENTE. EL NIVEL ESTRUCTURAL (NE) REFERENCIA LOS ESPACIOS DONDE SE DEBE ACONDICIONAR EL ACABADO DE PISO SEGÚN CORRESPONDA, CON LOS NIVELES DE PISO TERMINADO (NPT). LOS NIVELES PROYECTADOS DE EMPATE (NPE) EN LAS ÁREAS DE SERVICIOS ADICIONALES, REFERENCIAN LA ADECUACIÓN DE LOS DESNIVELES EN ESTAS ÁREAS; QUEDA COMO RESPONSABILIDAD DEL LOCATARIO DEFINIR Y ACONDICIONAR ESTE ACABADO DE PISO (NPE) EN LÍNEA CON EL NIVEL (NPT) DE ESPACIOS COLINDANTES. EL NIVEL ESTRUCTURAL (NE) SE ENCUENTRA A (- 0.10M) POR DEBAJO DE LOS NIVELES DE PISO TERMINADO (NPT) Y LOS NIVELES PROYECTADOS DE EMPATE (NPE) MARCADOS EN LA PLANIMETRÍA.

- ARQ_PL_00 = SÓTANO / NPT -6.75
- ARQ_PL_00.1 = ACCESO / NPT -0.45
- ARQ_PL_00.2 = ACCESO / NPT -0.35
- ARQ_PL_00.3 = ACCESO / NPT -0.30
- ARQ_PL_00.4 = ACCESO / NPT -0.20
- ARQ_PL_00.5 = ACCESO / NPT -0.10
- ARQ_PL_01 = ACCESO / NPT 0.00
- ARQ_PL_01.1 = ACCESO / NPT 0.10
- ARQ_PL_01.2 = ACCESS / NPT 0.15
- ARQ_PL_01.3 = ACCESS / NPT 0.20
- ARQ_PL_02 = INTERMEDIO / NPT 6.60
- ARQ_PL_02.2 = TOPE DE RIEL / NPT 14.20
- ARQ_PL_03 = PLATAFORMA / NPT 15.34
- ARQ_PL_04 = CUBIERTA EDIFICACIONES / NPT 21.94
- ARQ_PL_05 = CUBIERTA NAVE CENTRAL / NPT 24.59

CONVENCIONES

‐ ‐ ‐ ‐	LIMITE DE INTERVENCIÓN
‐ ‐ ‐ ‐	HUELLA APÉNDICE TÉCNICO
▬	MURO DIVISORIO
— — —	PROYECCIÓN NIVEL SUPERIOR
🟩	SERVICIOS ADICIONALES - ÁREA NO PAGA
🟩	SERVICIOS ADICIONALES - ÁREA PAGA
🟩	SERVICIO PÚBLICO
🟦	ZONA DE REFUGIO
🟥	ÁREA CULTURAL
🟪	ÁREA DE TAQUILLA BRT
🟨	ÁREA NO PAGA
🟦	ÁREA OPERATIVA
🟧	ÁREA PAGA
🟦	ÁREA PÚBLICA
⬜	ÁREA TÉCNICA

No.	PLANOS DE REFERENCIA	REV.

No.	MODELO BIM DE REFERENCIA	REV.
1	L1T1-1100-205-CON-ED-EST-MO-0001.rvt	V00
2	L1T1-1100-206-CON-ED-EST-MO-0001.rvt	V00
3	L1T1-1100-305-CON-ED-EST-MO-0001.rvt	V00
4	L1T1-1150-205-CON-ED-EST-MO-0001.rvt	V00
5	L1T1-1150-206-CON-ED-EST-MO-0001.rvt	V00
6	L1T1-1150-305-CON-ED-EST-MO-0001.rvt	V00
7	L1T1-1200-305-CON-ED-EST-MO-0001.rvt	V00
8	L1T1-1300-405-CON-ED-EST-MO-0001.rvt	V00
9	L1T1-1300-405-CON-ED-EST-MO-0002.rvt	V00
10	L1T1-1310-405-CON-ED-EST-MO-0001.rvt	V00
11	L1T1-1410-305-CON-ED-MEC-MO-0001.rvt	V00
12	L1T1-1420-305-CON-ED-MEC-MO-0001.rvt	V00
13	L1T1-5160-305-CON-ED-EST-MO-0001.rvt	V00
14	L1T1-5160-305-CON-ED-ARC-MO-0001.rvt	V00
15	L1T1-5300-305-CON-ED-MEC-MO-0001.rvt	V00
16	L1T1-5600-305-CON-ED-INS-MO-0001.rvt	V00
17	L1T1-1330-405-CON-ED-ARQ-MO-0011.rvt	V00
18	L1T1-1330-405-CON-ED-ARQ-MO-0012.rvt	V00

No.	PAQUETE DE TRABAJO DE REFERENCIA	REV.
1	XREF-URBANISM_CONTEXT_ST05.rvt	
2	XREF-SECONDARY-STRUCTURE-ST05.rvt	

0 2 10m
1:200

DISEÑÓ:	REN ZHENHUA Licencia de Arq.nivel I (China): 1101735-614
APROBÓ:	DIEGO ERNESTO DUEÑAS Mat.: 25202-53876 CND
REVISÓ:	CARLOS MAURICIO BARRETO BARBOSA Mat.: A4012012-14139353
DIBUJÓ:	EQUIPO CHEC

REVISIÓN No.	FECHA	DESCRIPCIÓN	REVISÓ	APROBÓ	APROBACIÓN CLIENTE
V01	20/03/2026	EMITIDO PARA CONSTRUCCIÓN	C.M.B.B	D.E.D	
V00	07/04/2025	REVISIÓN NO OBJETADA - EMITIDO PARA CONSTRUCCIÓN	F.B.R	E.O.M	
VHH	20/09/2024	EMITIDO PARA REVISIÓN Y COMENTARIOS DEL CLIENTE E INTERVENTORÍA - INCLUYE COMENTARIOS /(AJUSTES V3)	F.B.R	E.O.M	
VGG	23/05/2024	EMITIDO PARA REVISIÓN Y COMENTARIOS DEL CLIENTE E INTERVENTORÍA - INCLUYE COMENTARIOS /(AJUSTES V2)	F.B.R	E.O.M	
VFF	03/05/2023	EMITIDO PARA REVISIÓN Y COMENTARIOS DEL CLIENTE E INTERVENTORÍA - INCLUYE COMENTARIOS /(AJUSTES)	J.E.M	M.B.M	
VEE	18/12/2022	EMITIDO PARA REVISIÓN Y COMENTARIOS DEL CLIENTE E INTERVENTORÍA - INCLUYE COMENTARIOS /(NAVE CENTRAL)	J.E.M	M.B.M	
VDD	11/11/2022	EMITIDO PARA REVISIÓN Y COMENTARIOS DEL CLIENTE E INTERVENTORÍA - INCLUYE COMENTARIOS /(90% ACCESOS)	J.E.M	M.B.M	
VCC	22/08/2022	EMITIDO PARA REVISIÓN Y COMENTARIOS DEL CLIENTE E INTERVENTORÍA - INCLUYE COMENTARIOS /(ENTREGA 90%)	J.E.M	M.B.M	
VBB	06/12/2021	EMITIDO PARA REVISIÓN Y COMENTARIOS DEL CLIENTE E INTERVENTORÍA	J.E.M	M.B.M	
VA0	05/12/2021	EMITIDO PARA COMENTARIOS INTERNOS - EMISIÓN PRELIMINAR PARA COMENTARIOS	J.E.M	M.B.M	

METRO LÍNEA 1
CONTRATO DE CONCESIÓN No. 163 DE 2019

PROYECTO PRIMERA LÍNEA DEL METRO DE BOGOTÁ - TRAMO 1

DIRECTOR DE INTERVENTORÍA: JAVIER DESCARGA N. Mat.:25202-68697 CND	ESPECIALISTA INTERVENTORÍA: CARLOS ALBERTO HOYOS SOTO Mat.:A25072000-14251682	FECHA: MARZO 2026

INFRAESTRUCTURA VIAL

ARQUITECTURA

ESTACIÓN METRO 5 (KENNEDY)
GENERAL
VISTA EN PLANTA Y 3D - NIVEL PLATAFORMA

PLANCHA No: L1T1-0000-305-CON-ED-ARQ-PL-0001_07_V01	ESCALA: INDICADA	REVISIÓN No. V01	PLANO No. 07 DE 96
ARCHIVO: L1T1-0000-305-CON-ED-ARQ-MO-0001_V00.rvt	FECHA: DICIEMBRE 2021		