L1T1-CON-CAL-FR-0120 - B1 : 1000x707mm

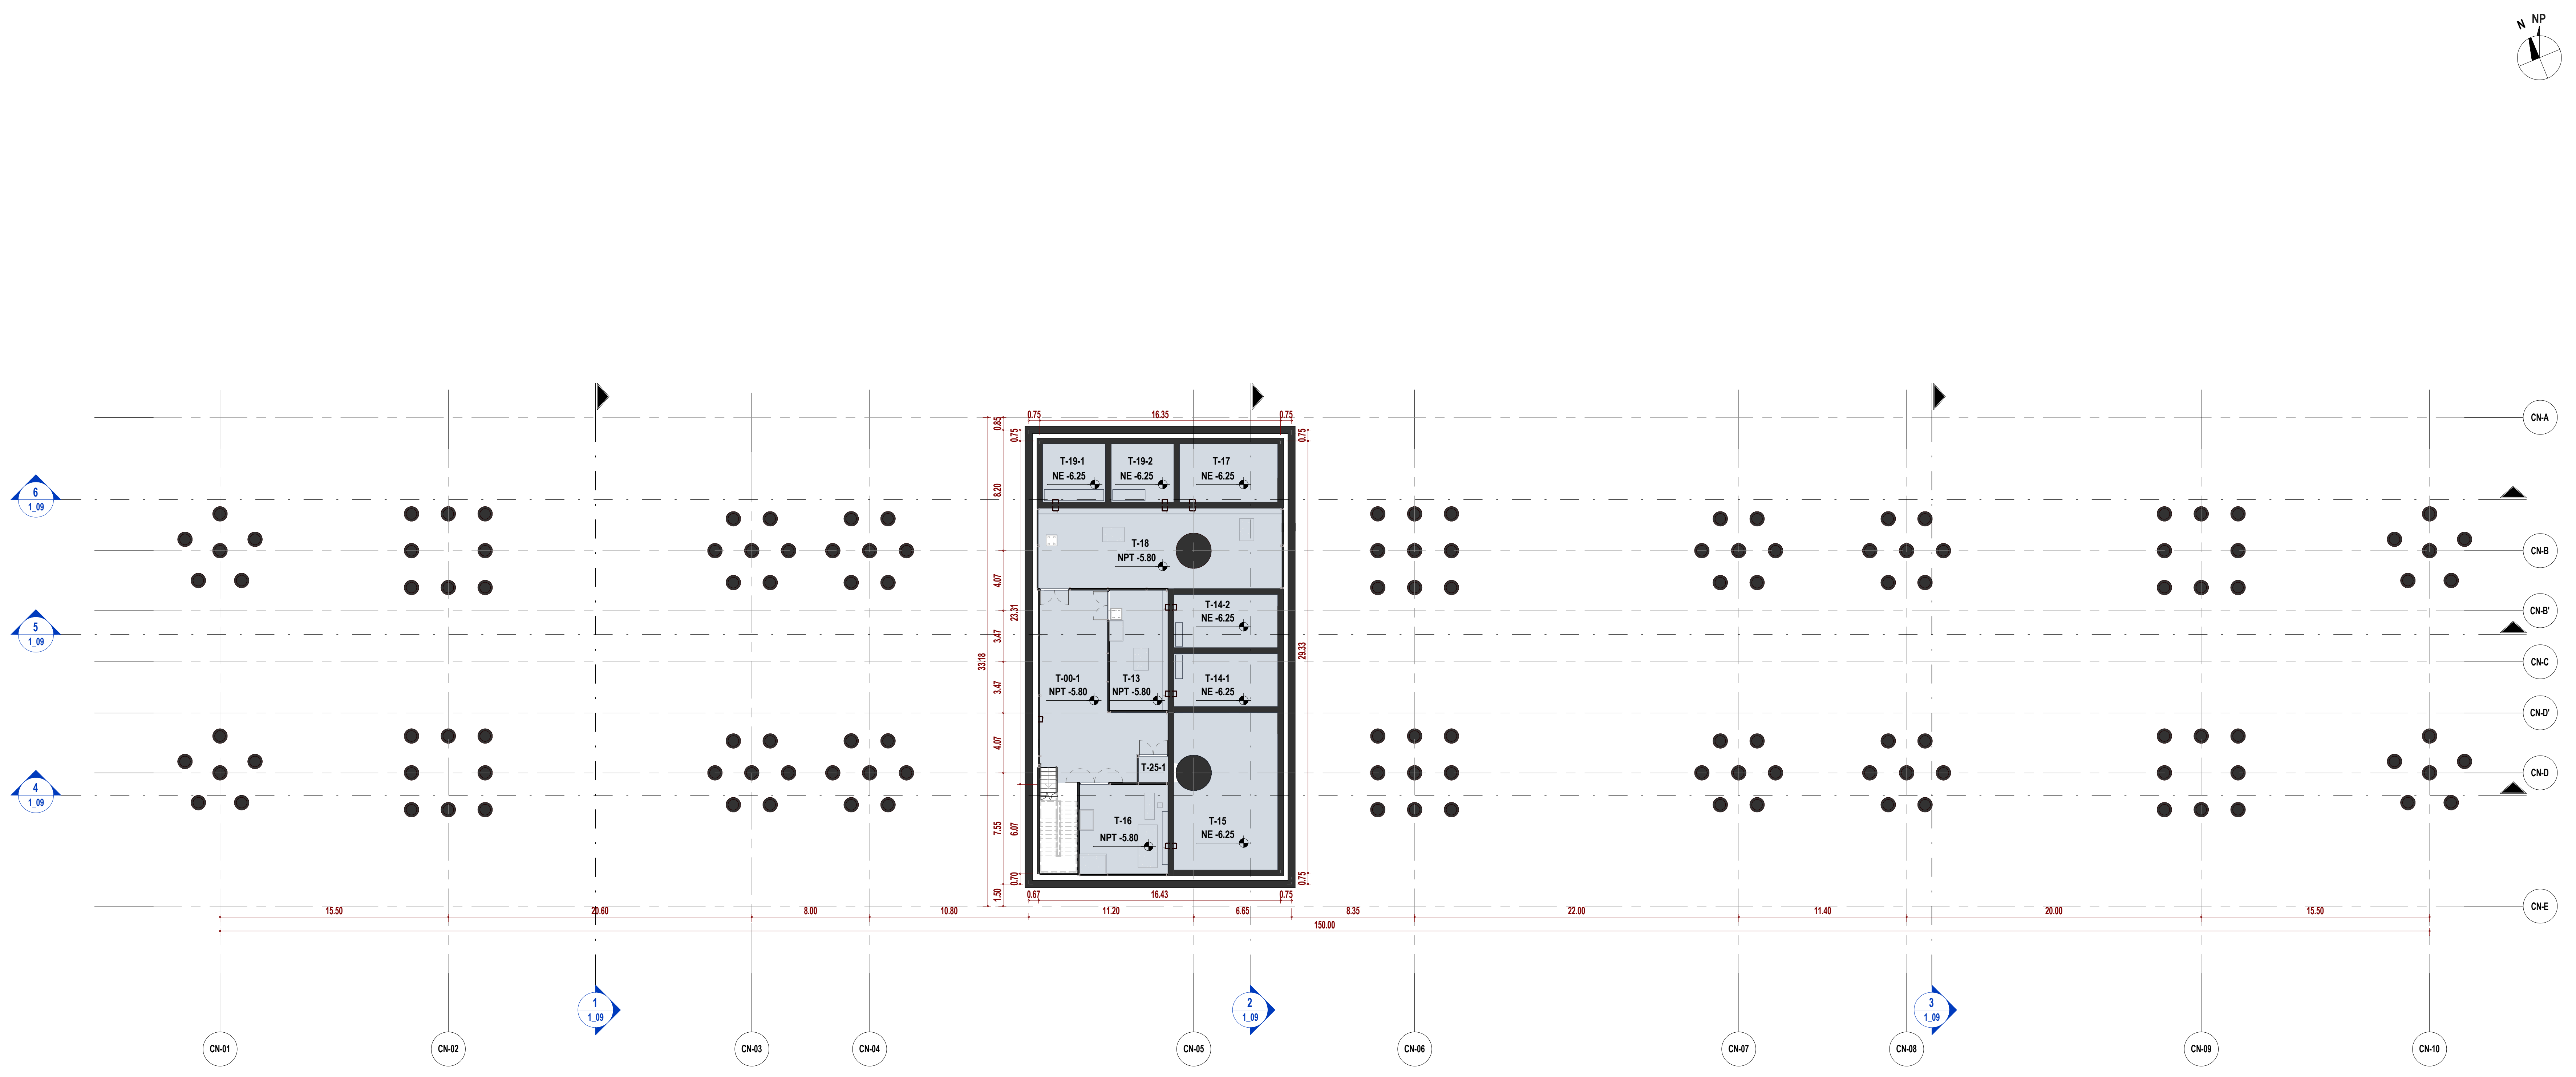

2 NIVEL SÓTANO_NAVE CENTRAL
ESC: 1 : 200

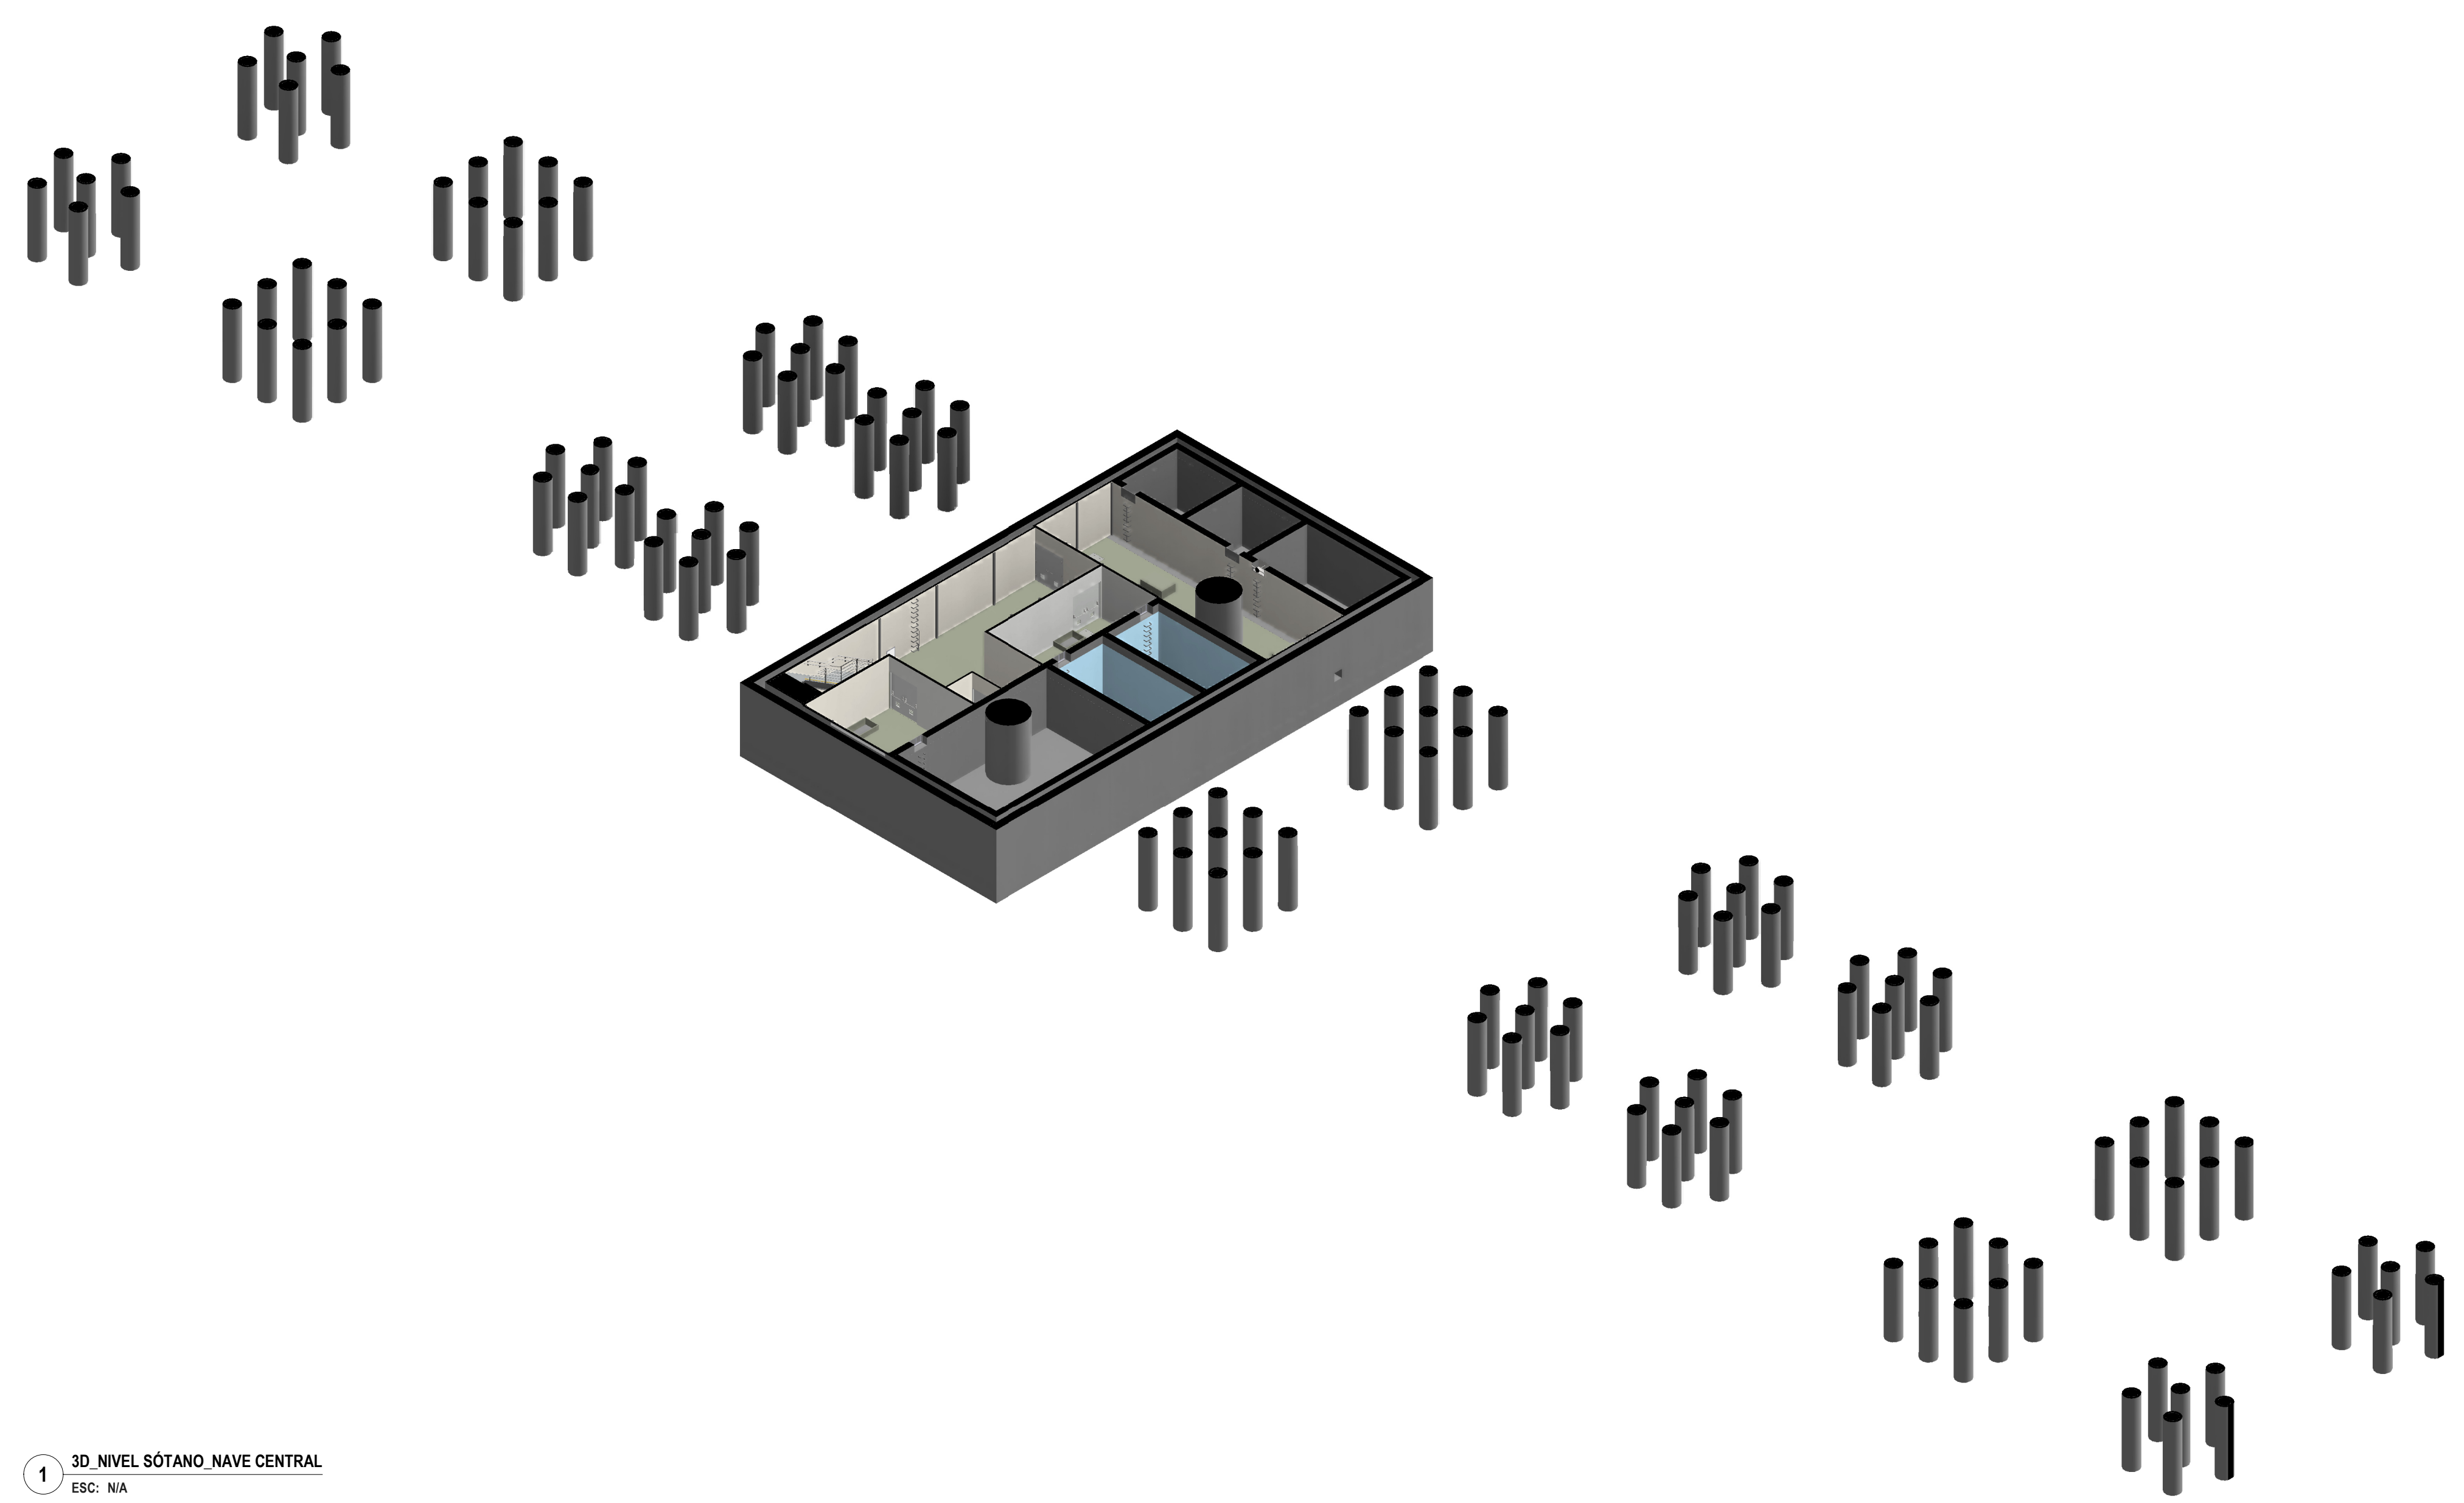

1 3D_NIVEL SÓTANO_NAVE CENTRAL
ESC: N/A

TABLA DE ÁREAS ÚTILES (NIVEL SÓTANO)

CÓDIGO	NOMBRE	ÁREA (m²)	DEPARTAMENTO
NAVE CENTRAL			
ARQ_PL_00_SÓTANO			
T-00-1	CIRCULACIÓN TÉCNICA	74.31	ÁREA TÉCNICA
T-13	CUARTO DE BOMBAS DE SUMINISTRO DE AGUA	32.30	ÁREA TÉCNICA
T-14-1	TANQUE DE SUMINISTRO DE AGUA	25.24	ÁREA TÉCNICA
T-14-2	TANQUE DE SUMINISTRO DE AGUA	25.24	ÁREA TÉCNICA
T-15	TANQUE SISTEMA DE EXTINCIÓN DE INCENDIOS (RCI)	70.38	ÁREA TÉCNICA
T-16	CUARTO DE BOMBAS PARA ROCIADORES	36.21	ÁREA TÉCNICA
T-17	TANQUE RECUPERACIÓN AGUAS LLUVIAS	26.17	ÁREA TÉCNICA
T-18	CUARTO DE BOMBAS DE RECUPERACIÓN DE AGUAS LLUVIAS Y EQUIPO DE FILTRACIÓN	85.61	ÁREA TÉCNICA
T-19-1	TANQUE DE AGUA TRATADA	16.71	ÁREA TÉCNICA
T-19-2	TANQUE DE AGUA TRATADA	16.71	ÁREA TÉCNICA
T-25-1	NODO DE ACCESO DE TELECOMUNICACIONES	3.60	ÁREA TÉCNICA
TOTAL NIVEL SÓTANO		412.48	

TABLA DE ÁREAS ÚTILES POR DEPARTAMENTO (NIVEL SÓTANO)

DEPARTAMENTO	ÁREA (m²)
ÁREA TÉCNICA	412.48
TOTAL NIVEL SÓTANO	412.48

LOCALIZACIÓN

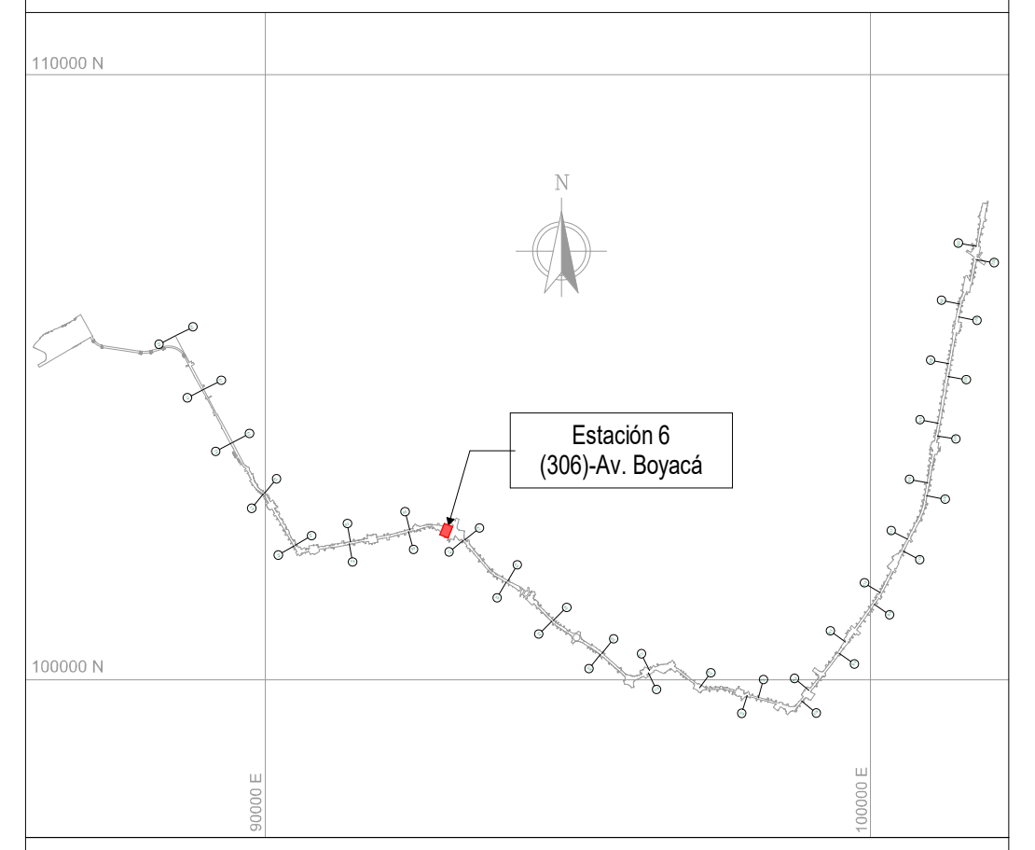

NOTAS

01 TODAS LAS DIMENSIONES ESTÁN CONFIGURADAS EN METROS A MENOS QUE SE INDIQUE UNA UNIDAD DE MEDIDA DIFERENTE.

02 TODAS LAS MEDIDAS, UBICACIÓN Y NIVELES DEBEN VERIFICARSE EN EL LUGAR DE CONSTRUCCIÓN.

03 EL NIVEL DE ACCESO AL EDIFICIO PL 01 CORRESPONDE AL +0,00 DE LA ESTACIÓN Y REFERENCIA AL NIVEL 2555.50 M.S.N.M

04 LOS NOMBRES ESPECÍFICOS DE LAS ÁREAS PUEDEN SER CONSULTADAS EN EL PLANO NO. 3 Ó EN LAS VISTAS EN PLANTA.

05 LOS COLORES QUE SE MUESTRAN EN LOS PLANOS COMO PROYECCIÓN DE ELEMENTOS ARQUITECTÓNICOS COMO CUBIERTAS, FACHADAS, MUROS, ETC. NO REPRESENTAN LA MATERIALIDAD Y REALIDAD DE ACABADOS DEL PROYECTO, SOLO SON INDICATIVOS PARA REALIZAR UNA CORRECTA LECTURA DE LA PLANIMETRÍA.

06 SE DEBEN REVISAR LOS NIVELES ESTRUCTURALES PARA NIVEL DE ACCESO PL_01 Y SUBNIVELES, PL_02 (INTERMEDIO), PL_03 (PLATAFORMA) CON LA PLANIMETRIA DE PLACAS ESTRUCTURALES EN LOS ENTREGABLES LL1T1-1200-306-CON-ED-EST-PL-0017, 20, 21, RESPECTIVAMENTE. EL NIVEL ESTRUCTURAL (NE) REFERENCIA LOS ESPACIOS DONDE SE DEBE ACONDICIONAR EL ACABADO DE PISO SEGÚN CORRESPONDA, CON LOS NIVELES DE PISO TERMINADO (NPT). LOS NIVELES PROYECTADOS DE EMPATE (NPE) EN LAS ÁREAS DE SERVICIOS ADICIONALES, REFERENCIAN LA ADECUACIÓN DE LOS DESNIVELES EN ESTAS ÁREAS; QUEDA COMO RESPONSABILIDAD DEL LOCATARIO DEFINIR Y ACONDICIONAR ESTE ACABADO DE PISO (NPE) EN LÍNEA CON EL NIVEL (NPT) DE ESPACIOS COLINDANTES. EL NIVEL ESTRUCTURAL (NE) SE ENCUENTRA A (- 0.10M) POR DEBAJO DE LOS NIVELES DE PISO TERMINADO (NPT) Y LOS NIVELES PROYECTADOS DE EMPATE (NPE) MARCADOS EN LA PLANIMETRÍA.

- ARQ_PL_00 = SÓTANO / NPT -5.80
- ARQ_PL_01 = ACCESO / NPT 0.00
- ARQ_PL_02 = INTERMEDIO / NPT 7.60
- ARQ_PL_02.1= PLACA INFERIOR VIGA CAJÓN / NPT 13.82
- ARQ_PL_02.2 = TOPE DE RIEL (TOR) / NPT 15.95
- ARQ_PL_03 = PLATAFORMA / NPT 17.09
- ARQ_PL_05 = CUBIERTA NAVE CENTRAL / NPT 26.53

CONVENCIONES

🟦	CADE
🟩	SERVICIOS ADICIONALES - ÁREA NO PAGA
🟩	SERVICIOS ADICIONALES - ÁREA PAGA
🟩	SERVICIO PÚBLICO
🟦	ZONA DE REFUGIO
🟥	ÁREA CULTURAL
🟨	ÁREA NO PAGA
🟦	ÁREA OPERATIVA
🟧	ÁREA PAGA
🟦	ÁREA PÚBLICA
⬜	ÁREA TÉCNICA

No.	PLANOS DE REFERENCIA	REV.

No.	MODELO BIM DE REFERENCIA	REV.
1	L1T1-1100-206-CON-ED-EST-MO-0001.rvt	V00
2	L1T1-1100-207-CON-ED-EST-MO-0001.rvt	V00
3	L1T1-1100-306-CON-ED-EST-MO-0001.rvt	V00
4	L1T1-1150-206-CON-ED-EST-MO-0001.rvt	V00
5	L1T1-1150-207-CON-ED-EST-MO-0001.rvt	V00
6	L1T1-1150-306-CON-ED-EST-MO-0001.rvt	V00
7	L1T1-1200-306-CON-ED-CIV-MO-0001.rvt	V00
8	L1T1-1410-306-CON-ED-MEC-MO-0001.rvt	V00
9	L1T1-1420-306-CON-ED-MEC-MO-0001.rvt	V00
10	L1T1-5160-306-CON-ED-EST-MO-0001.rvt	V00
11	L1T1-5160-306-CON-ED-ARQ-MO-0001.rvt	V00
12	L1T1-5300-306-CON-ED-MEC-MO-0001.rvt	V00
13	L1T1-5600-306-CON-ED-INS-MO-0001.rvt	V00
14	L1T1-1270-306-CON-ED-ARQ-MO-0011.rvt	V00

No.	PAQUETE DE TRABAJO DE REFERENCIA	REV.
1	XREF-URBANISM_CONTEXT_ST06.rvt	

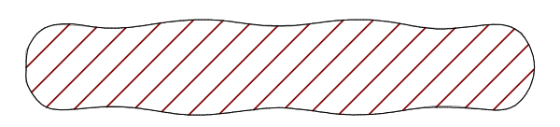

PLANO CLAVE ESTACIÓN 6

0 2 10m
1:200

VÁLIDO PARA CONSTRUCCIÓN
20-03-26

METRO BOGOTÁ
GCS Consorcio Consultores PMO Bogotá
CONSORCIO SUPERVISOR PLMB
CHEC

DISEÑÓ:	REN ZHENHUA Licencia de Arq.nivel I (China): 1101735-614	APROBÓ:	DIEGO ERNESTO DUEÑAS Mat.: 25202-53876 CND
REVISÓ:	CARLOS MAURICIO BARRETO BARBOSA Mat.: A4012012-14139353	DIBUJÓ:	EQUIPO CHEC

REVISIÓN No.	FECHA	DESCRIPCIÓN	REVISÓ	APROBÓ	APROBACIÓN CLIENTE
V01	20/03/2026	EMITIDO PARA CONSTRUCCIÓN	C.M.B.B	D.E.D	
V00	25/11/2024	REVISIÓN NO OBJETADA - EMITIDO PARA CONSTRUCCIÓN	F.B.R	E.O.M	
VGG	15/05/2024	EMITIDO PARA REVISIÓN Y COMENTARIOS DEL CLIENTE E INTERVENTORÍA - INCLUYE COMENTARIOS /(AJUSTES V4)	F.B.R	E.O.M	
VFF	22/12/2023	EMITIDO PARA REVISIÓN Y COMENTARIOS DEL CLIENTE E INTERVENTORÍA - INCLUYE COMENTARIOS /(AJUSTES V3)	F.B.R	M.B.M	
VEE	30/06/2023	EMITIDO PARA REVISIÓN Y COMENTARIOS DEL CLIENTE E INTERVENTORÍA - INCLUYE COMENTARIOS /(AJUSTES V2)	J.E.M	M.B.M	
VDD	18/12/2022	EMITIDO PARA REVISIÓN Y COMENTARIOS DEL CLIENTE E INTERVENTORÍA - INCLUYE COMENTARIOS /(AJUSTES)	J.E.M	M.B.M	
VCC	20/06/2022	EMITIDO PARA REVISIÓN Y COMENTARIOS DEL CLIENTE E INTERVENTORÍA - INCLUYE COMENTARIOS /(ENTREGA 90%)	J.E.M	M.B.M	
VBB	06/12/2021	EMITIDO PARA REVISIÓN Y COMENTARIOS DEL CLIENTE E INTERVENTORÍA	J.E.M	M.B.M	
VA0	30/06/2021	EMITIDO PARA COMENTARIOS INTERNOS - EMISIÓN PRELIMINAR PARA COMENTARIOS	J.E.M	M.B.M	

METRO LÍNEA 1

METRO LÍNEA 1
CONTRATO DE CONCESIÓN No. 163 DE 2019

PROYECTO PRIMERA LÍNEA DEL METRO DE BOGOTÁ - TRAMO 1

DIRECTOR DE INTERVENTORÍA: JAVIER DESCARGA N. Mat.:25202-68697 CND	ESPECIALISTA INTERVENTORÍA: CARLOS ALBERTO HOYOS SOTO Mat.:A25072000-14251682	FECHA: MARZO 2026

INFRAESTRUCTURA VIAL

ARQUITECTURA

ESTACIÓN METRO 6 (AVENIDA BOYACÁ)
NAVE CENTRAL
VISTA EN PLANTA Y 3D - NIVEL SÓTANO

PLANCHA No: L1T1-0000-306-CON-ED-ARQ-PL-0001_04_V01	ESCALA: INDICADA	REVISIÓN No. V01	PLANO No. 04 DE 47
ARCHIVO: L1T1-0000-306-CON-ED-ARQ-MO-0001_V00.rvt	FECHA: JUNIO 2021		