L1T1-CON-CAL-FR-0120 - B1 : 1000x707mm

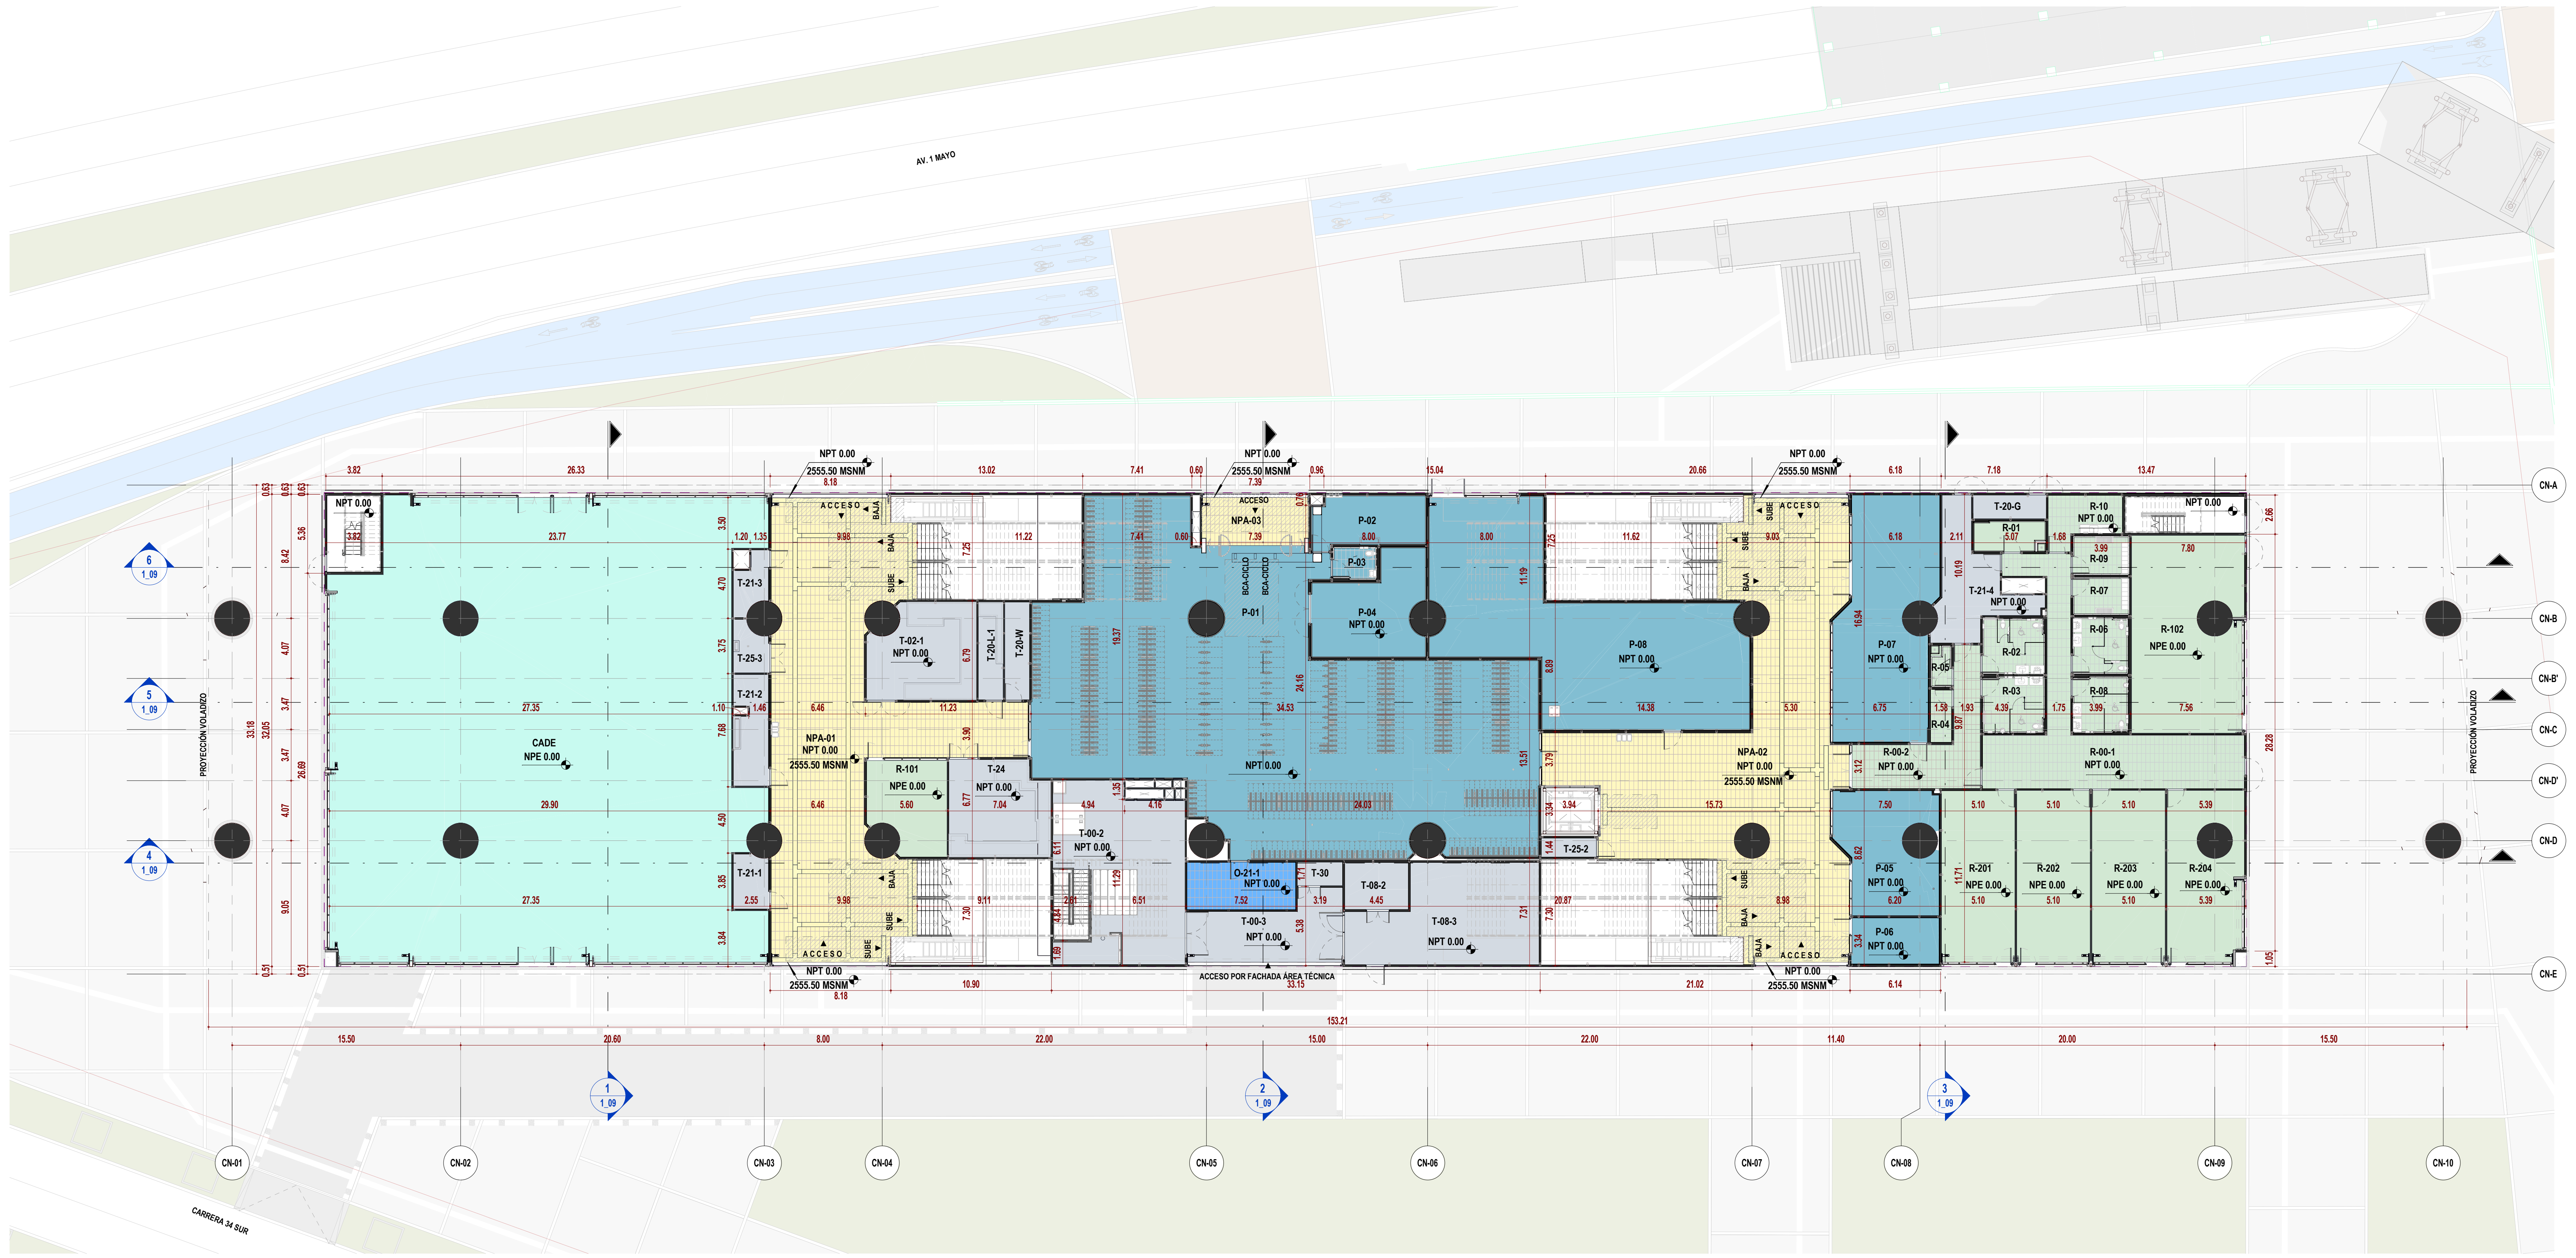

2 **NIVEL ACCESO_NAVE CENTRAL**
ESC: 1 : 200

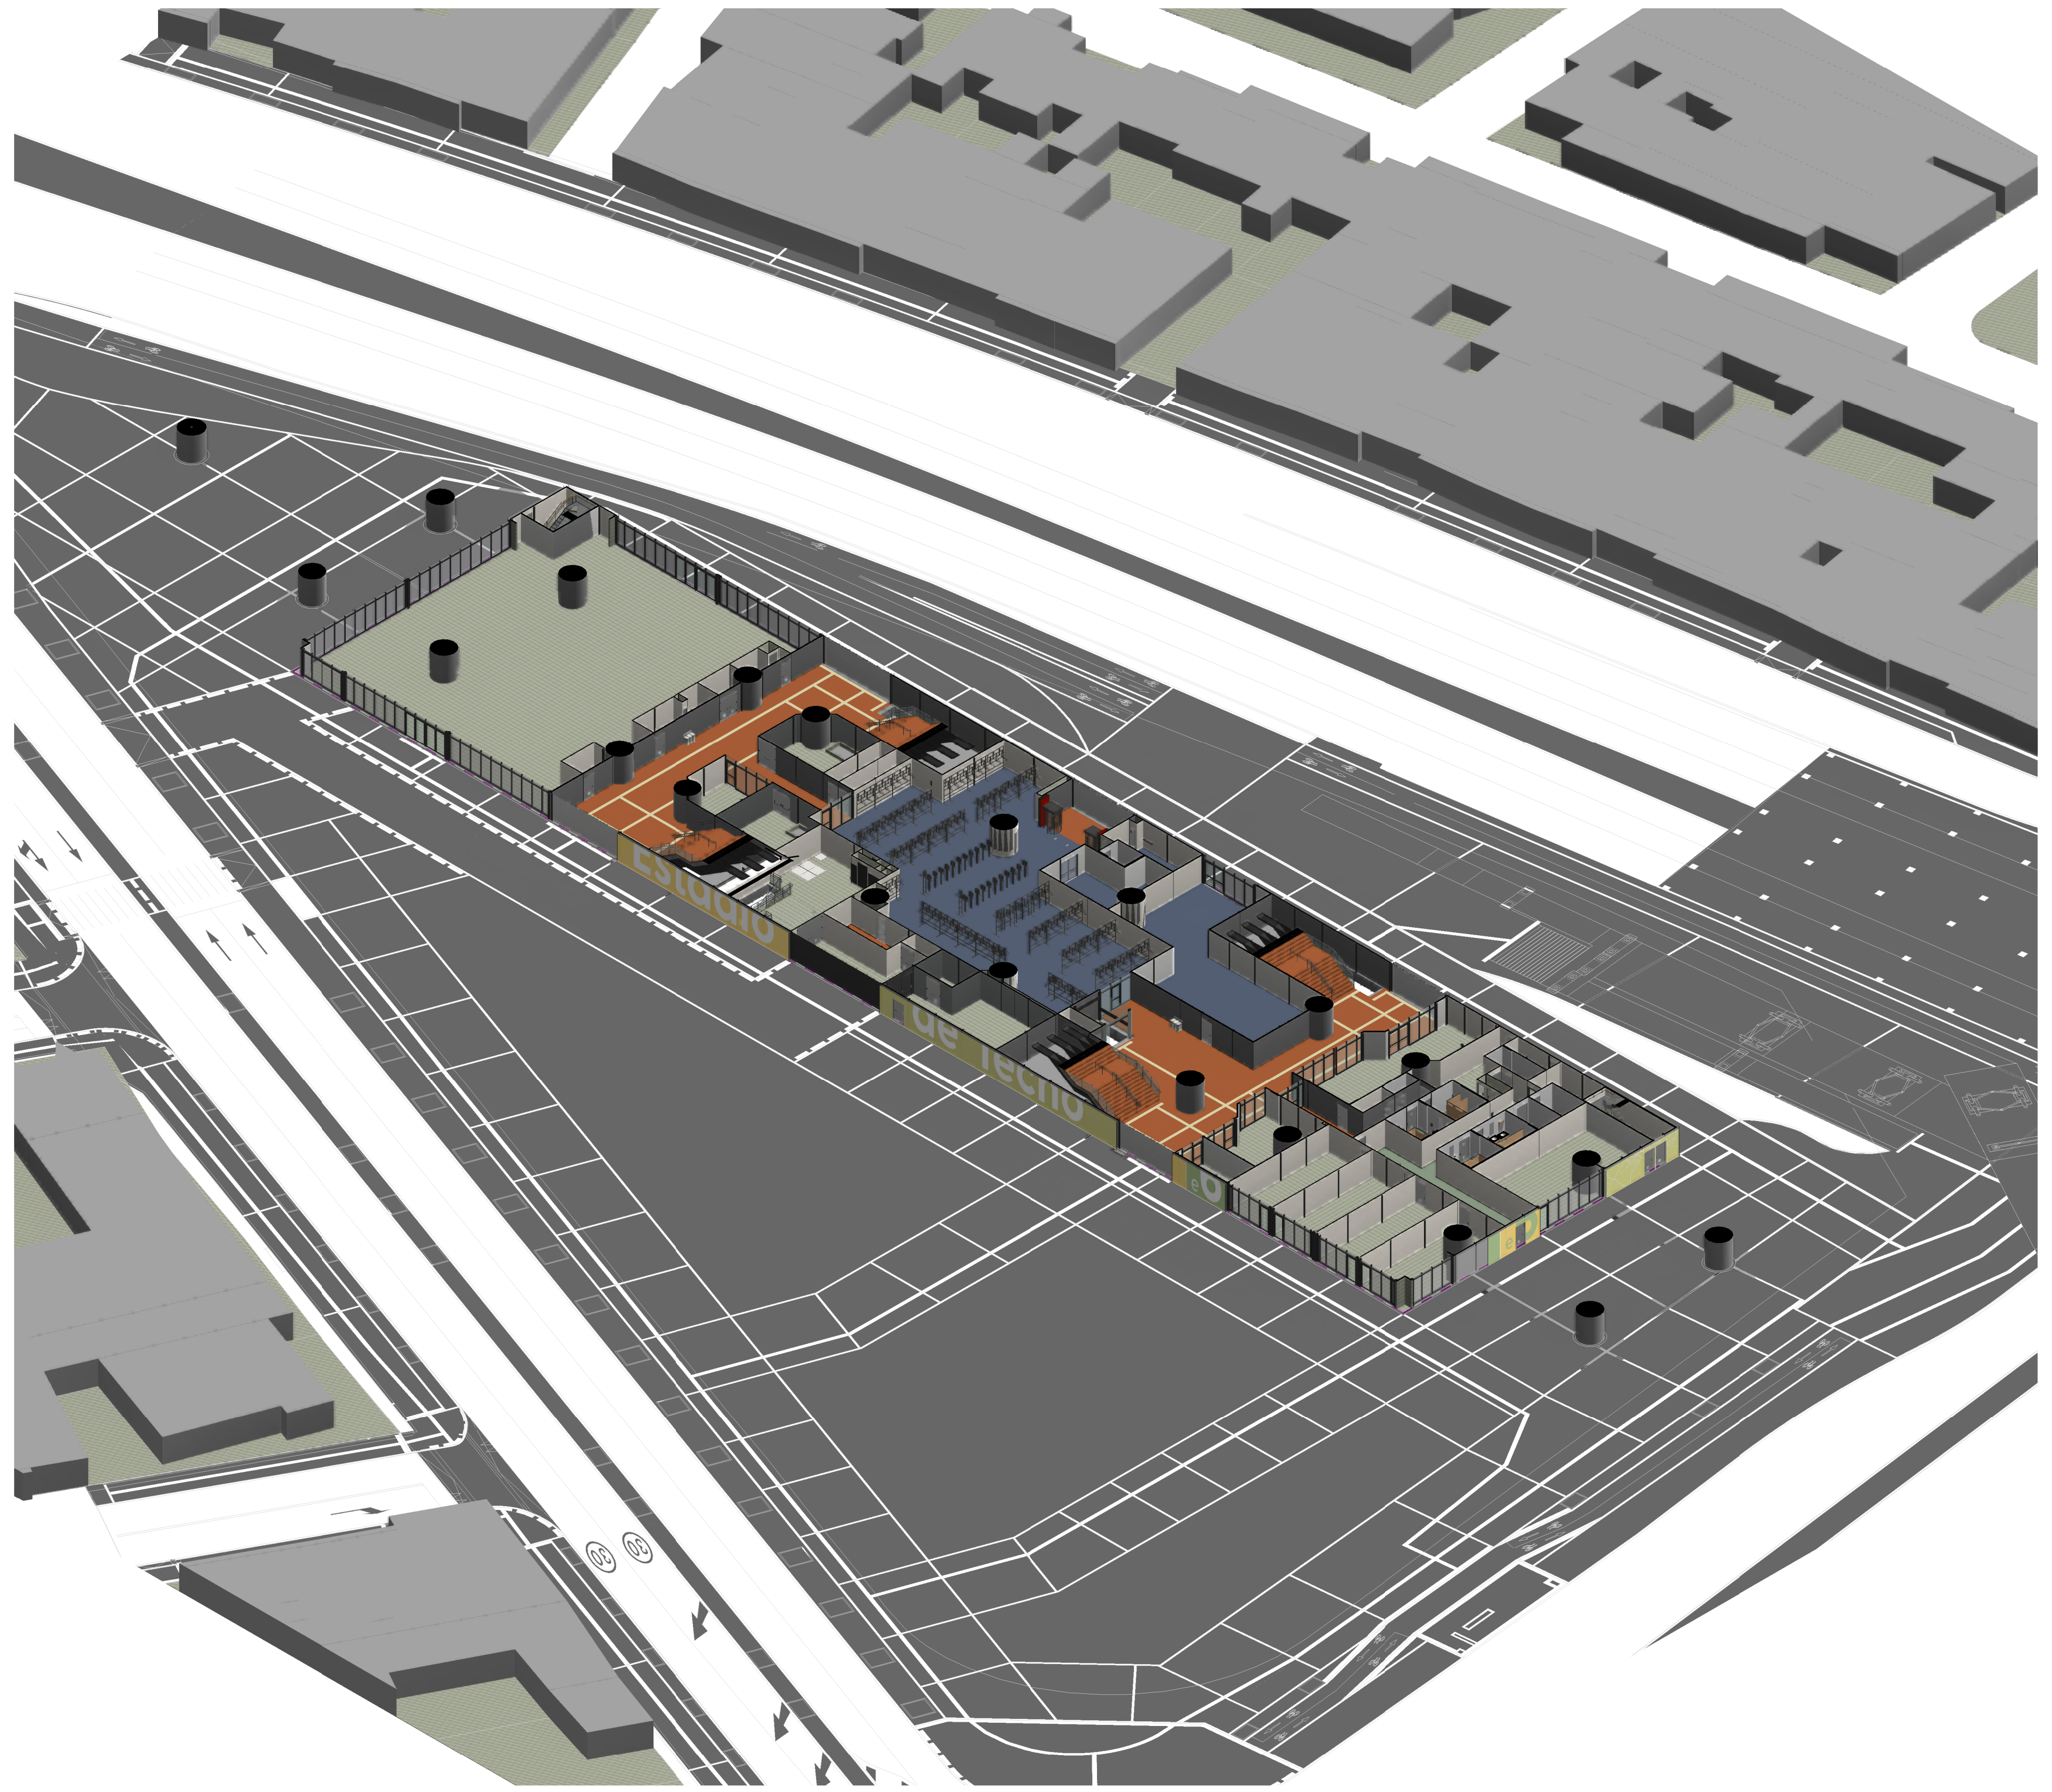

1 **3D_NIVEL ACCESO_NAVE CENTRAL**
ESC: N/A

TABLA DE ÁREAS ÚTILES (NIVEL ACCESO)

CÓDIGO	NOMBRE	ÁREA (m²)	DEPARTAMENTO
NAVE CENTRAL			
ARQ_PL_01_ACCESO			
CADE	CADE	857.70	CADE
NPA-01	ÁREA NO PAGA	289.48	ÁREA NO PAGA
NPA-02	ÁREA NO PAGA	317.51	ÁREA NO PAGA
NPA-03	ÁREA NO PAGA	23.41	ÁREA NO PAGA
O-21-1	ALMACENAMIENTO DE LA ESTACIÓN	23.99	ÁREA OPERATIVA
P-01	ÁREA CICLO-PARQUEADEROS	552.75	ÁREA PÚBLICA
P-02	ÁREA OPERATIVA CICLO-PARQUEADEROS	26.44	ÁREA PÚBLICA
P-03	BAÑO OPERADOR CICLO-PARQUEADEROS	6.49	ÁREA PÚBLICA
P-04	TALLER DE BICICLETAS	45.28	ÁREA PÚBLICA
P-05	BIBLIOMETRO	50.24	ÁREA PÚBLICA
P-06	ESPACIO IPES (INSTITUTO PARA LA ECONOMÍA SOCIAL)	18.54	ÁREA PÚBLICA
P-07	SALÓN MÚLTIPLE EMB	100.24	ÁREA PÚBLICA
P-08	ESPACIO CARGA DE VEHÍCULOS ELÉCTRICOS	203.34	ÁREA PÚBLICA
R-00-1	SERVICIOS ADICIONALES - CORREDOR OPERATIVO	90.11	SERVICIOS ADICIONALES - ÁREA NO PAGA
R-00-2	SERVICIOS ADICIONALES - CORREDOR OPERATIVO	38.38	SERVICIOS ADICIONALES - ÁREA NO PAGA
R-01	SERVICIOS ADICIONALES - CUARTO DE BASURAS PARA METRO	10.19	SERVICIOS ADICIONALES - ÁREA NO PAGA
R-02	SERVICIOS ADICIONALES - BAÑO PÚBLICO DE MUJERES	15.86	SERVICIOS ADICIONALES - ÁREA NO PAGA
R-03	SERVICIOS ADICIONALES - BAÑO PÚBLICO DE HOMBRES	15.99	SERVICIOS ADICIONALES - ÁREA NO PAGA
R-04	SERVICIOS ADICIONALES - CONTROL DE ACCESO BAÑOS PÚBLICOS	5.28	SERVICIOS ADICIONALES - ÁREA NO PAGA
R-05	SERVICIOS ADICIONALES - CUARTO DE LIMPIEZA	4.00	SERVICIOS ADICIONALES - ÁREA NO PAGA
R-06	SERVICIOS ADICIONALES - BAÑOS EMPLEADOS MUJERES	14.30	SERVICIOS ADICIONALES - ÁREA NO PAGA
R-07	SERVICIOS ADICIONALES - VESTIDORES EMPLEADOS MUJERES	9.84	SERVICIOS ADICIONALES - ÁREA NO PAGA
R-08	SERVICIOS ADICIONALES - BAÑOS EMPLEADOS HOMBRES	14.17	SERVICIOS ADICIONALES - ÁREA NO PAGA
R-09	SERVICIOS ADICIONALES - VESTIDORES EMPLEADOS HOMBRES	10.21	SERVICIOS ADICIONALES - ÁREA NO PAGA
R-10	SERVICIOS ADICIONALES - SALA DE EMPLEADOS	15.24	SERVICIOS ADICIONALES - ÁREA NO PAGA
R-101	SERVICIOS ADICIONALES - ÁREA DE SERVICIO	31.17	SERVICIOS ADICIONALES - ÁREA NO PAGA
R-102	SERVICIOS ADICIONALES - ÁREA DE SERVICIO	97.04	SERVICIOS ADICIONALES - ÁREA NO PAGA
R-201	SERVICIOS ADICIONALES - ÁREA DE COMIDAS	58.07	SERVICIOS ADICIONALES - ÁREA NO PAGA
R-202	SERVICIOS ADICIONALES - ÁREA DE COMIDAS	58.12	SERVICIOS ADICIONALES - ÁREA NO PAGA
R-203	SERVICIOS ADICIONALES - ÁREA DE COMIDAS	58.12	SERVICIOS ADICIONALES - ÁREA NO PAGA
R-204	SERVICIOS ADICIONALES - ÁREA DE COMIDAS	55.29	SERVICIOS ADICIONALES - ÁREA NO PAGA
T-00-2	CIRCULACIÓN TÉCNICA	94.53	ÁREA TÉCNICA
T-00-3	CIRCULACIÓN TÉCNICA	44.64	ÁREA TÉCNICA
T-02-1	UPS DEDICADA (CBTC)	44.88	ÁREA TÉCNICA
T-08-2	CENTRO DE TRANSFORMACIÓN ENEL-CODENSA (CT)_CUARTO BAJA TENSIÓN	13.73	ÁREA TÉCNICA
T-08-3	CENTRO DE TRANSFORMACIÓN ENEL-CODENSA (CT)_CUARTO MEDIA TENSIÓN	76.57	ÁREA TÉCNICA
T-20-G	MEDIDORES (GAS)	8.13	ÁREA TÉCNICA
T-20-L-1	MEDIDORES (LUZ)	11.16	ÁREA TÉCNICA
T-20-W	MEDIDORES (AGUA)	11.23	ÁREA TÉCNICA
T-21-1	ÁREA DE INSPECCIÓN	8.70	ÁREA TÉCNICA
T-21-2	ÁREA DE INSPECCIÓN	17.30	ÁREA TÉCNICA
T-21-3	ÁREA DE INSPECCIÓN	7.89	ÁREA TÉCNICA
T-21-4	ÁREA DE INSPECCIÓN	34.98	ÁREA TÉCNICA
T-24	TETRA UPS	43.72	ÁREA TÉCNICA
T-25-2	NODO DE ACCESO DE TELECOMUNICACIONES	4.85	ÁREA TÉCNICA
T-25-3	NODO DE ACCESO DE TELECOMUNICACIONES	7.30	ÁREA TÉCNICA
T-30	SISTEMA PROTECCIÓN CONTRA INCENDIO ENEL	4.90	ÁREA TÉCNICA
TOTAL NIVEL ACCESO		3551.32	

TABLA DE ÁREAS ÚTILES POR DEPARTAMENTO (NIVEL ACCESO)

DEPARTAMENTO	ÁREA (m²)
CADE	857.70
SERVICIOS ADICIONALES - ÁREA NO PAGA	601.38
ÁREA NO PAGA	630.40
ÁREA OPERATIVA	23.99
ÁREA PÚBLICA	1003.31
ÁREA TÉCNICA	434.53
TOTAL NIVEL ACCESO	3551.32

TABLA DE CICLO-PARQUEADEROS ESPECÍFICA

DESCRIPCIÓN	CANTIDAD (und)	USUARIOS
BICIPARQUEADERO ASISTIDO EN ACERO INOXIDABLE ASTM A240, a=0.70m X l=1.20m, h=1.70m.	1	EMPLEADOS
BICIPARQUEADERO DE COLGAR, 2 PUESTOS, a=1.20m X l=0.70m, h=2.40m. ACABADO EN PINTURA ELECTROSTÁTICA COLOR RAL9005 "NEGRO INTENSO".	4	EMPLEADOS
EMPLEADOS	5	
BICIPARQUEADERO ASISTIDO EN ACERO INOXIDABLE ASTM A240, a=0.70m X l=1.20m, h=1.70m.	51	VISITANTE
BICIPARQUEADERO DE COLGAR, 1 PUESTO, a=1.20m X l=0.70m, h=2.40m. ACABADO EN PINTURA ELECTROSTÁTICA COLOR RAL9005 "NEGRO INTENSO".	10	VISITANTE
BICIPARQUEADERO DE COLGAR, 2 PUESTOS, a=1.20m X l=0.70m, h=2.40m. ACABADO EN PINTURA ELECTROSTÁTICA COLOR RAL9005 "NEGRO INTENSO".	32	VISITANTE
BICIPARQUEADERO DE COLGAR DE 6 PUESTOS EN ACERO, a=1.20m X l=2.10m, h=2.40m. ACABADO EN PINTURA ELECTROSTÁTICA COLOR RAL9005 "NEGRO INTENSO".	402	VISITANTE
VISITANTE	495	
TOTAL CUPOS	500	

LOCALIZACIÓN

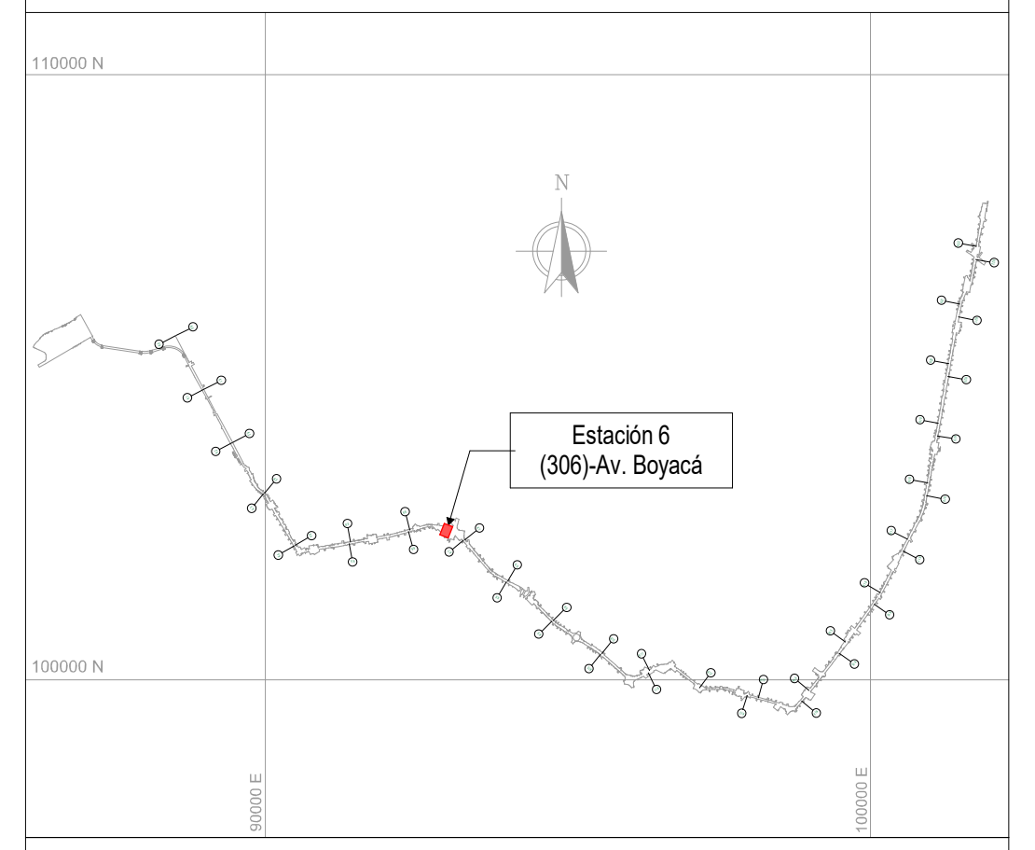

NOTAS

01 TODAS LAS DIMENSIONES ESTÁN CONFIGURADAS EN METROS A MENOS QUE SE INDIQUE UNA UNIDAD DE MEDIDA DIFERENTE.

02 TODAS LAS MEDIDAS, UBICACIÓN Y NIVELES DEBEN VERIFICARSE EN EL LUGAR DE CONSTRUCCIÓN.

03 EL NIVEL DE ACCESO AL EDIFICIO PL 01 CORRESPONDE AL +0,00 DE LA ESTACIÓN Y REFERENCIA AL NIVEL 2555.50 M.S.N.M

04 LOS NOMBRES ESPECÍFICOS DE LAS ÁREAS PUEDEN SER CONSULTADAS EN EL PLANO NO. 3 Ó EN LAS VISTAS EN PLANTA.

05 LOS COLORES QUE SE MUESTRAN EN LOS PLANOS COMO PROYECCIÓN DE ELEMENTOS ARQUITECTÓNICOS COMO CUBIERTAS, FACHADAS, MUROS, ETC. NO REPRESENTAN LA MATERIALIDAD Y REALIDAD DE ACABADOS DEL PROYECTO, SOLO SON INDICATIVOS PARA REALIZAR UNA CORRECTA LECTURA DE LA PLANIMETRÍA.

06 LAS ESCALERAS ELÉCTRICAS INDICAN SU SENTIDO CON LA SIGUIENTE NOMENCLATURA: "SUBE" Y "BAJA".

07 SE DEBEN REVISAR LOS NIVELES ESTRUCTURALES PARA NIVEL DE ACCESO PL_01 Y SUBNIVELES, PL_02 (INTERMEDIO), PL_03 (PLATAFORMA) CON LA PLANIMETRIA DE PLACAS ESTRUCTURALES EN LOS ENTREGABLES LL1T1-1200-306-CON-ED-EST-PL-0017, 20, 21, RESPECTIVAMENTE. EL NIVEL ESTRUCTURAL (NE) REFERENCIA LOS ESPACIOS DONDE SE DEBE ACONDICIONAR EL ACABADO DE PISO SEGÚN CORRESPONDA, CON LOS NIVELES DE PISO TERMINADO (NPT). LOS NIVELES PROYECTADOS DE EMPATE (NPE) EN LAS ÁREAS DE SERVICIOS ADICIONALES, REFERENCIAN LA ADECUACIÓN DE LOS DESNIVELES EN ESTAS ÁREAS; QUEDA COMO RESPONSABILIDAD DEL LOCATARIO DEFINIR Y ACONDICIONAR ESTE ACABADO DE PISO (NPE) EN LÍNEA CON EL NIVEL (NPT) DE ESPACIOS COLINDANTES. EL NIVEL ESTRUCTURAL (NE) SE ENCUENTRA A (- 0.10M) POR DEBAJO DE LOS NIVELES DE PISO TERMINADO (NPT) Y LOS NIVELES PROYECTADOS DE EMPATE (NPE) MARCADOS EN LA PLANIMETRÍA.

- ARQ_PL_00 = SÓTANO / NPT -5.80
- ARQ_PL_01 = ACCESO / NPT 0.00
- ARQ_PL_02 = INTERMEDIO / NPT 7.60
- ARQ_PL_02.1= PLACA INFERIOR VIGA CAJÓN / NPT 13.82
- ARQ_PL_02.2 = TOPE DE RIEL (TOR) / NPT 15.95
- ARQ_PL_03 = PLATAFORMA / NPT 17.09
- ARQ_PL_05 = CUBIERTA NAVE CENTRAL / NPT 26.53

CONVENCIONES

- - - -	LÍMITE DE INTERVENCIÓN
- - - -	HUELLA APÉNDICE TÉCNICO
▬	MURO DIVISORIO
— — —	PROYECCIÓN NIVEL SUPERIOR
▨	CADE
▨	SERVICIOS ADICIONALES - ÁREA NO PAGA
🟩	SERVICIOS ADICIONALES - ÁREA PAGA
🟩	SERVICIO PÚBLICO
🟦	ZONA DE REFUGIO
🟥	ÁREA CULTURAL
🟨	ÁREA NO PAGA
🟦	ÁREA OPERATIVA
🟧	ÁREA PAGA
🟦	ÁREA PÚBLICA
▨	ÁREA TÉCNICA

No.	PLANOS DE REFERENCIA	REV.

No.	MODELO BIM DE REFERENCIA	REV.
1	L1T1-1100-206-CON-ED-EST-MO-0001.rvt	V00
2	L1T1-1100-207-CON-ED-EST-MO-0001.rvt	V00
3	L1T1-1100-306-CON-ED-EST-MO-0001.rvt	V00
4	L1T1-1150-206-CON-ED-EST-MO-0001.rvt	V00
5	L1T1-1150-207-CON-ED-EST-MO-0001.rvt	V00
6	L1T1-1150-306-CON-ED-EST-MO-0001.rvt	V00
7	L1T1-1200-306-CON-ED-CIV-MO-0001.rvt	V00
8	L1T1-1410-306-CON-ED-MEC-MO-0001.rvt	V00
9	L1T1-1420-306-CON-ED-MEC-MO-0001.rvt	V00
10	L1T1-5160-306-CON-ED-EST-MO-0001.rvt	V00
11	L1T1-5160-306-CON-ED-ARQ-MO-0001.rvt	V00
12	L1T1-5300-306-CON-ED-MEC-MO-0001.rvt	V00
13	L1T1-5600-306-CON-ED-INS-MO-0001.rvt	V00
14	L1T1-1270-306-CON-ED-ARQ-MO-0011.rvt	V00

No.	PAQUETE DE TRABAJO DE REFERENCIA	REV.
1	XREF-URBANISM_CONTEXT_ST06.rvt	

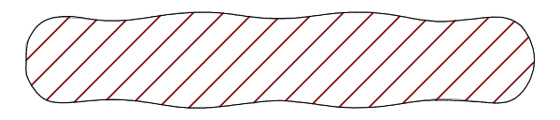

PLANO CLAVE ESTACIÓN 6

0 2 10m
1:200

VÁLIDO PARA CONSTRUCCIÓN
20-03-26

METRO BOGOTÁ
GCS Consorcio Consultores PMO Bogotá
CONSORCIO SUPERVISOR PLMB
CHEC

DISEÑÓ:
REN ZHENHUA
Licencia de Arq.nivel I (China): 1101735-614

REVISÓ:
CARLOS MAURICIO BARRETO BARBOSA
Mat.: A4012012-14139353

APROBÓ:
DIEGO ERNESTO DUEÑAS
Mat.: 25202-53876 CND

DIBUJÓ:
EQUIPO CHEC

REVISIÓN No.	FECHA	DESCRIPCIÓN	REVISÓ	APROBÓ	APROBACIÓN CLIENTE
V01	20/03/2026	EMITIDO PARA CONSTRUCCIÓN	C.M.B.B	D.E.D	
V00	25/11/2024	REVISIÓN NO OBJETADA - EMITIDO PARA CONSTRUCCIÓN	F.B.R	E.O.M	
VGG	15/05/2024	EMITIDO PARA REVISIÓN Y COMENTARIOS DEL CLIENTE E INTERVENTORÍA - INCLUYE COMENTARIOS /(AJUSTES V4)	F.B.R	E.O.M	
VFF	22/12/2023	EMITIDO PARA REVISIÓN Y COMENTARIOS DEL CLIENTE E INTERVENTORÍA - INCLUYE COMENTARIOS /(AJUSTES V3)	F.B.R	M.B.M	
VEE	30/06/2023	EMITIDO PARA REVISIÓN Y COMENTARIOS DEL CLIENTE E INTERVENTORÍA - INCLUYE COMENTARIOS /(AJUSTES V2)	J.E.M	M.B.M	
VDD	18/12/2022	EMITIDO PARA REVISIÓN Y COMENTARIOS DEL CLIENTE E INTERVENTORÍA - INCLUYE COMENTARIOS /(AJUSTES)	J.E.M	M.B.M	
VCC	20/06/2022	EMITIDO PARA REVISIÓN Y COMENTARIOS DEL CLIENTE E INTERVENTORÍA - INCLUYE COMENTARIOS /(ENTREGA 90%)	J.E.M	M.B.M	
VBB	06/12/2021	EMITIDO PARA REVISIÓN Y COMENTARIOS DEL CLIENTE E INTERVENTORÍA	J.E.M	M.B.M	
VA0	30/06/2021	EMITIDO PARA COMENTARIOS INTERNOS - EMISIÓN PRELIMINAR PARA COMENTARIOS	J.E.M	M.B.M	

METRO LÍNEA 1

DIRECTOR DE INTERVENTORÍA:
JAVIER DESCARGA N.
Mat.:25202-68697 CND

ESPECIALISTA INTERVENTORÍA:
CARLOS ALBERTO HOYOS SOTO
Mat.:A25072000-14251682

FECHA:
MARZO 2026

METRO LÍNEA 1
CONTRATO DE CONCESIÓN No. 163 DE 2019

PROYECTO PRIMERA LÍNEA DEL METRO DE BOGOTÁ - TRAMO 1

INFRAESTRUCTURA VIAL

ARQUITECTURA

ESTACIÓN METRO 6 (AVENIDA BOYACÁ)
NAVE CENTRAL
VISTA EN PLANTA Y 3D - NIVEL ACCESO

PLANCHA No: L1T1-0000-306-CON-ED-ARQ-PL-0001_05_V01
ARCHIVO: L1T1-0000-306-CON-ED-ARQ-MO-0001_V00.rvt
ESCALA: INDICADA
FECHA: JUNIO 2021
REVISIÓN No. V01
PLANO No. 05 DE 47