L1T1-CON-CAL-FR-0120 - B1 : 1000x707mm

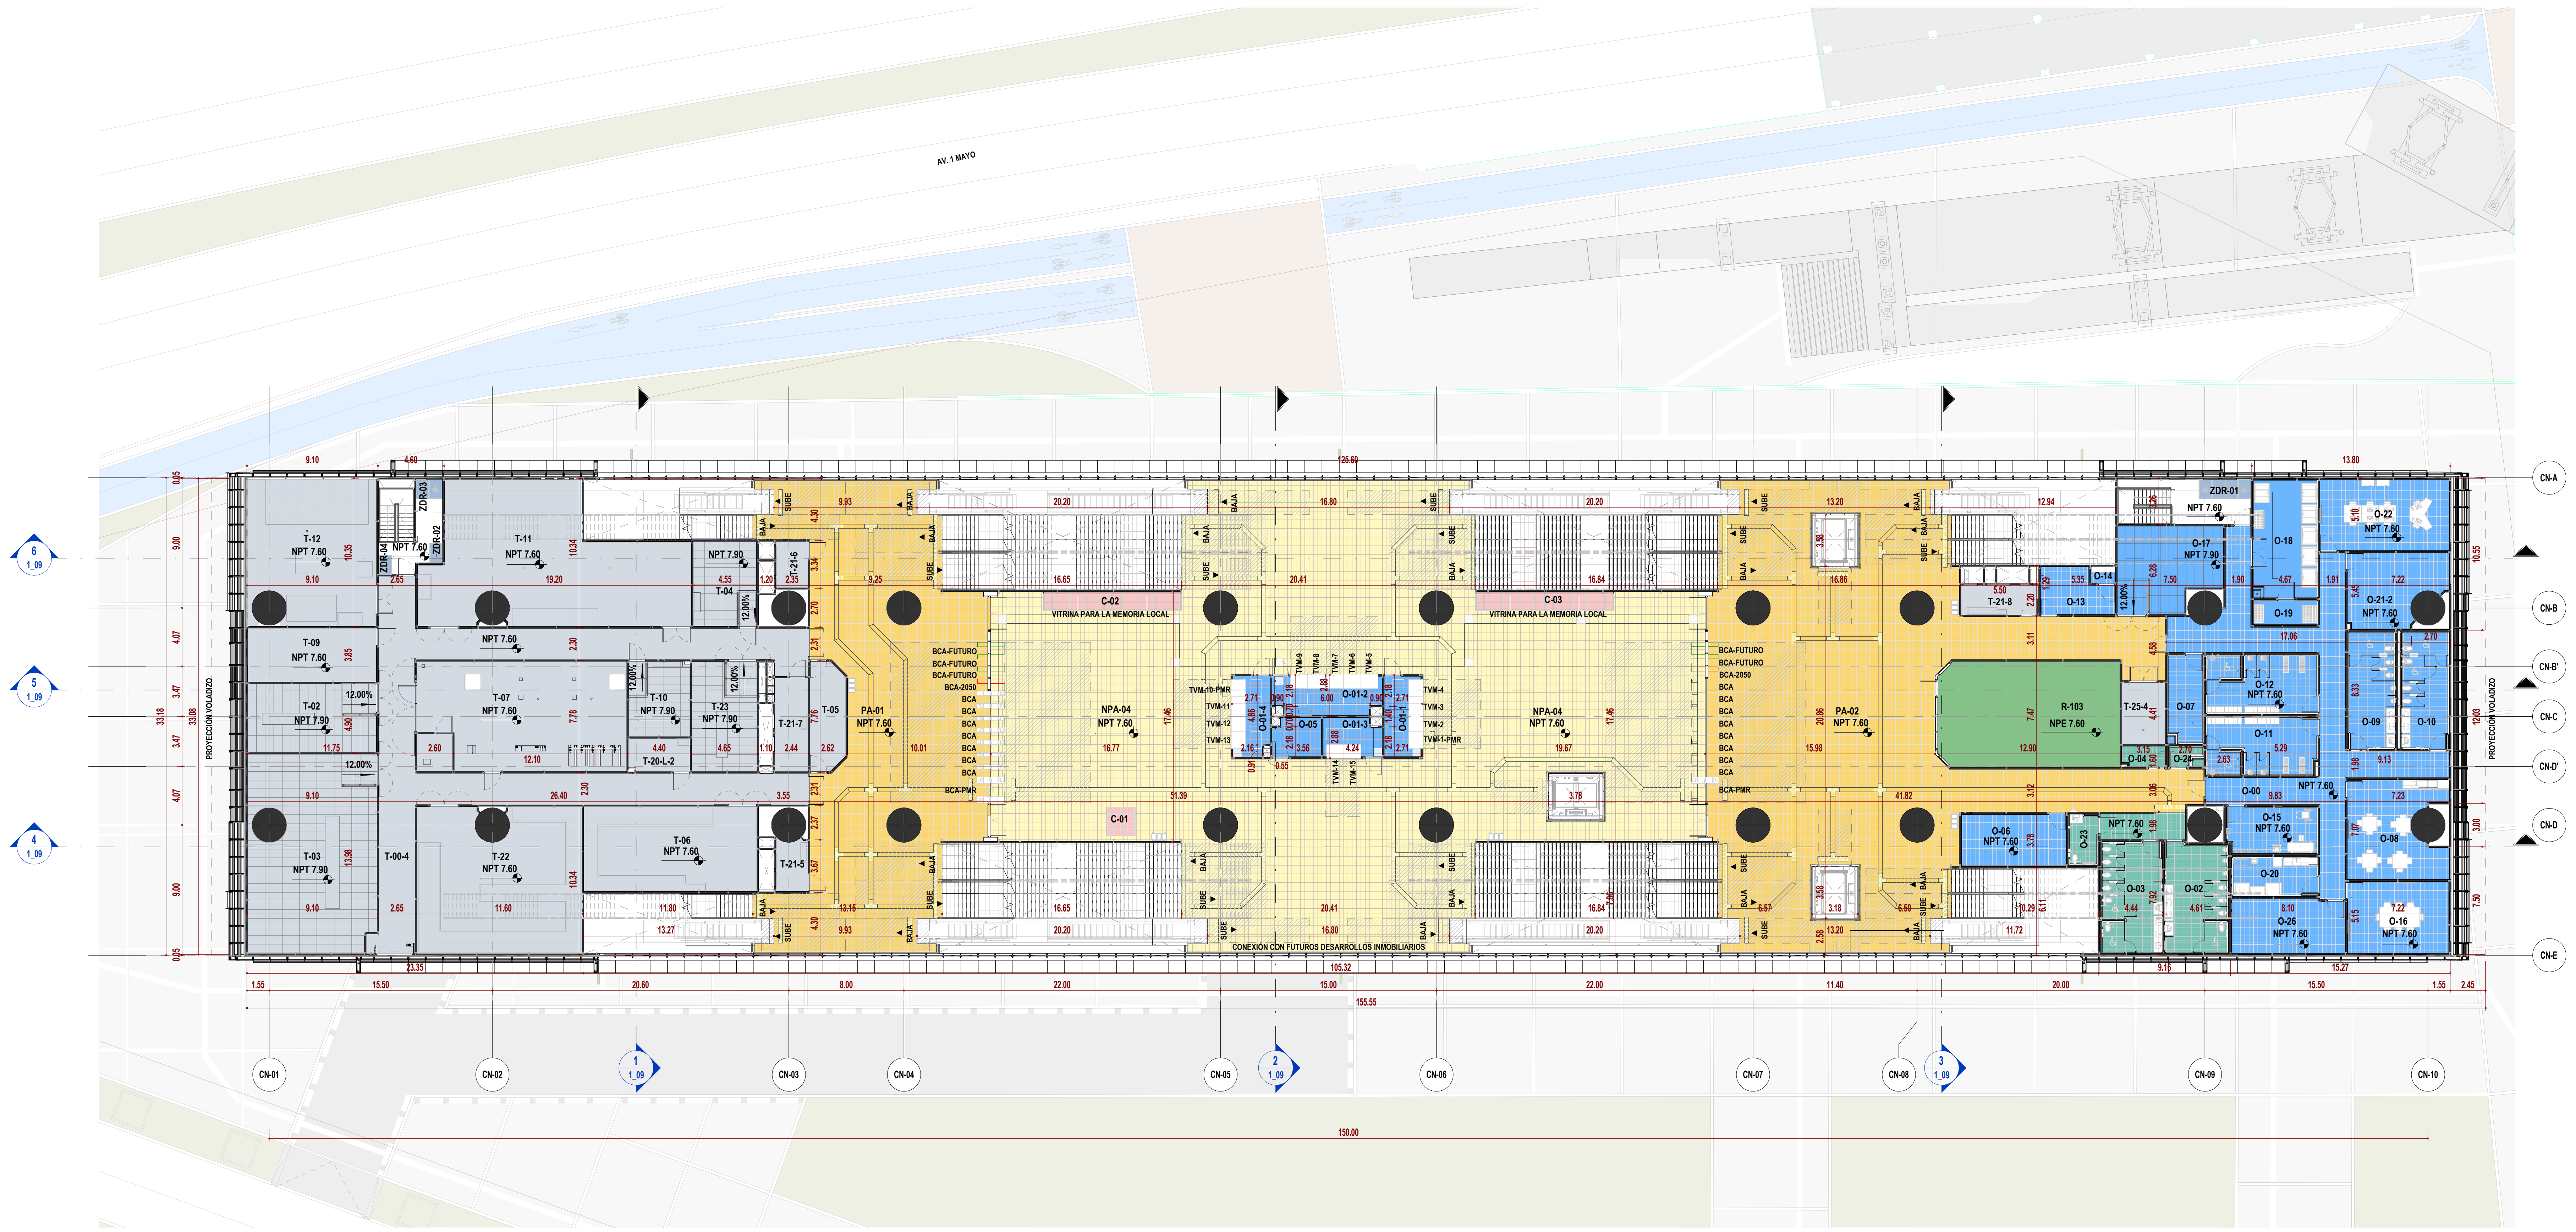

2 NIVEL INTERMEDIO_NAVE CENTRAL
ESC: 1 : 200

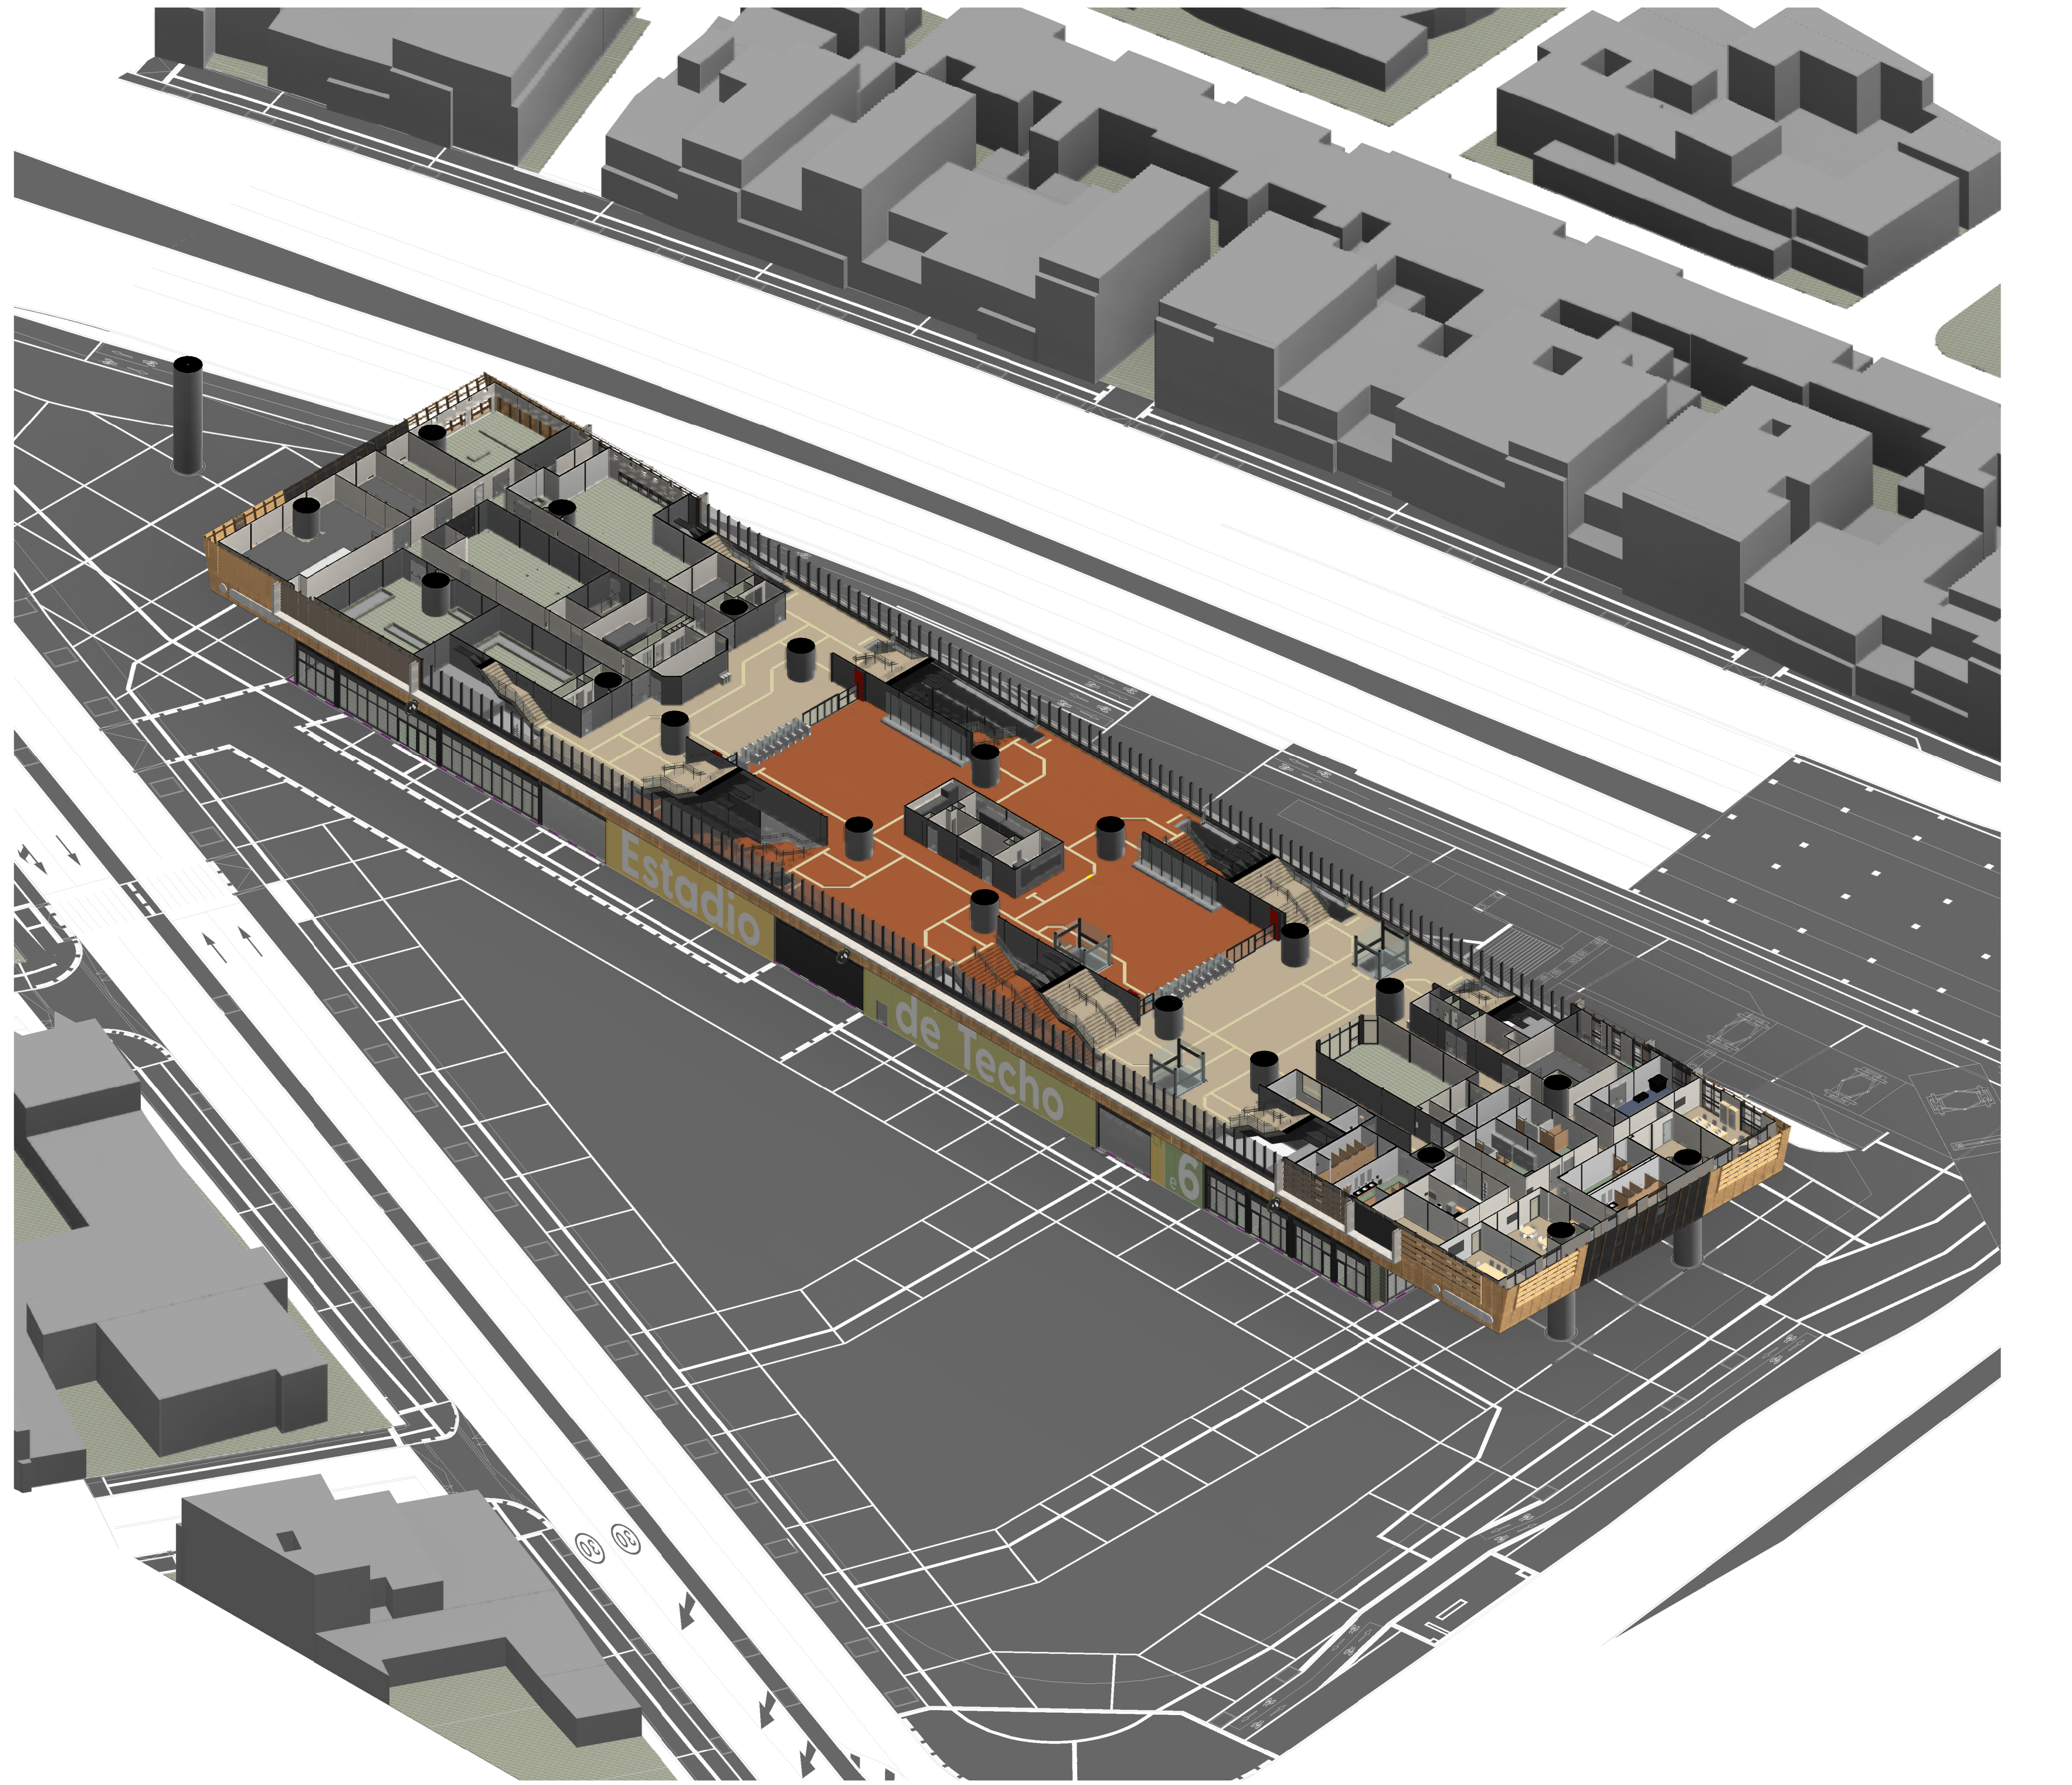

1 3D_NIVEL INTERMEDIO_NAVE CENTRAL
ESC: N/A

TABLA DE ÁREAS ÚTILES (NIVEL INTERMEDIO)

CÓDIGO	NOMBRE	ÁREA (m²)	DEPARTAMENTO
NAVE CENTRAL			
ARQ_PL_02_INTERMEDIO			
C-01	ÁREAS DE USO CULTURAL	4.00	ÁREA CULTURAL
C-02	ÁREAS DE USO CULTURAL	12.82	ÁREA CULTURAL
C-03	ÁREAS DE USO CULTURAL	12.79	ÁREA CULTURAL
NPA-04	ÁREA NO PAGA	1033.90	ÁREA NO PAGA
O-00	CIRCULACIÓN ÁREAS OPERATIVAS	105.53	ÁREA OPERATIVA
O-01-1	VENTA AUTOMÁTICA DE BOLETOS	14.50	ÁREA OPERATIVA
O-01-2	VENTA AUTOMÁTICA DE BOLETOS	19.93	ÁREA OPERATIVA
O-01-3	VENTA AUTOMÁTICA DE BOLETOS	10.75	ÁREA OPERATIVA
O-01-4	VENTA AUTOMÁTICA DE BOLETOS	14.01	ÁREA OPERATIVA
O-02	BAÑOS PÚBLICOS DE HOMBRES	33.42	SERVICIO PÚBLICO
O-03	BAÑOS PÚBLICOS DE MUJERES	32.53	SERVICIO PÚBLICO
O-04	CONTROL DE ACCESO BAÑOS PÚBLICOS	4.31	SERVICIO PÚBLICO
O-05	LOCAL DE INFORMACIÓN	9.08	ÁREA OPERATIVA
O-06	OFICINA DEL SUPERVISOR DE LA ESTACIÓN	25.79	ÁREA OPERATIVA
O-07	CUARTO DE LIMPIEZA	15.81	ÁREA OPERATIVA
O-08	SALA DE DESCANSO PARA EMPLEADOS	42.47	ÁREA OPERATIVA

TABLA DE ÁREAS ÚTILES (NIVEL INTERMEDIO)

CÓDIGO	NOMBRE	ÁREA (m²)	DEPARTAMENTO
O-09	BAÑOS EMPLEADOS HOMBRES	26.93	ÁREA OPERATIVA
O-10	BAÑOS EMPLEADOS MUJERES	26.94	ÁREA OPERATIVA
O-11	VESTIDORES EMPLEADOS HOMBRES	31.14	ÁREA OPERATIVA
O-12	VESTIDORES EMPLEADOS MUJERES	31.58	ÁREA OPERATIVA
O-13	LOCAL DE POLICÍA	15.01	ÁREA OPERATIVA
O-14	CALABOZO	2.01	ÁREA OPERATIVA
O-15	LOCAL PRIMEROS AUXILIOS	21.06	ÁREA OPERATIVA
O-16	SALA DE REUNIONES	35.22	ÁREA OPERATIVA
O-17	OPERADORES TELECOMUNICACIONES EXTERIORES	40.46	ÁREA OPERATIVA
O-18	CUARTO DE ALMACENAMIENTO DE RESIDUOS SÓLIDOS	37.26	ÁREA OPERATIVA
O-19	CUARTO DE ALMACENAMIENTO DE RESIDUOS PELIGROSOS	7.95	ÁREA OPERATIVA
O-20	SALA DE LACTANCIA	16.26	ÁREA OPERATIVA
O-21-2	ALMACENAMIENTO DE LA ESTACIÓN	30.94	ÁREA OPERATIVA
O-22	OFICINA DE MANTENIMIENTO	44.67	ÁREA OPERATIVA
O-23	BAÑO PÚBLICO - FAMILIAR	7.11	SERVICIO PÚBLICO
O-24	CUARTO DE LIMPIEZA DE BAÑOS PÚBLICOS	3.51	SERVICIO PÚBLICO
O-25	BAÑO PÚBLICO - CORREDOR OPERACIONAL	10.99	SERVICIO PÚBLICO
O-26	ALMACENAMIENTO DE BASURAS METRO	30.16	ÁREA OPERATIVA

TABLA DE ÁREAS ÚTILES (NIVEL INTERMEDIO)

CÓDIGO	NOMBRE	ÁREA (m²)	DEPARTAMENTO
PA-01	ÁREA PAGA	358.19	ÁREA PAGA
PA-02	ÁREA PAGA	599.21	ÁREA PAGA
R-103	SERVICIOS ADICIONALES - ÁREA DE SERVICIO	91.55	SERVICIOS ADICIONALES - ÁREA PAGA
T-00-4	CIRCULACIÓN TÉCNICA	190.06	ÁREA TÉCNICA
T-02	LOCAL DE CONDUCCIÓN AUTOMÁTICA (CBTC)	42.85	ÁREA TÉCNICA
T-03	TELECOMUNICACIONES ESTACIÓN - CORRIENTE DÉBIL	118.92	ÁREA TÉCNICA
T-04	EQUIPO BOLETERÍA	26.40	ÁREA TÉCNICA
T-05	ALMACÉN PARA MANTENIMIENTO	17.90	ÁREA TÉCNICA
T-06	SALA DE TABLEROS	70.99	ÁREA TÉCNICA
T-07	CENTRO DE TRANSFORMACIÓN (CT)	111.50	ÁREA TÉCNICA
T-09	ALMACÉN EQUIPO ELÉCTRICO	33.46	ÁREA TÉCNICA
T-10	CUARTO DE EQUIPO ELECTROMECÁNICO	22.27	ÁREA TÉCNICA
T-11	CUARTO DE VENTILACIÓN	144.24	ÁREA TÉCNICA
T-12	PLANTA DE REFRIGERACIÓN PARA LA CLIMATIZACIÓN	86.55	ÁREA TÉCNICA
T-20-L-2	MEDIDORES (LUZ)	9.80	ÁREA TÉCNICA
T-21-5	ÁREA DE INSPECCIÓN	7.87	ÁREA TÉCNICA
T-21-6	ÁREA DE INSPECCIÓN	7.14	ÁREA TÉCNICA
T-21-7	ÁREA DE INSPECCIÓN	15.20	ÁREA TÉCNICA

TABLA DE ÁREAS ÚTILES (NIVEL INTERMEDIO)

CÓDIGO	NOMBRE	ÁREA (m²)	DEPARTAMENTO
T-21-8	ÁREA DE INSPECCIÓN	11.08	ÁREA TÉCNICA
T-22	CUARTO DE UPS	112.27	ÁREA TÉCNICA
T-23	CUARTO PDAP	34.84	ÁREA TÉCNICA
T-25-4	NODO DE ACCESO DE TELECOMUNICACIONES	13.01	ÁREA TÉCNICA
ZDR-01	ZONA DE REFUGIO (PMR)	4.81	ZONA DE REFUGIO
ZDR-02	ZONA DE REFUGIO (PMR)	1.20	ZONA DE REFUGIO
ZDR-03	ZONA DE REFUGIO (PMR)	2.47	ZONA DE REFUGIO
ZDR-04	ZONA DE REFUGIO (PMR)	1.22	ZONA DE REFUGIO
TOTAL NIVEL INTERMEDIO		3945.82	

TABLA DE ÁREAS ÚTILES POR DEPARTAMENTO (NIVEL INTERMEDIO)

DEPARTAMENTO	ÁREA (m²)
SERVICIO PÚBLICO	91.88
SERVICIOS ADICIONALES - ÁREA PAGA	91.55
ZONA DE REFUGIO	9.70
ÁREA CULTURAL	29.61
ÁREA NO PAGA	1033.90
ÁREA OPERATIVA	655.45
ÁREA PAGA	957.40
ÁREA TÉCNICA	1076.33
TOTAL NIVEL INTERMEDIO	3945.82

LOCALIZACIÓN

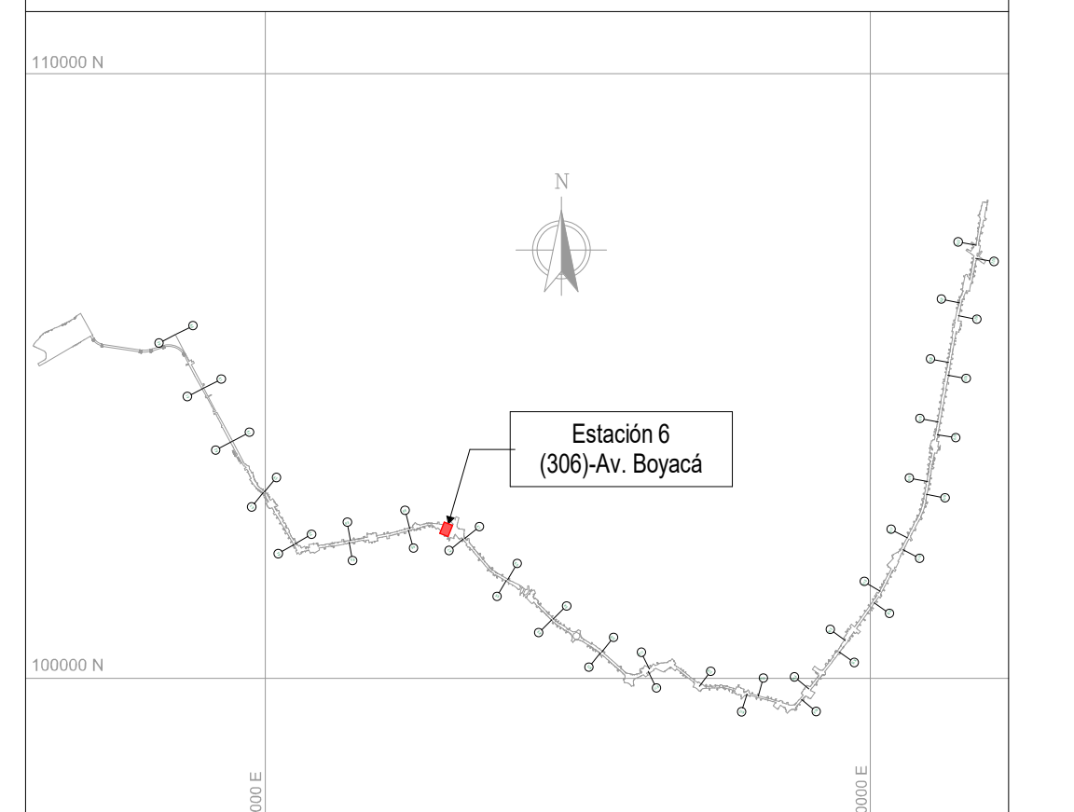

NOTAS

01 TODAS LAS DIMENSIONES ESTÁN CONFIGURADAS EN METROS A MENOS QUE SE INDIQUE UNA UNIDAD DE MEDIDA DIFERENTE.

02 TODAS LAS MEDIDAS, UBICACIÓN Y NIVELES DEBEN VERIFICARSE EN EL LUGAR DE CONSTRUCCIÓN.

03 EL NIVEL DE ACCESO AL EDIFICIO PL 01 CORRESPONDE AL +0,00 DE LA ESTACIÓN Y REFERENCIA AL NIVEL 2555.50 M.S.N.M

04 LOS NOMBRES ESPECÍFICOS DE LAS ÁREAS PUEDEN SER CONSULTADAS EN EL PLANO NO. 3 Ó EN LAS VISTAS EN PLANTA.

05 LOS COLORES QUE SE MUESTRAN EN LOS PLANOS COMO PROYECCIÓN DE ELEMENTOS ARQUITECTÓNICOS COMO CUBIERTAS, FACHADAS, MUROS, ETC. NO REPRESENTAN LA MATERIALIDAD Y REALIDAD DE ACABADOS DEL PROYECTO, SOLO SON INDICATIVOS PARA REALIZAR UNA CORRECTA LECTURA DE LA PLANIMETRÍA.

06 LAS ESCALERAS ELÉCTRICAS INDICAN SU SENTIDO CON LA SIGUIENTE NOMENCLATURA: "SUBE" Y "BAJA".

07 SE DEBEN REVISAR LOS NIVELES ESTRUCTURALES PARA NIVEL DE ACCESO PL_01 Y SUBNIVELES, PL_02 (INTERMEDIO), PL_03 (PLATAFORMA) CON LA PLANIMETRIA DE PLACAS ESTRUCTURALES EN LOS ENTREGABLES LL1T1-1200-306-CON-ED-EST-PL-0017, 20, 21, RESPECTIVAMENTE. EL NIVEL ESTRUCTURAL (NE) REFERENCIA LOS ESPACIOS DONDE SE DEBE ACONDICIONAR EL ACABADO DE PISO SEGÚN CORRESPONDA, CON LOS NIVELES DE PISO TERMINADO (NPT). LOS NIVELES PROYECTADOS DE EMPATE (NPE) EN LAS ÁREAS DE SERVICIOS ADICIONALES, REFERENCIAN LA ADECUACIÓN DE LOS DESNIVELES EN ESTAS ÁREAS; QUEDA COMO RESPONSABILIDAD DEL LOCATARIO DEFINIR Y ACONDICIONAR ESTE ACABADO DE PISO (NPE) EN LÍNEA CON EL NIVEL (NPT) DE ESPACIOS COLINDANTES. EL NIVEL ESTRUCTURAL (NE) SE ENCUENTRA A (- 0.10M) POR DEBAJO DE LOS NIVELES DE PISO TERMINADO (NPT) Y LOS NIVELES PROYECTADOS DE EMPATE (NPE) MARCADOS EN LA PLANIMETRÍA.

- ARQ_PL_00 = SÓTANO	/ NPT -5.80	- ARQ_PL_02.1= PLACA INFERIOR VIGA CAJÓN	/ NPT 13.82
- ARQ_PL_01 = ACCESO	/ NPT 0.00	- ARQ_PL_02.2 = TOPE DE RIEL (TOR)	/ NPT 15.95
- ARQ_PL_02 = INTERMEDIO	/ NPT 7.60	- ARQ_PL_03 = PLATAFORMA	/ NPT 17.09
		- ARQ_PL_05 = CUBIERTA NAVE CENTRAL	/ NPT 26.53

CONVENCIONES

- - - -	LÍMITE DE INTERVENCIÓN
- - - -	HUELLA APÉNDICE TÉCNICO
■	MURO DIVISORIO
— — —	PROYECCIÓN NIVEL SUPERIOR
▨	CADE
▨	SERVICIOS ADICIONALES - ÁREA NO PAGA
🟩	SERVICIOS ADICIONALES - ÁREA PAGA
▨	SERVICIO PÚBLICO
🟦	ZONA DE REFUGIO
🟥	ÁREA CULTURAL
🟨	ÁREA NO PAGA
🟦	ÁREA OPERATIVA
🟧	ÁREA PAGA
▨	ÁREA PÚBLICA
▨	ÁREA TÉCNICA

No.	PLANOS DE REFERENCIA	REV.

No.	MODELO BIM DE REFERENCIA	REV.
1	L1T1-1100-206-CON-ED-EST-MO-0001.rvt	V00
2	L1T1-1100-207-CON-ED-EST-MO-0001.rvt	V00
3	L1T1-1100-306-CON-ED-EST-MO-0001.rvt	V00
4	L1T1-1150-206-CON-ED-EST-MO-0001.rvt	V00
5	L1T1-1150-207-CON-ED-EST-MO-0001.rvt	V00
6	L1T1-1150-306-CON-ED-EST-MO-0001.rvt	V00
7	L1T1-1200-306-CON-ED-CIV-MO-0001.rvt	V00
8	L1T1-1410-306-CON-ED-MEC-MO-0001.rvt	V00
9	L1T1-1420-306-CON-ED-MEC-MO-0001.rvt	V00
10	L1T1-5160-306-CON-ED-EST-MO-0001.rvt	V00
11	L1T1-5160-306-CON-ED-ARQ-MO-0001.rvt	V00
12	L1T1-5300-306-CON-ED-MEC-MO-0001.rvt	V00
13	L1T1-5600-306-CON-ED-INS-MO-0001.rvt	V00
14	L1T1-1270-306-CON-ED-ARQ-MO-0011.rvt	V00

No.	PAQUETE DE TRABAJO DE REFERENCIA	REV.
1	XREF-URBANISM_CONTEXT_ST06.rvt	

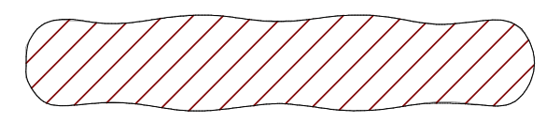

PLANO CLAVE ESTACIÓN 6

0 2 10m
1:200

VÁLIDO PARA CONSTRUCCIÓN
20-03-26

Consorcio Consultores PMO Bogotá
CONSORCIO SUPERVISOR PLMB

DISEÑÓ:
REN ZHENHUA
Licencia de Arq.nivel I (China): 1101735-614

APROBÓ:
DIEGO ERNESTO DUEÑAS
Mat.: 25202-53876 CND

REVISÓ:
CARLOS MAURICIO BARRETO BARBOSA
Mat.: A4012012-14139353

DIBUJÓ:
EQUIPO CHEC

REVISIÓN No.	FECHA	DESCRIPCIÓN	REVISÓ	APROBÓ	APROBACIÓN CLIENTE
V01	20/03/2026	EMITIDO PARA CONSTRUCCIÓN	C.M.B.B	D.E.D	
V00	25/11/2024	REVISIÓN NO OBJETADA - EMITIDO PARA CONSTRUCCIÓN	F.B.R	E.O.M	
VGG	15/05/2024	EMITIDO PARA REVISIÓN Y COMENTARIOS DEL CLIENTE E INTERVENTORÍA - INCLUYE COMENTARIOS /(AJUSTES V4)	F.B.R	E.O.M	
VFF	22/12/2023	EMITIDO PARA REVISIÓN Y COMENTARIOS DEL CLIENTE E INTERVENTORÍA - INCLUYE COMENTARIOS /(AJUSTES V3)	F.B.R	M.B.M	
VEE	30/06/2023	EMITIDO PARA REVISIÓN Y COMENTARIOS DEL CLIENTE E INTERVENTORÍA - INCLUYE COMENTARIOS /(AJUSTES V2)	J.E.M	M.B.M	
VDD	18/12/2022	EMITIDO PARA REVISIÓN Y COMENTARIOS DEL CLIENTE E INTERVENTORÍA - INCLUYE COMENTARIOS /(AJUSTES)	J.E.M	M.B.M	
VCC	20/06/2022	EMITIDO PARA REVISIÓN Y COMENTARIOS DEL CLIENTE E INTERVENTORÍA - INCLUYE COMENTARIOS /(ENTREGA 90%)	J.E.M	M.B.M	
VBB	06/12/2021	EMITIDO PARA REVISIÓN Y COMENTARIOS DEL CLIENTE E INTERVENTORÍA	J.E.M	M.B.M	
VA0	30/06/2021	EMITIDO PARA COMENTARIOS INTERNOS - EMISIÓN PRELIMINAR PARA COMENTARIOS	J.E.M	M.B.M	

METRO LÍNEA 1

METRO LÍNEA 1
CONTRATO DE CONCESIÓN No. 163 DE 2019

PROYECTO PRIMERA LÍNEA DEL METRO DE BOGOTÁ - TRAMO 1

DIRECTOR DE INTERVENTORÍA:
JAVIER DESCARGA N.
Mat.:25202-68697 CND

ESPECIALISTA INTERVENTORÍA:
CARLOS ALBERTO HOYOS SOTO
Mat.:A25072000-14251682

FECHA:
MARZO 2026

INFRAESTRUCTURA VIAL
ARQUITECTURA

ESTACIÓN METRO 6 (AVENIDA BOYACÁ)
NAVE CENTRAL
VISTA EN PLANTA Y 3D - NIVEL INTERMEDIO

PLANCHA No: L1T1-0000-306-CON-ED-ARQ-PL-0001_06_V01
ARCHIVO: L1T1-0000-306-CON-ED-ARQ-MO-0001_V00.rvt
ESCALA: INDICADA
FECHA: JUNIO 2021
REVISIÓN No. V01
PLANO No. 06 DE 47