L1T1-CON-CAL-FR-0120 - B1 : 1000x707mm

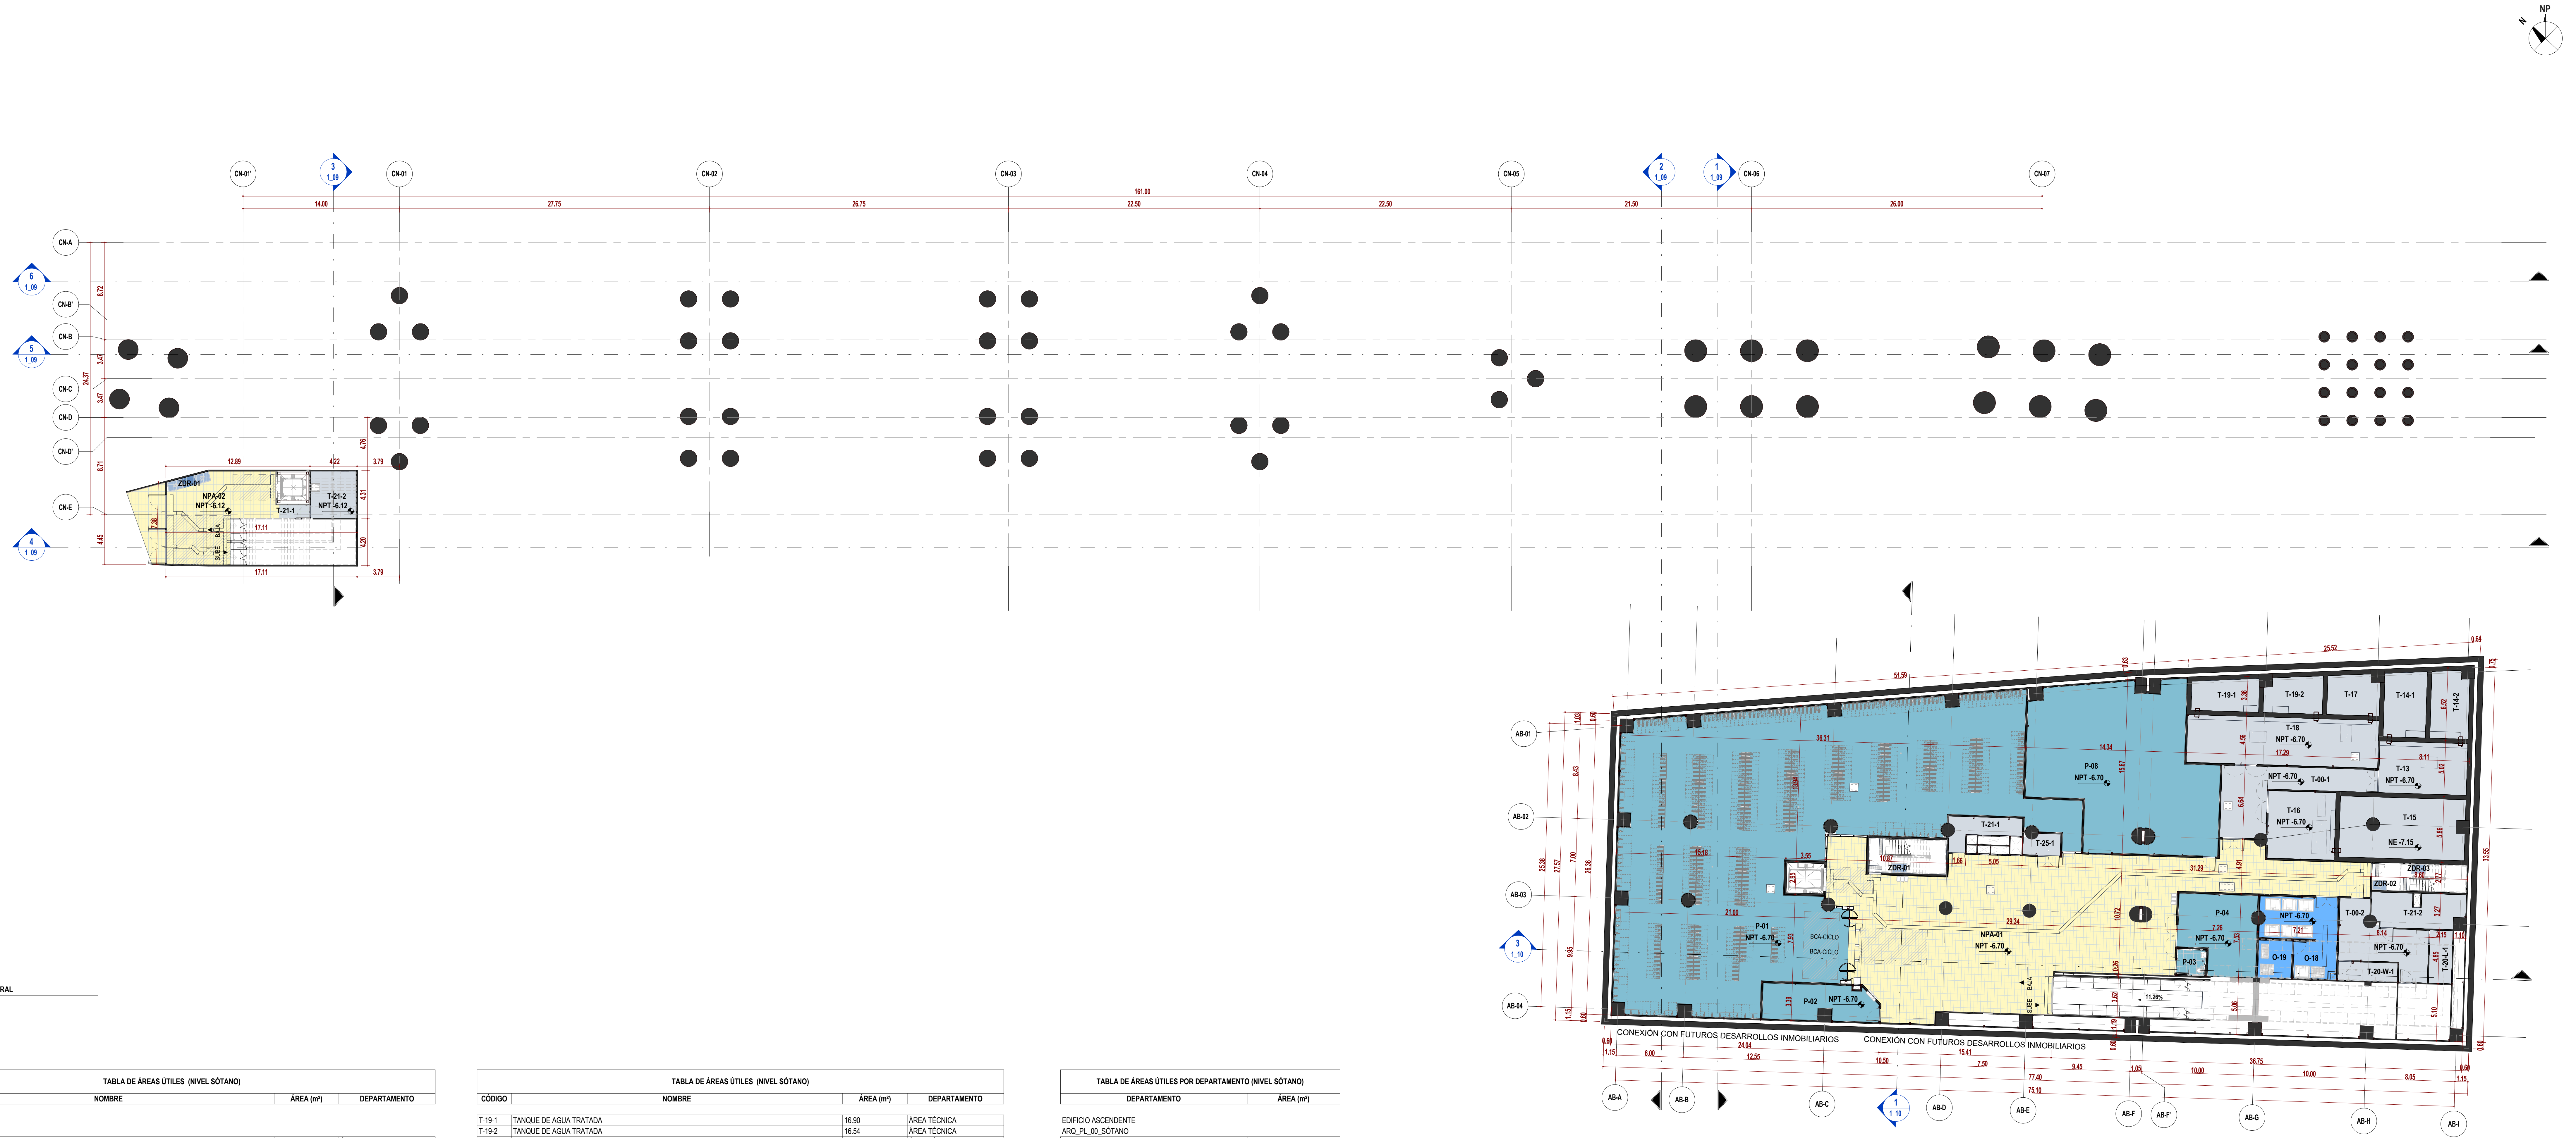
NP
CN-01
CN-02
CN-03
CN-04
CN-05
CN-06
CN-07
CONEXIÓN CON FUTUROS DESARROLLOS INMOBILIARIOS
CONEXIÓN CON FUTUROS DESARROLLOS INMOBILIARIOS

2 NIVEL SÓTANO_GENERAL
ESC: 1 : 200

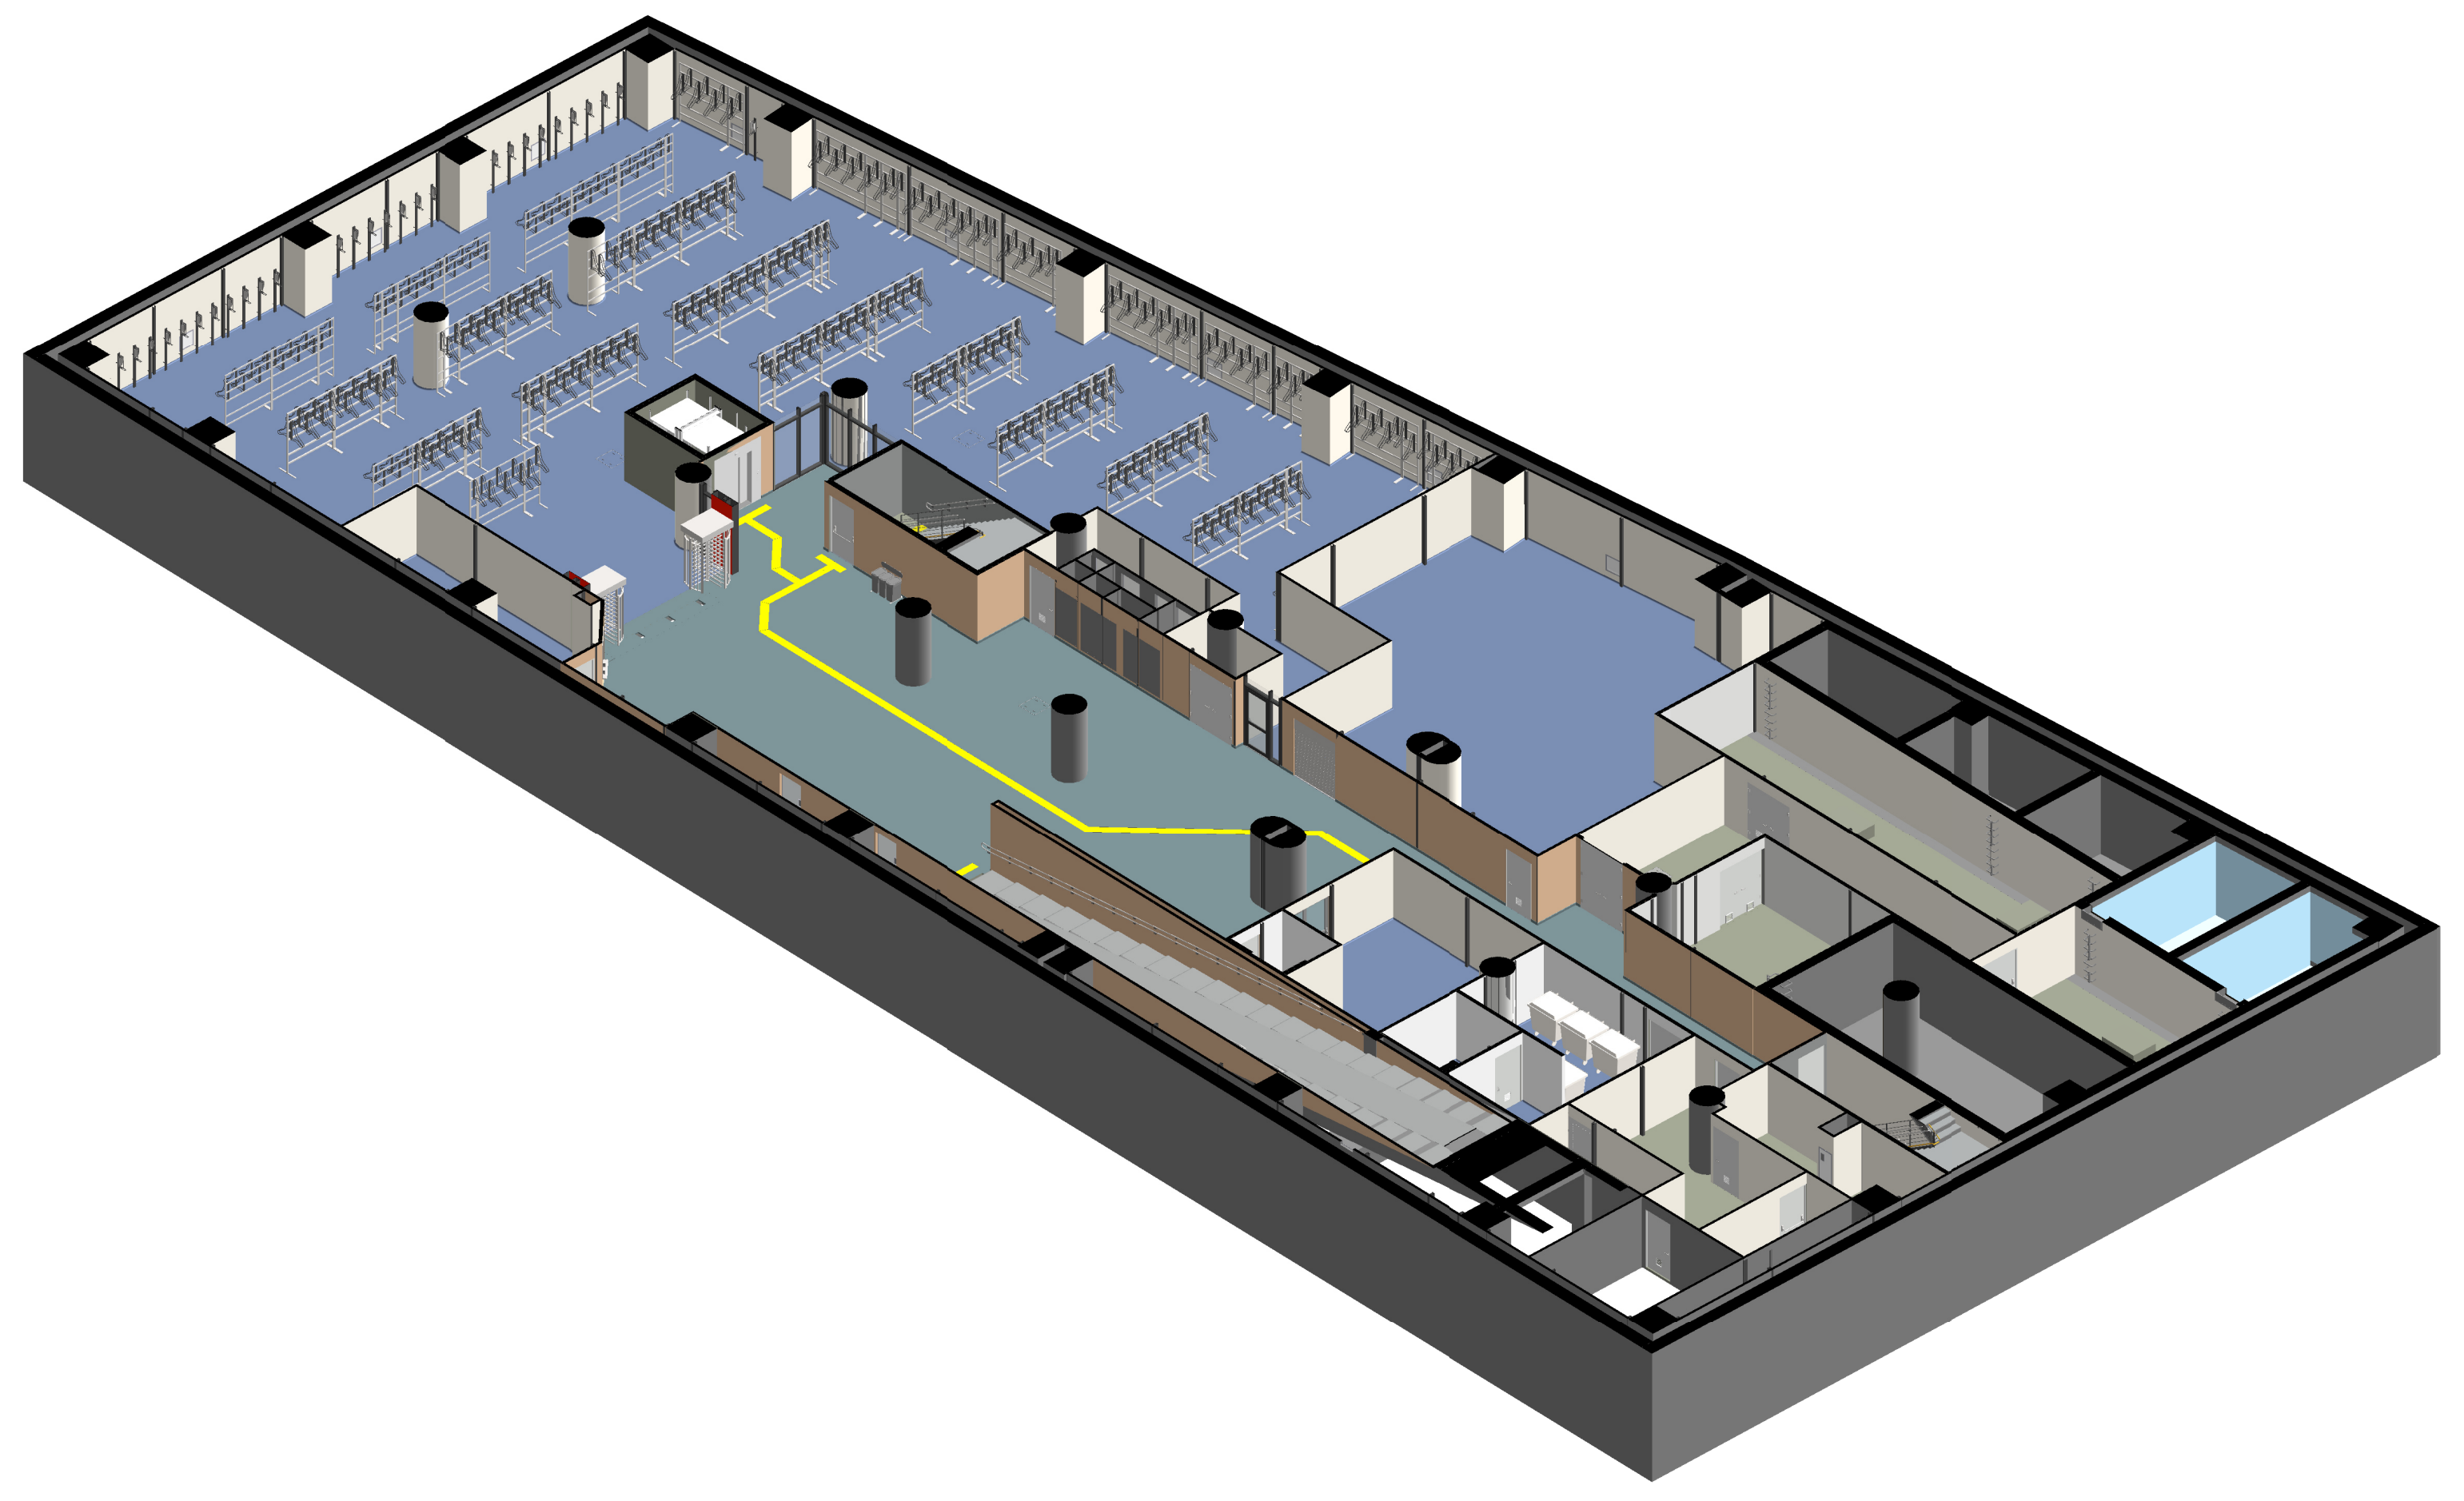

1 3D_NIVEL SÓTANO_GENERAL
ESC: N/A

TABLA DE ÁREAS ÚTILES (NIVEL SÓTANO)

CÓDIGO	NOMBRE	ÁREA (m²)	DEPARTAMENTO
EDIFICIO ASCENDENTE			
ARQ_PL_00_SÓTANO			
NPA-01	ÁREA NO PAGA	431.77	ÁREA NO PAGA
O-18	CUARTO DE ALMACENAMIENTO DE RESIDUOS SÓLIDOS	39.59	ÁREA OPERATIVA
O-19	CUARTO DE ALMACENAMIENTO DE RESIDUOS PELIGROSOS	10.23	ÁREA OPERATIVA
P-01	ÁREA CICLO-PARQUEADEROS	707.02	ÁREA PÚBLICA
P-02	ÁREA OPERATIVA CICLO-PARQUEADEROS	31.31	ÁREA PÚBLICA
P-03	BAÑO OPERADOR CICLO-PARQUEADEROS	6.02	ÁREA PÚBLICA
P-04	TALLER DE BICICLETAS	45.19	ÁREA PÚBLICA
P-08	ESPACIO CARGA DE VEHÍCULOS ELÉCTRICOS	211.47	ÁREA PÚBLICA
T-00-1	CIRCULACIÓN TÉCNICA	46.19	ÁREA TÉCNICA
T-00-2	CIRCULACIÓN TÉCNICA	34.99	ÁREA TÉCNICA
T-13	CUARTO DE BOMBAS DE SUMINISTRO DE AGUA	36.20	ÁREA TÉCNICA
T-14-1	TANQUE DE SUMINISTRO DE AGUA	21.85	ÁREA TÉCNICA
T-14-2	TANQUE DE SUMINISTRO DE AGUA	20.07	ÁREA TÉCNICA
T-15	TANQUE SISTEMA DE EXTINCIÓN DE INCENDIOS (RCI)	59.10	ÁREA TÉCNICA
T-16	CUARTO DE BOMBAS PARA ROCIADORES	36.13	ÁREA TÉCNICA
T-17	TANQUE RECUPERACIÓN AGUAS LLUVIAS	16.36	ÁREA TÉCNICA
T-18	CUARTO DE BOMBAS DE RECUPERACIÓN DE AGUAS LLUVIAS Y EQUIPO DE FILTRACIÓN	72.83	ÁREA TÉCNICA

TABLA DE ÁREAS ÚTILES (NIVEL SÓTANO)

CÓDIGO	NOMBRE	ÁREA (m²)	DEPARTAMENTO
T-19-1	TANQUE DE AGUA TRATADA	16.90	ÁREA TÉCNICA
T-19-2	TANQUE DE AGUA TRATADA	16.54	ÁREA TÉCNICA
T-20-L-1	MEDIDORES (LUZ)	9.68	ÁREA TÉCNICA
T-20-W-1	MEDIDORES (AGUA)	8.99	ÁREA TÉCNICA
T-21-1	ÁREA DE INSPECCIÓN	12.49	ÁREA TÉCNICA
T-21-2	ÁREA DE INSPECCIÓN	23.71	ÁREA TÉCNICA
T-25-1	NODO DE ACCESO DE TELECOMUNICACIONES	5.88	ÁREA TÉCNICA
ZDR-01	ZONA DE REFUGIO (PMR)	1.22	ZONA DE REFUGIO
ZDR-02	ZONA DE REFUGIO (PMR)	1.22	ZONA DE REFUGIO
ZDR-03	ZONA DE REFUGIO (PMR)	1.22	ZONA DE REFUGIO
		1924.16	
NAVE CENTRAL			
ARQ_PL_00_SÓTANO			
NPA-01	ÁREA NO PAGA	16.49	ÁREA NO PAGA
NPA-02	ÁREA NO PAGA	60.45	ÁREA NO PAGA
T-21-1	ÁREA DE INSPECCIÓN	3.60	ÁREA TÉCNICA
T-21-2	ÁREA DE INSPECCIÓN	17.41	ÁREA TÉCNICA
ZDR-01	ZONA DE REFUGIO (PMR)	3.50	ZONA DE REFUGIO
		101.45	
TOTAL NIVEL SÓTANO		2025.60	

TABLA DE ÁREAS ÚTILES POR DEPARTAMENTO (NIVEL SÓTANO)

DEPARTAMENTO	ÁREA (m²)
EDIFICIO ASCENDENTE	
ARQ_PL_00_SÓTANO	
ZONA DE REFUGIO	3.65
ÁREA NO PAGA	431.77
ÁREA OPERATIVA	49.82
ÁREA PÚBLICA	1001.02
ÁREA TÉCNICA	437.89
NAVE CENTRAL	
ARQ_PL_00_SÓTANO	
ZONA DE REFUGIO	3.50
ÁREA NO PAGA	76.94
ÁREA TÉCNICA	21.01
TOTAL NIVEL SÓTANO	2025.60

TABLA DE CICLO-PARQUEADEROS ESPECÍFICA

DESCRIPCIÓN	CANTIDAD (und)	USUARIOS
ARQ_PL_00_SÓTANO		
BICIPARQUEADERO ASISTIDO EN ACERO INOXIDABLE ASTM A240, a=0.70m X l=1.20m, h=1.70m.	1	EMPLEADOS
BICIPARQUEADERO DE COLGAR, 2 PUESTOS, a=1.20m X l=0.70m, h=2.40m. ACABADO EN PINTURA ELECTROSTÁTICA COLOR RAL9005 "NEGRO INTENSO".	4	EMPLEADOS
EMPLEADOS	5	
BICIPARQUEADERO ASISTIDO EN ACERO INOXIDABLE ASTM A240, a=0.70m X l=1.20m, h=1.70m.	54	VISITANTE
BICIPARQUEADERO DE COLGAR DE 6 PUESTOS EN ACERO, a=1.20m X l=2.10m, h=2.40m. ACABADO EN PINTURA ELECTROSTÁTICA COLOR RAL9005 "NEGRO INTENSO".	396	VISITANTE
BICIPARQUEADERO DE COLGAR, 1 PUESTO, a=1.20m X l=0.70m, h=2.40m. ACABADO EN PINTURA ELECTROSTÁTICA COLOR RAL9005 "NEGRO INTENSO".	29	VISITANTE
BICIPARQUEADERO DE COLGAR, 2 PUESTOS, a=1.20m X l=0.70m, h=2.40m. ACABADO EN PINTURA ELECTROSTÁTICA COLOR RAL9005 "NEGRO INTENSO".	56	VISITANTE
VISITANTE	535	
TOTAL CUPOS	540	

LOCALIZACIÓN

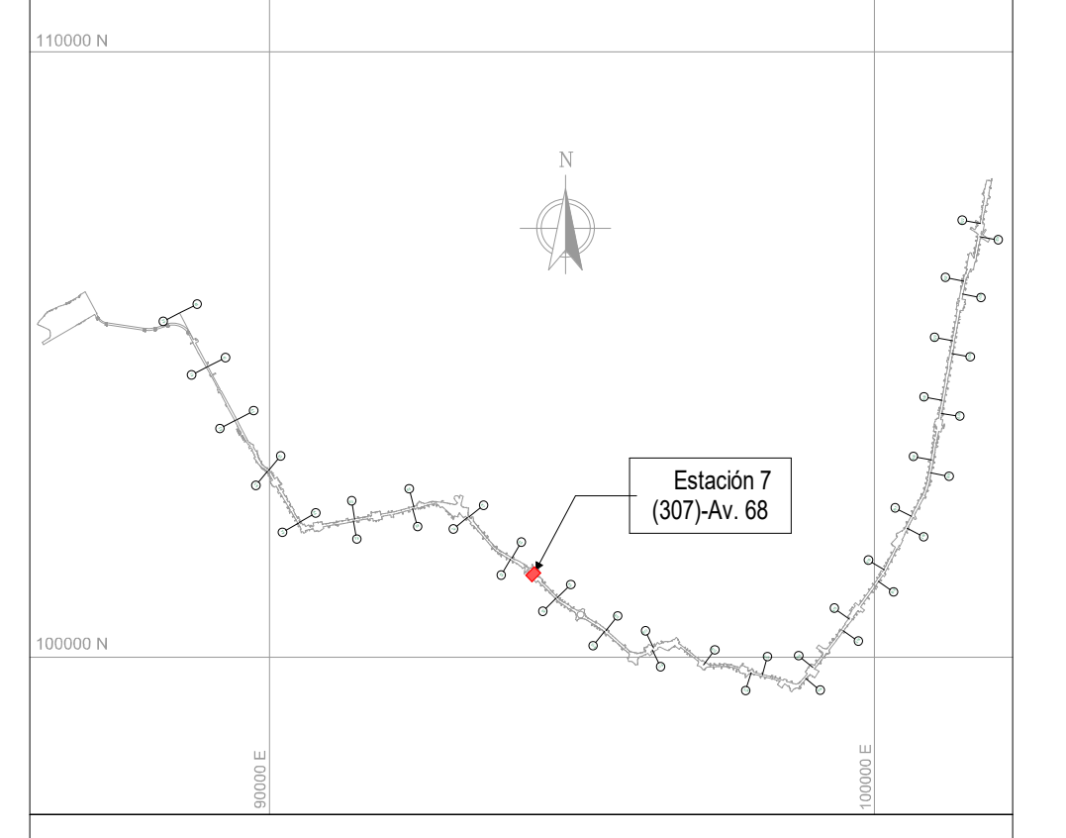

NOTAS

01 TODAS LAS DIMENSIONES ESTÁN CONFIGURADAS EN METROS A MENOS QUE SE INDIQUE UNA UNIDAD DE MEDIDA DIFERENTE.

02 TODAS LAS MEDIDAS, UBICACIÓN Y NIVELES DEBEN VERIFICARSE EN EL LUGAR DE CONSTRUCCIÓN.

03 EL NIVEL DE ACCESO AL EDIFICIO PL 01 CORRESPONDE AL +0,00 DE LA ESTACIÓN Y REFERENCIA AL NIVEL 2557.05 M.S.N.M.

04 LOS NOMBRES ESPECIFICOS DE LAS ÁREAS PUEDEN SER CONSULTADAS EN EL PLANO NO. 3 Ó EN LAS VISTAS EN PLANTA.

05 LOS COLORES QUE SE MUESTRAN EN LOS PLANOS COMO PROYECCIÓN DE ELEMENTOS ARQUITECTÓNICOS COMO CUBIERTAS FACHADAS MUROS ETC. NO REPRESENTAN LA MATERIALIDAD Y REALIDAD DE ACABADOS DEL PROYECTO, SOLO SON INDICATIVOS PARA REALIZAR UNA CORRECTA LECTURA DE LA PLANIMETRÍA.

06 SE DEBEN REVISAR LOS NIVELES ESTRUCTURALES PARA NIVEL DE ACCESO PL_01 Y SUBNIVELES, PL_02 (INTERMEDIO), PL_03 (PLATAFORMA) CON LA PLANIMETRÍA DE PLACAS ESTRUCTURALES EN LOS ENTREGABLES L1T1-1200-307-CON-ED-EST-PL-0018,19 Y L1T1-1300-407-CON-ED-EST-PL-0026, 30, 76, RESPECTIVAMENTE. EL NIVEL ESTRUCTURAL (NE) REFERENCIA LOS ESPACIOS DONDE SE DEBE ACONDICIONAR EL ACABADO DE PISO SEGÚN CORRESPONDA, CON LOS NIVELES DE PISO TERMINADO (NPT). LOS NIVELES PROYECTADOS DE EMPATE (NPE) EN LAS ÁREAS DE SERVICIOS ADICIONALES, REFERENCIAN LA ADECUACIÓN DE LOS DESNIVELES EN ESTAS ÁREAS; QUEDA COMO RESPONSABILIDAD DEL LOCATARIO DEFINIR Y ACONDICIONAR ESTE ACABADO DE PISO (NPE) EN LÍNEA CON EL NIVEL (NPT) DE ESPACIOS COLINDANTES. EL NIVEL ESTRUCTURAL (NE) SE ENCUENTRA A (- 0.10M) POR DEBAJO DE LOS NIVELES DE PISO TERMINADO (NPT) Y LOS NIVELES PROYECTADOS DE EMPATE (NPE) MARCADOS EN LA PLANIMETRÍA.

- ARQ_PL_00 = SÓTANO	/ NPT -6.70m	- ARQ_PL_01 = ACCESO	/ NPT 0.00m
- ARQ_PL_00.1 = SÓTANO BRT	/ NPT -6.12m	- ARQ_PL_02 = INTERMEDIO	/ NPT 7.35m
- ARQ_PL_00.1 = ACCESO	/ NPT -0.70m	- ARQ_PL_02.2 = TOPE DE RIEL (TOR)	/ NPT 15.25m
- ARQ_PL_00.2 = ACCESO	/ NPT -0.55m	- ARQ_PL_03 = PLATAFORMA	/ NPT 16.39m
- ARQ_PL_00.3 = ACCESO	/ NPT -0.45m	- ARQ_PL_04 = CUBIERTA EDIFICACIONES	/ NPT 22.99m
- ARQ_PL_00.4 = ACCESO	/ NPT -0.30m	- ARQ_PL_05 = CUBIERTA NAVE CENTRAL	/ NPT 25.70m

CONVENCIONES

🟩	SERVICIOS ADICIONALES - ÁREA NO PAGA	🟨	ÁREA NO PAGA
🟩	SERVICIOS ADICIONALES - ÁREA PAGA	🟨	ÁREA PAGA
🟩	SERVICIO PÚBLICO	🟦	ÁREA PÚBLICA
🟦	ZONA DE REFUGIO	⬜	ÁREA TÉCNICA
🟥	ÁREA CULTURAL	🟦	ÁREA OPERATIVA

No.	PLANOS DE REFERENCIA	REV.

No.	MODELO BIM DE REFERENCIA	REV.
1	L1T1-1100-207-CON-ED-EST-MO-0001.rvt	V00
2	L1T1-1100-307-CON-ED-EST-MO-0001.rvt	V00
3	L1T1-1150-207-CON-ED-EST-MO-0001.rvt	V00
4	L1T1-1150-307-CON-ED-EST-MO-0001.rvt	V00
5	L1T1-1200-307-CON-ED-EST-MO-0001.rvt	V00
6	L1T1-1300-407-CON-ED-EST-MO-0001.rvt	V00
7	L1T1-1300-407-CON-ED-EST-MO-0002.rvt	V00
8	L1T1-1310-407-CON-ED-EST-MO-0001.rvt	V00
9	L1T1-1410-307-CON-ED-MEC-MO-0001.rvt	V00
10	L1T1-1420-307-CON-ED-MEC-MO-0001.rvt	V00
11	L1T1-2410-501-CON-ED-EST-MO-0001.rvt	V00
12	L1T1-2410-502-CON-ED-EST-MO-0001.rvt	V00
13	L1T1-2430-407-CON-ED-EST-MO-0001.rvt	V00
14	L1T1-5160-307-CON-ED-EST-MO-0001.rvt	V00
15	L1T1-5160-307-CON-ED-ARQ-MO-0001.rvt	V00
16	L1T1-5300-307-CON-ED-MEC-MO-0001.rvt	V00
17	L1T1-5600-307-CON-ED-INS-MO-0001.rvt	V00
18	L1T1-1270-307-CON-ED-ARQ-MO-0011.rvt	V00
19	L1T1-1330-407-CON-ED-ARQ-MO-0011.rvt	V00
20	L1T1-1330-407-CON-ED-ARQ-MO-0012.rvt	V00

No.	PAQUETE DE TRABAJO DE REFERENCIA	REV.
1	XREF-URBANISM_CONTEXT_ST07.rvt	
2	XREF-SECONDARY-STRUCTURE-ST07.rvt	

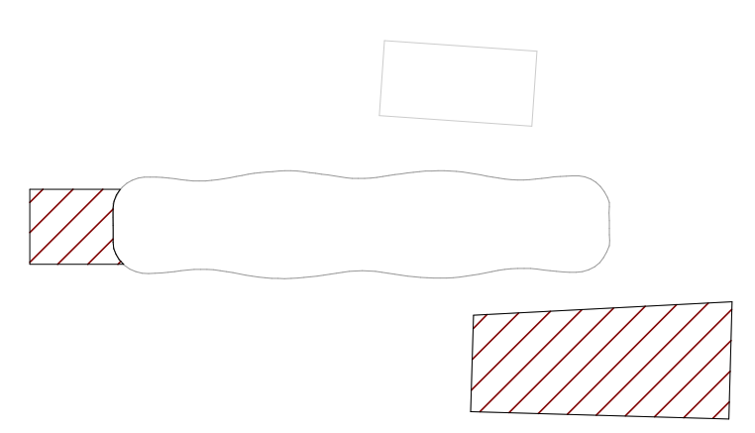

VÁLIDO PARA CONSTRUCCIÓN
20-03-26

PLANO CLAVE ESTACIÓN 7

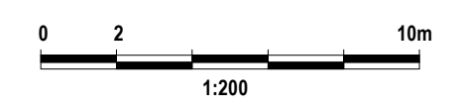

METRO BOGOTÁ
Consorcio Consultores PMO Bogotá
CONSORCIO SUPERVISOR PLMB

DISEÑÓ:
REN ZHENHUA
Licencia de Arq.nivel I (China): 1101735-614

APROBÓ:
DIEGO ERNESTO DUEÑAS
Mat.: 25202-53876 CND

REVISÓ:
CARLOS MAURICIO BARRETO BARBOSA
Mat.: A4012012-14139353

DIBUJÓ:
EQUIPO CHEC

REVISIÓN No.	FECHA	DESCRIPCIÓN	REVISÓ	APROBÓ	APROBACIÓN CLIENTE
V01	20/03/2026	EMITIDO PARA CONSTRUCCIÓN	C.M.B.B	D.E.D	
V00	27/01/2025	REVISIÓN NO OBJETADA - EMITIDO PARA CONSTRUCCIÓN	F.B.R	E.O.M	
VFF	04/10/2024	EMITIDO PARA REVISIÓN Y COMENTARIOS DEL CLIENTE E INTERVENTORÍA - INCLUYE COMENTARIOS /(AJUSTES V3)	F.B.R	E.O.M	
VEE	11/06/2024	EMITIDO PARA REVISIÓN Y COMENTARIOS DEL CLIENTE E INTERVENTORÍA - INCLUYE COMENTARIOS /(AJUSTES V2)	F.B.R	E.O.M	
VDD	18/12/2022	EMITIDO PARA REVISIÓN Y COMENTARIOS DEL CLIENTE E INTERVENTORÍA - INCLUYE COMENTARIOS /(AJUSTES)	J.E.M	M.B.M	
VCC	02/06/2022	EMITIDO PARA REVISIÓN Y COMENTARIOS DEL CLIENTE E INTERVENTORÍA - INCLUYE COMENTARIOS /(ENTREGA 90%)	J.E.M	M.B.M	
VBB	06/12/2021	EMITIDO PARA REVISIÓN Y COMENTARIOS DEL CLIENTE E INTERVENTORÍA	J.E.M	M.B.M	
VA0	30/06/2021	EMITIDO PARA COMENTARIOS INTERNOS - EMISIÓN PRELIMINAR PARA COMENTARIOS	J.E.M	M.B.M	

METRO LÍNEA 1

METRO LÍNEA 1
CONTRATO DE CONCESIÓN No. 163 DE 2019

PROYECTO PRIMERA LÍNEA DEL METRO DE BOGOTÁ - TRAMO 1

INFRAESTRUCTURA VIAL

ARQUITECTURA

ESTACIÓN METRO 7 (AV 68)
GENERAL
VISTA EN PLANTA Y 3D - NIVEL SÓTANO

DIRECTOR DE INTERVENTORÍA:
JAVIER DESCARGA N.
Mat.:25202-68697 CND

ESPECIALISTA INTERVENTORÍA:
CARLOS ALBERTO HOYOS SOTO
Mat.:A25072000-14251682

FECHA:
MARZO 2026

PLANCHA No: L1T1-0000-307-CON-ED-ARQ-PL-0001_04_V01
ARCHIVO: L1T1-0000-307-CON-ED-ARQ-MO-0001_V00.rvt
ESCALA: INDICADA
FECHA: JUNIO 2021
REVISIÓN No. V01
PLANO No. 04 DE 107