L1T1-CON-CAL-FR-0120 - B1 : 1000x707mm

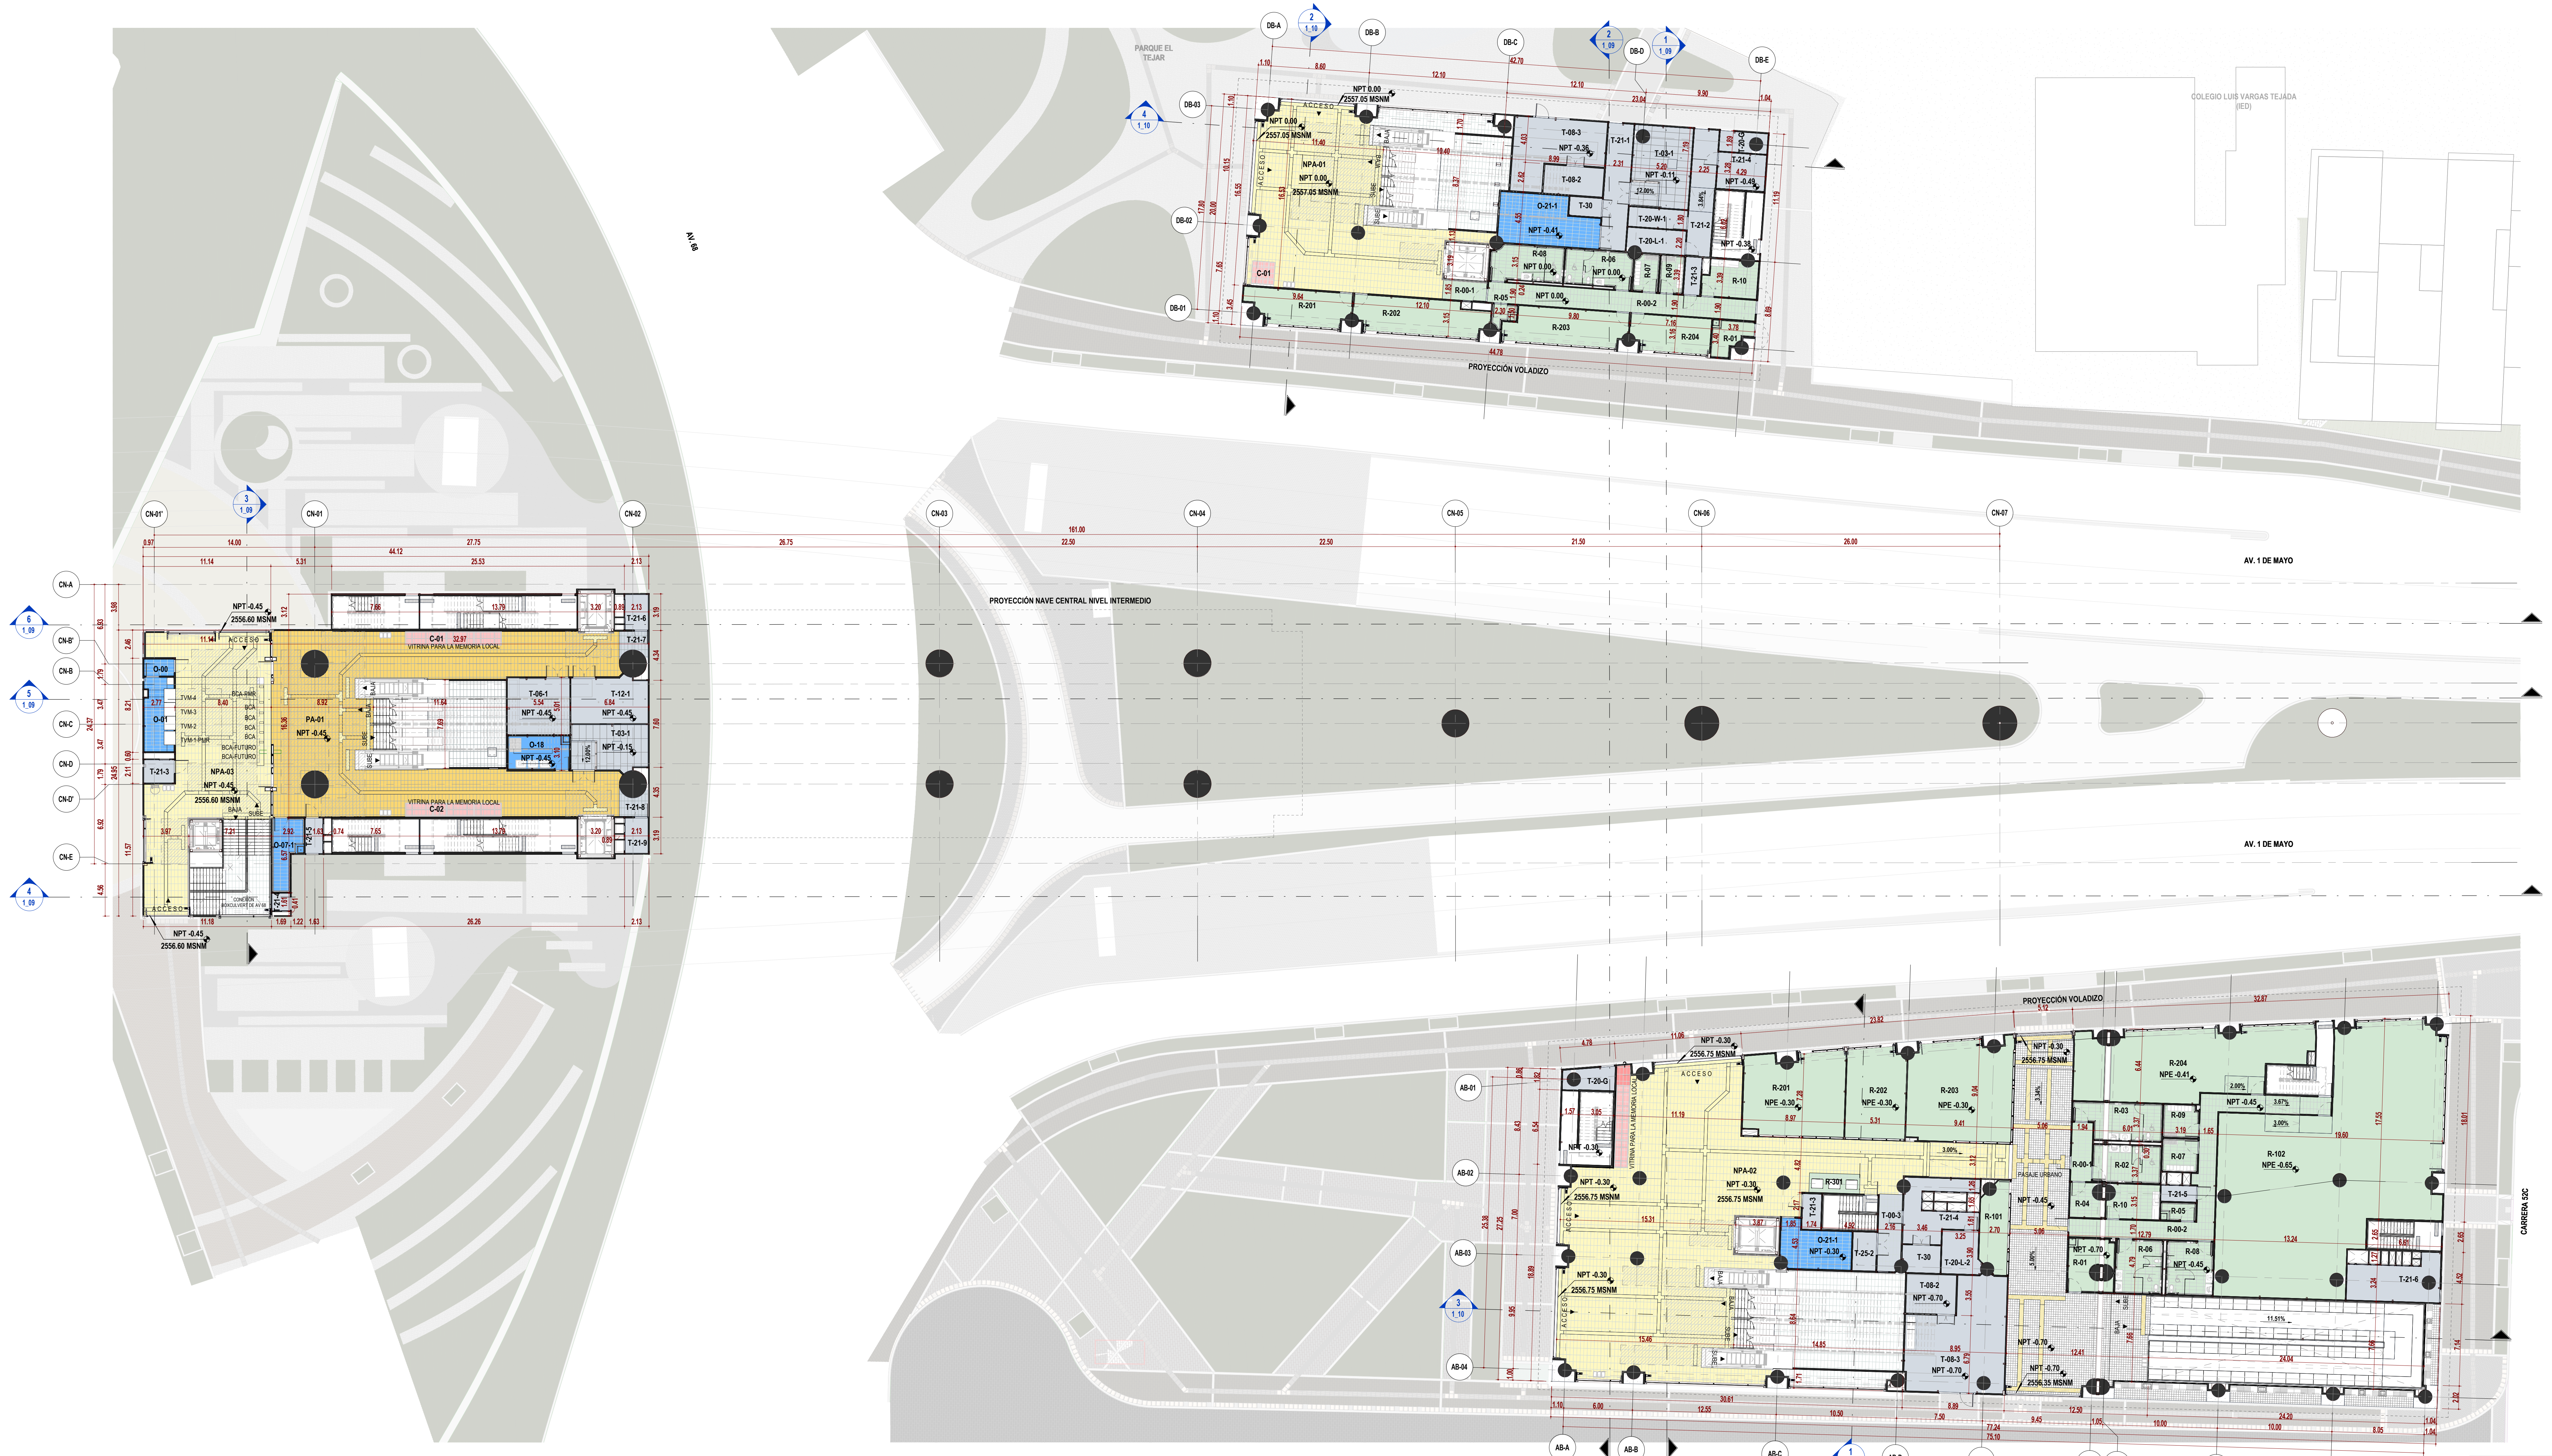

2 NIVEL ACCESO_GENERAL
ESC: 1 : 200

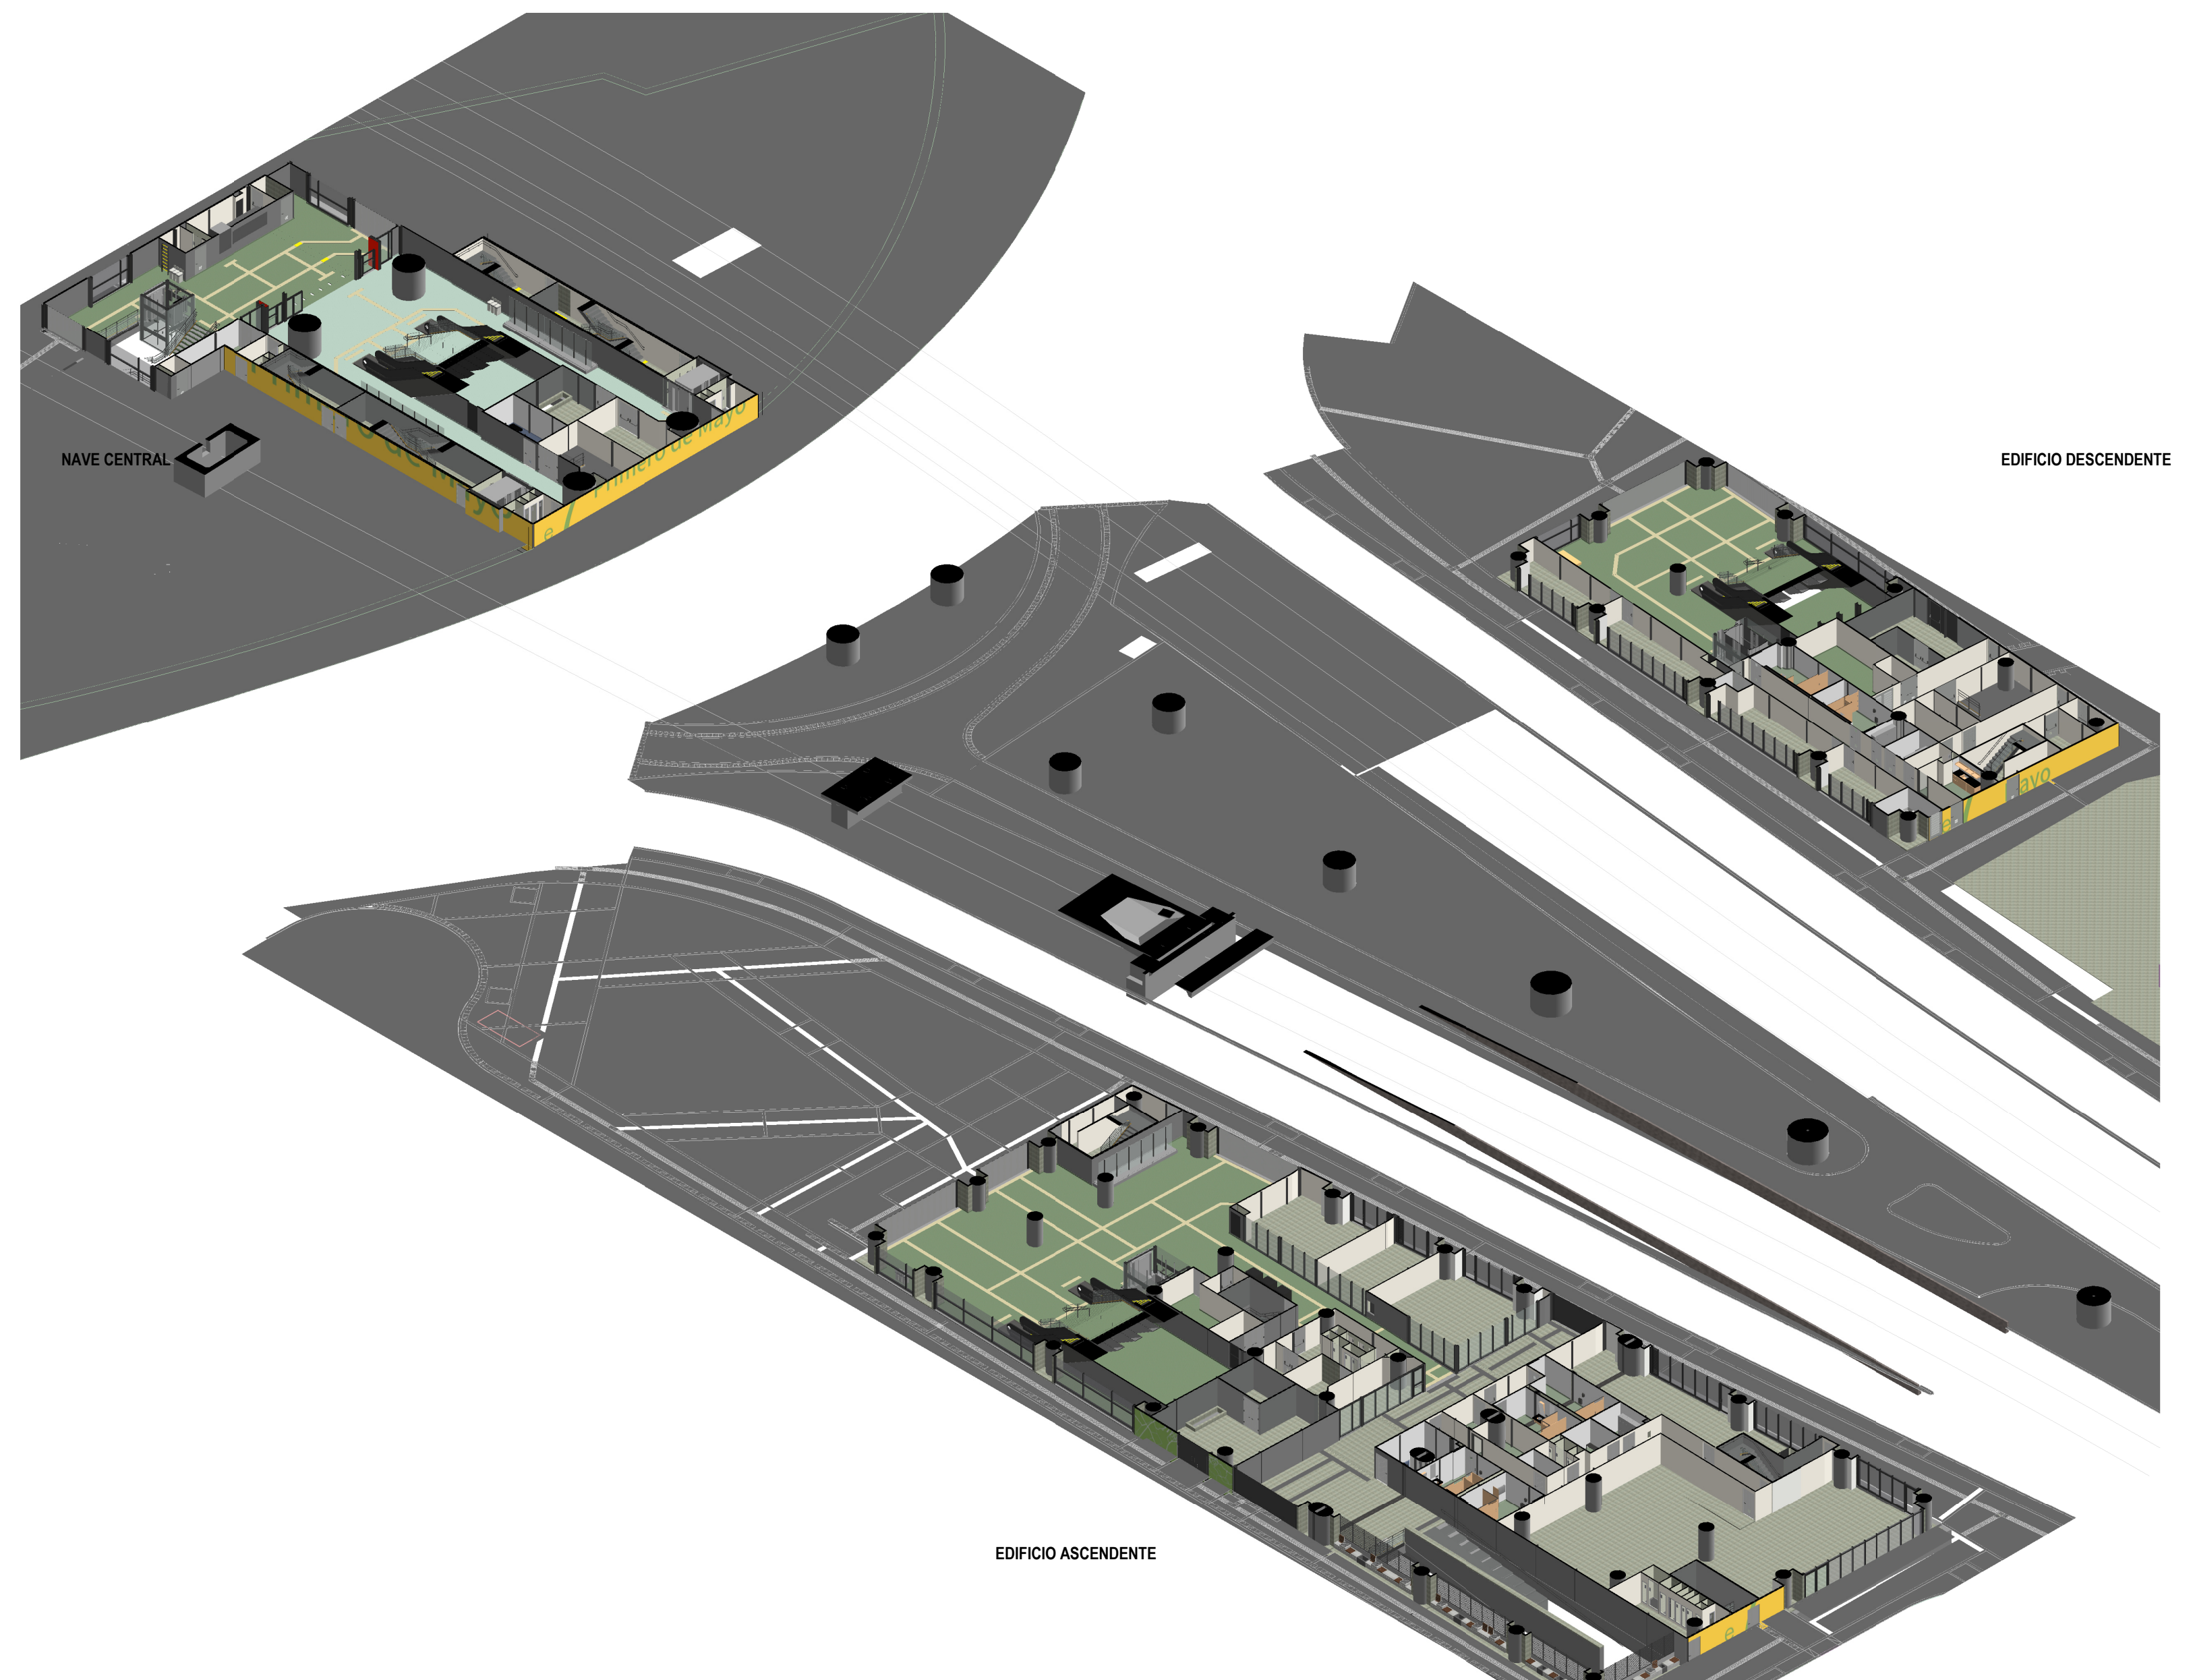

1 3D_NIVEL ACCESO_GENERAL
ESC: N/A

## TABLA DE ÁREAS ÚTILES (NIVEL ACCESO)

| CÓDIGO | NOMBRE | ÁREA (m²) | DEPARTAMENTO |
|---|---|---|---|
| EDIFICIO ASCENDENTE | | | |
| ARQ_PL_00.1_ACCESO | | | |
| R-00-2 | SERVICIOS ADICIONALES - CORREDOR OPERATIVO | 53.58 | SERVICIOS ADICIONALES - ÁREA NO PAGA |
| R-01 | SERVICIOS ADICIONALES - CUARTO DE BASURAS PARA METRO | 15.77 | SERVICIOS ADICIONALES - ÁREA NO PAGA |
| R-102 | SERVICIOS ADICIONALES - ÁREA DE SERVICIO | 330.58 | SERVICIOS ADICIONALES - ÁREA NO PAGA |
| T-08-2 | CENTRO DE TRANSFORMACIÓN ENEL-CODENSA (CT)_CUARTO BAJA TENSIÓN | 14.67 | ÁREA TÉCNICA |
| T-08-3 | CENTRO DE TRANSFORMACIÓN ENEL-CODENSA (CT)_CUARTO MEDIA TENSIÓN | 71.88 | ÁREA TÉCNICA |
| T-21-6 | ÁREA DE INSPECCIÓN | 26.47 | ÁREA TÉCNICA |
| | | 512.93 | |
| ARQ_PL_00.3_ACCESO | | | |
| R-00-1 | SERVICIOS ADICIONALES - CORREDOR OPERATIVO | 9.27 | SERVICIOS ADICIONALES - ÁREA NO PAGA |
| R-02 | SERVICIOS ADICIONALES - BAÑO PÚBLICO DE MUJERES | 18.76 | SERVICIOS ADICIONALES - ÁREA NO PAGA |
| R-03 | SERVICIOS ADICIONALES - BAÑO PÚBLICO DE HOMBRES | 21.95 | SERVICIOS ADICIONALES - ÁREA NO PAGA |
| R-04 | SERVICIOS ADICIONALES - CONTROL DE ACCESO BAÑOS PÚBLICOS | 7.78 | SERVICIOS ADICIONALES - ÁREA NO PAGA |
| R-05 | SERVICIOS ADICIONALES - CUARTO DE LIMPIEZA | 4.56 | SERVICIOS ADICIONALES - ÁREA NO PAGA |
| R-06 | SERVICIOS ADICIONALES - BAÑOS EMPLEADOS MUJERES | 18.28 | SERVICIOS ADICIONALES - ÁREA NO PAGA |
| R-07 | SERVICIOS ADICIONALES - VESTIDORES EMPLEADOS MUJERES | 8.55 | SERVICIOS ADICIONALES - ÁREA NO PAGA |
| R-08 | SERVICIOS ADICIONALES - BAÑOS EMPLEADOS HOMBRES | 18.28 | SERVICIOS ADICIONALES - ÁREA NO PAGA |
| R-09 | SERVICIOS ADICIONALES - VESTIDORES EMPLEADOS HOMBRES | 8.42 | SERVICIOS ADICIONALES - ÁREA NO PAGA |
| R-10 | SERVICIOS ADICIONALES - SALA DE EMPLEADOS | 13.09 | SERVICIOS ADICIONALES - ÁREA NO PAGA |
| R-101 | SERVICIOS ADICIONALES - ÁREA DE SERVICIO | 17.06 | SERVICIOS ADICIONALES - ÁREA NO PAGA |
| R-204 | SERVICIOS ADICIONALES - ÁREA DE COMIDAS | 110.80 | SERVICIOS ADICIONALES - ÁREA NO PAGA |
| T-21-5 | ÁREA DE INSPECCIÓN | 4.27 | ÁREA TÉCNICA |
| | | 261.06 | |
| ARQ_PL_00.4_ACCESO | | | |
| C | ÁREAS DE USO CULTURAL | 10.96 | ÁREA CULTURAL |
| NPA-02 | ÁREA NO PAGA | 461.17 | ÁREA NO PAGA |
| O-21-1 | ALMACENAMIENTO DE LA ESTACIÓN | 22.05 | ÁREA OPERATIVA |
| R-201 | SERVICIOS ADICIONALES - ÁREA DE COMIDAS | 60.66 | SERVICIOS ADICIONALES - ÁREA NO PAGA |
| R-202 | SERVICIOS ADICIONALES - ÁREA DE COMIDAS | 40.21 | SERVICIOS ADICIONALES - ÁREA NO PAGA |
| R-203 | SERVICIOS ADICIONALES - ÁREA DE COMIDAS | 76.88 | SERVICIOS ADICIONALES - ÁREA NO PAGA |
| R-301 | SERVICIOS ADICIONALES - MÁQUINAS EXPENDEDORAS/CAJEROS AUTOMÁTICOS | 7.53 | SERVICIOS ADICIONALES - ÁREA NO PAGA |
| T-00-3 | CIRCULACIÓN TÉCNICA | 13.32 | ÁREA TÉCNICA |
| T-20-G | MEDIDORES (GAS) | 7.33 | ÁREA TÉCNICA |
| T-20-L-2 | MEDIDORES (LUZ) | 12.23 | ÁREA TÉCNICA |
| T-21-3 | ÁREA DE INSPECCIÓN | 4.99 | ÁREA TÉCNICA |
| T-21-4 | ÁREA DE INSPECCIÓN | 24.09 | ÁREA TÉCNICA |
| T-25-2 | NODO DE ACCESO DE TELECOMUNICACIONES | 6.84 | ÁREA TÉCNICA |
| T-30 | SISTEMA PROTECCIÓN CONTRA INCENDIO ENEL | 7.49 | ÁREA TÉCNICA |
| | | 755.73 | |
| EDIFICIO DESCENDENTE | | | |
| ARQ_PL_00.2_ACCESO | | | |
| T-20-G | MEDIDORES (GAS) | 6.09 | ÁREA TÉCNICA |
| T-21-2 | ÁREA DE INSPECCIÓN | 23.47 | ÁREA TÉCNICA |
| T-21-4 | ÁREA DE INSPECCIÓN | 13.16 | ÁREA TÉCNICA |
| | | 42.72 | |
| ARQ_PL_00.3_ACCESO | | | |
| O-21-1 | ALMACENAMIENTO DE LA ESTACIÓN | 34.08 | ÁREA OPERATIVA |
| T-03-1 | LOCAL SECUNDARIO DE TELECOMUNICACIONES | 34.77 | ÁREA TÉCNICA |
| T-08-2 | CENTRO DE TRANSFORMACIÓN ENEL-CODENSA (CT)_CUARTO BAJA TENSIÓN | 12.85 | ÁREA TÉCNICA |
| T-08-3 | CENTRO DE TRANSFORMACIÓN ENEL-CODENSA (CT)_CUARTO MEDIA TENSIÓN | 38.62 | ÁREA TÉCNICA |
| T-20-L-1 | MEDIDORES (LUZ) | 10.09 | ÁREA TÉCNICA |
| T-20-W-1 | MEDIDORES (AGUA) | 8.67 | ÁREA TÉCNICA |
| T-21-1 | ÁREA DE INSPECCIÓN | 24.28 | ÁREA TÉCNICA |
| T-30 | SISTEMA PROTECCIÓN CONTRA INCENDIO ENEL | 4.62 | ÁREA TÉCNICA |
| | | 167.99 | |
| ARQ_PL_01_ACCESO | | | |
| C-01 | ÁREAS DE USO CULTURAL | 4.00 | ÁREA CULTURAL |
| NPA-01 | ÁREA NO PAGA | 201.01 | ÁREA NO PAGA |
| R-00-1 | SERVICIOS ADICIONALES - CORREDOR OPERATIVO | 6.25 | SERVICIOS ADICIONALES - ÁREA NO PAGA |
| R-00-2 | SERVICIOS ADICIONALES - CORREDOR OPERATIVO | 41.87 | SERVICIOS ADICIONALES - ÁREA NO PAGA |
| R-01 | SERVICIOS ADICIONALES - CUARTO DE BASURAS PARA METRO | 8.40 | SERVICIOS ADICIONALES - ÁREA NO PAGA |
| R-05 | SERVICIOS ADICIONALES - CUARTO DE LIMPIEZA | 3.38 | SERVICIOS ADICIONALES - ÁREA NO PAGA |
| R-06 | SERVICIOS ADICIONALES - BAÑOS EMPLEADOS MUJERES | 17.74 | SERVICIOS ADICIONALES - ÁREA NO PAGA |
| R-07 | SERVICIOS ADICIONALES - VESTIDORES EMPLEADOS MUJERES | 6.65 | SERVICIOS ADICIONALES - ÁREA NO PAGA |
| R-08 | SERVICIOS ADICIONALES - BAÑOS EMPLEADOS HOMBRES | 18.88 | SERVICIOS ADICIONALES - ÁREA NO PAGA |
| R-09 | SERVICIOS ADICIONALES - VESTIDORES EMPLEADOS HOMBRES | 6.54 | SERVICIOS ADICIONALES - ÁREA NO PAGA |
| R-10 | SERVICIOS ADICIONALES - SALA DE EMPLEADOS | 14.27 | SERVICIOS ADICIONALES - ÁREA NO PAGA |
| R-201 | SERVICIOS ADICIONALES - ÁREA DE COMIDAS | 25.35 | SERVICIOS ADICIONALES - ÁREA NO PAGA |
| R-202 | SERVICIOS ADICIONALES - ÁREA DE COMIDAS | 33.03 | SERVICIOS ADICIONALES - ÁREA NO PAGA |
| R-203 | SERVICIOS ADICIONALES - ÁREA DE COMIDAS | 31.23 | SERVICIOS ADICIONALES - ÁREA NO PAGA |
| R-204 | SERVICIOS ADICIONALES - ÁREA DE COMIDAS | 20.84 | SERVICIOS ADICIONALES - ÁREA NO PAGA |
| T-21-3 | ÁREA DE INSPECCIÓN | 4.58 | ÁREA TÉCNICA |
| | | 444.03 | |
| NAVE CENTRAL | | | |
| ARQ_PL_00.3_ACCESO | | | |
| C-01 | ÁREAS DE USO CULTURAL | 10.23 | ÁREA CULTURAL |
| C-02 | ÁREAS DE USO CULTURAL | 10.22 | ÁREA CULTURAL |
| NPA-03 | ÁREA NO PAGA | 183.88 | ÁREA NO PAGA |
| O-00 | CIRCULACIÓN ÁREAS OPERATIVAS | 3.88 | ÁREA OPERATIVA |
| O-01 | VENTA AUTOMÁTICA DE BOLETOS | 16.71 | ÁREA OPERATIVA |
| O-07-1 | CUARTO DE LIMPIEZA COMPLEMENTARIO | 13.33 | ÁREA OPERATIVA |
| O-18 | CUARTO DE ALMACENAMIENTO DE RESIDUOS SÓLIDOS | 15.74 | ÁREA OPERATIVA |
| PA-01 | ÁREA PAGA | 281.84 | ÁREA PAGA |
| T-03-1 | LOCAL SECUNDARIO DE TELECOMUNICACIONES | 26.21 | ÁREA TÉCNICA |
| T-06-1 | LOCAL SECUNDARIO DE TABLEROS | 26.36 | ÁREA TÉCNICA |
| T-12-1 | PLANTA DE REFRIGERACIÓN PARA LA CLIMATIZACIÓN SECUNDARIO | 26.39 | ÁREA TÉCNICA |
| T-21-3 | ÁREA DE INSPECCIÓN | 5.19 | ÁREA TÉCNICA |
| T-21-4 | ÁREA DE INSPECCIÓN | 2.32 | ÁREA TÉCNICA |
| T-21-5 | ÁREA DE INSPECCIÓN | 4.61 | ÁREA TÉCNICA |
| T-21-6 | ÁREA DE INSPECCIÓN | 6.11 | ÁREA TÉCNICA |
| T-21-7 | ÁREA DE INSPECCIÓN | 4.83 | ÁREA TÉCNICA |
| T-21-8 | ÁREA DE INSPECCIÓN | 4.83 | ÁREA TÉCNICA |
| T-21-9 | ÁREA DE INSPECCIÓN | 6.11 | ÁREA TÉCNICA |
| | | 648.78 | |
| TOTAL NIVEL ACCESO | | 2833.26 | |

## TABLA DE ÁREAS ÚTILES POR DEPARTAMENTO (NIVEL ACCESO)

| DEPARTAMENTO | ÁREA (m²) |
|---|---|
| EDIFICIO ASCENDENTE | |
| ARQ_PL_00.1_ACCESO | |
| SERVICIOS ADICIONALES - ÁREA NO PAGA | 399.92 |
| ÁREA TÉCNICA | 113.01 |
| ARQ_PL_00.3_ACCESO | |
| SERVICIOS ADICIONALES - ÁREA NO PAGA | 256.79 |
| ÁREA TÉCNICA | 4.27 |
| ARQ_PL_00.4_ACCESO | |
| SERVICIOS ADICIONALES - ÁREA NO PAGA | 185.27 |
| ÁREA CULTURAL | 10.96 |
| ÁREA NO PAGA | 461.17 |
| ÁREA OPERATIVA | 22.05 |
| ÁREA TÉCNICA | 76.29 |
| EDIFICIO DESCENDENTE | |
| ARQ_PL_00.2_ACCESO | |
| ÁREA TÉCNICA | 42.72 |
| ARQ_PL_00.3_ACCESO | |
| ÁREA OPERATIVA | 34.08 |
| ÁREA TÉCNICA | 133.91 |
| ARQ_PL_01_ACCESO | |
| SERVICIOS ADICIONALES - ÁREA NO PAGA | 234.44 |
| ÁREA CULTURAL | 4.00 |
| ÁREA NO PAGA | 201.01 |
| ÁREA TÉCNICA | 4.58 |
| NAVE CENTRAL | |
| ARQ_PL_00.3_ACCESO | |
| ÁREA CULTURAL | 20.45 |
| ÁREA NO PAGA | 183.88 |
| ÁREA OPERATIVA | 49.66 |
| ÁREA PAGA | 281.84 |
| ÁREA TÉCNICA | 112.96 |
| TOTAL NIVEL ACCESO | 2833.26 |

## LOCALIZACIÓN

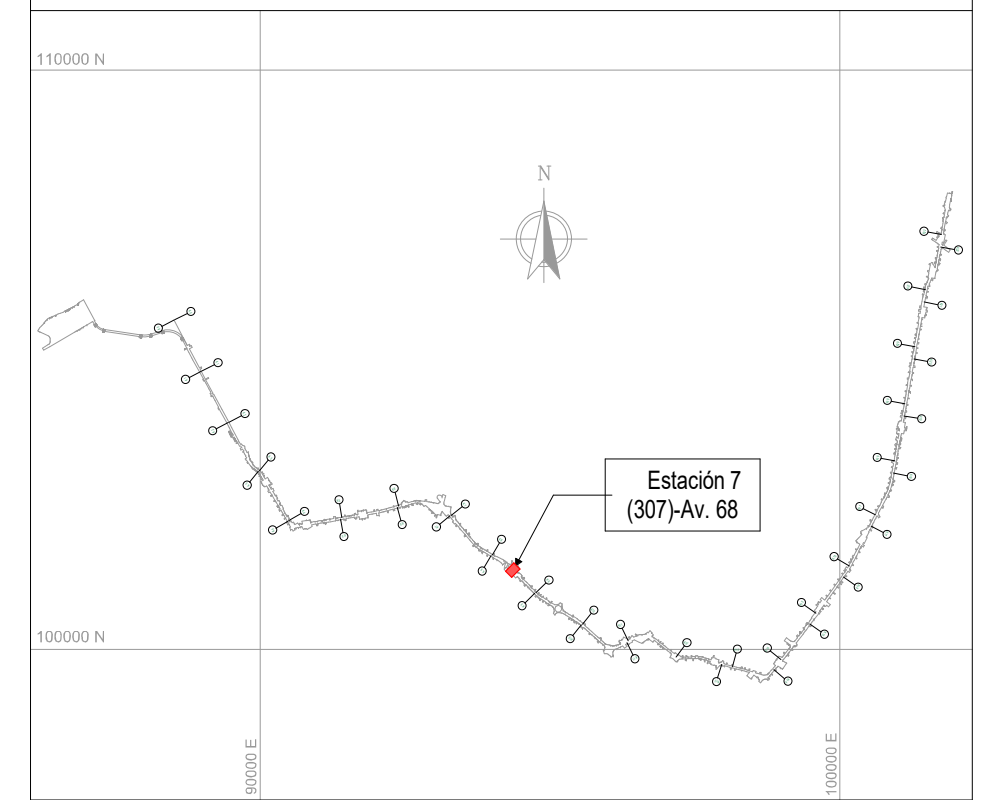

## NOTAS

01 TODAS LAS DIMENSIONES ESTÁN CONFIGURADAS EN METROS A MENOS QUE SE INDIQUE UNA UNIDAD DE MEDIDA DIFERENTE.

02 TODAS LAS MEDIDAS, UBICACIÓN Y NIVELES DEBEN VERIFICARSE EN EL LUGAR DE CONSTRUCCIÓN.

03 EL NIVEL DE ACCESO AL EDIFICIO PL 01 CORRESPONDE AL +0,00 DE LA ESTACIÓN Y REFERENCIA AL NIVEL 2557.05 M.S.N.M.

04 LOS NOMBRES ESPECÍFICOS DE LAS ÁREAS PUEDEN SER CONSULTADAS EN EL PLANO NO. 3 Ó EN LAS VISTAS EN PLANTA.

05 LOS COLORES QUE SE MUESTRAN EN LOS PLANOS COMO PROYECCIÓN DE ELEMENTOS ARQUITECTÓNICOS COMO CUBIERTAS FACHADAS MUROS ETC. NO REPRESENTAN LA MATERIALIDAD Y REALIDAD DE ACABADOS DEL PROYECTO, SOLO SON INDICATIVOS PARA REALIZAR UNA CORRECTA LECTURA DE LA PLANIMETRÍA.

06 LAS ESCALERAS ELÉCTRICAS INDICAN SU SENTIDO CON LA SIGUIENTE NOMENCLATURA: "SUBE" Y "BAJA".

07 SE DEBEN REVISAR LOS NIVELES ESTRUCTURALES PARA NIVEL DE ACCESO PL_01 Y SUBNIVELES, PL_02 (INTERMEDIO), PL_03 (PLATAFORMA) CON LA PLANIMETRÍA DE PLACAS ESTRUCTURALES EN LOS ENTREGABLES L1T1-1200-307-CON-ED-EST-PL-0018,19 Y L1T1-1300-407-CON-ED-EST-PL-0026, 30, 76, RESPECTIVAMENTE. EL NIVEL ESTRUCTURAL (NE) REFERENCIA LOS ESPACIOS DONDE SE DEBE ACONDICIONAR EL ACABADO DE PISO SEGÚN CORRESPONDA, CON LOS NIVELES DE PISO TERMINADO (NPT). LOS NIVELES PROYECTADOS DE EMPATE (NPE) EN LAS ÁREAS DE SERVICIOS ADICIONALES, REFERENCIAN LA ADECUACIÓN DE LOS DESNIVELES EN ESTAS ÁREAS; QUEDA COMO RESPONSABILIDAD DEL LOCATARIO DEFINIR Y ACONDICIONAR ESTE ACABADO DE PISO (NPE) EN LÍNEA CON EL NIVEL (NPT) DE ESPACIOS COLINDANTES. EL NIVEL ESTRUCTURAL (NE) SE ENCUENTRA A (- 0.10M) POR DEBAJO DE LOS NIVELES DE PISO TERMINADO (NPT) Y LOS NIVELES PROYECTADOS DE EMPATE (NPE) MARCADOS EN LA PLANIMETRÍA.

- ARQ_PL_00 = SÓTANO / NPT -6.70m
- ARQ_PL_00.1 = SÓTANO BRT / NPT -6.12m
- ARQ_PL_00.1 = ACCESO / NPT -0.70m
- ARQ_PL_00.2 = ACCESO / NPT -0.55m
- ARQ_PL_00.3 = ACCESO / NPT -0.45m
- ARQ_PL_00.4 = ACCESO / NPT -0.30m
- ARQ_PL_01 = ACCESO / NPT 0.00m
- ARQ_PL_02 = INTERMEDIO / NPT 7.35m
- ARQ_PL_02.2 = TOPE DE RIEL (TOR) / NPT 15.25m
- ARQ_PL_03 = PLATAFORMA / NPT 16.39m
- ARQ_PL_04 = CUBIERTA EDIFICACIONES / NPT 22.99m
- ARQ_PL_05 = CUBIERTA NAVE CENTRAL / NPT 25.70m

## CONVENCIONES

- - - LÍMITE DE INTERVENCIÓN
- - - HUELLA APÉNDICE TÉCNICO
▬ MURO DIVISORIO
— — PROYECCIÓN NIVEL SUPERIOR

| | | | |
|---|---|---|---|
| 🟩 | SERVICIOS ADICIONALES - ÁREA NO PAGA | 🟨 | ÁREA NO PAGA |
| 🟩 | SERVICIOS ADICIONALES - ÁREA PAGA | 🟧 | ÁREA PAGA |
| 🟩 | SERVICIO PÚBLICO | 🟦 | ÁREA PÚBLICA |
| 🟦 | ZONA DE REFUGIO | ⬜ | ÁREA TÉCNICA |
| 🟥 | ÁREA CULTURAL | 🟦 | ÁREA OPERATIVA |

| No. | PLANOS DE REFERENCIA | REV. |
|---|---|---|
| | | |
| **No.** | **MODELO BIM DE REFERENCIA** | **REV.** |
| 1 | L1T1-1100-207-CON-ED-EST-MO-0001.rvt | V00 |
| 2 | L1T1-1100-307-CON-ED-EST-MO-0001.rvt | V00 |
| 3 | L1T1-1150-207-CON-ED-EST-MO-0001.rvt | V00 |
| 4 | L1T1-1150-307-CON-ED-EST-MO-0001.rvt | V00 |
| 5 | L1T1-1200-307-CON-ED-EST-MO-0001.rvt | V00 |
| 6 | L1T1-1300-407-CON-ED-EST-MO-0001.rvt | V00 |
| 7 | L1T1-1300-407-CON-ED-EST-MO-0002.rvt | V00 |
| 8 | L1T1-1310-407-CON-ED-EST-MO-0001.rvt | V00 |
| 9 | L1T1-1410-307-CON-ED-MEC-MO-0001.rvt | V00 |
| 10 | L1T1-1420-307-CON-ED-MEC-MO-0001.rvt | V00 |
| 11 | L1T1-2410-501-CON-ED-EST-MO-0001.rvt | V00 |
| 12 | L1T1-2410-502-CON-ED-EST-MO-0001.rvt | V00 |
| 13 | L1T1-2430-407-CON-ED-EST-MO-0001.rvt | V00 |
| 14 | L1T1-5160-307-CON-ED-EST-MO-0001.rvt | V00 |
| 15 | L1T1-5160-307-CON-ED-ARQ-MO-0001.rvt | V00 |
| 16 | L1T1-5300-307-CON-ED-MEC-MO-0001.rvt | V00 |
| 17 | L1T1-5600-307-CON-ED-INS-MO-0001.rvt | V00 |
| 18 | L1T1-1270-307-CON-ED-ARQ-MO-0011.rvt | V00 |
| 19 | L1T1-1330-407-CON-ED-ARQ-MO-0011.rvt | V00 |
| 20 | L1T1-1330-407-CON-ED-ARQ-MO-0012.rvt | V00 |
| **No.** | **PAQUETE DE TRABAJO DE REFERENCIA** | **REV.** |
| 1 | XREF-URBANISM_CONTEXT_ST07.rvt | |
| 2 | XREF-SECONDARY-STRUCTURE-ST07.rvt | |

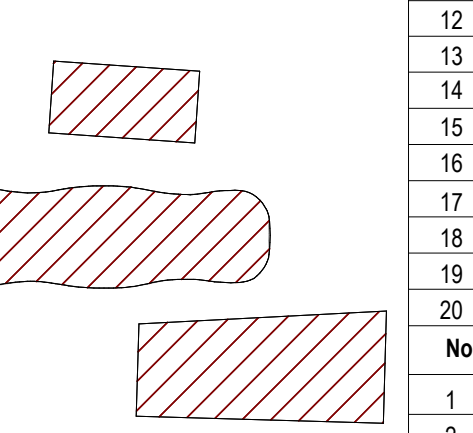

PLANO CLAVE ESTACIÓN 7

0 2 10m
1:200

VÁLIDO PARA CONSTRUCCIÓN
20-03-26

METRO BOGOTÁ · GCS Consorcio Consultores PMO Bogotá · CONSORCIO SUPERVISOR PLMB · CHEC

| | |
|---|---|
| DISEÑÓ: | REN ZHENHUA<br>Licencia de Arq.nivel I (China): 1101735-614 |
| APROBÓ: | DIEGO ERNESTO DUEÑAS<br>Mat.: 25202-53876 CND |
| REVISÓ: | CARLOS MAURICIO BARRETO BARBOSA<br>Mat.: A4012012-14139353 |
| DIBUJÓ: | EQUIPO CHEC |

| REVISIÓN No. | FECHA | DESCRIPCIÓN | REVISÓ | APROBÓ | APROBACIÓN CLIENTE |
|---|---|---|---|---|---|
| V01 | 20/03/2026 | EMITIDO PARA CONSTRUCCIÓN | C.M.B.B | D.E.D | |
| V00 | 27/01/2025 | REVISIÓN NO OBJETADA - EMITIDO PARA CONSTRUCCIÓN | F.B.R | E.O.M | |
| VFF | 04/10/2024 | EMITIDO PARA REVISIÓN Y COMENTARIOS DEL CLIENTE E INTERVENTORÍA - INCLUYE COMENTARIOS /(AJUSTES V3) | F.B.R | E.O.M | |
| VEE | 11/06/2024 | EMITIDO PARA REVISIÓN Y COMENTARIOS DEL CLIENTE E INTERVENTORÍA - INCLUYE COMENTARIOS /(AJUSTES V2) | F.B.R | E.O.M | |
| VDD | 18/12/2022 | EMITIDO PARA REVISIÓN Y COMENTARIOS DEL CLIENTE E INTERVENTORÍA - INCLUYE COMENTARIOS /(AJUSTES) | J.E.M | M.B.M | |
| VCC | 02/06/2022 | EMITIDO PARA REVISIÓN Y COMENTARIOS DEL CLIENTE E INTERVENTORÍA - INCLUYE COMENTARIOS /(ENTREGA 90%) | J.E.M | M.B.M | |
| VBB | 06/12/2021 | EMITIDO PARA REVISIÓN Y COMENTARIOS DEL CLIENTE E INTERVENTORÍA | J.E.M | M.B.M | |
| VA0 | 30/06/2021 | EMITIDO PARA COMENTARIOS INTERNOS - EMISIÓN PRELIMINAR PARA COMENTARIOS | J.E.M | M.B.M | |

METRO LÍNEA 1

METRO LÍNEA 1
CONTRATO DE CONCESIÓN No. 163 DE 2019

PROYECTO PRIMERA LÍNEA DEL METRO DE BOGOTÁ - TRAMO 1

DIRECTOR DE INTERVENTORÍA:
JAVIER DESCARGA N.
Mat.:25202-68697 CND

ESPECIALISTA INTERVENTORÍA:
CARLOS ALBERTO HOYOS SOTO
Mat.:A25072000-14251682

FECHA:
MARZO 2026

INFRAESTRUCTURA VIAL
ARQUITECTURA
ESTACIÓN METRO 7 (AV 68)
GENERAL
VISTA EN PLANTA Y 3D - NIVEL ACCESO

| PLANCHA No: | ESCALA: | REVISIÓN No. | PLANO No. |
|---|---|---|---|
| L1T1-0000-307-CON-ED-ARQ-PL-0001_05_V01 | INDICADA | V01 | 05 DE 107 |
| ARCHIVO: L1T1-0000-307-CON-ED-ARQ-MO-0001_V00.rvt | FECHA: JUNIO 2021 | | |