L1T1-CON-CAL-FR-0120 - B1 : 1000x707mm

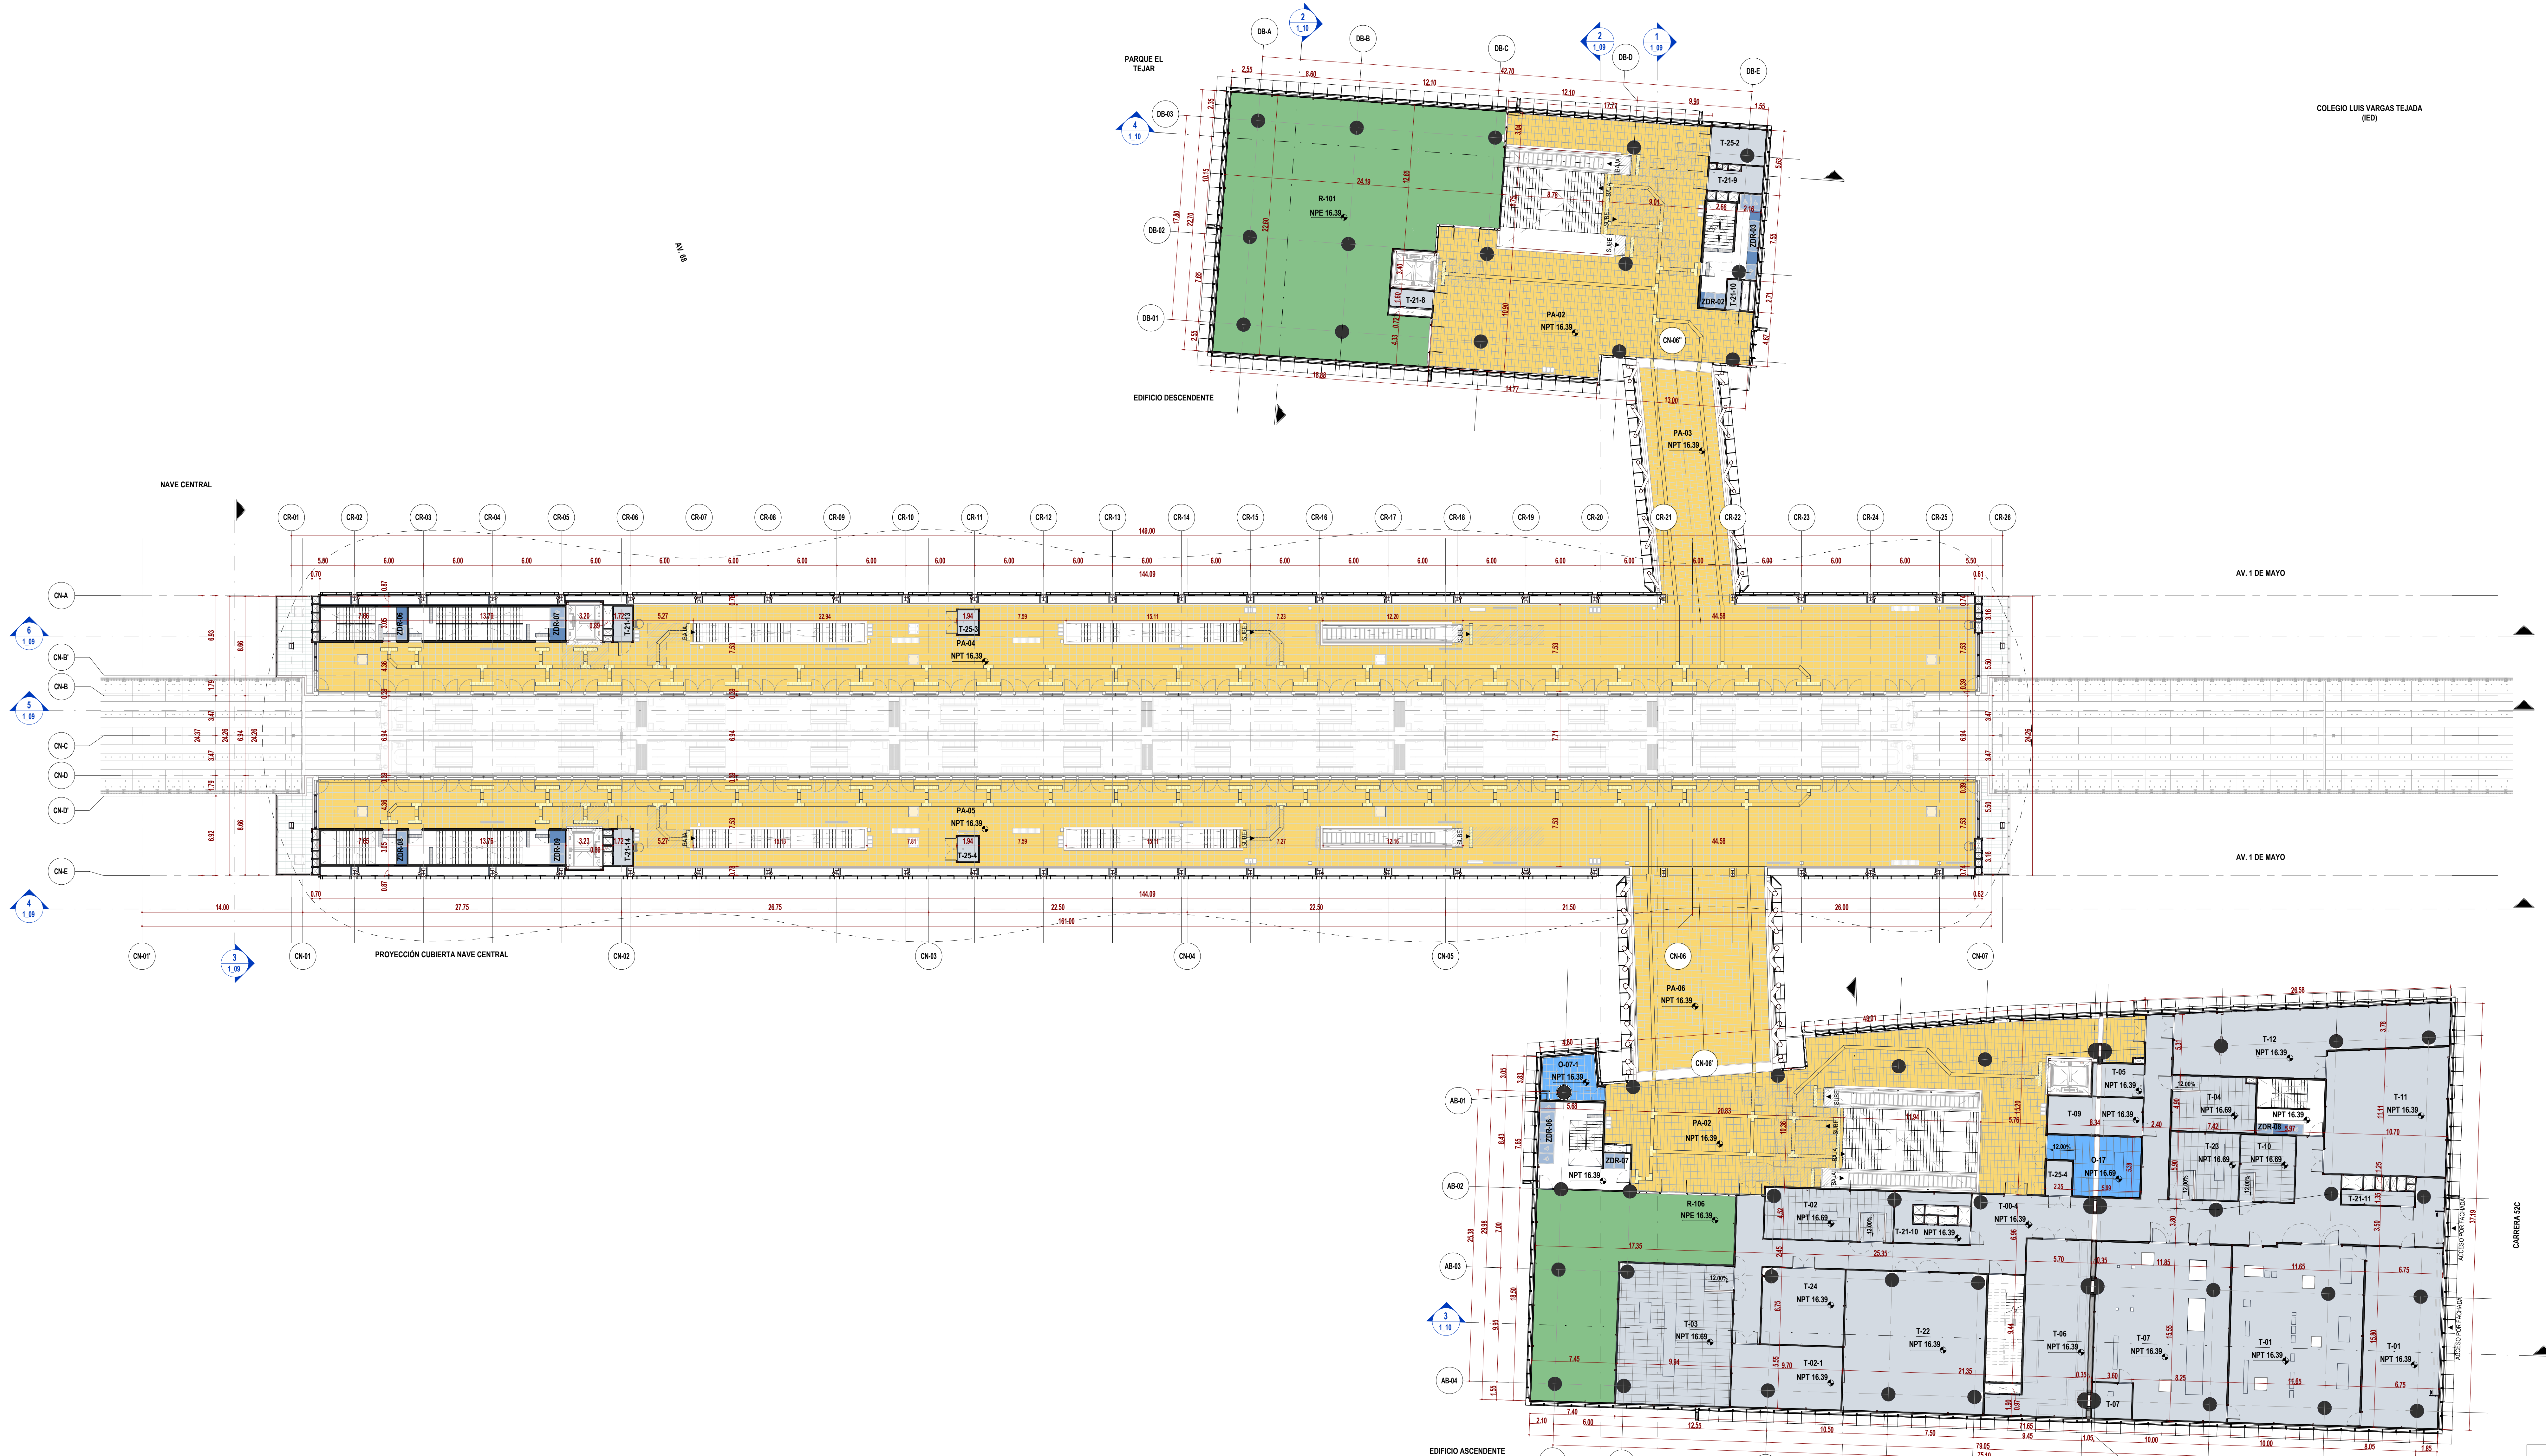

2 NIVEL PLATAFORMA_GENERAL
ESC: 1 : 200

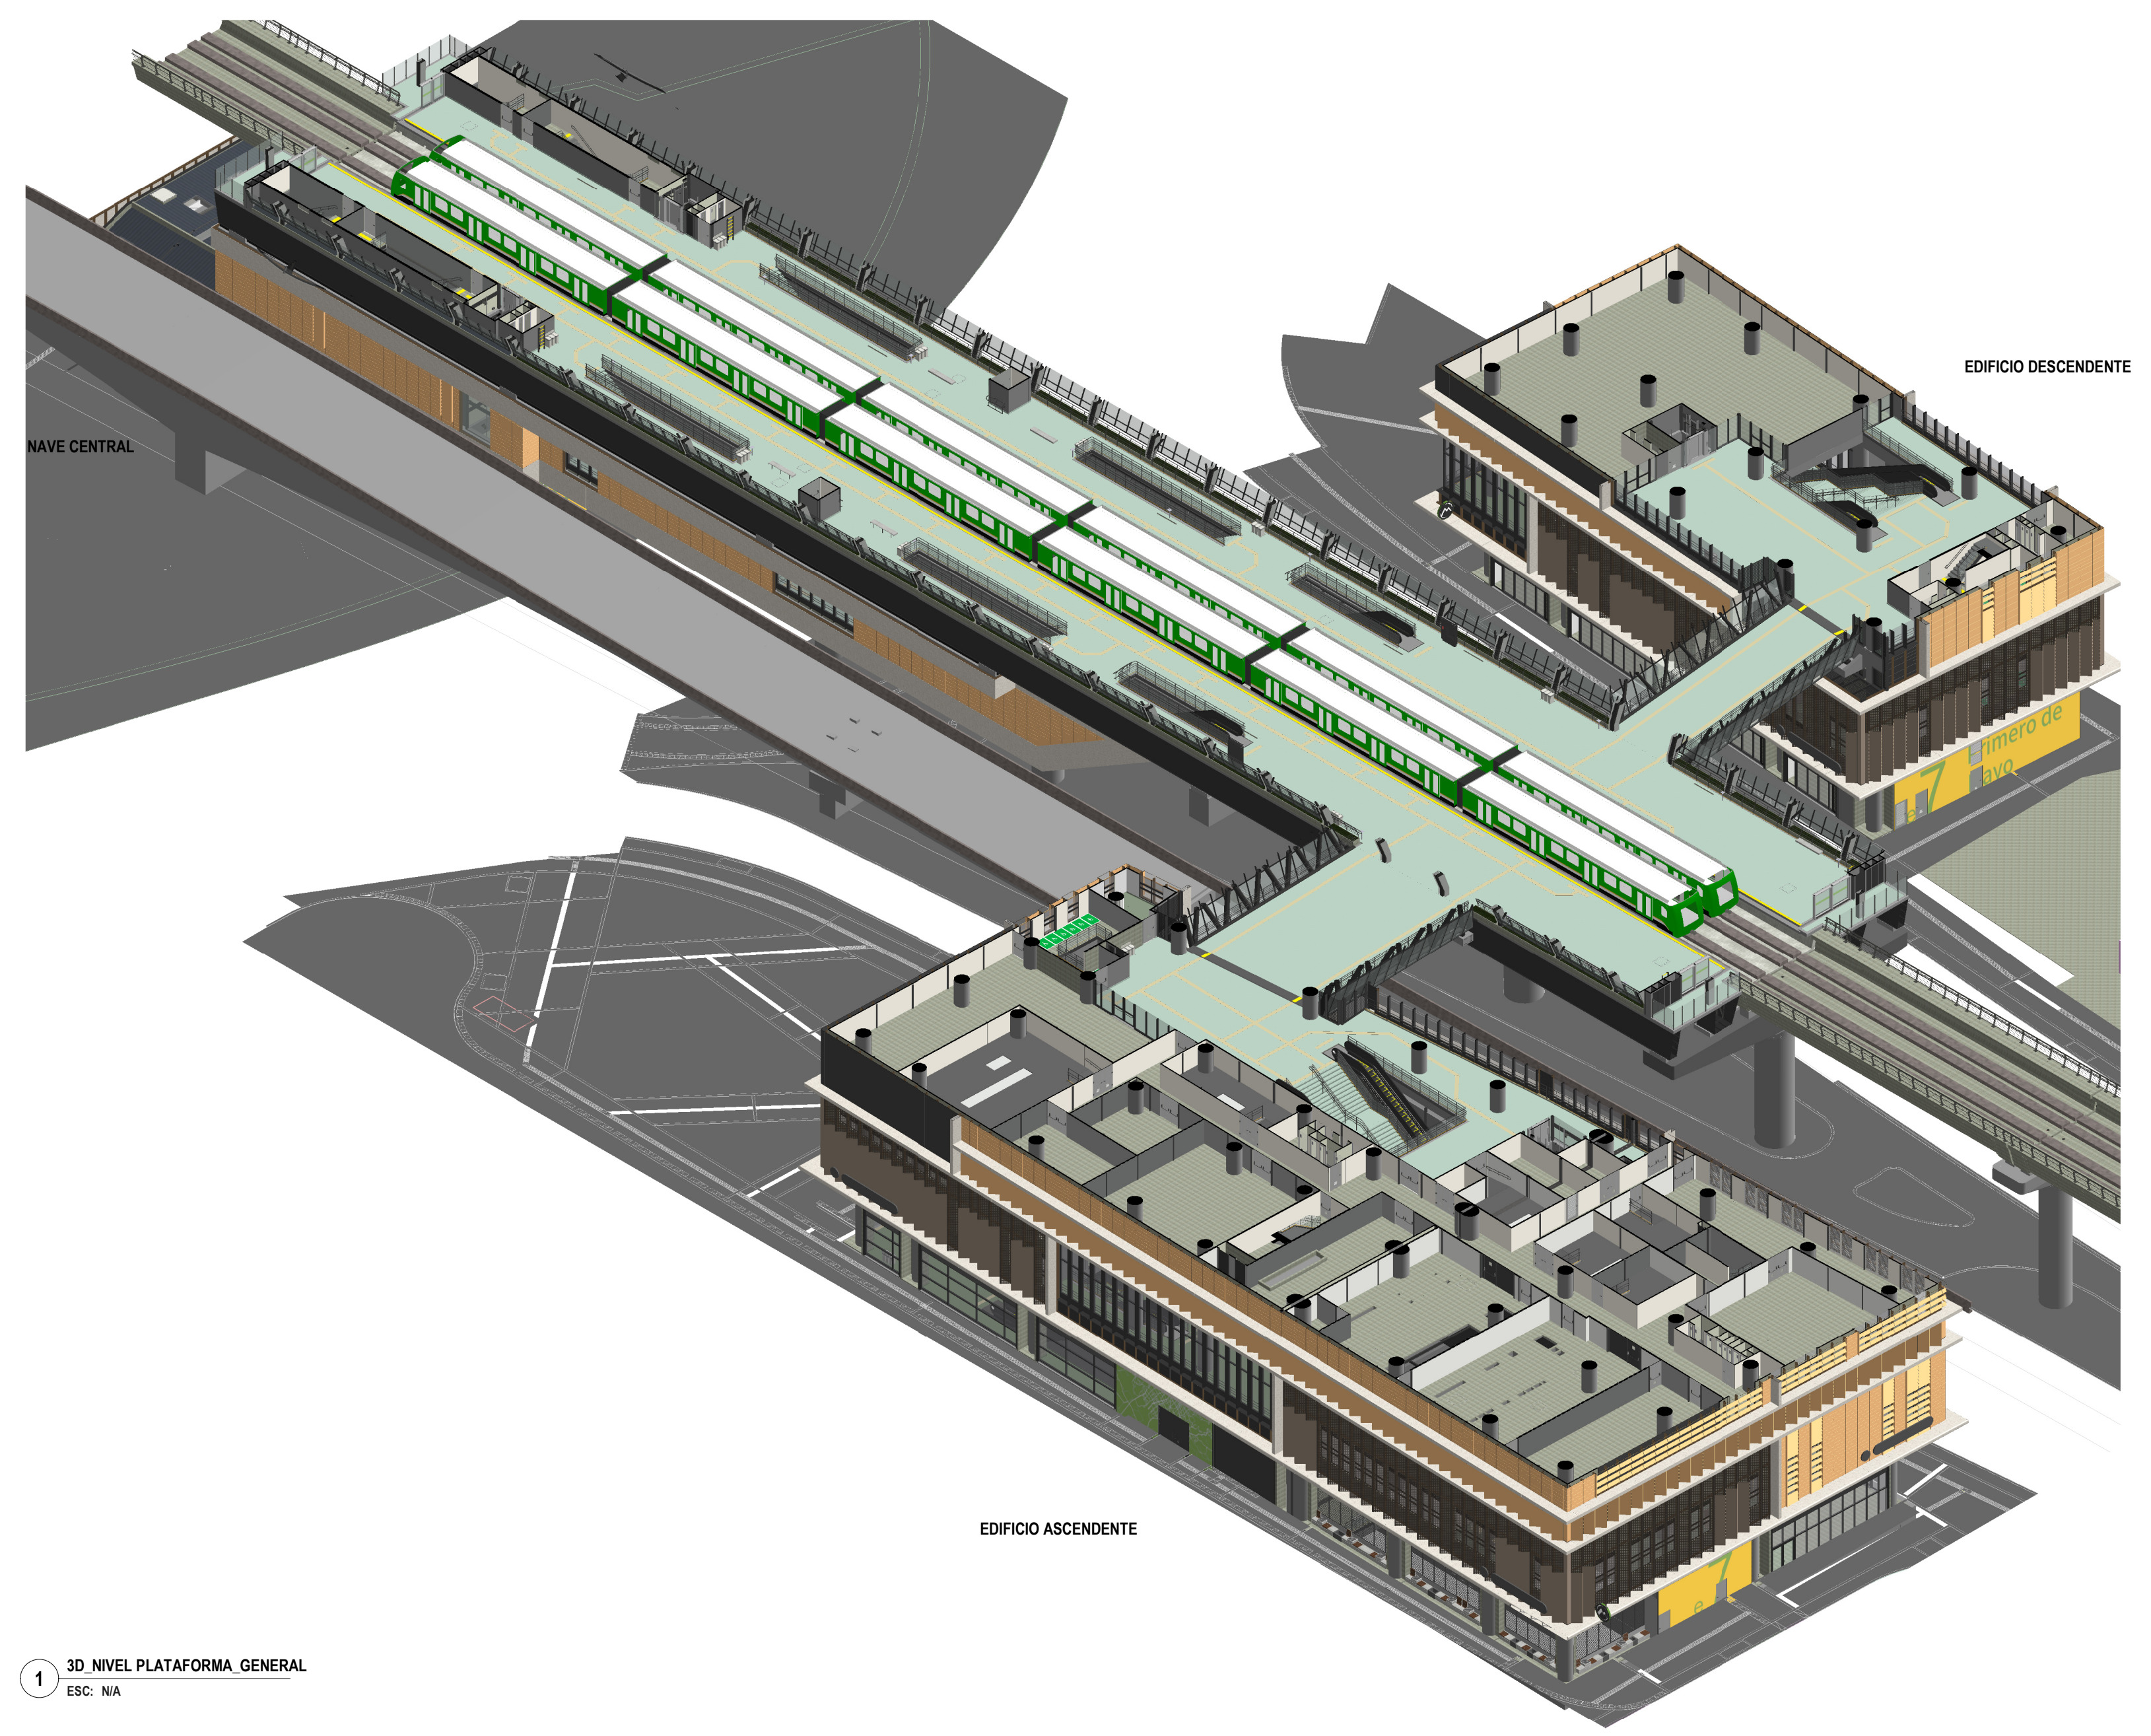

1 3D_NIVEL PLATAFORMA_GENERAL
ESC: N/A

TABLA DE ÁREAS ÚTILES (NIVEL PLATAFORMA)

CÓDIGO	NOMBRE	ÁREA (m²)	DEPARTAMENTO
EDIFICIO ASCENDENTE			
ARQ_PL_03_PLATAFORMA			
O-07-1	CUARTO DE LIMPIEZA COMPLEMENTARIO	18.53	ÁREA OPERATIVA
O-17	OPERADORES TELECOMUNICACIONES EXTERIORES	35.01	ÁREA OPERATIVA
PA-02	ÁREA PAGA	382.13	ÁREA PAGA
R-106	SERVICIOS ADICIONALES - ÁREA DE SERVICIO	189.81	SERVICIOS ADICIONALES - ÁREA PAGA
T-00-4	CIRCULACIÓN TÉCNICA	287.60	ÁREA TÉCNICA
T-01	SUBESTACIÓN DE TRACCIÓN (SET)	279.55	ÁREA TÉCNICA
T-02	LOCAL DE CONDUCCIÓN AUTOMÁTICA (CBTC)	47.21	ÁREA TÉCNICA
T-02-1	UPS DEDICADA (CBTC)	50.74	ÁREA TÉCNICA
T-03	TELECOMUNICACIONES ESTACIÓN - CORRIENTE DÉBIL	117.89	ÁREA TÉCNICA
T-04	EQUIPO BOLETERÍA	33.79	ÁREA TÉCNICA
T-05	ALMACÉN PARA MANTENIMIENTO	12.56	ÁREA TÉCNICA
T-06	SALA DE TABLEROS	89.61	ÁREA TÉCNICA
T-07	CENTRO DE TRANSFORMACIÓN (CT)	175.16	ÁREA TÉCNICA
T-09	ALMACÉN EQUIPO ELÉCTRICO	26.75	ÁREA TÉCNICA
T-10	CUARTO DE EQUIPO ELECTROMECÁNICO	27.23	ÁREA TÉCNICA
T-11	CUARTO DE VENTILACIÓN	115.44	ÁREA TÉCNICA
T-12	PLANTA DE REFRIGERACIÓN PARA LA CLIMATIZACIÓN	110.95	ÁREA TÉCNICA
T-21-10	ÁREA DE INSPECCIÓN	19.53	ÁREA TÉCNICA
T-21-11	ÁREA DE INSPECCIÓN	7.86	ÁREA TÉCNICA
T-22	CUARTO DE UPS	143.50	ÁREA TÉCNICA
T-23	CUARTO PDAP	34.64	ÁREA TÉCNICA
T-24	TETRA UPS	45.60	ÁREA TÉCNICA
T-25-4	NODO DE ACCESO DE TELECOMUNICACIONES	6.67	ÁREA TÉCNICA
ZDR-06	ZONA DE REFUGIO (PMR)	7.30	ZONA DE REFUGIO
ZDR-07	ZONA DE REFUGIO (PMR)	2.49	ZONA DE REFUGIO
ZDR-08	ZONA DE REFUGIO (PMR)	3.69	ZONA DE REFUGIO

TABLA DE ÁREAS ÚTILES (NIVEL PLATAFORMA)

CÓDIGO	NOMBRE	ÁREA (m²)	DEPARTAMENTO
EDIFICIO DESCENDENTE			
ARQ_PL_03_PLATAFORMA			
PA-02	ÁREA PAGA	375.03	ÁREA PAGA
R-101	SERVICIOS ADICIONALES - ÁREA DE SERVICIO	446.27	SERVICIOS ADICIONALES - ÁREA PAGA
T-21-8	ÁREA DE INSPECCIÓN	5.46	ÁREA TÉCNICA
T-21-9	ÁREA DE INSPECCIÓN	9.52	ÁREA TÉCNICA
T-21-10	ÁREA DE INSPECCIÓN	3.10	ÁREA TÉCNICA
T-25-2	NODO DE ACCESO DE TELECOMUNICACIONES	13.28	ÁREA TÉCNICA
ZDR-02	ZONA DE REFUGIO (PMR)	2.92	ZONA DE REFUGIO
ZDR-03	ZONA DE REFUGIO (PMR)	7.89	ZONA DE REFUGIO
NAVE CENTRAL			
ARQ_PL_03_PLATAFORMA			
PA-03	ÁREA PAGA	128.19	ÁREA PAGA
PA-04	ÁREA PAGA	907.70	ÁREA PAGA
PA-05	ÁREA PAGA	907.84	ÁREA PAGA
PA-06	ÁREA PAGA	202.65	ÁREA PAGA
T-21-13	ÁREA DE INSPECCIÓN	4.84	ÁREA TÉCNICA
T-21-14	ÁREA DE INSPECCIÓN	4.84	ÁREA TÉCNICA
T-25-3	NODO DE ACCESO DE TELECOMUNICACIONES	3.74	ÁREA TÉCNICA
T-25-4	NODO DE ACCESO DE TELECOMUNICACIONES	3.73	ÁREA TÉCNICA
ZDR-06	ZONA DE REFUGIO (PMR)	2.58	ZONA DE REFUGIO
ZDR-07	ZONA DE REFUGIO (PMR)	3.87	ZONA DE REFUGIO
ZDR-08	ZONA DE REFUGIO (PMR)	2.58	ZONA DE REFUGIO
ZDR-09	ZONA DE REFUGIO (PMR)	3.87	ZONA DE REFUGIO
TOTAL NIVEL PLATAFORMA		5311.14	

TABLA DE ÁREAS ÚTILES POR DEPARTAMENTO (NIVEL PLATAFORMA)

DEPARTAMENTO	ÁREA (m²)
EDIFICIO ASCENDENTE	
ARQ_PL_03_PLATAFORMA	
SERVICIOS ADICIONALES - ÁREA PAGA	189.81
ZONA DE REFUGIO	13.48
ÁREA OPERATIVA	53.54
ÁREA PAGA	382.13
ÁREA TÉCNICA	1632.27
EDIFICIO DESCENDENTE	
ARQ_PL_03_PLATAFORMA	
SERVICIOS ADICIONALES - ÁREA PAGA	446.27
ZONA DE REFUGIO	10.80
ÁREA PAGA	375.03
ÁREA TÉCNICA	31.36
NAVE CENTRAL	
ARQ_PL_03_PLATAFORMA	
ZONA DE REFUGIO	12.91
ÁREA PAGA	2146.38
ÁREA TÉCNICA	17.16
TOTAL NIVEL PLATAFORMA	5311.14

LOCALIZACIÓN

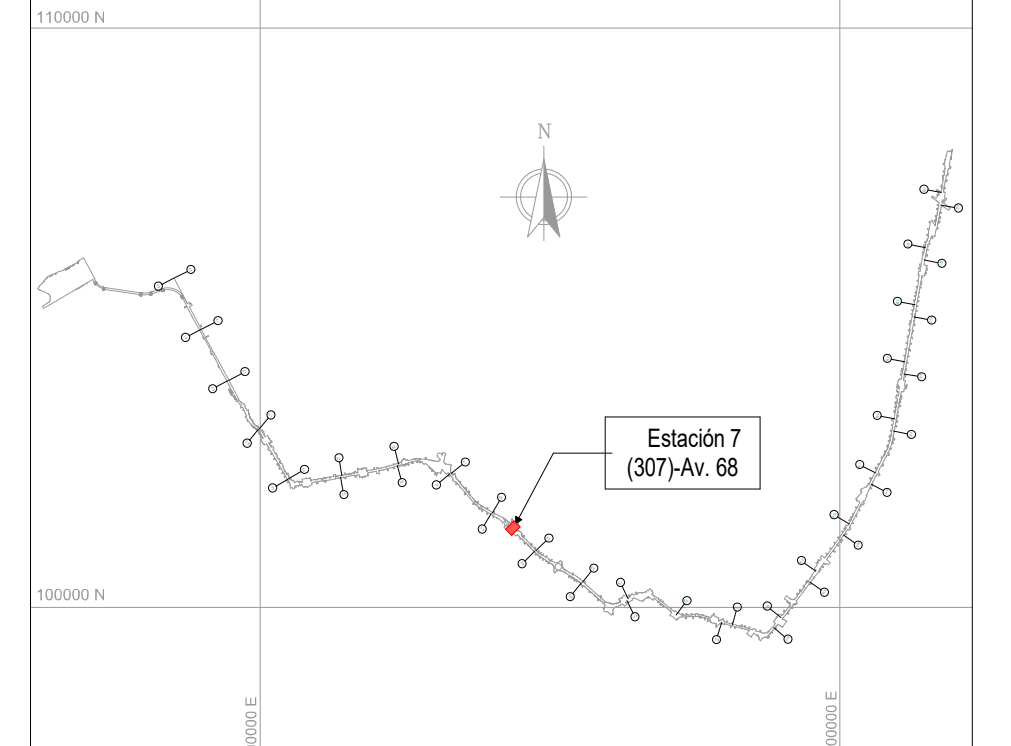

NOTAS

01 TODAS LAS DIMENSIONES ESTÁN CONFIGURADAS EN METROS A MENOS QUE SE INDIQUE UNA UNIDAD DE MEDIDA DIFERENTE.

02 TODAS LAS MEDIDAS, UBICACIÓN Y NIVELES DEBEN VERIFICARSE EN EL LUGAR DE CONSTRUCCIÓN.

03 EL NIVEL DE ACCESO AL EDIFICIO PL 01 CORRESPONDE AL +0,00 DE LA ESTACIÓN Y REFERENCIA AL NIVEL 2557.05 M.S.N.M.

04 LOS NOMBRES ESPECIFICOS DE LAS ÁREAS PUEDEN SER CONSULTADAS EN EL PLANO NO. 3 Ó EN LAS VISTAS EN PLANTA.

05 LOS COLORES QUE SE MUESTRAN EN LOS PLANOS COMO PROYECCIÓN DE ELEMENTOS ARQUITECTÓNICOS COMO CUBIERTAS FACHADAS MUROS ETC. NO REPRESENTAN LA MATERIALIDAD Y REALIDAD DE ACABADOS DEL PROYECTO, SOLO SON INDICATIVOS PARA REALIZAR UNA CORRECTA LECTURA DE LA PLANIMETRÍA.

06 LAS ESCALERAS ELÉCTRICAS INDICAN SU SENTIDO CON LA SIGUIENTE NOMENCLATURA: "SUBE" Y "BAJA".

07 SE DEBEN REVISAR LOS NIVELES ESTRUCTURALES PARA NIVEL DE ACCESO PL_01 Y SUBNIVELES, PL_02 (INTERMEDIO), PL_03 (PLATAFORMA) CON LA PLANIMETRÍA DE PLACAS ESTRUCTURALES EN LOS ENTREGABLES L1T1-1200-307-CON-ED-EST-PL-0018,19 Y L1T1-1300-407-CON-ED-EST-PL-0026, 30, 76, RESPECTIVAMENTE. EL NIVEL ESTRUCTURAL (NE) REFERENCIA LOS ESPACIOS DONDE SE DEBE ACONDICIONAR EL ACABADO DE PISO SEGÚN CORRESPONDA, CON LOS NIVELES DE PISO TERMINADO (NPT). LOS NIVELES PROYECTADOS DE EMPATE (NPE) EN LAS ÁREAS DE SERVICIOS ADICIONALES, REFERENCIAN LA ADECUACIÓN DE LOS DESNIVELES EN ESTAS ÁREAS; QUEDA COMO RESPONSABILIDAD DEL LOCATARIO DEFINIR Y ACONDICIONAR ESTE ACABADO DE PISO (NPE) EN LÍNEA CON EL NIVEL (NPT) DE ESPACIOS COLINDANTES. EL NIVEL ESTRUCTURAL (NE) SE ENCUENTRA A (- 0.10M) POR DEBAJO DE LOS NIVELES DE PISO TERMINADO (NPT) Y LOS NIVELES PROYECTADOS DE EMPATE (NPE) MARCADOS EN LA PLANIMETRÍA.

- ARQ_PL_00 = SÓTANO	/ NPT -6.70m	- ARQ_PL_01 = ACCESO	/ NPT 0.00m
- ARQ_PL_00.1 = SÓTANO BRT	/ NPT -6.12m	- ARQ_PL_02 = INTERMEDIO	/ NPT 7.35m
- ARQ_PL_00.1 = ACCESO	/ NPT -0.70m	- ARQ_PL_02.2 = TOPE DE RIEL (TOR)	/ NPT 15.25m
- ARQ_PL_00.2 = ACCESO	/ NPT -0.55m	- ARQ_PL_03 = PLATAFORMA	/ NPT 16.39m
- ARQ_PL_00.3 = ACCESO	/ NPT -0.45m	- ARQ_PL_04 = CUBIERTA EDIFICACIONES	/ NPT 22.99m
- ARQ_PL_00.4 = ACCESO	/ NPT -0.30m	- ARQ_PL_05 = CUBIERTA NAVE CENTRAL	/ NPT 25.70m

CONVENCIONES

▬ ▬ ▬	LÍMITE DE INTERVENCIÓN
– – –	HUELLA APÉNDICE TÉCNICO
■	MURO DIVISORIO
— — —	PROYECCIÓN NIVEL SUPERIOR

🟩	SERVICIOS ADICIONALES - ÁREA NO PAGA	🟨	ÁREA NO PAGA
🟩	SERVICIOS ADICIONALES - ÁREA PAGA	🟨	ÁREA PAGA
🟩	SERVICIO PÚBLICO	🟦	ÁREA PÚBLICA
🟦	ZONA DE REFUGIO	⬜	ÁREA TÉCNICA
🟥	ÁREA CULTURAL	🟦	ÁREA OPERATIVA

No.	PLANOS DE REFERENCIA	REV.
No.	**MODELO BIM DE REFERENCIA**	**REV.**
1	L1T1-1100-207-CON-ED-EST-MO-0001.rvt	V00
2	L1T1-1100-307-CON-ED-EST-MO-0001.rvt	V00
3	L1T1-1150-207-CON-ED-EST-MO-0001.rvt	V00
4	L1T1-1150-307-CON-ED-EST-MO-0001.rvt	V00
5	L1T1-1200-307-CON-ED-EST-MO-0001.rvt	V00
6	L1T1-1300-407-CON-ED-EST-MO-0001.rvt	V00
7	L1T1-1300-407-CON-ED-EST-MO-0002.rvt	V00
8	L1T1-1310-407-CON-ED-EST-MO-0001.rvt	V00
9	L1T1-1410-307-CON-ED-MEC-MO-0001.rvt	V00
10	L1T1-1420-307-CON-ED-MEC-MO-0001.rvt	V00
11	L1T1-2410-501-CON-ED-EST-MO-0001.rvt	V00
12	L1T1-2410-502-CON-ED-EST-MO-0001.rvt	V00
13	L1T1-2430-407-CON-ED-EST-MO-0001.rvt	V00
14	L1T1-5160-307-CON-ED-EST-MO-0001.rvt	V00
15	L1T1-5160-307-CON-ED-ARQ-MO-0001.rvt	V00
16	L1T1-5300-307-CON-ED-MEC-MO-0001.rvt	V00
17	L1T1-5600-307-CON-ED-INS-MO-0001.rvt	V00
18	L1T1-1270-307-CON-ED-ARQ-MO-0011.rvt	V00
19	L1T1-1330-407-CON-ED-ARQ-MO-0011.rvt	V00
20	L1T1-1330-407-CON-ED-ARQ-MO-0012.rvt	V00
No.	**PAQUETE DE TRABAJO DE REFERENCIA**	**REV.**
1	XREF-URBANISM_CONTEXT_ST07.rvt	
2	XREF-SECONDARY-STRUCTURE-ST07.rvt	

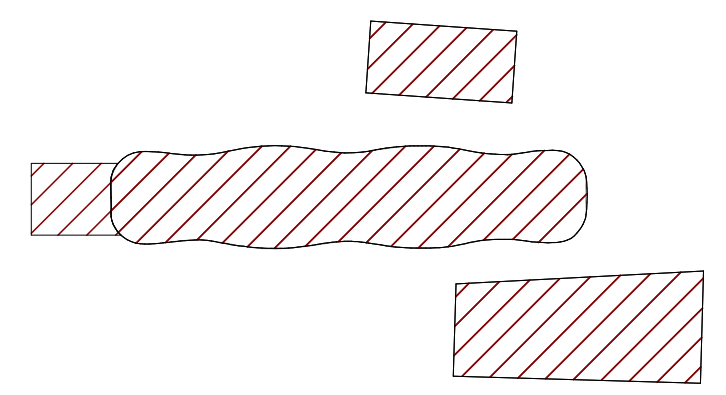

VÁLIDO PARA CONSTRUCCIÓN
20-03-26

PLANO CLAVE ESTACIÓN 7

0 2 10m
1:200

DISEÑO:
REN ZHENHUA
Licencia de Arq.nivel I (China): 1101735-614

APROBÓ:
DIEGO ERNESTO DUEÑAS
Mat.: 25202-53876 CND

REVISÓ:
CARLOS MAURICIO BARRETO BARBOSA
Mat.: A4012012-14139353

DIBUJÓ:
EQUIPO CHEC

REVISIÓN No.	FECHA	DESCRIPCIÓN	REVISÓ	APROBÓ	APROBACIÓN CLIENTE
V01	20/03/2026	EMITIDO PARA CONSTRUCCIÓN	C.M.B.B	D.E.D	
V00	27/01/2025	REVISIÓN NO OBJETADA - EMITIDO PARA CONSTRUCCIÓN	F.B.R	E.O.M	
VFF	04/10/2024	EMITIDO PARA REVISIÓN Y COMENTARIOS DEL CLIENTE E INTERVENTORÍA - INCLUYE COMENTARIOS /(AJUSTES V3)	F.B.R	E.O.M	
VEE	11/06/2024	EMITIDO PARA REVISIÓN Y COMENTARIOS DEL CLIENTE E INTERVENTORÍA - INCLUYE COMENTARIOS /(AJUSTES V2)	F.B.R	E.O.M	
VDD	18/12/2022	EMITIDO PARA REVISIÓN Y COMENTARIOS DEL CLIENTE E INTERVENTORÍA - INCLUYE COMENTARIOS /(AJUSTES)	J.E.M	M.B.M	
VCC	02/06/2022	EMITIDO PARA REVISIÓN Y COMENTARIOS DEL CLIENTE E INTERVENTORÍA - INCLUYE COMENTARIOS /(ENTREGA 90%)	J.E.M	M.B.M	
VBB	06/12/2021	EMITIDO PARA REVISIÓN Y COMENTARIOS DEL CLIENTE E INTERVENTORÍA	J.E.M	M.B.M	
VA0	30/06/2021	EMITIDO PARA COMENTARIOS INTERNOS - EMISIÓN PRELIMINAR PARA COMENTARIOS	J.E.M	M.B.M	

METRO LÍNEA 1
CONTRATO DE CONCESIÓN No. 163 DE 2019

PROYECTO PRIMERA LÍNEA DEL METRO DE BOGOTÁ - TRAMO 1

DIRECTOR DE INTERVENTORÍA:
JAVIER DESCARGA N.
Mat.:25202-68697 CND

ESPECIALISTA INTERVENTORÍA:
CARLOS ALBERTO HOYOS SOTO
Mat.:A25072000-14251682

FECHA: MARZO 2026

INFRAESTRUCTURA VIAL
ARQUITECTURA
ESTACIÓN METRO 7 (AV 68)
GENERAL
VISTA EN PLANTA Y 3D - NIVEL PLATAFORMA

PLANCHA No: L1T1-0000-307-CON-ED-ARQ-PL-0001_07_V01
ARCHIVO: L1T1-0000-307-CON-ED-ARQ-MO-0001_V00.rvt
ESCALA: INDICADA
FECHA: JUNIO 2021
REVISIÓN No. V01
PLANO No. 07 DE 107