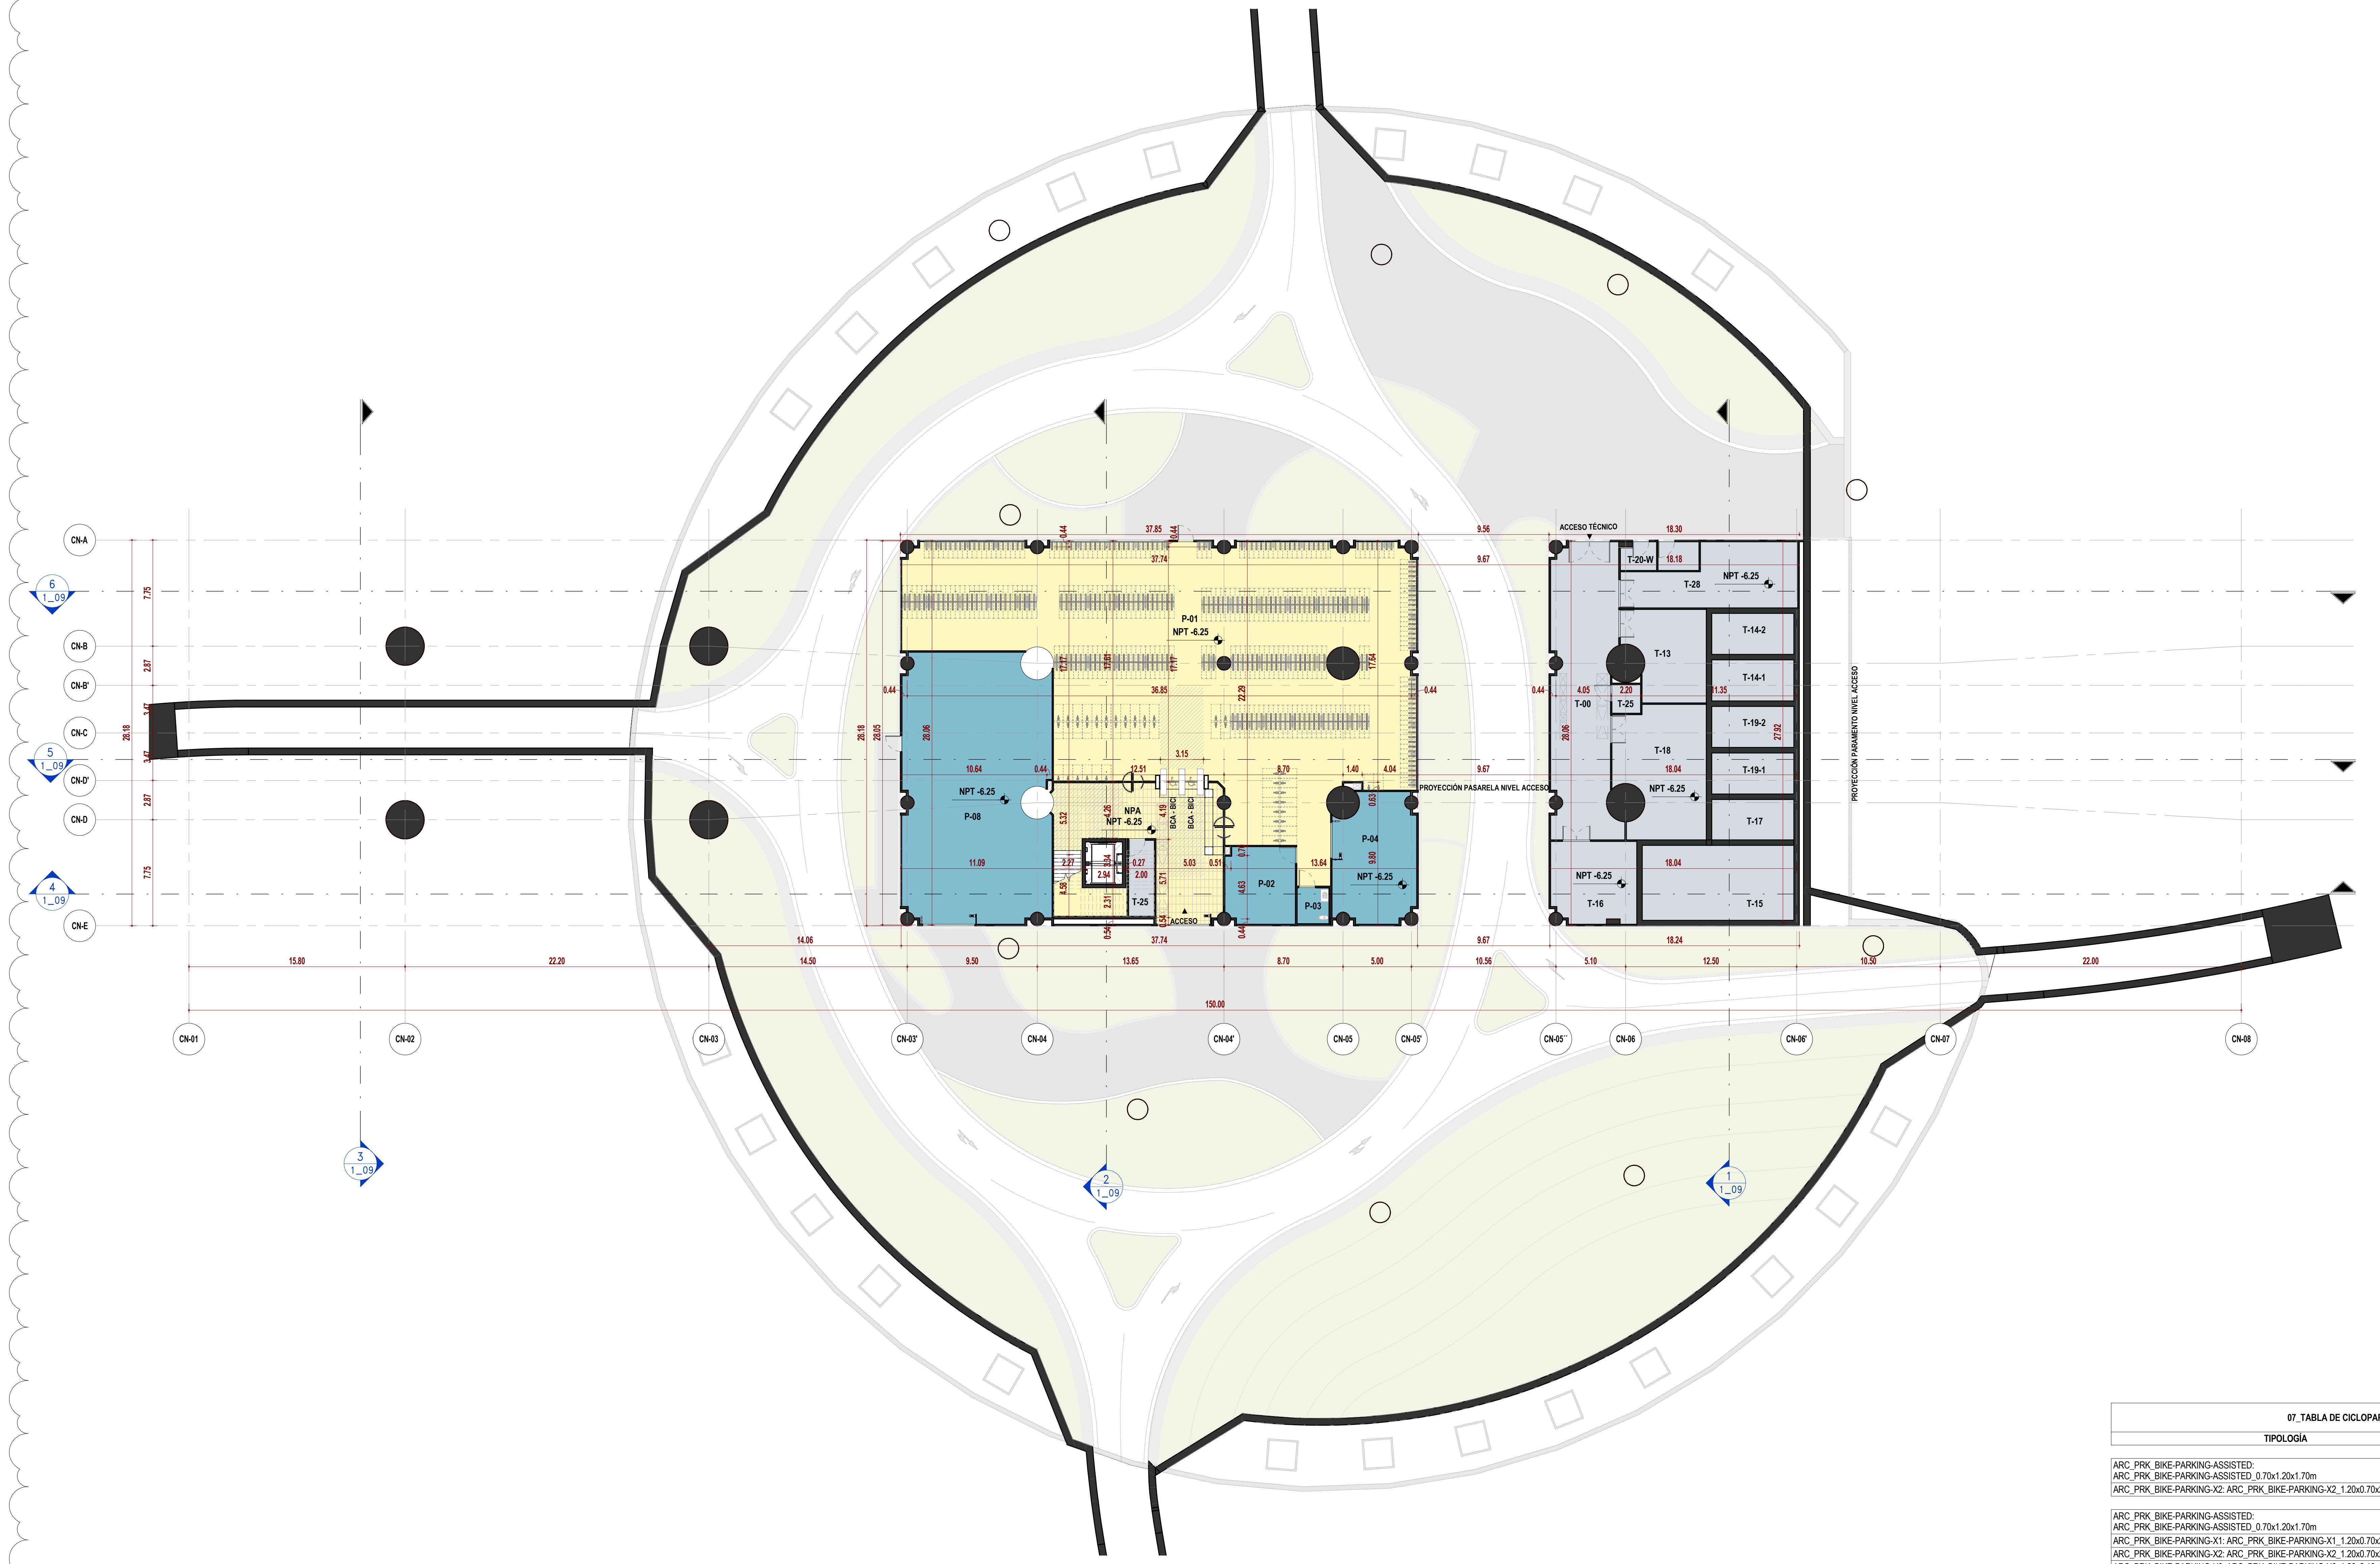

2 **NIVEL SÓTANO_NAVE CENTRAL**
ESC: 1 : 200

VDD

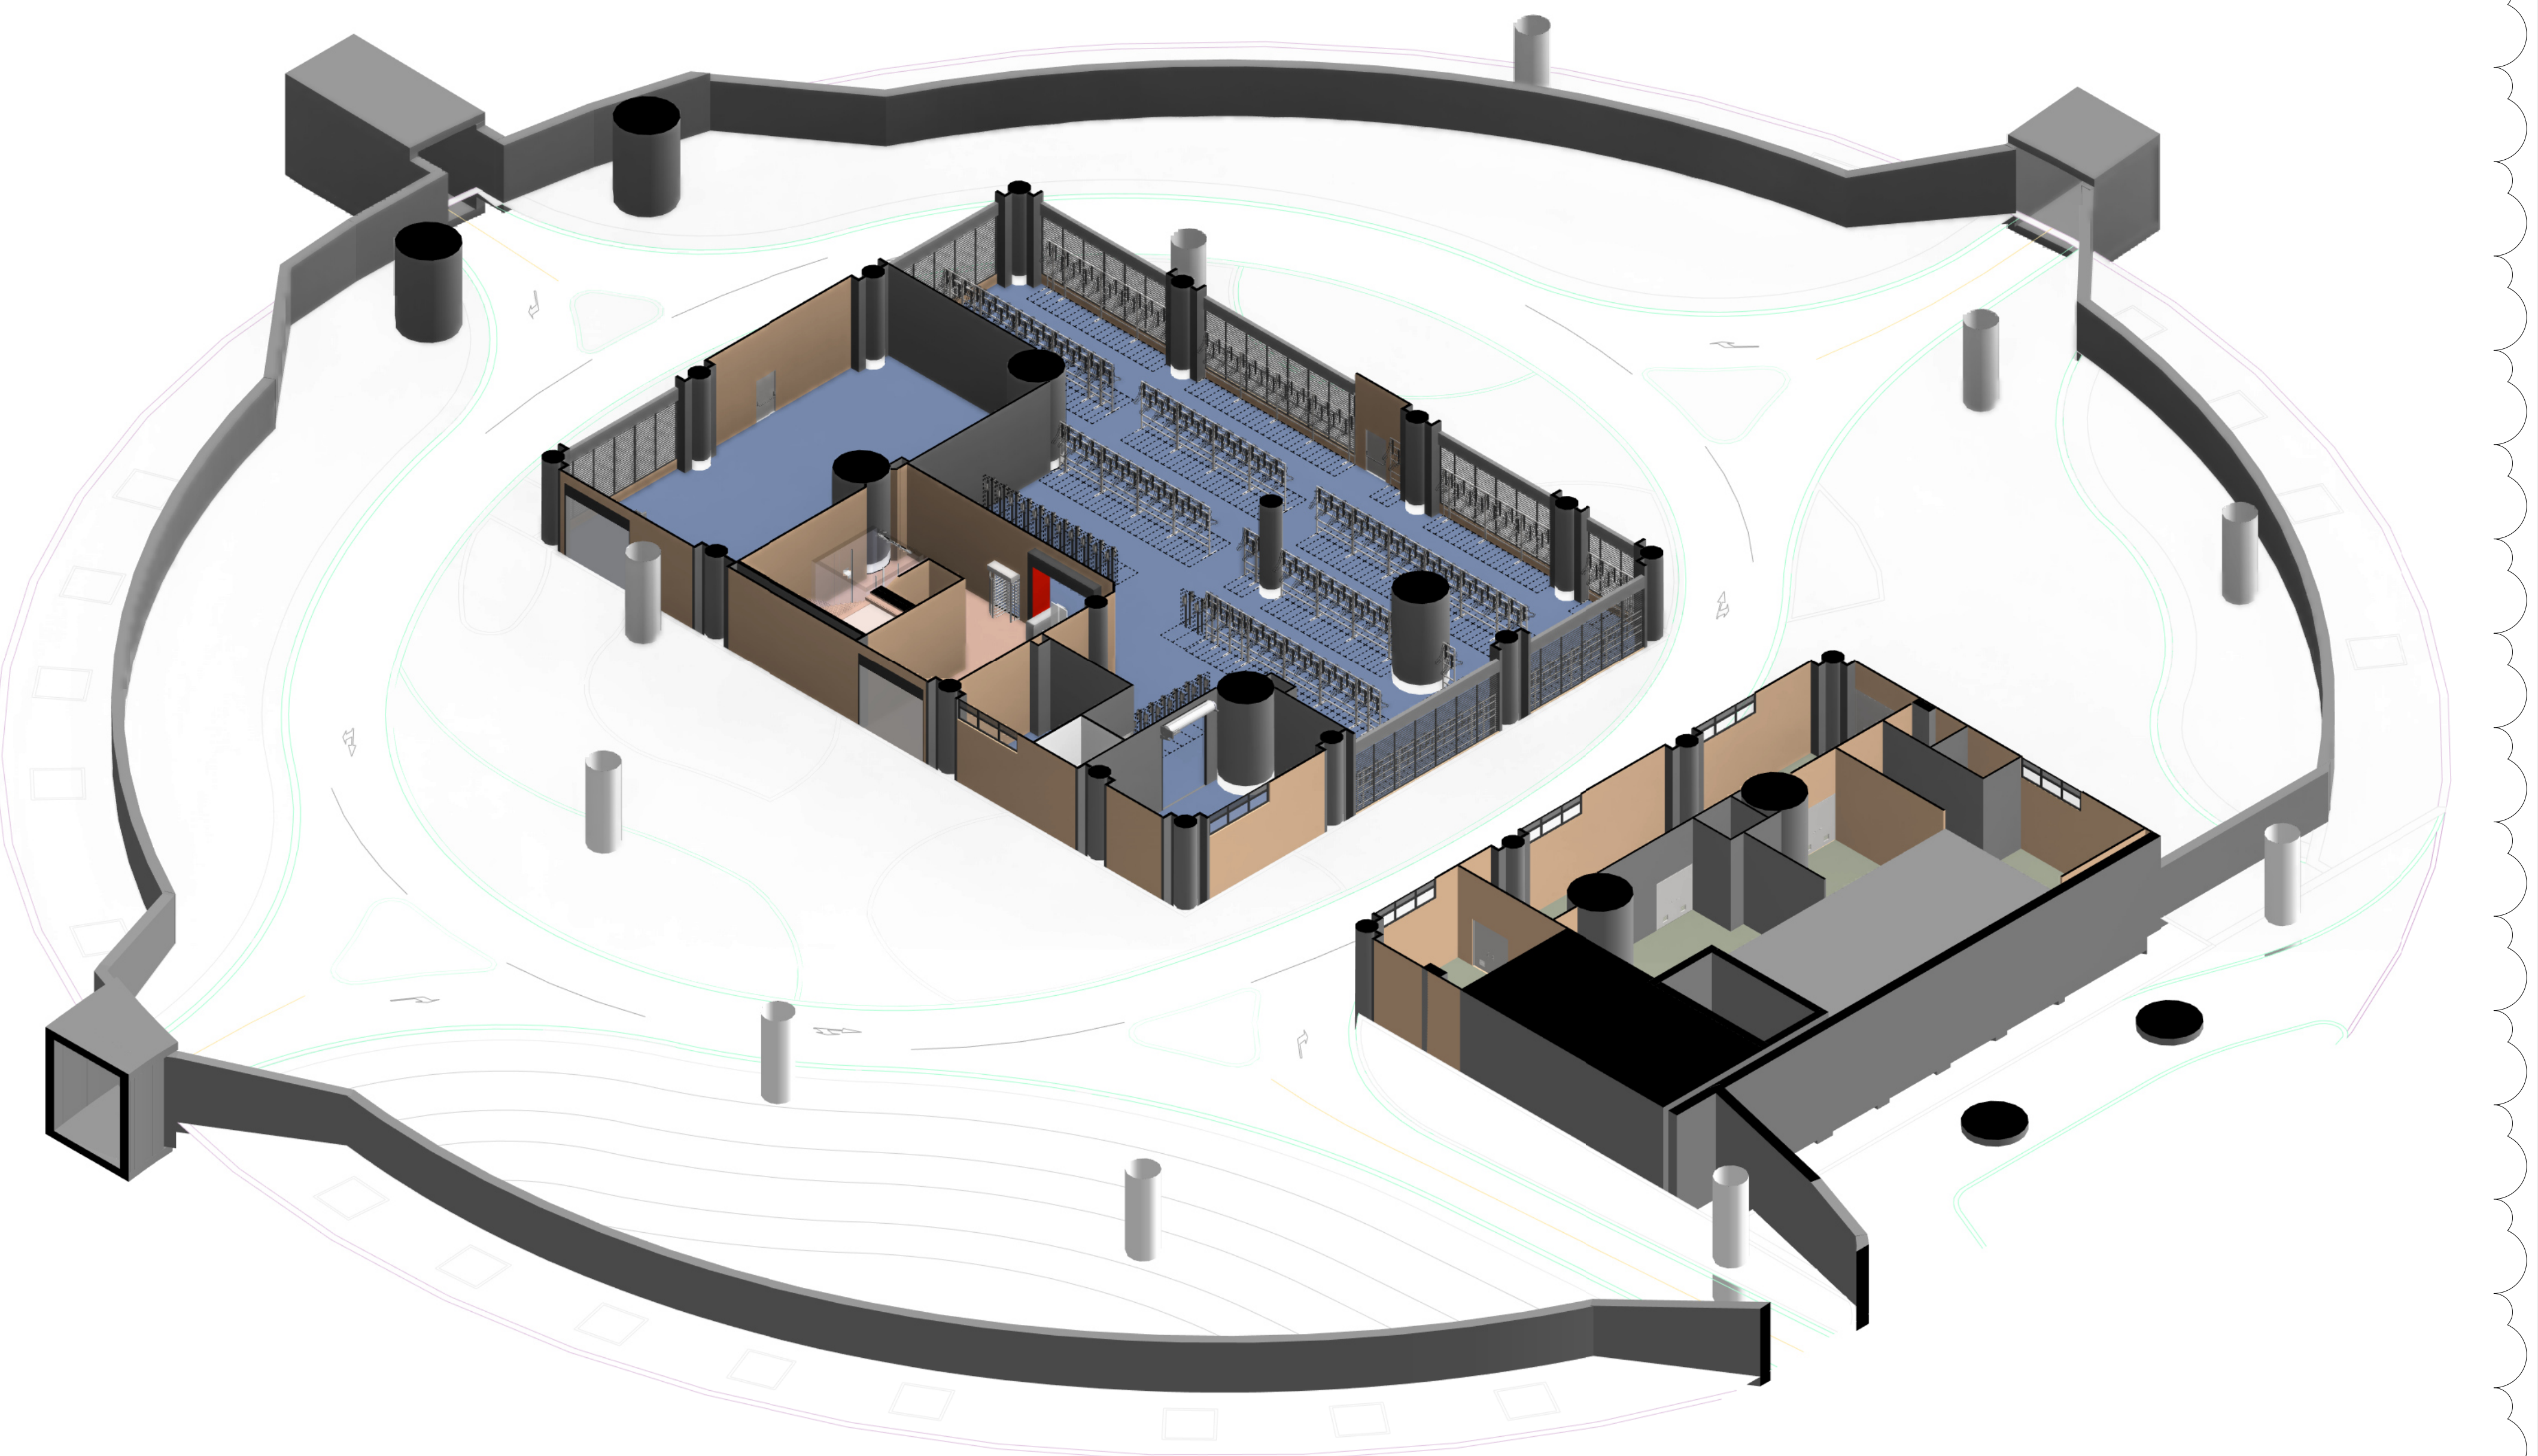

1 **3D_NIVEL SÓTANO_NAVE CENTRAL**
ESC: N/A

07_TABLA DE CICLOPARQUEADEROS

TIPOLOGÍA	CANTIDAD	USUARIOS
ARC_PRK_BIKE-PARKING-ASSISTED: ARC_PRK_BIKE-PARKING-ASSISTED_0.70x1.20x1.70m	1	EMPLEADOS
ARC_PRK_BIKE-PARKING-X2: ARC_PRK_BIKE-PARKING-X2_1.20x0.70x2.40m	4	EMPLEADOS
	5	
ARC_PRK_BIKE-PARKING-ASSISTED: ARC_PRK_BIKE-PARKING-ASSISTED_0.70x1.20x1.70m	49	VISITANTE
ARC_PRK_BIKE-PARKING-X1: ARC_PRK_BIKE-PARKING-X1_1.20x0.70x2.40m	20	VISITANTE
ARC_PRK_BIKE-PARKING-X2: ARC_PRK_BIKE-PARKING-X2_1.20x0.70x2.40m	54	VISITANTE
ARC_PRK_BIKE-PARKING-X6: ARC_PRK_BIKE-PARKING-X6_1.20x2.10x2.40m	372	VISITANTE
	495	
TOTAL CUPOS	500	

06_TABLA DE ÁREAS (NIVEL SÓTANO_NAVE CENTRAL)

CÓDIGO	NOMBRE	ÁREA (m²)	DEPARTAMENTO
ARC_PL_00			
P-01	ÁREA CICLO-PARQUEADEROS	686.02	ÁREA PÚBLICA
P-02	ÁREA OPERATIVA CICLO-PARQUEADEROS	28.38	ÁREA PÚBLICA
P-03	BAÑO OPERADOR CICLO-PARQUEADEROS	6.09	ÁREA PÚBLICA
P-04	TALLER DE BICICLETAS	53.16	ÁREA PÚBLICA
P-08	ESPACIO CARGA DE VEHÍCULOS ELÉCTRICOS	204.56	ÁREA PÚBLICA
T-00	CIRCULACIÓN TÉCNICA	97.50	ÁREA TÉCNICA
T-13	CUARTO DE BOMBAS DE SUMINISTRO DE AGUA	36.19	ÁREA TÉCNICA
T-14-1	TANQUE DE SUMINISTRO DE AGUA	18.00	ÁREA TÉCNICA
T-14-2	TANQUE DE SUMINISTRO DE AGUA	18.00	ÁREA TÉCNICA
T-15	TANQUE SISTEMA CONTRA INCENDIOS (RCI)	60.72	ÁREA TÉCNICA
T-16	CUARTO DE BOMBAS DE ROCIADORES	36.62	ÁREA TÉCNICA

06_TABLA DE ÁREAS (NIVEL SÓTANO_NAVE CENTRAL)

CÓDIGO	NOMBRE	ÁREA (m²)	DEPARTAMENTO
T-17	TANQUE DE RECUPERACIÓN DE AGUAS LLUVIAS	17.70	ÁREA TÉCNICA
T-18	CUARTO DE BOMBAS DE RECUPERACIÓN DE AGUAS LLUVIAS Y EQUIPO DE FILTRACIÓN	59.52	ÁREA TÉCNICA
T-19-1	TANQUE DE AGUA TRATADA	18.00	ÁREA TÉCNICA
T-19-2	TANQUE DE AGUA TRATADA	18.00	ÁREA TÉCNICA
T-20-L	MEDIDORES (LUZ)	6.30	ÁREA TÉCNICA
T-20-W	MEDIDORES (AGUA)	5.22	ÁREA TÉCNICA
T-25	NODO DE ACCESO DE TELECOMUNICACIONES	10.47	ÁREA TÉCNICA
T-25	NODO DE ACCESO DE TELECOMUNICACIONES	4.41	ÁREA TÉCNICA
T-28	CUARTO DE MAQUINAS DE ESTACIÓN DE BOMBEO	49.84	ÁREA TÉCNICA
TOTAL NIVEL SÓTANO		1434.70	

05_TABLA DE ÁREAS POR DEPARTAMENTO (NIVEL SÓTANO)

DEPARTAMENTO	ÁREA (m²)
ÁREA NO PAGA	0.00
ÁREA PÚBLICA	978.21
ÁREA TÉCNICA	456.49
TOTAL NIVEL	1434.70

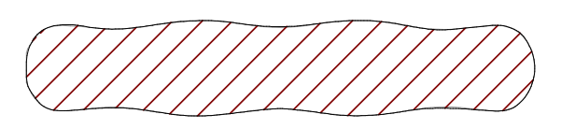

PLANO CLAVE ESTACIÓN 08

LOCALIZACIÓN

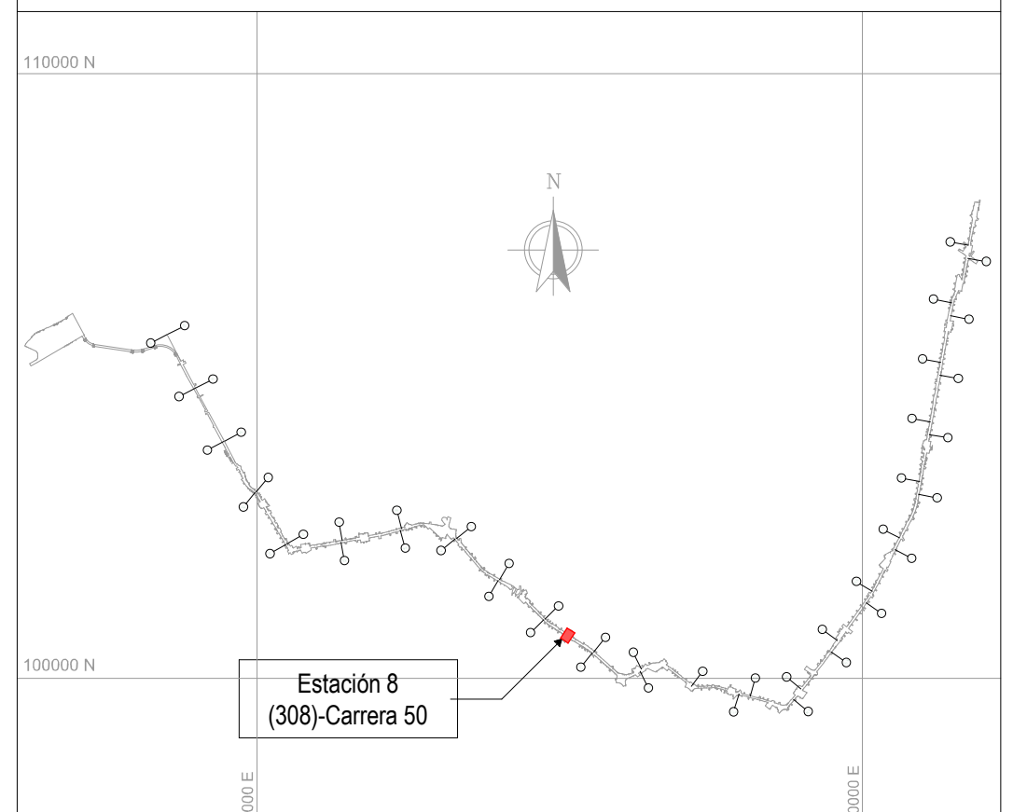

NOTAS

01 TODAS LAS DIMENSIONES ESTÁN CONFIGURADAS EN METROS A MENOS QUE SE INDIQUE UNA UNIDAD DE MEDIDA DIFERENTE.

02 TODAS LAS MEDIDAS, UBICACIÓN Y NIVELES DEBEN VERIFICARSE EN EL LUGAR DE CONSTRUCCIÓN.

03 EL NIVEL DE ACCESO AL EDIFICIO PL 01 CORRESPONDE AL +0,00 DE LA ESTACIÓN Y REFERENCIA AL NIVEL 2555.56 M.S.N.M

04 LOS NOMBRES ESPECIFICOS DE LAS ÁREAS PUEDEN SER CONSULTADAS EN EL PLANO NO. 3 O EN LAS VISTAS EN PLANTA.

05 LOS COLORES QUE SE MUESTRAN EN LOS PLANOS COMO PROYECCIÓN DE ELEMENTOS ARQUITECTÓNICOS COMO CUBIERTAS FACHADAS MUROS ETC. NO REPRESENTAN LA MATERIALIDAD Y REALIDAD DE ACABADOS DEL PROYECTO, SOLO SON INDICATIVOS PARA REALIZAR UNA CORRECTA LECTURA DE LA PLANIMETRÍA.

06 EN LOS NIVELES DE ACCESO COMPRENDIDOS DESDE PL_00.1 A PL_01 SE DEBEN REVISAR LOS NIVELES ESTRUCTURALES CON LA PLANIMETRIA CORRESPONDIENTE A LAS PLACAS ESTRUCTURALES QUE SE ENCUENTRA EN LOS ENTREGABLES L1T1-0000-30X-CON-ED-STR-PL-0000 AL L1T1-0000-30X-CON-ED-STR-PL-0000. EN LOS NIVELES PL_02 (INTERMEDIO) Y PL_03 (PLATAFORMA), EL NIVEL ESTRUCTURAL (NE) SE ENCUENTRA A (- 0.10m) POR DEBAJO DE LOS NIVELES DE PISO TERMINADO (NPT) MARCADOS EN LA PLANIMETRÍA. A EXCEPCIÓN DE LOS NIVELES ESPECIFICADOS PARA LOCALES COMERCIALES, LOS CUALES SE UBICAN SOBRE PLACAS ESTRUCTURALES REFERENCIADOS COMO NIVEL ESTRUCTURAL (NE) Y ES RESPONSABILIDAD DEL LOCATARIO DEFINIR Y COLOCAR EL ACABADO DE PISO PARA EMPATAR CON EL NIVEL DE PISO TERMINADO (NPT) DEL ESPACIO INMEDIATO A SU ACCESO.

- ARC_PL_00 = SÓTANO	/ NPT -6.25
- ARC_PL_01 = ACCESO	/ NPT 0.00
- ARC_PL_02 = INTERMEDIO	/ NPT 7.60
- ARC_PL_02.1 = PLACA INFERIOR VIGA CAJÓN	/ NPT 13.82
- ARC_PL_02.2 = TOPE DE RIEL (TOR)	/ NPT 15.95
- ARC_PL_03 = PLATAFORMA	/ NPT 17.09
- ARC_PL_05 = CUBIERTA NAVE CENTRAL	/ NPT 26.42

CONVENCIONES

- ■ CADE
- ■ COMERCIAL ÁREA NO PAGA
- ■ COMERCIAL ÁREA PAGA
- ■ MUSEO
- ■ SERVICIO PÚBLICO
- ■ ZONA DE REFUGIO
- ■ ÁREA CULTURAL
- ■ ÁREA DE TAQUILLAS BRT
- ■ ÁREA JARDÍN
- ■ ÁREA NO PAGA
- ■ ÁREA OPERACIONAL
- ■ ÁREA PAGA
- ■ ÁREA PÚBLICA
- ■ ÁREA TÉCNICA

VDD CAMBIOS EFECTUADOS:
CAMBIO DE LAYOUT

No.	PLANOS DE REFERENCIA	REV.

No.	MODELO BIM DE REFERENCIA	REV.
1	L1T1-1100-208-CON-ED-EST-MO-0001.rvt	VCC
2	L1T1-1100-209-CON-ED-EST-MO-0001.rvt	VCC
3	L1T1-1100-308-CON-ED-EST-MO-0001.rvt	VCC
4	L1T1-1150-208-CON-ED-EST-MO-0001.rvt	VCC
5	L1T1-1150-209-CON-ED-EST-MO-0001.rvt	VCC
6	L1T1-1150-308-CON-ED-EST-MO-0001.rvt	VCC
7	L1T1-1410-308-CON-ED-MEC-MO-0001.rvt	VCC
8	L1T1-1420-308-CON-ED-MEC-MO-0001.rvt	VCC
9	L1T1-2420-561-CON-ED-MEC-MO-0001.rvt	VCC

No.	PAQUETE DE TRABAJO DE REFERENCIA	REV.
1	XREF-URBANISM_CONTEXT_ST08.rvt	

METRO BOGOTÁ
GCS Consorcio Consultores PMO Bogotá
CONSORCIO SUPERVISOR PLMB
wsp

DISEÑÓ:
ALBERTO ARANDA
Mat.: A25071999-79785641

APROBÓ:
MÓNICA F. BEDOYA M.
Mat.: 25202-75140 CND

REVISÓ:
JAIRO ESPEJO M.
Mat.:25202-20801 CND

DIBUJÓ:
EQUIPO WSP

REVISIÓN No.	FECHA	DESCRIPCIÓN	REVISÓ	APROBÓ	APROBACIÓN CLIENTE
VDD	17/07/2023	EMITIDO PARA REVISIÓN Y COMENTARIOS DEL CLIENTE E INTERVENTORÍA - INCLUYE COMENTARIOS /(AJUSTES)	J.E.M	M.B.M	
VCC	20/06/2022	EMITIDO PARA REVISIÓN Y COMENTARIOS DEL CLIENTE E INTERVENTORÍA - INCLUYE COMENTARIOS /(ENTREGA 90%)	J.E.M	M.B.M	
VBB	06/12/2021	EMITIDO PARA REVISIÓN Y COMENTARIOS DEL CLIENTE E INTERVENTORÍA	J.E.M	M.B.M	
VA0	30/06/2021	EMITIDO PARA COMENTARIOS INTERNOS - EMISIÓN PRELIMINAR PARA COMENTARIOS	J.E.M	M.B.M	

METRO LÍNEA 1

METRO LÍNEA 1
CONTRATO DE CONCESIÓN No. 163 DE 2019

PROYECTO PRIMERA LÍNEA DEL METRO DE BOGOTÁ - TRAMO 1

DIRECTOR DE INTERVENTORÍA:
JAVIER DESCARGA N.
Mat.:2520268697 CND

ESPECIALISTA INTERVENTORÍA:
MARIA AUXILIADORA SANCHEZ H.
INT: PAH138382-RES.No.34 DE 2021

FECHA:
JULIO 2023

INFRAESTRUCTURA VIAL

ARQUITECTURA

ESTACIÓN 08 - CARRERA 50
NAVE CENTRAL
VISTA EN PLANTA - NIVEL SÓTANO 01

PLANCHA No: L1T1-0000-308-CON-ED-ARQ-PL-0001_04_VDD
ARCHIVO: L1T1-0000-308-CON-ED-ARQ-MO-0001_VCC.rvt
ESCALA: INDICADA
FECHA: JUNIO 2021
REVISIÓN No. VDD
PLANO No. 04 DE 32