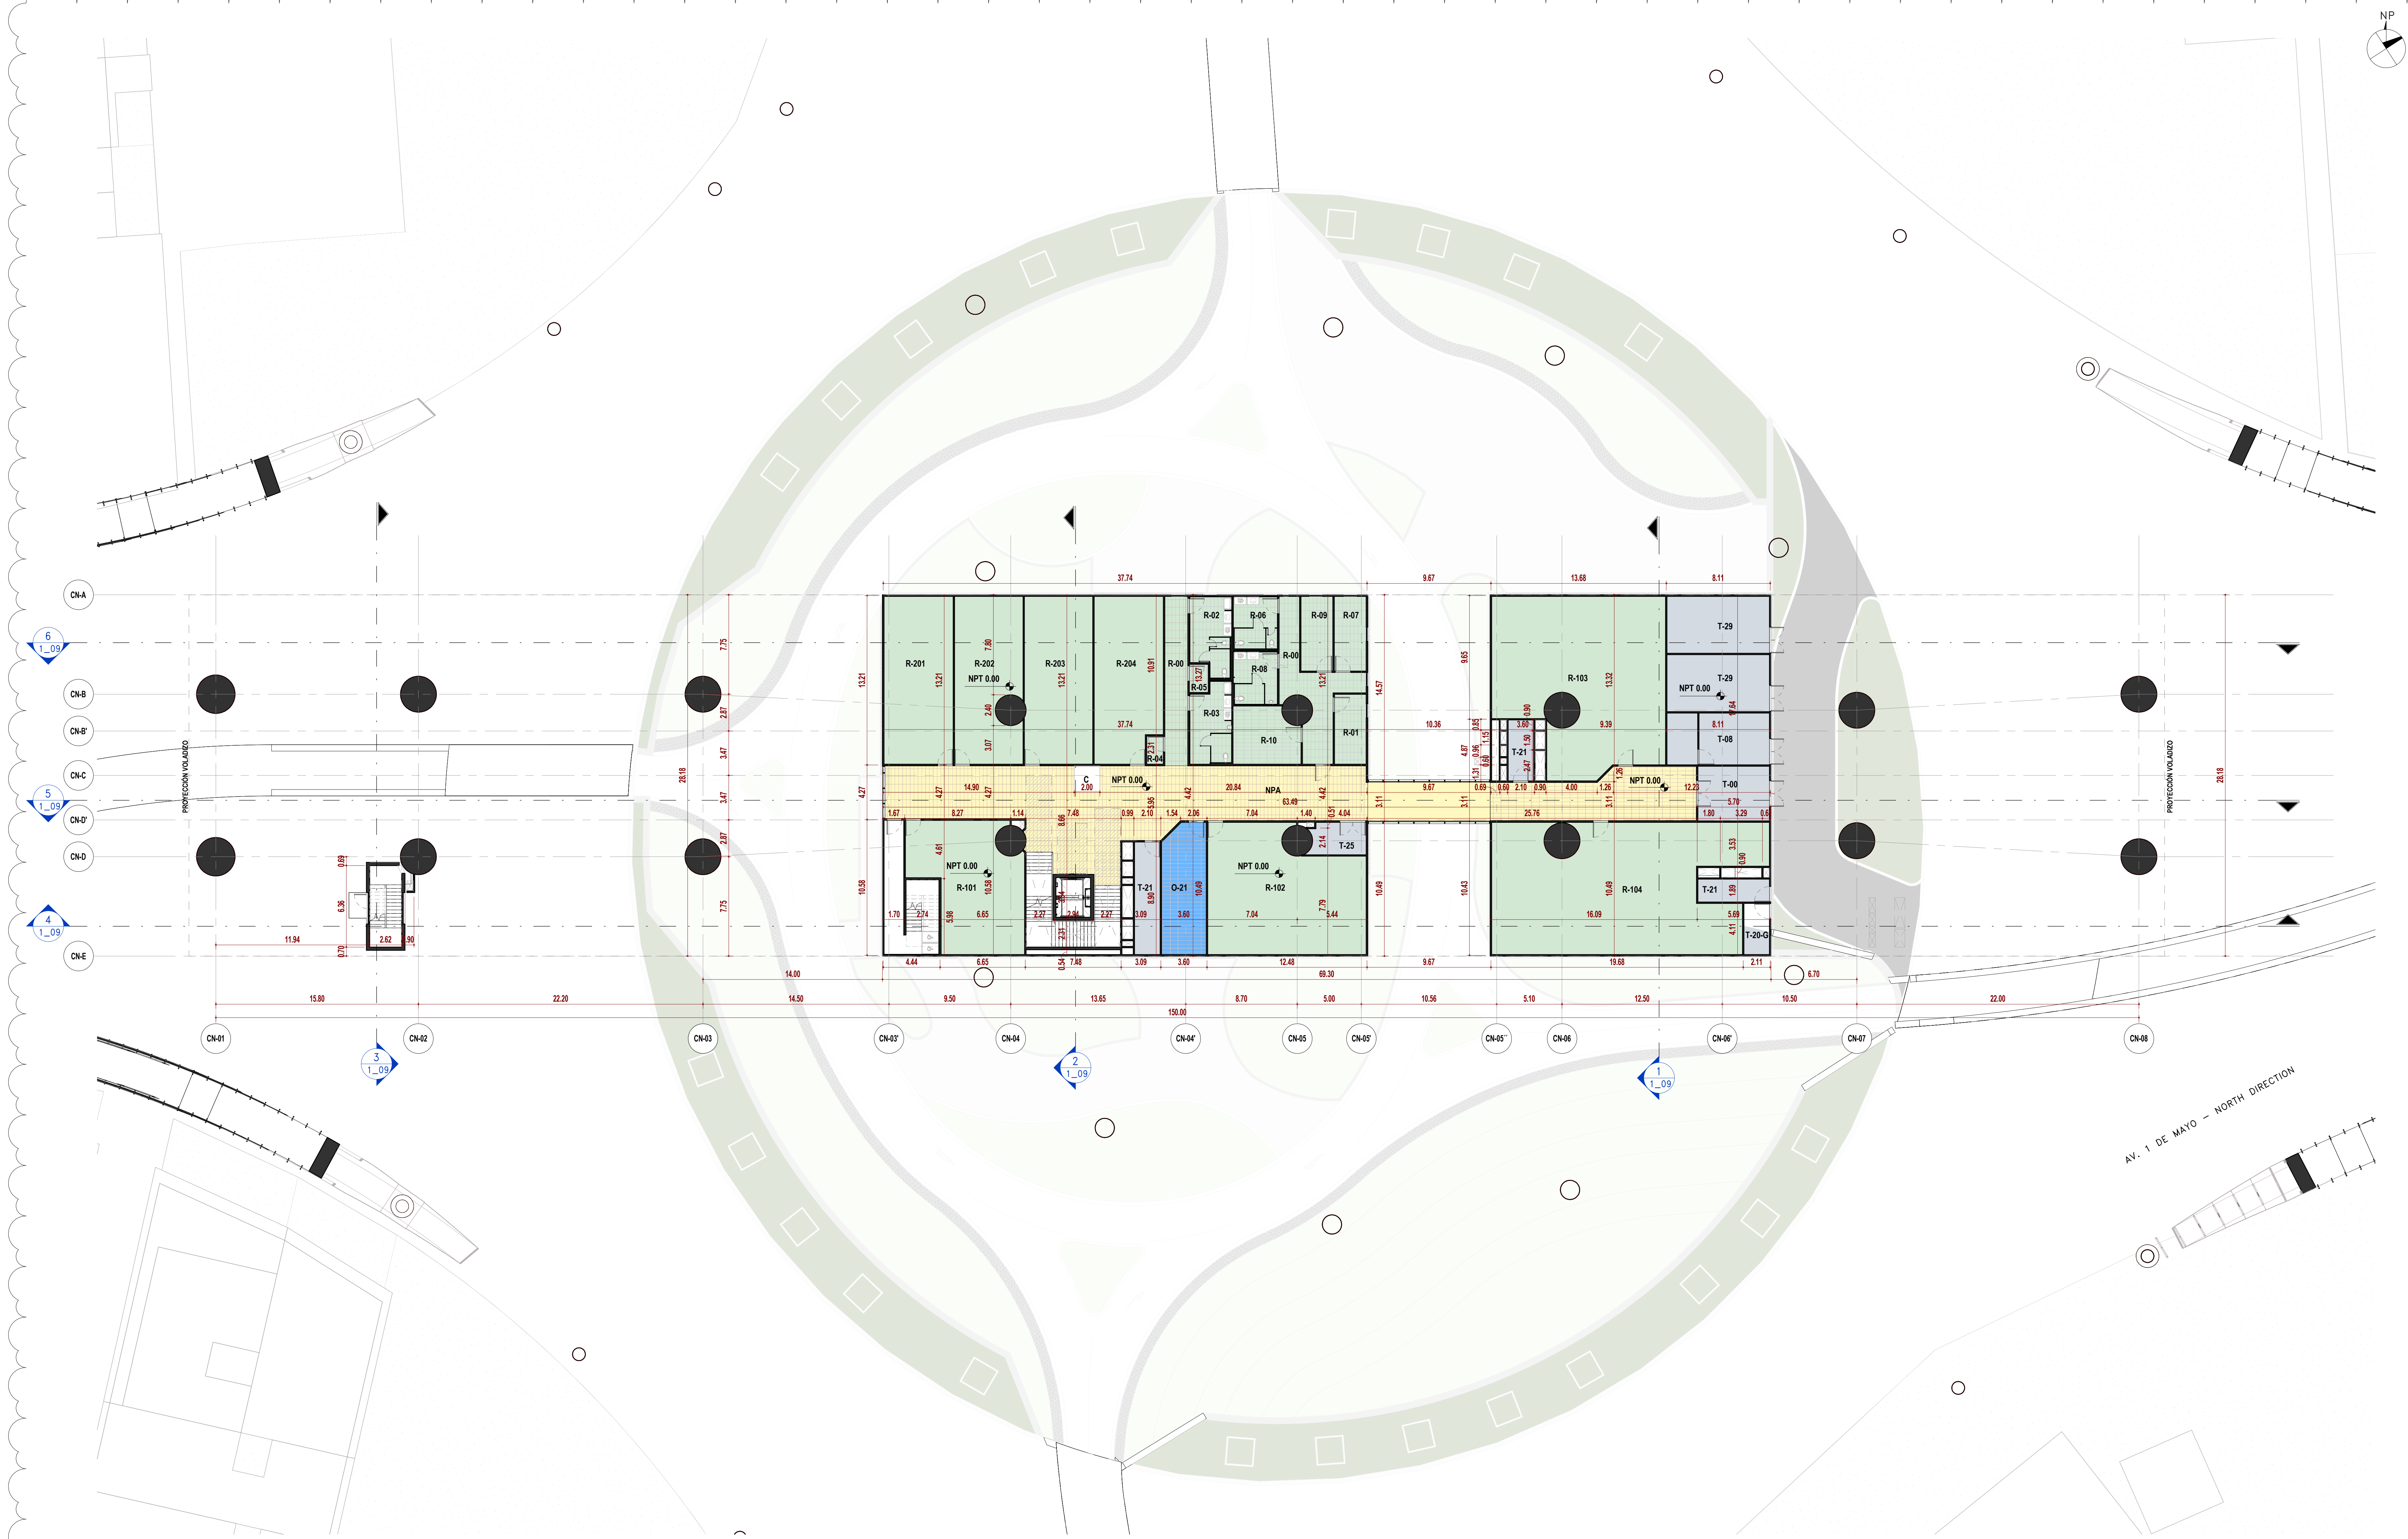

2 NIVEL ACCESO_NAVE CENTRAL
ESC: 1 : 200

VDD

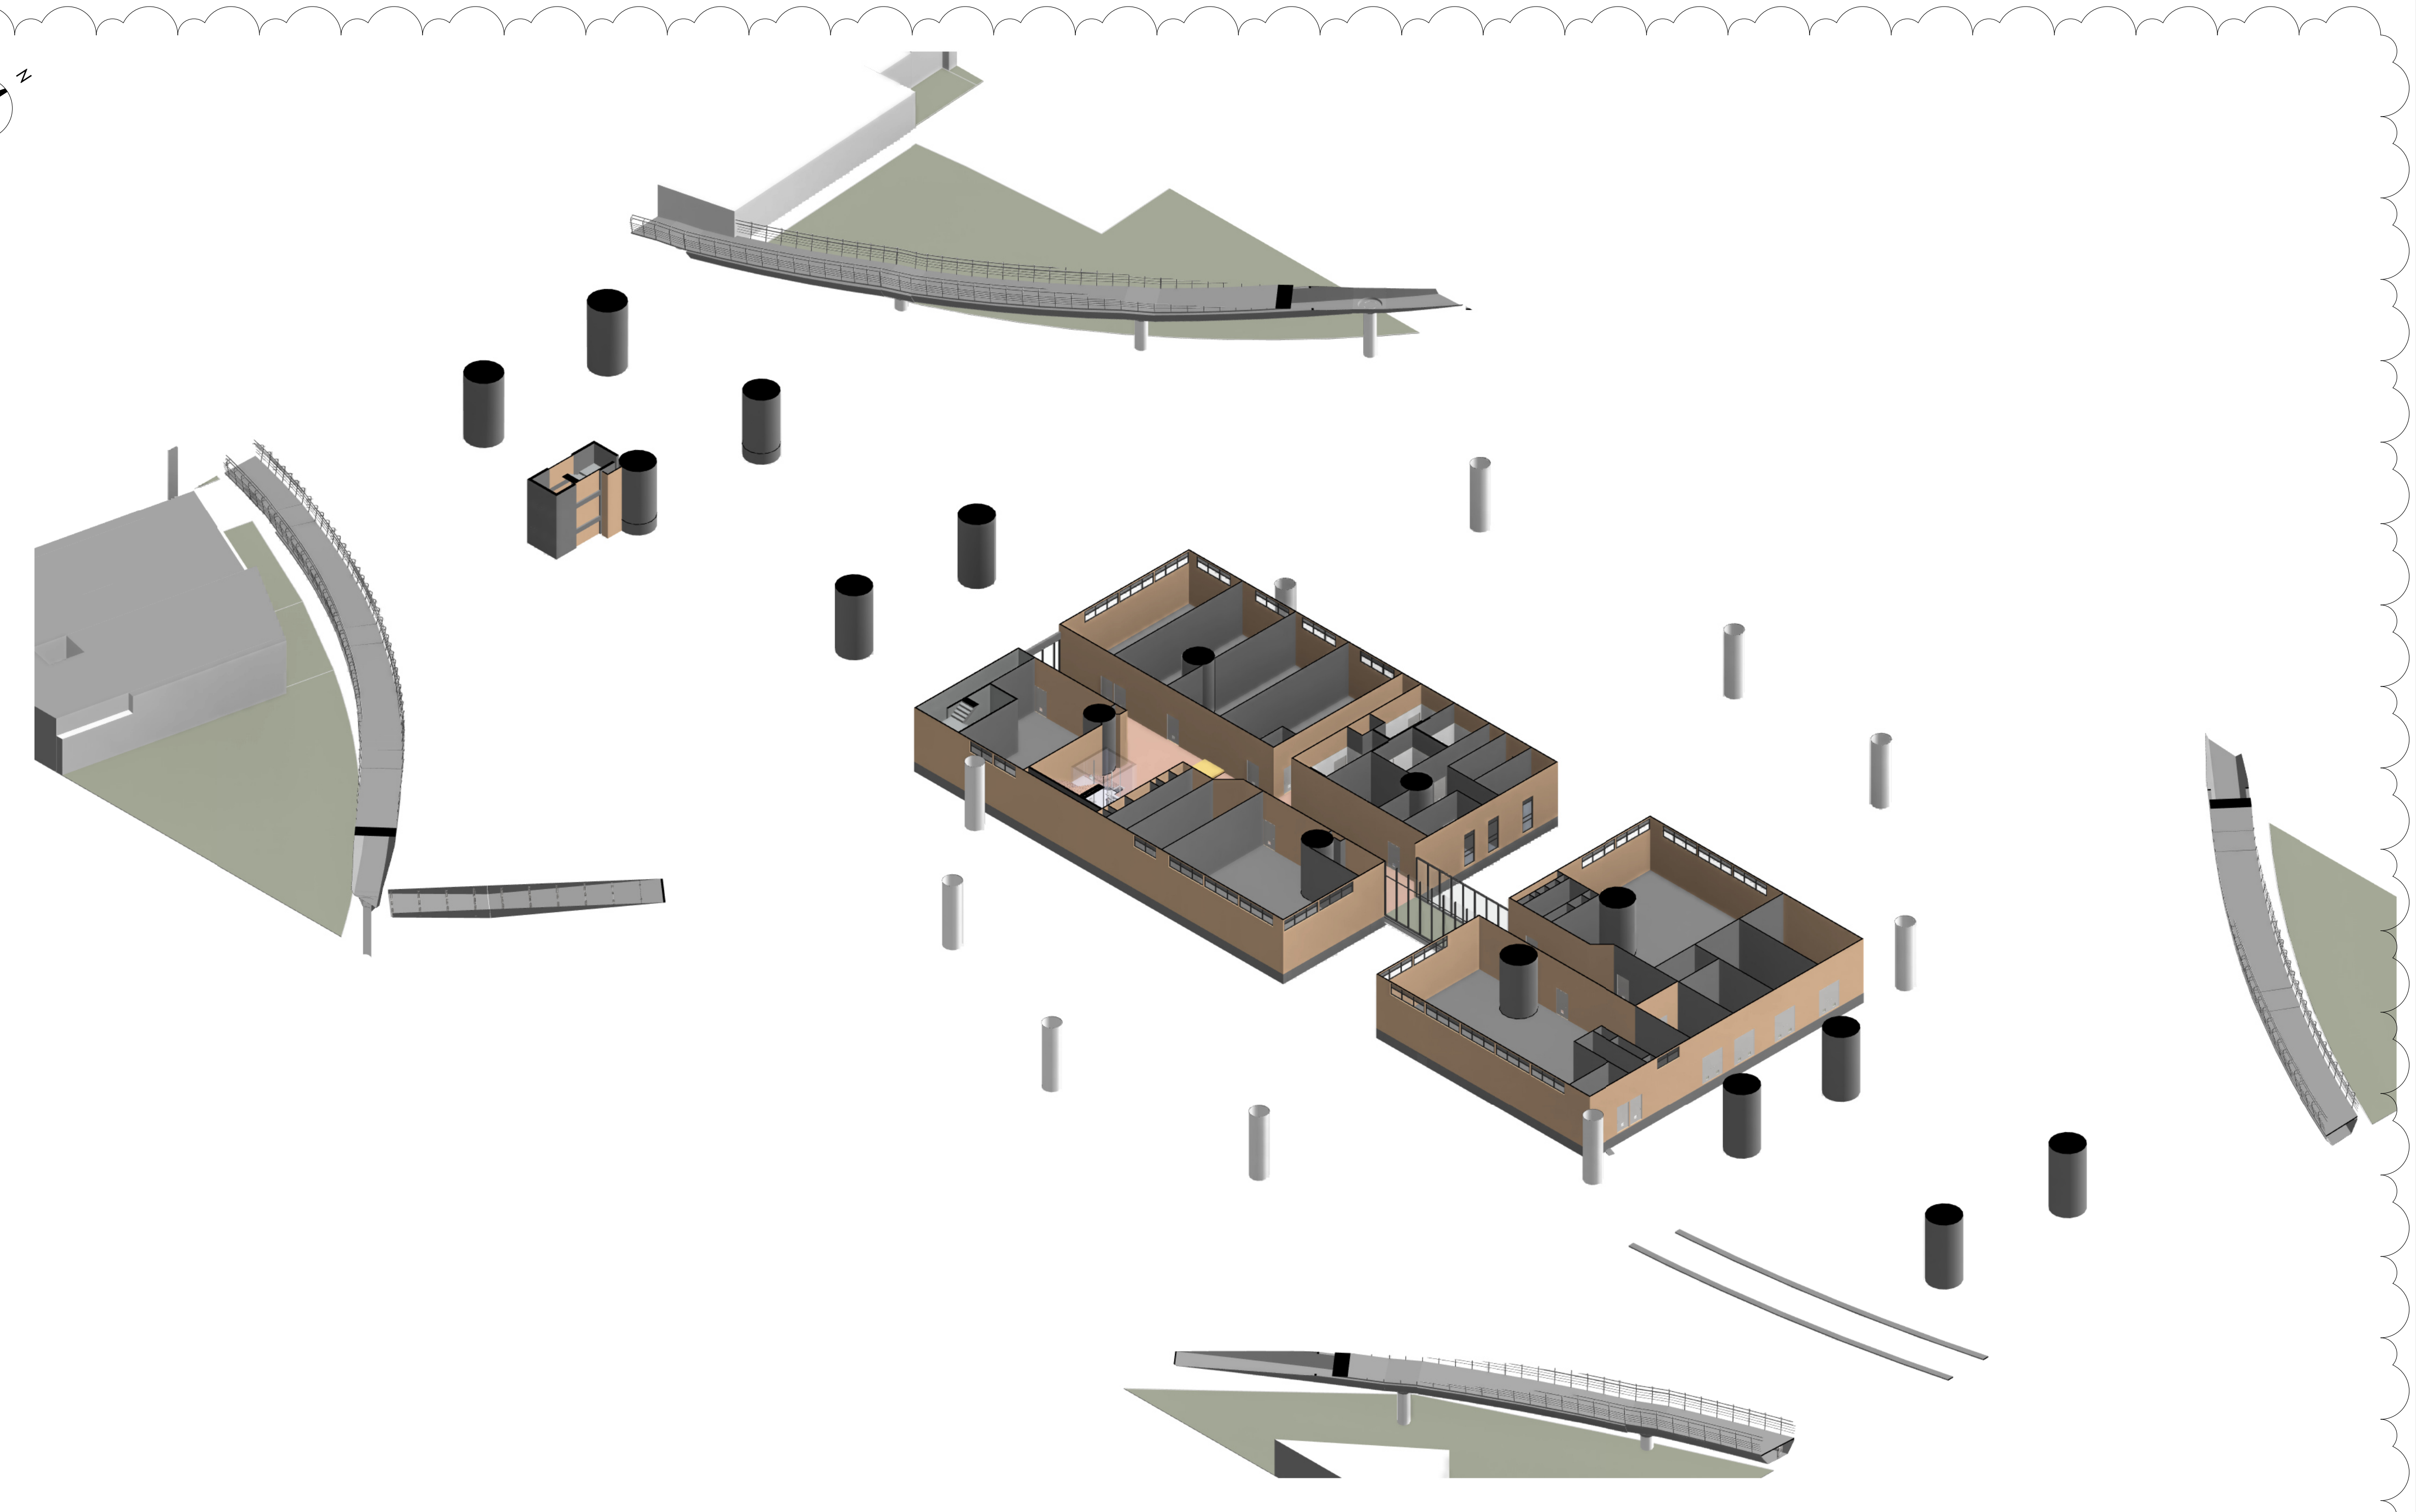

1 3D_NIVEL ACCESO_NAVE CENTRAL
ESC: N/A

08_TABLA DE ÁREAS (ACCESO)

CÓDIGO	NOMBRE	ÁREA (m²)	DEPARTAMENTO	FILTER
ARC_PL_01				
C	ÁREAS DE USO CULTURAL	4.00	ÁREA CULTURAL	ACCESS
NPA	ÁREA NO PAGA	278.65	ÁREA NO PAGA	ACCESS
O-21	ALMACENAMIENTO DE LA ESTACIÓN	34.94	ÁREA OPERATIVA	ACCESS
R-00	COMERCIO - CORREDOR OPERATIVA	23.79	COMERCIO - ÁREA NO PAGA	ACCESS
R-00	COMERCIO - CORREDOR OPERATIVA	33.16	COMERCIO - ÁREA NO PAGA	ACCESS
R-01	COMERCIO - ALMACENAMIENTO DE BASURAS	13.58	COMERCIO - ÁREA NO PAGA	ACCESS
R-02	COMERCIO - BAÑO PÚBLICO - MUJERES	18.33	COMERCIO - ÁREA NO PAGA	ACCESS
R-03	COMERCIO - BAÑO PÚBLICO - HOMBRES	19.12	COMERCIO - ÁREA NO PAGA	ACCESS
R-04	COMERCIO - CONTROL DE ACCESO BAÑOS PÚBLICOS	2.86	COMERCIO - ÁREA NO PAGA	ACCESS
R-05	COMERCIO - CUARTO DE LIMPIEZA	3.26	COMERCIO - ÁREA NO PAGA	ACCESS
R-06	COMERCIO - BAÑOS EMPLEADOS - MUJERES	13.78	COMERCIO - ÁREA NO PAGA	ACCESS
R-07	COMERCIO - VESTIDORES EMPLEADOS - MUJERES	14.59	COMERCIO - ÁREA NO PAGA	ACCESS
R-08	COMERCIO - BAÑOS EMPLEADOS - HOMBRES	13.93	COMERCIO - ÁREA NO PAGA	ACCESS
R-09	COMERCIO - VESTIDORES EMPLEADOS - HOMBRES	14.59	COMERCIO - ÁREA NO PAGA	ACCESS
R-10	COMERCIO - SALA DE REPOSO DE EMPLEADOS	22.20	COMERCIO - ÁREA NO PAGA	ACCESS
R-101	COMERCIO - ÁREA COMERCIAL	75.57	COMERCIO - ÁREA NO PAGA	ACCESS
R-102	COMERCIO - ÁREA COMERCIAL	111.24	COMERCIO - ÁREA NO PAGA	ACCESS
R-103	COMERCIO - ÁREA COMERCIAL	162.48	COMERCIO - ÁREA NO PAGA	ACCESS
R-104	COMERCIO - ÁREA COMERCIAL	192.00	COMERCIO - ÁREA NO PAGA	ACCESS
R-201	COMERCIO - LOCAL DE COMIDAS	70.74	COMERCIO - ÁREA NO PAGA	ACCESS
R-202	COMERCIO - LOCAL DE COMIDAS	65.79	COMERCIO - ÁREA NO PAGA	ACCESS
R-203	COMERCIO - LOCAL DE COMIDAS	69.85	COMERCIO - ÁREA NO PAGA	ACCESS
R-204	COMERCIO - LOCAL DE COMIDAS	67.52	COMERCIO - ÁREA NO PAGA	ACCESS
T-00	CIRCULACIÓN TÉCNICA	23.90	ÁREA TÉCNICA	ACCESS
T-08	CENTRO DE TRANSFORMACIÓN ENEL-CODENSA (CT)	32.40	ÁREA TÉCNICA	ACCESS
T-20-G	MEDIDORES (GAS)	3.49	ÁREA TÉCNICA	ACCESS
T-21	ÁREA DE INSPECCIÓN	17.57	ÁREA TÉCNICA	ACCESS
T-21	ÁREA DE INSPECCIÓN	10.00	ÁREA TÉCNICA	ACCESS
T-21	ÁREA DE INSPECCIÓN	9.52	ÁREA TÉCNICA	ACCESS
T-25	NODO DE ACCESO DE TELECOMUNICACIONES	10.84	ÁREA TÉCNICA	ACCESS
T-29	SUBESTACIÓN ELÉCTRICA ESTACIÓN DE BOMBEO	35.60	ÁREA TÉCNICA	ACCESS
T-29	SUBESTACIÓN ELÉCTRICA ESTACIÓN DE BOMBEO	35.60	ÁREA TÉCNICA	ACCESS
TOTAL NIVEL		1504.88		

09_TABLA DE ÁREAS POR DEPARTAMENTO (ACCESO)

DEPARTAMENTO	ÁREA (m²)
ARC_PL_01	
COMERCIO - ÁREA NO PAGA	1008.36
ÁREA CULTURAL	4.00
ÁREA NO PAGA	278.65
ÁREA OPERATIVA	34.94
ÁREA TÉCNICA	178.92
TOTAL NIVEL	1504.88

PLANO CLAVE ESTACIÓN 08

LOCALIZACIÓN

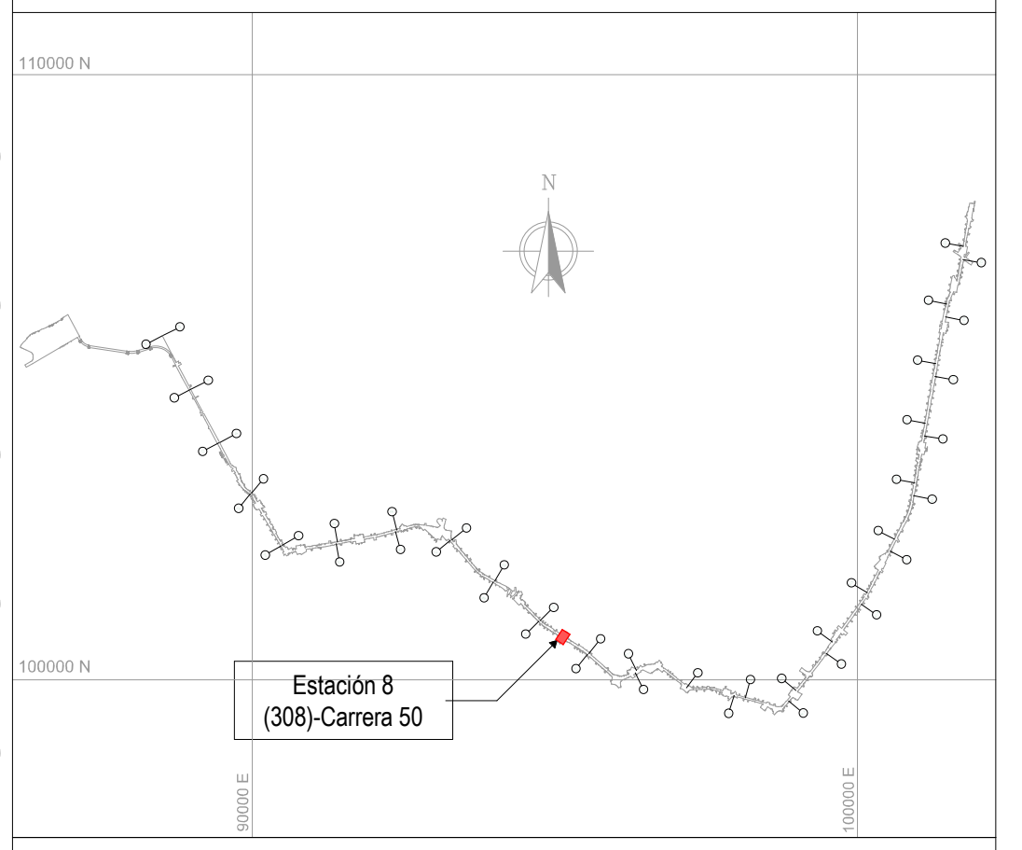

NOTAS

01 TODAS LAS DIMENSIONES ESTÁN CONFIGURADAS EN METROS A MENOS QUE SE INDIQUE UNA UNIDAD DE MEDIDA DIFERENTE.

02 TODAS LAS MEDIDAS, UBICACIÓN Y NIVELES DEBEN VERIFICARSE EN EL LUGAR DE CONSTRUCCIÓN.

03 EL NIVEL DE ACCESO AL EDIFICIO PL 01 CORRESPONDE AL +0,00 DE LA ESTACIÓN Y REFERENCIA AL NIVEL 2555.56 M.S.N.M

04 LOS NOMBRES ESPECIFICOS DE LAS ÁREAS PUEDEN SER CONSULTADAS EN EL PLANO NO. 3 O EN LAS VISTAS EN PLANTA.

05 LOS COLORES QUE SE MUESTRAN EN LOS PLANOS COMO PROYECCIÓN DE ELEMENTOS ARQUITECTÓNICOS COMO CUBIERTAS FACHADAS MUROS ETC. NO REPRESENTAN LA MATERIALIDAD Y REALIDAD DE ACABADOS DEL PROYECTO, SOLO SON INDICATIVOS PARA REALIZAR UNA CORRECTA LECTURA DE LA PLANIMETRÍA.

06 EN LOS NIVELES DE ACCESO COMPRENDIDOS DESDE PL_00.1 A PL_01 SE DEBEN REVISAR LOS NIVELES ESTRUCTURALES CON LA PLANIMETRIA CORRESPONDIENTE A LAS PLACAS ESTRUCTURALES QUE SE ENCUENTRA EN LOS ENTREGABLES L1T1-0000-30X-CON-ED-STR-PL-0000 AL L1T1-0000-30X-CON-ED-STR-PL-0000. EN LOS NIVELES PL_02 (INTERMEDIO) Y PL_03 (PLATAFORMA), EL NIVEL ESTRUCTURAL (NE) SE ENCUENTRA A (- 0.10m) POR DEBAJO DE LOS NIVELES DE PISO TERMINADO (NPT) MARCADOS EN LA PLANIMETRÍA. A EXCEPCIÓN DE LOS NIVELES ESPECIFICADOS PARA LOCALES COMERCIALES, LOS CUALES SE UBICAN SOBRE PLACAS ESTRUCTURALES REFERENCIADOS COMO NIVEL ESTRUCTURAL (NE) Y ES RESPONSABILIDAD DEL LOCATARIO DEFINIR Y COLOCAR EL ACABADO DE PISO PARA EMPATAR CON EL NIVEL DE PISO TERMINADO (NPT) DEL ESPACIO INMEDIATO A SU ACCESO.

- ARC_PL_00 = SÓTANO	/ NPT -6.25
- ARC_PL_01 = ACCESO	/ NPT 0.00
- ARC_PL_02 = INTERMEDIO	/ NPT 7.60
- ARC_PL_02.1 = PLACA INFERIOR VIGA CAJÓN	/ NPT 13.82
- ARC_PL_02.2 = TOPE DE RIEL (TOR)	/ NPT 15.95
- ARC_PL_03 = PLATAFORMA	/ NPT 17.09
- ARC_PL_05 = CUBIERTA NAVE CENTRAL	/ NPT 26.42

CONVENCIONES

▭	CADE
▭	COMERCIAL ÁREA NO PAGA
🟩	COMERCIAL ÁREA PAGA
▭	MUSEO
▭	SERVICIO PÚBLICO
🟦	ZONA DE REFUGIO
🟥	ÁREA CULTURAL
🟪	ÁREA DE TAQUILLAS BRT
🟩	ÁREA JARDÍN
🟨	ÁREA NO PAGA
🟦	ÁREA OPERACIONAL
🟧	ÁREA PAGA
🟦	ÁREA PÚBLICA
▭	ÁREA TÉCNICA

VDD CAMBIOS EFECTUADOS:
CAMBIO DE LAYOUT

No.	PLANOS DE REFERENCIA	REV.

No.	MODELO BIM DE REFERENCIA	REV.
1	L1T1-1100-208-CON-ED-EST-MO-0001.rvt	VCC
2	L1T1-1100-209-CON-ED-EST-MO-0001.rvt	VCC
3	L1T1-1100-308-CON-ED-EST-MO-0001.rvt	VCC
4	L1T1-1150-208-CON-ED-EST-MO-0001.rvt	VCC
5	L1T1-1150-209-CON-ED-EST-MO-0001.rvt	VCC
6	L1T1-1150-308-CON-ED-EST-MO-0001.rvt	VCC
7	L1T1-1410-308-CON-ED-MEC-MO-0001.rvt	VCC
8	L1T1-1420-308-CON-ED-MEC-MO-0001.rvt	VCC
9	L1T1-2420-561-CON-ED-MEC-MO-0001.rvt	VCC

No.	PAQUETE DE TRABAJO DE REFERENCIA	REV.
1	XREF-URBANISM_CONTEXT_ST08.rvt	

0 2 10m
1:200

METRO BOGOTÁ
GCS Consorcio Consultores PMO Bogotá
CONSORCIO SUPERVISOR PLMB
wsp

DISEÑÓ:
ALBERTO ARANDA
Mat.: A25071999-79785641

APROBÓ:
MÓNICA F. BEDOYA M.
Mat.: 25202-75140 CND

REVISÓ:
JAIRO ESPEJO M.
Mat.:25202-20801 CND

DIBUJÓ:
EQUIPO WSP

REVISIÓN No.	FECHA	DESCRIPCIÓN	REVISÓ	APROBÓ	APROBACIÓN CLIENTE
VDD	17/07/2023	EMITIDO PARA REVISIÓN Y COMENTARIOS DEL CLIENTE E INTERVENTORÍA - INCLUYE COMENTARIOS /(AJUSTES)	J.E.M	M.B.M	
VCC	20/06/2022	EMITIDO PARA REVISIÓN Y COMENTARIOS DEL CLIENTE E INTERVENTORÍA - INCLUYE COMENTARIOS /(ENTREGA 90%)	J.E.M	M.B.M	
VBB	06/12/2021	EMITIDO PARA REVISIÓN Y COMENTARIOS DEL CLIENTE E INTERVENTORÍA	J.E.M	M.B.M	
VA0	30/06/2021	EMITIDO PARA COMENTARIOS INTERNOS - EMISIÓN PRELIMINAR PARA COMENTARIOS	J.E.M	M.B.M	

METRO LÍNEA 1

METRO LÍNEA 1
CONTRATO DE CONCESIÓN No. 163 DE 2019

PROYECTO PRIMERA LÍNEA DEL METRO DE BOGOTÁ - TRAMO 1

DIRECTOR DE INTERVENTORÍA:
JAVIER DESCARGA N.
Mat.:2520268697 CND

ESPECIALISTA INTERVENTORÍA:
MARIA AUXILIADORA SANCHEZ H.
INT: PAH138382-RES.No.34 DE 2021

FECHA:
JULIO 2023

INFRAESTRUCTURA VIAL

ARQUITECTURA

ESTACIÓN 08 - CARRERA 50
NAVE CENTRAL
VISTA EN PLANTA - NIVEL DE ACCESO 01

PLANCHA No: L1T1-0000-308-CON-ED-ARQ-PL-0001_05_VDD
ARCHIVO: L1T1-0000-308-CON-ED-ARQ-MO-0001_VCC.rvt
ESCALA: INDICADA
FECHA: JUNIO 2021
REVISIÓN No. VDD
PLANO No. 05 DE 32