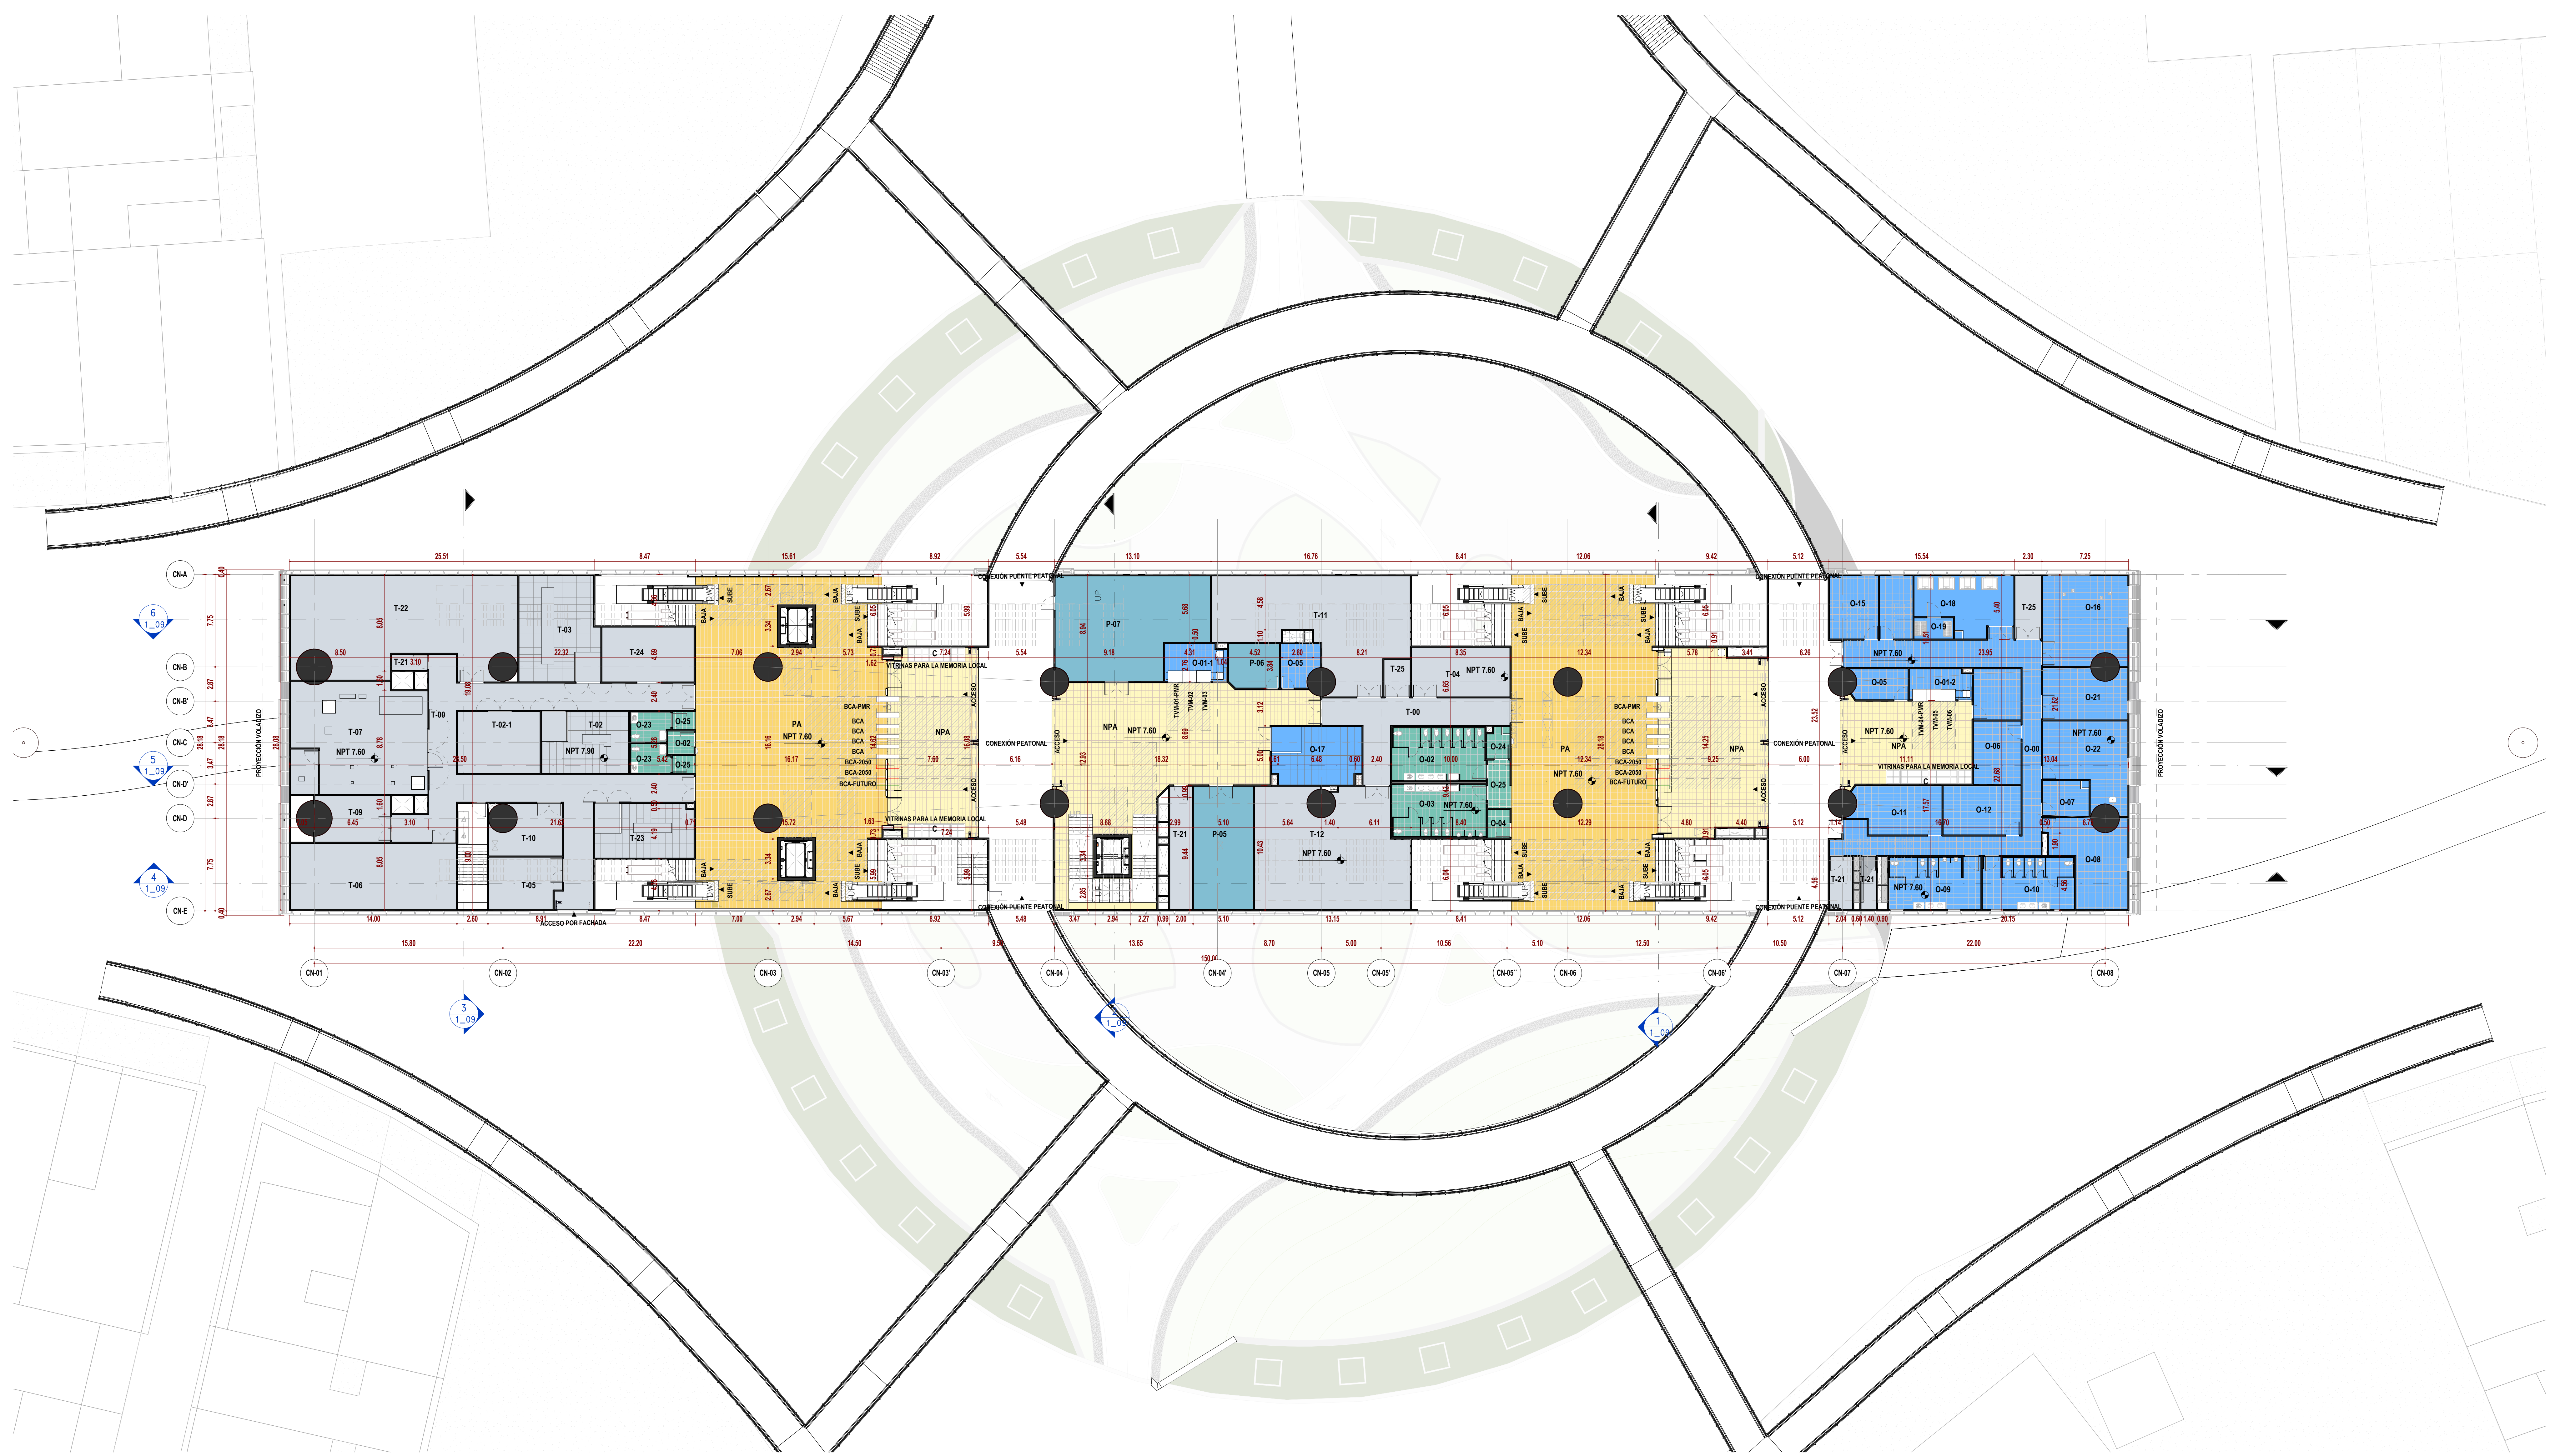

2 **NIVEL INTERMEDIO_NAVE CENTRAL**
ESC: 1 : 200

VDD

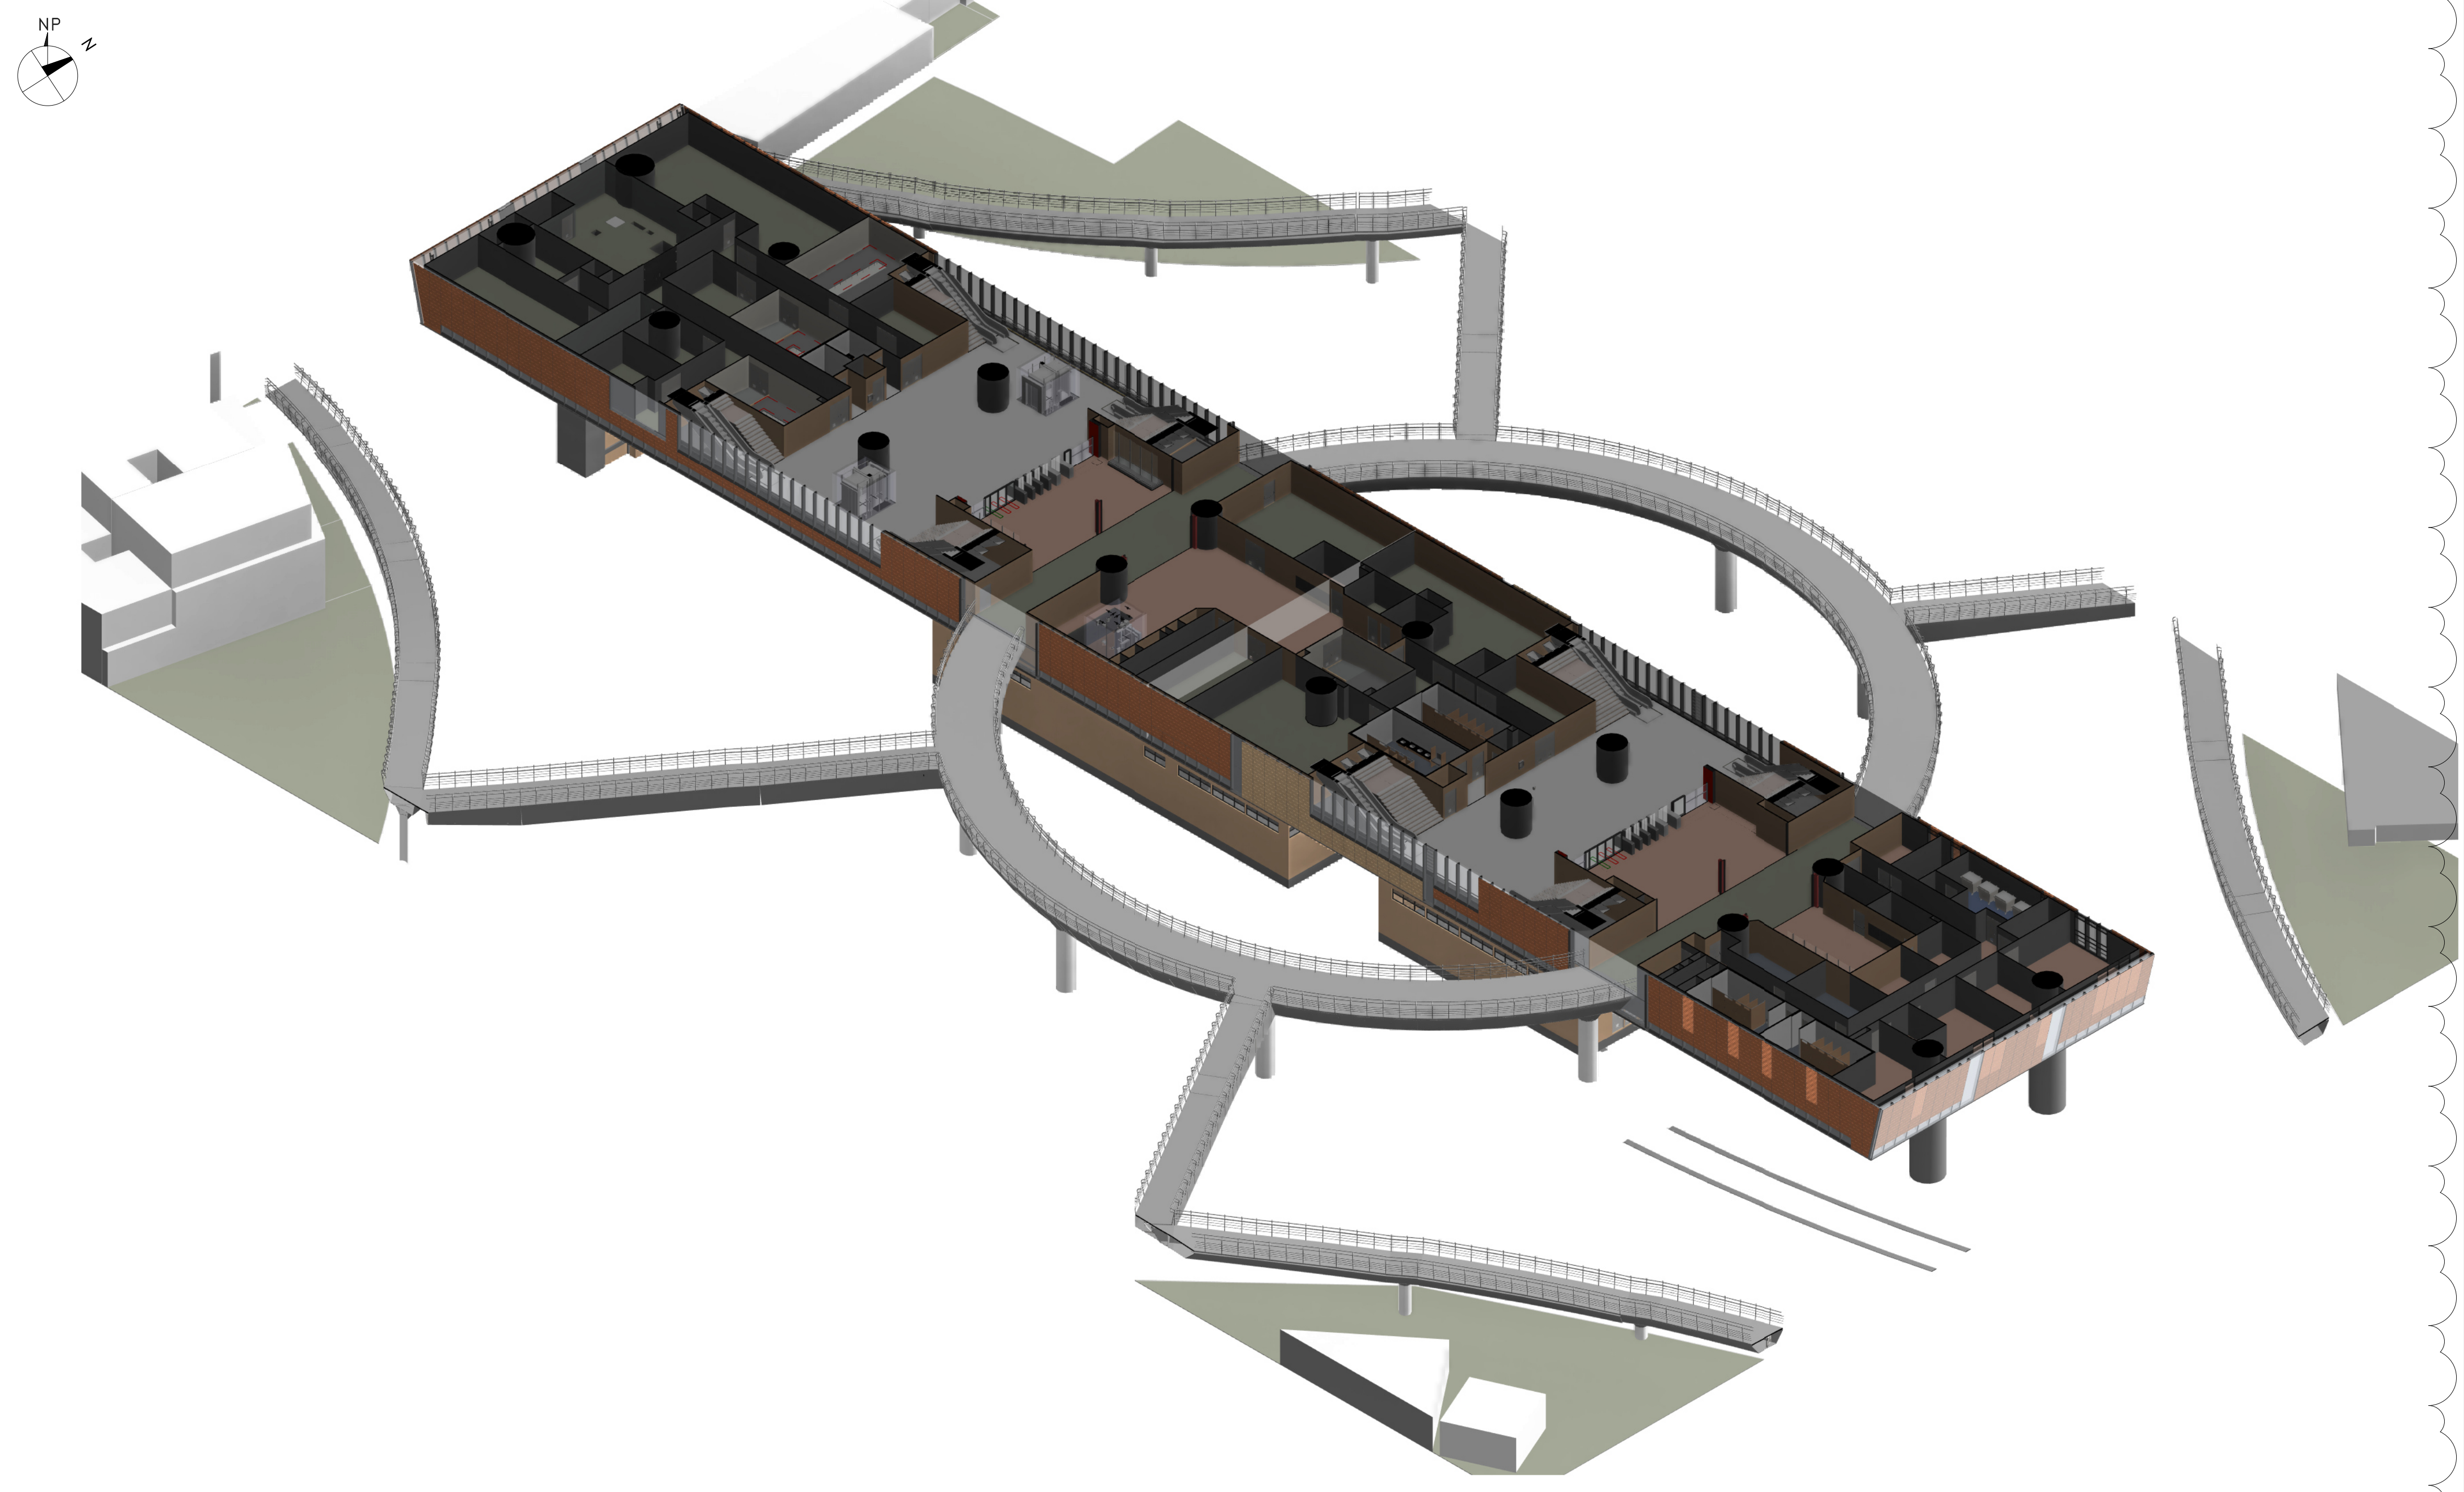

1 **3D_NIVEL INTERMEDIO_NAVE CENTRAL**
ESC: N/A

11_TABLA DE ÁREAS (NIVEL INTERMEDIO_NAVE CENTRAL)

ARC_PL_02

CÓDIGO	NOMBRE	ÁREA (m²)	DEPARTAMENTO
C	ÁREAS DE USO CULTURAL	5.76	ÁREA CULTURAL
C	ÁREAS DE USO CULTURAL	8.66	ÁREA CULTURAL
C	ÁREAS DE USO CULTURAL	5.76	ÁREA CULTURAL
NPA	ÁREA NO PAGA	107.66	ÁREA NO PAGA
NPA	ÁREA NO PAGA	140.14	ÁREA NO PAGA
NPA	ÁREA NO PAGA	241.99	ÁREA NO PAGA
NPA	ÁREA NO PAGA	69.01	ÁREA NO PAGA
O-00	CIRCULACIÓN ÁREAS OPERATIVAS	93.98	ÁREA OPERATIVA
O-01-1	VENTA AUTOMÁTICA DE BOLETOS	16.03	ÁREA OPERATIVA
O-01-2	VENTA AUTOMÁTICA DE BOLETOS	13.35	ÁREA OPERATIVA
O-02	BAÑOS PÚBLICOS - HOMBRES	33.95	SERVICIO PÚBLICO
O-02	BAÑOS PÚBLICOS - HOMBRES	4.32	SERVICIO PÚBLICO
O-03	BAÑOS PÚBLICOS - MUJERES	34.19	SERVICIO PÚBLICO
O-04	CONTROL DE ACCESO BAÑOS PÚBLICOS	4.39	SERVICIO PÚBLICO
O-05	LOCAL DE INFORMACIÓN	10.88	ÁREA OPERATIVA
O-05	LOCAL DE INFORMACIÓN	11.67	ÁREA OPERATIVA
O-06	SUPERVISOR DE LA ESTACIÓN	21.09	ÁREA OPERATIVA
O-07	CUARTO DE LIMPIEZA	11.70	ÁREA OPERATIVA
O-08	SALA DE DESCANSO PARA EMPLEADOS	38.96	ÁREA OPERATIVA
O-09	BAÑOS EMPLEADOS - HOMBRES	32.84	ÁREA OPERATIVA
O-10	BAÑOS EMPLEADOS - MUJERES	32.92	ÁREA OPERATIVA
O-11	VESTIDORES EMPLEADOS - HOMBRES	28.85	ÁREA OPERATIVA
O-12	VESTIDORES EMPLEADOS - MUJERES	26.98	ÁREA OPERATIVA
O-13	LOCAL DE POLICÍA	17.07	ÁREA OPERATIVA
O-15	LOCAL DE PRIMEROS AUXILIOS	21.66	ÁREA OPERATIVA
O-16	SALA DE REUNIÓN	52.20	ÁREA OPERATIVA
O-17	OPERADORES TELECOMUNICACIONES EXTERIORES	35.31	ÁREA OPERATIVA
O-18	CUARTO DE ALMACENAMIENTO DE BASURAS - RESIDUOS SÓLIDOS	35.40	ÁREA OPERATIVA
O-19	CUARTO DE ALMACENAMIENTO DE BASURAS - RESIDUOS PELIGROSOS	5.82	ÁREA OPERATIVA
O-20	CUARTO DE LACTANCIA	14.84	ÁREA OPERATIVA
O-21	ALMACENAMIENTO DE LA ESTACIÓN	29.18	ÁREA OPERATIVA
O-22	OFICINA DE MANTENIMIENTO	42.83	ÁREA OPERATIVA
O-23	BAÑO PÚBLICO - FAMILIAR	7.90	SERVICIO PÚBLICO
O-23	BAÑO PÚBLICO - FAMILIAR	7.90	SERVICIO PÚBLICO
O-24	CUARTO DE LIMPIEZA DE BAÑOS PÚBLICOS	4.94	SERVICIO PÚBLICO
O-25	BAÑO PÚBLICO - CORREDOR OPERACIONAL	7.64	SERVICIO PÚBLICO
O-25	BAÑO PÚBLICO - CORREDOR OPERACIONAL	2.87	SERVICIO PÚBLICO
O-25	BAÑO PÚBLICO - CORREDOR OPERACIONAL	2.87	SERVICIO PÚBLICO
P-05	BIBLIOMETRO	51.60	ÁREA PÚBLICA
P-06	ESPACIO IPES (INSTITUTO PARA LA ECONOMÍA SOCIAL)	15.72	ÁREA PÚBLICA
P-07	SALÓN MULTIPLE EMB	100.95	ÁREA PÚBLICA
PA	ÁREA PAGA	414.67	ÁREA PAGA
PA	ÁREA PAGA	334.09	ÁREA PAGA
T-00	CIRCULACIÓN TÉCNICA	158.66	ÁREA TÉCNICA
T-00	CIRCULACIÓN TÉCNICA	47.68	ÁREA TÉCNICA
T-02	LOCAL DE CONDUCCIÓN AUTOMÁTICA (CBTC)	37.59	ÁREA TÉCNICA
T-02-1	UPS DEDICADA (CBTC)	35.85	ÁREA TÉCNICA
T-03	TELECOMUNICACIÓN ESTACIÓN - CORRIENTE DÉBIL	58.22	ÁREA TÉCNICA
T-04	EQUIPOS DE BOLETERÍA	34.18	ÁREA TÉCNICA
T-05	ALMACÉN PARA MANTENIMIENTO	25.96	ÁREA TÉCNICA
T-06	SALA DE TABLEROS	77.15	ÁREA TÉCNICA
T-07	CENTRO DE TRANSFORMACIÓN (CT)	106.18	ÁREA TÉCNICA
T-09	ALMACÉN EQUIPO ELÉCTRICO	21.38	ÁREA TÉCNICA
T-10	CUARTO DE EQUIPO ELECTROMECÁNICO	22.36	ÁREA TÉCNICA
T-11	CUARTO DE VENTILACIÓN	114.03	ÁREA TÉCNICA
T-12	PLANTA DE REFRIGERACIÓN PARA LA CLIMATIZACIÓN	122.10	ÁREA TÉCNICA
T-21	ÁREA DE INSPECCIÓN	4.05	ÁREA TÉCNICA
T-21	ÁREA DE INSPECCIÓN	19.61	ÁREA TÉCNICA
T-21	ÁREA DE INSPECCIÓN	8.63	ÁREA TÉCNICA
T-21	ÁREA DE INSPECCIÓN	5.80	ÁREA TÉCNICA
T-22	CUARTO DE UPS	143.32	ÁREA TÉCNICA
T-23	CUARTO PDAP	37.32	ÁREA TÉCNICA
T-24	TETRA UPS	35.37	ÁREA TÉCNICA
T-25	NODO DE ACCESO DE TELECOMUNICACIONES	11.66	ÁREA TÉCNICA
T-25	NODO DE ACCESO DE TELECOMUNICACIONES	6.82	ÁREA TÉCNICA
TOTAL NIVEL		3334.49	

10_TABLA DE ÁREAS POR DEPARTAMENTO (NIVEL INTERMEDIO)

DEPARTAMENTO	ÁREA (m²)
SERVICIO PÚBLICO	110.97
ÁREA CULTURAL	20.18
ÁREA NO PAGA	558.80
ÁREA OPERATIVA	593.58
ÁREA PAGA	748.77
ÁREA PÚBLICA	168.27
ÁREA TÉCNICA	1133.91
TOTAL NIVEL	3334.49

LOCALIZACIÓN

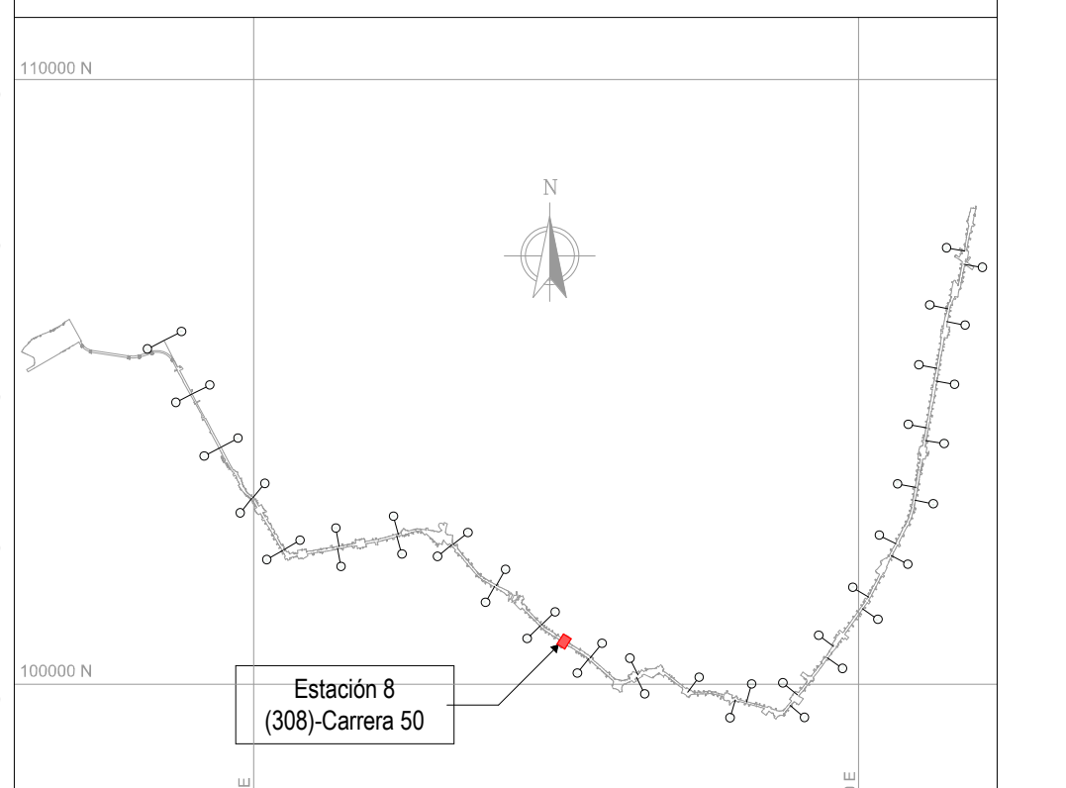

Estación 8
(308)-Carrera 50

NOTAS

01 TODAS LAS DIMENSIONES ESTÁN CONFIGURADAS EN METROS A MENOS QUE SE INDIQUE UNA UNIDAD DE MEDIDA DIFERENTE.

02 TODAS LAS MEDIDAS, UBICACIÓN Y NIVELES DEBEN VERIFICARSE EN EL LUGAR DE CONSTRUCCIÓN.

03 EL NIVEL DE ACCESO AL EDIFICIO PL 01 CORRESPONDE AL +0,00 DE LA ESTACIÓN Y REFERENCIA AL NIVEL 2555.56 M.S.N.M

04 LOS NOMBRES ESPECIFICOS DE LAS ÁREAS PUEDEN SER CONSULTADAS EN EL PLANO NO. 3 O EN LAS VISTAS EN PLANTA.

05 LOS COLORES QUE SE MUESTRAN EN LOS PLANOS COMO PROYECCIÓN DE ELEMENTOS ARQUITECTÓNICOS COMO CUBIERTAS FACHADAS MUROS ETC. NO REPRESENTAN LA MATERIALIDAD Y REALIDAD DE ACABADOS DEL PROYECTO, SOLO SON INDICATIVOS PARA REALIZAR UNA CORRECTA LECTURA DE LA PLANIMETRÍA.

06 LAS ESCALERAS ELÉCTRICAS INDICAN SU SENTIDO CON LA SIGUIENTE NOMENCLATURA: "SUBE" Y "BAJA".

07 EN LOS NIVELES DE ACCESO COMPRENDIDOS DESDE PL_00.1 A PL_01 SE DEBEN REVISAR LOS NIVELES ESTRUCTURALES CON LA PLANIMETRIA CORRESPONDIENTE A LAS PLACAS ESTRUCTURALES QUE SE ENCUENTRA EN LOS ENTREGABLES L1T1-0000-30X-CON-ED-STR-PL-0000 AL L1T1-0000-30X-CON-ED-STR-PL-0000. EN LOS NIVELES PL_02 (INTERMEDIO) Y PL_03 (PLATAFORMA), EL NIVEL ESTRUCTURAL (NE) SE ENCUENTRA A (- 0.10m) POR DEBAJO DE LOS NIVELES DE PISO TERMINADO (NPT) MARCADOS EN LA PLANIMETRÍA. A EXCEPCIÓN DE LOS NIVELES ESPECIFICADOS PARA LOCALES COMERCIALES, LOS CUALES SE UBICAN SOBRE PLACAS ESTRUCTURALES REFERENCIADOS COMO NIVEL ESTRUCTURAL (NE) Y ES RESPONSABILIDAD DEL LOCATARIO DEFINIR Y COLOCAR EL ACABADO DE PISO PARA EMPATAR CON EL NIVEL DE PISO TERMINADO (NPT) DEL ESPACIO INMEDIATO A SU ACCESO.

- ARC_PL_00 = SÓTANO	/ NPT -6.25
- ARC_PL_01 = ACCESO	/ NPT 0.00
- ARC_PL_02 = INTERMEDIO	/ NPT 7.60
- ARC_PL_02.1 = PLACA INFERIOR VIGA CAJÓN	/ NPT 13.82
- ARC_PL_02.2 = TOPE DE RIEL (TOR)	/ NPT 15.95
- ARC_PL_03 = PLATAFORMA	/ NPT 17.09
- ARC_PL_05 = CUBIERTA NAVE CENTRAL	/ NPT 26.42

CONVENCIONES

🟦	CADE
🟩	COMERCIAL ÁREA NO PAGA
🟩	COMERCIAL ÁREA PAGA
🟪	MUSEO
🟩	SERVICIO PÚBLICO
🟦	ZONA DE REFUGIO
🟥	ÁREA CULTURAL
🟪	ÁREA DE TAQUILLAS BRT
🟩	ÁREA JARDÍN
🟨	ÁREA NO PAGA
🟦	ÁREA OPERACIONAL
🟧	ÁREA PAGA
🟦	ÁREA PÚBLICA
⬜	ÁREA TÉCNICA

VDD CAMBIOS EFECTUADOS:
CAMBIO DE LAYOUT

No.	PLANOS DE REFERENCIA	REV.

No.	MODELO BIM DE REFERENCIA	REV.
1	L1T1-1100-208-CON-ED-EST-MO-0001.rvt	VCC
2	L1T1-1100-209-CON-ED-EST-MO-0001.rvt	VCC
3	L1T1-1100-308-CON-ED-EST-MO-0001.rvt	VCC
4	L1T1-1150-208-CON-ED-EST-MO-0001.rvt	VCC
5	L1T1-1150-209-CON-ED-EST-MO-0001.rvt	VCC
6	L1T1-1150-308-CON-ED-EST-MO-0001.rvt	VCC
7	L1T1-1410-308-CON-ED-MEC-MO-0001.rvt	VCC
8	L1T1-1420-308-CON-ED-MEC-MO-0001.rvt	VCC
9	L1T1-2420-561-CON-ED-MEC-MO-0001.rvt	VCC

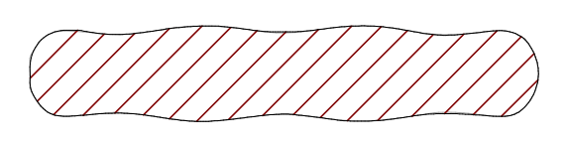

PLANO CLAVE ESTACIÓN 08

No.	PAQUETE DE TRABAJO DE REFERENCIA	REV.
1	XREF-URBANISM_CONTEXT_ST08.rvt	

0 2 10m
1:200

METRO BOGOTÁ
GCS Consorcio Consultores PMO Bogotá
CONSORCIO SUPERVISOR PLMB
wsp

DISEÑÓ:
ALBERTO ARANDA
Mat.: A25071999-79785641

APROBÓ:
MÓNICA F. BEDOYA M.
Mat.: 25202-75140 CND

REVISÓ:
JAIRO ESPEJO M.
Mat.:25202-20801 CND

DIBUJÓ:
EQUIPO WSP

REVISIÓN No.	FECHA	DESCRIPCIÓN	REVISÓ	APROBÓ	APROBACIÓN CLIENTE
VDD	17/07/2023	EMITIDO PARA REVISIÓN Y COMENTARIOS DEL CLIENTE E INTERVENTORÍA - INCLUYE COMENTARIOS /(AJUSTES)	J.E.M	M.B.M	
VCC	20/06/2022	EMITIDO PARA REVISIÓN Y COMENTARIOS DEL CLIENTE E INTERVENTORÍA - INCLUYE COMENTARIOS /(ENTREGA 90%)	J.E.M	M.B.M	
VBB	06/12/2021	EMITIDO PARA REVISIÓN Y COMENTARIOS DEL CLIENTE E INTERVENTORÍA	J.E.M	M.B.M	
VA0	30/06/2021	EMITIDO PARA COMENTARIOS INTERNOS - EMISIÓN PRELIMINAR PARA COMENTARIOS	J.E.M	M.B.M	

METRO LÍNEA 1

METRO LÍNEA 1
CONTRATO DE CONCESIÓN No. 163 DE 2019

PROYECTO PRIMERA LÍNEA DEL METRO DE BOGOTÁ - TRAMO 1

DIRECTOR DE INTERVENTORÍA:
JAVIER DESCARGA N.
Mat.:2520268697 CND

ESPECIALISTA INTERVENTORÍA:
MARIA AUXILIADORA SANCHEZ H.
INT: PAH138382-RES.No.34 DE 2021

FECHA: JULIO 2023

INFRAESTRUCTURA VIAL
ARQUITECTURA
ESTACIÓN 08 - CARRERA 50
NAVE CENTRAL
VISTA EN PLANTA - NIVEL INTERMEDIO 01

PLANCHA No: L1T1-0000-308-CON-ED-ARQ-PL-0001_06_VDD
ARCHIVO: L1T1-0000-308-CON-ED-ARQ-MO-0001_VCC.rvt
ESCALA: INDICADA
FECHA: JUNIO 2021
REVISIÓN No. VDD
PLANO No. 06 DE 32