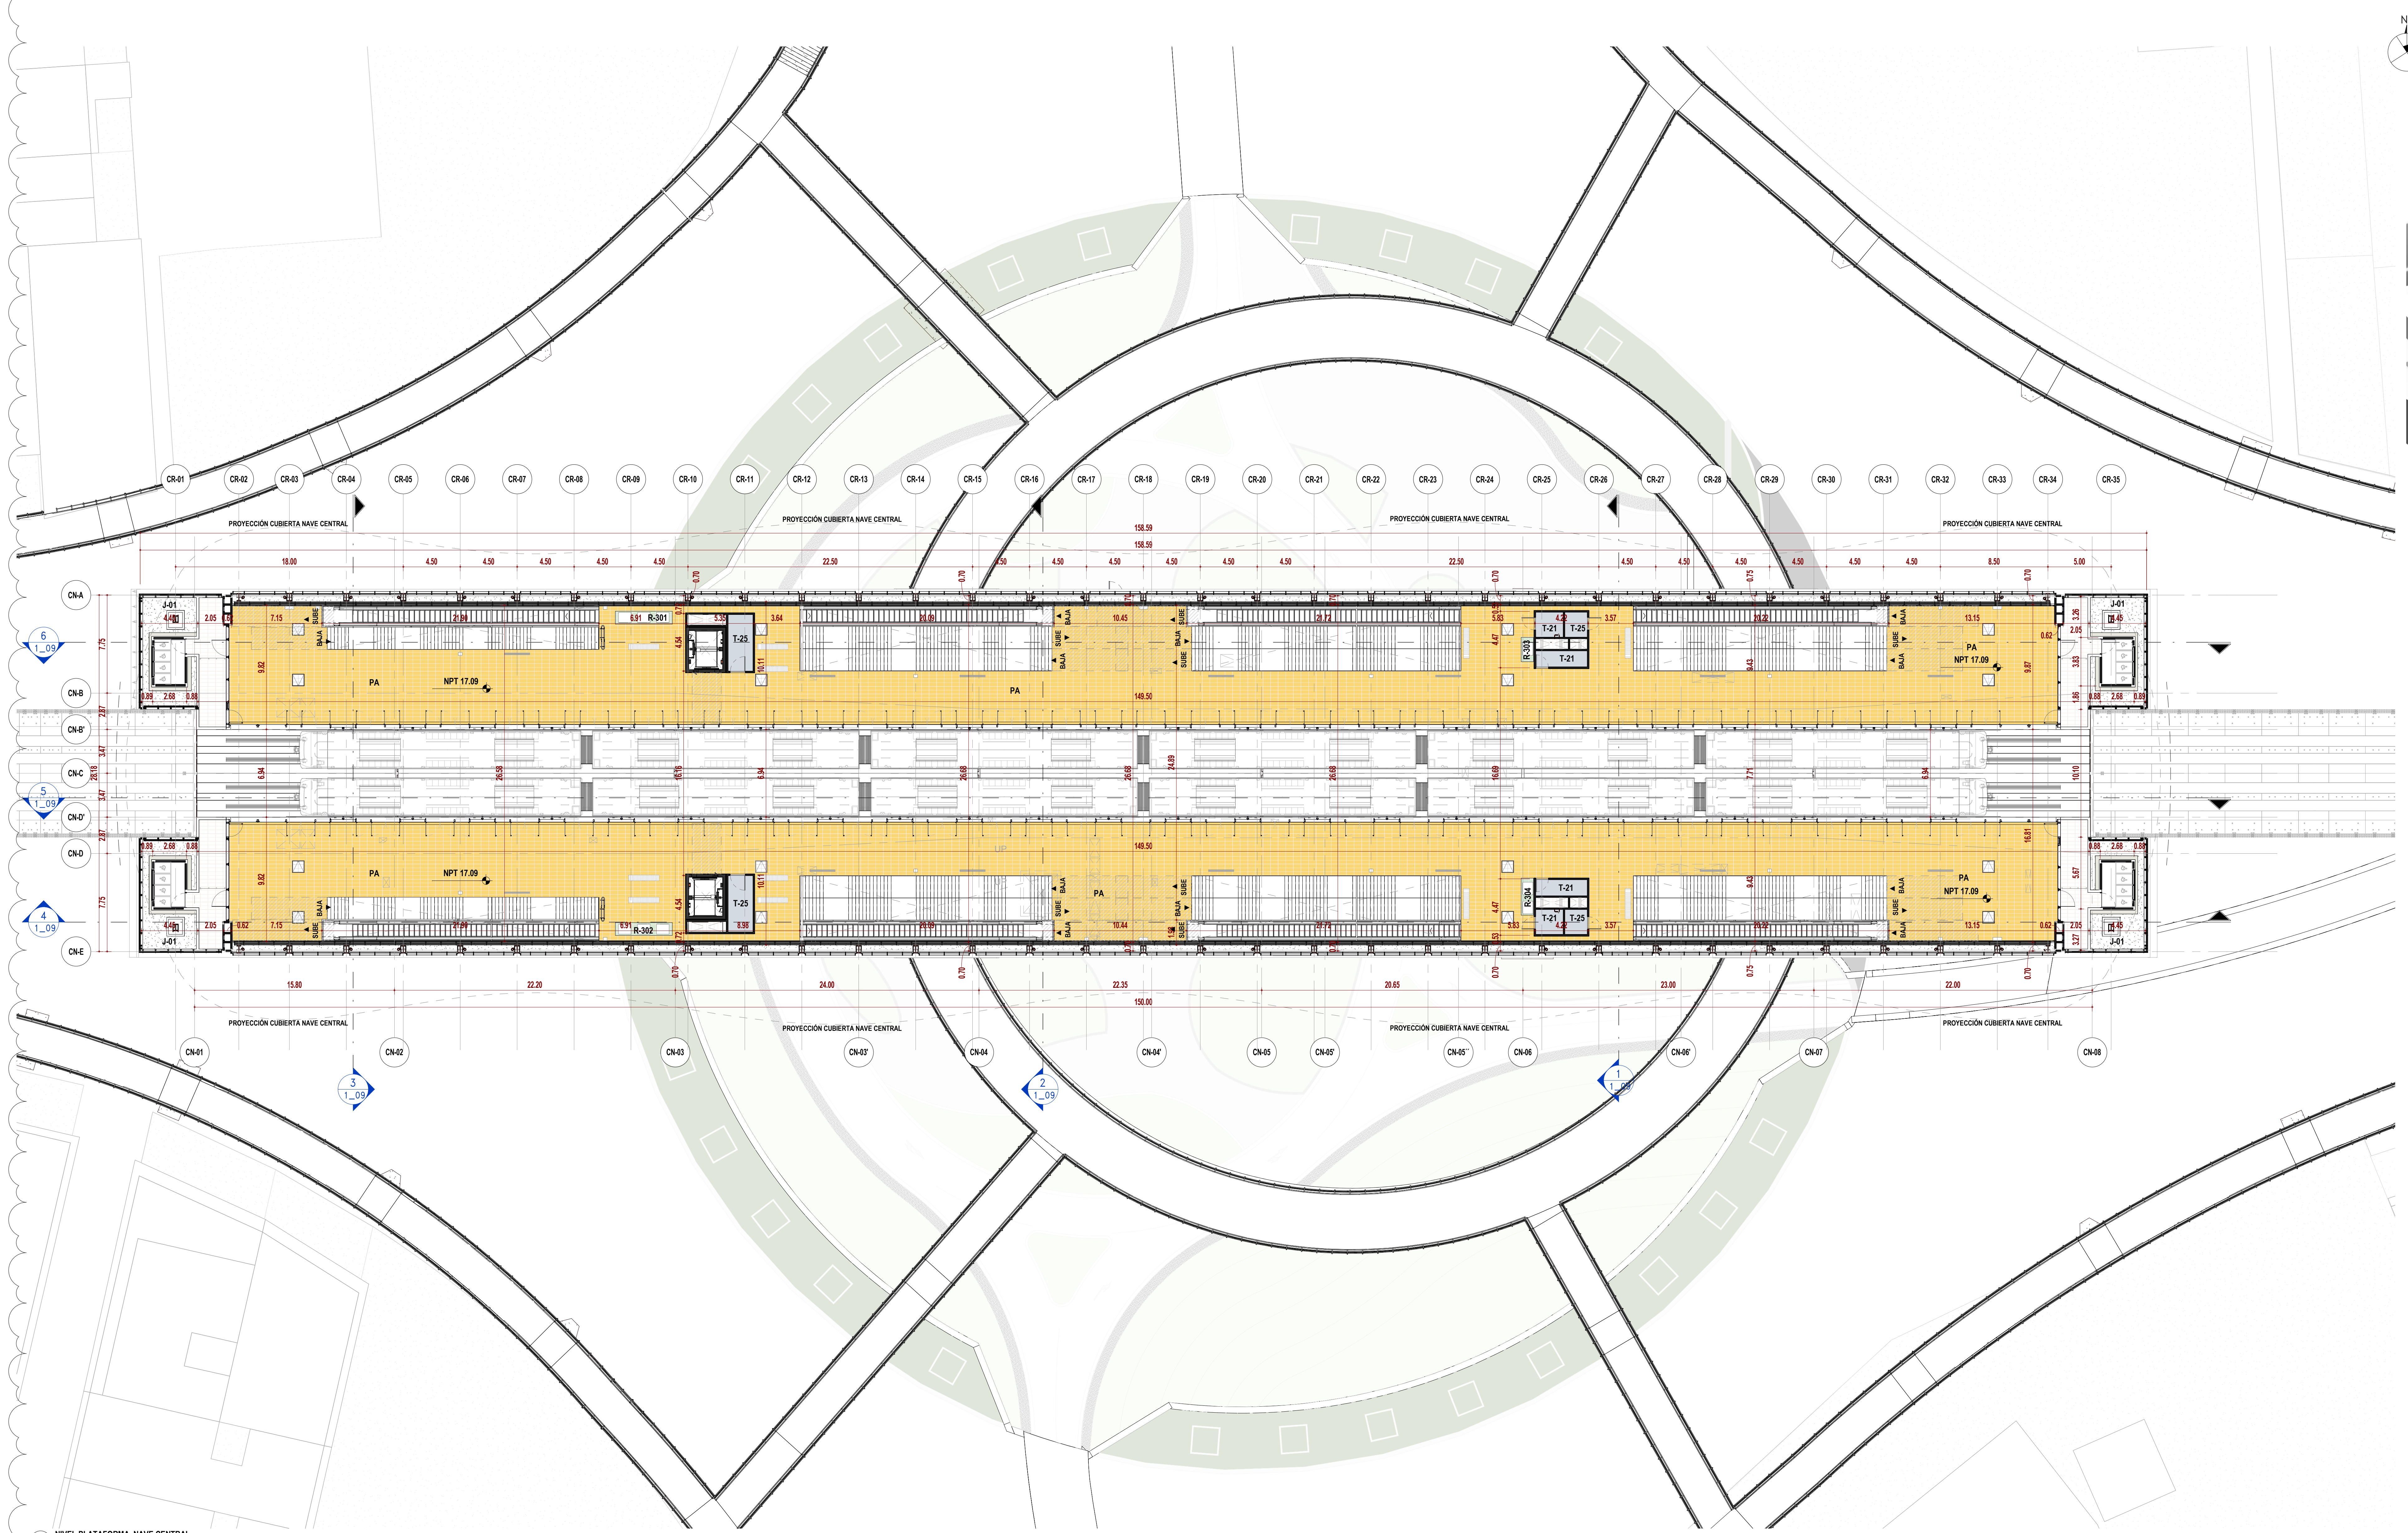

2 NIVEL PLATAFORMA_NAVE CENTRAL
ESC: 1 : 200

VDD

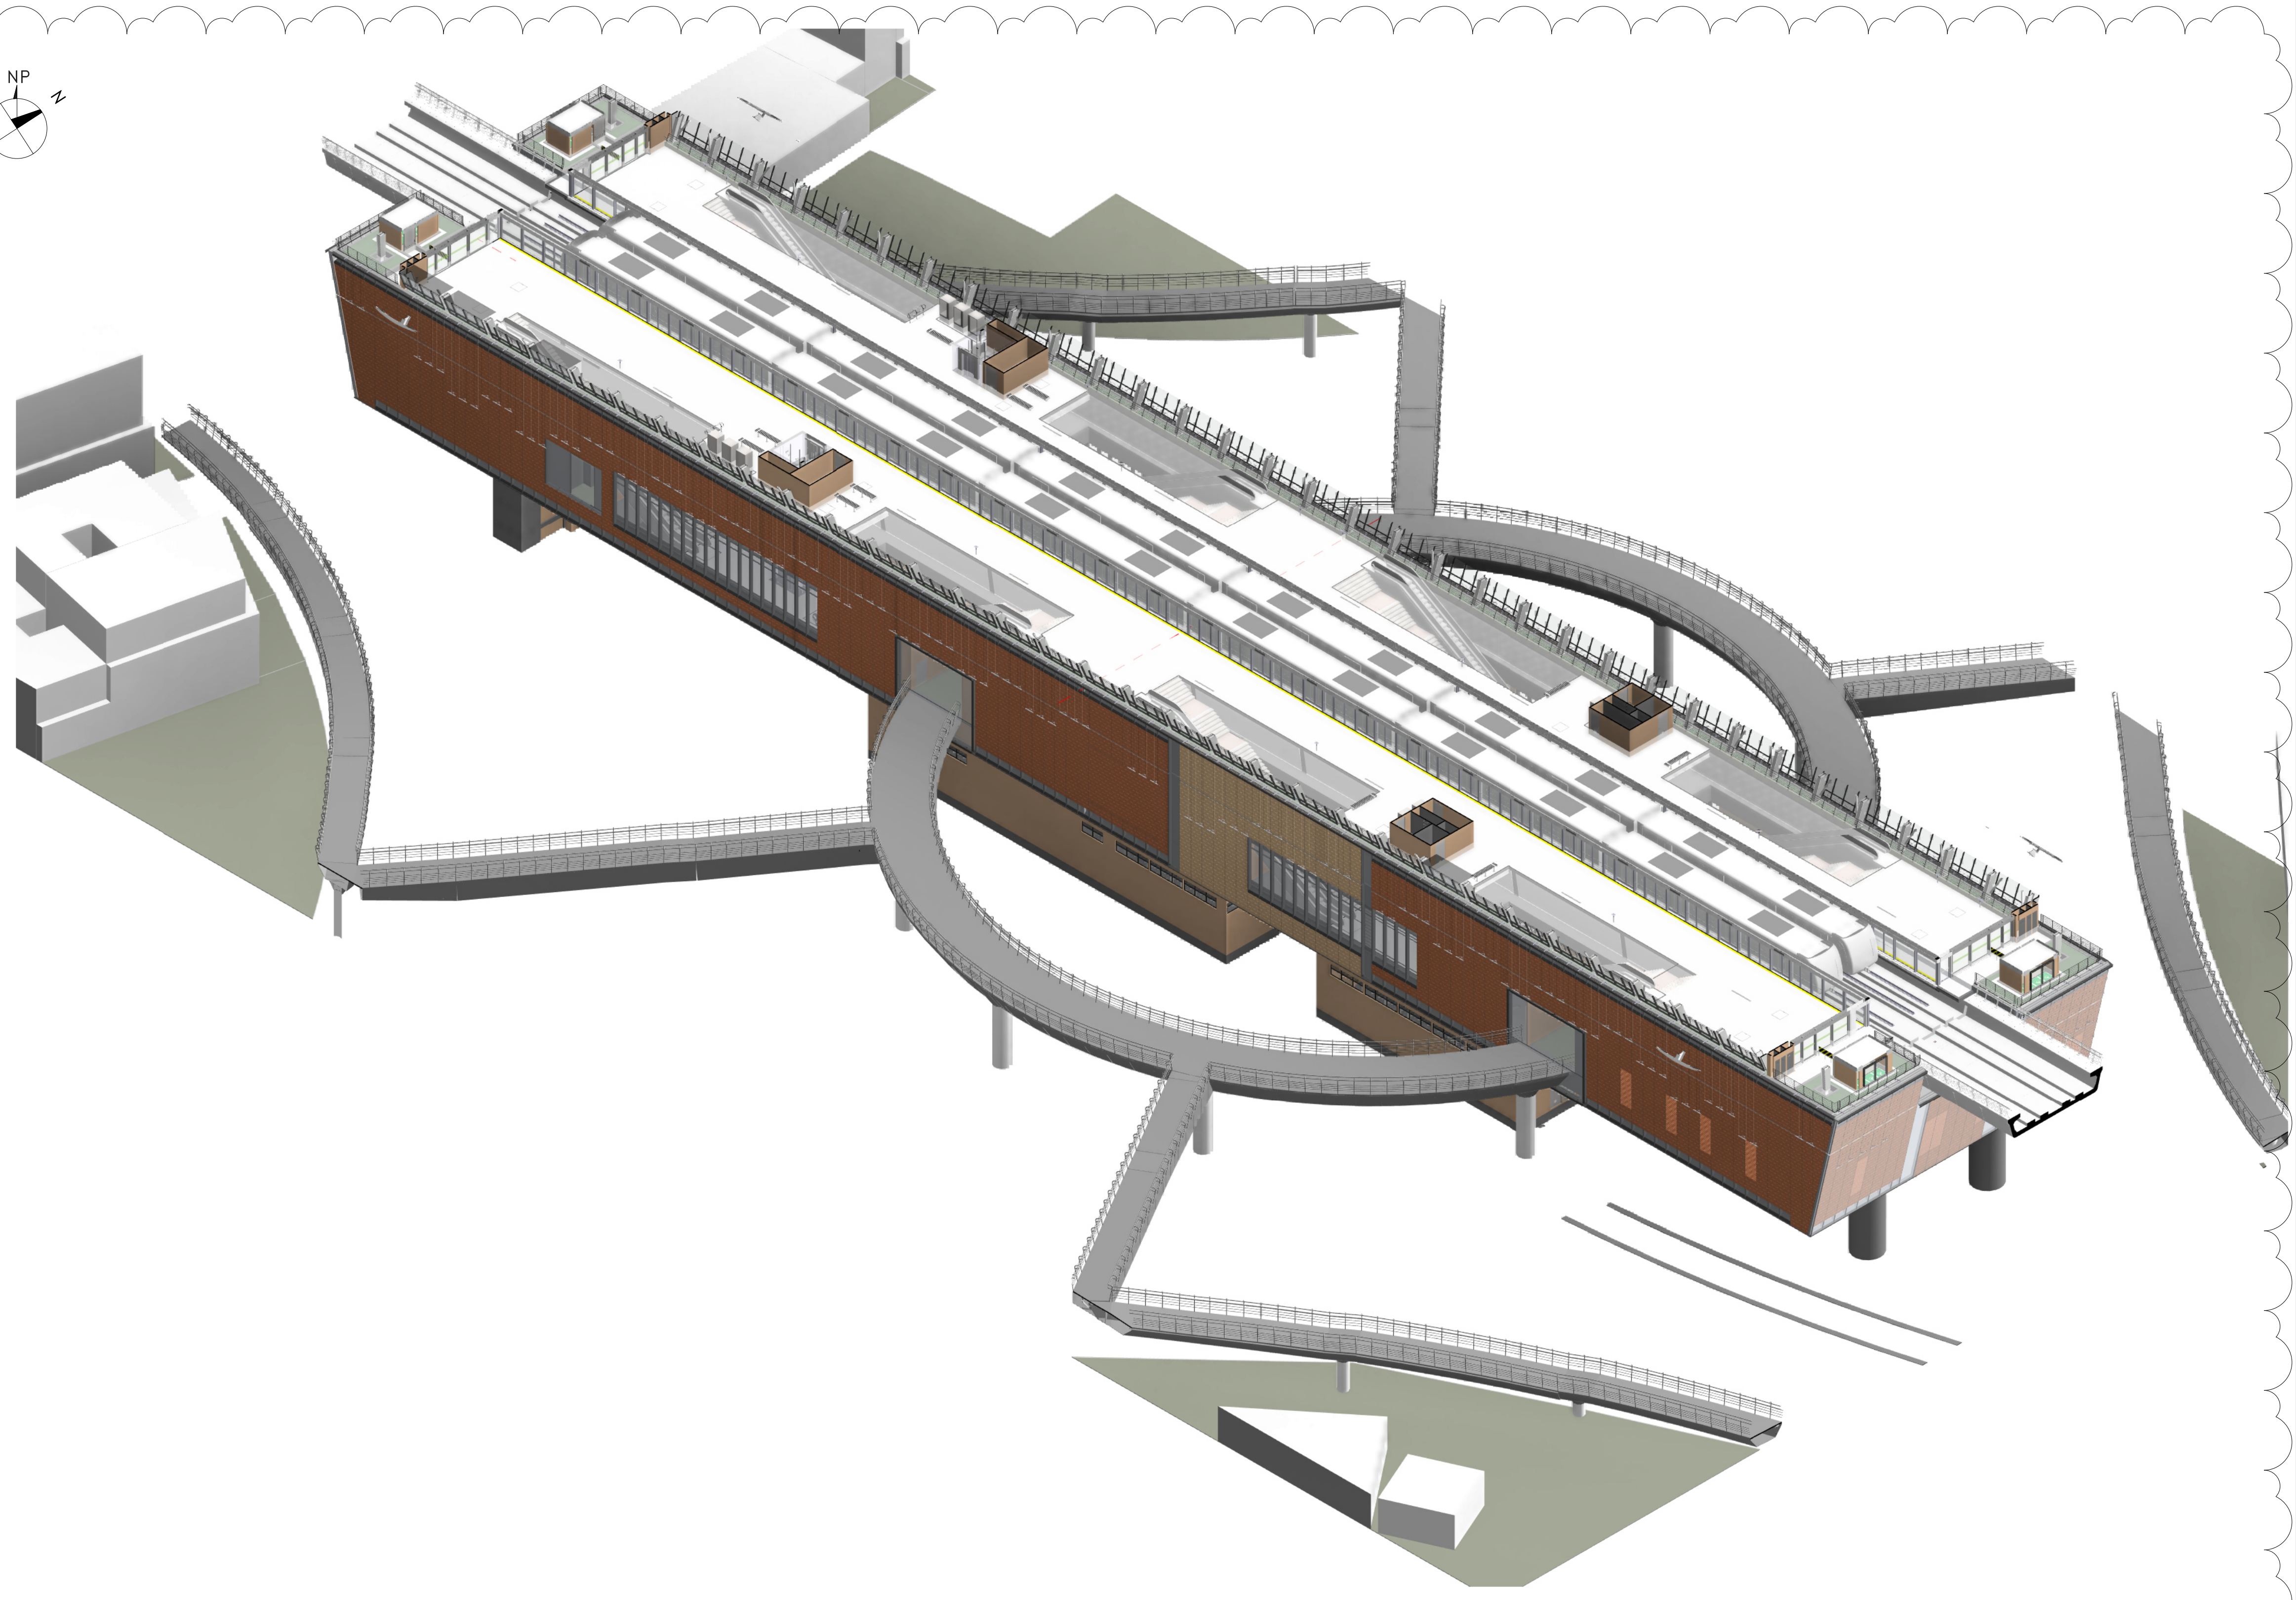

1 3D_NIVEL PLATAFORMA_NAVE CENTRAL
ESC: N/A

## 13_TABLA DE ÁREAS (NIVEL PLATAFORMA_NAVE CENTRAL)

| CÓDIGO | NOMBRE | ÁREA (m²) | DEPARTAMENTO |
|---|---|---|---|
| J-01 | JARDÍN | 18.43 | ÁREA JARDIN |
| J-01 | JARDÍN | 18.43 | ÁREA JARDIN |
| J-01 | JARDÍN | 18.43 | ÁREA JARDIN |
| J-01 | JARDÍN | 18.43 | ÁREA JARDIN |
| PA | ÁREA PAGA | 915.62 | ÁREA PAGA |
| PA | ÁREA PAGA | 921.62 | ÁREA PAGA |
| R-301 | COMERCIO - MÁQUINAS EXPENDEDORAS/CAJEROS AUTOMÁTICOS | 4.59 | COMERCIO - ÁREA NO PAGA |
| R-302 | COMERCIO - MÁQUINAS EXPENDEDORAS/CAJEROS AUTOMÁTICOS | 4.59 | COMERCIO - ÁREA NO PAGA |
| R-303 | COMERCIO - MÁQUINAS EXPENDEDORAS/CAJEROS AUTOMÁTICOS | 1.87 | COMERCIO - ÁREA NO PAGA |
| R-304 | COMERCIO - MÁQUINAS EXPENDEDORAS/CAJEROS AUTOMÁTICOS | 2.84 | COMERCIO - ÁREA NO PAGA |
| T-21 | ÁREA DE INSPECCIÓN | 5.33 | ÁREA TÉCNICA |
| T-21 | ÁREA DE INSPECCIÓN | 5.33 | ÁREA TÉCNICA |
| T-21 | ÁREA DE INSPECCIÓN | 4.40 | ÁREA TÉCNICA |
| T-21 | ÁREA DE INSPECCIÓN | 4.40 | ÁREA TÉCNICA |
| T-25 | NODO DE ACCESO DE TELECOMUNICACIONES | 9.00 | ÁREA TÉCNICA |
| T-25 | NODO DE ACCESO DE TELECOMUNICACIONES | 8.98 | ÁREA TÉCNICA |
| T-25 | NODO DE ACCESO DE TELECOMUNICACIONES | 3.60 | ÁREA TÉCNICA |
| T-25 | NODO DE ACCESO DE TELECOMUNICACIONES | 3.60 | ÁREA TÉCNICA |
| ZDR | ZONA DE REFUGIO (PMR) | 4.86 | ZONA DE REFUGIO |
| ZDR | ZONA DE REFUGIO (PMR) | 4.86 | ZONA DE REFUGIO |
| ZDR | ZONA DE REFUGIO (PMR) | 4.86 | ZONA DE REFUGIO |
| ZDR | ZONA DE REFUGIO (PMR) | 4.86 | ZONA DE REFUGIO |
| TOTAL NIVEL |  | 1988.92 |  |

## 13_TABLA DE ÁREAS POR DEPARTAMENTO (PLATAFORMA)

| DEPARTAMENTO | ÁREA (m²) |
|---|---|
| COMERCIO - ÁREA NO PAGA | 13.89 |
| ZONA DE REFUGIO | 19.44 |
| ÁREA JARDIN | 73.72 |
| ÁREA PAGA | 1837.24 |
| ÁREA TÉCNICA | 44.64 |
| TOTAL | 1988.92 |

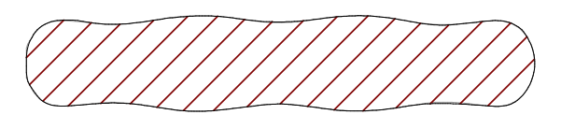

PLANO CLAVE ESTACIÓN 08

## LOCALIZACIÓN

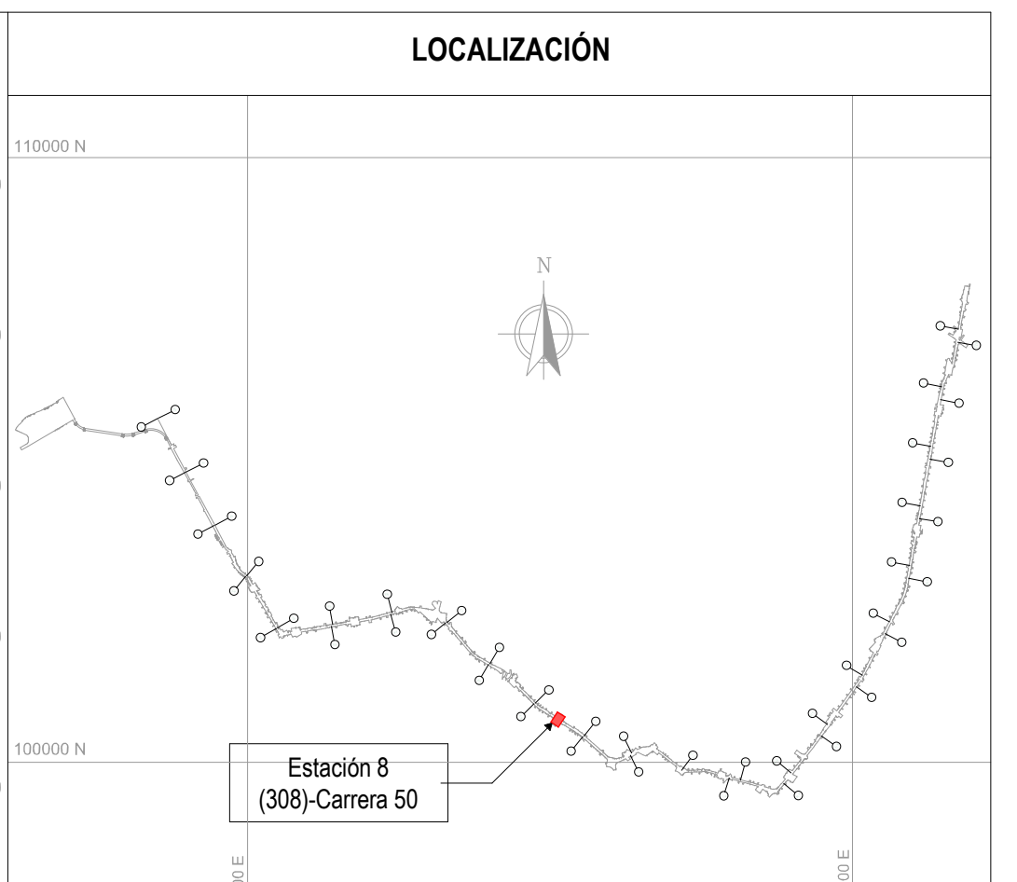

Estación 8
(308)-Carrera 50

## NOTAS

01 TODAS LAS DIMENSIONES ESTÁN CONFIGURADAS EN METROS A MENOS QUE SE INDIQUE UNA UNIDAD DE MEDIDA DIFERENTE.

02 TODAS LAS MEDIDAS, UBICACIÓN Y NIVELES DEBEN VERIFICARSE EN EL LUGAR DE CONSTRUCCIÓN.

03 EL NIVEL DE ACCESO AL EDIFICIO PL 01 CORRESPONDE AL +0,00 DE LA ESTACIÓN Y REFERENCIA AL NIVEL 2555.56 M.S.N.M

04 LOS NOMBRES ESPECIFICOS DE LAS ÁREAS PUEDEN SER CONSULTADAS EN EL PLANO NO. 3 O EN LAS VISTAS EN PLANTA.

05 LOS COLORES QUE SE MUESTRAN EN LOS PLANOS COMO PROYECCIÓN DE ELEMENTOS ARQUITECTÓNICOS COMO CUBIERTAS FACHADAS MUROS ETC. NO REPRESENTAN LA MATERIALIDAD Y REALIDAD DE ACABADOS DEL PROYECTO, SOLO SON INDICATIVOS PARA REALIZAR UNA CORRECTA LECTURA DE LA PLANIMETRÍA.

06 LAS ESCALERAS ELÉCTRICAS INDICAN SU SENTIDO CON LA SIGUIENTE NOMENCLATURA: "SUBE" Y "BAJA".

07 EN LOS NIVELES DE ACCESO COMPRENDIDOS DESDE PL_00.1 A PL_01 SE DEBEN REVISAR LOS NIVELES ESTRUCTURALES CON LA PLANIMETRIA CORRESPONDIENTE A LAS PLACAS ESTRUCTURALES QUE SE ENCUENTRA EN LOS ENTREGABLES L1T1-0000-30X-CON-ED-STR-PL-0000 AL L1T1-0000-30X-CON-ED-STR-PL-0000. EN LOS NIVELES PL_02 (INTERMEDIO) Y PL_03 (PLATAFORMA), EL NIVEL ESTRUCTURAL (NE) SE ENCUENTRA A (- 0.10m) POR DEBAJO DE LOS NIVELES DE PISO TERMINADO (NPT) MARCADOS EN LA PLANIMETRÍA. A EXCEPCIÓN DE LOS NIVELES ESPECIFICADOS PARA LOCALES COMERCIALES, LOS CUALES SE UBICAN SOBRE PLACAS ESTRUCTURALES REFERENCIADOS COMO NIVEL ESTRUCTURAL (NE) Y ES RESPONSABILIDAD DEL LOCATARIO DEFINIR Y COLOCAR EL ACABADO DE PISO PARA EMPATAR CON EL NIVEL DE PISO TERMINADO (NPT) DEL ESPACIO INMEDIATO A SU ACCESO.

| | |
|---|---|
| - ARC_PL_00 = SÓTANO | / NPT -6.25 |
| - ARC_PL_01 = ACCESO | / NPT 0.00 |
| - ARC_PL_02 = INTERMEDIO | / NPT 7.60 |
| - ARC_PL_02.1 = PLACA INFERIOR VIGA CAJÓN | / NPT 13.82 |
| - ARC_PL_02.2 = TOPE DE RIEL (TOR) | / NPT 15.95 |
| - ARC_PL_03 = PLATAFORMA | / NPT 17.09 |
| - ARC_PL_05 = CUBIERTA NAVE CENTRAL | / NPT 26.42 |

## CONVENCIONES

| | |
|---|---|
| 🟩 | CADE |
| 🟩 | COMERCIAL ÁREA NO PAGA |
| 🟩 | COMERCIAL ÁREA PAGA |
| 🟥 | MUSEO |
| 🟩 | SERVICIO PÚBLICO |
| 🟦 | ZONA DE REFUGIO |
| 🟥 | ÁREA CULTURAL |
| 🟪 | ÁREA DE TAQUILLAS BRT |
| 🟩 | ÁREA JARDÍN |
| 🟨 | ÁREA NO PAGA |
| 🟦 | ÁREA OPERACIONAL |
| 🟧 | ÁREA PAGA |
| 🟦 | ÁREA PÚBLICA |
| ⬜ | ÁREA TÉCNICA |

VDD CAMBIOS EFECTUADOS:
REDISTRIBUCIÓN TRAMOS DE ESCALERAS

| No. | PLANOS DE REFERENCIA | REV. |
|---|---|---|
|  |  |  |
|  |  |  |

| No. | MODELO BIM DE REFERENCIA | REV. |
|---|---|---|
| 1 | L1T1-1100-208-CON-ED-EST-MO-0001.rvt | VCC |
| 2 | L1T1-1100-209-CON-ED-EST-MO-0001.rvt | VCC |
| 3 | L1T1-1100-308-CON-ED-EST-MO-0001.rvt | VCC |
| 4 | L1T1-1150-208-CON-ED-EST-MO-0001.rvt | VCC |
| 5 | L1T1-1150-209-CON-ED-EST-MO-0001.rvt | VCC |
| 6 | L1T1-1150-308-CON-ED-EST-MO-0001.rvt | VCC |
| 7 | L1T1-1410-308-CON-ED-MEC-MO-0001.rvt | VCC |
| 8 | L1T1-1420-308-CON-ED-MEC-MO-0001.rvt | VCC |
| 9 | L1T1-2420-561-CON-ED-MEC-MO-0001.rvt | VCC |

| No. | PAQUETE DE TRABAJO DE REFERENCIA | REV. |
|---|---|---|
| 1 | XREF-URBANISM_CONTEXT_ST08.rvt |  |

0 2 10m
1:200

METRO BOGOTÁ
GCS Consorcio Consultores PMO Bogotá
CONSORCIO SUPERVISOR PLMB
wsp

DISEÑÓ:
ALBERTO ARANDA
Mat.: A25071999-79785641

APROBÓ:
MÓNICA F. BEDOYA M.
Mat.: 25202-75140 CND

REVISÓ:
JAIRO ESPEJO M.
Mat.:25202-20801 CND

DIBUJÓ:
EQUIPO WSP

| REVISIÓN No. | FECHA | DESCRIPCIÓN | REVISÓ | APROBÓ | APROBACIÓN CLIENTE |
|---|---|---|---|---|---|
| VDD | 17/07/2023 | EMITIDO PARA REVISIÓN Y COMENTARIOS DEL CLIENTE E INTERVENTORÍA - INCLUYE COMENTARIOS /(AJUSTES) | J.E.M | M.B.M |  |
| VCC | 20/06/2022 | EMITIDO PARA REVISIÓN Y COMENTARIOS DEL CLIENTE E INTERVENTORÍA - INCLUYE COMENTARIOS /(ENTREGA 90%) | J.E.M | M.B.M |  |
| VBB | 06/12/2021 | EMITIDO PARA REVISIÓN Y COMENTARIOS DEL CLIENTE E INTERVENTORÍA | J.E.M | M.B.M |  |
| VA0 | 30/06/2021 | EMITIDO PARA COMENTARIOS INTERNOS - EMISIÓN PRELIMINAR PARA COMENTARIOS | J.E.M | M.B.M |  |

METRO LÍNEA 1

METRO LÍNEA 1
CONTRATO DE CONCESIÓN No. 163 DE 2019

PROYECTO PRIMERA LÍNEA DEL METRO DE BOGOTÁ - TRAMO 1

DIRECTOR DE INTERVENTORÍA:
JAVIER DESCARGA N.
Mat.:2520268697 CND

ESPECIALISTA INTERVENTORÍA:
MARIA AUXILIADORA SANCHEZ H.
INT: PAH138382-RES.No.34 DE 2021

FECHA:
JULIO 2023

INFRAESTRUCTURA VIAL

ARQUITECTURA

ESTACIÓN 08 - CARRERA 50
NAVE CENTRAL
VISTA EN PLANTA - NIVEL DE PLATAFORMA 01

PLANCHA No: L1T1-0000-308-CON-ED-ARQ-PL-0001_07_VDD
ARCHIVO: L1T1-0000-308-CON-ED-ARQ-MO-0001_VCC.rvt
ESCALA: INDICADA
FECHA: JUNIO 2021
REVISIÓN No. VDD
PLANO No. 07 DE 32