L1T1-CON-CAL-FR-0120 - B1 : 1000x707mm

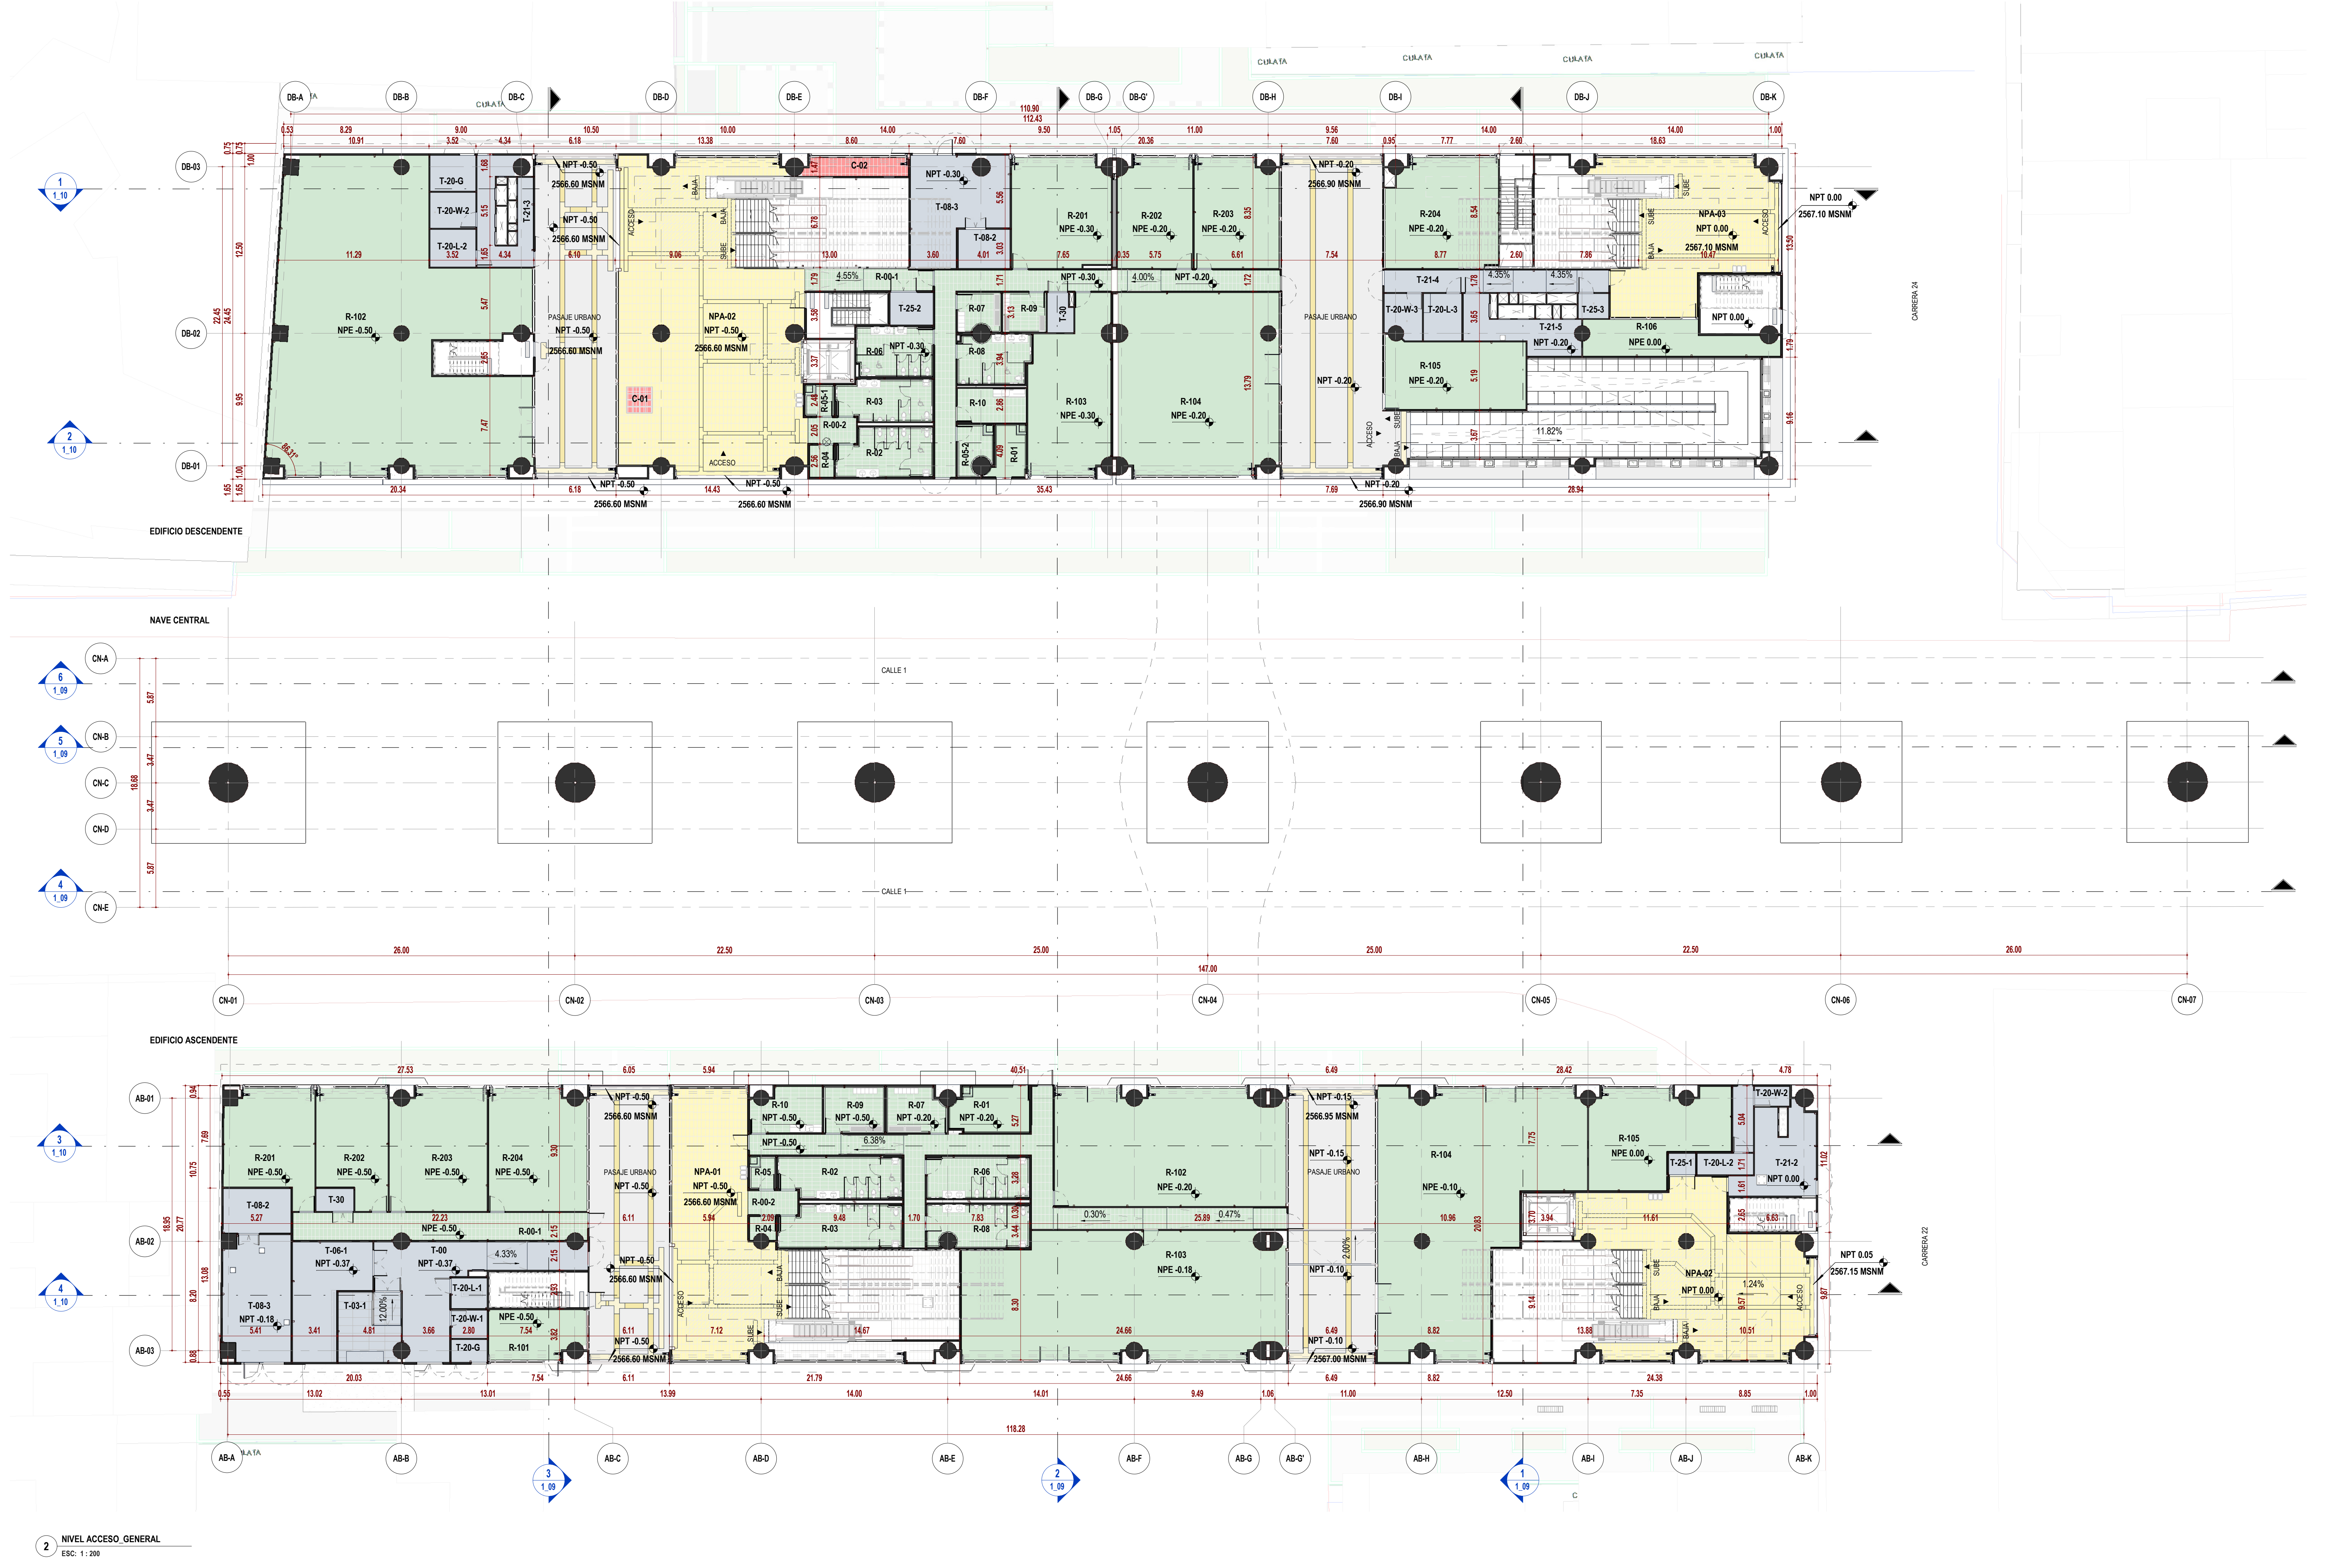

2 NIVEL ACCESO_GENERAL
ESC: 1 : 200

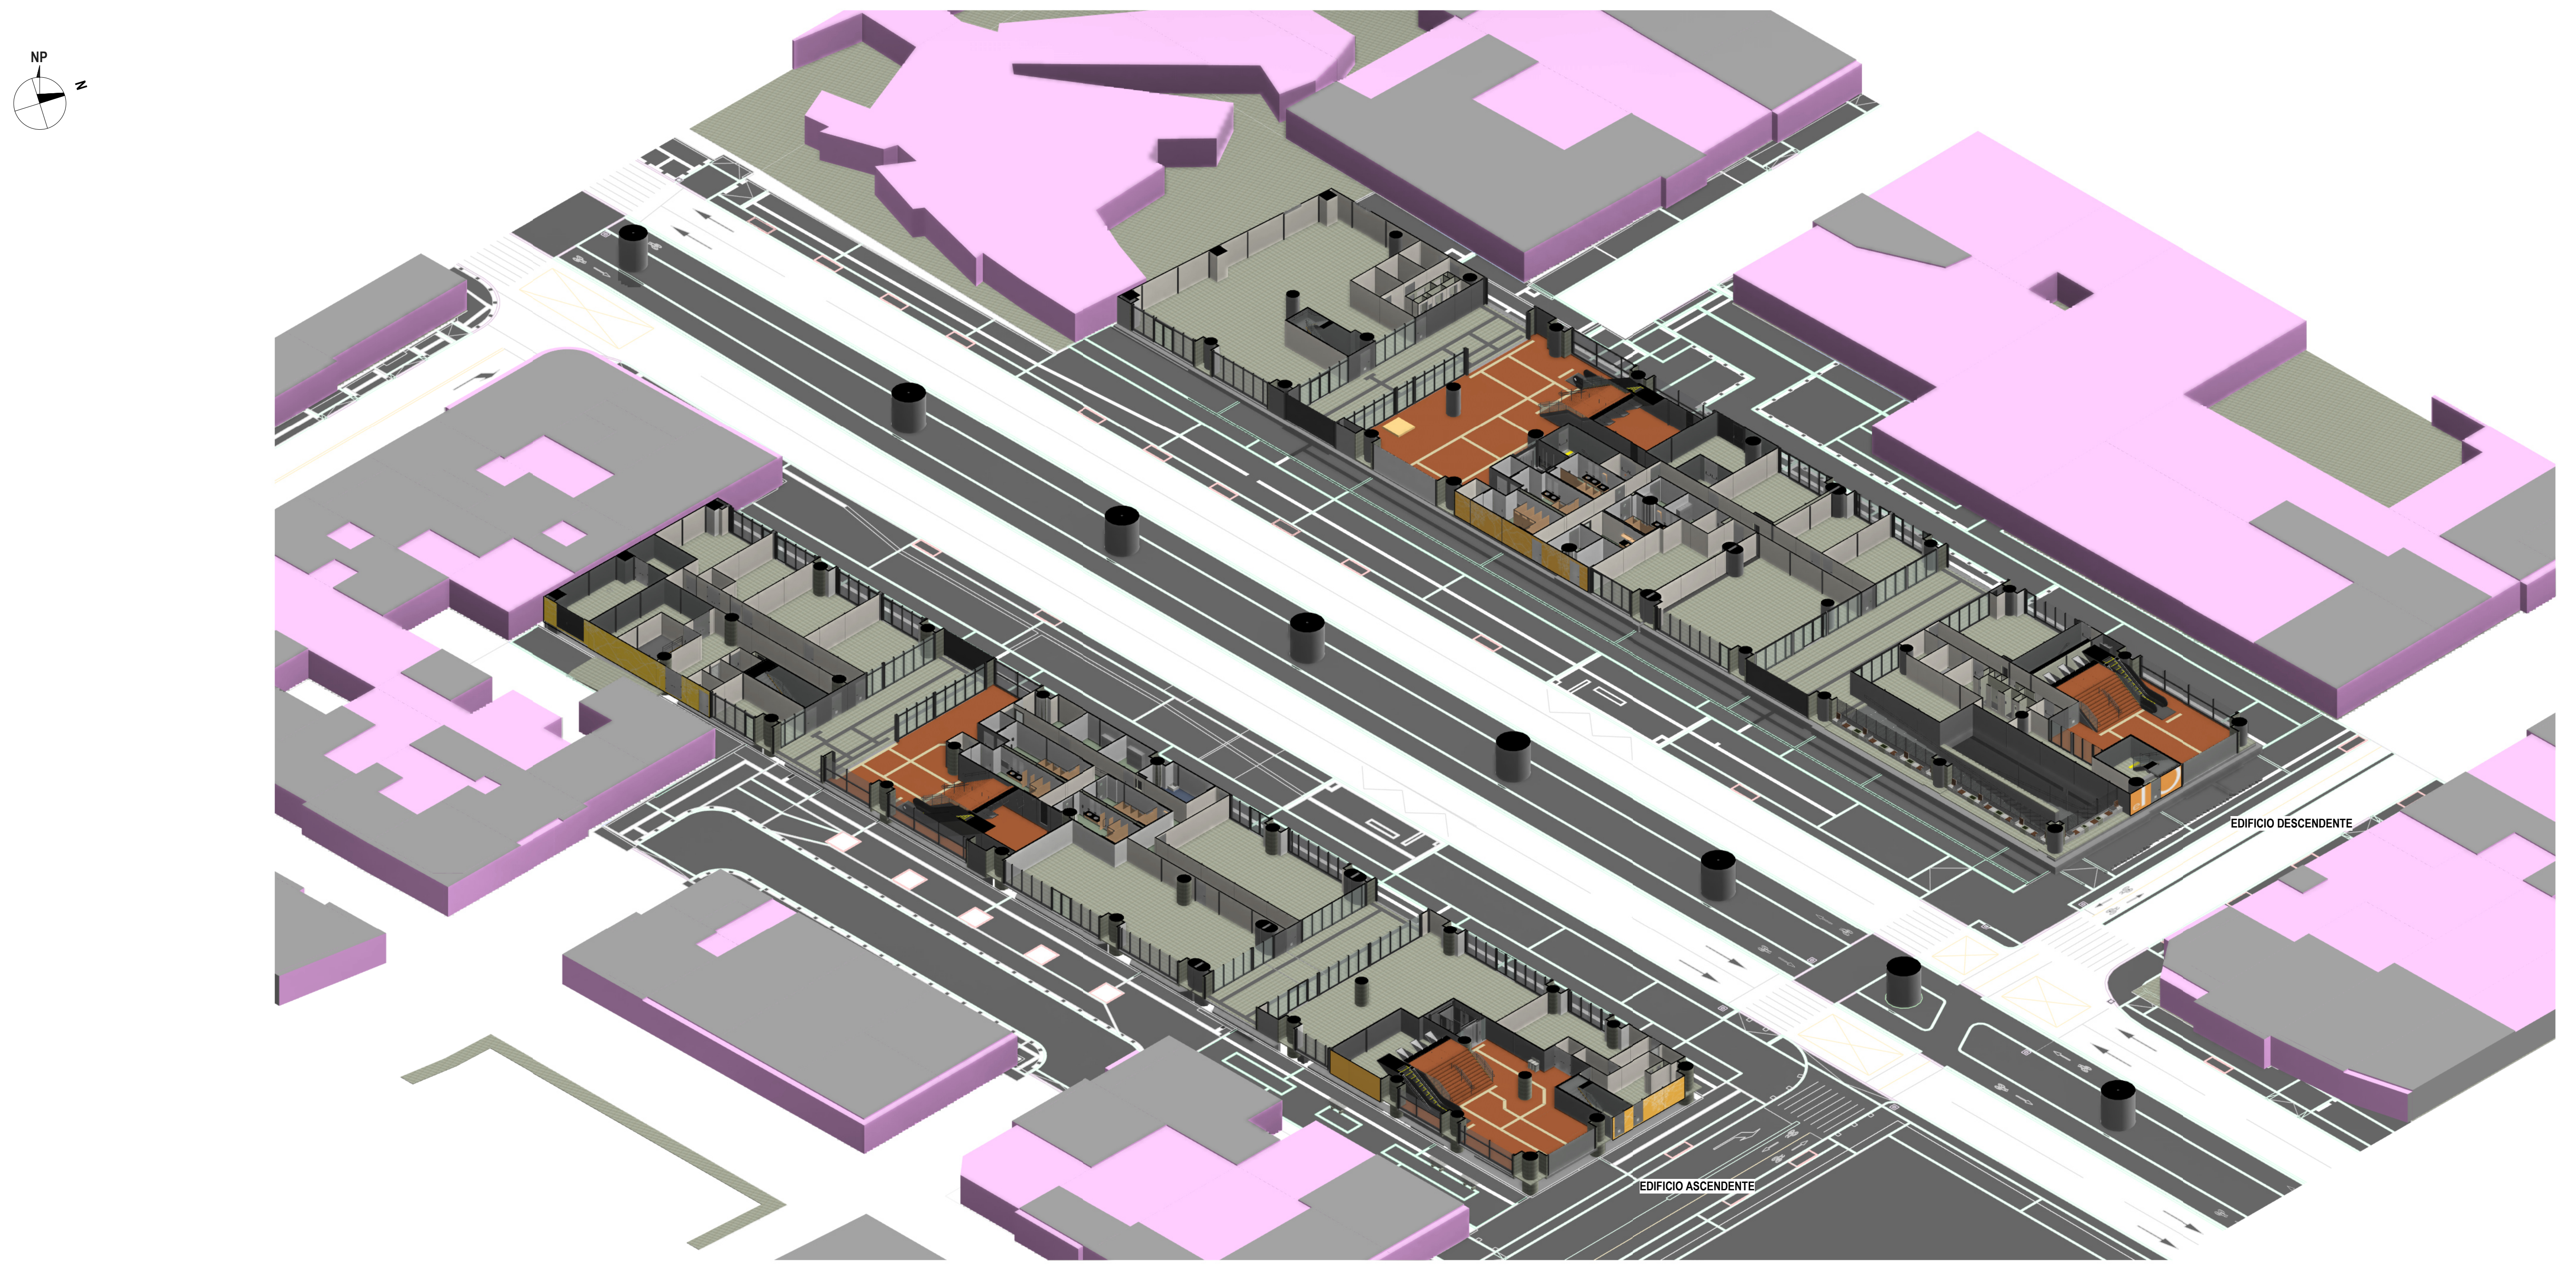

1 3D_NIVEL ACCESO_GENERAL
ESC: N/A

TABLA DE ÁREAS ÚTILES (NIVEL ACCESO)

CÓDIGO	NOMBRE	ÁREA (m²)	DEPARTAMENTO
EDIFICIO ASCENDENTE			
ARQ_PL_00.1_ACCESO			
NPA-01	ÁREA NO PAGA	138.30	ÁREA NO PAGA
R-00-1	SERVICIOS ADICIONALES - CORREDOR OPERATIVO	45.10	SERVICIOS ADICIONALES - ÁREA NO PAGA
R-00-2	SERVICIOS ADICIONALES - CORREDOR OPERATIVO	6.74	SERVICIOS ADICIONALES - ÁREA NO PAGA
R-00-3	SERVICIOS ADICIONALES - CORREDOR OPERATIVO	17.81	SERVICIOS ADICIONALES - ÁREA NO PAGA
R-02	SERVICIOS ADICIONALES - BAÑO PÚBLICO DE MUJERES	27.74	SERVICIOS ADICIONALES - ÁREA NO PAGA
R-03	SERVICIOS ADICIONALES - BAÑO PÚBLICO DE HOMBRES	28.32	SERVICIOS ADICIONALES - ÁREA NO PAGA
R-04	SERVICIOS ADICIONALES - CONTROL DE ACCESO BAÑOS PÚBLICOS	3.03	SERVICIOS ADICIONALES - ÁREA NO PAGA
R-05	SERVICIOS ADICIONALES - CUARTO DE LIMPIEZA	4.66	SERVICIOS ADICIONALES - ÁREA NO PAGA
R-09	SERVICIOS ADICIONALES - VESTIDORES EMPLEADOS HOMBRES	15.70	SERVICIOS ADICIONALES - ÁREA NO PAGA
R-10	SERVICIOS ADICIONALES - SALA DE EMPLEADOS	16.60	SERVICIOS ADICIONALES - ÁREA NO PAGA
R-101	SERVICIOS ADICIONALES - ÁREA DE SERVICIO	25.25	SERVICIOS ADICIONALES - ÁREA NO PAGA
R-201	SERVICIOS ADICIONALES - ÁREA DE COMIDAS	51.77	SERVICIOS ADICIONALES - ÁREA NO PAGA
R-202	SERVICIOS ADICIONALES - ÁREA DE COMIDAS	44.25	SERVICIOS ADICIONALES - ÁREA NO PAGA
R-203	SERVICIOS ADICIONALES - ÁREA DE COMIDAS	65.06	SERVICIOS ADICIONALES - ÁREA NO PAGA
R-204	SERVICIOS ADICIONALES - ÁREA DE COMIDAS	65.57	SERVICIOS ADICIONALES - ÁREA NO PAGA
T-00	CIRCULACIÓN TÉCNICA	60.16	ÁREA TÉCNICA
T-03-1	LOCAL SECUNDARIO DE TELECOMUNICACIONES	24.09	ÁREA TÉCNICA
T-06-1	LOCAL SECUNDARIO DE TABLEROS	39.27	ÁREA TÉCNICA
T-20-G	MEDIDORES (GAS)	4.59	ÁREA TÉCNICA
T-20-L-1	MEDIDORES (LUZ)	6.23	ÁREA TÉCNICA
T-20-W-1	MEDIDORES (AGUA)	5.73	ÁREA TÉCNICA
T-30	SISTEMA PROTECCIÓN CONTRA INCENDIO ENEL	4.73	ÁREA TÉCNICA
		700.71	
ARQ_PL_00.3_ACCESO			
R-00	SERVICIOS ADICIONALES - CORREDOR OPERATIVO	71.50	SERVICIOS ADICIONALES - ÁREA NO PAGA
R-01	SERVICIOS ADICIONALES - CUARTO DE BASURAS PARA METRO	19.27	SERVICIOS ADICIONALES - ÁREA NO PAGA
R-06	SERVICIOS ADICIONALES - BAÑOS EMPLEADOS MUJERES	23.67	SERVICIOS ADICIONALES - ÁREA NO PAGA
R-07	SERVICIOS ADICIONALES - VESTIDORES EMPLEADOS MUJERES	14.46	SERVICIOS ADICIONALES - ÁREA NO PAGA
R-08	SERVICIOS ADICIONALES - BAÑOS EMPLEADOS HOMBRES	23.49	SERVICIOS ADICIONALES - ÁREA NO PAGA
R-102	SERVICIOS ADICIONALES - ÁREA DE SERVICIO	148.01	SERVICIOS ADICIONALES - ÁREA NO PAGA
R-103	SERVICIOS ADICIONALES - ÁREA DE SERVICIO	218.67	SERVICIOS ADICIONALES - ÁREA NO PAGA
T-08-2	CENTRO DE TRANSFORMACIÓN ENEL-CODENSA (CT)_CUARTO BAJA TENSIÓN	17.01	ÁREA TÉCNICA
T-08-3	CENTRO DE TRANSFORMACIÓN ENEL-CODENSA (CT)_CUARTO MEDIA TENSIÓN	46.75	ÁREA TÉCNICA
		582.83	
ARQ_PL_00.4_ACCESO			
R-104	SERVICIOS ADICIONALES - ÁREA DE SERVICIO	232.17	SERVICIOS ADICIONALES - ÁREA NO PAGA
		232.17	

TABLA DE ÁREAS ÚTILES (NIVEL ACCESO)

CÓDIGO	NOMBRE	ÁREA (m²)	DEPARTAMENTO
ARQ_PL_01_ACCESO			
NPA-02	ÁREA NO PAGA	158.99	ÁREA NO PAGA
R-105	SERVICIOS ADICIONALES - ÁREA DE SERVICIO	64.61	SERVICIOS ADICIONALES - ÁREA NO PAGA
T-20-L-2	MEDIDORES (LUZ)	6.71	ÁREA TÉCNICA
T-20-W-2	MEDIDORES (AGUA)	3.85	ÁREA TÉCNICA
T-21-1	ÁREA DE INSPECCIÓN	7.40	ÁREA TÉCNICA
T-21-2	ÁREA DE INSPECCIÓN	31.41	ÁREA TÉCNICA
T-25-1	NODO DE ACCESO DE TELECOMUNICACIONES	3.21	ÁREA TÉCNICA
		276.20	
EDIFICIO DESCENDENTE			
ARQ_PL_00.1_ACCESO			
C-01	ÁREAS DE USO CULTURAL	4.00	ÁREA CULTURAL
C-02	ÁREAS DE USO CULTURAL	10.76	ÁREA CULTURAL
NPA-02	ÁREA NO PAGA	281.43	ÁREA NO PAGA
R-00-1	SERVICIOS ADICIONALES - CORREDOR OPERATIVO	15.93	SERVICIOS ADICIONALES - ÁREA NO PAGA
R-00-2	SERVICIOS ADICIONALES - CORREDOR OPERATIVO	7.04	SERVICIOS ADICIONALES - ÁREA NO PAGA
R-02	SERVICIOS ADICIONALES - BAÑO PÚBLICO DE MUJERES	24.60	SERVICIOS ADICIONALES - ÁREA NO PAGA
R-03	SERVICIOS ADICIONALES - BAÑO PÚBLICO DE HOMBRES	21.31	SERVICIOS ADICIONALES - ÁREA NO PAGA
R-04	SERVICIOS ADICIONALES - CONTROL DE ACCESO BAÑOS PÚBLICOS	4.39	SERVICIOS ADICIONALES - ÁREA NO PAGA
R-05-1	SERVICIOS ADICIONALES - CUARTO DE LIMPIEZA	4.85	SERVICIOS ADICIONALES - ÁREA NO PAGA
R-102	SERVICIOS ADICIONALES - ÁREA DE SERVICIO	363.03	SERVICIOS ADICIONALES - ÁREA NO PAGA
T-20-G	MEDIDORES (GAS)	9.07	ÁREA TÉCNICA
T-20-L-2	MEDIDORES (LUZ)	9.60	ÁREA TÉCNICA
T-20-W-2	MEDIDORES (AGUA)	9.08	ÁREA TÉCNICA
T-21-3	ÁREA DE INSPECCIÓN	24.19	ÁREA TÉCNICA
		789.28	
ARQ_PL_00.2_ACCESO			
R-01	SERVICIOS ADICIONALES - CUARTO DE BASURAS PARA METRO	9.35	SERVICIOS ADICIONALES - ÁREA NO PAGA
R-05-2	SERVICIOS ADICIONALES - CUARTO DE LIMPIEZA	8.47	SERVICIOS ADICIONALES - ÁREA NO PAGA
R-06	SERVICIOS ADICIONALES - BAÑOS EMPLEADOS MUJERES	20.96	SERVICIOS ADICIONALES - ÁREA NO PAGA
R-07	SERVICIOS ADICIONALES - VESTIDORES EMPLEADOS MUJERES	8.97	SERVICIOS ADICIONALES - ÁREA NO PAGA
R-08	SERVICIOS ADICIONALES - BAÑOS EMPLEADOS HOMBRES	18.98	SERVICIOS ADICIONALES - ÁREA NO PAGA
R-09	SERVICIOS ADICIONALES - VESTIDORES EMPLEADOS HOMBRES	9.64	SERVICIOS ADICIONALES - ÁREA NO PAGA
R-10	SERVICIOS ADICIONALES - SALA DE EMPLEADOS	13.38	SERVICIOS ADICIONALES - ÁREA NO PAGA
R-103	SERVICIOS ADICIONALES - ÁREA DE SERVICIO	71.82	SERVICIOS ADICIONALES - ÁREA NO PAGA
R-201	SERVICIOS ADICIONALES - ÁREA DE COMIDAS	60.44	SERVICIOS ADICIONALES - ÁREA NO PAGA
T-08-2	CENTRO DE TRANSFORMACIÓN ENEL-CODENSA (CT)_CUARTO BAJA TENSIÓN	11.16	ÁREA TÉCNICA
T-08-3	CENTRO DE TRANSFORMACIÓN ENEL-CODENSA (CT)_CUARTO MEDIA TENSIÓN	49.24	ÁREA TÉCNICA
T-25-2	NODO DE ACCESO DE TELECOMUNICACIONES	7.99	ÁREA TÉCNICA
T-30	SISTEMA PROTECCIÓN CONTRA INCENDIO ENEL	5.61	ÁREA TÉCNICA
		296.03	

TABLA DE ÁREAS ÚTILES (NIVEL ACCESO)

CÓDIGO	NOMBRE	ÁREA (m²)	DEPARTAMENTO
ARQ_PL_00.3_ACCESO			
R-00-3	SERVICIOS ADICIONALES - CORREDOR OPERATIVO	63.76	SERVICIOS ADICIONALES - ÁREA NO PAGA
R-104	SERVICIOS ADICIONALES - ÁREA DE SERVICIO	164.57	SERVICIOS ADICIONALES - ÁREA NO PAGA
R-105	SERVICIOS ADICIONALES - ÁREA DE SERVICIO	53.80	SERVICIOS ADICIONALES - ÁREA NO PAGA
R-202	SERVICIOS ADICIONALES - ÁREA DE COMIDAS	45.46	SERVICIOS ADICIONALES - ÁREA NO PAGA
R-203	SERVICIOS ADICIONALES - ÁREA DE COMIDAS	50.78	SERVICIOS ADICIONALES - ÁREA NO PAGA
R-204	SERVICIOS ADICIONALES - ÁREA DE COMIDAS	67.50	SERVICIOS ADICIONALES - ÁREA NO PAGA
T-20-L-3	MEDIDORES (LUZ)	10.09	ÁREA TÉCNICA
T-20-W-3	MEDIDORES (AGUA)	8.72	ÁREA TÉCNICA
T-21-4	ÁREA DE INSPECCIÓN	28.31	ÁREA TÉCNICA
T-21-5	ÁREA DE INSPECCIÓN	22.33	ÁREA TÉCNICA
		515.32	
ARQ_PL_01_ACCESO			
NPA-03	ÁREA NO PAGA	110.26	ÁREA NO PAGA
R-106	SERVICIOS ADICIONALES - ÁREA DE SERVICIO	32.11	SERVICIOS ADICIONALES - ÁREA NO PAGA
T-25-3	NODO DE ACCESO DE TELECOMUNICACIONES	4.18	ÁREA TÉCNICA
		146.55	
TOTAL NIVEL ACCESO		3539.07	

TABLA DE ÁREAS ÚTILES POR DEPARTAMENTO (NIVEL ACCESO)

DEPARTAMENTO	ÁREA (m²)
SERVICIOS ADICIONALES - ÁREA NO PAGA	2374.61
ÁREA CULTURAL	14.76
ÁREA NO PAGA	688.97
ÁREA TÉCNICA	460.72
TOTAL NIVEL ACCESO	3539.07

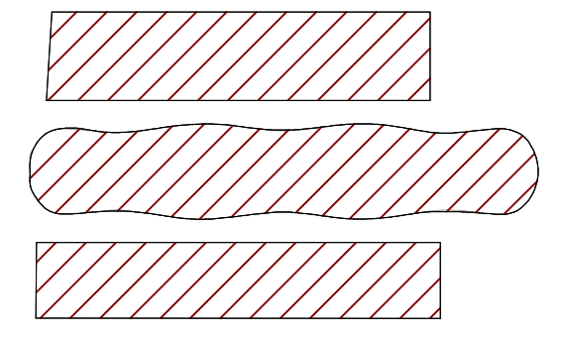

PLANO CLAVE ESTACIÓN 10

VÁLIDO PARA CONSTRUCCIÓN
20-03-26

LOCALIZACIÓN

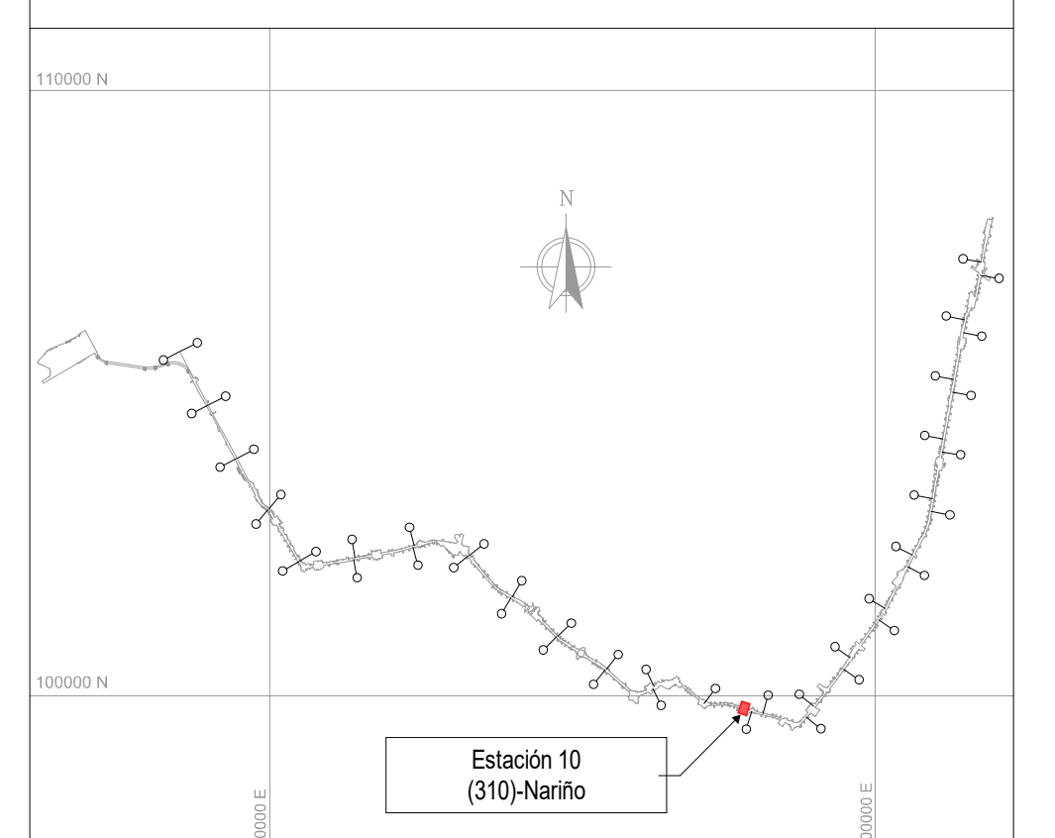

NOTAS

01. TODAS LAS DIMENSIONES ESTÁN CONFIGURADAS EN METROS A MENOS QUE SE INDIQUE UNA UNIDAD DE MEDIDA DIFERENTE.
02. TODAS LAS MEDIDAS, UBICACIÓN Y NIVELES DEBEN VERIFICARSE EN EL LUGAR DE CONSTRUCCIÓN.
03. NIVEL DE ACCESO AL EDIFICIO PL 01 CORRESPONDE AL +0.00m DE LA ESTACIÓN Y REFERENCIA AL NIVEL 2567.10 M.S.N.M
04. LOS NOMBRES ESPECÍFICOS DE LAS ÁREAS PUEDEN SER CONSULTADAS EN EL PLANO NO. 3 Ó EN LAS VISTAS EN PLANTA.
05. LOS COLORES QUE SE MUESTRAN EN LOS PLANOS COMO PROYECCIÓN DE ELEMENTOS ARQUITECTÓNICOS COMO CUBIERTAS FACHADAS MUROS ETC. NO REPRESENTAN LA MATERIALIDAD Y REALIDAD DE ACABADOS DEL PROYECTO, SOLO SON INDICATIVOS PARA REALIZAR UNA CORRECTA LECTURA DE LA PLANIMETRÍA.
06. LAS ESCALERAS ELÉCTRICAS INDICAN SU SENTIDO CON LA SIGUIENTE NOMENCLATURA: "SUBE" Y "BAJA".
07. SE DEBEN REVISAR LOS NIVELES ESTRUCTURALES PARA NIVEL DE ACCESO PL_01 Y SUBNIVELES, PL_02 (INTERMEDIO), PL_03 (PLATAFORMA) CON LA PLANIMETRÍA DE PLACAS ESTRUCTURALES EN LOS ENTREGABLES L1T1-1300-410-CON-ED-EST-PL-0069, 70, 71, 72, 107, 108, 109, 110, 111, 112, 113, 114, 115, RESPECTIVAMENTE. EL NIVEL ESTRUCTURAL (NE) REFERENCIA LOS ESPACIOS DONDE SE DEBE ACONDICIONAR EL ACABADO DE PISO SEGÚN CORRESPONDA, CON LOS NIVELES DE PISO TERMINADO (NPT). LOS NIVELES PROYECTADOS DE EMPATE (NPE) EN LAS ÁREAS DE SERVICIOS ADICIONALES, REFERENCIAN LA ADECUACIÓN DE LOS DESNIVELES EN ESTAS ÁREAS; QUEDA COMO RESPONSABILIDAD DEL LOCATARIO DEFINIR Y ACONDICIONAR ESTE ACABADO DE PISO (NPE) EN LÍNEA CON EL NIVEL (NPT) DE ESPACIOS COLINDANTES. EL NIVEL ESTRUCTURAL (NE) SE ENCUENTRA A (- 0.10M) POR DEBAJO DE LOS NIVELES DE PISO TERMINADO (NPT) Y LOS NIVELES PROYECTADOS DE EMPATE (NPE) MARCADOS EN LA PLANIMETRÍA.

- ARQ_PL_00 = SÓTANO /NPT -6.80
- ARQ_PL_00.1 = ACCESO /NPT -0.50
- ARQ_PL_00.2 = ACCESO /NPT -0.30
- ARQ_PL_00.3 = ACCESO /NPT -0.20
- ARQ_PL_00.4 = ACCESO /NPT -0.10
- ARQ_PL_01 = ACCESO /NPT 0.00
- ARQ_PL_02 = INTERMEDIO /NPT 6.60
- ARQ_PL_02.2 = TOPE DE RIEL /NPT 14.20
- ARQ_PL_03 = PLATAFORMA /NPT 15.34
- ARQ_PL_04 = CUBIERTA EDIFICACIONES /NPT 21.94
- ARQ_PL_05 = CUBIERTA NAVE CENTRAL /NPT 24.59

CONVENCIONES

- ▬ ▬ ▬ LÍMITE DE INTERVENCIÓN
- ▬ ▬ ▬ HUELLA APÉNDICE TÉCNICO
- ■ MURO DIVISORIO
- — — — PROYECCIÓN NIVEL SUPERIOR

🟩	SERVICIOS ADICIONALES - ÁREA NO PAGA	🟨	ÁREA NO PAGA
🟩	SERVICIOS ADICIONALES - ÁREA PAGA	🟦	ÁREA OPERATIVA
🟩	SERVICIO PÚBLICO	🟧	ÁREA PAGA
🟦	ZONA DE REFUGIO	🟦	ÁREA PÚBLICA
🟥	ÁREA CULTURAL	⬜	ÁREA TÉCNICA

No.	PLANOS DE REFERENCIA	REV.

No.	MODELO BIM DE REFERENCIA	REV.
1	L1T1-1100-210-CON-ED-EST-MO-0001.rvt	V00
2	L1T1-1100-211-CON-ED-EST-MO-0001.rvt	V00
3	L1T1-1100-310-CON-ED-EST-MO-0001.rvt	V00
4	L1T1-1150-210-CON-ED-EST-MO-0001.rvt	V00
5	L1T1-1150-211-CON-ED-EST-MO-0001.rvt	V00
6	L1T1-1150-310-CON-ED-EST-MO-0001.rvt	V00
7	L1T1-1200-310-CON-ED-EST-MO-0001.rvt	V00
8	L1T1-1300-410-CON-ED-EST-MO-0001.rvt	V00
9	L1T1-1300-410-CON-ED-EST-MO-0002.rvt	V00
10	L1T1-1310-410-CON-ED-EST-MO-0001.rvt	V00
11	L1T1-1410-310-CON-ED-MEC-MO-0001.rvt	V00
12	L1T1-1420-310-CON-ED-MEC-MO-0001.rvt	V00
13	L1T1-5160-310-CON-ED-EST-MO-0001.rvt	V00
14	L1T1-5160-310-CON-ED-ARQ-MO-0001.rvt	V00
15	L1T1-5300-310-CON-ED-MEC-MO-0001.rvt	V00
16	L1T1-5600-310-CON-ED-INS-MO-0001.rvt	V00
17	L1T1-1330-410-CON-ED-ARQ-MO-0011.rvt	V00
18	L1T1-1330-410-CON-ED-ARQ-MO-0012.rvt	V00

No.	PAQUETE DE TRABAJO DE REFERENCIA	REV.
1	XREF-URBANISM_CONTEXT_ST10.rvt	
2	XREF-SECONDARY-STRUCTURE-ST10.rvt	

0 2 10m
1:200

METRO BOGOTÁ
Consorcio Consultores PMO Bogotá
CONSORCIO SUPERVISOR PLMB

DISEÑÓ:
REN ZHENHUA
Licencia de Arq.nivel I (China): 1101735-614

APROBÓ:
DIEGO ERNESTO DUEÑAS
Mat.: 25202-53876 CND

REVISÓ:
CARLOS MAURICIO BARRETO BARBOSA
Mat.: A4012012-14139353

DIBUJÓ:
EQUIPO CHEC

REVISIÓN No.	FECHA	DESCRIPCIÓN	REVISÓ	APROBÓ	APROBACIÓN CLIENTE
V01	20/03/2026	EMITIDO PARA CONSTRUCCIÓN	C.M.B.B	D.E.D	
V00	26/03/2025	REVISIÓN NO OBJETADA - EMITIDO PARA CONSTRUCCIÓN	F.B.R	E.O.M	
VHH	01/11/2024	EMITIDO PARA REVISIÓN Y COMENTARIOS DEL CLIENTE E INTERVENTORÍA - INCLUYE COMENTARIOS /(AJUSTES V3)	F.B.R	E.O.M	
VGG	29/07/2024	EMITIDO PARA REVISIÓN Y COMENTARIOS DEL CLIENTE E INTERVENTORÍA - INCLUYE COMENTARIOS /(AJUSTES V2)	F.B.R	E.O.M	
VFF	20/04/2023	EMITIDO PARA REVISIÓN Y COMENTARIOS DEL CLIENTE E INTERVENTORÍA - INCLUYE COMENTARIOS /(AJUSTES)	J.E.M	M.B.M	
VEE	18/12/2022	EMITIDO PARA REVISIÓN Y COMENTARIOS DEL CLIENTE E INTERVENTORÍA - INCLUYE COMENTARIOS /(NO APLICA)	J.E.M	M.B.M	
VDD	01/12/2022	EMITIDO PARA REVISIÓN Y COMENTARIOS DEL CLIENTE E INTERVENTORÍA - INCLUYE COMENTARIOS /(90% ACCESOS)	J.E.M	M.B.M	
VCC	22/08/2022	EMITIDO PARA REVISIÓN Y COMENTARIOS DEL CLIENTE E INTERVENTORÍA - INCLUYE COMENTARIOS /(NO APLICA)	J.E.M	M.B.M	
VBB	06/12/2021	EMITIDO PARA REVISIÓN Y COMENTARIOS DEL CLIENTE E INTERVENTORÍA	J.E.M	M.B.M	
VA0	05/12/2021	EMITIDO PARA COMENTARIOS INTERNOS - EMISIÓN PRELIMINAR PARA COMENTARIOS	J.E.M	M.B.M	

METRO LÍNEA 1

DIRECTOR DE INTERVENTORÍA:
JAVIER DESCARGA N.
Mat.:25202-68697 CND

ESPECIALISTA INTERVENTORÍA:
CARLOS ALBERTO HOYOS SOTO
Mat.:A25072000-14251682

FECHA:
MARZO 2026

METRO LÍNEA 1
CONTRATO DE CONCESIÓN No. 163 DE 2019

PROYECTO PRIMERA LÍNEA DEL METRO DE BOGOTÁ - TRAMO 1

INFRAESTRUCTURA VIAL

ARQUITECTURA

ESTACIÓN METRO 10 (NARIÑO)
GENERAL
VISTA EN PLANTA Y 3D - NIVEL ACCESO

PLANCHA No: L1T1-0000-310-CON-ED-ARQ-PL-0001_05_V01
ARCHIVO: L1T1-0000-310-CON-ED-ARQ-MO-0001_V00.rvt
ESCALA: INDICADA
FECHA: DICIEMBRE 2021
REVISIÓN No. V01
PLANO No. 05 DE 96