L1T1-CON-CAL-FR-0120 - B1 : 1000x707mm

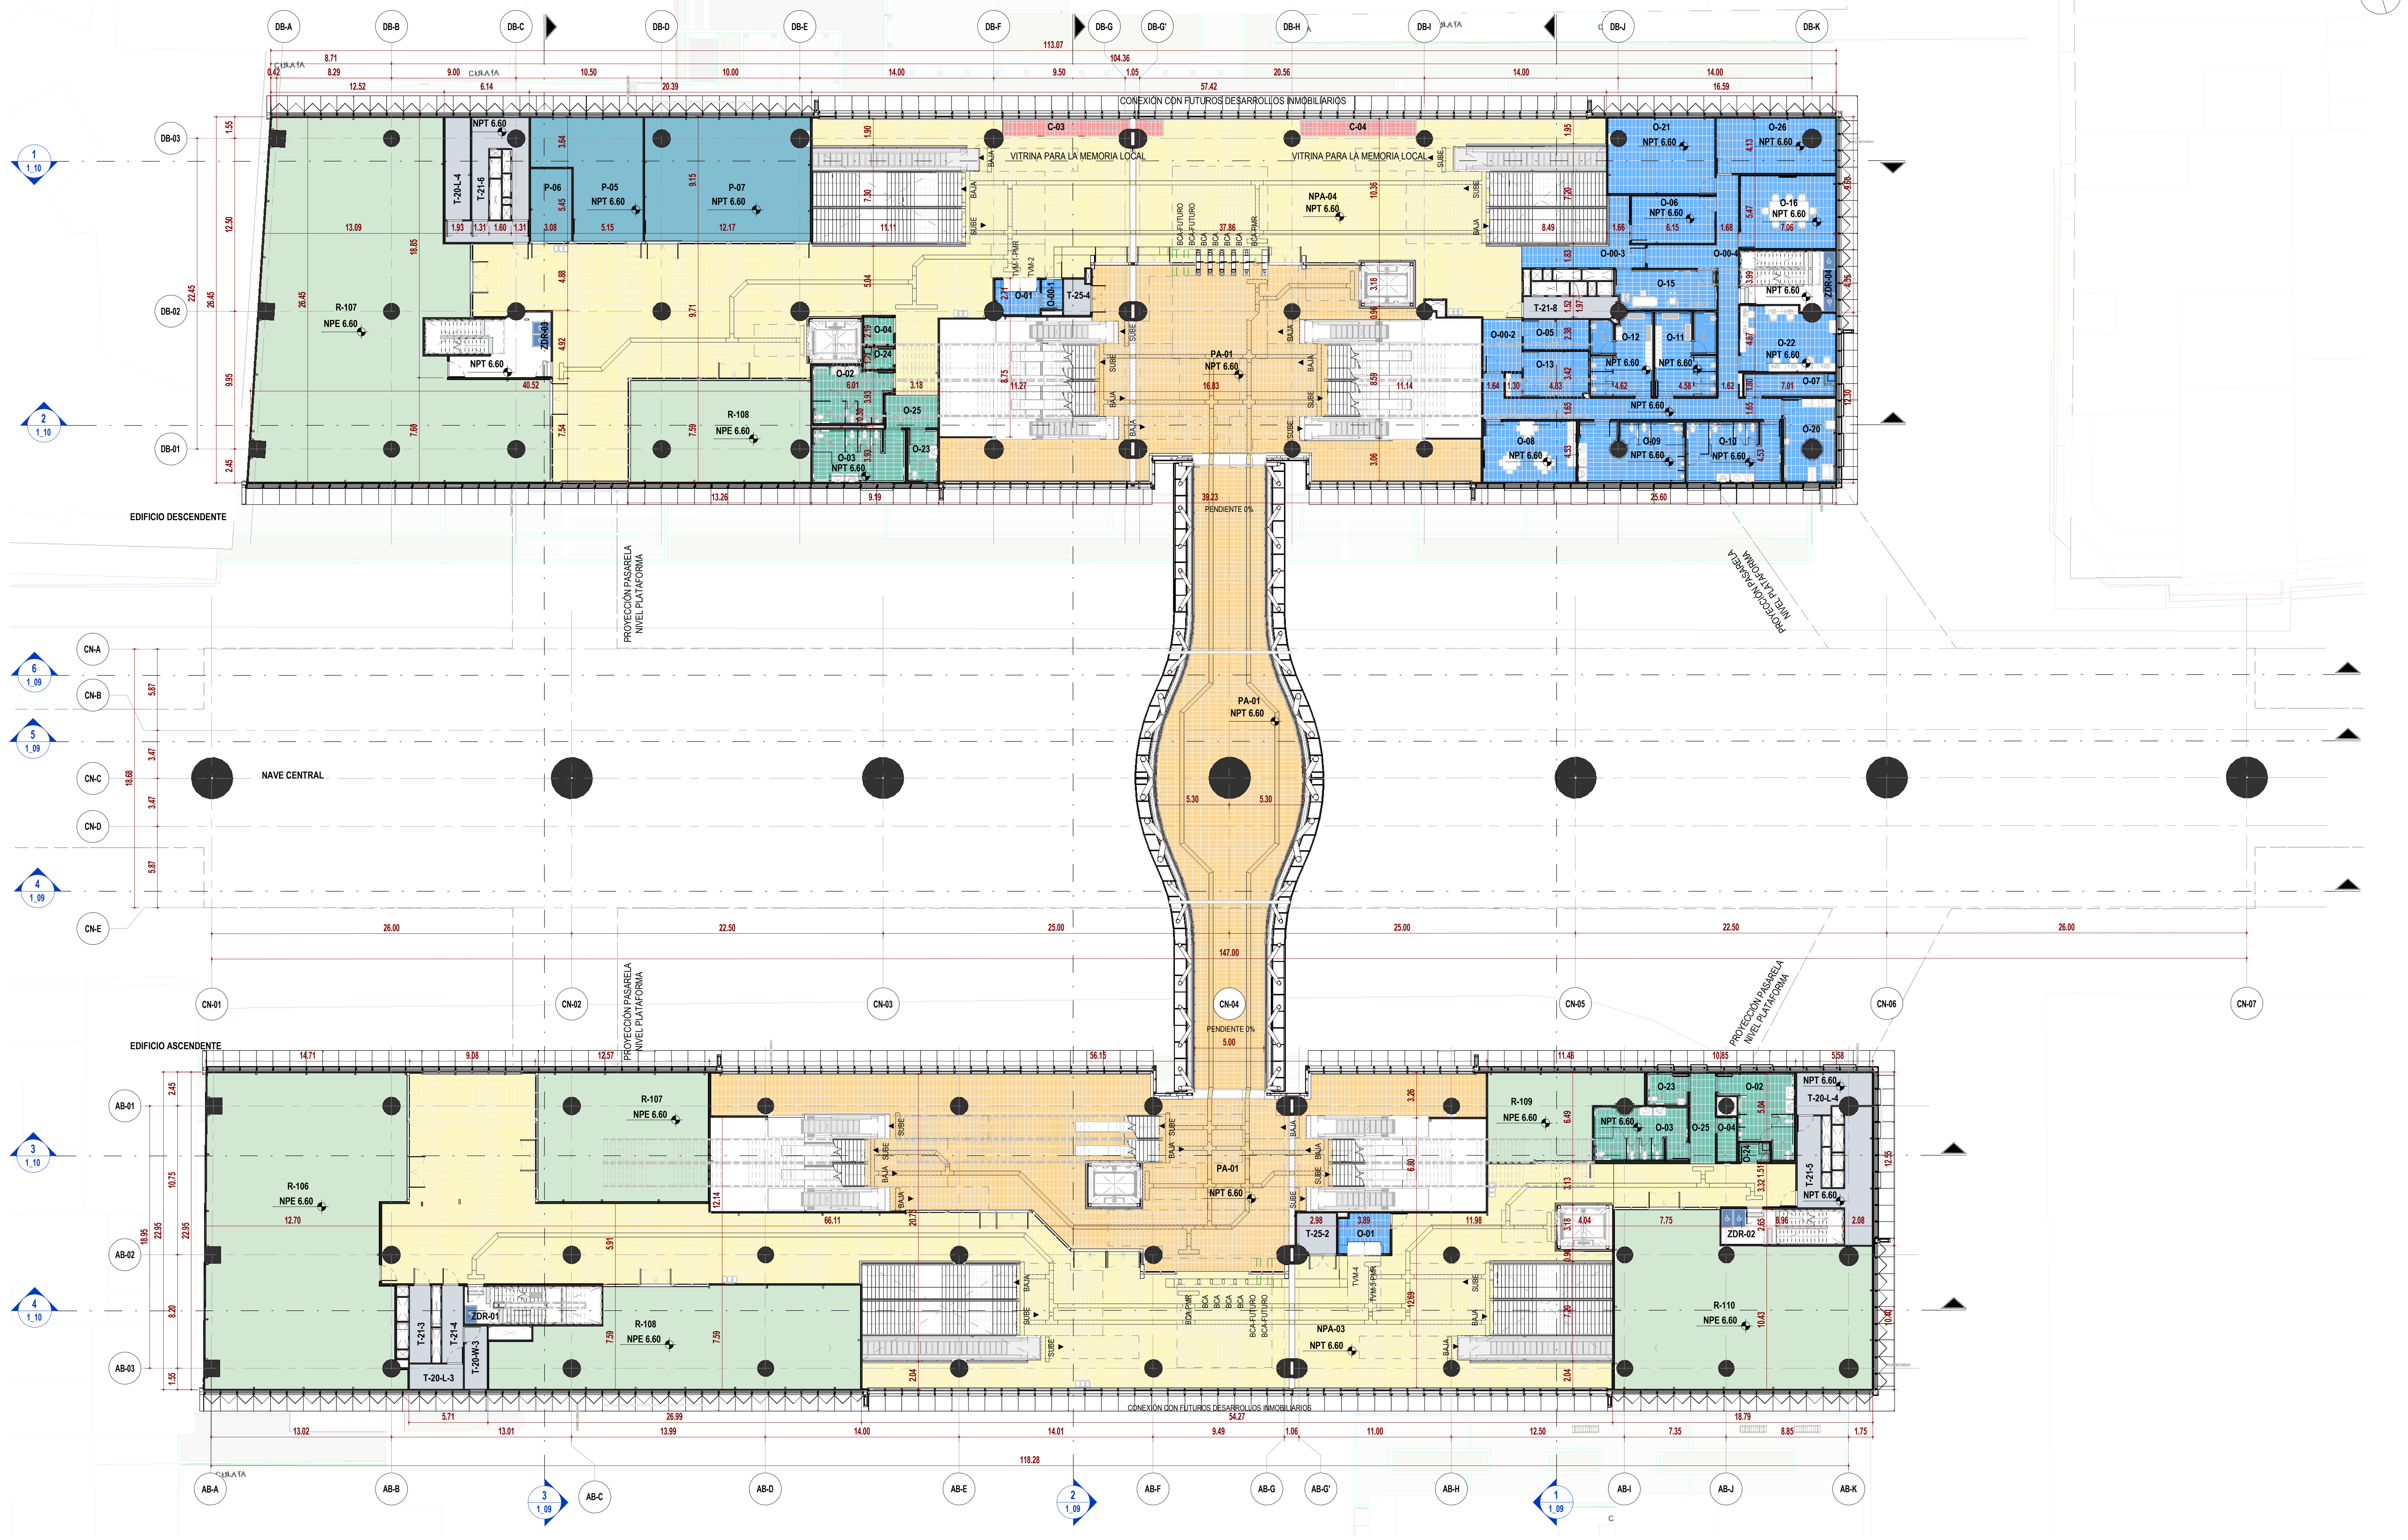
EDIFICIO DESCENDENTE
EDIFICIO ASCENDENTE
NAVE CENTRAL
PROYECCIÓN PASARELA NIVEL PLATAFORMA
CONEXIÓN CON FUTUROS DESARROLLOS INMOBILIARIOS
VITRINA PARA LA MEMORIA LOCAL
NPT 6.60
PA-01
NPA-03
NPA-04
R-106
R-107
R-108
R-109
R-110
C-03
C-04
NP

2 NIVEL INTERMEDIO_GENERAL
ESC.: 1 : 200

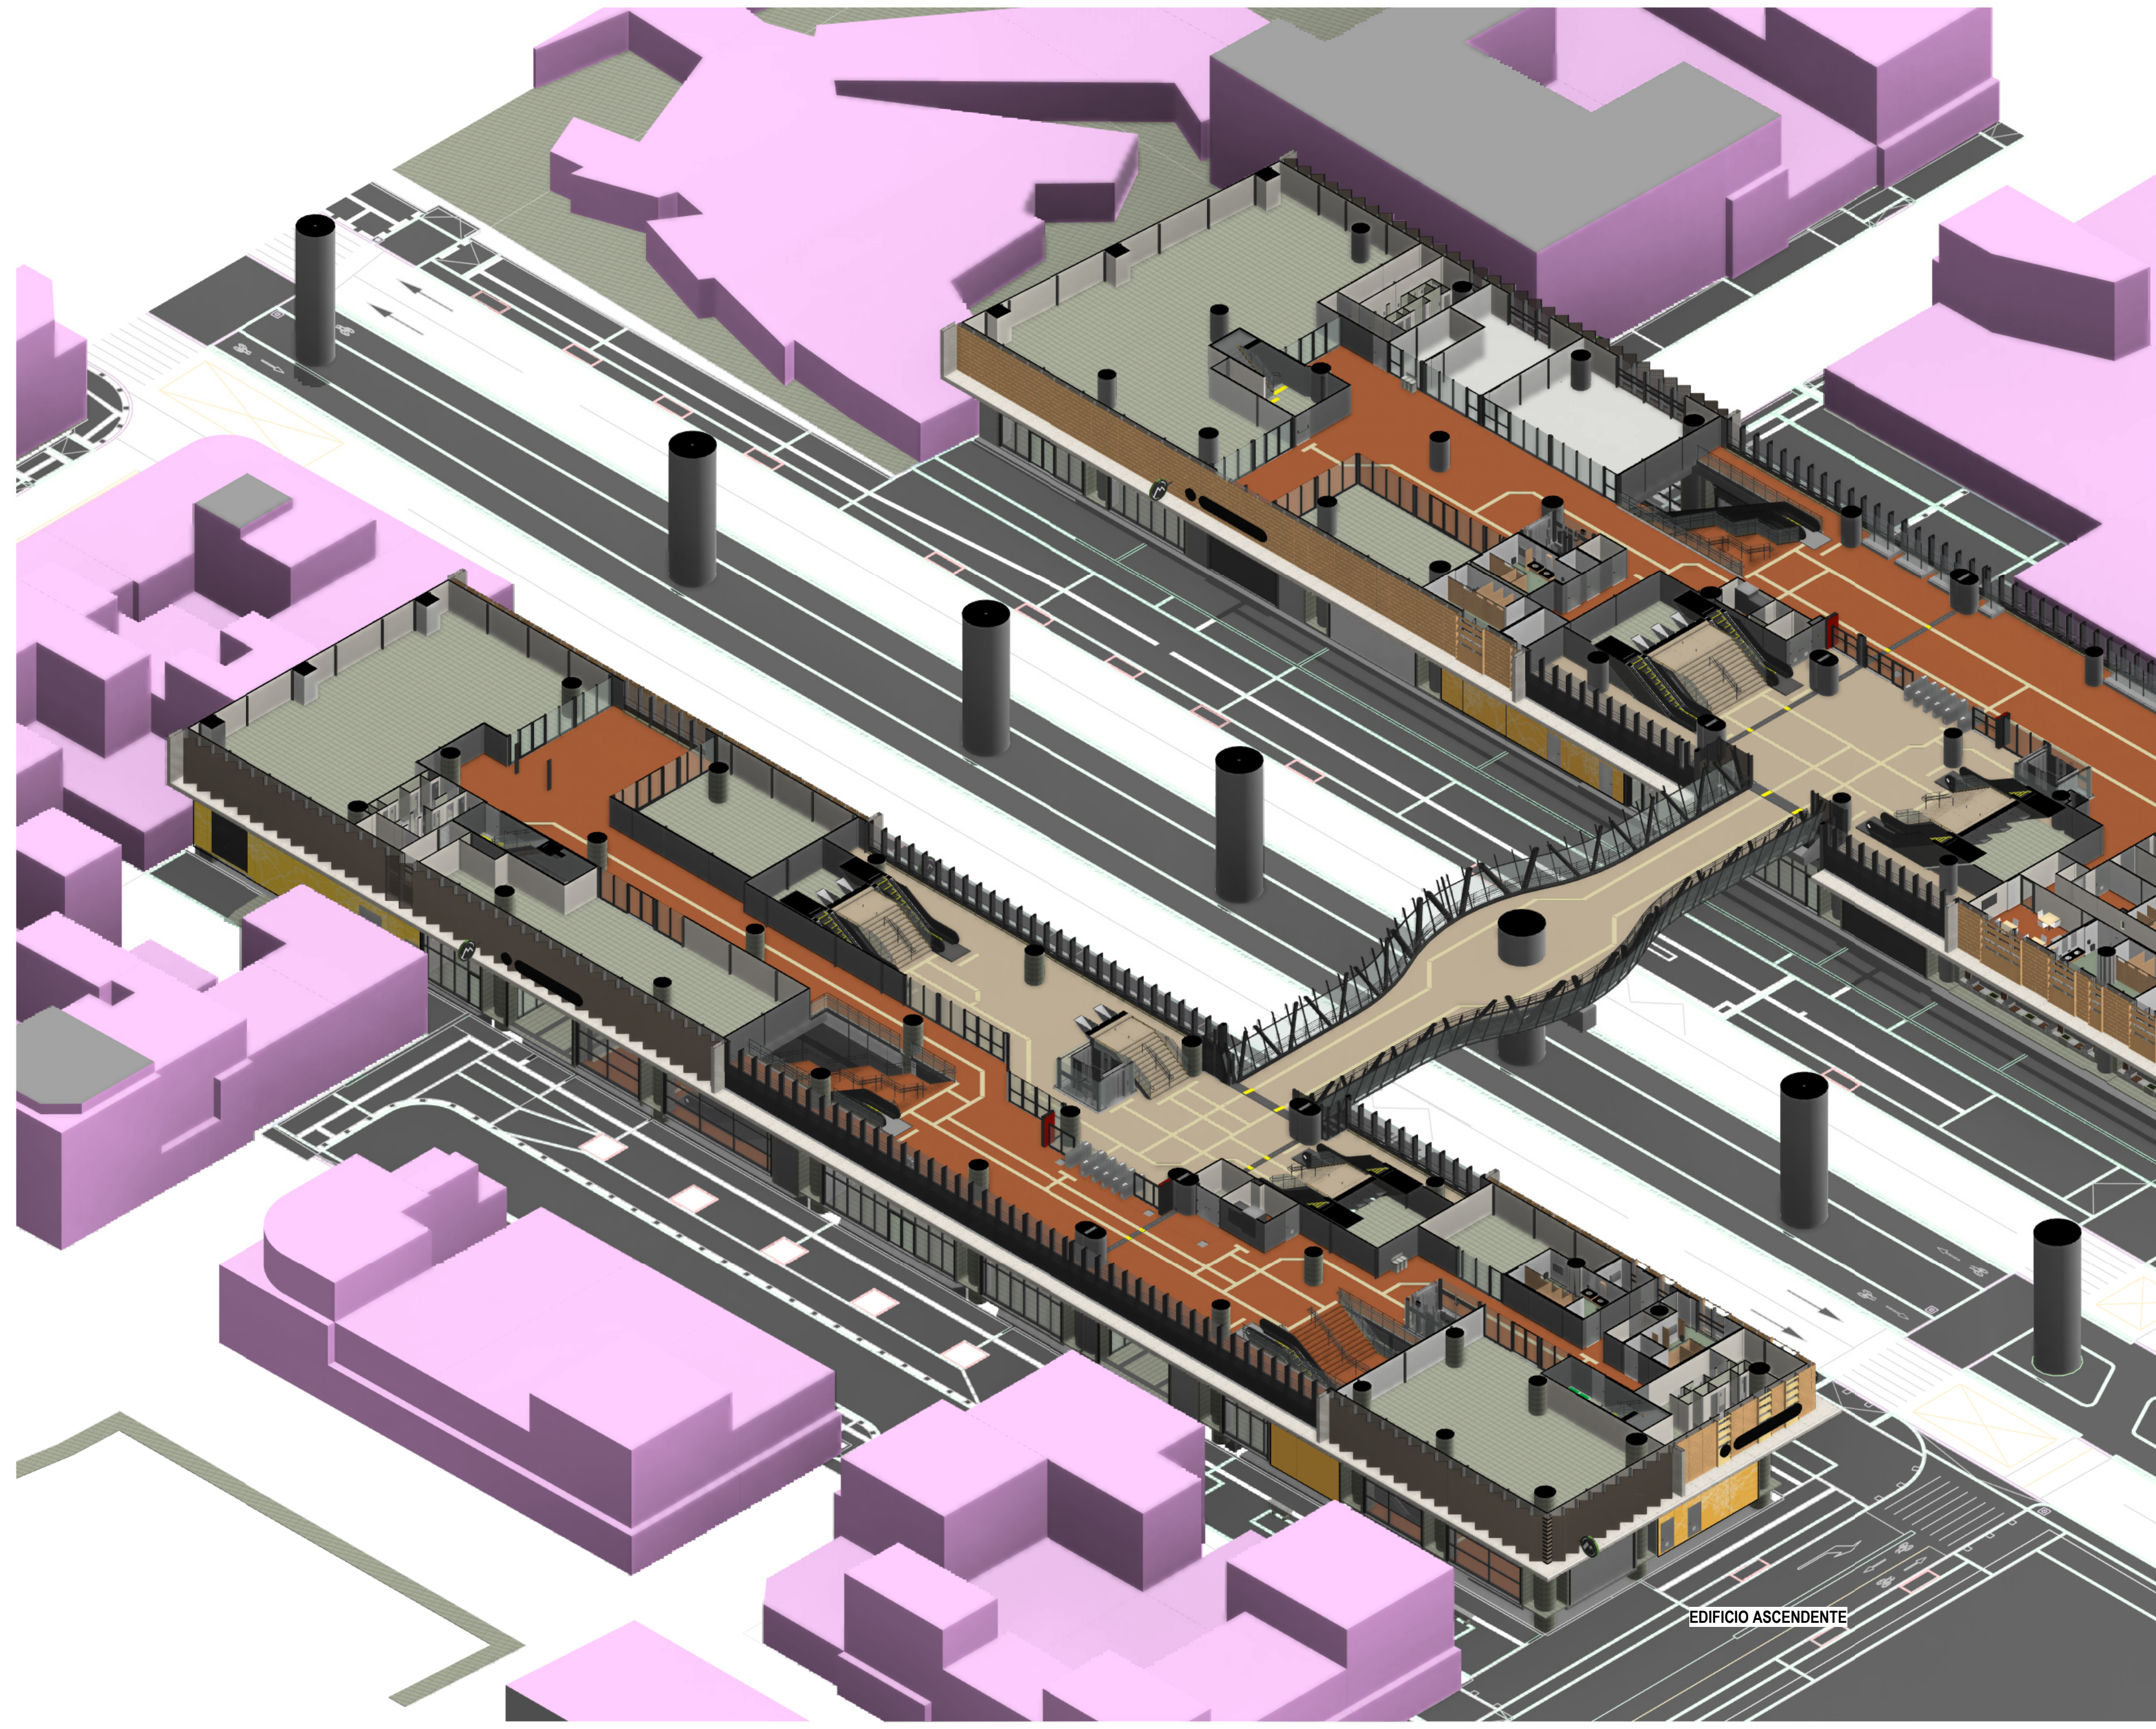

1 3D_NIVEL INTERMEDIO_GENERAL
ESC: N/A

TABLA DE ÁREAS ÚTILES (NIVEL INTERMEDIO)

CÓDIGO	NOMBRE	ÁREA (m²)	DEPARTAMENTO
EDIFICIO ASCENDENTE			
ARQ_PL_02_INTERMEDIO			
NPA-03	ÁREA NO PAGA	727.58	ÁREA NO PAGA
NPA-04	ÁREA NO PAGA	41.28	ÁREA NO PAGA
O-01	VENTA AUTOMÁTICA DE BOLETOS	10.78	ÁREA OPERATIVA
O-02	BAÑOS PÚBLICOS DE HOMBRES	24.19	SERVICIO PÚBLICO
O-03	BAÑOS PÚBLICOS DE MUJERES	25.36	SERVICIO PÚBLICO
O-04	CONTROL DE ACCESO BAÑOS PÚBLICOS	4.65	SERVICIO PÚBLICO
O-23	BAÑO PÚBLICO - FAMILIAR	6.62	SERVICIO PÚBLICO
O-24	CUARTO DE LIMPIEZA DE BAÑOS PÚBLICOS	2.91	SERVICIO PÚBLICO
O-25	BAÑO PÚBLICO - CORREDOR OPERACIONAL	11.91	SERVICIO PÚBLICO
PA-01	ÁREA PAGA	406.25	ÁREA PAGA
R-106	SERVICIOS ADICIONALES - ÁREA DE SERVICIO	309.60	SERVICIOS ADICIONALES - ÁREA NO PAGA
R-107	SERVICIOS ADICIONALES - ÁREA DE SERVICIO	112.69	SERVICIOS ADICIONALES - ÁREA NO PAGA
R-108	SERVICIOS ADICIONALES - ÁREA DE SERVICIO	169.96	SERVICIOS ADICIONALES - ÁREA NO PAGA
R-109	SERVICIOS ADICIONALES - ÁREA DE SERVICIO	56.31	SERVICIOS ADICIONALES - ÁREA NO PAGA
R-110	SERVICIOS ADICIONALES - ÁREA DE SERVICIO	204.09	SERVICIOS ADICIONALES - ÁREA NO PAGA
T-20-L-3	MEDIDORES (LUZ)	6.88	ÁREA TÉCNICA
T-20-L-4	MEDIDORES (LUZ)	13.61	ÁREA TÉCNICA
T-20-W-3	MEDIDORES (AGUA)	7.45	ÁREA TÉCNICA
T-21-3	ÁREA DE INSPECCIÓN	8.49	ÁREA TÉCNICA
T-21-4	ÁREA DE INSPECCIÓN	8.40	ÁREA TÉCNICA
T-21-5	ÁREA DE INSPECCIÓN	32.87	ÁREA TÉCNICA
T-25-2	NODO DE ACCESO DE TELECOMUNICACIONES	8.04	ÁREA TÉCNICA
ZDR-01	ZONA DE REFUGIO (PMR)	1.21	ZONA DE REFUGIO
ZDR-02	ZONA DE REFUGIO (PMR)	2.43	ZONA DE REFUGIO
		2203.59	
EDIFICIO DESCENDENTE			
ARQ_PL_02_INTERMEDIO			
C-03	ÁREAS DE USO CULTURAL	13.01	ÁREA CULTURAL
C-04	ÁREAS DE USO CULTURAL	10.15	ÁREA CULTURAL
NPA-04	ÁREA NO PAGA	757.99	ÁREA NO PAGA
O-00-1	CIRCULACIÓN ÁREAS OPERATIVAS	3.27	ÁREA OPERATIVA
O-00-2	CIRCULACIÓN ÁREAS OPERATIVAS	10.59	ÁREA OPERATIVA
O-00-3	CIRCULACIÓN ÁREAS OPERATIVAS	19.75	ÁREA OPERATIVA
O-00-4	CIRCULACIÓN ÁREAS OPERATIVAS	69.76	ÁREA OPERATIVA
O-01	VENTA AUTOMÁTICA DE BOLETOS	7.90	ÁREA OPERATIVA
O-02	BAÑOS PÚBLICOS DE HOMBRES	21.53	SERVICIO PÚBLICO
O-03	BAÑOS PÚBLICOS DE MUJERES	24.80	SERVICIO PÚBLICO
O-04	CONTROL DE ACCESO BAÑOS PÚBLICOS	4.24	SERVICIO PÚBLICO
O-05	LOCAL DE INFORMACIÓN	10.09	ÁREA OPERATIVA
O-06	OFICINA DEL SUPERVISOR DE LA ESTACIÓN	20.58	ÁREA OPERATIVA
O-07	CUARTO DE LIMPIEZA	10.72	ÁREA OPERATIVA

TABLA DE ÁREAS ÚTILES (NIVEL INTERMEDIO)

CÓDIGO	NOMBRE	ÁREA (m²)	DEPARTAMENTO
O-08	SALA DE DESCANSO PARA EMPLEADOS	29.58	ÁREA OPERATIVA
O-09	BAÑOS EMPLEADOS HOMBRES	31.53	ÁREA OPERATIVA
O-10	BAÑOS EMPLEADOS MUJERES	29.27	ÁREA OPERATIVA
O-11	VESTIDORES EMPLEADOS HOMBRES	26.44	ÁREA OPERATIVA
O-12	VESTIDORES EMPLEADOS MUJERES	25.37	ÁREA OPERATIVA
O-13	LOCAL DE POLICÍA	15.16	ÁREA OPERATIVA
O-14	CALABOZO	2.00	ÁREA OPERATIVA
O-15	LOCAL PRIMEROS AUXILIOS	20.69	ÁREA OPERATIVA
O-16	SALA DE REUNIONES	36.10	ÁREA OPERATIVA
O-20	SALA DE LACTANCIA	21.21	ÁREA OPERATIVA
O-21	ALMACENAMIENTO DE LA ESTACIÓN	41.03	ÁREA OPERATIVA
O-22	OFICINA DE MANTENIMIENTO	30.68	ÁREA OPERATIVA
O-23	BAÑO PÚBLICO - FAMILIAR	7.78	SERVICIO PÚBLICO
O-24	CUARTO DE LIMPIEZA DE BAÑOS PÚBLICOS	3.32	SERVICIO PÚBLICO
O-25	BAÑO PÚBLICO - CORREDOR OPERACIONAL	9.01	SERVICIO PÚBLICO
O-26	ALMACENAMIENTO DE BASURAS METRO	33.17	ÁREA OPERATIVA
P-05	BIBLIOMETRO	55.30	ÁREA PÚBLICA
P-06	ESPACIO IPES (INSTITUTO PARA LA ECONOMÍA SOCIAL)	15.24	ÁREA PÚBLICA
P-07	SALÓN MÚLTIPLE EMB	103.30	ÁREA PÚBLICA
PA-01	ÁREA PAGA	296.97	ÁREA PAGA
R-107	SERVICIOS ADICIONALES - ÁREA DE SERVICIO	404.08	SERVICIOS ADICIONALES - ÁREA NO PAGA
R-108	SERVICIOS ADICIONALES - ÁREA DE SERVICIO	93.35	SERVICIOS ADICIONALES - ÁREA NO PAGA
T-20-L-4	MEDIDORES (LUZ)	13.38	ÁREA TÉCNICA
T-21-6	ÁREA DE INSPECCIÓN	20.07	ÁREA TÉCNICA
T-21-7	ÁREA DE INSPECCIÓN	9.17	ÁREA TÉCNICA
T-21-8	ÁREA DE INSPECCIÓN	9.98	ÁREA TÉCNICA
T-25-4	NODO DE ACCESO DE TELECOMUNICACIONES	4.71	ÁREA TÉCNICA
ZDR-03	ZONA DE REFUGIO (PMR)	2.43	ZONA DE REFUGIO
ZDR-04	ZONA DE REFUGIO (PMR)	3.95	ZONA DE REFUGIO
		2378.64	
NAVE CENTRAL			
ARQ_PL_02_INTERMEDIO			
PA-01	ÁREA PAGA	287.33	ÁREA PAGA
		287.33	
TOTAL NIVEL INTERMEDIO		4869.55	

TABLA DE ÁREAS ÚTILES POR DEPARTAMENTO (NIVEL INTERMEDIO)

DEPARTAMENTO	ÁREA (m²)
	0.00
SERVICIO PÚBLICO	146.32
SERVICIOS ADICIONALES - ÁREA NO PAGA	1350.08
ZONA DE REFUGIO	10.03
ÁREA CULTURAL	23.16
ÁREA NO PAGA	1526.84
ÁREA OPERATIVA	505.68
ÁREA PAGA	990.55
ÁREA PÚBLICA	173.84
ÁREA TÉCNICA	143.06
TOTAL NIVEL INTERMEDIO	4869.55

LOCALIZACIÓN

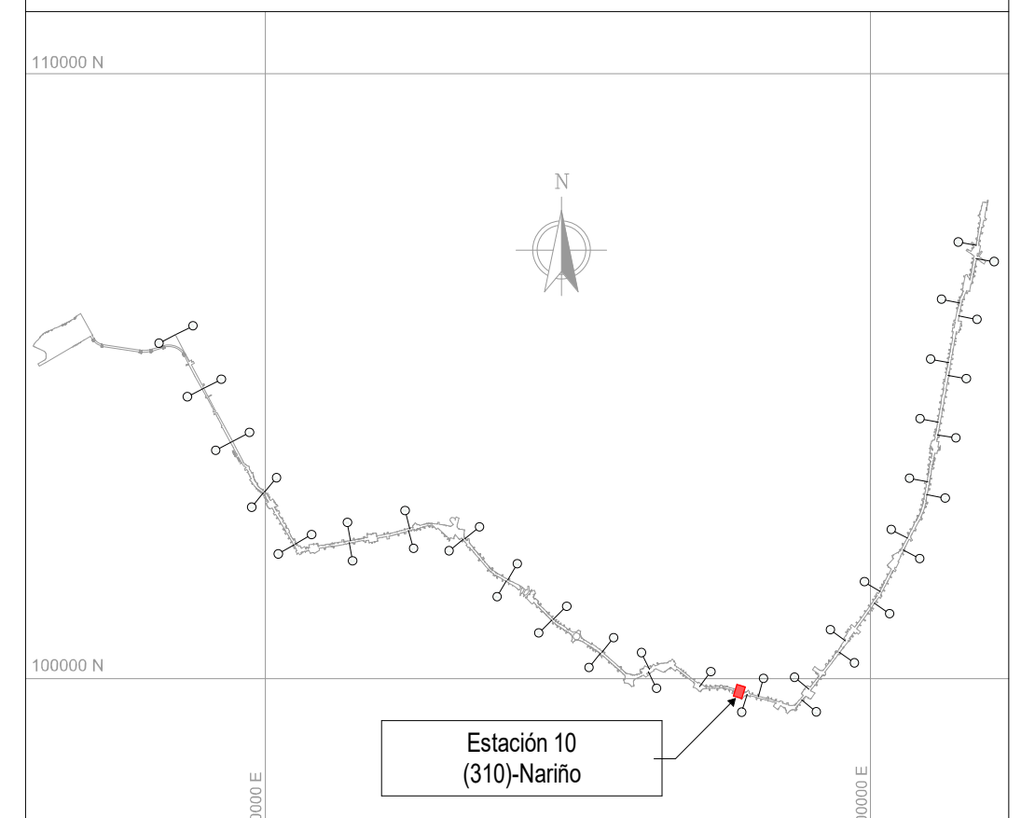

Estación 10
(310)-Nariño

NOTAS

01 TODAS LAS DIMENSIONES ESTÁN CONFIGURADAS EN METROS A MENOS QUE SE INDIQUE UNA UNIDAD DE MEDIDA DIFERENTE.

02 TODAS LAS MEDIDAS, UBICACIÓN Y NIVELES DEBEN VERIFICARSE EN EL LUGAR DE CONSTRUCCIÓN.

03 NIVEL DE ACCESO AL EDIFICIO PL 01 CORRESPONDE AL +0.00m DE LA ESTACIÓN Y REFERENCIA AL NIVEL 2567.10 M.S.N.M

04 LOS NOMBRES ESPECÍFICOS DE LAS ÁREAS PUEDEN SER CONSULTADAS EN EL PLANO NO. 3 Ó EN LAS VISTAS EN PLANTA.

05 LOS COLORES QUE SE MUESTRAN EN LOS PLANOS COMO PROYECCIÓN DE ELEMENTOS ARQUITECTÓNICOS COMO CUBIERTAS FACHADAS MUROS ETC. NO REPRESENTAN LA MATERIALIDAD Y REALIDAD DE ACABADOS DEL PROYECTO, SOLO SON INDICATIVOS PARA REALIZAR UNA CORRECTA LECTURA DE LA PLANIMETRÍA.

06 LAS ESCALERAS ELÉCTRICAS INDICAN SU SENTIDO CON LA SIGUIENTE NOMENCLATURA: “SUBE” Y “BAJA”.

07 SE DEBEN REVISAR LOS NIVELES ESTRUCTURALES PARA NIVEL DE ACCESO PL_01 Y SUBNIVELES, PL_02 (INTERMEDIO), PL_03 (PLATAFORMA) CON LA PLANIMETRÍA DE PLACAS ESTRUCTURALES EN LOS ENTREGABLES L1T1-1300-410-CON-ED-EST-PL-0069, 70, 71, 72, 107, 108, 109, 110, 111, 112, 113, 114, 115, RESPECTIVAMENTE. EL NIVEL ESTRUCTURAL (NE) REFERENCIA LOS ESPACIOS DONDE SE DEBE ACONDICIONAR EL ACABADO DE PISO SEGÚN CORRESPONDA, CON LOS NIVELES DE PISO TERMINADO (NPT). LOS NIVELES PROYECTADOS DE EMPATE (NPE) EN LAS ÁREAS DE SERVICIOS ADICIONALES, REFERENCIAN LA ADECUACIÓN DE LOS DESNIVELES EN ESTAS ÁREAS; QUEDA COMO RESPONSABILIDAD DEL LOCATARIO DEFINIR Y ACONDICIONAR ESTE ACABADO DE PISO (NPE) EN LÍNEA CON EL NIVEL (NPT) DE ESPACIOS COLINDANTES. EL NIVEL ESTRUCTURAL (NE) SE ENCUENTRA A (- 0.10M) POR DEBAJO DE LOS NIVELES DE PISO TERMINADO (NPT) Y LOS NIVELES PROYECTADOS DE EMPATE (NPE) MARCADOS EN LA PLANIMETRÍA.

- ARQ_PL_00 = SÓTANO /NPT -6.80
- ARQ_PL_00.1 = ACCESO /NPT -0.50
- ARQ_PL_00.2 = ACCESO /NPT -0.30
- ARQ_PL_00.3 = ACCESO /NPT -0.20
- ARQ_PL_00.4 = ACCESO /NPT -0.10
- ARQ_PL_01 = ACCESO /NPT 0.00
- ARQ_PL_02 = INTERMEDIO /NPT 6.60
- ARQ_PL_02.2 = TOPE DE RIEL /NPT 14.20
- ARQ_PL_03 = PLATAFORMA /NPT 15.34
- ARQ_PL_04 = CUBIERTA EDIFICACIONES /NPT 21.94
- ARQ_PL_05 = CUBIERTA NAVE CENTRAL /NPT 24.59

CONVENCIONES

- LÍMITE DE INTERVENCIÓN
- HUELLA APÉNDICE TÉCNICO
- MURO DIVISORIO
- PROYECCIÓN NIVEL SUPERIOR

🟩	SERVICIOS ADICIONALES - ÁREA NO PAGA	🟨	ÁREA NO PAGA
🟩	SERVICIOS ADICIONALES - ÁREA PAGA	🟦	ÁREA OPERATIVA
🟩	SERVICIO PÚBLICO	🟧	ÁREA PAGA
🟦	ZONA DE REFUGIO	🟦	ÁREA PÚBLICA
🟥	ÁREA CULTURAL	⬜	ÁREA TÉCNICA

No.	PLANOS DE REFERENCIA	REV.

No.	MODELO BIM DE REFERENCIA	REV.
1	L1T1-1100-210-CON-ED-EST-MO-0001.rvt	V00
2	L1T1-1100-211-CON-ED-EST-MO-0001.rvt	V00
3	L1T1-1100-310-CON-ED-EST-MO-0001.rvt	V00
4	L1T1-1150-210-CON-ED-EST-MO-0001.rvt	V00
5	L1T1-1150-211-CON-ED-EST-MO-0001.rvt	V00
6	L1T1-1150-310-CON-ED-EST-MO-0001.rvt	V00
7	L1T1-1200-310-CON-ED-EST-MO-0001.rvt	V00
8	L1T1-1300-410-CON-ED-EST-MO-0001.rvt	V00
9	L1T1-1300-410-CON-ED-EST-MO-0002.rvt	V00
10	L1T1-1310-410-CON-ED-EST-MO-0001.rvt	V00
11	L1T1-1410-310-CON-ED-MEC-MO-0001.rvt	V00
12	L1T1-1420-310-CON-ED-MEC-MO-0001.rvt	V00
13	L1T1-5160-310-CON-ED-EST-MO-0001.rvt	V00
14	L1T1-5160-310-CON-ED-ARQ-MO-0001.rvt	V00
15	L1T1-5300-310-CON-ED-MEC-MO-0001.rvt	V00
16	L1T1-5600-310-CON-ED-INS-MO-0001.rvt	V00
17	L1T1-1330-410-CON-ED-ARQ-MO-0011.rvt	V00
18	L1T1-1330-410-CON-ED-ARQ-MO-0012.rvt	V00

No.	PAQUETE DE TRABAJO DE REFERENCIA	REV.
1	XREF-URBANISM_CONTEXT_ST10.rvt	
2	XREF-SECONDARY-STRUCTURE-ST10.rvt	

0 2 10m
1:200

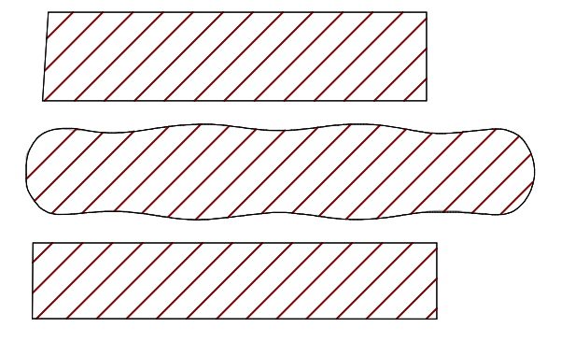

PLANO CLAVE ESTACIÓN 10

VÁLIDO PARA CONSTRUCCIÓN
20-03-26

CONSORCIO SUPERVISOR PLMB

DISEÑÓ: REN ZHENHUA Licencia de Arq.nivel I (China): 1101735-614	APROBÓ: DIEGO ERNESTO DUEÑAS Mat.: 25202-53876 CND
REVISÓ: CARLOS MAURICIO BARRETO BARBOSA Mat.: A4012012-14139353	DIBUJÓ: EQUIPO CHEC

REVISIÓN No.	FECHA	DESCRIPCIÓN	REVISÓ	APROBÓ	APROBACIÓN CLIENTE
V01	20/03/2026	EMITIDO PARA CONSTRUCCIÓN	C.M.B.B	D.E.D	
V00	26/03/2025	REVISIÓN NO OBJETADA - EMITIDO PARA CONSTRUCCIÓN	F.B.R	E.O.M	
VHH	01/11/2024	EMITIDO PARA REVISIÓN Y COMENTARIOS DEL CLIENTE E INTERVENTORÍA - INCLUYE COMENTARIOS /(AJUSTES V3)	F.B.R	E.O.M	
VGG	29/07/2024	EMITIDO PARA REVISIÓN Y COMENTARIOS DEL CLIENTE E INTERVENTORÍA - INCLUYE COMENTARIOS /(AJUSTES V2)	F.B.R	E.O.M	
VFF	20/04/2023	EMITIDO PARA REVISIÓN Y COMENTARIOS DEL CLIENTE E INTERVENTORÍA - INCLUYE COMENTARIOS /(AJUSTES)	J.E.M	M.B.M	
VEE	18/12/2022	EMITIDO PARA REVISIÓN Y COMENTARIOS DEL CLIENTE E INTERVENTORÍA - INCLUYE COMENTARIOS /(NO APLICA)	J.E.M	M.B.M	
VDD	01/12/2022	EMITIDO PARA REVISIÓN Y COMENTARIOS DEL CLIENTE E INTERVENTORÍA - INCLUYE COMENTARIOS /(90% ACCESOS)	J.E.M	M.B.M	
VCC	22/08/2022	EMITIDO PARA REVISIÓN Y COMENTARIOS DEL CLIENTE E INTERVENTORÍA - INCLUYE COMENTARIOS /(NO APLICA)	J.E.M	M.B.M	
VBB	06/12/2021	EMITIDO PARA REVISIÓN Y COMENTARIOS DEL CLIENTE E INTERVENTORÍA	J.E.M	M.B.M	
VA0	05/12/2021	EMITIDO PARA COMENTARIOS INTERNOS - EMISIÓN PRELIMINAR PARA COMENTARIOS	J.E.M	M.B.M	

METRO LÍNEA 1
CONTRATO DE CONCESIÓN No. 163 DE 2019

PROYECTO PRIMERA LÍNEA DEL METRO DE BOGOTÁ - TRAMO 1

DIRECTOR DE INTERVENTORÍA: JAVIER DESCARGA N. Mat.:25202-68697 CND	ESPECIALISTA INTERVENTORÍA: CARLOS ALBERTO HOYOS SOTO Mat.:A25072000-14251682	FECHA: MARZO 2026

INFRAESTRUCTURA VIAL

ARQUITECTURA

ESTACIÓN METRO 10 (NARIÑO)
GENERAL
VISTA EN PLANTA Y 3D - NIVEL INTERMEDIO

PLANCHA No: L1T1-0000-310-CON-ED-ARQ-PL-0001_06_V01	ESCALA: INDICADA	REVISIÓN No. V01	PLANO No. 06 DE 96
ARCHIVO: L1T1-0000-310-CON-ED-ARQ-MO-0001_V00.rvt	FECHA: DICIEMBRE 2021		