L1T1-CON-CAL-FR-0120 - B1 : 1000x707mm

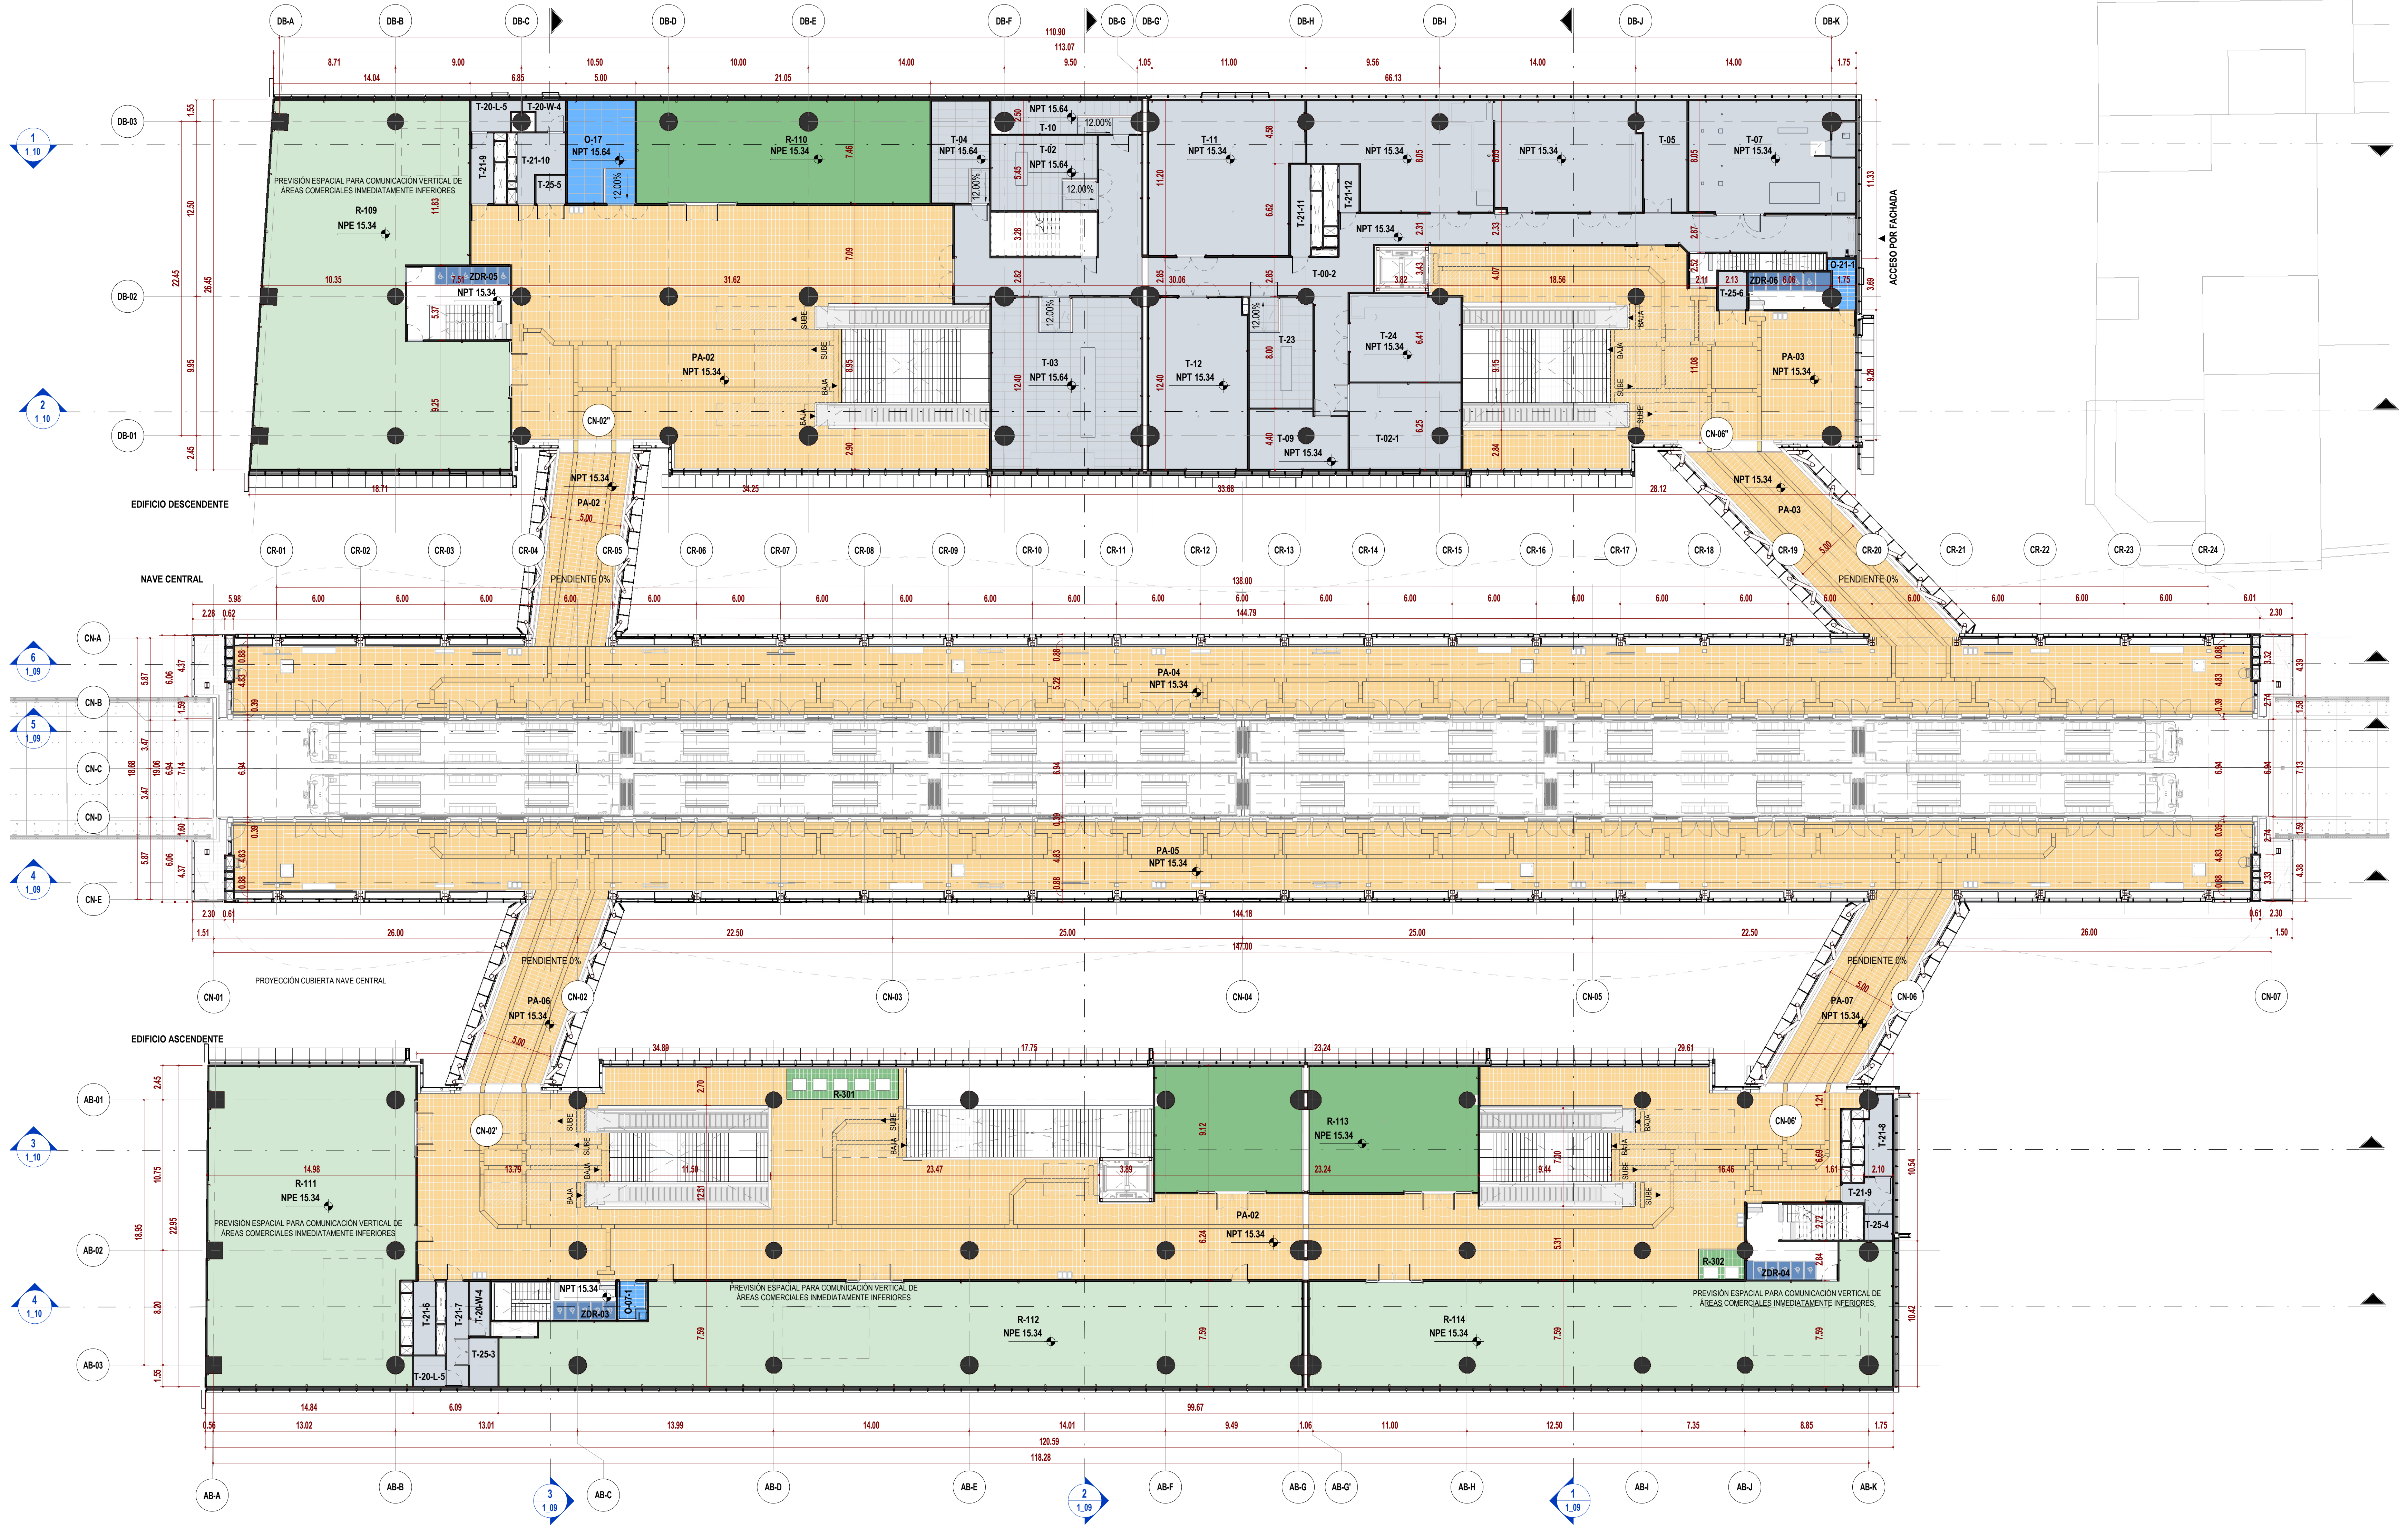

2 NIVEL PLATAFORMA_GENERAL
ESC: 1 : 200

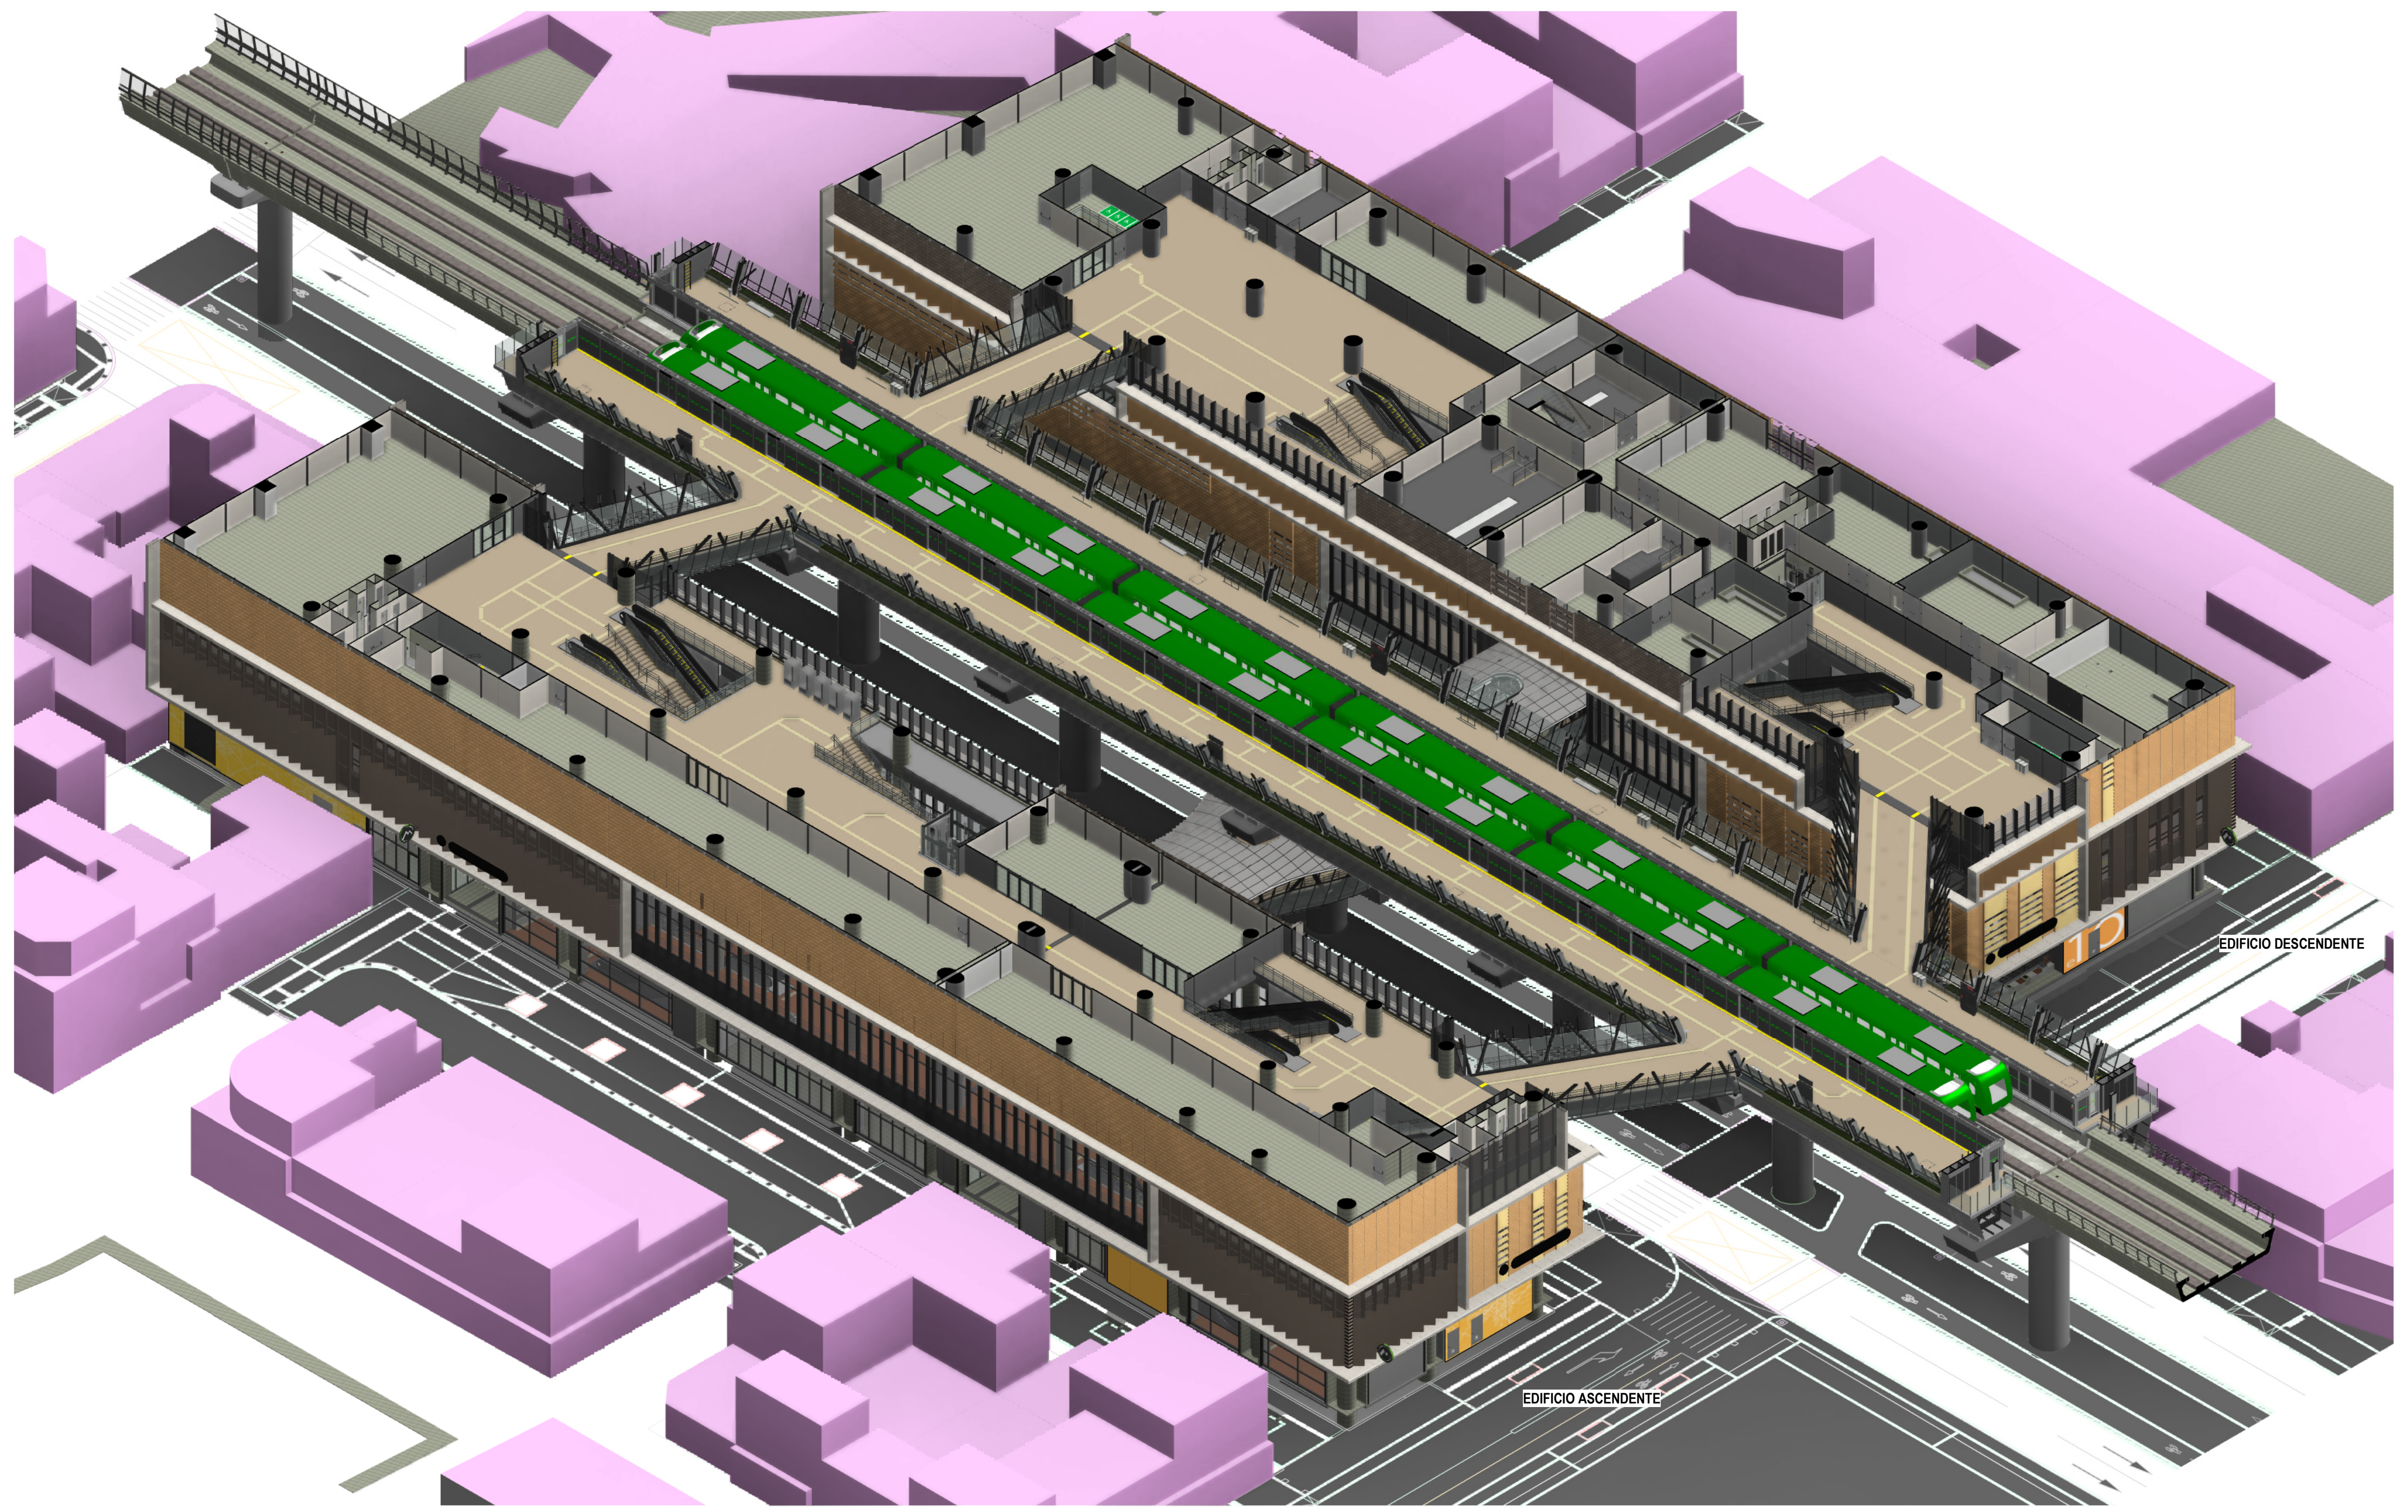

1 3D_NIVEL PLATAFORMA_GENERAL
ESC: N/A

TABLA DE ÁREAS ÚTILES (NIVEL PLATAFORMA)

EDIFICIO ASCENDENTE
ARQ_PL_03_PLATAFORMA

CÓDIGO	NOMBRE	ÁREA (m²)	DEPARTAMENTO
O-07-1	CUARTO DE LIMPIEZA COMPLEMENTARIO	5.60	ÁREA OPERATIVA
PA-02	ÁREA PAGA	920.65	ÁREA PAGA
R-111	SERVICIOS ADICIONALES - ÁREA DE SERVICIO	324.60	SERVICIOS ADICIONALES - ÁREA NO PAGA
R-112	SERVICIOS ADICIONALES - ÁREA DE SERVICIO	387.87	SERVICIOS ADICIONALES - ÁREA NO PAGA
R-113	SERVICIOS ADICIONALES - ÁREA DE SERVICIO	201.43	SERVICIOS ADICIONALES - ÁREA PAGA
R-114	SERVICIOS ADICIONALES - ÁREA DE SERVICIO	316.53	SERVICIOS ADICIONALES - ÁREA NO PAGA
R-301	SERVICIOS ADICIONALES - MÁQUINAS EXPENDEDORAS/CAJEROS AUTOMÁTICOS	17.60	SERVICIOS ADICIONALES - ÁREA PAGA
R-302	SERVICIOS ADICIONALES - MÁQUINAS EXPENDEDORAS/CAJEROS AUTOMÁTICOS	6.96	SERVICIOS ADICIONALES - ÁREA PAGA
T-20-L-5	MEDIDORES (LUZ)	4.75	ÁREA TÉCNICA
T-20-W-4	MEDIDORES (AGUA)	5.65	ÁREA TÉCNICA
T-21-6	ÁREA DE INSPECCIÓN	7.96	ÁREA TÉCNICA
T-21-7	ÁREA DE INSPECCIÓN	11.50	ÁREA TÉCNICA
T-21-8	ÁREA DE INSPECCIÓN	10.44	ÁREA TÉCNICA
T-21-9	ÁREA DE INSPECCIÓN	7.19	ÁREA TÉCNICA
T-25-3	NODO DE ACCESO DE TELECOMUNICACIONES	6.84	ÁREA TÉCNICA
T-25-4	NODO DE ACCESO DE TELECOMUNICACIONES	3.56	ÁREA TÉCNICA
ZDR-03	ZONA DE REFUGIO (PMR)	6.08	ZONA DE REFUGIO
ZDR-04	ZONA DE REFUGIO (PMR)	6.78	ZONA DE REFUGIO
		2251.99	

EDIFICIO DESCENDENTE
ARQ_PL_03_PLATAFORMA

CÓDIGO	NOMBRE	ÁREA (m²)	DEPARTAMENTO
O-17	OPERADORES TELECOMUNICACIONES EXTERIORES	35.21	ÁREA OPERATIVA
O-21-1	ALMACENAMIENTO DE LA ESTACIÓN	5.35	ÁREA OPERATIVA
PA-02	ÁREA PAGA	503.28	ÁREA PAGA
PA-03	ÁREA PAGA	265.93	ÁREA PAGA
R-109	SERVICIOS ADICIONALES - ÁREA DE SERVICIO	383.67	SERVICIOS ADICIONALES - ÁREA NO PAGA
R-110	SERVICIOS ADICIONALES - ÁREA DE SERVICIO	150.28	SERVICIOS ADICIONALES - ÁREA PAGA
T-00-2	CIRCULACIÓN TÉCNICA	226.50	ÁREA TÉCNICA
T-02	LOCAL DE CONDUCCIÓN AUTOMÁTICA (CBTC)	40.42	ÁREA TÉCNICA
T-02-1	UPS DEDICADA (CBTC)	47.56	ÁREA TÉCNICA

TABLA DE ÁREAS ÚTILES (NIVEL PLATAFORMA)

CÓDIGO	NOMBRE	ÁREA (m²)	DEPARTAMENTO
T-03	TELECOMUNICACIONES ESTACIÓN - CORRIENTE DÉBIL	128.07	ÁREA TÉCNICA
T-04	EQUIPO BOLETERÍA	29.66	ÁREA TÉCNICA
T-05	ALMACÉN PARA MANTENIMIENTO	24.93	ÁREA TÉCNICA
T-06	SALA DE TABLEROS	81.19	ÁREA TÉCNICA
T-07	CENTRO DE TRANSFORMACIÓN (CT)	93.32	ÁREA TÉCNICA
T-09	ALMACÉN EQUIPO ELÉCTRICO	27.84	ÁREA TÉCNICA
T-10	CUARTO DE EQUIPO ELECTROMECÁNICO	22.49	ÁREA TÉCNICA
T-11	CUARTO DE VENTILACIÓN	114.44	ÁREA TÉCNICA
T-12	PLANTA DE REFRIGERACIÓN PARA LA CLIMATIZACIÓN	84.17	ÁREA TÉCNICA
T-20-L-5	MEDIDORES (LUZ)	6.70	ÁREA TÉCNICA
T-20-W-4	MEDIDORES (AGUA)	5.31	ÁREA TÉCNICA
T-21-9	ÁREA DE INSPECCIÓN	8.07	ÁREA TÉCNICA
T-21-10	ÁREA DE INSPECCIÓN	12.62	ÁREA TÉCNICA
T-21-11	ÁREA DE INSPECCIÓN	9.05	ÁREA TÉCNICA
T-21-12	ÁREA DE INSPECCIÓN	4.72	ÁREA TÉCNICA
T-22	CUARTO DE UPS	90.47	ÁREA TÉCNICA
T-23	CUARTO PDAP	35.68	ÁREA TÉCNICA
T-24	TETRA UPS	48.75	ÁREA TÉCNICA
T-25-5	NODO DE ACCESO DE TELECOMUNICACIONES	4.14	ÁREA TÉCNICA
T-25-6	NODO DE ACCESO DE TELECOMUNICACIONES	5.30	ÁREA TÉCNICA
ZDR-05	ZONA DE REFUGIO (PMR)	7.29	ZONA DE REFUGIO
ZDR-06	ZONA DE REFUGIO (PMR)	7.94	ZONA DE REFUGIO
		2510.34	

NAVE CENTRAL
ARQ_PL_03_PLATAFORMA

CÓDIGO	NOMBRE	ÁREA (m²)	DEPARTAMENTO
PA-02	ÁREA PAGA	71.06	ÁREA PAGA
PA-03	ÁREA PAGA	96.90	ÁREA PAGA
PA-04	ÁREA PAGA	697.49	ÁREA PAGA
PA-05	ÁREA PAGA	697.45	ÁREA PAGA
PA-06	ÁREA PAGA	76.15	ÁREA PAGA
PA-07	ÁREA PAGA	82.27	ÁREA PAGA
		1721.32	
TOTAL NIVEL PLATAFORMA		6483.65	

TABLA DE ÁREAS ÚTILES POR DEPARTAMENTO (NIVEL PLATAFORMA)

DEPARTAMENTO	ÁREA (m²)
SERVICIOS ADICIONALES - ÁREA NO PAGA	1412.66
SERVICIOS ADICIONALES - ÁREA PAGA	376.27
ZONA DE REFUGIO	28.09
ÁREA OPERATIVA	46.16
ÁREA PAGA	3411.18
ÁREA TÉCNICA	1209.29
TOTAL NIVEL PLATAFORMA	6483.65

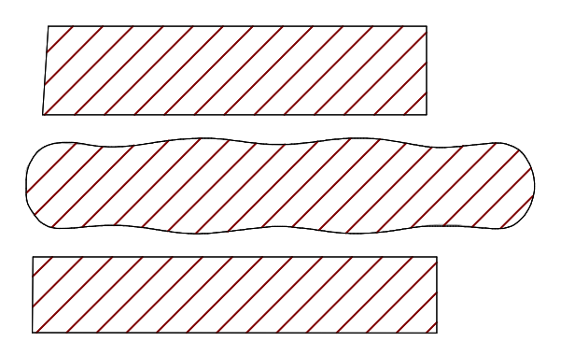

PLANO CLAVE ESTACIÓN 10

VÁLIDO PARA CONSTRUCCIÓN
20-03-26

LOCALIZACIÓN

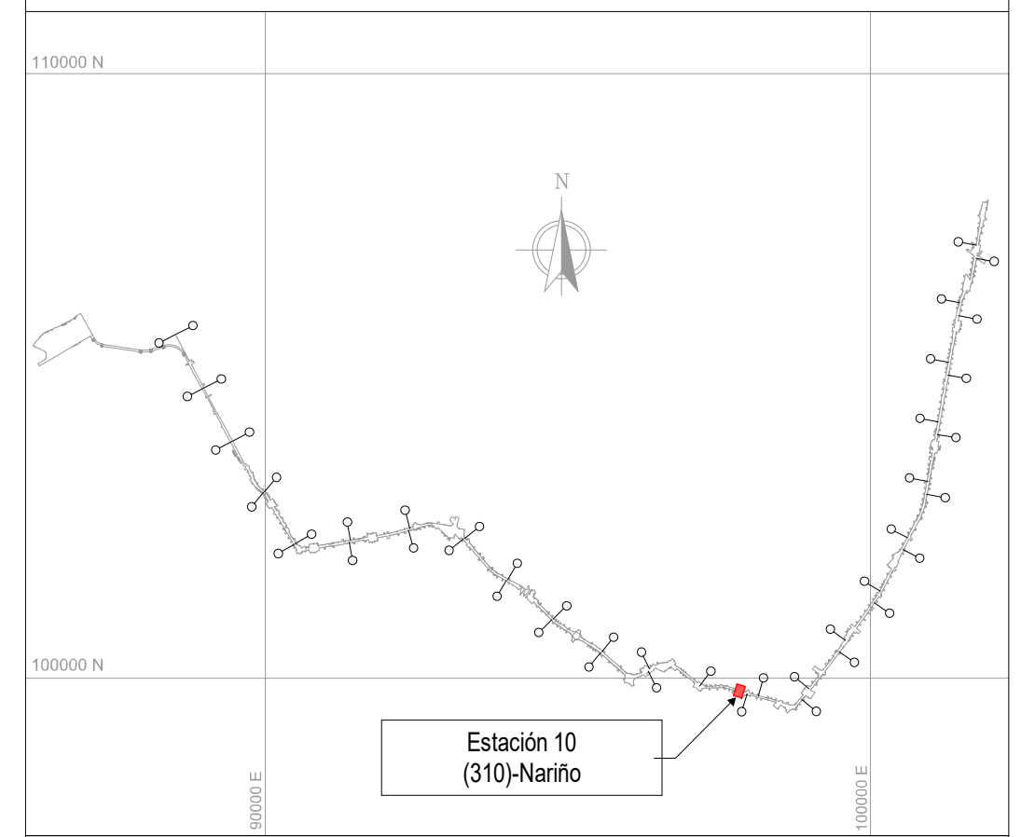

NOTAS

01 TODAS LAS DIMENSIONES ESTÁN CONFIGURADAS EN METROS A MENOS QUE SE INDIQUE UNA UNIDAD DE MEDIDA DIFERENTE.

02 TODAS LAS MEDIDAS, UBICACIÓN Y NIVELES DEBEN VERIFICARSE EN EL LUGAR DE CONSTRUCCIÓN.

03 NIVEL DE ACCESO AL EDIFICIO PL 01 CORRESPONDE AL +0.00m DE LA ESTACIÓN Y REFERENCIA AL NIVEL 2567.10 M.S.N.M

04 LOS NOMBRES ESPECÍFICOS DE LAS ÁREAS PUEDEN SER CONSULTADAS EN EL PLANO NO. 3 Ó EN LAS VISTAS EN PLANTA.

05 LOS COLORES QUE SE MUESTRAN EN LOS PLANOS COMO PROYECCIÓN DE ELEMENTOS ARQUITECTÓNICOS COMO CUBIERTAS FACHADAS MUROS ETC. NO REPRESENTAN LA MATERIALIDAD Y REALIDAD DE ACABADOS DEL PROYECTO, SOLO SON INDICATIVOS PARA REALIZAR UNA CORRECTA LECTURA DE LA PLANIMETRÍA.

06 LAS ESCALERAS ELÉCTRICAS INDICAN SU SENTIDO CON LA SIGUIENTE NOMENCLATURA: "SUBE" Y "BAJA".

07 SE DEBEN REVISAR LOS NIVELES ESTRUCTURALES PARA NIVEL DE ACCESO PL_01 Y SUBNIVELES, PL_02 (INTERMEDIO), PL_03 (PLATAFORMA) CON LA PLANIMETRÍA DE PLACAS ESTRUCTURALES EN LOS ENTREGABLES L1T1-1300-410-CON-ED-EST-PL-0069, 70, 71, 72, 107, 108, 109, 110, 111, 112, 113, 114, 115, RESPECTIVAMENTE. EL NIVEL ESTRUCTURAL (NE) REFERENCIA LOS ESPACIOS DONDE SE DEBE ACONDICIONAR EL ACABADO DE PISO SEGÚN CORRESPONDA, CON LOS NIVELES DE PISO TERMINADO (NPT). LOS NIVELES PROYECTADOS DE EMPATE (NPE) EN LAS ÁREAS DE SERVICIOS ADICIONALES, REFERENCIAN LA ADECUACIÓN DE LOS DESNIVELES EN ESTAS ÁREAS; QUEDA COMO RESPONSABILIDAD DEL LOCATARIO DEFINIR Y ACONDICIONAR ESTE ACABADO DE PISO (NPE) EN LÍNEA CON EL NIVEL (NPT) DE ESPACIOS COLINDANTES. EL NIVEL ESTRUCTURAL (NE) SE ENCUENTRA A (- 0.10M) POR DEBAJO DE LOS NIVELES DE PISO TERMINADO (NPT) Y LOS NIVELES PROYECTADOS DE EMPATE (NPE) MARCADOS EN LA PLANIMETRÍA.

- ARQ_PL_00 = SÓTANO /NPT -6.80
- ARQ_PL_00.1 = ACCESO /NPT -0.50
- ARQ_PL_00.2 = ACCESO /NPT -0.30
- ARQ_PL_00.3 = ACCESO /NPT -0.20
- ARQ_PL_00.4 = ACCESO /NPT -0.10
- ARQ_PL_01 = ACCESO /NPT 0.00
- ARQ_PL_02 = INTERMEDIO /NPT 6.60
- ARQ_PL_02.2 = TOPE DE RIEL /NPT 14.20
- ARQ_PL_03 = PLATAFORMA /NPT 15.34
- ARQ_PL_04 = CUBIERTA EDIFICACIONES /NPT 21.94
- ARQ_PL_05 = CUBIERTA NAVE CENTRAL /NPT 24.59

CONVENCIONES

- - - LÍMITE DE INTERVENCIÓN
- - - HUELLA APÉNDICE TÉCNICO
▬ MURO DIVISORIO
— — — PROYECCIÓN NIVEL SUPERIOR

🟩	SERVICIOS ADICIONALES - ÁREA NO PAGA	🟨	ÁREA NO PAGA
🟩	SERVICIOS ADICIONALES - ÁREA PAGA	🟦	ÁREA OPERATIVA
🟩	SERVICIO PÚBLICO	🟧	ÁREA PAGA
🟦	ZONA DE REFUGIO	🟦	ÁREA PÚBLICA
🟥	ÁREA CULTURAL	⬜	ÁREA TÉCNICA

No.	PLANOS DE REFERENCIA	REV.

No.	MODELO BIM DE REFERENCIA	REV.
1	L1T1-1100-210-CON-ED-EST-MO-0001.rvt	V00
2	L1T1-1100-211-CON-ED-EST-MO-0001.rvt	V00
3	L1T1-1100-310-CON-ED-EST-MO-0001.rvt	V00
4	L1T1-1150-210-CON-ED-EST-MO-0001.rvt	V00
5	L1T1-1150-211-CON-ED-EST-MO-0001.rvt	V00
6	L1T1-1150-310-CON-ED-EST-MO-0001.rvt	V00
7	L1T1-1200-310-CON-ED-EST-MO-0001.rvt	V00
8	L1T1-1300-410-CON-ED-EST-MO-0001.rvt	V00
9	L1T1-1300-410-CON-ED-EST-MO-0002.rvt	V00
10	L1T1-1310-410-CON-ED-EST-MO-0001.rvt	V00
11	L1T1-1410-310-CON-ED-MEC-MO-0001.rvt	V00
12	L1T1-1420-310-CON-ED-MEC-MO-0001.rvt	V00
13	L1T1-5160-310-CON-ED-EST-MO-0001.rvt	V00
14	L1T1-5160-310-CON-ED-ARQ-MO-0001.rvt	V00
15	L1T1-5300-310-CON-ED-MEC-MO-0001.rvt	V00
16	L1T1-5600-310-CON-ED-INS-MO-0001.rvt	V00
17	L1T1-1330-410-CON-ED-ARQ-MO-0011.rvt	V00
18	L1T1-1330-410-CON-ED-ARQ-MO-0012.rvt	V00

No.	PAQUETE DE TRABAJO DE REFERENCIA	REV.
1	XREF-URBANISM_CONTEXT_ST10.rvt	
2	XREF-SECONDARY-STRUCTURE-ST10.rvt	

0 2 10m
1:200

METRO BOGOTÁ
GCS
CONSORCIO SUPERVISOR PLMB
CHEC

DISEÑÓ: REN ZHENHUA Licencia de Arq.nivel I (China): 1101735-614	APROBÓ: DIEGO ERNESTO DUEÑAS Mat.: 25202-53876 CND
REVISÓ: CARLOS MAURICIO BARRETO BARBOSA Mat.: A4012012-14139353	DIBUJÓ: EQUIPO CHEC

REVISIÓN No.	FECHA	DESCRIPCIÓN	REVISÓ	APROBÓ	APROBACIÓN CLIENTE
V01	20/03/2026	EMITIDO PARA CONSTRUCCIÓN	C.M.B.B	D.E.D	
V00	26/03/2025	REVISIÓN NO OBJETADA - EMITIDO PARA CONSTRUCCIÓN	F.B.R	E.O.M	
VHH	01/11/2024	EMITIDO PARA REVISIÓN Y COMENTARIOS DEL CLIENTE E INTERVENTORÍA - INCLUYE COMENTARIOS /(AJUSTES V3)	F.B.R	E.O.M	
VGG	29/07/2024	EMITIDO PARA REVISIÓN Y COMENTARIOS DEL CLIENTE E INTERVENTORÍA - INCLUYE COMENTARIOS /(AJUSTES V2)	F.B.R	E.O.M	
VFF	20/04/2023	EMITIDO PARA REVISIÓN Y COMENTARIOS DEL CLIENTE E INTERVENTORÍA - INCLUYE COMENTARIOS /(AJUSTES)	J.E.M	M.B.M	
VEE	18/12/2022	EMITIDO PARA REVISIÓN Y COMENTARIOS DEL CLIENTE E INTERVENTORÍA - INCLUYE COMENTARIOS /(NAVE CENTRAL)	J.E.M	M.B.M	
VDD	01/12/2022	EMITIDO PARA REVISIÓN Y COMENTARIOS DEL CLIENTE E INTERVENTORÍA - INCLUYE COMENTARIOS /(90% ACCESOS)	J.E.M	M.B.M	
VCC	22/08/2022	EMITIDO PARA REVISIÓN Y COMENTARIOS DEL CLIENTE E INTERVENTORÍA - INCLUYE COMENTARIOS /(ENTREGA 90%)	J.E.M	M.B.M	
VBB	06/12/2021	EMITIDO PARA REVISIÓN Y COMENTARIOS DEL CLIENTE E INTERVENTORÍA	J.E.M	M.B.M	
VA0	05/12/2021	EMITIDO PARA COMENTARIOS INTERNOS - EMISIÓN PRELIMINAR PARA COMENTARIOS	J.E.M	M.B.M	

METRO LÍNEA 1

METRO LÍNEA 1
CONTRATO DE CONCESIÓN No. 163 DE 2019

PROYECTO PRIMERA LÍNEA DEL METRO DE BOGOTÁ - TRAMO 1

DIRECTOR DE INTERVENTORÍA: JAVIER DESCARGA N. Mat.:25202-68697 CND	ESPECIALISTA INTERVENTORÍA: CARLOS ALBERTO HOYOS SOTO Mat.:A25072000-14251682	FECHA: MARZO 2026

INFRAESTRUCTURA VIAL

ARQUITECTURA

ESTACIÓN METRO 10 (NARIÑO)
GENERAL
VISTA EN PLANTA Y 3D - NIVEL PLATAFORMA

PLANCHA No: L1T1-0000-310-CON-ED-ARQ-PL-0001_07_V01	ESCALA: INDICADA	REVISIÓN No. V01	PLANO No. 07 DE 96
ARCHIVO: L1T1-0000-310-CON-ED-ARQ-MO-0001_V00.rvt	FECHA: DICIEMBRE 2021		