L1T1-CON-CAL-FR-0120 - B1 : 1000x707mm

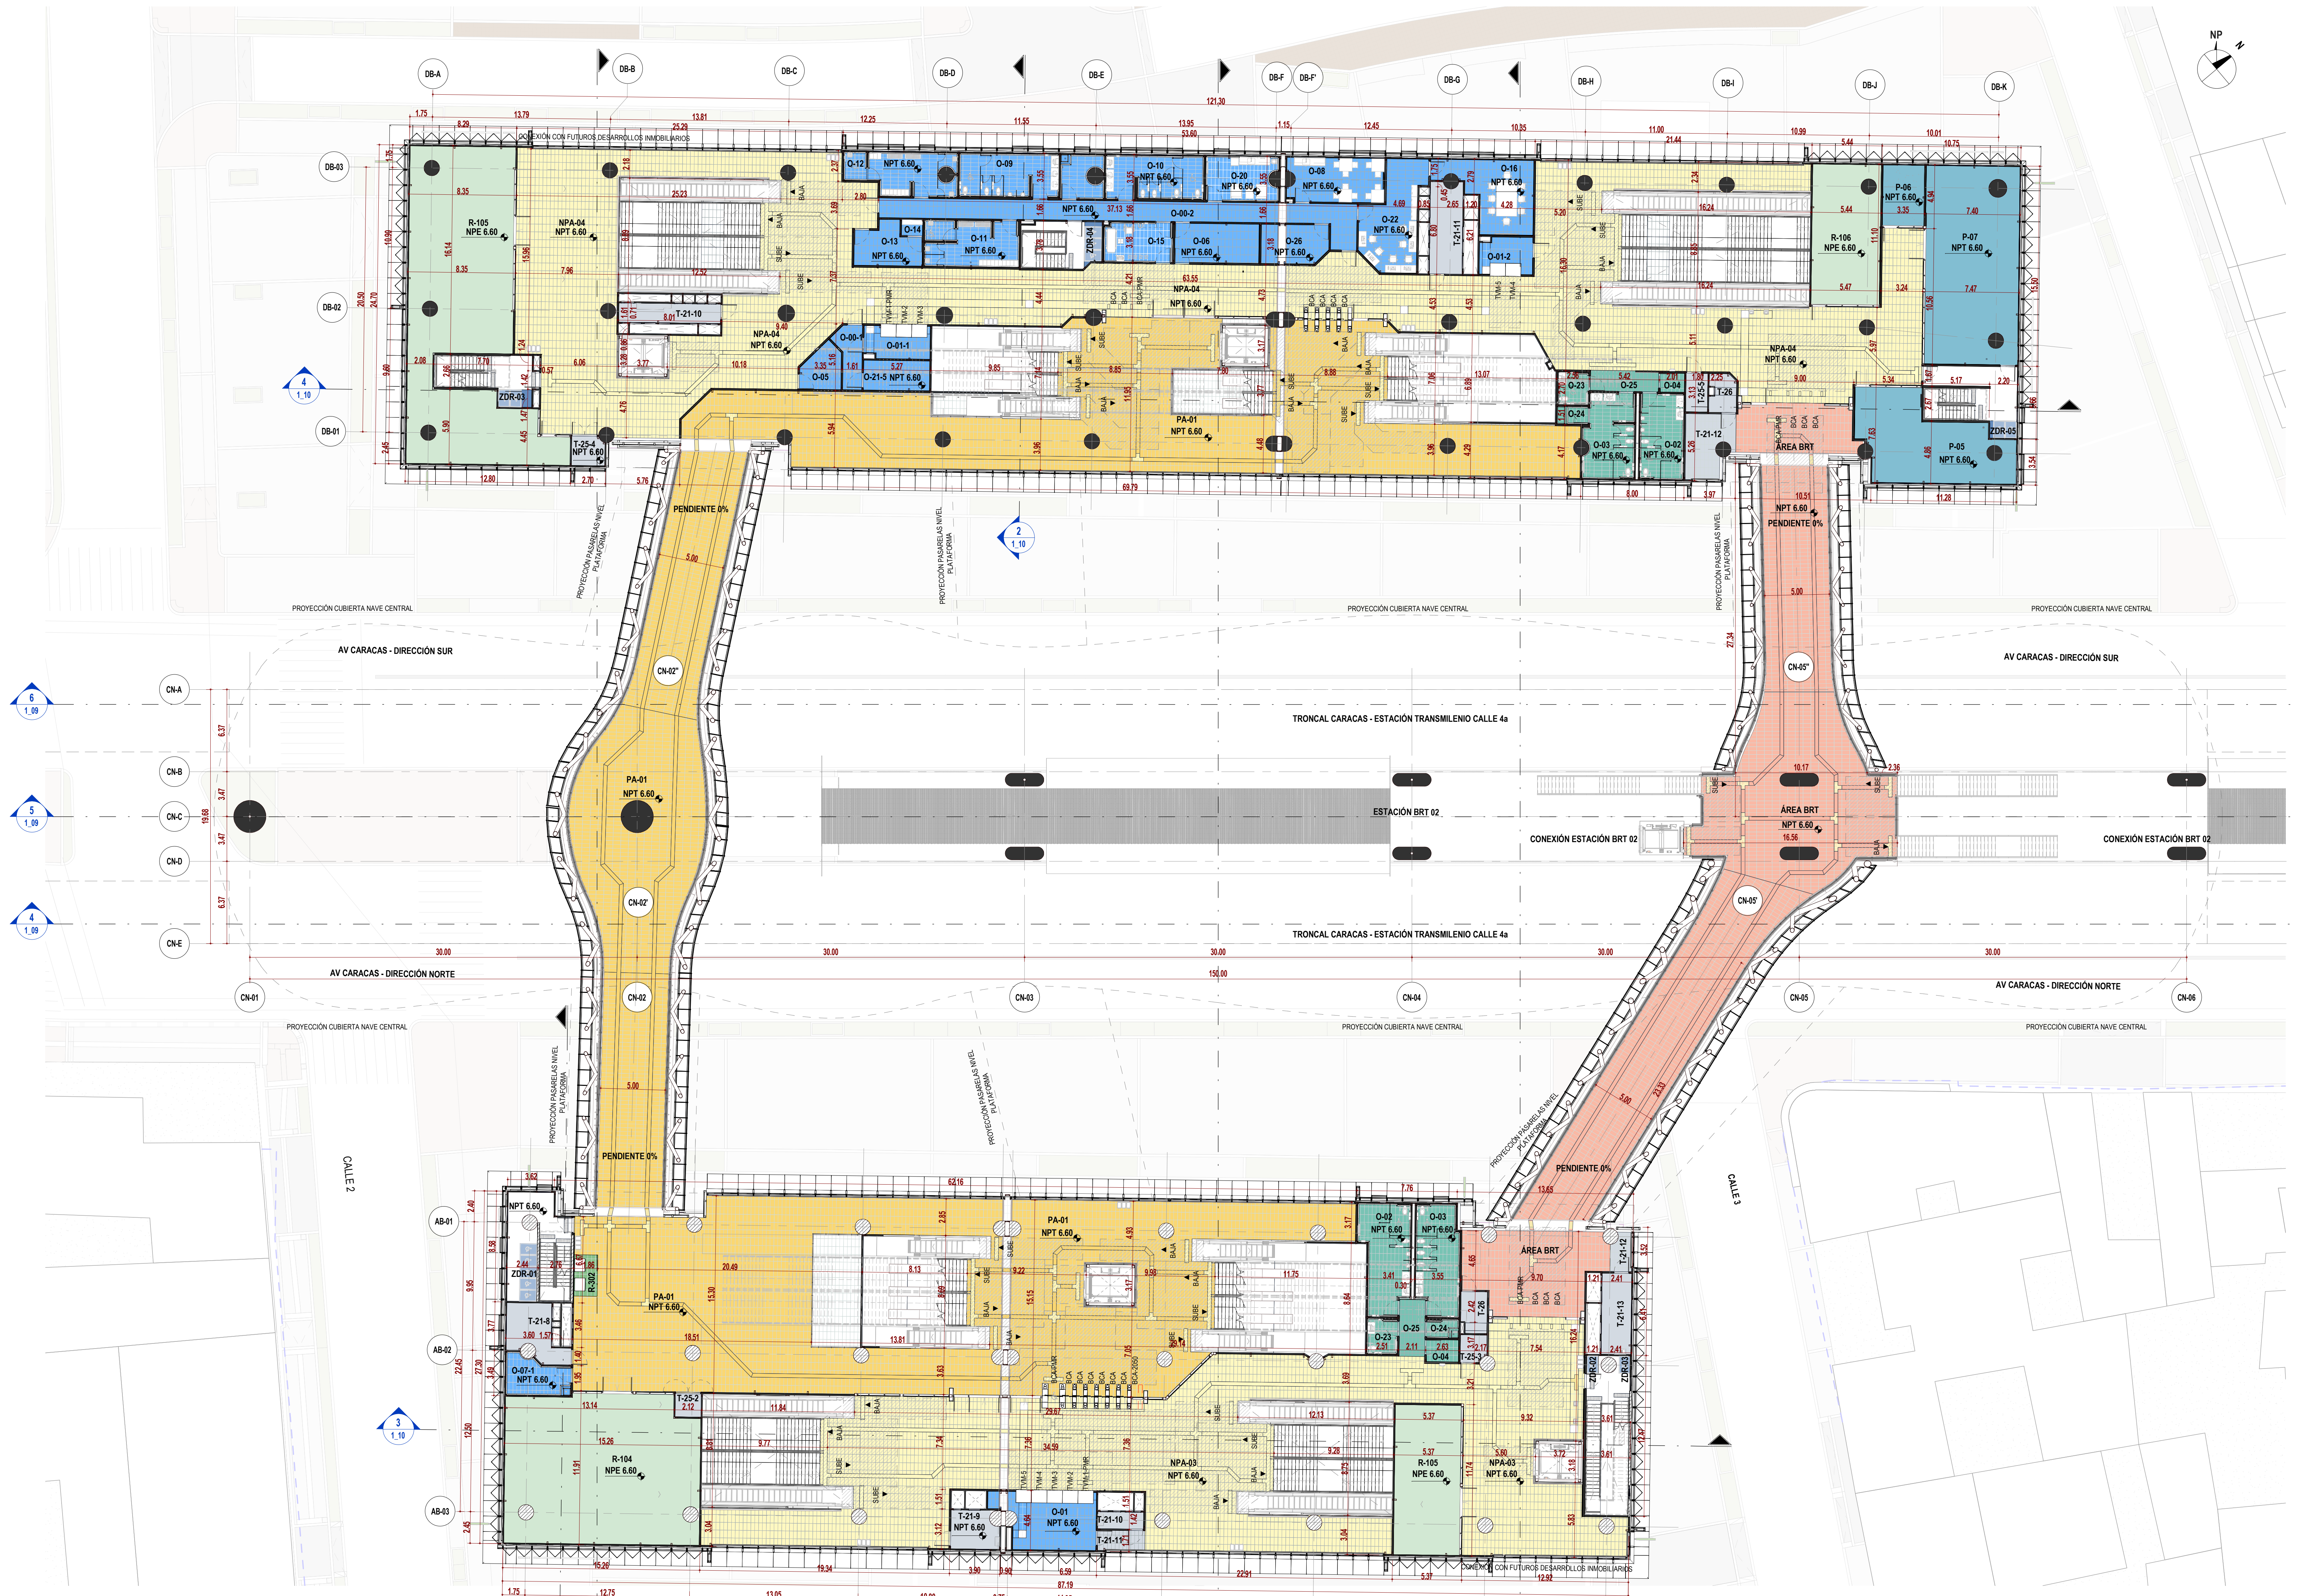
AV CARACAS - DIRECCIÓN SUR
TRONCAL CARACAS - ESTACIÓN TRANSMILENIO CALLE 4a
ESTACIÓN BRT 02
CONEXIÓN ESTACIÓN BRT 02
AV CARACAS - DIRECCIÓN NORTE
PROYECCIÓN CUBIERTA NAVE CENTRAL
PENDIENTE 8%
PENDIENTE 0%
PA-01 NPT 6.60
ÁREA BRT
CALLE 2
CALLE 3

2 **NIVEL INTERMEDIO_GENERAL**
ESC: 1:200

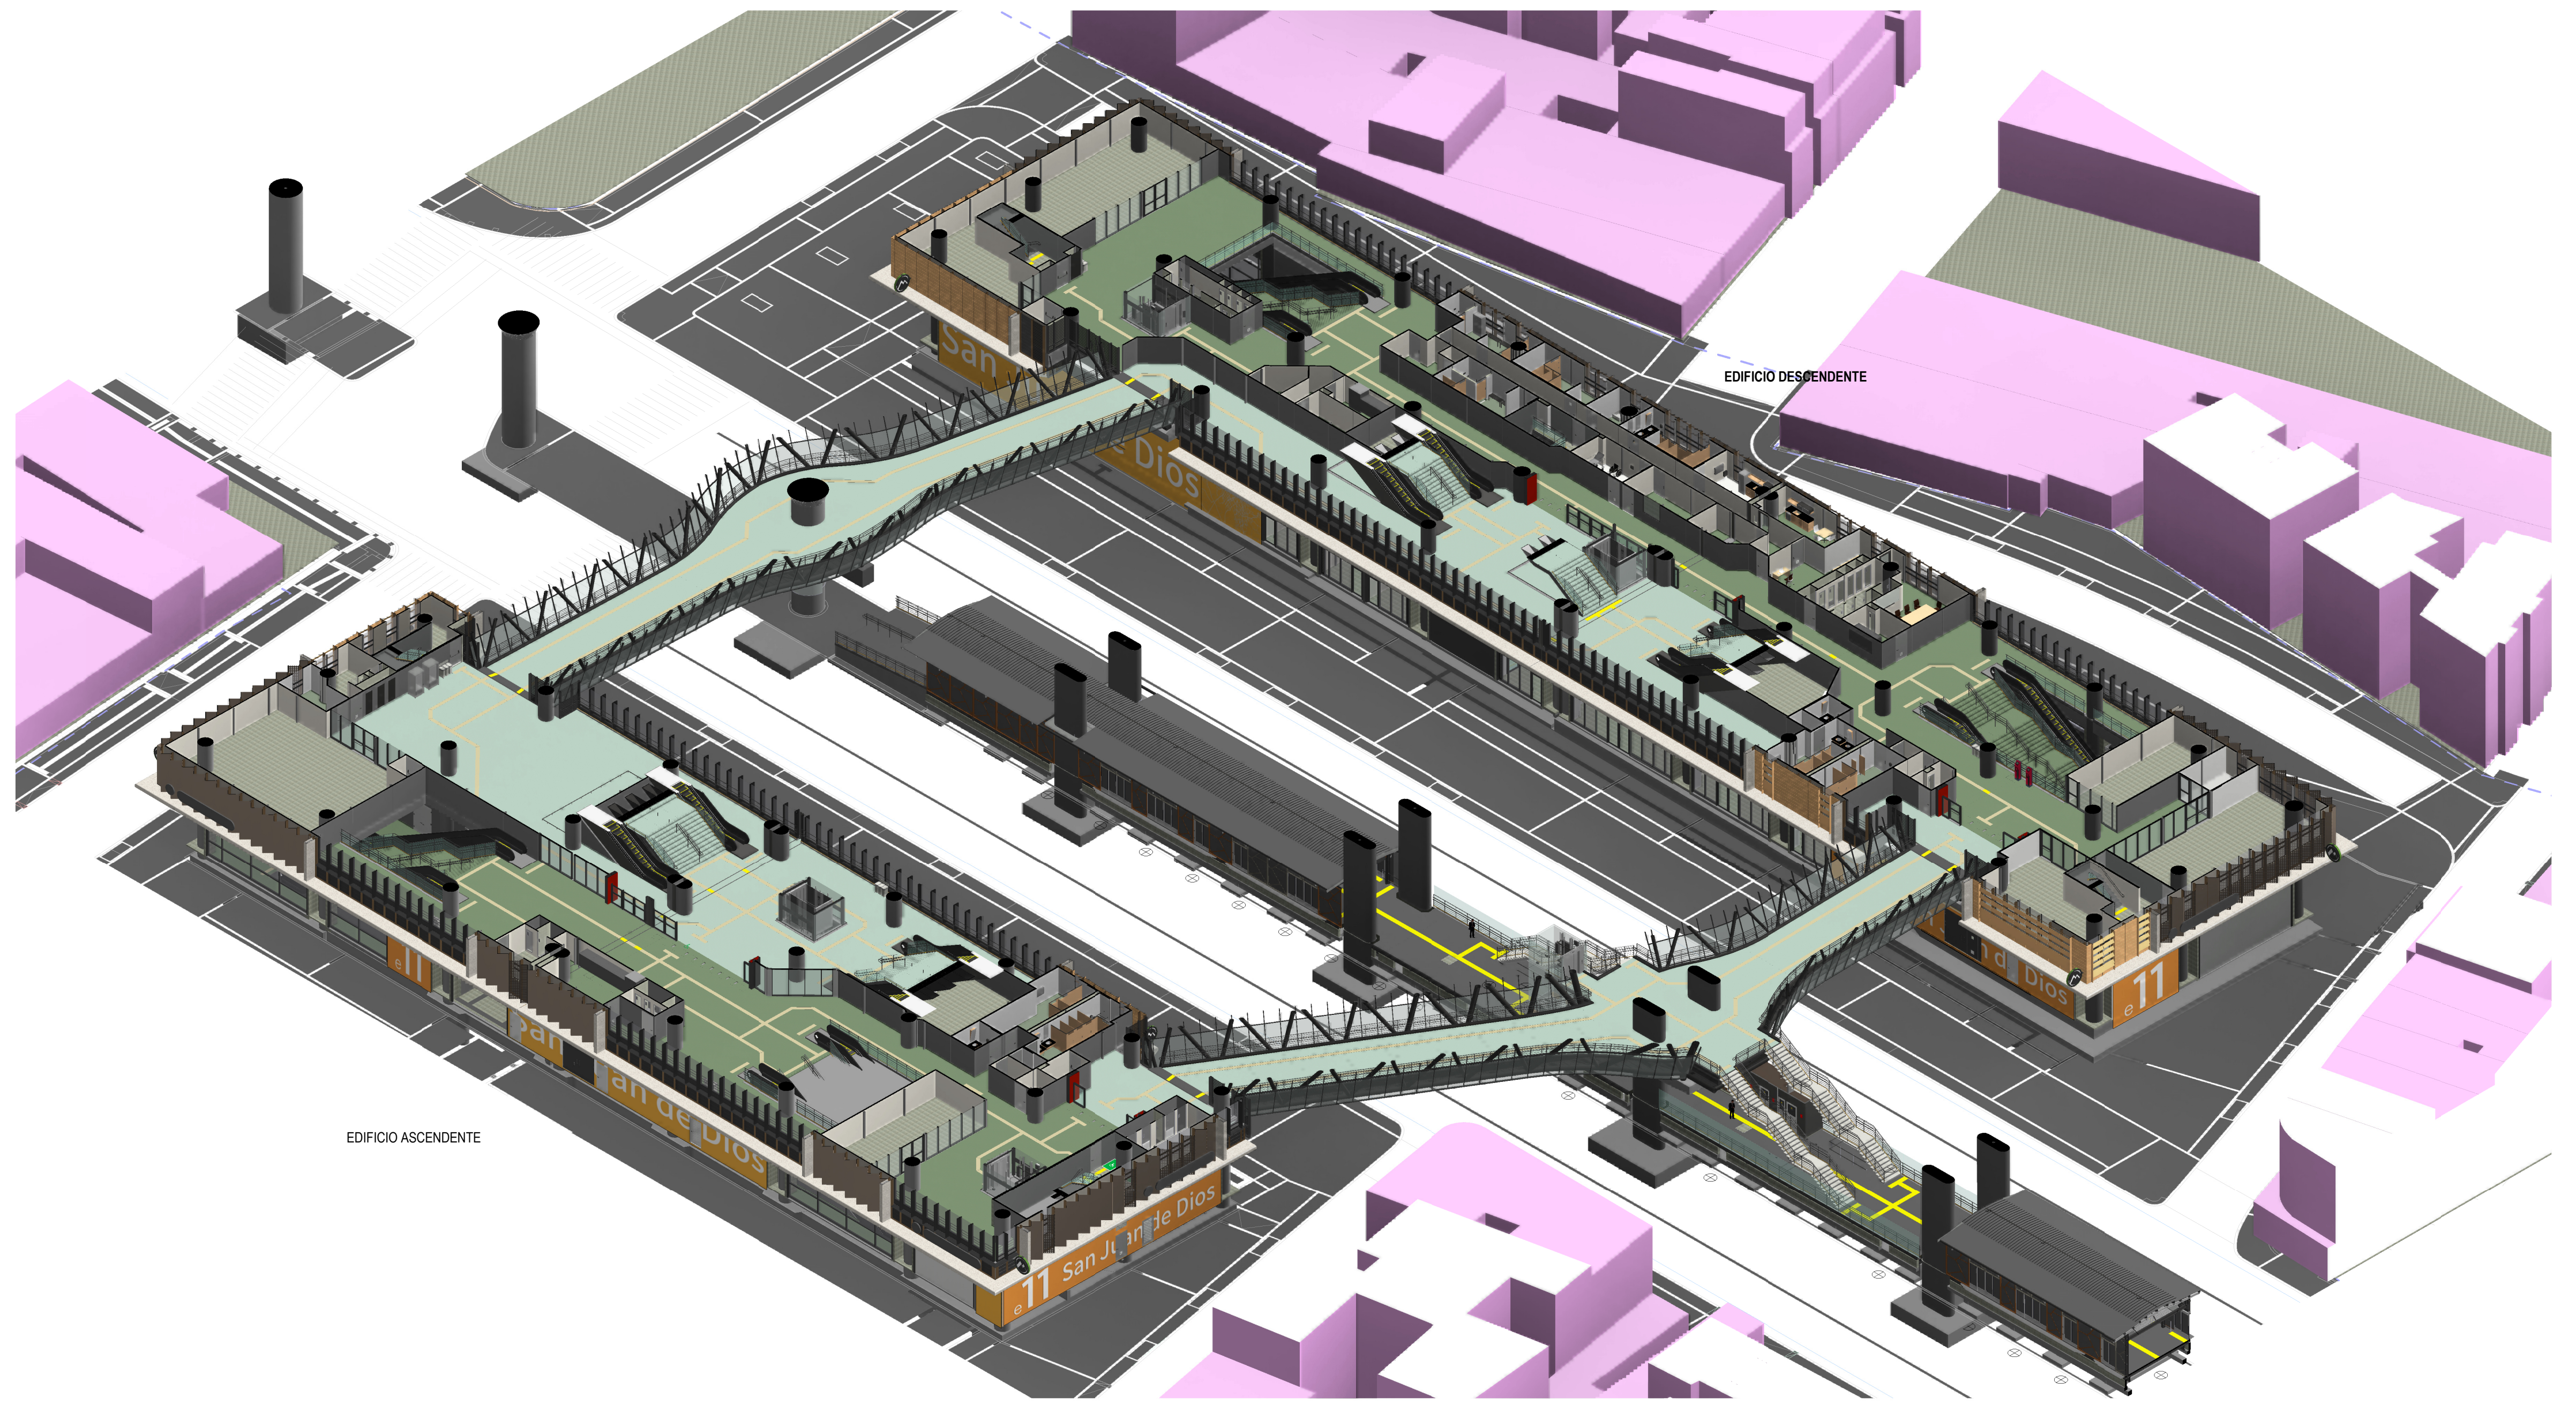

1 **3D_NIVEL INTERMEDIO_GENERAL**
ESC: N/A

TABLA DE ÁREAS ÚTILES (NIVEL INTERMEDIO)

CÓDIGO	NOMBRE	ÁREA (m²)	DEPARTAMENTO
EDIFICIO ASCENDENTE			
ARQ_PL_02_INTERMEDIO			
NPA-03	ÁREA NO PAGA	611.04	ÁREA NO PAGA
O-01	VENTA AUTOMÁTICA DE BOLETOS	31.76	ÁREA OPERATIVA
O-02	BAÑOS PÚBLICOS DE HOMBRES	29.39	SERVICIO PÚBLICO
O-03	BAÑOS PÚBLICOS DE MUJERES	27.31	SERVICIO PÚBLICO
O-04	CONTROL DE ACCESO BAÑOS PÚBLICOS	4.31	SERVICIO PÚBLICO
O-07-1	CUARTO DE LIMPIEZA COMPLEMENTARIO	13.29	ÁREA OPERATIVA
O-23	BAÑO PÚBLICO - FAMILIAR	6.26	SERVICIO PÚBLICO
O-24	CUARTO DE LIMPIEZA DE BAÑOS PÚBLICOS	3.44	SERVICIO PÚBLICO
O-25	BAÑO PÚBLICO - CORREDOR OPERACIONAL	8.81	SERVICIO PÚBLICO
PA-01	ÁREA PAGA	627.67	ÁREA PAGA
R-104	SERVICIOS ADICIONALES - ÁREA DE SERVICIO	168.55	SERVICIOS ADICIONALES - ÁREA NO PAGA
R-105	SERVICIOS ADICIONALES - ÁREA DE SERVICIO	59.20	SERVICIOS ADICIONALES - ÁREA NO PAGA
R-302	SERVICIOS ADICIONALES - MÁQUINAS EXPENDEDORAS/CAJEROS AUTOMÁTICOS	5.87	SERVICIOS ADICIONALES - ÁREA PAGA
T-21-8	ÁREA DE INSPECCIÓN	15.48	ÁREA TÉCNICA
T-21-9	ÁREA DE INSPECCIÓN	10.53	ÁREA TÉCNICA
T-21-10	ÁREA DE INSPECCIÓN	4.58	ÁREA TÉCNICA
T-21-11	ÁREA DE INSPECCIÓN	6.21	ÁREA TÉCNICA
T-21-12	ÁREA DE INSPECCIÓN	4.99	ÁREA TÉCNICA
T-21-13	ÁREA DE INSPECCIÓN	14.41	ÁREA TÉCNICA
T-25-2	NODO DE ACCESO DE TELECOMUNICACIONES	3.57	ÁREA TÉCNICA
T-25-3	NODO DE ACCESO DE TELECOMUNICACIONES	4.11	ÁREA TÉCNICA
T-26	NODO DE ACCESO DE TELECOMUNICACIONES TMSA	6.21	ÁREA TÉCNICA
ZDR-01	ZONA DE REFUGIO (PMR)	6.08	ZONA DE REFUGIO
ZDR-02	ZONA DE REFUGIO (PMR)	1.21	ZONA DE REFUGIO
ZDR-03	ZONA DE REFUGIO (PMR)	1.22	ZONA DE REFUGIO
ÁREA BRT	ÁREA BRT	65.35	ÁREA BRT
EDIFICIO ASCENDENTE		1740.83	
EDIFICIO DESCENDENTE			
ARQ_PL_02_INTERMEDIO			
NPA-04	ÁREA NO PAGA	888.01	ÁREA NO PAGA
O-00-1	CIRCULACIÓN ÁREAS OPERATIVAS	8.61	ÁREA OPERATIVA
O-00-2	CIRCULACIÓN ÁREAS OPERATIVAS	61.48	ÁREA OPERATIVA
O-01-1	VENTA AUTOMÁTICA DE BOLETOS	12.78	ÁREA OPERATIVA
O-01-2	VENTA AUTOMÁTICA DE BOLETOS	11.65	ÁREA OPERATIVA
O-02	BAÑOS PÚBLICOS DE HOMBRES	22.01	SERVICIO PÚBLICO
O-03	BAÑOS PÚBLICOS DE MUJERES	24.26	SERVICIO PÚBLICO
O-04	CONTROL DE ACCESO BAÑOS PÚBLICOS	2.80	SERVICIO PÚBLICO
O-05	LOCAL DE INFORMACIÓN	9.62	ÁREA OPERATIVA
O-06	OFICINA DEL SUPERVISOR DE LA ESTACIÓN	20.01	ÁREA OPERATIVA
O-07	CUARTO DE LIMPIEZA	10.00	ÁREA OPERATIVA
O-08	SALA DE DESCANSO PARA EMPLEADOS	25.27	ÁREA OPERATIVA
O-09	BAÑOS EMPLEADOS HOMBRES	25.36	ÁREA OPERATIVA
O-10	BAÑOS EMPLEADOS MUJERES	24.73	ÁREA OPERATIVA
O-11	VESTIDORES EMPLEADOS HOMBRES	25.27	ÁREA OPERATIVA
O-12	VESTIDORES EMPLEADOS MUJERES	25.00	ÁREA OPERATIVA
O-13	LOCAL DE POLICÍA	15.08	ÁREA OPERATIVA
O-14	CALABOZO	2.05	ÁREA OPERATIVA
O-15	LOCAL PRIMEROS AUXILIOS	16.05	ÁREA OPERATIVA
O-16	SALA DE REUNIONES	31.15	ÁREA OPERATIVA
O-20	SALA DE LACTANCIA	19.08	ÁREA OPERATIVA
O-21-5	ALMACENAMIENTO DE LA ESTACIÓN	12.01	ÁREA OPERATIVA
O-22	OFICINA DE MANTENIMIENTO	32.84	ÁREA OPERATIVA
O-23	BAÑO PÚBLICO - FAMILIAR	5.74	SERVICIO PÚBLICO
O-24	CUARTO DE LIMPIEZA DE BAÑOS PÚBLICOS	3.20	SERVICIO PÚBLICO
O-25	BAÑO PÚBLICO - CORREDOR OPERACIONAL	8.33	SERVICIO PÚBLICO
O-26	ALMACENAMIENTO DE BASURAS METRO	15.44	ÁREA OPERATIVA
P-05	BIBLIOMETRO	64.43	ÁREA PÚBLICA
P-06	ESPACIO IPES (INSTITUTO PARA LA ECONOMÍA SOCIAL)	15.01	ÁREA PÚBLICA
P-07	SALÓN MÚLTIPLE EMB	105.11	ÁREA PÚBLICA
PA-01	ÁREA PAGA	448.65	ÁREA PAGA
R-105	SERVICIOS ADICIONALES - ÁREA DE SERVICIO	191.61	SERVICIOS ADICIONALES - ÁREA NO PAGA
R-106	SERVICIOS ADICIONALES - ÁREA DE SERVICIO	56.81	SERVICIOS ADICIONALES - ÁREA NO PAGA
T-21-10	ÁREA DE INSPECCIÓN	11.80	ÁREA TÉCNICA
T-21-11	ÁREA DE INSPECCIÓN	17.57	ÁREA TÉCNICA
T-21-12	ÁREA DE INSPECCIÓN	16.80	ÁREA TÉCNICA
T-25-4	NODO DE ACCESO DE TELECOMUNICACIONES	5.71	ÁREA TÉCNICA
T-25-5	NODO DE ACCESO DE TELECOMUNICACIONES	5.04	ÁREA TÉCNICA
T-26	NODO DE ACCESO DE TELECOMUNICACIONES TMSA	5.77	ÁREA TÉCNICA
ZDR-03	ZONA DE REFUGIO (PMR)	3.50	ZONA DE REFUGIO
ZDR-04	ZONA DE REFUGIO (PMR)	4.23	ZONA DE REFUGIO
ZDR-05	ZONA DE REFUGIO (PMR)	2.81	ZONA DE REFUGIO
ÁREA BRT	ÁREA BRT	36.18	ÁREA BRT
EDIFICIO DESCENDENTE		2348.86	
NAVE CENTRAL			
ARQ_PL_02_INTERMEDIO			
PA-01	ÁREA PAGA	357.44	ÁREA PAGA
ÁREA BRT	ÁREA BRT	408.55	ÁREA BRT
NAVE CENTRAL		765.99	
TOTAL NIVEL INTERMEDIO		4855.68	

TABLA DE ÁREAS ÚTILES POR DEPARTAMENTO (NIVEL INTERMEDIO)

DEPARTAMENTO	ÁREA (m²)
SERVICIO PÚBLICO	145.84
SERVICIOS ADICIONALES - ÁREA NO PAGA	476.16
SERVICIOS ADICIONALES - ÁREA PAGA	5.87
ZONA DE REFUGIO	19.04
ÁREA BRT	510.07
ÁREA NO PAGA	1499.05
ÁREA OPERATIVA	448.54
ÁREA PAGA	1433.76
ÁREA PÚBLICA	184.55
ÁREA TÉCNICA	132.79
TOTAL NIVEL INTERMEDIO	4855.68

LOCALIZACIÓN

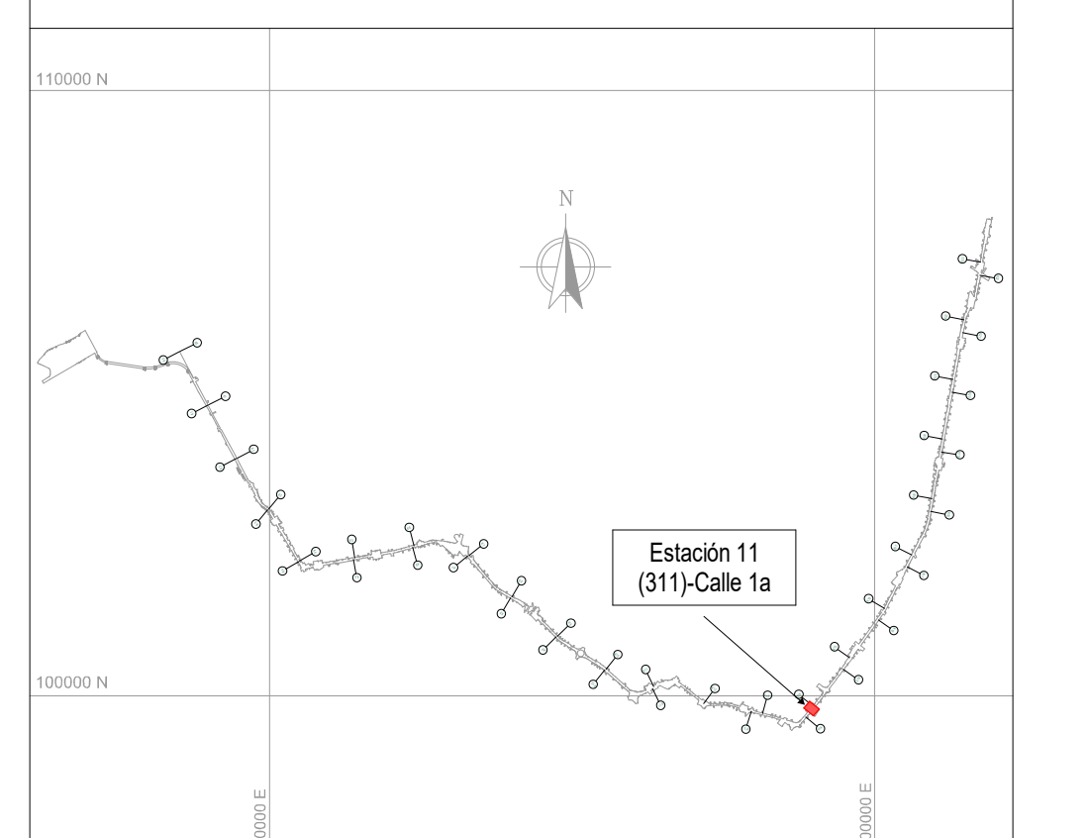

NOTAS

01 TODAS LAS DIMENSIONES ESTÁN CONFIGURADAS EN METROS A MENOS QUE SE INDIQUE UNA UNIDAD DE MEDIDA DIFERENTE.

02 TODAS LAS MEDIDAS, UBICACIÓN Y NIVELES DEBEN VERIFICARSE EN EL LUGAR DE CONSTRUCCIÓN.

03 EL NIVEL DE ACCESO AL EDIFICIO PL 01 CORRESPONDE AL +0,00 DE LA ESTACIÓN Y REFERENCIA AL NIVEL 2575.40 M.S.N.M.

04 LOS NOMBRES ESPECÍFICOS DE LAS ÁREAS PUEDEN SER CONSULTADAS EN EL PLANO NO. 3 Ó EN LAS VISTAS EN PLANTA.

05 LOS COLORES QUE SE MUESTRAN EN LOS PLANOS COMO PROYECCIÓN DE ELEMENTOS ARQUITECTÓNICOS COMO CUBIERTAS, FACHADAS, MUROS, ETC. NO REPRESENTAN LA MATERIALIDAD Y REALIDAD DE ACABADOS DEL PROYECTO, SOLO SON INDICATIVOS PARA REALIZAR UNA CORRECTA LECTURA DE LA PLANIMETRÍA.

06 LAS ESCALERAS ELÉCTRICAS INDICAN SU SENTIDO CON LA SIGUIENTE NOMENCLATURA: "SUBE" Y "BAJA".

07 SE DEBEN REVISAR LOS NIVELES ESTRUCTURALES PARA NIVEL DE ACCESO PL_01 Y SUBNIVELES, PL_02 (INTERMEDIO), PL_03 (PLATAFORMA) CON LA PLANIMETRÍA DE PLACAS ESTRUCTURALES EN LOS ENTREGABLES L1T1-1300-411-CON-ED-EST-PL-0070, 71, 72, 73, 99, 100, 101, 102, 103, 104, 105, 125, 126, RESPECTIVAMENTE. EL NIVEL ESTRUCTURAL (NE) REFERENCIA LOS ESPACIOS DONDE SE DEBE ACONDICIONAR EL ACABADO DE PISO SEGÚN CORRESPONDA, CON LOS NIVELES DE PISO TERMINADO (NPT). LOS NIVELES PROYECTADOS DE EMPATE (NPE) EN LAS ÁREAS DE SERVICIOS ADICIONALES, REFERENCIAN LA ADECUACIÓN DE LOS DESNIVELES EN ESTAS ÁREAS; QUEDA COMO RESPONSABILIDAD DEL LOCATARIO DEFINIR Y ACONDICIONAR ESTE ACABADO DE PISO (NPE) EN LÍNEA CON EL NIVEL (NPT) DE ESPACIOS COLINDANTES. EL NIVEL ESTRUCTURAL (NE) SE ENCUENTRA A (- 0.10M) POR DEBAJO DE LOS NIVELES DE PISO TERMINADO (NPT) Y LOS NIVELES PROYECTADOS DE EMPATE (NPE) MARCADOS EN LA PLANIMETRÍA.

- ARQ_PL_-00.1 = SER-2 / NPT -12.00
- ARQ_PL_00 = SÓTANO / NPT -7.70
- ARQ_PL_00.1 = ACCESO / NPT -1.40
- ARQ_PL_00.2 = ACCESO / NPT -1.25
- ARQ_PL_00.3 = ACCESO / NPT -0.90
- ARQ_PL_00.4 = ACCESO / NPT -0.80
- ARQ_PL_00.5 = ACCESO / NPT -0.65
- ARQ_PL_00.6 = ACCESO / NPT -0.40
- ARQ_PL_00.7 = ACCESO / NPT -0.25
- ARQ_PL_00.8 = ACCESO / NPT -0.20
- ARQ_PL_00.9 = ACCESO / NPT -0.10
- ARQ_PL_01 = ACCESO / NPT 0.00
- ARQ_PL_02 = INTERMEDIO / NPT 6.60
- ARQ_PL_02.2 = TOPE DE RIEL (TOR) / NPT 14.20
- ARQ_PL_03 = PLATAFORMA / NPT 15.34
- ARQ_PL_04 = CUBIERTA EDIFICACIONES / NPT 21.94
- ARQ_PL_05 = CUBIERTA NAVE CENTRAL / NPT 24.60

CONVENCIONES

- LÍMITE DE NIVEL ARQUITECTÓNICO
- HUELLA APÉNDICE TÉCNICO
- MURO DIVISORIO
- PROYECCIÓN NIVEL SUPERIOR

🟩	SERVICIOS ADICIONALES - ÁREA NO PAGA	🟨	ÁREA NO PAGA
🟩	SERVICIOS ADICIONALES - ÁREA PAGA	🟦	ÁREA OPERATIVA
🟩	SERVICIO PÚBLICO	🟨	ÁREA PAGA
🟦	ZONA DE REFUGIO	🟦	ÁREA PÚBLICA
🟥	ÁREA CULTURAL	⬜	ÁREA TÉCNICA
🟪	ÁREA DE TAQUILLAS BRT	🟧	ÁREA BRT

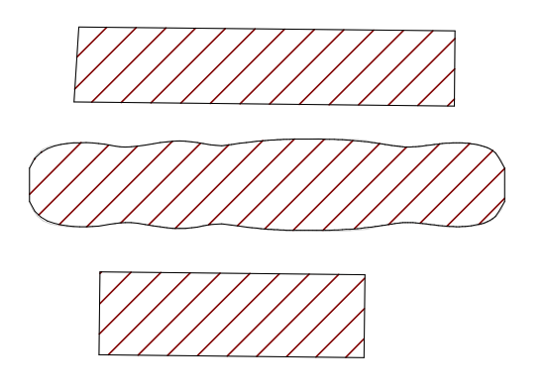

PLANO CLAVE ESTACIÓN 11

No.	PLANOS DE REFERENCIA	REV.

No.	MODELO BIM DE REFERENCIA	REV.
1	L1T1-1100-211-CON-ED-EST-MO-0001.rvt	V00
2	L1T1-1100-212-CON-ED-EST-MO-0001.rvt	V00
3	L1T1-1100-311-CON-ED-EST-MO-0001.rvt	V00
4	L1T1-1150-211-CON-ED-EST-MO-0001.rvt	V00
5	L1T1-1150-212-CON-ED-EST-MO-0001.rvt	V00
6	L1T1-1150-311-CON-ED-EST-MO-0001.rvt	V00
7	L1T1-1200-311-CON-ED-EST-MO-0001.rvt	V00
8	L1T1-1300-411-CON-ED-EST-MO-0001.rvt	V00
9	L1T1-1300-411-CON-ED-EST-MO-0002.rvt	V00
10	L1T1-1310-411-CON-ED-EST-MO-0001.rvt	V00
11	L1T1-1410-311-CON-ED-MEC-MO-0001.rvt	V00
12	L1T1-1420-311-CON-ED-MEC-MO-0001.rvt	V00
13	L1T1-2320-582-CON-ED-EST-MO-0001.rvt	V00
14	L1T1-2330-582-CON-ED-ARQ-MO-0001.rvt	V00
15	L1T1-5110-571-CON-ED-EST-MO-0001.rvt	V00
16	L1T1-5160-311-CON-ED-EST-MO-0001.rvt	V00
17	L1T1-5160-311-CON-ED-ARQ-MO-0001.rvt	V00
18	L1T1-5300-311-CON-ED-MEC-MO-0001.rvt	V00
19	L1T1-5600-311-CON-ED-INS-MO-0001.rvt	V00
20	L1T1-1330-411-CON-ED-ARQ-MO-0011.rvt	V00
21	L1T1-1330-411-CON-ED-ARQ-MO-0012.rvt	V00

No.	PAQUETE DE TRABAJO DE REFERENCIA	REV.
1	XREF-URBANISM_CONTEXT_ST11.rvt	
2	XREF-SECONDARY-STRUCTURE-ST11.rvt	

0 2 10m
1:200

VÁLIDO PARA CONSTRUCCIÓN
20-03-26

METRO BOGOTÁ
GCS Consorcio Consultores PMO Bogotá
CONSORCIO SUPERVISOR PLMB
CHEC

DISEÑÓ:
REN ZHENHUA
Licencia de Arq.nivel I (China): 1101735-614

APROBÓ:
DIEGO ERNESTO DUEÑAS
Mat.: 25202-53876 CND

REVISÓ:
CARLOS MAURICIO BARRETO BARBOSA
Mat.: A4012012-14139353

DIBUJÓ:
EQUIPO CHEC

REVISIÓN No.	FECHA	DESCRIPCIÓN	REVISÓ	APROBÓ	APROBACIÓN CLIENTE
V01	20/03/2026	EMITIDO PARA CONSTRUCCIÓN	C.M.B.B	D.E.D	
V00	31/03/2025	REVISIÓN NO OBJETADA - EMITIDO PARA CONSTRUCCIÓN	F.B.R	E.O.M	
VII	22/07/2024	EMITIDO PARA REVISIÓN Y COMENTARIOS DEL CLIENTE E INTERVENTORÍA - INCLUYE COMENTARIOS /(AJUSTES V4)	F.B.R	E.O.M	
VHH	26/04/2024	EMITIDO PARA REVISIÓN Y COMENTARIOS DEL CLIENTE E INTERVENTORÍA - INCLUYE COMENTARIOS /(AJUSTES V3)	F.B.R	E.O.M	
VGG	30/10/2023	EMITIDO PARA REVISIÓN Y COMENTARIOS DEL CLIENTE E INTERVENTORÍA - INCLUYE COMENTARIOS /(AJUSTES V2)	J.E.M	M.B.M	
VFF	20/04/2023	EMITIDO PARA REVISIÓN Y COMENTARIOS DEL CLIENTE E INTERVENTORÍA - INCLUYE COMENTARIOS /(AJUSTES)	J.E.M	M.B.M	
VEE	18/12/2022	EMITIDO PARA REVISIÓN Y COMENTARIOS DEL CLIENTE E INTERVENTORÍA - INCLUYE COMENTARIOS /(NO APLICA)	J.E.M	M.B.M	
VDD	11/11/2022	EMITIDO PARA REVISIÓN Y COMENTARIOS DEL CLIENTE E INTERVENTORÍA - INCLUYE COMENTARIOS /(90% ACCESOS)	J.E.M	M.B.M	
VCC	22/08/2022	EMITIDO PARA REVISIÓN Y COMENTARIOS DEL CLIENTE E INTERVENTORÍA - INCLUYE COMENTARIOS /(NO APLICA)	J.E.M	M.B.M	
VBB	06/12/2021	EMITIDO PARA REVISIÓN Y COMENTARIOS DEL CLIENTE E INTERVENTORÍA	J.E.M	M.B.M	

METRO LÍNEA 1

DIRECTOR DE INTERVENTORÍA:
JAVIER DESCARGA N.
Mat.:25202-68697 CND

ESPECIALISTA INTERVENTORÍA:
CARLOS ALBERTO HOYOS SOTO
Mat.:A25072000-14251682

FECHA:
MARZO 2026

METRO LÍNEA 1
CONTRATO DE CONCESIÓN No. 163 DE 2019

PROYECTO PRIMERA LÍNEA DEL METRO DE BOGOTÁ - TRAMO 1

INFRAESTRUCTURA VIAL

ARQUITECTURA

ESTACIÓN METRO 11 (CALLE 1)
GENERAL
VISTA EN PLANTA Y 3D - NIVEL INTERMEDIO

PLANCHA No: L1T1-0000-311-CON-ED-ARQ-PL-0001_06_V01
ARCHIVO: L1T1-0000-311-CON-ED-ARQ-MO-0001_V00.rvt
ESCALA: INDICADA
FECHA: DICIEMBRE 2021
REVISIÓN No. V01
PLANO No. 06 DE 97