L1T1-CON-CAL-FR-0120 - B1 : 1000x707mm

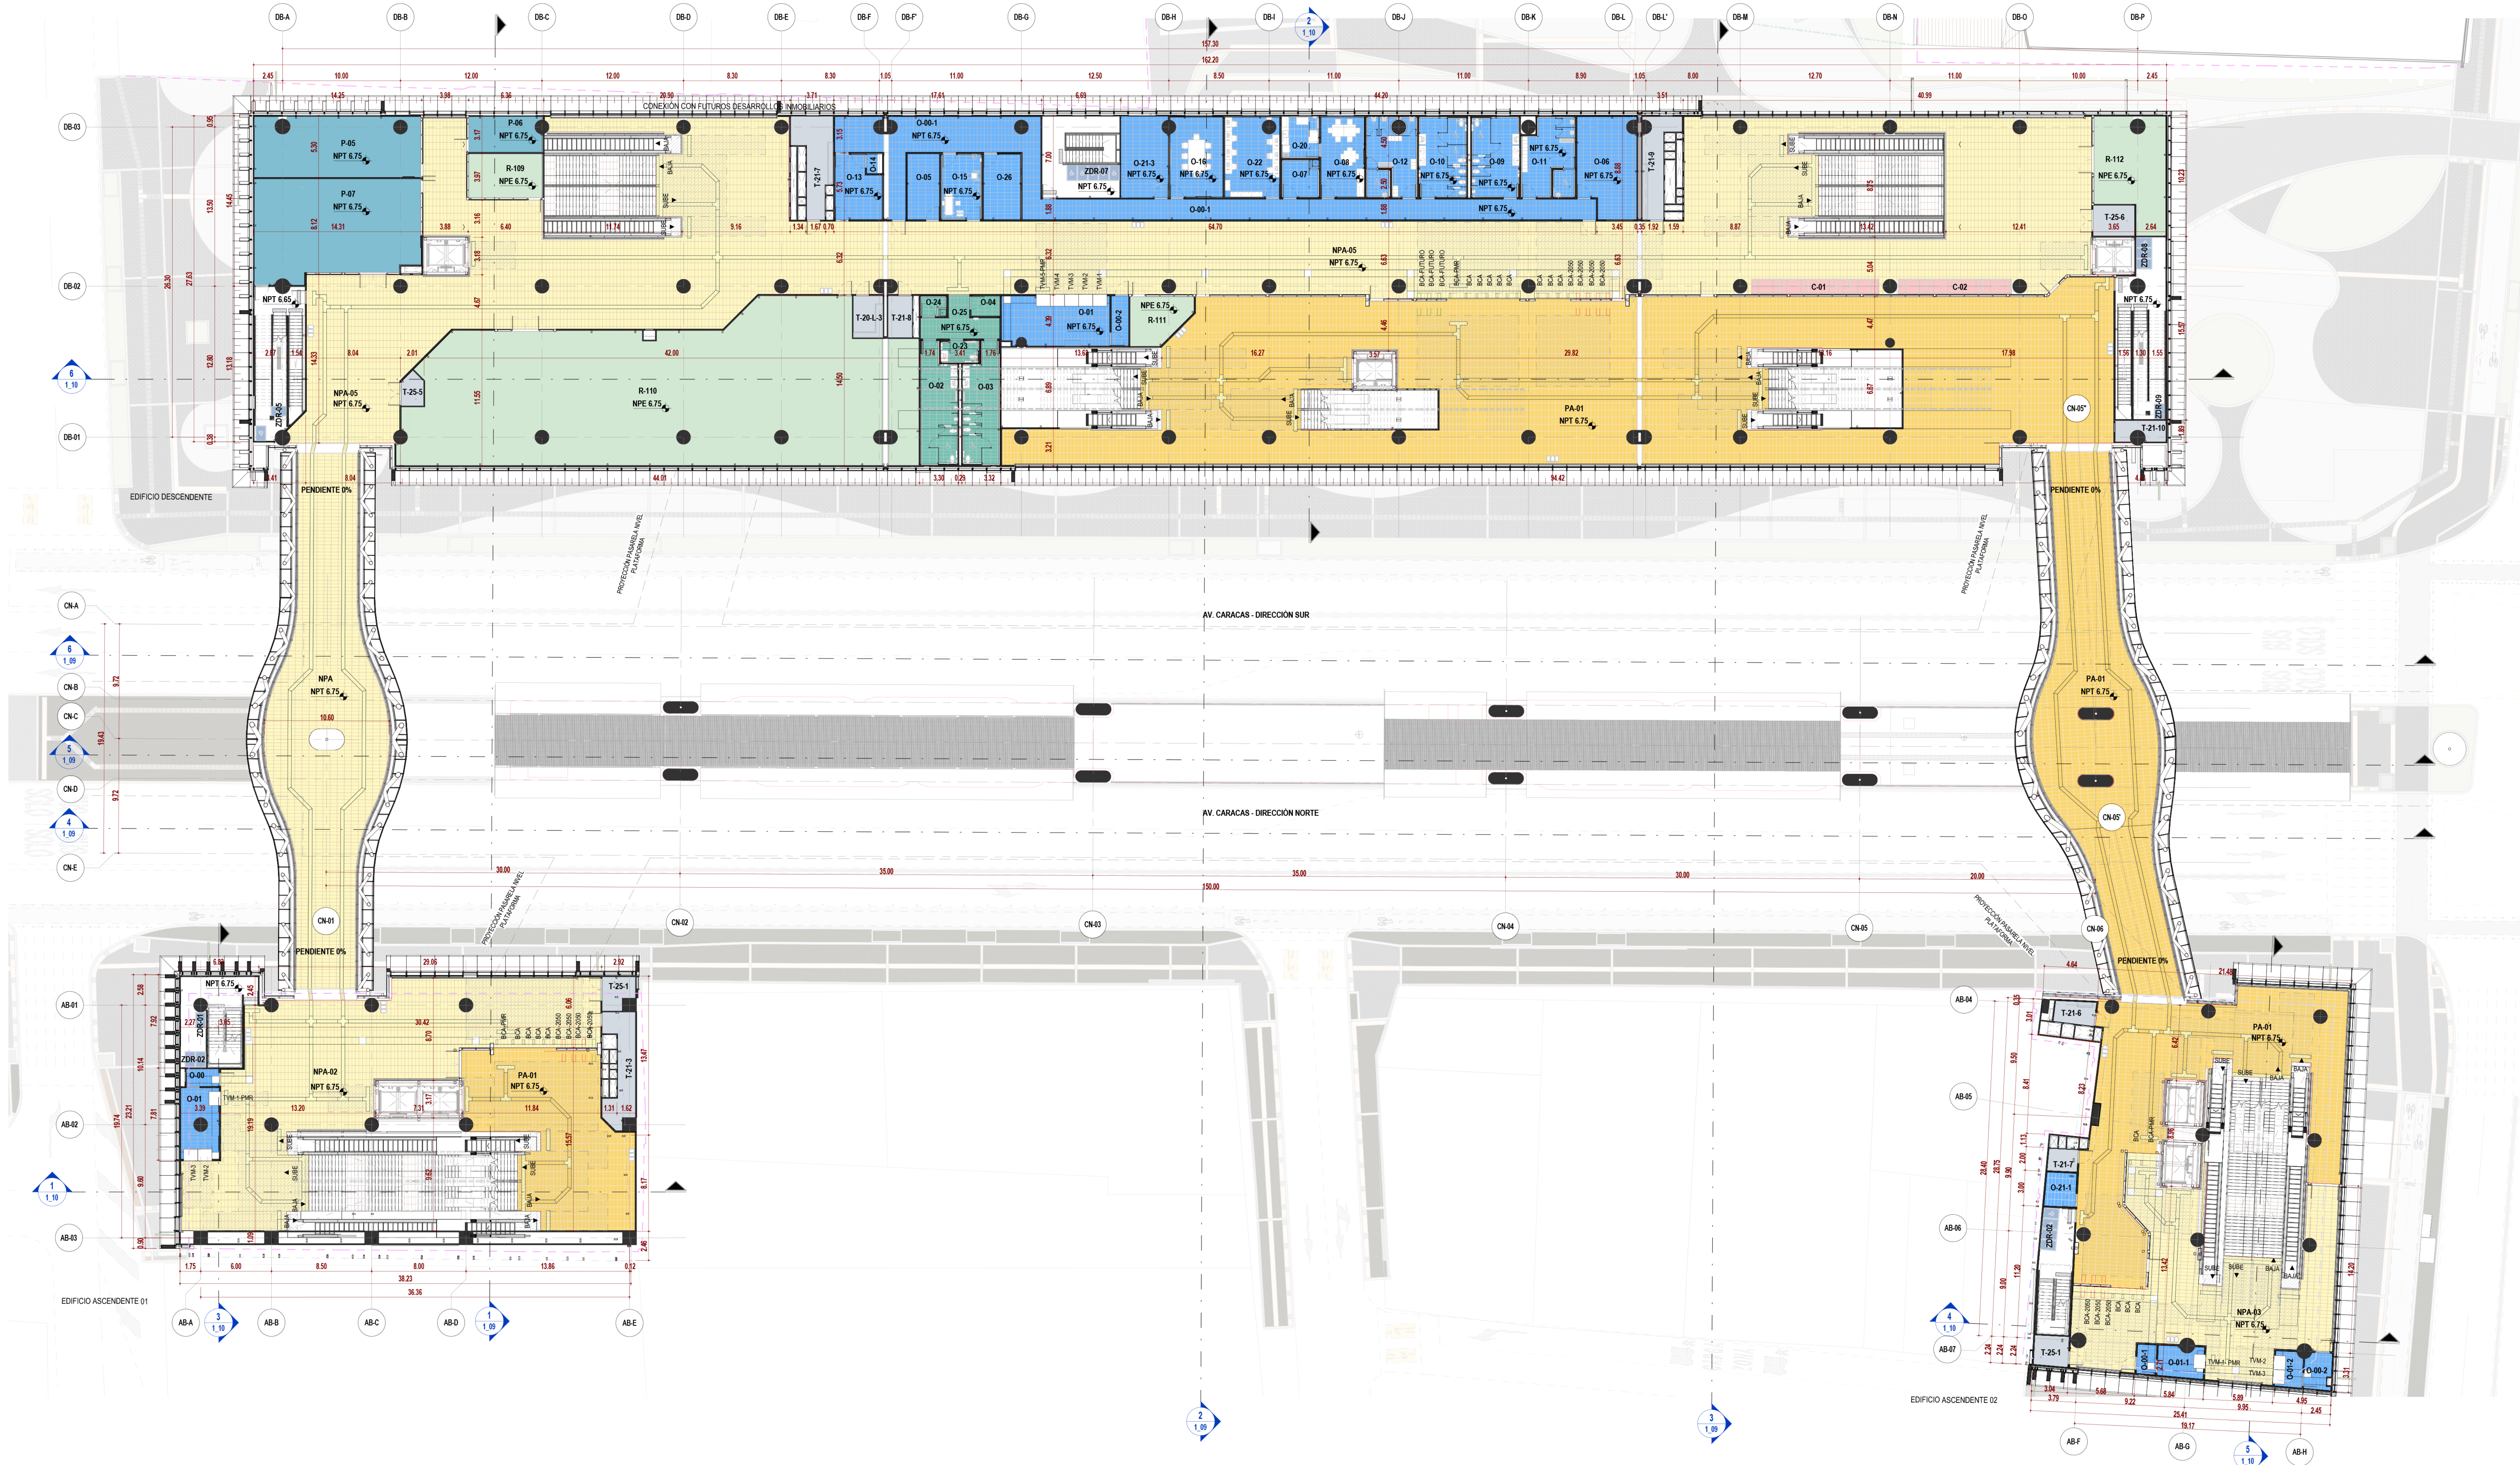

2 NIVEL INTERMEDIO_GENERAL
ESC: 1 : 200

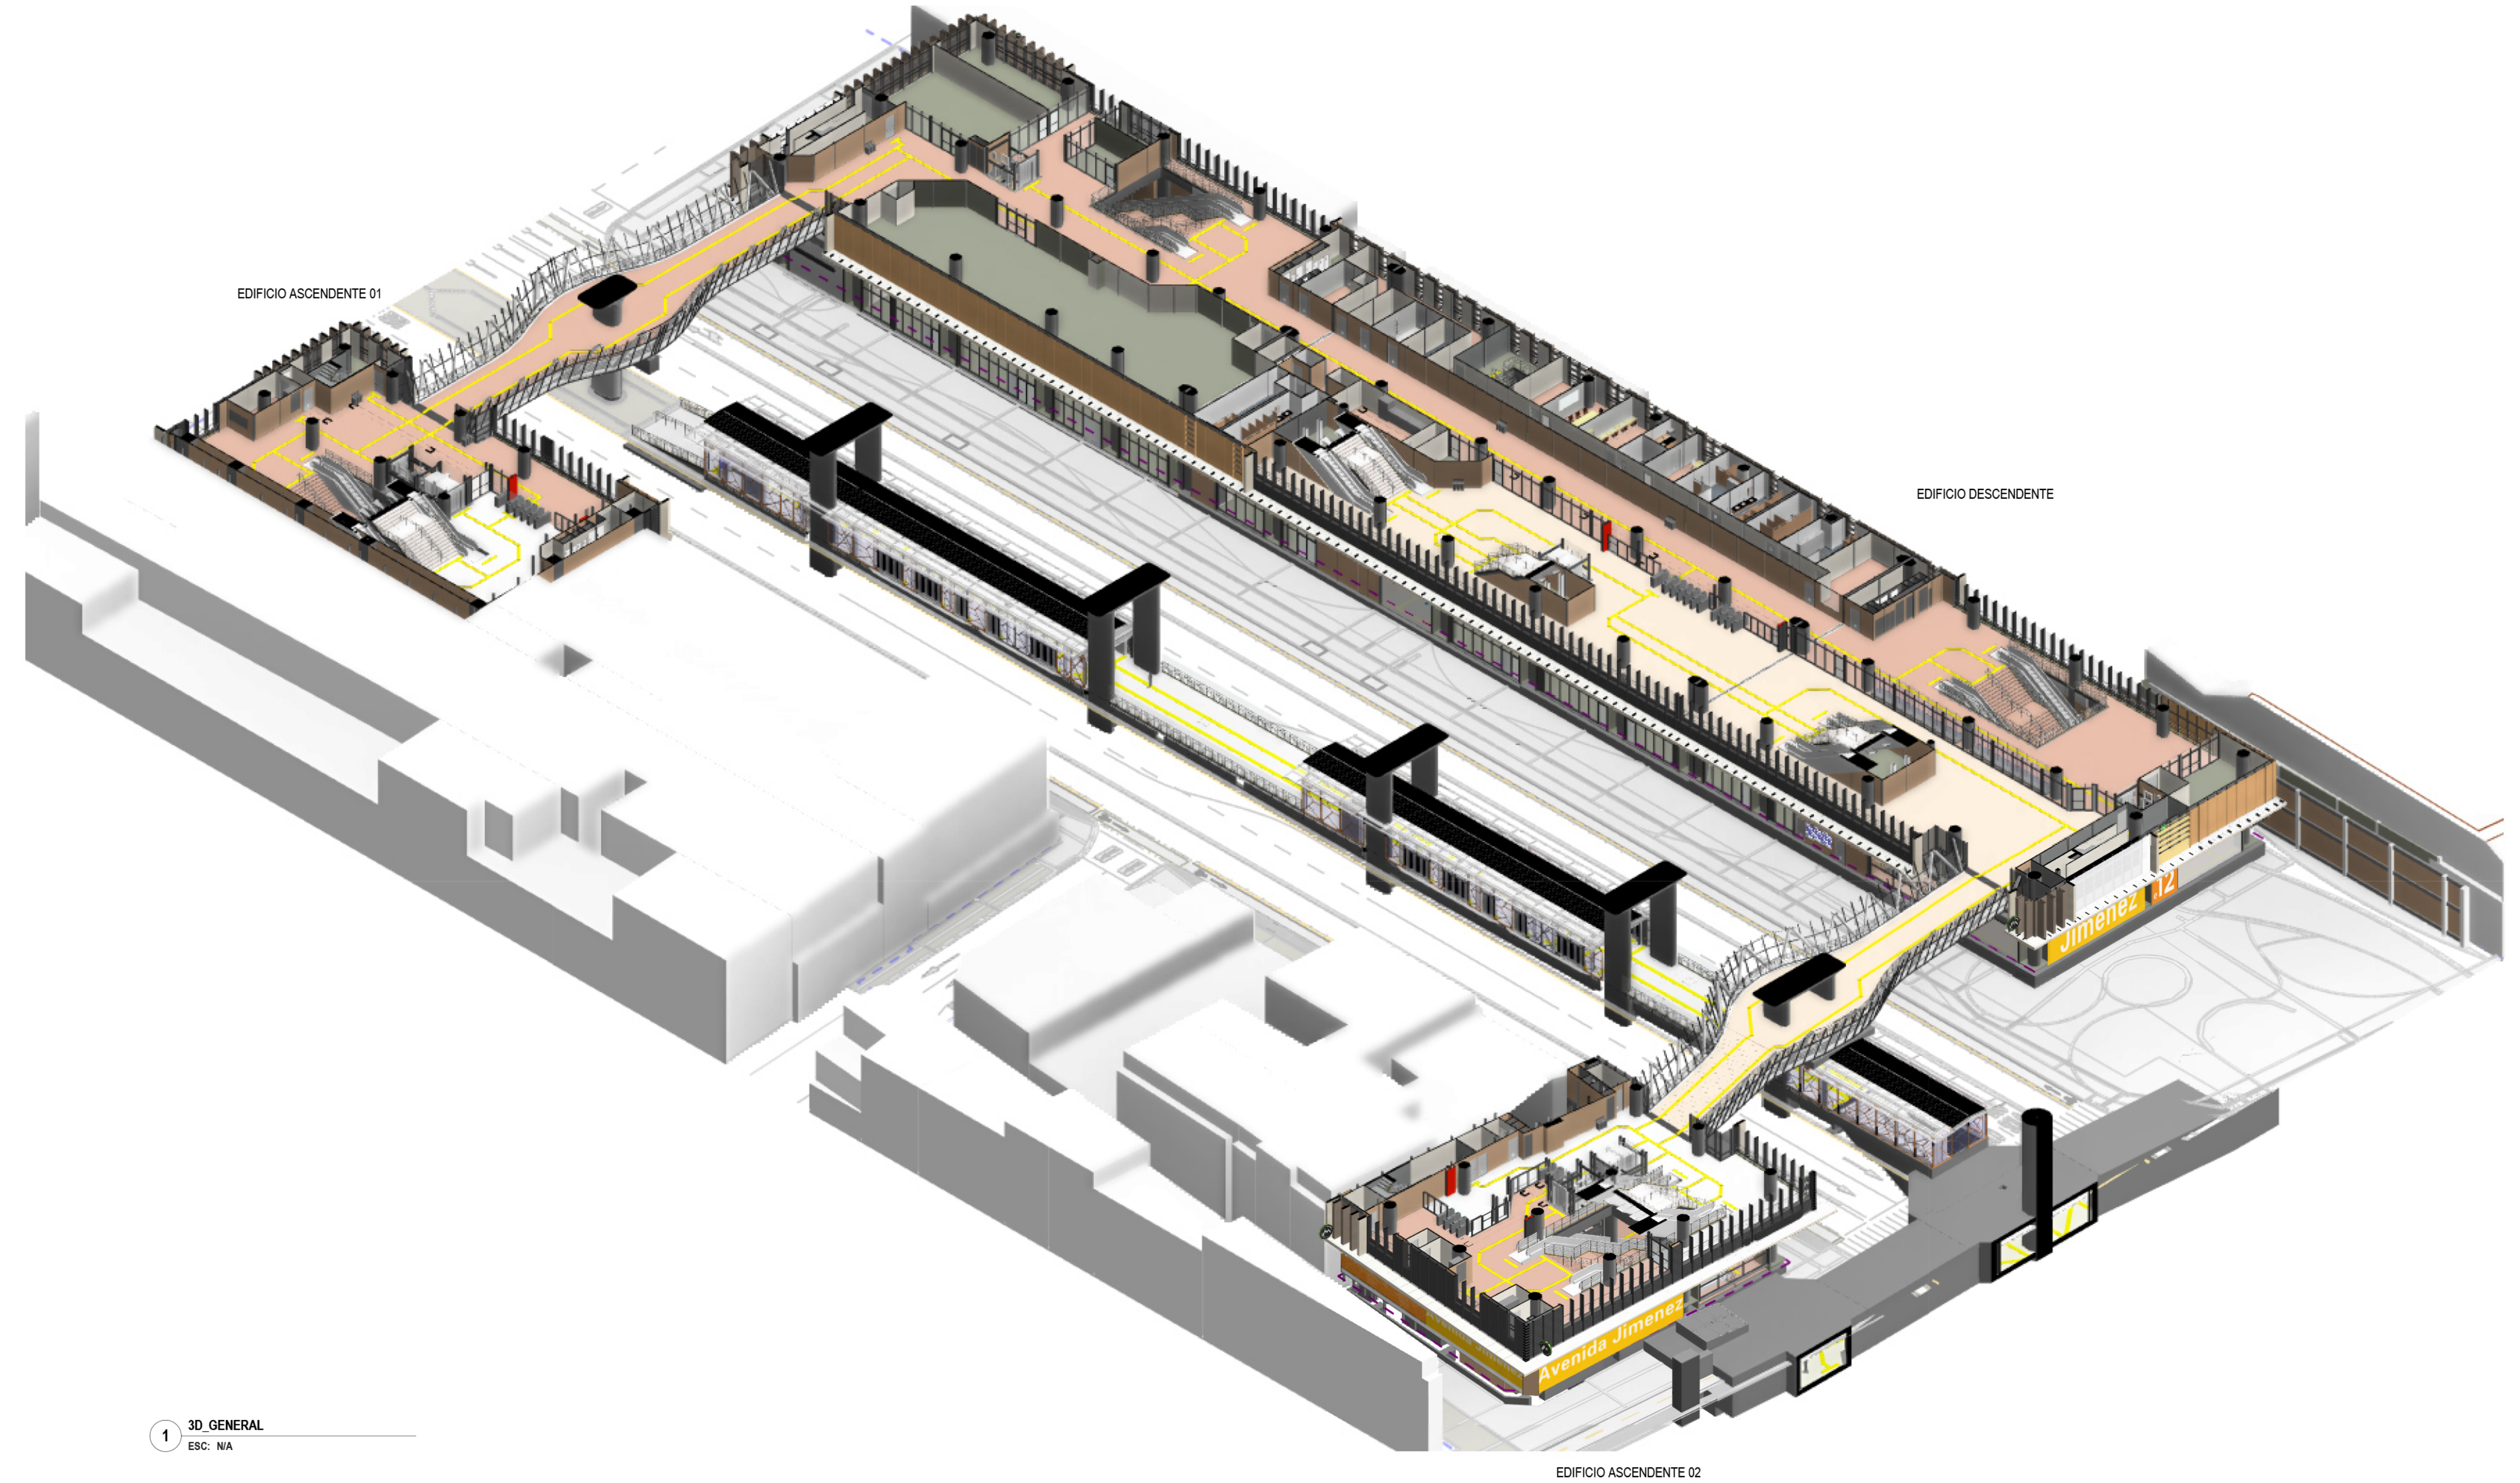

1 3D_GENERAL
ESC: N/A

TABLA DE ÁREAS ÚTILES (NIVEL INTERMEDIO)

CÓDIGO	NOMBRE	ÁREA (m²)	DEPARTAMENTO
EDIFICIO ASCENDENTE 01			
ARQ_PL_02_INTERMEDIO			
NPA-02	ÁREA NO PAGA	331.95	ÁREA NO PAGA
O-00	CIRCULACIÓN ÁREAS OPERATIVAS	4.23	ÁREA OPERATIVA
O-01	VENTA AUTOMÁTICA DE BOLETOS	18.71	ÁREA OPERATIVA
PA-01	ÁREA PAGA	159.91	ÁREA PAGA
T-21-3	ÁREA DE INSPECCIÓN	19.06	ÁREA TÉCNICA
T-25-1	NODO DE ACCESO DE TELECOMUNICACIONES	6.86	ÁREA TÉCNICA
ZDR-01	ZONA DE REFUGIO (PMR)	1.22	ZONA DE REFUGIO
ZDR-02	ZONA DE REFUGIO (PMR)	2.44	ZONA DE REFUGIO
EDIFICIO ASCENDENTE 02			
ARQ_PL_02_INTERMEDIO			
NPA-03	ÁREA NO PAGA	223.87	ÁREA NO PAGA
O-00-1	CIRCULACIÓN ÁREAS OPERATIVAS	4.17	ÁREA OPERATIVA
O-00-2	CIRCULACIÓN ÁREAS OPERATIVAS	6.76	ÁREA OPERATIVA
O-01-1	VENTA AUTOMÁTICA DE BOLETOS	9.87	ÁREA OPERATIVA
O-01-2	VENTA AUTOMÁTICA DE BOLETOS	6.95	ÁREA OPERATIVA
O-21-1	ALMACENAMIENTO DE LA ESTACIÓN	7.54	ÁREA OPERATIVA
PA-01	ÁREA PAGA	253.29	ÁREA PAGA
T-21-6	ÁREA DE INSPECCIÓN	6.61	ÁREA TÉCNICA
T-21-7	ÁREA DE INSPECCIÓN	4.72	ÁREA TÉCNICA
T-25-1	NODO DE ACCESO DE TELECOMUNICACIONES	7.41	ÁREA TÉCNICA
ZDR-02	ZONA DE REFUGIO (PMR)	4.91	ZONA DE REFUGIO
EDIFICIO DESCENDENTE			
ARQ_PL_02_INTERMEDIO			
C-01	ÁREAS DE USO CULTURAL	13.96	ÁREA CULTURAL
C-02	ÁREAS DE USO CULTURAL	12.41	ÁREA CULTURAL
NPA-05	ÁREA NO PAGA	1354.95	ÁREA NO PAGA
O-00-1	CIRCULACIÓN ÁREAS OPERATIVAS	151.99	ÁREA OPERATIVA
O-00-2	CIRCULACIÓN ÁREAS OPERATIVAS	6.37	ÁREA OPERATIVA
O-01	VENTA AUTOMÁTICA DE BOLETOS	38.09	ÁREA OPERATIVA
O-02	BAÑOS PÚBLICOS DE HOMBRES	29.85	SERVICIO PÚBLICO
O-03	BAÑOS PÚBLICOS DE MUJERES	29.88	SERVICIO PÚBLICO
O-04	CONTROL DE ACCESO BAÑOS PÚBLICOS	4.23	SERVICIO PÚBLICO
O-05	LOCAL DE INFORMACIÓN	15.41	ÁREA OPERATIVA
O-06	OFICINA DEL SUPERVISOR DE LA ESTACIÓN	40.42	ÁREA OPERATIVA
O-07	CUARTO DE LIMPIEZA	10.04	ÁREA OPERATIVA
O-08	SALA DE DESCANSO PARA EMPLEADOS	25.08	ÁREA OPERATIVA
O-09	BAÑOS EMPLEADOS HOMBRES	27.39	ÁREA OPERATIVA
O-10	BAÑOS EMPLEADOS MUJERES	27.39	ÁREA OPERATIVA
O-11	VESTIDORES EMPLEADOS HOMBRES	28.42	ÁREA OPERATIVA
O-12	VESTIDORES EMPLEADOS MUJERES	27.65	ÁREA OPERATIVA
O-13	LOCAL DE POLICÍA	19.76	ÁREA OPERATIVA
O-14	CALABOZO	2.22	ÁREA OPERATIVA
O-15	LOCAL PRIMEROS AUXILIOS	18.98	ÁREA OPERATIVA
O-16	SALA DE REUNIONES	30.21	ÁREA OPERATIVA
O-20	SALA DE LACTANCIA	11.22	ÁREA OPERATIVA
O-21-3	ALMACENAMIENTO DE LA ESTACIÓN	27.00	ÁREA OPERATIVA
O-22	OFICINA DE MANTENIMIENTO	30.52	ÁREA OPERATIVA
O-23	BAÑO PÚBLICO - FAMILIAR	5.87	SERVICIO PÚBLICO
O-24	CUARTO DE LIMPIEZA DE BAÑOS PÚBLICOS	3.71	SERVICIO PÚBLICO
O-25	BAÑO PÚBLICO - CORREDOR OPERACIONAL	15.72	SERVICIO PÚBLICO
O-26	ALMACENAMIENTO DE BASURAS METRO	17.47	ÁREA OPERATIVA
P-05	BIBLIOMETRO	68.57	ÁREA PÚBLICA
P-06	ESPACIO IPES (INSTITUTO PARA LA ECONOMÍA SOCIAL)	18.26	ÁREA PÚBLICA
P-07	SALÓN MÚLTIPLE EMB	112.96	ÁREA PÚBLICA
PA-01	ÁREA PAGA	1018.66	ÁREA PAGA
R-109	SERVICIOS ADICIONALES - ÁREA DE SERVICIO	23.16	SERVICIOS ADICIONALES - ÁREA NO PAGA
R-110	SERVICIOS ADICIONALES - ÁREA DE SERVICIO	503.83	SERVICIOS ADICIONALES - ÁREA NO PAGA
R-111	SERVICIOS ADICIONALES - ÁREA DE SERVICIO	18.58	SERVICIOS ADICIONALES - ÁREA NO PAGA
R-112	SERVICIOS ADICIONALES - ÁREA DE SERVICIO	50.68	SERVICIOS ADICIONALES - ÁREA NO PAGA
T-20-L-3	MEDIDORES (LUZ)	8.77	ÁREA TÉCNICA
T-21-7	ÁREA DE INSPECCIÓN	20.92	ÁREA TÉCNICA
T-21-8	ÁREA DE INSPECCIÓN	7.22	ÁREA TÉCNICA
T-21-9	ÁREA DE INSPECCIÓN	17.11	ÁREA TÉCNICA
T-21-10	ÁREA DE INSPECCIÓN	6.64	ÁREA TÉCNICA
T-25-5	NODO DE ACCESO DE TELECOMUNICACIONES	4.78	ÁREA TÉCNICA
T-25-6	NODO DE ACCESO DE TELECOMUNICACIONES	9.02	ÁREA TÉCNICA
ZDR-05	ZONA DE REFUGIO (PMR)	1.20	ZONA DE REFUGIO
ZDR-06	ZONA DE REFUGIO (PMR)	1.21	ZONA DE REFUGIO
ZDR-07	ZONA DE REFUGIO (PMR)	6.07	ZONA DE REFUGIO
ZDR-08	ZONA DE REFUGIO (PMR)	3.65	ZONA DE REFUGIO
ZDR-09	ZONA DE REFUGIO (PMR)	1.22	ZONA DE REFUGIO
NAVE CENTRAL			
ARQ_PL_02_INTERMEDIO			
NPA	ÁREA NO PAGA	288.38	ÁREA NO PAGA
PA-01	ÁREA PAGA	300.22	ÁREA PAGA
TOTAL NIVEL INTERMEDIO		5597.78	

TABLA DE ÁREAS ÚTILES POR DEPARTAMENTO (NIVEL INTERMEDIO)

DEPARTAMENTO	ÁREA (m²)
EDIFICIO ASCENDENTE 01	
ARQ_PL_02_INTERMEDIO	
ZONA DE REFUGIO	3.66
ÁREA NO PAGA	331.95
ÁREA OPERATIVA	22.93
ÁREA PAGA	159.91
ÁREA TÉCNICA	25.92
EDIFICIO ASCENDENTE 02	
ARQ_PL_02_INTERMEDIO	
ZONA DE REFUGIO	4.91
ÁREA NO PAGA	223.87
ÁREA OPERATIVA	35.30
ÁREA PAGA	253.29
ÁREA TÉCNICA	18.74
EDIFICIO DESCENDENTE	
ARQ_PL_02_INTERMEDIO	
SERVICIO PÚBLICO	89.25
SERVICIOS ADICIONALES - ÁREA NO PAGA	596.26
ZONA DE REFUGIO	13.35
ÁREA CULTURAL	26.37
ÁREA NO PAGA	1354.95
ÁREA OPERATIVA	555.63
ÁREA PAGA	1018.66
ÁREA PÚBLICA	199.79
ÁREA TÉCNICA	74.46
NAVE CENTRAL	
ARQ_PL_02_INTERMEDIO	
ÁREA NO PAGA	288.38
ÁREA PAGA	300.22
TOTAL NIVEL INTERMEDIO	5597.78

TABLA GENERAL DE NIVELES

NOMBRE	NIVEL	ELEVACIÓN (m)
ARQ_PL_05_CUB_NVC	CUBIERTA NAVE CENTRAL	24.75
ARQ_PL_04_CUB_EDIFICACIONES	CUBIERTA EDIFICACIONES	22.09
ARQ_PL_02.2_TOR	TOPE DE RIEL	14.35
ARQ_PL_03_PLATAFORMA	PLATAFORMA	15.49
ARQ_PL_02_INTERMEDIO	INTERMEDIO	6.75
ARQ_PL_00.1_ACCESO	ACCESO	-2.40
ARQ_PL_00.2_ACCESO	ACCESO	-2.10
ARQ_PL_00.3_ACCESO	ACCESO	-1.85
ARQ_PL_00.4_ACCESO	ACCESO	-1.65
ARQ_PL_00.5_ACCESO	ACCESO	-1.45
ARQ_PL_00.6_ACCESO	ACCESO	-1.25
ARQ_PL_00.7_ACCESO	ACCESO	-0.85
ARQ_PL_00.8_ACCESO	ACCESO	-0.45
ARQ_PL_00.9_ACCESO	ACCESO	-0.20
ARQ_PL_00.10_ACCESO	ACCESO	-0.15
ARQ_PL_01.1_ACCESO	ACCESO	0.97
ARQ_PL_01_ACCESO	ACCESO*	2589.25 M.S.N.M
ARQ_PL_00.1_SÓTANO	SÓTANO	-7.93
ARQ_PL_00.2_SÓTANO	SÓTANO	-7.45
ARQ_PL_00.3_SÓTANO	SÓTANO	-6.98
ARQ_PL_00.4_SÓTANO	SÓTANO	-6.50
ARQ_PL_00.5_SÓTANO	SÓTANO	-4.70
ARQ_PL_00_SÓTANO	SÓTANO	-8.40

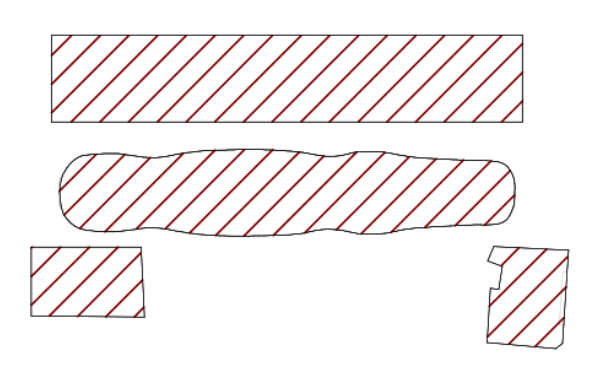

PLANO CLAVE ESTACIÓN 12

VÁLIDO PARA CONSTRUCCIÓN
31-03-26

LOCALIZACIÓN

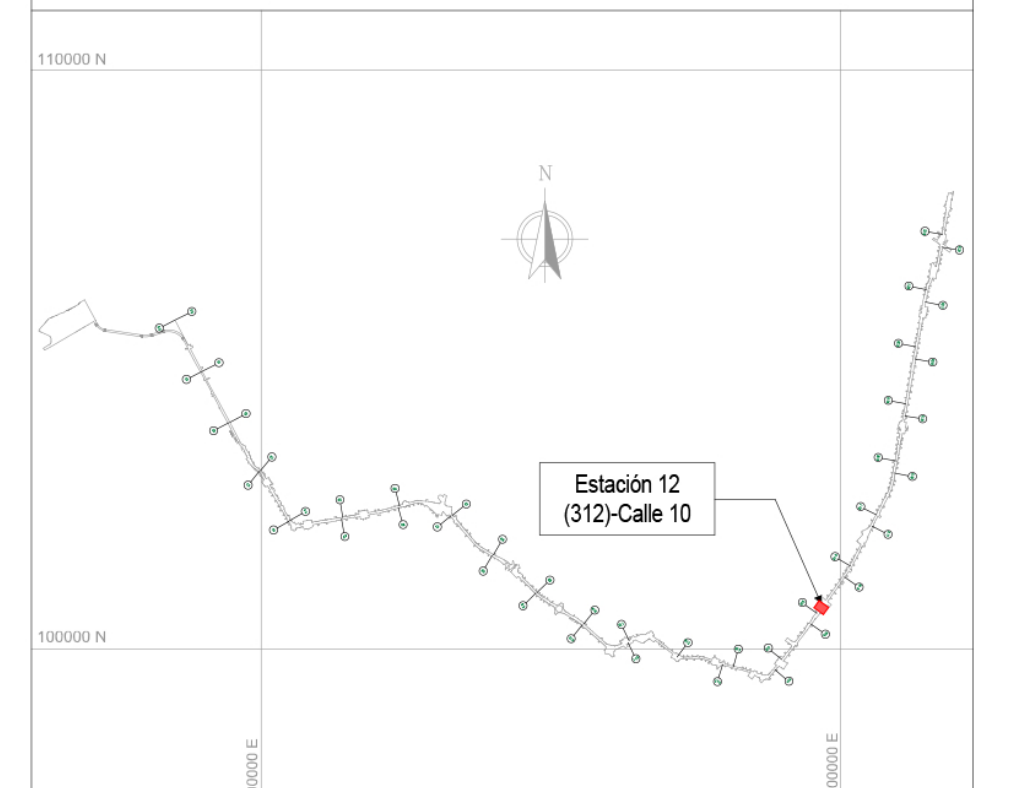

NOTAS

01 TODAS LAS DIMENSIONES ESTÁN CONFIGURADAS EN METROS A MENOS QUE SE INDIQUE UNA UNIDAD DE MEDIDA DIFERENTE.

02 TODAS LAS MEDIDAS, UBICACIÓN Y NIVELES DEBEN VERIFICARSE EN EL LUGAR DE CONSTRUCCIÓN.

03 EL NIVEL DE ACCESO AL EDIFICIO PL 01 CORRESPONDE AL +0,00 DE LA ESTACIÓN Y REFERENCIA AL NIVEL 2589.25 M.S.N.M.

04 LOS NOMBRES ESPECÍFICOS DE LAS ÁREAS PUEDEN SER CONSULTADAS EN EL PLANO NO. 3 Ó EN LAS VISTAS EN PLANTA.

05 LOS COLORES QUE SE MUESTRAN EN LOS PLANOS COMO PROYECCIÓN DE ELEMENTOS ARQUITECTÓNICOS COMO CUBIERTAS FACHADAS MUROS ETC. NO REPRESENTAN LA MATERIALIDAD Y REALIDAD DE ACABADOS DEL PROYECTO, SOLO SON INDICATIVOS PARA REALIZAR UNA CORRECTA LECTURA DE LA PLANIMETRÍA.

06 LAS ESCALERAS ELÉCTRICAS INDICAN SU SENTIDO CON LA SIGUIENTE NOMENCLATURA: "SUBE" Y "BAJA".

07 SE DEBEN REVISAR LOS NIVELES ESTRUCTURALES PARA NIVEL DE ACCESO PL_01 Y SUBNIVELES, PL_02 (INTERMEDIO), PL_03 (PLATAFORMA) CON LA PLANIMETRÍA DE PLACAS ESTRUCTURALES EN LOS ENTREGABLES L1T1-1300-412-CON-ED-EST-PL-0045, 86, 88, 129, 130, 131, 134, 135, 136, RESPECTIVAMENTE. EL NIVEL ESTRUCTURAL (NE) REFERENCIA LOS ESPACIOS DONDE SE DEBE ACONDICIONAR EL ACABADO DE PISO SEGÚN CORRESPONDA, CON LOS NIVELES DE PISO TERMINADO (NPT). LOS NIVELES PROYECTADOS DE EMPATE (NPE) EN LAS ÁREAS DE SERVICIOS ADICIONALES, REFERENCIAN LA ADECUACIÓN DE LOS DESNIVELES EN ESTAS ÁREAS; QUEDA COMO RESPONSABILIDAD DEL LOCATARIO DEFINIR Y ACONDICIONAR ESTE ACABADO DE PISO (NPE) EN LÍNEA CON EL NIVEL (NPT) DE ESPACIOS COLINDANTES. EL NIVEL ESTRUCTURAL (NE) SE ENCUENTRA A (- 0.10M) POR DEBAJO DE LOS NIVELES DE PISO TERMINADO (NPT) Y LOS NIVELES PROYECTADOS DE EMPATE (NPE) MARCADOS EN LA PLANIMETRÍA.

08 RESPECTO A LAS ÁREAS CONSTRUIDAS Y DE ACUERDO CON LA COMUNICACIÓN EXTS22-0002544 DE EMB, SE IDENTIFICA QUE EL CONCESIONARIO SE ENCUENTRA BUSCANDO ESTRATEGIAS PARA MEJORAR EL DISEÑO CON EL PROGRAMA ARQUITECTÓNICO, UNA DE ESTAS ESTRATEGIAS ES MEJORAR EL FUNCIONAMIENTO DEL DISEÑO URBANO Y BRINDAR UNA SOLUCIÓN INTEGRAL RESPECTO A LOS INMUEBLES DE INTERÉS CULTURAL. DE ACUERDO CON LO ANTERIOR, PARA LA EMB, ESTAS ACTIVIDADES OBEDECEN AL PROCESO NATURAL DE LOS ESTUDIOS Y DISEÑOS DEFINITIVOS QUE DEBE DESARROLLAR METRO LÍNEA 1.

CONVENCIONES

▬ ▬ ▬	LÍMITE DE INTERVENCIÓN
▬ ▬ ▬	HUELLA APÉNDICE TÉCNICO
▬ ▬ ▬	HUELLA LÍMITE LEVANTAMIENTO TOPOGRÁFICO
■	MURO DIVISORIO
— — —	PROYECCIÓN NIVEL SUPERIOR
🟩	SERVICIOS ADICIONALES ÁREA NO PAGA
🟩	SERVICIOS ADICIONALES ÁREA PAGA
🟩	SERVICIO PÚBLICO
🟦	ZONA DE REFUGIO
🟥	ÁREA CULTURAL
🟩	CADE
🟨	ÁREA NO PAGA
🟦	ÁREA OPERATIVA
🟧	ÁREA PAGA
🟦	ÁREA PÚBLICA
⬜	ÁREA TÉCNICA

No.	PLANOS DE REFERENCIA	REV.

No.	MODELO BIM DE REFERENCIA	REV.
1	L1T1-1100-212-CON-ED-EST-MO-0001.rvt	V00
2	L1T1-1100-213-CON-ED-EST-MO-0001.rvt	V00
3	L1T1-1100-312-CON-ED-EST-MO-0001.rvt	V00
4	L1T1-1150-212-CON-ED-EST-MO-0001.rvt	V00
5	L1T1-1150-213-CON-ED-EST-MO-0001.rvt	V00
6	L1T1-1150-312-CON-ED-EST-MO-0001.rvt	V00
7	L1T1-1200-312-CON-ED-EST-MO-0001.rvt	V00
8	L1T1-1300-412-CON-ED-EST-MO-0001.rvt	V00
9	L1T1-1300-412-CON-ED-EST-MO-0002.rvt	V00
10	L1T1-1300-412-CON-ED-EST-MO-0003.rvt	V00
11	L1T1-1310-412-CON-ED-EST-MO-0001.rvt	V00
12	L1T1-1410-312-CON-ED-MEC-MO-0001.rvt	V00
13	L1T1-1420-312-CON-ED-MEC-MO-0001.rvt	V00
14	L1T1-2320-584-CON-ED-EST-MO-0001.rvt	V00
15	L1T1-2330-584-CON-ED-ARQ-MO-0001.rvt	V00
16	L1T1-2430-551-CON-ED-ARQ-MO-0001.rvt	V00
17	L1T1-2430-551-CON-ED-EST-MO-0001.rvt	V00
18	L1T1-5160-312-CON-ED-ARQ-MO-0001.rvt	V00
19	L1T1-5160-312-CON-ED-EST-MO-0001.rvt	V00
20	L1T1-5300-312-CON-ED-MEC-MO-0001.rvt	V00
21	L1T1-5600-312-CON-ED-INS-MO-0001.rvt	V00
22	L1T1-1330-412-CON-ED-ARQ-MO-0011.rvt	V00
23	L1T1-1330-412-CON-ED-ARQ-MO-0012.rvt	V00
24	L1T1-1330-412-CON-ED-ARQ-MO-0013.rvt	V00

No.	PAQUETE DE TRABAJO DE REFERENCIA	REV.
1	XREF-URBANISM_CONTEXT_ST12.rvt	
2	XREF-SECONDARY-STRUCTURE-ST12.rvt	

0 2 10m
1:200

METRO BOGOTÁ
GCS Consorcio Consultores PMO Bogotá
CONSORCIO SUPERVISOR PLMB
CHEC

DISEÑO:	REN ZHENHUA Licencia de Arq.nivel I (China): 1101735-614
APROBÓ:	DIEGO ERNESTO DUEÑAS Mat.: 25202-53876 CND
REVISÓ:	CARLOS MAURICIO BARRETO BARBOSA Mat.: A4012012-14139353
DIBUJÓ:	EQUIPO CHEC

REVISIÓN No.	FECHA	DESCRIPCIÓN	REVISÓ	APROBÓ	APROBACIÓN CLIENTE
V02	31/03/2026	EMITIDO PARA CONSTRUCCIÓN	C.M.B.B	D.E.D	
V01	16/07/2025	REVISIÓN NO OBJETADA - EMITIDO PARA CONSTRUCCIÓN	F.B.R	M.M.R	
VB1	20/03/2025	EMITIDO PARA REVISIÓN Y COMENTARIOS DEL CLIENTE E INTERVENTORÍA	F.B.R	E.O.M	
V00	13/02/2025	REVISIÓN NO OBJETADA - EMITIDO PARA CONSTRUCCIÓN	F.B.R	E.O.M	
VGG	18/10/2024	EMITIDO PARA REVISIÓN Y COMENTARIOS DEL CLIENTE E INTERVENTORÍA - INCLUYE COMENTARIOS /(AJUSTES V2)	F.B.R	E.O.M	
VFF	21/05/2024	EMITIDO PARA REVISIÓN Y COMENTARIOS DEL CLIENTE E INTERVENTORÍA - INCLUYE COMENTARIOS /(AJUSTES)	F.B.R	E.O.M	
VEE	25/01/2023	EMITIDO PARA REVISIÓN Y COMENTARIOS DEL CLIENTE E INTERVENTORÍA - INCLUYE COMENTARIOS /(90% ACCESOS)	J.E.M	M.B.M	
VDD	18/12/2022	EMITIDO PARA REVISIÓN Y COMENTARIOS DEL CLIENTE E INTERVENTORÍA - INCLUYE COMENTARIOS /(NAVE CENTRAL)	J.E.M	M.B.M	
VCC	22/08/2022	EMITIDO PARA REVISIÓN Y COMENTARIOS DEL CLIENTE E INTERVENTORÍA - INCLUYE COMENTARIOS /(ENTREGA 90%)	J.E.M	M.B.M	
VBB	06/12/2021	EMITIDO PARA REVISIÓN Y COMENTARIOS DEL CLIENTE E INTERVENTORÍA	J.E.M	M.B.M	

METRO LÍNEA 1

METRO LÍNEA 1
CONTRATO DE CONCESIÓN No. 163 DE 2019

PROYECTO PRIMERA LÍNEA DEL METRO DE BOGOTÁ - TRAMO 1

DIRECTOR DE INTERVENTORÍA:	JAVIER DESCARGA N. Mat.:25202-68697 CND
ESPECIALISTA INTERVENTORÍA:	CARLOS ALBERTO HOYOS SOTO Mat.:A25072000-14251682
FECHA:	MARZO 2026

INFRAESTRUCTURA VIAL
ARQUITECTURA
ESTACIÓN METRO 12 - (CALLE 10)
NAVE CENTRAL - EDIFICIO ASCENDENTE 01 - EDIFICIO ASCENDENTE 02 - EDIFICIO DESCENDENTE
VISTA EN PLANTA Y 3D - NIVEL INTERMEDIO

PLANCHA No:	L1T1-0000-312-CON-ED-ARQ-PL-0001_06_V02
ARCHIVO:	L1T1-0000-312-CON-ED-ARQ-MO-0001_V01.rvt
ESCALA:	INDICADA
FECHA:	JUNIO 2021
REVISIÓN No.	V02
PLANO No.	06 DE 100