L1T1-CON-CAL-FR-0120 - B1 : 1000x707mm

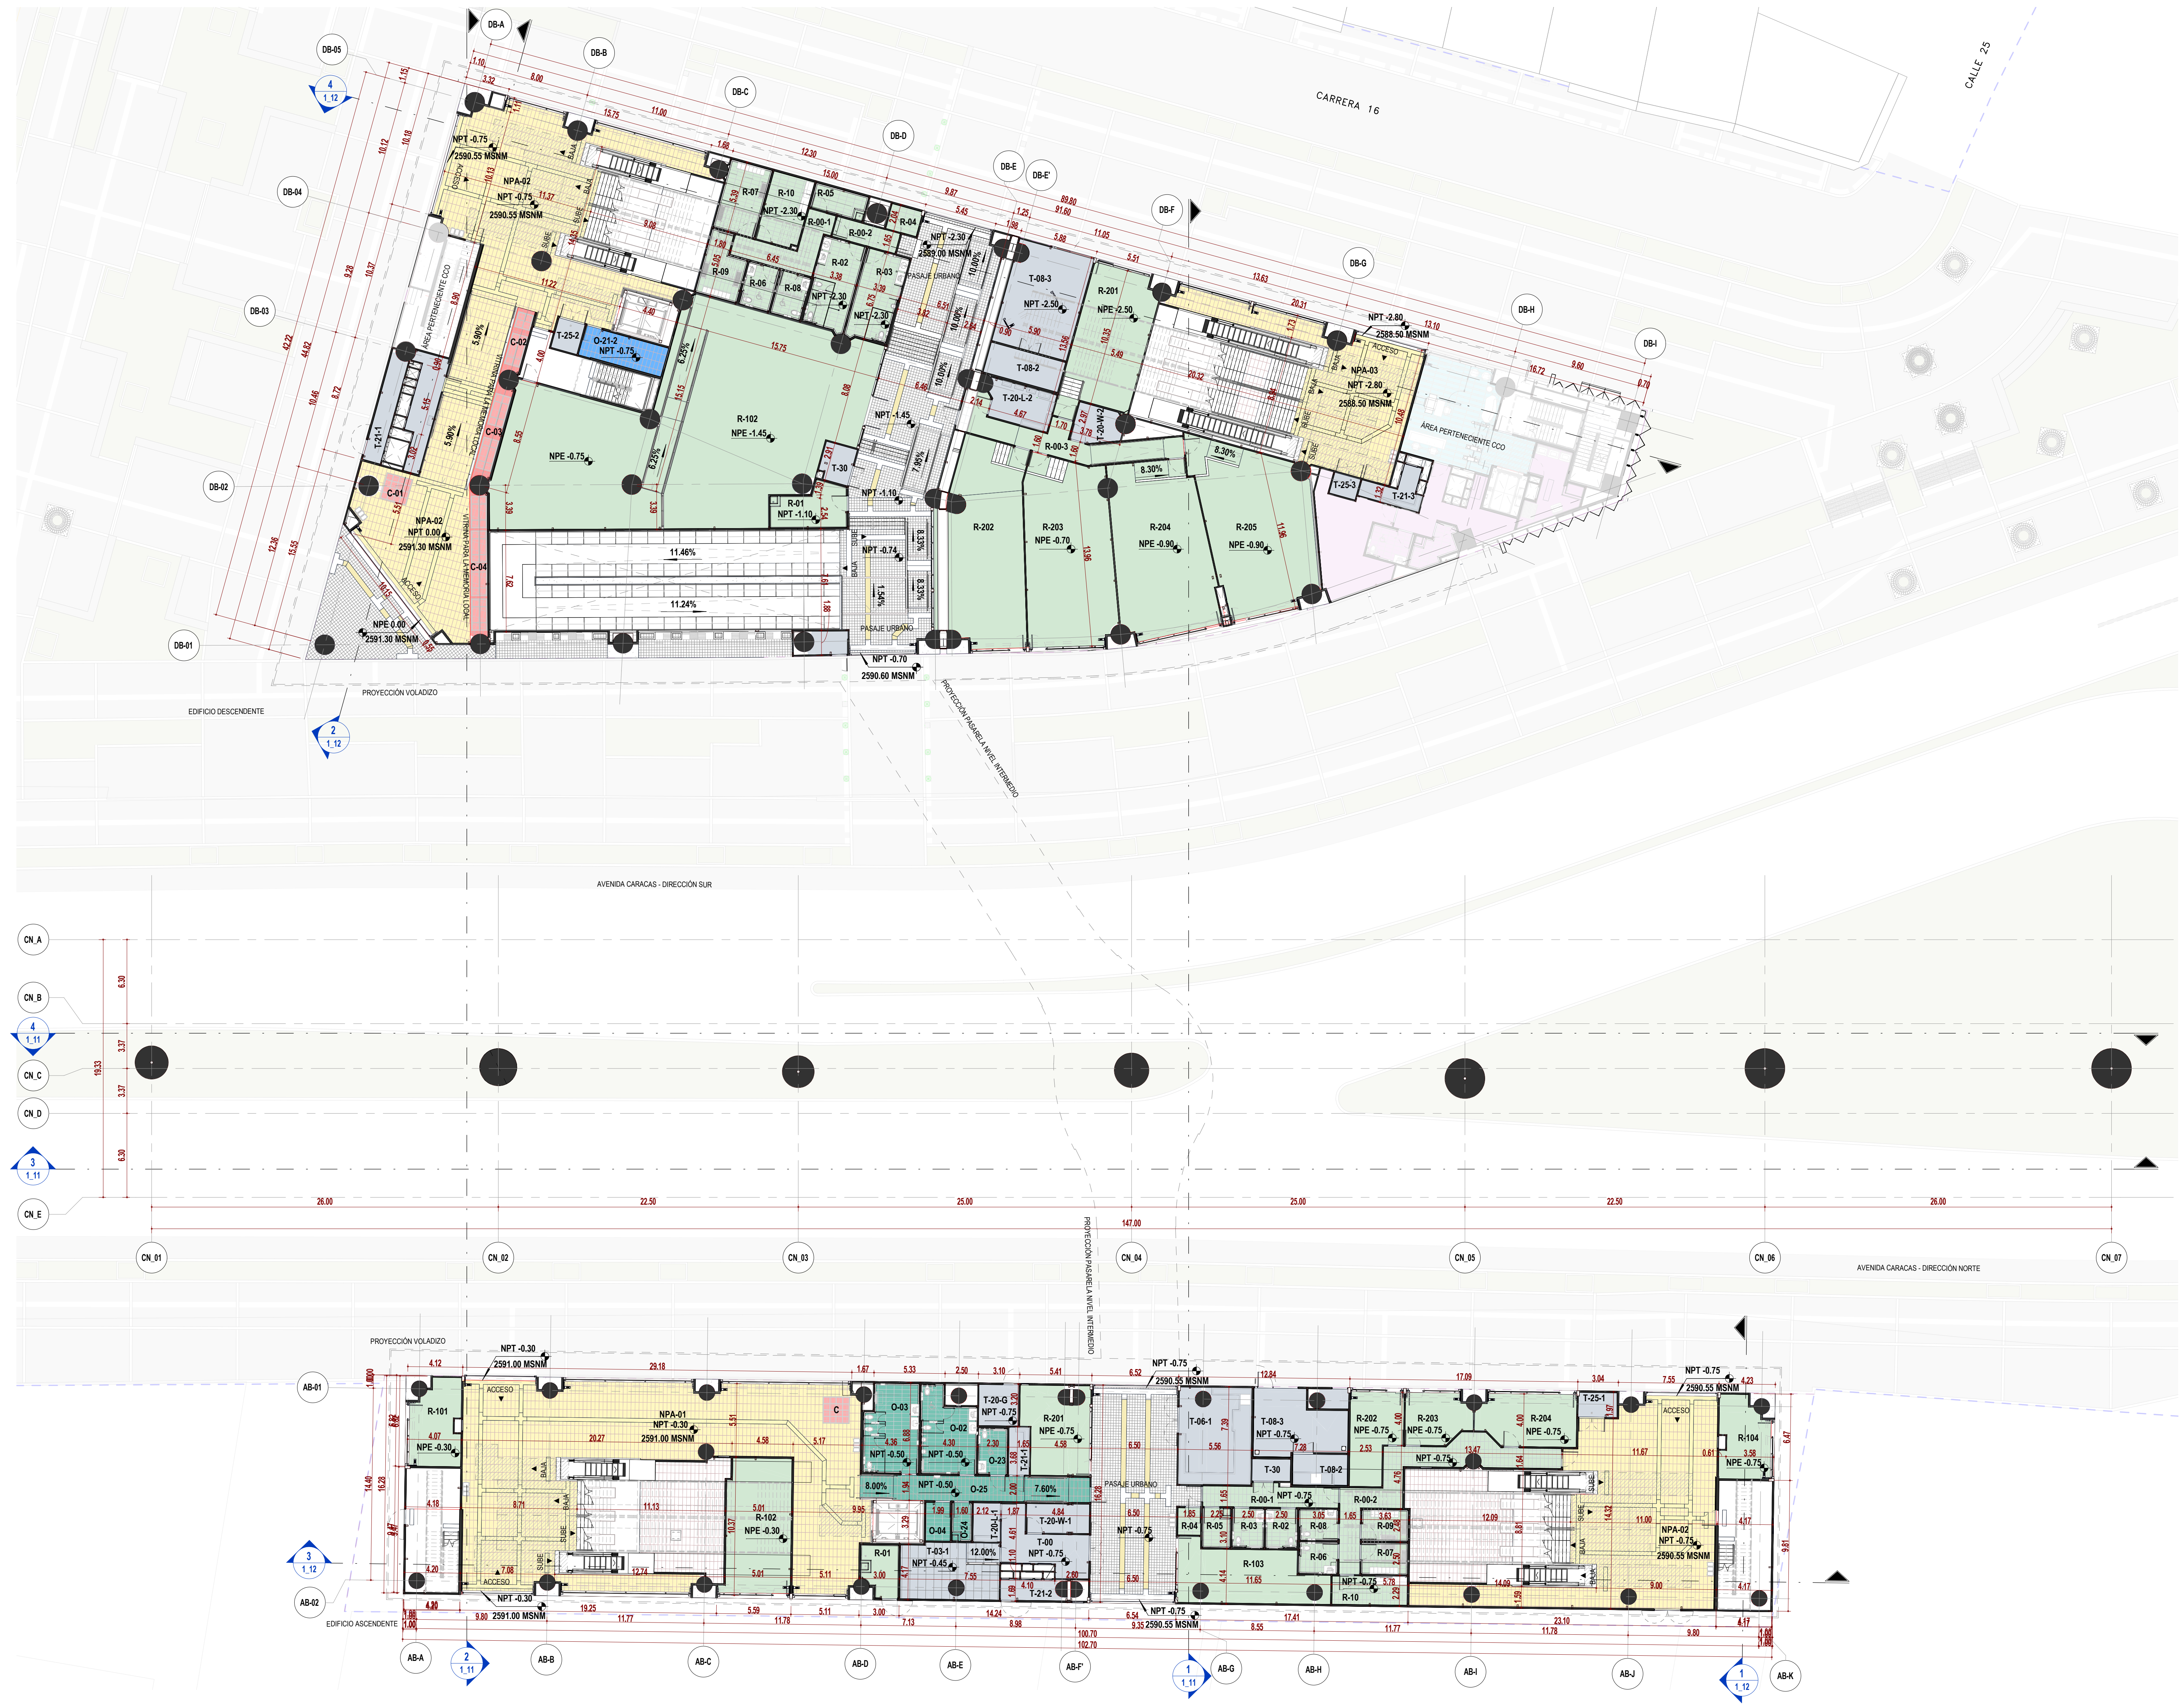

2 NIVEL ACCESO_GENERAL
ESC: 1 : 200

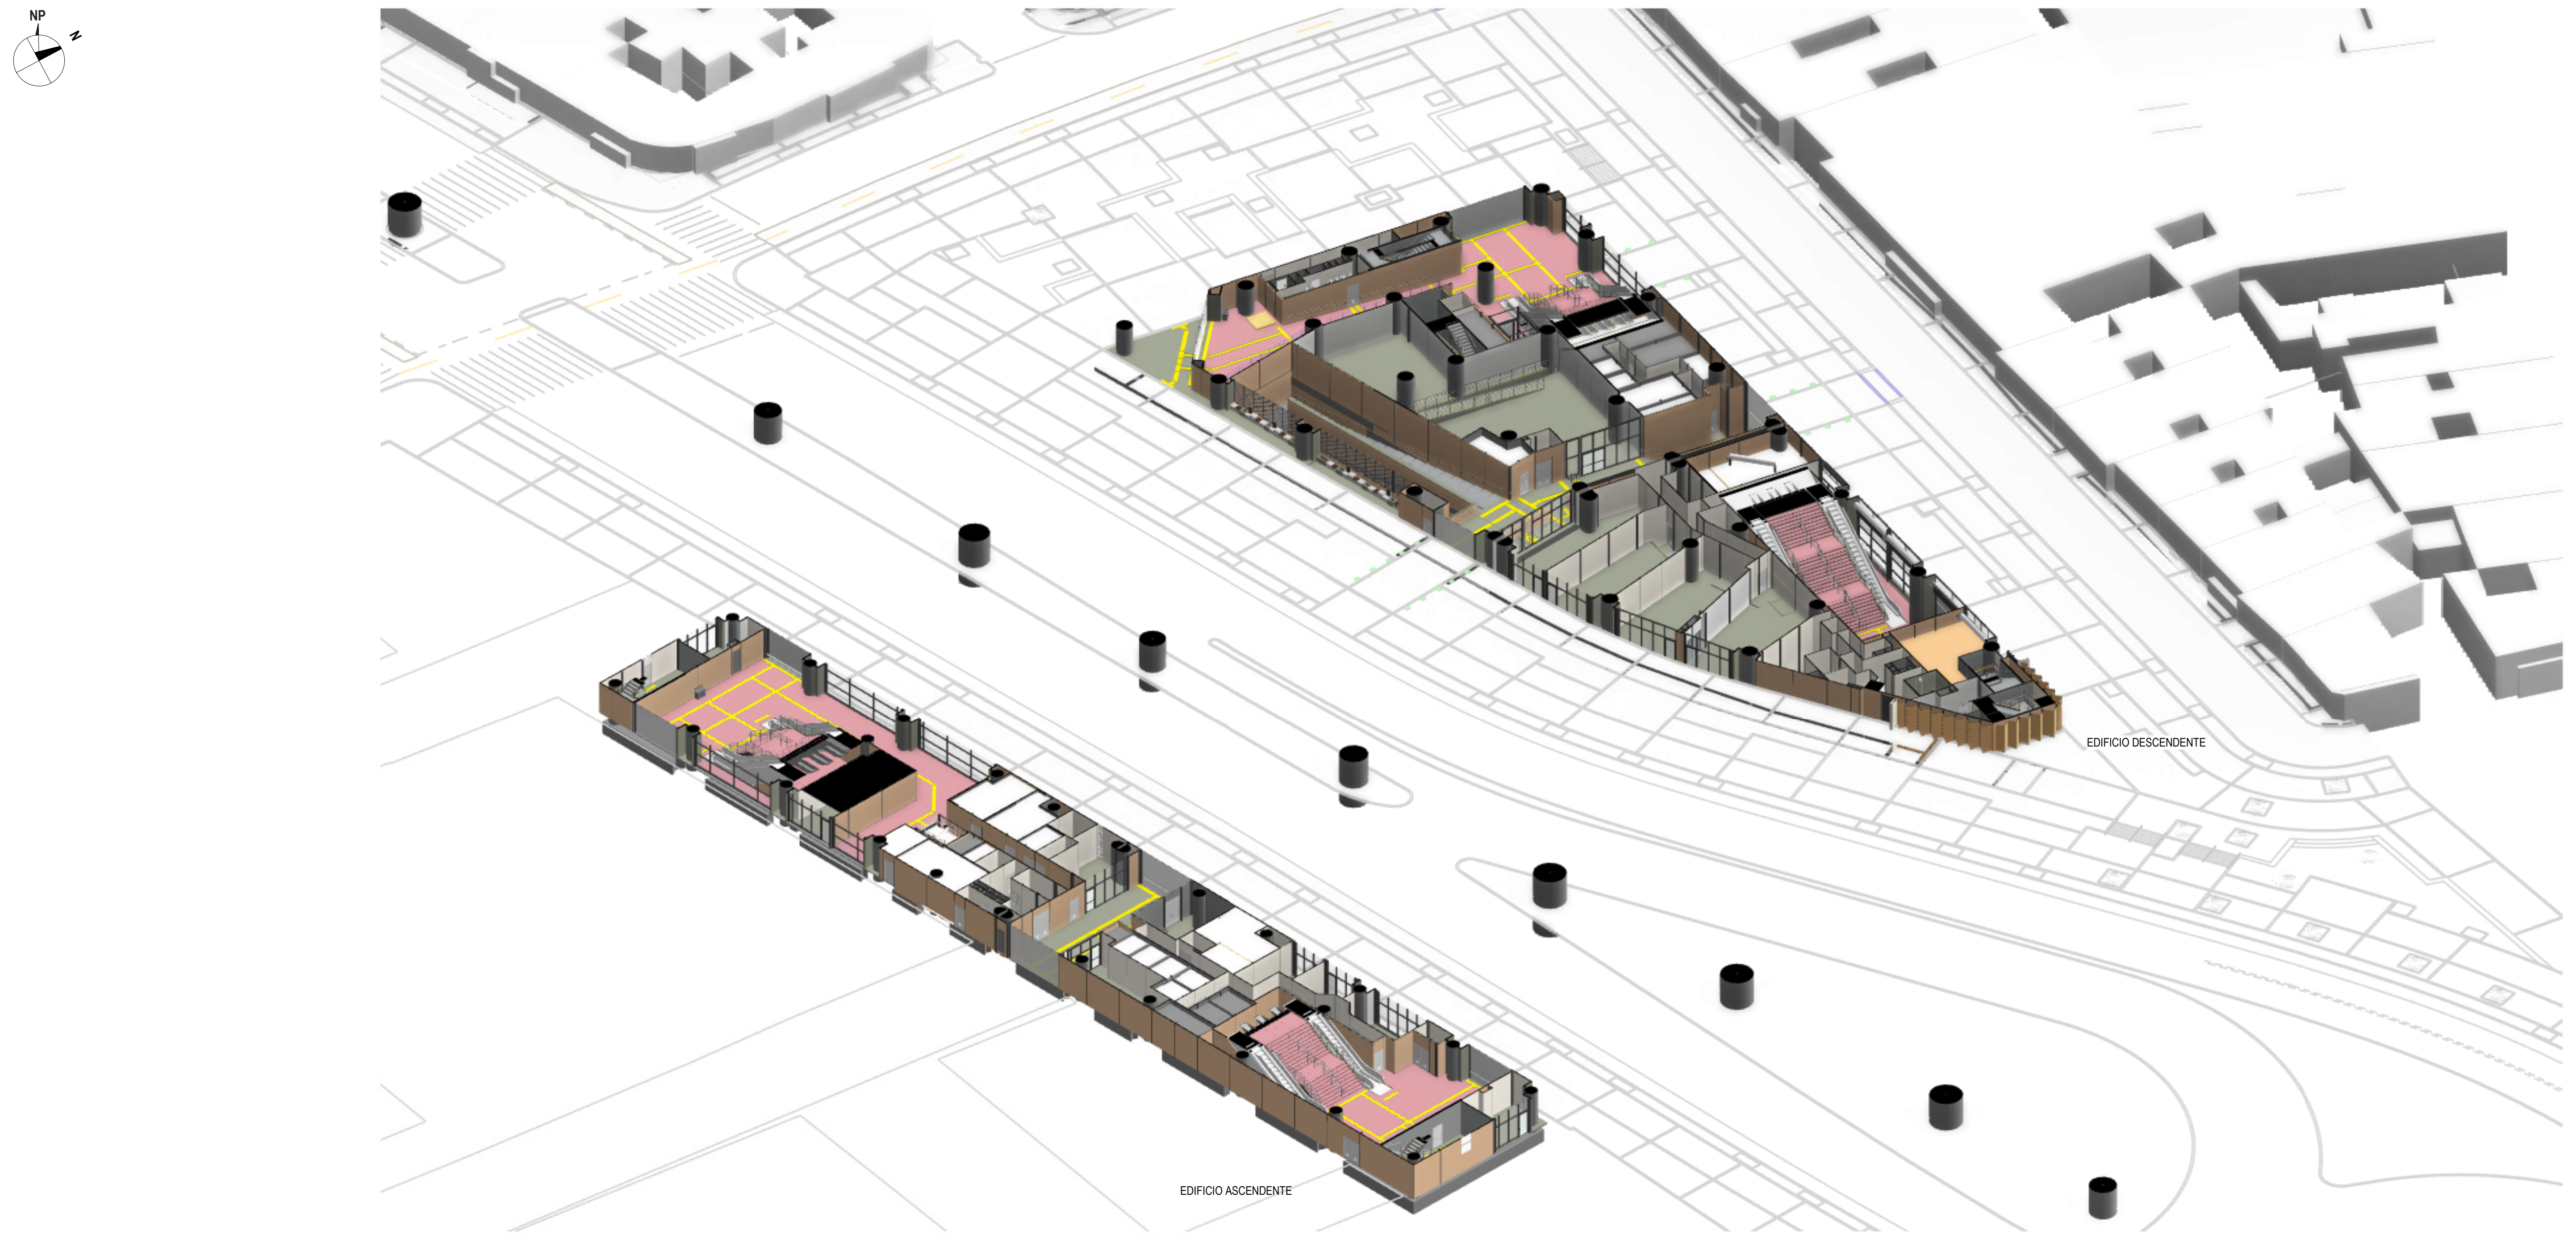

1 3D_NIVEL ACCESO_GENERAL
ESC: N/A

TABLA DE ÁREAS ÚTILES (NIVEL ACCESO)

CÓDIGO	NOMBRE	ÁREA (m²)	DEPARTAMENTO
EDIFICIO ASCENDENTE			
ARQ_PL_00.5_ACCESO			
R-04	SERVICIOS ADICIONALES - CONTROL DE ACCESO BAÑOS PÚBLICOS	3.53	SERVICIOS ADICIONALES - ÁREA NO PAGA
R-05	SERVICIOS ADICIONALES - CUARTO DE LIMPIEZA	6.18	SERVICIOS ADICIONALES - ÁREA NO PAGA
R-03	SERVICIOS ADICIONALES - BAÑO PÚBLICO DE HOMBRES	6.82	SERVICIOS ADICIONALES - ÁREA NO PAGA
R-02	SERVICIOS ADICIONALES - BAÑO PÚBLICO DE MUJERES	6.82	SERVICIOS ADICIONALES - ÁREA NO PAGA
R-08	SERVICIOS ADICIONALES - BAÑOS EMPLEADOS HOMBRES	6.56	SERVICIOS ADICIONALES - ÁREA NO PAGA
R-06	SERVICIOS ADICIONALES - BAÑOS EMPLEADOS MUJERES	6.70	SERVICIOS ADICIONALES - ÁREA NO PAGA
R-09	SERVICIOS ADICIONALES - VESTIDORES EMPLEADOS HOMBRES	8.06	SERVICIOS ADICIONALES - ÁREA NO PAGA
R-07	SERVICIOS ADICIONALES - VESTIDORES EMPLEADOS MUJERES	8.11	SERVICIOS ADICIONALES - ÁREA NO PAGA
R-10	SERVICIOS ADICIONALES - SALA DE EMPLEADOS	12.19	SERVICIOS ADICIONALES - ÁREA NO PAGA
T-20-G	MEDIDORES (GAS)	9.20	ÁREA TÉCNICA
NPA-02	ÁREA NO PAGA	175.36	ÁREA NO PAGA
R-201	SERVICIOS ADICIONALES - ÁREA DE COMIDAS	29.90	SERVICIOS ADICIONALES - ÁREA NO PAGA
R-104	SERVICIOS ADICIONALES - ÁREA DE SERVICIO	21.31	SERVICIOS ADICIONALES - ÁREA NO PAGA
R-204	SERVICIOS ADICIONALES - ÁREA DE COMIDAS	27.48	SERVICIOS ADICIONALES - ÁREA NO PAGA
R-203	SERVICIOS ADICIONALES - ÁREA DE COMIDAS	17.43	SERVICIOS ADICIONALES - ÁREA NO PAGA
R-202	SERVICIOS ADICIONALES - ÁREA DE COMIDAS	23.47	SERVICIOS ADICIONALES - ÁREA NO PAGA
R-103	SERVICIOS ADICIONALES - ÁREA DE SERVICIO	40.41	SERVICIOS ADICIONALES - ÁREA NO PAGA
R-00-2	SERVICIOS ADICIONALES - CORREDOR OPERATIVO	39.71	SERVICIOS ADICIONALES - ÁREA NO PAGA
T-06-1	LOCAL SECUNDARIO DE TABLEROS	38.06	ÁREA TÉCNICA
T-20-W-1	MEDIDORES (AGUA)	10.28	ÁREA TÉCNICA
T-00	CIRCULACIÓN TÉCNICA	21.13	ÁREA TÉCNICA
T-20-L-1	MEDIDORES (LUZ)	5.83	ÁREA TÉCNICA
T-03-1	LOCAL SECUNDARIO DE TELECOMUNICACIONES	30.72	ÁREA TÉCNICA
T-21-2	ÁREA DE INSPECCIÓN	6.67	ÁREA TÉCNICA
T-25-1	NODO DE ACCESO DE TELECOMUNICACIONES	5.26	ÁREA TÉCNICA
O-25	BAÑO PÚBLICO - CORREDOR OPERACIONAL	31.58	SERVICIO PÚBLICO
R-00-1	SERVICIOS ADICIONALES - CORREDOR OPERATIVO	16.22	SERVICIOS ADICIONALES - ÁREA NO PAGA
T-08-3	CENTRO DE TRANSFORMACIÓN ENEL-CODENSA (CT)_CUARTO MEDIA TENSIÓN	29.57	ÁREA TÉCNICA
T-08-2	CENTRO DE TRANSFORMACIÓN ENEL-CODENSA (CT)_CUARTO BAJA TENSIÓN	9.34	ÁREA TÉCNICA
T-30	SISTEMA PROTECCIÓN CONTRA INCENDIO ENEL	4.68	ÁREA TÉCNICA
T-21-3	ÁREA DE INSPECCIÓN	2.86	ÁREA TÉCNICA
		661.44	
ARQ_PL_00.6_ACCESO			
O-04	CONTROL DE ACCESO BAÑOS PÚBLICOS	5.38	SERVICIO PÚBLICO
O-24	CUARTO DE LIMPIEZA DE BAÑOS PÚBLICOS	4.16	SERVICIO PÚBLICO
O-03	BAÑOS PÚBLICOS DE MUJERES	25.78	SERVICIO PÚBLICO
O-02	BAÑOS PÚBLICOS DE HOMBRES	23.46	SERVICIO PÚBLICO
O-23	BAÑO PÚBLICO - FAMILIAR	7.34	SERVICIO PÚBLICO
T-21-1	ÁREA DE INSPECCIÓN	5.48	ÁREA TÉCNICA
		71.59	
ARQ_PL_00.7_ACCESO			
NPA-01	ÁREA NO PAGA	303.41	ÁREA NO PAGA
R-01	SERVICIOS ADICIONALES - CUARTO DE BASURAS PARA METRO	9.99	SERVICIOS ADICIONALES - ÁREA NO PAGA
R-102	SERVICIOS ADICIONALES - ÁREA DE SERVICIO	48.82	SERVICIOS ADICIONALES - ÁREA NO PAGA
R-101	SERVICIOS ADICIONALES - ÁREA DE SERVICIO	22.57	SERVICIOS ADICIONALES - ÁREA NO PAGA
C	ÁREAS DE USO CULTURAL	4.00	ÁREA CULTURAL
		388.79	
EDIFICIO DESCENDENTE			
ARQ_PL_00.1_ACCESO			
NPA-03	ÁREA NO PAGA	96.27	ÁREA NO PAGA
T-25-3	NODO DE ACCESO DE TELECOMUNICACIONES	3.16	ÁREA TÉCNICA
T-21-3	ÁREA DE INSPECCIÓN	8.31	ÁREA TÉCNICA
T-08-3	CENTRO DE TRANSFORMACIÓN ENEL-CODENSA (CT)_CUARTO MEDIA TENSIÓN	44.38	ÁREA TÉCNICA
R-201	SERVICIOS ADICIONALES - ÁREA DE COMIDAS	56.91	SERVICIOS ADICIONALES - ÁREA NO PAGA
T-08-2	CENTRO DE TRANSFORMACIÓN ENEL-CODENSA (CT)_CUARTO BAJA TENSIÓN	13.21	ÁREA TÉCNICA
		222.24	
ARQ_PL_00.2_ACCESO			
R-03	SERVICIOS ADICIONALES - BAÑO PÚBLICO DE HOMBRES	20.96	SERVICIOS ADICIONALES - ÁREA NO PAGA
R-02	SERVICIOS ADICIONALES - BAÑO PÚBLICO DE MUJERES	20.99	SERVICIOS ADICIONALES - ÁREA NO PAGA
R-08	SERVICIOS ADICIONALES - BAÑOS EMPLEADOS HOMBRES	7.32	SERVICIOS ADICIONALES - ÁREA NO PAGA
R-06	SERVICIOS ADICIONALES - BAÑOS EMPLEADOS MUJERES	7.56	SERVICIOS ADICIONALES - ÁREA NO PAGA
R-09	SERVICIOS ADICIONALES - VESTIDORES EMPLEADOS HOMBRES	13.03	SERVICIOS ADICIONALES - ÁREA NO PAGA
R-07	SERVICIOS ADICIONALES - VESTIDORES EMPLEADOS MUJERES	16.43	SERVICIOS ADICIONALES - ÁREA NO PAGA
R-10	SERVICIOS ADICIONALES - SALA DE EMPLEADOS	16.65	SERVICIOS ADICIONALES - ÁREA NO PAGA
R-05	SERVICIOS ADICIONALES - CUARTO DE LIMPIEZA	7.58	SERVICIOS ADICIONALES - ÁREA NO PAGA
R-04	SERVICIOS ADICIONALES - CONTROL DE ACCESO BAÑOS PÚBLICOS	4.57	SERVICIOS ADICIONALES - ÁREA NO PAGA
R-00-1	SERVICIOS ADICIONALES - CORREDOR OPERATIVO	15.77	SERVICIOS ADICIONALES - ÁREA NO PAGA
R-00-2	SERVICIOS ADICIONALES - CORREDOR OPERATIVO	7.53	SERVICIOS ADICIONALES - ÁREA NO PAGA
		138.36	
ARQ_PL_00.3_ACCESO			
R-102	SERVICIOS ADICIONALES - ÁREA DE SERVICIO	325.11	SERVICIOS ADICIONALES - ÁREA NO PAGA
T-20-L-2	MEDIDORES (LUZ)	13.55	ÁREA TÉCNICA
T-20-W-2	MEDIDORES (AGUA)	8.81	ÁREA TÉCNICA
R-00-3	SERVICIOS ADICIONALES - CORREDOR OPERATIVO	32.05	SERVICIOS ADICIONALES - ÁREA NO PAGA
R-01	SERVICIOS ADICIONALES - CUARTO DE BASURAS PARA METRO	16.66	SERVICIOS ADICIONALES - ÁREA NO PAGA
T-30	SISTEMA PROTECCIÓN CONTRA INCENDIO ENEL	6.41	ÁREA TÉCNICA
		402.59	
ARQ_PL_00.4_ACCESO			
R-205	SERVICIOS ADICIONALES - ÁREA DE COMIDAS	95.48	SERVICIOS ADICIONALES - ÁREA NO PAGA
R-204	SERVICIOS ADICIONALES - ÁREA DE COMIDAS	89.23	SERVICIOS ADICIONALES - ÁREA NO PAGA
		184.71	
ARQ_PL_00.5_ACCESO			
NPA-02	ÁREA NO PAGA	300.43	ÁREA NO PAGA
O-21-2	ALMACENAMIENTO DE LA ESTACIÓN	14.40	ÁREA OPERATIVA
R-202	SERVICIOS ADICIONALES - ÁREA DE COMIDAS	92.63	SERVICIOS ADICIONALES - ÁREA NO PAGA
T-25-2	NODO DE ACCESO DE TELECOMUNICACIONES	4.58	ÁREA TÉCNICA
T-20-G	MEDIDORES (GAS)	4.71	ÁREA TÉCNICA
R-203	SERVICIOS ADICIONALES - ÁREA DE COMIDAS	88.53	SERVICIOS ADICIONALES - ÁREA NO PAGA
		505.29	
ARQ_PL_00.6_ACCESO			
C-02	ÁREAS DE USO CULTURAL	6.44	ÁREA CULTURAL
T-21-2	ÁREA DE INSPECCIÓN	15.59	ÁREA TÉCNICA
		22.03	
ARQ_PL_01_ACCESO			
C-01	ÁREAS DE USO CULTURAL	4.00	ÁREA CULTURAL
C-04	ÁREAS DE USO CULTURAL	14.13	ÁREA CULTURAL
C-03	ÁREAS DE USO CULTURAL	9.28	ÁREA CULTURAL
T-21-1	ÁREA DE INSPECCIÓN	11.00	ÁREA TÉCNICA
		38.41	
TOTAL NIVEL ACCESO		2635.45	

TABLA DE ÁREAS ÚTILES POR DEPARTAMENTO (NIVEL ACCESO)

DEPARTAMENTO	ÁREA (m²)
EDIFICIO ASCENDENTE	
ARQ_PL_00.5_ACCESO	
SERVICIO PÚBLICO	31.58
SERVICIOS ADICIONALES - ÁREA NO PAGA	280.89
ÁREA NO PAGA	175.36
ÁREA TÉCNICA	173.61
ARQ_PL_00.6_ACCESO	
SERVICIO PÚBLICO	66.11
ÁREA TÉCNICA	5.48
ARQ_PL_00.7_ACCESO	
SERVICIOS ADICIONALES - ÁREA NO PAGA	81.38
ÁREA CULTURAL	4.00
ÁREA NO PAGA	303.41
EDIFICIO DESCENDENTE	
ARQ_PL_00.1_ACCESO	
SERVICIOS ADICIONALES - ÁREA NO PAGA	56.91
ÁREA NO PAGA	96.27
ÁREA TÉCNICA	69.06
ARQ_PL_00.2_ACCESO	
SERVICIOS ADICIONALES - ÁREA NO PAGA	138.36
ARQ_PL_00.3_ACCESO	
SERVICIOS ADICIONALES - ÁREA NO PAGA	373.82
ÁREA TÉCNICA	28.77
ARQ_PL_00.4_ACCESO	
SERVICIOS ADICIONALES - ÁREA NO PAGA	184.71
ARQ_PL_00.5_ACCESO	
SERVICIOS ADICIONALES - ÁREA NO PAGA	181.17
ÁREA NO PAGA	300.43
ÁREA OPERATIVA	14.40
ÁREA TÉCNICA	9.29
ARQ_PL_00.6_ACCESO	
ÁREA CULTURAL	6.44
ÁREA TÉCNICA	15.59
ARQ_PL_01_ACCESO	
ÁREA CULTURAL	27.41
ÁREA TÉCNICA	11.00
TOTAL NIVEL ACCESO	2635.45

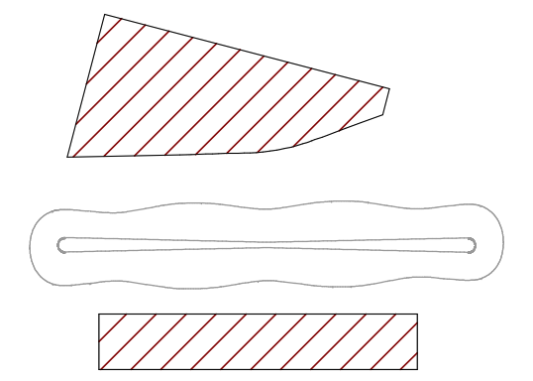

PLANO CLAVE ESTACIÓN 13

VÁLIDO PARA CONSTRUCCIÓN
31-03-26

LOCALIZACIÓN

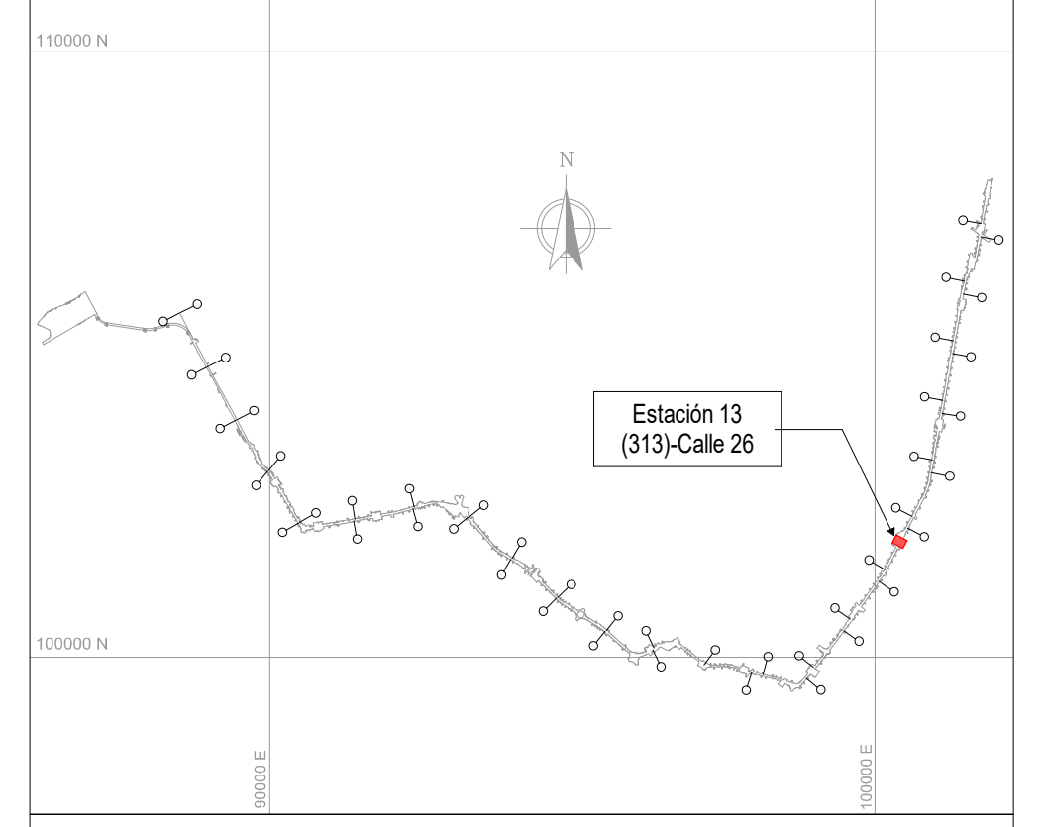

NOTAS

01 TODAS LAS DIMENSIONES ESTÁN CONFIGURADAS EN METROS A MENOS QUE SE INDIQUE UNA UNIDAD DE MEDIDA DIFERENTE.

02 TODAS LAS MEDIDAS, UBICACIÓN Y NIVELES DEBEN VERIFICARSE EN EL LUGAR DE CONSTRUCCIÓN.

03 EL NIVEL DE ACCESO AL EDIFICIO PL 01 CORRESPONDE AL +0,00 DE LA ESTACIÓN Y REFERENCIA AL NIVEL 2591.30 M.S.N.M.

04 LOS NOMBRES ESPECIFICOS DE LAS ÁREAS PUEDEN SER CONSULTADAS EN EL PLANO NO. 3 Ó EN LAS VISTAS EN PLANTA.

05 LOS COLORES QUE SE MUESTRAN EN LOS PLANOS COMO PROYECCIÓN DE ELEMENTOS ARQUITECTÓNICOS COMO CUBIERTAS FACHADAS MUROS ETC. NO REPRESENTAN LA MATERIALIDAD Y REALIDAD DE ACABADOS DEL PROYECTO, SOLO SON INDICATIVOS PARA REALIZAR UNA CORRECTA LECTURA DE LA PLANIMETRÍA.

06 LAS ESCALERAS ELÉCTRICAS INDICAN SU SENTIDO CON LA SIGUIENTE NOMENCLATURA: "SUBE" Y "BAJA".

07 SE DEBEN REVISAR LOS NIVELES ESTRUCTURALES PARA NIVEL DE ACCESO PL_01 Y SUBNIVELES, PL_02 (INTERMEDIO), PL_03 (PLATAFORMA) CON LA PLANIMETRÍA DE PLACAS ESTRUCTURALES EN LOS ENTREGABLES L1T1-1300-413-CON-ED-EST-PL-0046, 45, 47, 67, 68, 69, 70, 71, 91 RESPECTIVAMENTE. EL NIVEL ESTRUCTURAL (NE) REFERENCIA LOS ESPACIOS DONDE SE DEBE ACONDICIONAR EL ACABADO DE PISO SEGÚN CORRESPONDA, CON LOS NIVELES DE PISO TERMINADO (NPT). LOS NIVELES PROYECTADOS DE EMPATE (NPE) EN LAS ÁREAS DE SERVICIOS ADICIONALES, REFERENCIAN LA ADECUACIÓN DE LOS DESNIVELES EN ESTAS ÁREAS; QUEDA COMO RESPONSABILIDAD DEL LOCATARIO DEFINIR Y ACONDICIONAR ESTE ACABADO DE PISO (NPE) EN LÍNEA CON EL NIVEL (NPT) DE ESPACIOS COLINDANTES. EL NIVEL ESTRUCTURAL (NE) SE ENCUENTRA A (- 0.10M) POR DEBAJO DE LOS NIVELES DE PISO TERMINADO (NPT) Y LOS NIVELES PROYECTADOS DE EMPATE (NPE) MARCADOS EN LA PLANIMETRÍA.

- ARQ_PL_00 = SÓTANO / NPT -9.10m
- ARQ_PL_00.1 = ACCESO / NPT -2.80m
- ARQ_PL_00.2 = ACCESO / NPT -2.30m
- ARQ_PL_00.3 = ACCESO / NPT -1.50m
- ARQ_PL_00.4 = ACCESO / NPT -0.90m
- ARQ_PL_00.5 = ACCESO / NPT -0.75m
- ARQ_PL_00.6 = ACCESO / NPT -0.50m
- ARQ_PL_00.7 = ACCESO / NPT -0.30m
- ARQ_PL_01 = ACCESO / NPT 0.00m
- ARQ_PL_02 = INTERMEDIO / NPT 6.60m
- ARQ_PL_02.2 = TOPE DE RIEL (TOR) / NPT 14.20m
- ARQ_PL_03 = PLATAFORMA/ NIVEL 1 CCO / NPT 15.34m
- ARQ_PL_04 = CUBIERTA EDIFICIO ASCENDENTE / NPT 21.94m
- ARQ_PL_05 = CUBIERTA NAVE CENTRAL / NPT 24.60m
- ARQ_PL_06 = NIVEL 2 CCO / NPT 28.54m
- ARQ_PL_07 = CUBIERTA EDIFICIO ASCENDENTE / NPT 36.84m

CONVENCIONES

- - - -	LÍMITE DE INTERVENCIÓN
- - - -	HUELLA APÉNDICE TÉCNICO
▬	MURO DIVISORIO
— — —	PROYECCIÓN NIVEL SUPERIOR
🟩	SERVICIOS ADICIONALES - ÁREA NO PAGA
🟩	SERVICIOS ADICIONALES - ÁREA PAGA
🟥	ÁREA CULTURAL
🟦	ÁREA OPERATIVA
🟧	ÁREA PAGA
🟨	ÁREA NO PAGA
🟦	ÁREA PÚBLICA
🟩	SERVICIO PÚBLICO
🟦	ZONA DE REFUGIO
⬜	ÁREA TÉCNICA
🟦	SERVICIOS ADICIONALES - ÁREA DE OFICINAS

No.	PLANOS DE REFERENCIA	REV.

No.	MODELO BIM DE REFERENCIA	REV.
1	L1T1-1100-213-CON-ED-EST-MO-0001.rvt	V00
2	L1T1-1100-214-CON-ED-EST-MO-0001.rvt	V00
3	L1T1-1100-313-CON-ED-EST-MO-0001.rvt	V00
4	L1T1-1150-213-CON-ED-EST-MO-0001.rvt	V00
5	L1T1-1150-214-CON-ED-EST-MO-0001.rvt	V00
6	L1T1-1150-313-CON-ED-EST-MO-0001.rvt	V00
7	L1T1-1200-313-CON-ED-EST-MO-0001.rvt	V00
8	L1T1-1300-413-CON-ED-EST-MO-0001.rvt	V00
9	L1T1-1300-413-CON-ED-EST-MO-0002.rvt	V00
10	L1T1-1310-413-CON-ED-EST-MO-0001.rvt	V00
11	L1T1-1410-313-CON-ED-MEC-MO-0001.rvt	V00
12	L1T1-1420-313-CON-ED-MEC-MO-0001.rvt	V00
13	L1T1-5160-313-CON-ED-EST-MO-0001.rvt	V00
14	L1T1-5160-313-CON-ED-ARQ-MO-0001.rvt	V00
15	L1T1-5300-313-CON-ED-MEC-MO-0001.rvt	V00
16	L1T1-5600-313-CON-ED-INS-MO-0001.rvt	V00
17	L1T1-1330-413-CON-ED-ARQ-MO-0011.rvt	V00
18	L1T1-1330-413-CON-ED-ARQ-MO-0012.rvt	V00

No.	PAQUETE DE TRABAJO DE REFERENCIA	REV.
1	XREF-URBANISM-CONTEXT-ST13.rvt	
2	XREF-SECONDARY-STRUCTURE-ST13.rvt	

0 2 10m
1:200

METRO BOGOTÁ
GCS Consorcio Consultores PMO Bogotá
CONSORCIO SUPERVISOR PLMB
CHEC

DISEÑÓ:
REN ZHENHUA
Licencia de Arq.nivel I (China): 1101735-614

APROBÓ:
DIEGO ERNESTO DUEÑAS
Mat.: 25202-53876 CND

REVISÓ:
CARLOS MAURICIO BARRETO BARBOSA
Mat.: A4012012-14139353

DIBUJÓ:
EQUIPO CHEC

REVISIÓN No.	FECHA	DESCRIPCIÓN	REVISÓ	APROBÓ	APROBACIÓN CLIENTE
V01	31/03/2026	EMITIDO PARA CONSTRUCCIÓN	C.M.B.B	D.E.D	
V00	13/05/2025	REVISION NO OBJETADA - EMITIDO PARA CONSTRUCCION	F.B.R	E.O.M	
VGG	09/09/2024	EMITIDO PARA REVISIÓN Y COMENTARIOS DEL CLIENTE E INTERVENTORÍA -INCLUYE COMENTARIOS /(AJUSTES V3)	F.B.R	E.O.M	
VFF	04/06/2024	EMITIDO PARA REVISIÓN Y COMENTARIOS DEL CLIENTE E INTERVENTORÍA -INCLUYE COMENTARIOS /(AJUSTES V2)	F.B.R	E.O.M	
VEE	06/01/2023	EMITIDO PARA REVISIÓN Y COMENTARIOS DEL CLIENTE E INTERVENTORÍA -INCLUYE COMENTARIOS /(90% ACCESOS)	J.E.M	M.B.M	
VDD	18/12/2022	EMITIDO PARA REVISIÓN Y COMENTARIOS DEL CLIENTE E INTERVENTORÍA - INCLUYE COMENTARIOS /(NAVE CENTRAL)	J.E.M	M.B.M	
VCC	22/08/2022	EMITIDO PARA REVISIÓN Y COMENTARIOS DEL CLIENTE E INTERVENTORÍA - INCLUYE COMENTARIOS /(ENTREGA 90%)	J.E.M	M.B.M	
VBB	06/12/2021	EMITIDO PARA REVISIÓN Y COMENTARIOS DEL CLIENTE E INTERVENTORÍA	J.E.M	M.B.M	
VA0	05/12/2021	EMITIDO PARA COMENTARIOS INTERNOS - EMISIÓN PRELIMINAR PARA COMENTARIOS	J.E.M	M.B.M	

METRO LÍNEA 1

METRO LÍNEA 1
CONTRATO DE CONCESIÓN No. 163 DE 2019

PROYECTO PRIMERA LÍNEA DEL METRO DE BOGOTÁ - TRAMO 1

DIRECTOR DE INTERVENTORÍA:
JAVIER DESCARGA N.
Mat.:25202-68697 CND

ESPECIALISTA INTERVENTORÍA:
CARLOS ALBERTO HOYOS SOTO
Mat.:A25072000-14251682

FECHA:
MARZO 2026

INFRAESTRUCTURA VIAL
ARQUITECTURA
ESTACIÓN METRO 13 (CALLE 26)
GENERAL
VISTA EN PLANTA Y 3D - NIVEL ACCESO

PLANCHA No: L1T1-0000-313-CON-ED-ARQ-PL-0001_05_V01
ARCHIVO: L1T1-0000-313-CON-ED-ARQ-MO-0001_V00.rvt
ESCALA: INDICADA
FECHA: DICIEMBRE 2021
REVISIÓN No. V01
PLANO No. 05 DE 101