L1T1-CON-CAL-FR-0120 - B1 : 1000x707mm

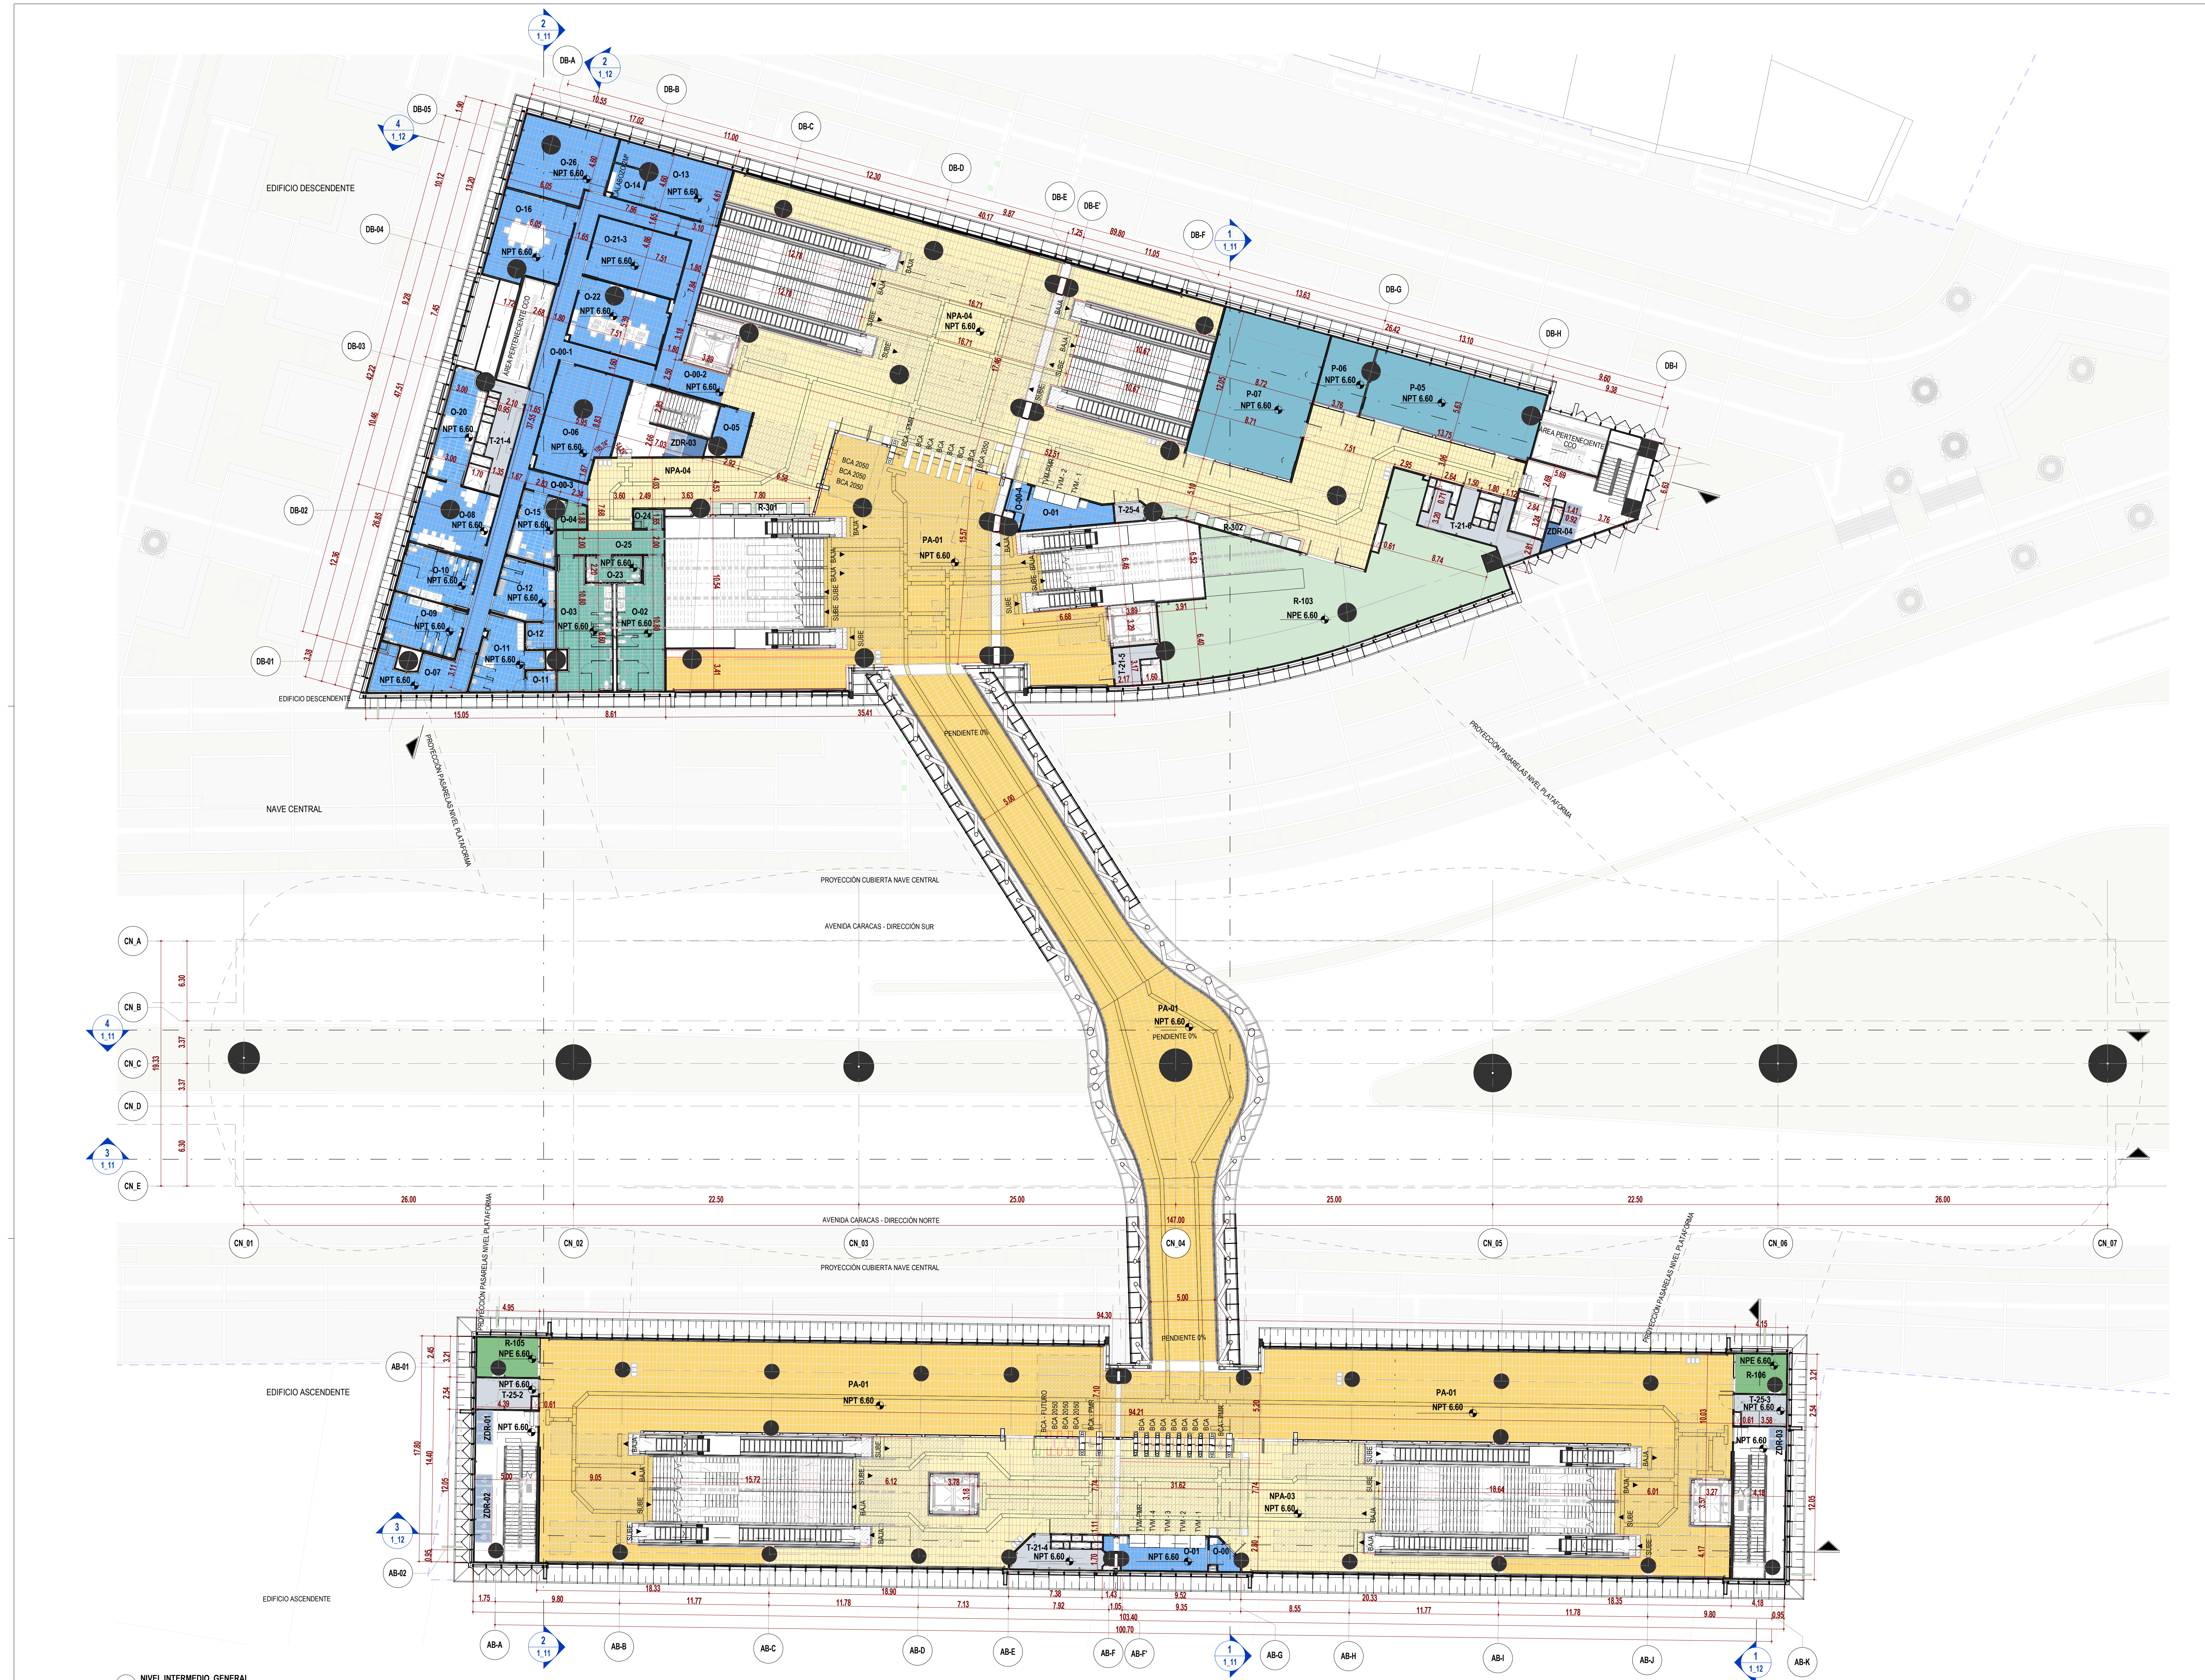

2 NIVEL INTERMEDIO_GENERAL
ESC: 1 : 200

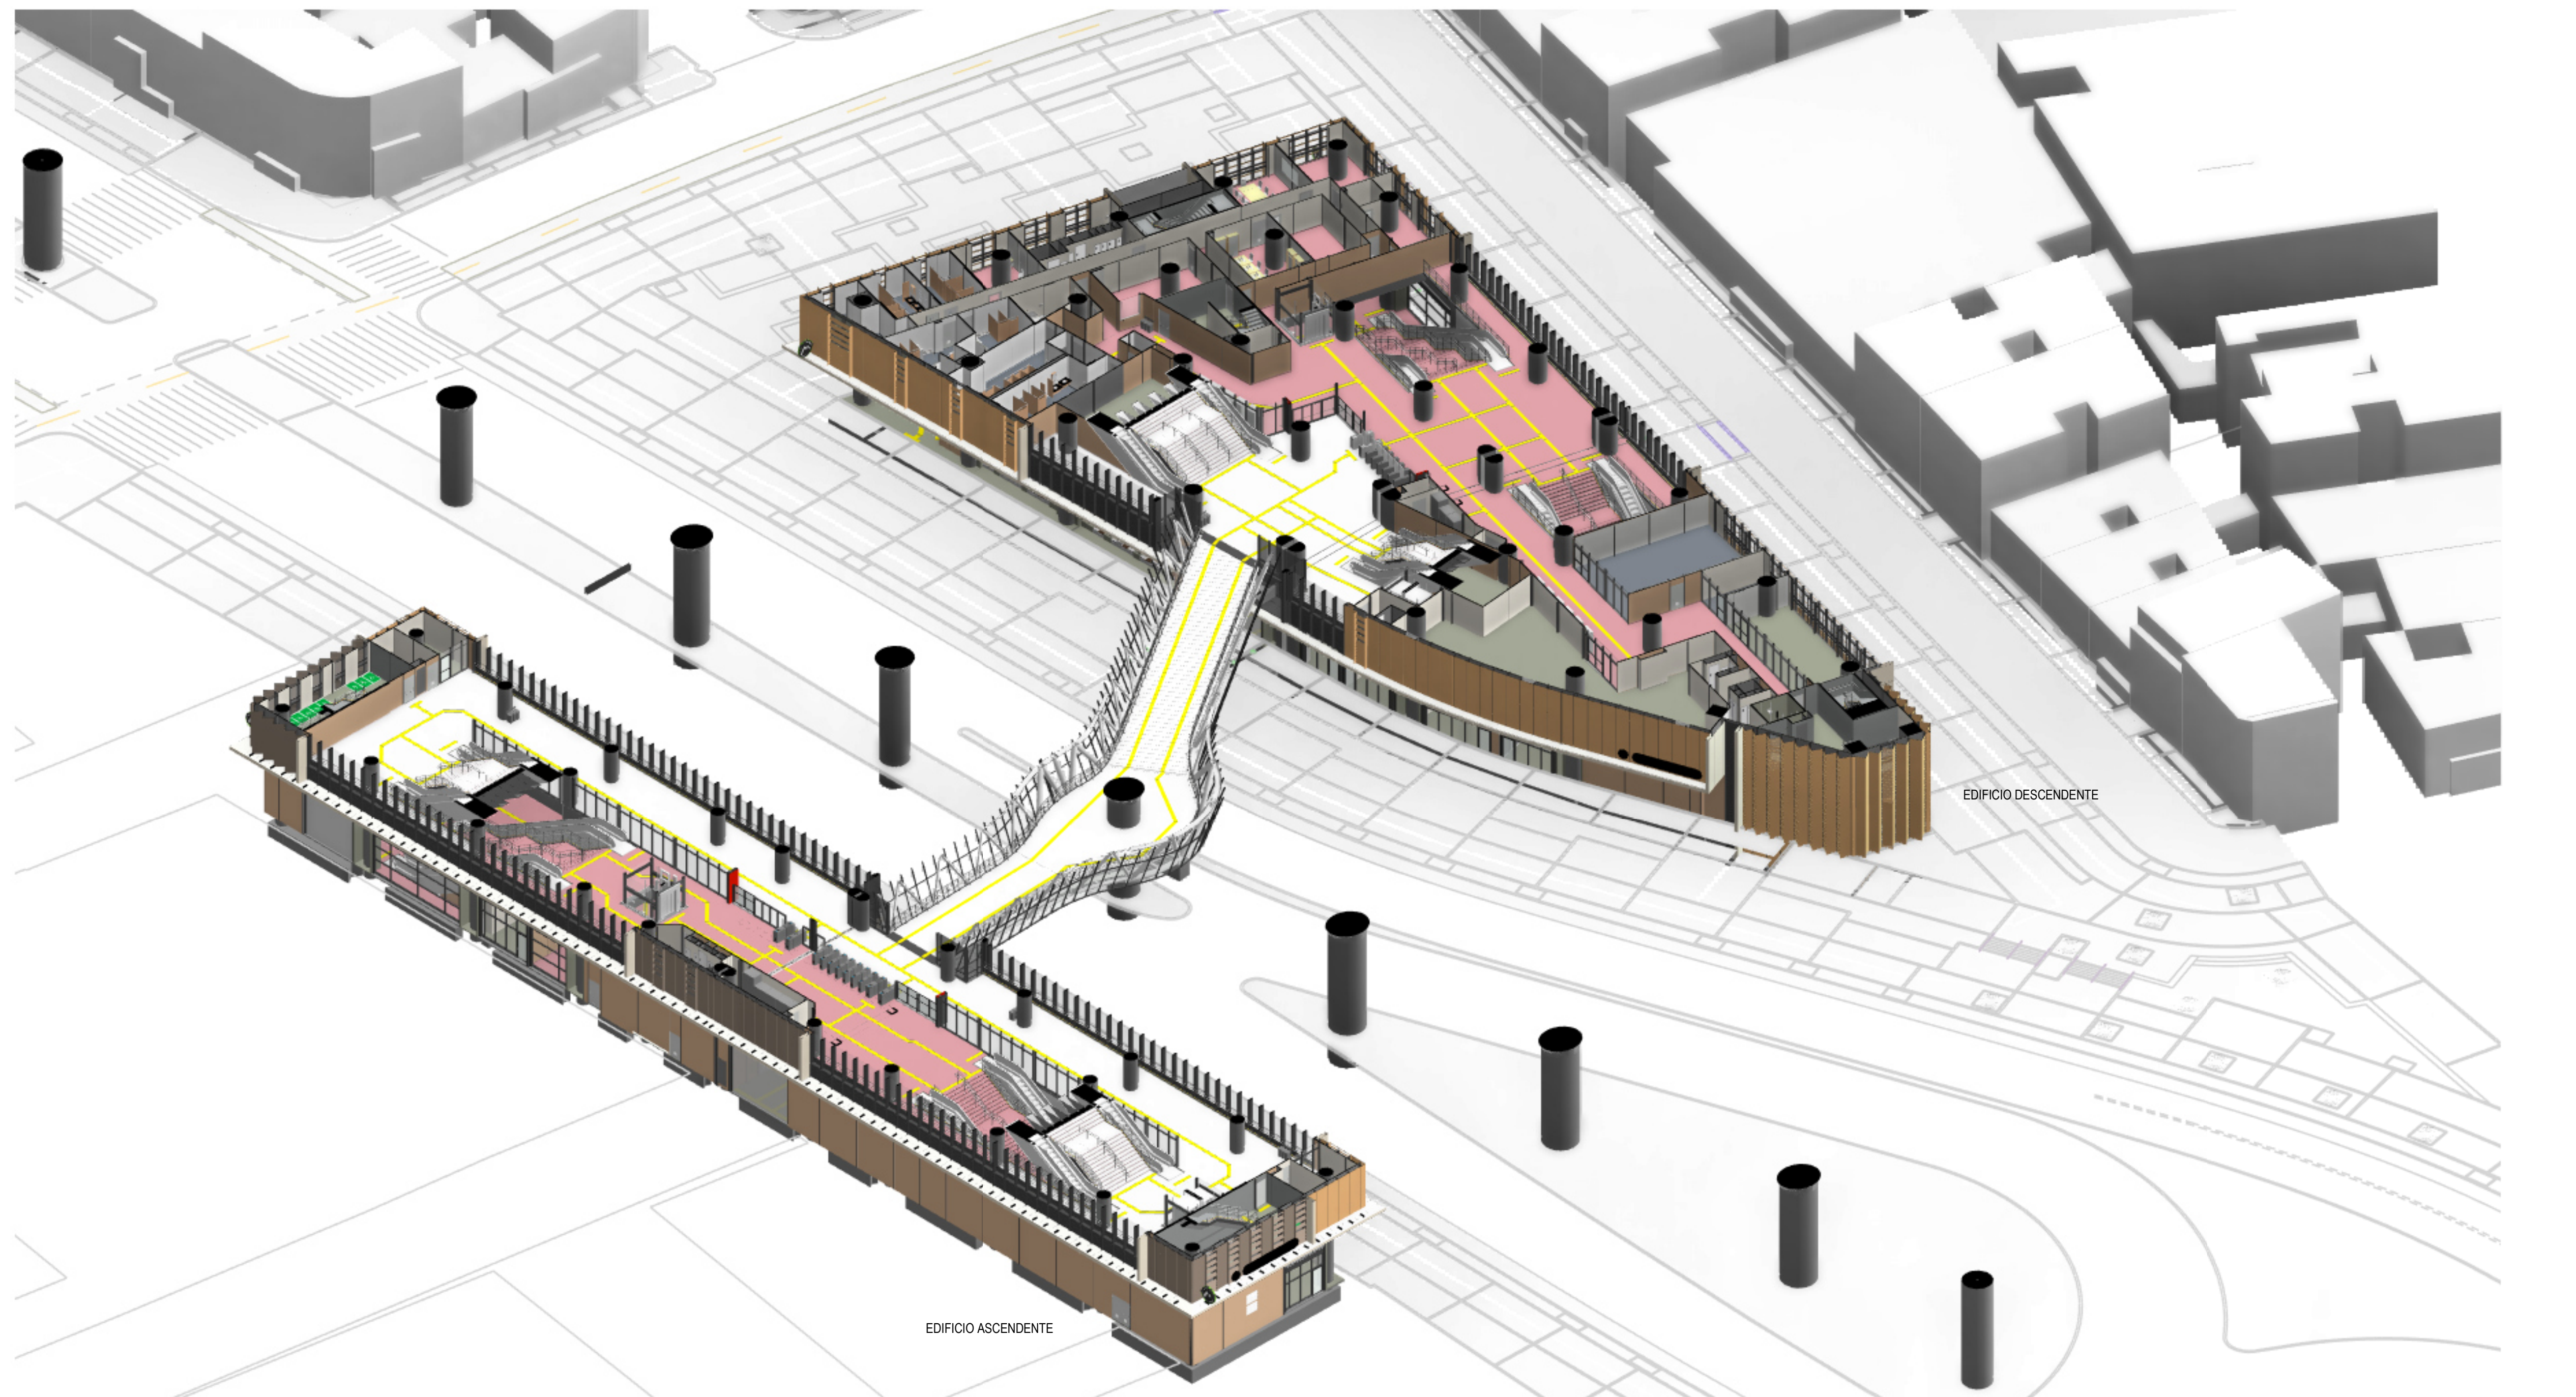

1 3D_NIVEL INTERMEDIO_GENERAL
ESC: N/A

TABLA DE ÁREAS ÚTILES (NIVEL INTERMEDIO)

CÓDIGO	NOMBRE	ÁREA (m²)	DEPARTAMENTO
EDIFICIO ASCENDENTE			
ARQ_PL_02_INTERMEDIO			
NPA-03	ÁREA NO PAGA	377.95	ÁREA NO PAGA
O-00	CIRCULACIÓN ÁREAS OPERATIVAS	4.30	ÁREA OPERATIVA
O-01	VENTA AUTOMÁTICA DE BOLETOS	19.39	ÁREA OPERATIVA
PA-01	ÁREA PAGA	816.87	ÁREA PAGA
R-105	SERVICIOS ADICIONALES - ÁREA DE SERVICIO	13.58	SERVICIOS ADICIONALES - ÁREA PAGA
R-106	SERVICIOS ADICIONALES - ÁREA DE SERVICIO	11.10	SERVICIOS ADICIONALES - ÁREA PAGA
T-21-4	ÁREA DE INSPECCIÓN	13.14	ÁREA TÉCNICA
T-25-2	NODO DE ACCESO DE TELECOMUNICACIONES	11.18	ÁREA TÉCNICA
T-25-3	NODO DE ACCESO DE TELECOMUNICACIONES	9.21	ÁREA TÉCNICA
ZDR-01	ZONA DE REFUGIO (PMR)	3.64	ZONA DE REFUGIO
ZDR-02	ZONA DE REFUGIO (PMR)	7.29	ZONA DE REFUGIO
ZDR-03	ZONA DE REFUGIO (PMR)	2.43	ZONA DE REFUGIO
		1290.07	
EDIFICIO DESCENDENTE			
ARQ_PL_02_INTERMEDIO			
NPA-04	ÁREA NO PAGA	690.73	ÁREA NO PAGA
O-00-1	CIRCULACIÓN ÁREAS OPERATIVAS	79.23	ÁREA OPERATIVA
O-00-2	CIRCULACIÓN ÁREAS OPERATIVAS	33.85	ÁREA OPERATIVA
O-00-3	CIRCULACIÓN ÁREAS OPERATIVAS	7.84	ÁREA OPERATIVA
O-00-4	CIRCULACIÓN ÁREAS OPERATIVAS	3.92	ÁREA OPERATIVA
O-01	VENTA AUTOMÁTICA DE BOLETOS	16.27	ÁREA OPERATIVA
O-02	BAÑOS PÚBLICOS DE HOMBRES	34.66	SERVICIO PÚBLICO
O-03	BAÑOS PÚBLICOS DE MUJERES	39.50	SERVICIO PÚBLICO
O-04	CONTROL DE ACCESO BAÑOS PÚBLICOS	4.07	SERVICIO PÚBLICO
O-05	LOCAL DE INFORMACIÓN	7.90	ÁREA OPERATIVA
O-06	OFICINA DEL SUPERVISOR DE LA ESTACIÓN	45.65	ÁREA OPERATIVA
O-07	CUARTO DE LIMPIEZA	21.38	ÁREA OPERATIVA
O-08	SALA DE DESCANSO PARA EMPLEADOS	28.81	ÁREA OPERATIVA
O-09	BAÑOS EMPLEADOS HOMBRES	22.57	ÁREA OPERATIVA
O-10	BAÑOS EMPLEADOS MUJERES	22.59	ÁREA OPERATIVA
O-11	VESTIDORES EMPLEADOS HOMBRES	26.82	ÁREA OPERATIVA
O-12	VESTIDORES EMPLEADOS MUJERES	25.01	ÁREA OPERATIVA
O-13	LOCAL DE POLICÍA	32.13	ÁREA OPERATIVA
O-14	CALABOZO	6.58	ÁREA OPERATIVA
O-15	LOCAL PRIMEROS AUXILIOS	16.02	ÁREA OPERATIVA
O-16	SALA DE REUNIONES	37.40	ÁREA OPERATIVA
O-20	SALA DE LACTANCIA	24.43	ÁREA OPERATIVA
O-21-3	ALMACENAMIENTO DE LA ESTACIÓN	35.10	ÁREA OPERATIVA
O-22	OFICINA DE MANTENIMIENTO	36.33	ÁREA OPERATIVA
O-23	BAÑO PÚBLICO - FAMILIAR	8.72	SERVICIO PÚBLICO
O-24	CUARTO DE LIMPIEZA DE BAÑOS PÚBLICOS	3.37	SERVICIO PÚBLICO
O-25	BAÑO PÚBLICO - CORREDOR OPERACIONAL	15.95	SERVICIO PÚBLICO
O-26	ALMACENAMIENTO DE BASURAS METRO	40.70	ÁREA OPERATIVA
P-05	BIBLIOMETRO	71.29	ÁREA PÚBLICA
P-06	ESPACIO IPES (INSTITUTO PARA LA ECONOMÍA SOCIAL)	18.80	ÁREA PÚBLICA
P-07	SALÓN MÚLTIPLE EMB	100.16	ÁREA PÚBLICA
PA-01	ÁREA PAGA	281.35	ÁREA PAGA
R-103	SERVICIOS ADICIONALES - ÁREA DE SERVICIO	208.90	SERVICIOS ADICIONALES - ÁREA NO PAGA
R-301	SERVICIOS ADICIONALES - MÁQUINAS EXPENDEDORAS/CAJEROS AUTOMÁTICOS	7.92	SERVICIOS ADICIONALES - ÁREA NO PAGA
R-302	SERVICIOS ADICIONALES - MÁQUINAS EXPENDEDORAS/CAJEROS AUTOMÁTICOS	11.97	SERVICIOS ADICIONALES - ÁREA NO PAGA
T-21-4	ÁREA DE INSPECCIÓN	15.89	ÁREA TÉCNICA
T-21-5	ÁREA DE INSPECCIÓN	7.58	ÁREA TÉCNICA
T-21-6	ÁREA DE INSPECCIÓN	22.20	ÁREA TÉCNICA
T-25-4	NODO DE ACCESO DE TELECOMUNICACIONES	3.25	ÁREA TÉCNICA
ZDR-03	ZONA DE REFUGIO (PMR)	5.25	ZONA DE REFUGIO
ZDR-04	ZONA DE REFUGIO (PMR)	6.36	ZONA DE REFUGIO
		2128.46	
NAVE CENTRAL			
ARQ_PL_02_INTERMEDIO			
PA-01	ÁREA PAGA	355.94	ÁREA PAGA
		355.94	
TOTAL NIVEL INTERMEDIO		3774.46	

TABLA DE ÁREAS ÚTILES POR DEPARTAMENTO (NIVEL INTERMEDIO)

DEPARTAMENTO	ÁREA (m²)
EDIFICIO ASCENDENTE	
ARQ_PL_02_INTERMEDIO	
SERVICIOS ADICIONALES - ÁREA PAGA	24.68
ZONA DE REFUGIO	13.36
ÁREA NO PAGA	377.95
ÁREA OPERATIVA	23.69
ÁREA PAGA	816.87
ÁREA TÉCNICA	33.53
EDIFICIO DESCENDENTE	
ARQ_PL_02_INTERMEDIO	
SERVICIO PÚBLICO	106.27
SERVICIOS ADICIONALES - ÁREA NO PAGA	228.80
ZONA DE REFUGIO	11.61
ÁREA NO PAGA	690.73
ÁREA OPERATIVA	570.52
ÁREA PAGA	281.35
ÁREA PÚBLICA	190.26
ÁREA TÉCNICA	48.92
NAVE CENTRAL	
ARQ_PL_02_INTERMEDIO	
ÁREA PAGA	355.94
TOTAL NIVEL INTERMEDIO	3774.46

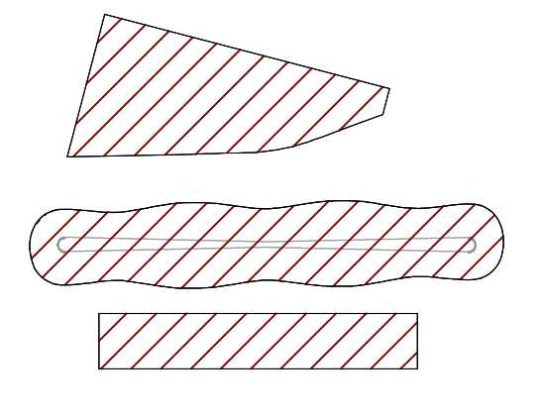

PLANO CLAVE ESTACIÓN 13

VÁLIDO PARA CONSTRUCCIÓN
31-03-26

LOCALIZACIÓN

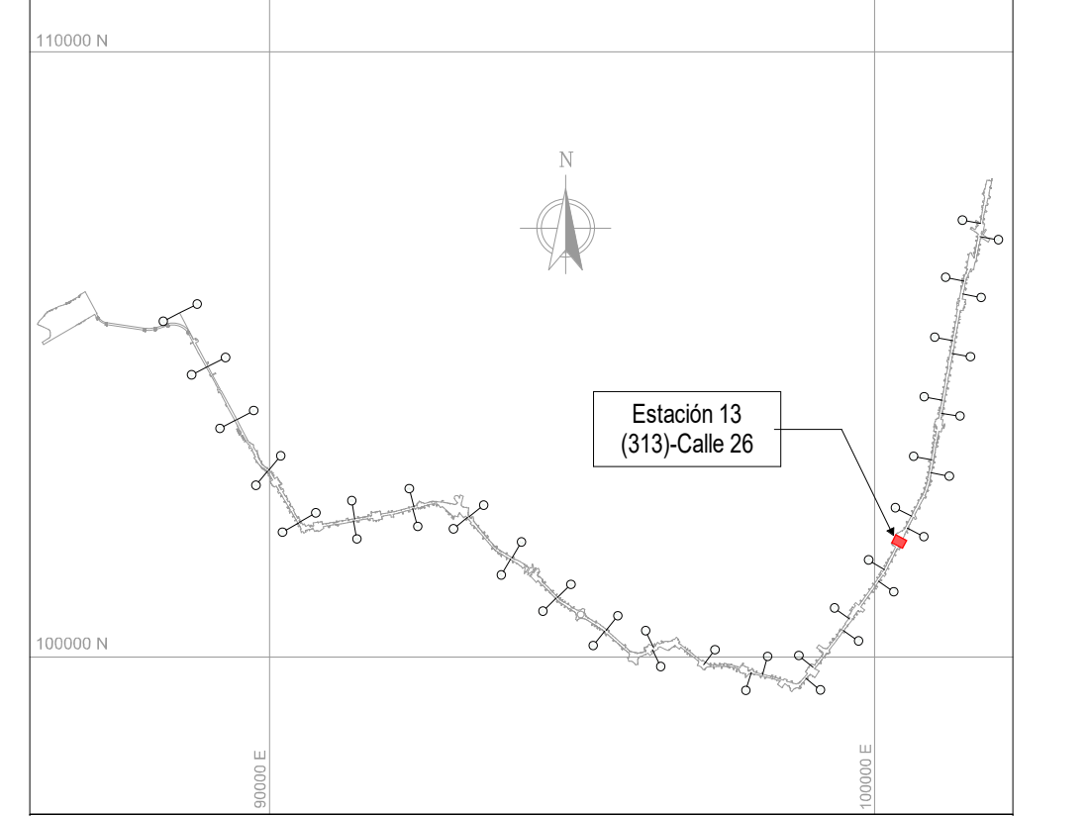

NOTAS

01 TODAS LAS DIMENSIONES ESTÁN CONFIGURADAS EN METROS A MENOS QUE SE INDIQUE UNA UNIDAD DE MEDIDA DIFERENTE.

02 TODAS LAS MEDIDAS, UBICACIÓN Y NIVELES DEBEN VERIFICARSE EN EL LUGAR DE CONSTRUCCIÓN.

03 EL NIVEL DE ACCESO AL EDIFICIO PL 01 CORRESPONDE AL +0,00 DE LA ESTACIÓN Y REFERENCIA AL NIVEL 2591.30 M.S.N.M.

04 LOS NOMBRES ESPECIFICOS DE LAS ÁREAS PUEDEN SER CONSULTADAS EN EL PLANO NO. 3 Ó EN LAS VISTAS EN PLANTA.

05 LOS COLORES QUE SE MUESTRAN EN LOS PLANOS COMO PROYECCIÓN DE ELEMENTOS ARQUITECTÓNICOS COMO CUBIERTAS FACHADAS MUROS ETC. NO REPRESENTAN LA MATERIALIDAD Y REALIDAD DE ACABADOS DEL PROYECTO, SOLO SON INDICATIVOS PARA REALIZAR UNA CORRECTA LECTURA DE LA PLANIMETRÍA.

06 LAS ESCALERAS ELÉCTRICAS INDICAN SU SENTIDO CON LA SIGUIENTE NOMENCLATURA: "SUBE" Y "BAJA".

07 SE DEBEN REVISAR LOS NIVELES ESTRUCTURALES PARA NIVEL DE ACCESO PL_01 Y SUBNIVELES, PL_02 (INTERMEDIO), PL_03 (PLATAFORMA) CON LA PLANIMETRÍA DE PLACAS ESTRUCTURALES EN LOS ENTREGABLES L1T1-1300-413-CON-ED-EST-PL-0046, 45, 47, 67, 68, 69, 70, 71, 91 RESPECTIVAMENTE. EL NIVEL ESTRUCTURAL (NE) REFERENCIA LOS ESPACIOS DONDE SE DEBE ACONDICIONAR EL ACABADO DE PISO SEGÚN CORRESPONDA, CON LOS NIVELES DE PISO TERMINADO (NPT). LOS NIVELES PROYECTADOS DE EMPATE (NPE) EN LAS ÁREAS DE SERVICIOS ADICIONALES, REFERENCIAN LA ADECUACIÓN DE LOS DESNIVELES EN ESTAS ÁREAS; QUEDA COMO RESPONSABILIDAD DEL LOCATARIO DEFINIR Y ACONDICIONAR ESTE ACABADO DE PISO (NPE) EN LÍNEA CON EL NIVEL (NPT) DE ESPACIOS COLINDANTES. EL NIVEL ESTRUCTURAL (NE) SE ENCUENTRA A (- 0.10M) POR DEBAJO DE LOS NIVELES DE PISO TERMINADO (NPT) Y LOS NIVELES PROYECTADOS DE EMPATE (NPE) MARCADOS EN LA PLANIMETRÍA.

- ARQ_PL_00 = SÓTANO / NPT -9.10m
- ARQ_PL_00.1 = ACCESO / NPT -2.80m
- ARQ_PL_00.2 = ACCESO / NPT -2.30m
- ARQ_PL_00.3 = ACCESO / NPT -1.50m
- ARQ_PL_00.4 = ACCESO / NPT -0.90m
- ARQ_PL_00.5 = ACCESO / NPT -0.75m
- ARQ_PL_00.6 = ACCESO / NPT -0.50m
- ARQ_PL_00.7 = ACCESO / NPT -0.30m
- ARQ_PL_01 = ACCESO / NPT 0.00m
- ARQ_PL_02 = INTERMEDIO / NPT 6.60m
- ARQ_PL_02.2 = TOPE DE RIEL (TOR) / NPT 14.20m
- ARQ_PL_03 = PLATAFORMA/ NIVEL 1 CCO / NPT 15.34m
- ARQ_PL_04 = CUBIERTA EDIFICIO ASCENDENTE / NPT 21.94m
- ARQ_PL_05 = CUBIERTA NAVE CENTRAL / NPT 24.60m
- ARQ_PL_06 = NIVEL 2 CCO / NPT 28.54m
- ARQ_PL_07 = CUBIERTA EDIFICIO ASCENDENTE / NPT 36.84m

CONVENCIONES

╍╍	LÍMITE DE INTERVENCIÓN
╍╍	HUELLA APÉNDICE TÉCNICO
▬	MURO DIVISORIO
---	PROYECCIÓN NIVEL SUPERIOR
🟩	SERVICIOS ADICIONALES - ÁREA NO PAGA
🟩	SERVICIOS ADICIONALES - ÁREA PAGA
🟥	ÁREA CULTURAL
🟦	ÁREA OPERATIVA
🟧	ÁREA PAGA
🟨	ÁREA NO PAGA
🟦	ÁREA PÚBLICA
🟩	SERVICIO PÚBLICO
🟦	ZONA DE REFUGIO
⬜	ÁREA TÉCNICA
🟦	SERVICIOS ADICIONALES - ÁREA DE OFICINAS

No.	PLANOS DE REFERENCIA	REV.

No.	MODELO BIM DE REFERENCIA	REV.
1	L1T1-1100-213-CON-ED-EST-MO-0001.rvt	V00
2	L1T1-1100-214-CON-ED-EST-MO-0001.rvt	V00
3	L1T1-1100-313-CON-ED-EST-MO-0001.rvt	V00
4	L1T1-1150-213-CON-ED-EST-MO-0001.rvt	V00
5	L1T1-1150-214-CON-ED-EST-MO-0001.rvt	V00
6	L1T1-1150-313-CON-ED-EST-MO-0001.rvt	V00
7	L1T1-1200-313-CON-ED-EST-MO-0001.rvt	V00
8	L1T1-1300-413-CON-ED-EST-MO-0001.rvt	V00
9	L1T1-1300-413-CON-ED-EST-MO-0002.rvt	V00
10	L1T1-1310-413-CON-ED-EST-MO-0001.rvt	V00
11	L1T1-1410-313-CON-ED-MEC-MO-0001.rvt	V00
12	L1T1-1420-313-CON-ED-MEC-MO-0001.rvt	V00
13	L1T1-5160-313-CON-ED-EST-MO-0001.rvt	V00
14	L1T1-5160-313-CON-ED-ARQ-MO-0001.rvt	V00
15	L1T1-5300-313-CON-ED-MEC-MO-0001.rvt	V00
16	L1T1-5600-313-CON-ED-INS-MO-0001.rvt	V00
17	L1T1-1330-413-CON-ED-ARQ-MO-0011.rvt	V00
18	L1T1-1330-413-CON-ED-ARQ-MO-0012.rvt	V00

No.	PAQUETE DE TRABAJO DE REFERENCIA	REV.
1	XREF-URBANISM-CONTEXT-ST13.rvt	
2	XREF-SECONDARY-STRUCTURE-ST13.rvt	

0 2 10m
1:200

METRO BOGOTÁ

Consorcio Consultores PMO Bogotá

CONSORCIO SUPERVISOR PLMB

DISEÑÓ:
REN ZHENHUA
Licencia de Arq.nivel I (China): 1101735-614

APROBÓ:
DIEGO ERNESTO DUEÑAS
Mat.: 25202-53876 CND

REVISÓ:
CARLOS MAURICIO BARRETO BARBOSA
Mat.: A4012012-14139353

DIBUJÓ:
EQUIPO CHEC

REVISIÓN No.	FECHA	DESCRIPCIÓN	REVISÓ	APROBÓ	APROBACIÓN CLIENTE
V01	31/03/2026	EMITIDO PARA CONSTRUCCIÓN	C.M.B.B	D.E.D	
V00	13/05/2025	REVISION NO OBJETADA - EMITIDO PARA CONSTRUCCION	F.B.R	E.O.M	
VGG	09/09/2024	EMITIDO PARA REVISIÓN Y COMENTARIOS DEL CLIENTE E INTERVENTORÍA -INCLUYE COMENTARIOS /(AJUSTES V3)	F.B.R	E.O.M	
VFF	04/06/2024	EMITIDO PARA REVISIÓN Y COMENTARIOS DEL CLIENTE E INTERVENTORÍA -INCLUYE COMENTARIOS /(AJUSTES V2)	F.B.R	E.O.M	
VEE	06/01/2023	EMITIDO PARA REVISIÓN Y COMENTARIOS DEL CLIENTE E INTERVENTORÍA -INCLUYE COMENTARIOS /(90% ACCESOS)	J.E.M	M.B.M	
VDD	18/12/2022	EMITIDO PARA REVISIÓN Y COMENTARIOS DEL CLIENTE E INTERVENTORÍA - INCLUYE COMENTARIOS /(NAVE CENTRAL)	J.E.M	M.B.M	
VCC	22/08/2022	EMITIDO PARA REVISIÓN Y COMENTARIOS DEL CLIENTE E INTERVENTORÍA - INCLUYE COMENTARIOS /(ENTREGA 90%)	J.E.M	M.B.M	
VBB	06/12/2021	EMITIDO PARA REVISIÓN Y COMENTARIOS DEL CLIENTE E INTERVENTORÍA	J.E.M	M.B.M	
VA0	05/12/2021	EMITIDO PARA COMENTARIOS INTERNOS - EMISIÓN PRELIMINAR PARA COMENTARIOS	J.E.M	M.B.M	

METRO LÍNEA 1

METRO LÍNEA 1
CONTRATO DE CONCESIÓN No. 163 DE 2019

PROYECTO PRIMERA LÍNEA DEL METRO DE BOGOTÁ - TRAMO 1

DIRECTOR DE INTERVENTORÍA:
JAVIER DESCARGA N.
Mat.:25202-68697 CND

ESPECIALISTA INTERVENTORÍA:
CARLOS ALBERTO HOYOS SOTO
Mat.:A25072000-14251682

FECHA:
MARZO 2026

INFRAESTRUCTURA VIAL

ARQUITECTURA

ESTACIÓN METRO 13 (CALLE 26)
GENERAL
VISTA EN PLANTA Y 3D - NIVEL INTERMEDIO

PLANCHA No: L1T1-0000-313-CON-ED-ARQ-PL-0001_06_V01
ARCHIVO: L1T1-0000-313-CON-ED-ARQ-MO-0001_V00.rvt
ESCALA: INDICADA
FECHA: DICIEMBRE 2021
REVISIÓN No. V01
PLANO No. 06 DE 101