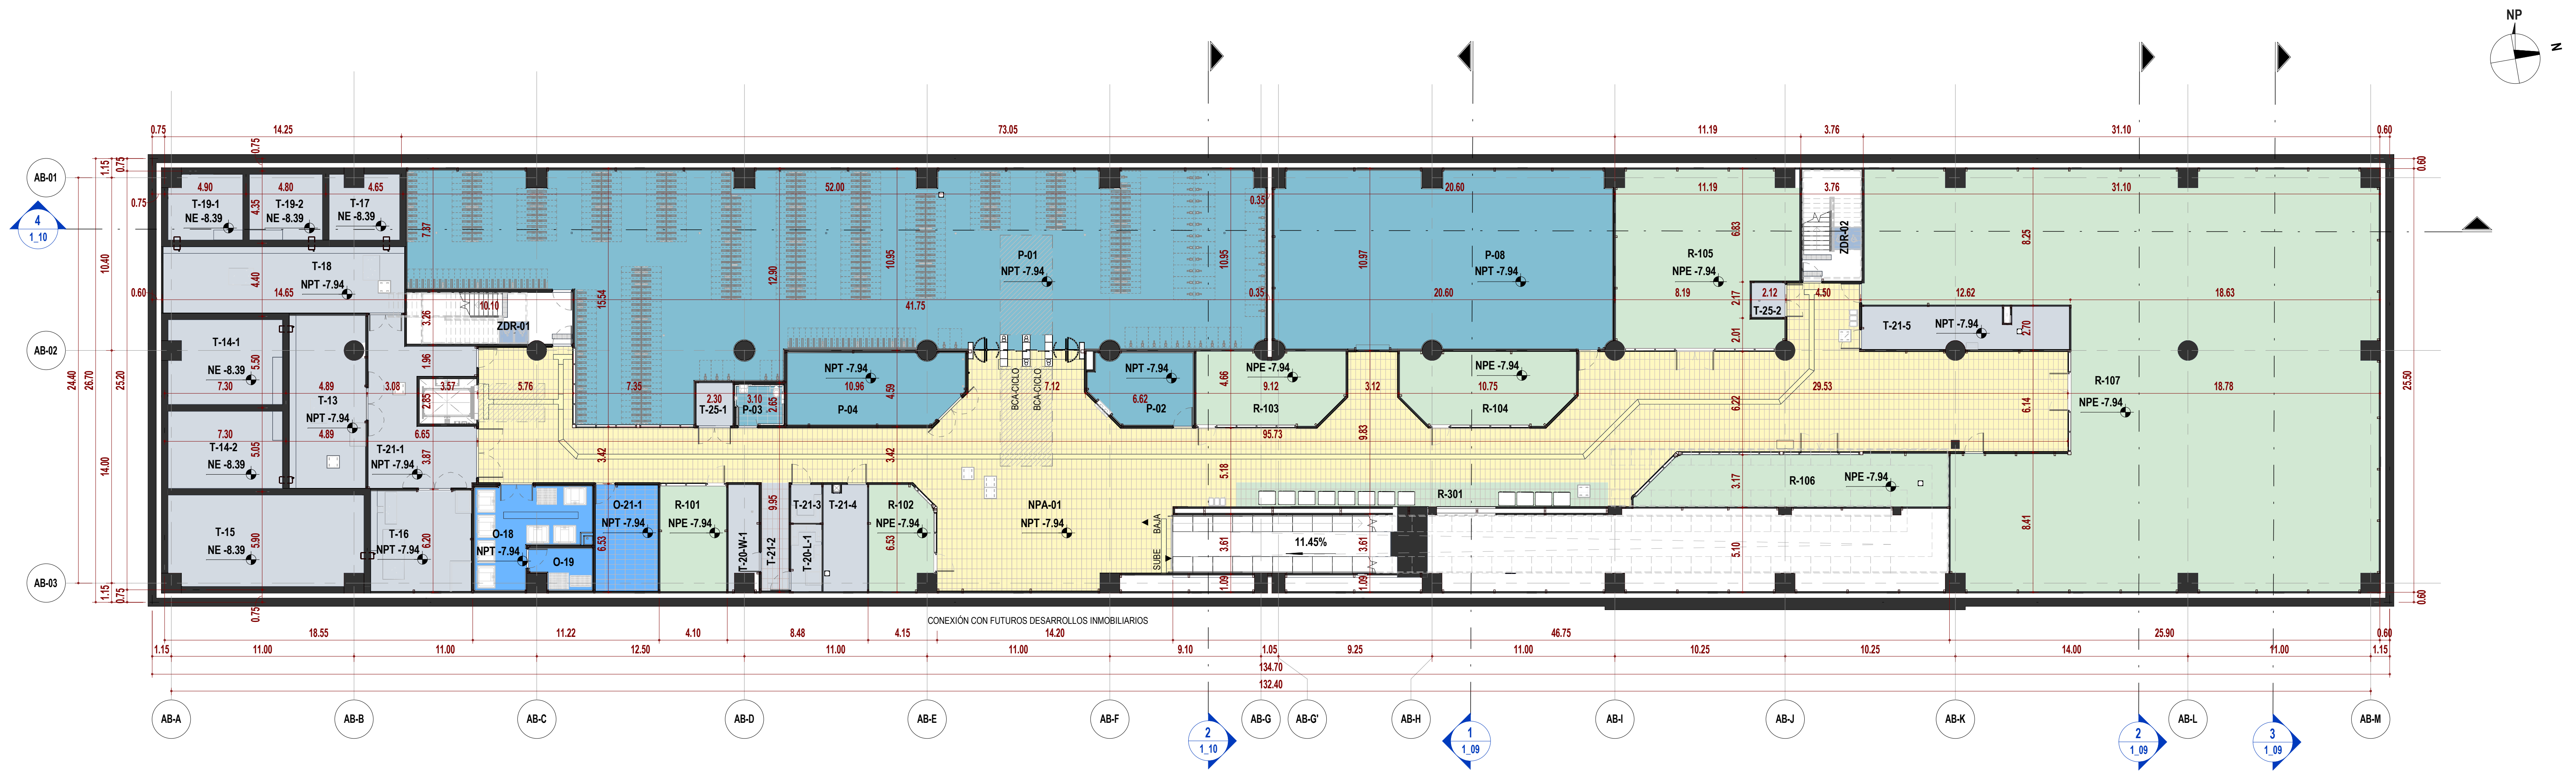

2 NIVEL SÓTANO_EDIFICIO ASCENDENTE
ESC: 1 : 200

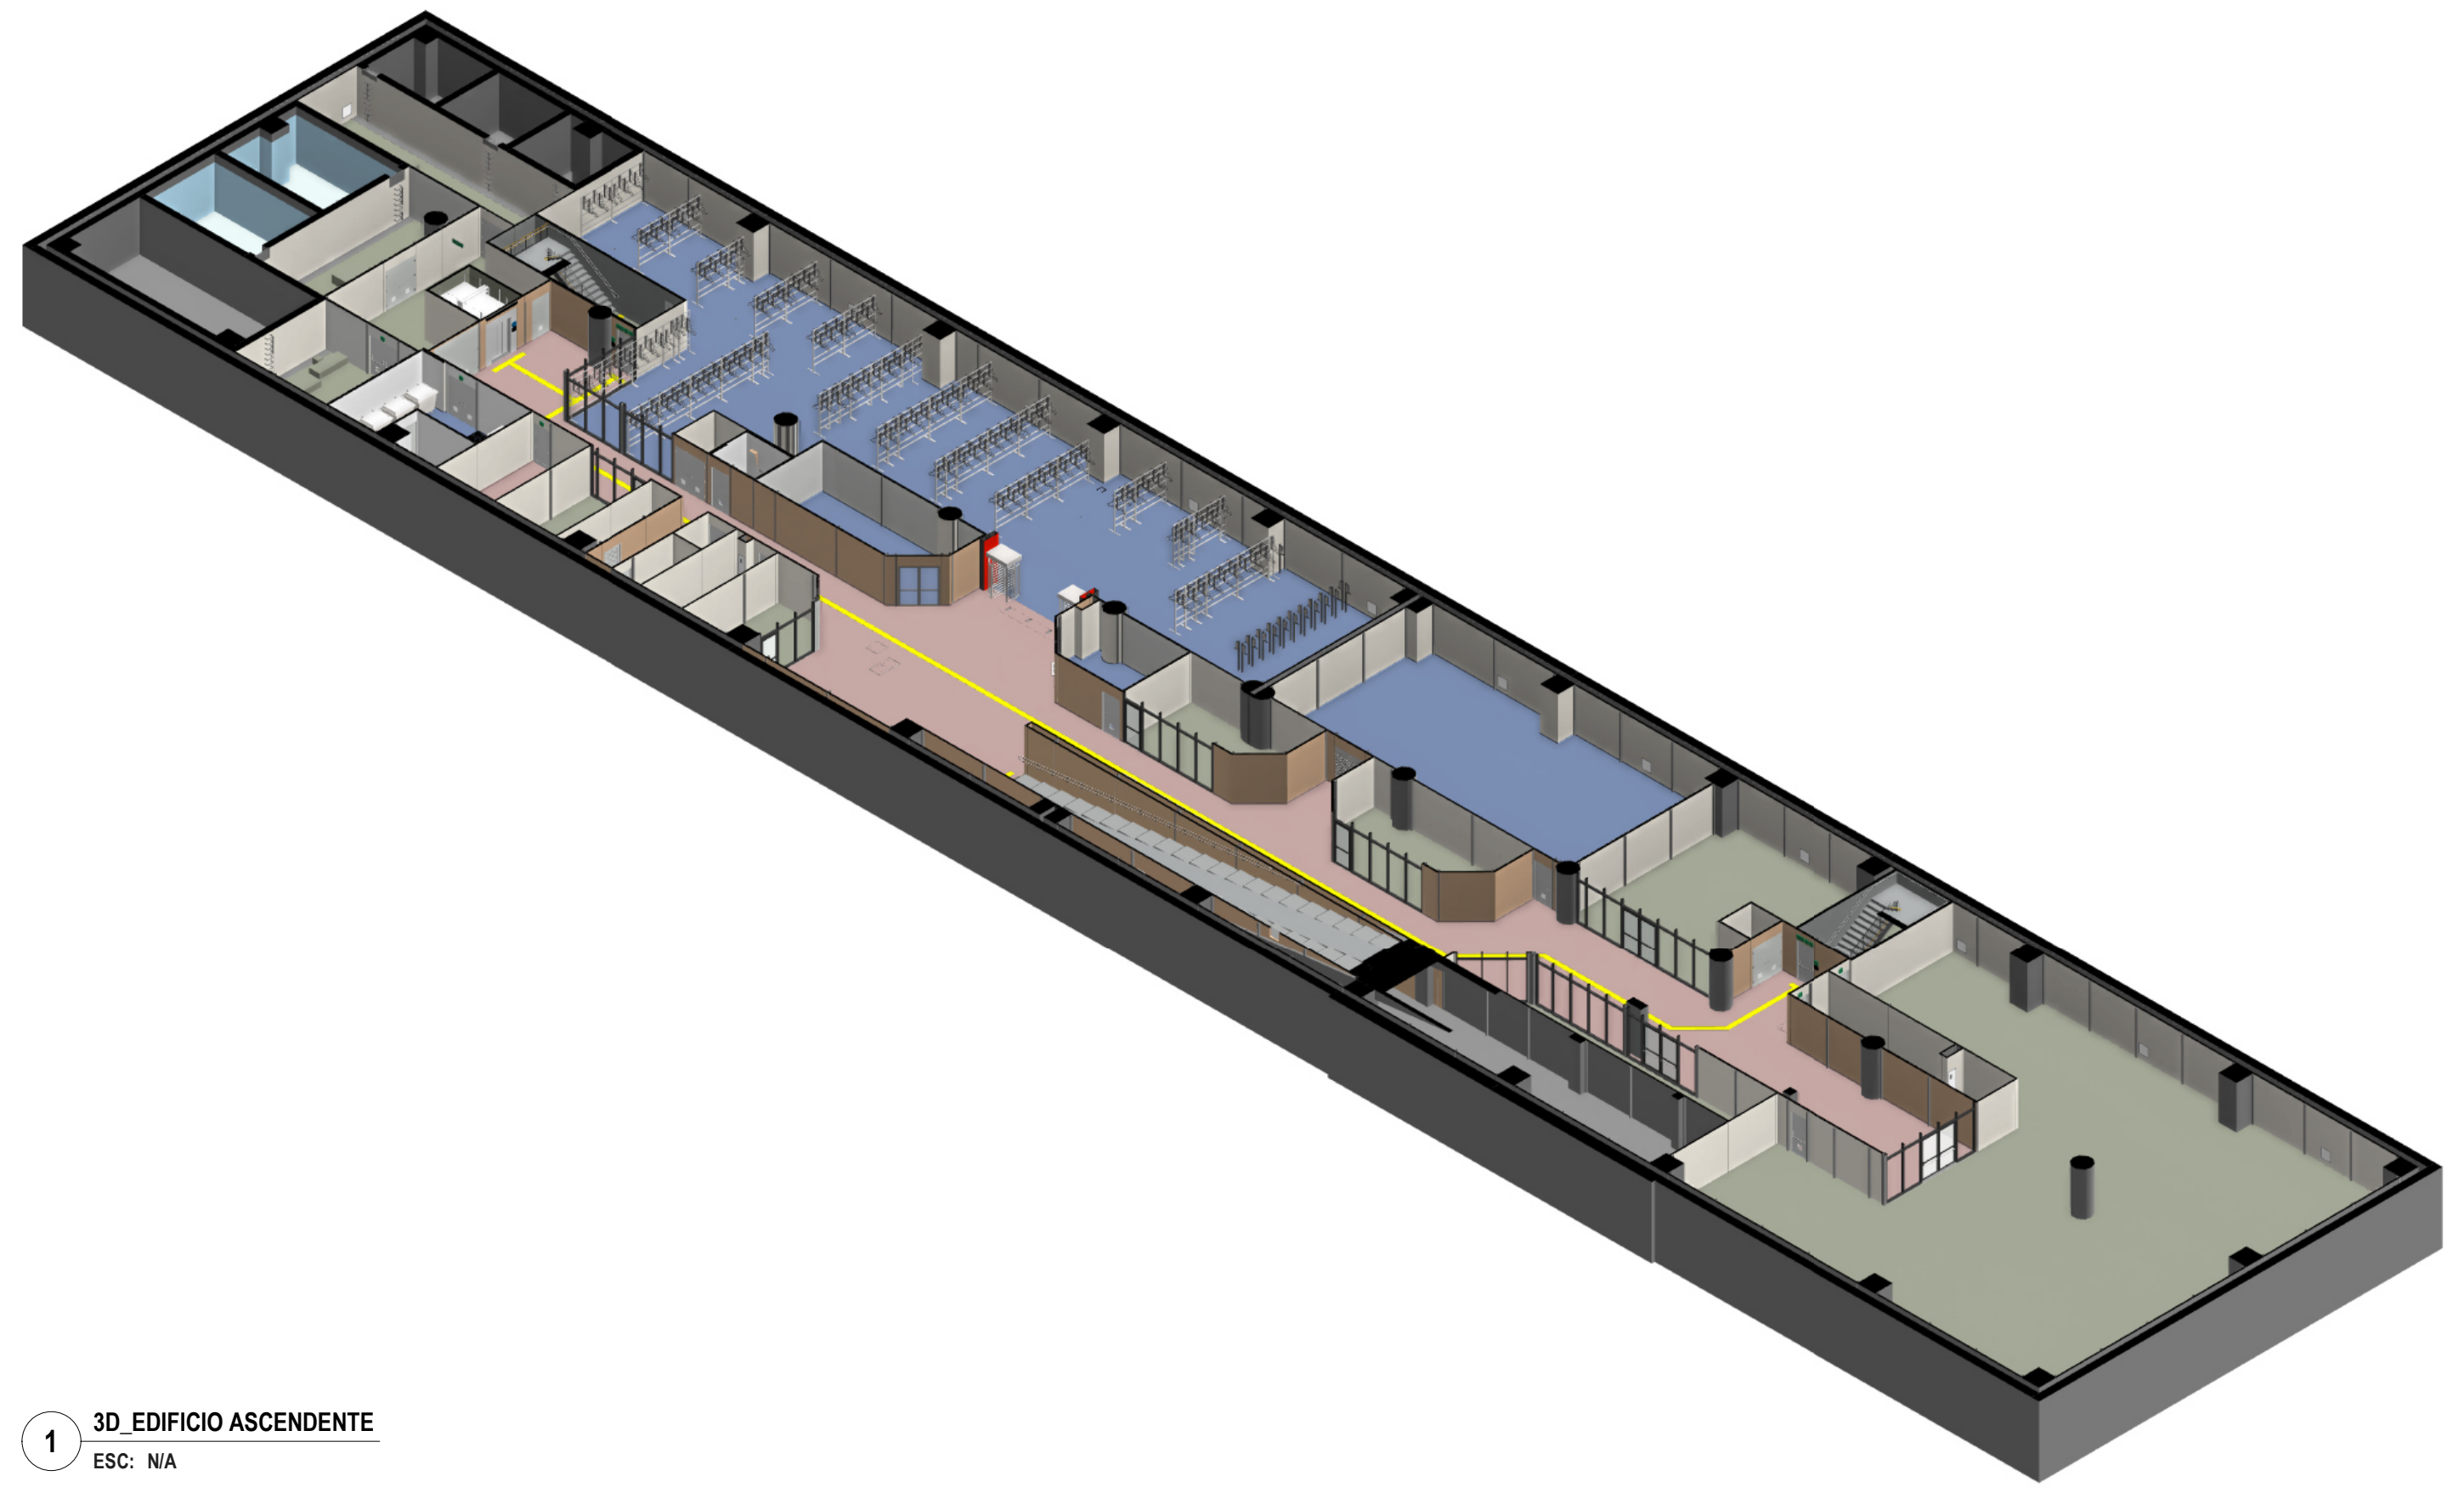

1 3D_EDIFICIO ASCENDENTE
ESC: N/A

TABLA DE ÁREAS ÚTILES (NIVEL SÓTANO)

CÓDIGO	NOMBRE	ÁREA (m²)	DEPARTAMENTO
EDIFICIO ASCENDENTE			
ARQ_PL_00_SÓTANO			
NPA-01	ÁREA NO PAGA	603.43	ÁREA NO PAGA
O-18	CUARTO DE ALMACENAMIENTO DE RESIDUOS SÓLIDOS	34.34	ÁREA OPERATIVA
O-19	CUARTO DE ALMACENAMIENTO DE RESIDUOS PELIGROSOS	8.85	ÁREA OPERATIVA
O-21-1	ALMACENAMIENTO DE LA ESTACIÓN	24.31	ÁREA OPERATIVA
P-01	ÁREA CICLO-PARQUEADEROS	558.48	ÁREA PÚBLICA
P-02	ÁREA OPERATIVA CICLO-PARQUEADEROS	25.45	ÁREA PÚBLICA
P-03	BAÑO OPERADOR CICLO-PARQUEADEROS	7.06	ÁREA PÚBLICA
P-04	TALLER DE BICICLETAS	45.15	ÁREA PÚBLICA
P-08	ESPACIO CARGA DE VEHÍCULOS ELÉCTRICOS	217.99	ÁREA PÚBLICA
R-101	SERVICIOS ADICIONALES - ÁREA DE SERVICIO	25.28	SERVICIOS ADICIONALES - ÁREA NO PAGA
R-102	SERVICIOS ADICIONALES - ÁREA DE SERVICIO	22.87	SERVICIOS ADICIONALES - ÁREA NO PAGA
R-103	SERVICIOS ADICIONALES - ÁREA DE SERVICIO	37.43	SERVICIOS ADICIONALES - ÁREA NO PAGA
R-104	SERVICIOS ADICIONALES - ÁREA DE SERVICIO	43.28	SERVICIOS ADICIONALES - ÁREA NO PAGA
R-105	SERVICIOS ADICIONALES - ÁREA DE SERVICIO	107.97	SERVICIOS ADICIONALES - ÁREA NO PAGA
R-106	SERVICIOS ADICIONALES - ÁREA DE SERVICIO	55.84	SERVICIOS ADICIONALES - ÁREA NO PAGA
R-107	SERVICIOS ADICIONALES - ÁREA DE SERVICIO	622.22	SERVICIOS ADICIONALES - ÁREA NO PAGA
R-301	SERVICIOS ADICIONALES - MÁQUINAS EXPENDEDORAS/CAJEROS AUTOMÁTICOS	32.81	SERVICIOS ADICIONALES - ÁREA NO PAGA
T-13	CUARTO DE BOMBAS DE SUMINISTRO DE AGUA	46.48	ÁREA TÉCNICA
T-14-1	TANQUE DE SUMINISTRO DE AGUA	34.12	ÁREA TÉCNICA
T-14-2	TANQUE DE SUMINISTRO DE AGUA	31.97	ÁREA TÉCNICA
T-15	TANQUE SISTEMA DE EXTINCIÓN DE INCENDIOS (RCI)	63.14	ÁREA TÉCNICA
T-16	CUARTO DE BOMBAS PARA ROCIADORES	36.61	ÁREA TÉCNICA
T-17	TANQUE RECUPERACIÓN AGUAS LLUVIAS	15.74	ÁREA TÉCNICA
T-18	CUARTO DE BOMBAS DE RECUPERACIÓN DE AGUAS LLUVIAS Y EQUIPO DE FILTRACIÓN	58.01	ÁREA TÉCNICA
T-19-1	TANQUE DE AGUA TRATADA	17.05	ÁREA TÉCNICA
T-19-2	TANQUE DE AGUA TRATADA	17.30	ÁREA TÉCNICA
T-20-L-1	MEDIDORES (LUZ)	7.33	ÁREA TÉCNICA
T-20-W-1	MEDIDORES (AGUA)	10.15	ÁREA TÉCNICA
T-21-1	ÁREA DE INSPECCIÓN	48.96	ÁREA TÉCNICA
T-21-2	ÁREA DE INSPECCIÓN	11.00	ÁREA TÉCNICA
T-21-3	ÁREA DE INSPECCIÓN	4.16	ÁREA TÉCNICA
T-21-4	ÁREA DE INSPECCIÓN	16.63	ÁREA TÉCNICA
T-21-5	ÁREA DE INSPECCIÓN	31.02	ÁREA TÉCNICA
T-25-1	NODO DE ACCESO DE TELECOMUNICACIONES	5.65	ÁREA TÉCNICA
T-25-2	NODO DE ACCESO DE TELECOMUNICACIONES	4.04	ÁREA TÉCNICA
ZDR-01	ZONA DE REFUGIO (PMR)	2.43	ZONA DE REFUGIO
ZDR-02	ZONA DE REFUGIO (PMR)	2.43	ZONA DE REFUGIO
TOTAL NIVEL SÓTANO		2937.01	

TABLA DE ÁREAS ÚTILES POR DEPARTAMENTO (NIVEL SÓTANO_EDIFICIO ASCENDENTE)

DEPARTAMENTO	ÁREA (m²)
EDIFICIO ASCENDENTE	
ARQ_PL_00_SÓTANO	
SERVICIOS ADICIONALES - ÁREA NO PAGA	947.70
ZONA DE REFUGIO	4.86
ÁREA NO PAGA	603.43
ÁREA OPERATIVA	67.51
ÁREA PÚBLICA	854.13
ÁREA TÉCNICA	459.37
TOTAL NIVEL SÓTANO	2937.01

TABLA DE CICLO-PARQUEADEROS ESPECÍFICA

TIPOLOGÍA	CANTIDAD	USUARIOS
ARQ_PL_00_SÓTANO		
BICIPARQUEADERO ASISTIDO EN ACERO INOXIDABLE ASTM A240, a=0.70m X l=1.20m, h=1.70m.	1	EMPLEADOS
BICIPARQUEADERO DE COLGAR, 2 PUESTOS, a=1.20m X l=0.70m, h=2.40m. ACABADO EN PINTURA ELECTROSTÁTICA COLOR RAL9005 "NEGRO INTENSO".	4	EMPLEADOS
EMPLEADOS	5	
BICIPARQUEADERO ASISTIDO EN ACERO INOXIDABLE ASTM A240, a=0.70m X l=1.20m, h=1.70m.	50	VISITANTE
BICIPARQUEADERO DE COLGAR DE 6 PUESTOS EN ACERO, a=1.20m X l=2.10m, h=2.40m. ACABADO EN PINTURA ELECTROSTÁTICA COLOR RAL9005 "NEGRO INTENSO".	396	VISITANTE
BICIPARQUEADERO DE COLGAR, 1 PUESTO, a=1.20m X l=0.70m, h=2.40m. ACABADO EN PINTURA ELECTROSTÁTICA COLOR RAL9005 "NEGRO INTENSO".	8	VISITANTE
BICIPARQUEADERO DE COLGAR, 2 PUESTOS, a=1.20m X l=0.70m, h=2.40m. ACABADO EN PINTURA ELECTROSTÁTICA COLOR RAL9005 "NEGRO INTENSO".	58	VISITANTE
VISITANTE	512	
TOTAL CUPOS	517	

LOCALIZACIÓN

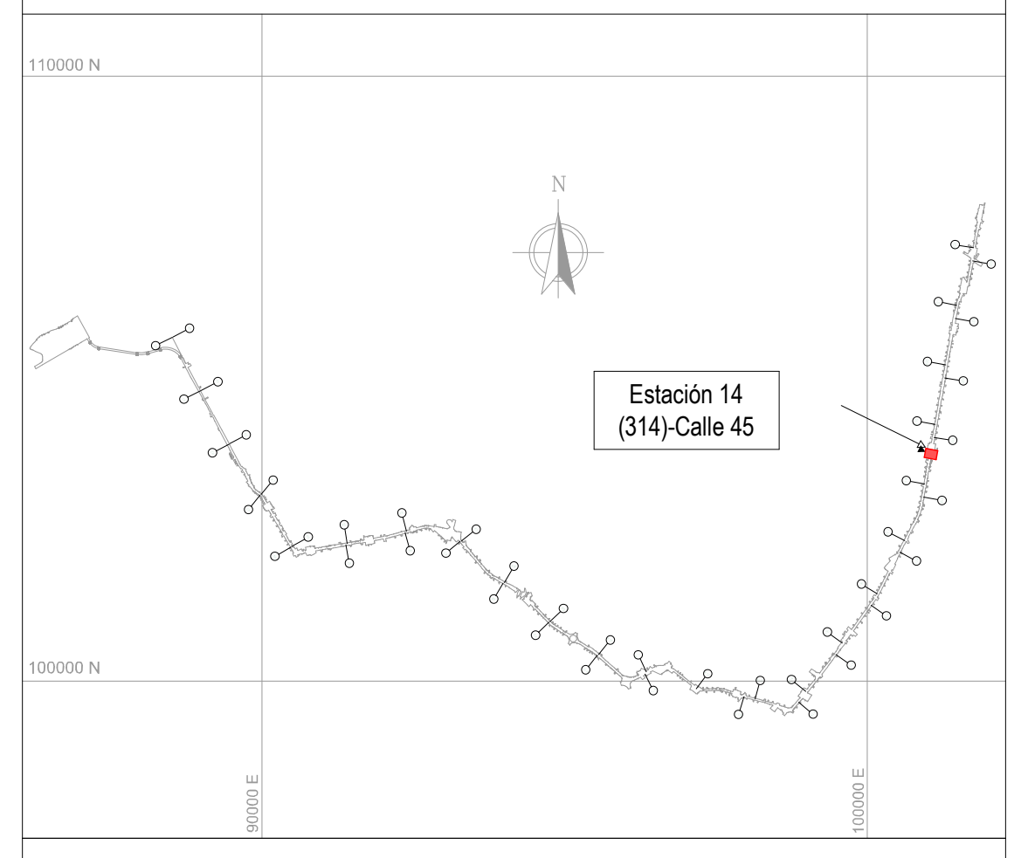

NOTAS

01 TODAS LAS DIMENSIONES ESTÁN CONFIGURADAS EN METROS A MENOS QUE SE INDIQUE UNA UNIDAD DE MEDIDA DIFERENTE.

02 TODAS LAS MEDIDAS, UBICACIÓN Y NIVELES DEBEN VERIFICARSE EN EL LUGAR DE CONSTRUCCIÓN.

03 EL NIVEL DE ACCESO AL EDIFICIO PL 01 CORRESPONDE AL +0,00 DE LA ESTACIÓN Y REFERENCIA AL NIVEL 2574.39 M.S.N.M.

04 LOS NOMBRES ESPECÍFICOS DE LAS ÁREAS PUEDEN SER CONSULTADAS EN EL PLANO NO. 3 Ó EN LAS VISTAS EN PLANTA.

05 LOS COLORES QUE SE MUESTRAN EN LOS PLANOS COMO PROYECCIÓN DE ELEMENTOS ARQUITECTÓNICOS COMO CUBIERTAS FACHADAS MUROS ETC. NO REPRESENTAN LA MATERIALIDAD Y REALIDAD DE ACABADOS DEL PROYECTO, SOLO SON INDICATIVOS PARA REALIZAR UNA CORRECTA LECTURA DE LA PLANIMETRÍA.

06 SE DEBEN REVISAR LOS NIVELES ESTRUCTURALES PARA NIVEL DE ACCESO PL_01 Y SUBNIVELES, PL_02 (INTERMEDIO), PL_03 (PLATAFORMA) CON LA PLANIMETRÍA DE PLACAS ESTRUCTURALES EN LOS ENTREGABLES L1T1-1300-414-CON-ED-EST-PL-0038, 39, 42, 43, 126, 86, RESPECTIVAMENTE. EL NIVEL ESTRUCTURAL (NE) REFERENCIA LOS ESPACIOS DONDE SE DEBE ACONDICIONAR EL ACABADO DE PISO SEGÚN CORRESPONDA, CON LOS NIVELES DE PISO TERMINADO (NPT). LOS NIVELES PROYECTADOS DE EMPATE (NPE) EN LAS ÁREAS DE SERVICIOS ADICIONALES, REFERENCIAN LA ADECUACIÓN DE LOS DESNIVELES EN ESTAS ÁREAS; QUEDA COMO RESPONSABILIDAD DEL LOCATARIO DEFINIR Y ACONDICIONAR ESTE ACABADO DE PISO (NPE) EN LÍNEA CON EL NIVEL (NPT) DE ESPACIOS COLINDANTES. EL NIVEL ESTRUCTURAL (NE) SE ENCUENTRA A (- 0.10M) POR DEBAJO DE LOS NIVELES DE PISO TERMINADO (NPT) Y LOS NIVELES PROYECTADOS DE EMPATE (NPE) MARCADOS EN LA PLANIMETRÍA.

07 RESPECTO A LAS ÁREAS CONSTRUIDAS Y DE ACUERDO CON LA COMUNICACIÓN EXTS22-0002544 DE EMB, SE IDENTIFICA QUE EL CONCESIONARIO SE ENCUENTRA BUSCANDO ESTRATEGIAS PARA MEJORAR EL DISEÑO CON EL PROGRAMA ARQUITECTÓNICO, UNA DE ESTAS ESTRATEGIAS ES MEJORAR EL FUNCIONAMIENTO DEL DISEÑO URBANO Y BRINDAR UNA SOLUCIÓN INTEGRAL RESPECTO A LOS INMUEBLES DE INTERÉS CULTURAL. DE ACUERDO CON LO ANTERIOR, PARA LA EMB, ESTAS ACTIVIDADES OBEDECEN AL PROCESO NATURAL DE LOS ESTUDIOS Y DISEÑOS DEFINITIVOS QUE DEBE DESARROLLAR METRO LÍNEA 1.

- ARQ_PL_00 = SÓTANO / NPT -7.94m
- ARQ_PL_00.1 = ACCESO / NPT -3.84m
- ARQ_PL_00.2 = ACCESO / NPT -3.69m
- ARQ_PL_00.3 = ACCESO / NPT -3.39m
- ARQ_PL_00.4 = ACCESO / NPT -3.29m
- ARQ_PL_00.5 = ACCESO / NPT -3.19m
- ARQ_PL_00.6 = ACCESO / NPT -3.04m
- ARQ_PL_00.7 = ACCESO / NPT -2.89m
- ARQ_PL_00.8 = ACCESO / NPT -2.69m
- ARQ_PL_00.9 = ACCESO / NPT -2.54m
- ARQ_PL_00.10 = ACCESO / NPT -2.09m
- ARQ_PL_00.11 = ACCESO / NPT -1.84m
- ARQ_PL_00.12 = ACCESO / NPT -1.59m
- ARQ_PL_00.13 = ACCESO / NPT -1.29m
- ARQ_PL_00.14 = ACCESO / NPT -1.09m
- ARQ_PL_00.15 = ACCESO / NPT -0.99m
- ARQ_PL_00.16 = ACCESO / NPT -0.79m
- ARQ_PL_00.17 = ACCESO / NPT -0.69m
- ARQ_PL_00.18 = ACCESO / NPT -0.49m
- ARQ_PL_00.19 = ACCESO / NPT -0.34m
- ARQ_PL_01 = ACCESO / NPT 0.00m
- ARQ_PL_02 = INTERMEDIO / NPT 6.64m
- ARQ_PL_02.2 = TOPE DE RIEL (TOR) / NPT 14.24m
- ARQ_PL_03 = PLATAFORMA / NPT 15.38m
- ARQ_PL_04 = CUBIERTA EDIFICACIONES / NPT 21.98m
- ARQ_PL_05 = CUBIERTA NAVE CENTRAL / NPT 24.64m

CONVENCIONES

🟩	SERVICIOS ADICIONALES - ÁREA NO PAGA	🟨	ÁREA NO PAGA
🟩	SERVICIOS ADICIONALES - ÁREA PAGA	🟨	ÁREA PAGA
🟩	SERVICIO PÚBLICO	🟦	ÁREA PÚBLICA
🟦	ZONA DE REFUGIO	⬜	ÁREA TÉCNICA
🟥	ÁREA CULTURAL	🟦	ÁREA OPERATIVA
🟪	ÁREA DE TAQUILLAS BRT		

No.	PLANOS DE REFERENCIA	REV.

No.	MODELO BIM DE REFERENCIA	REV.
1	L1T1-1100-214-CON-ED-EST-MO-0001.rvt	V00
2	L1T1-1100-215-CON-ED-EST-MO-0001.rvt	V00
3	L1T1-1100-314-CON-ED-EST-MO-0001.rvt	V00
4	L1T1-1150-214-CON-ED-EST-MO-0001.rvt	V00
5	L1T1-1150-215-CON-ED-EST-MO-0001.rvt	V00
6	L1T1-1150-314-CON-ED-EST-MO-0001.rvt	V00
7	L1T1-1200-314-CON-ED-EST-MO-0001.rvt	V00
8	L1T1-1300-414-CON-ED-EST-MO-0001.rvt	V01
9	L1T1-1300-414-CON-ED-EST-MO-0002.rvt	V01
10	L1T1-1300-414-CON-ED-EST-MO-0003.rvt	V01
11	L1T1-1310-414-CON-ED-EST-MO-0001.rvt	V00
12	L1T1-1410-314-CON-ED-MEC-MO-0001.rvt	V00
13	L1T1-1420-314-CON-ED-MEC-MO-0002.rvt	V00
14	L1T1-2320-588-CON-ED-EST-MO-0001.rvt	V00
15	L1T1-2320-588-CON-ED-ARQ-MO-0001.rvt	V00
16	L1T1-5160-314-CON-ED-EST-MO-0001.rvt	V00
17	L1T1-5160-314-CON-ED-ARQ-MO-0001.rvt	V00
18	L1T1-5300-314-CON-ED-MEC-MO-0001.rvt	V00
19	L1T1-5600-314-CON-ED-INS-MO-0001.rvt	V00

No.	PAQUETE DE TRABAJO DE REFERENCIA	REV.
1	XREF-URBANISM_CONTEXT_ST14.rvt	
2	XREF-SECONDARY-STRUCTURE-ST14.rvt	

0 2 10m
1:200

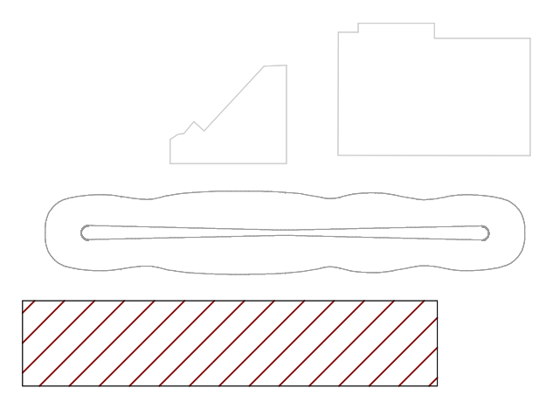

PLANO CLAVE ESTACIÓN 14

DISEÑÓ: Santiago A. David G SANTIAGO ANDRES DAVID GUZMÁN Mat.: A413202011-1010176190	APROBÓ: MAURICIO MEJÍA RESTREPO Mat.: 25202-72411 CND
REVISÓ: FREDDY BAUTISTA R. Mat.:25202-092831 CND	DIBUJÓ: EQUIPO WSP

REVISIÓN No.	FECHA	DESCRIPCIÓN	REVISÓ	APROBÓ	APROBACIÓN CLIENTE
V01	12/11/2025	REVISIÓN NO OBJETADA - EMITIDO PARA CONSTRUCCIÓN	F.B.R	M.M.R	
VB1	20/03/2025	EMITIDO PARA REVISIÓN Y COMENTARIOS DEL CLIENTE E INTERVENTORÍA	F.B.R	E.O.M	
V00	13/02/2025	REVISIÓN NO OBJETADA - EMITIDO PARA CONSTRUCCIÓN	F.B.R	E.O.M	
VFF	18/10/2024	EMITIDO PARA REVISIÓN Y COMENTARIOS DEL CLIENTE E INTERVENTORÍA - INCLUYE COMENTARIOS /(AJUSTES V3)	F.B.R	E.O.M	
VEE	17/07/2024	EMITIDO PARA REVISIÓN Y COMENTARIOS DEL CLIENTE E INTERVENTORÍA - INCLUYE COMENTARIOS /(AJUSTES V2)	F.B.R	E.O.M	
VDD	18/12/2022	EMITIDO PARA REVISIÓN Y COMENTARIOS DEL CLIENTE E INTERVENTORÍA - INCLUYE COMENTARIOS /(AJUSTES)	J.E.M	M.B.M	
VCC	02/06/2022	EMITIDO PARA REVISIÓN Y COMENTARIOS DEL CLIENTE E INTERVENTORÍA - INCLUYE COMENTARIOS /(ENTREGA 90%)	J.E.M	M.B.M	
VBB	06/12/2021	EMITIDO PARA REVISIÓN Y COMENTARIOS DEL CLIENTE E INTERVENTORÍA	J.E.M	M.B.M	
VA0	30/06/2021	EMITIDO PARA COMENTARIOS INTERNOS - EMISIÓN PRELIMINAR PARA COMENTARIOS	J.E.M	M.B.M	

METRO LÍNEA 1
CONTRATO DE CONCESIÓN No. 163 DE 2019

PROYECTO PRIMERA LÍNEA DEL METRO DE BOGOTÁ - TRAMO 1

INFRAESTRUCTURA VIAL
ARQUITECTURA
ESTACIÓN METRO 14 - (CALLE 45)
EDIFICIO ASCENDENTE
VISTA EN PLANTA Y 3D - NIVEL SÓTANO

DIRECTOR DE INTERVENTORÍA: JAVIER DESCARGA N. Mat.:25202-68697 CND	ESPECIALISTA INTERVENTORÍA: MARIA AUXILIADORA SANCHEZ HERMOSIN INT: PAH138382-RES.NO.34 DE 2021	FECHA: NOVIEMBRE 2025

PLANCHA No: L1T1-0000-314-CON-ED-ARQ-PL-0001_04_V01	ESCALA: INDICADA	REVISIÓN No. V01	PLANO No. 04 DE 96
ARCHIVO: L1T1-0000-314-CON-ED-ARQ-MO-0001_V01.rvt	FECHA: JUNIO 2021		