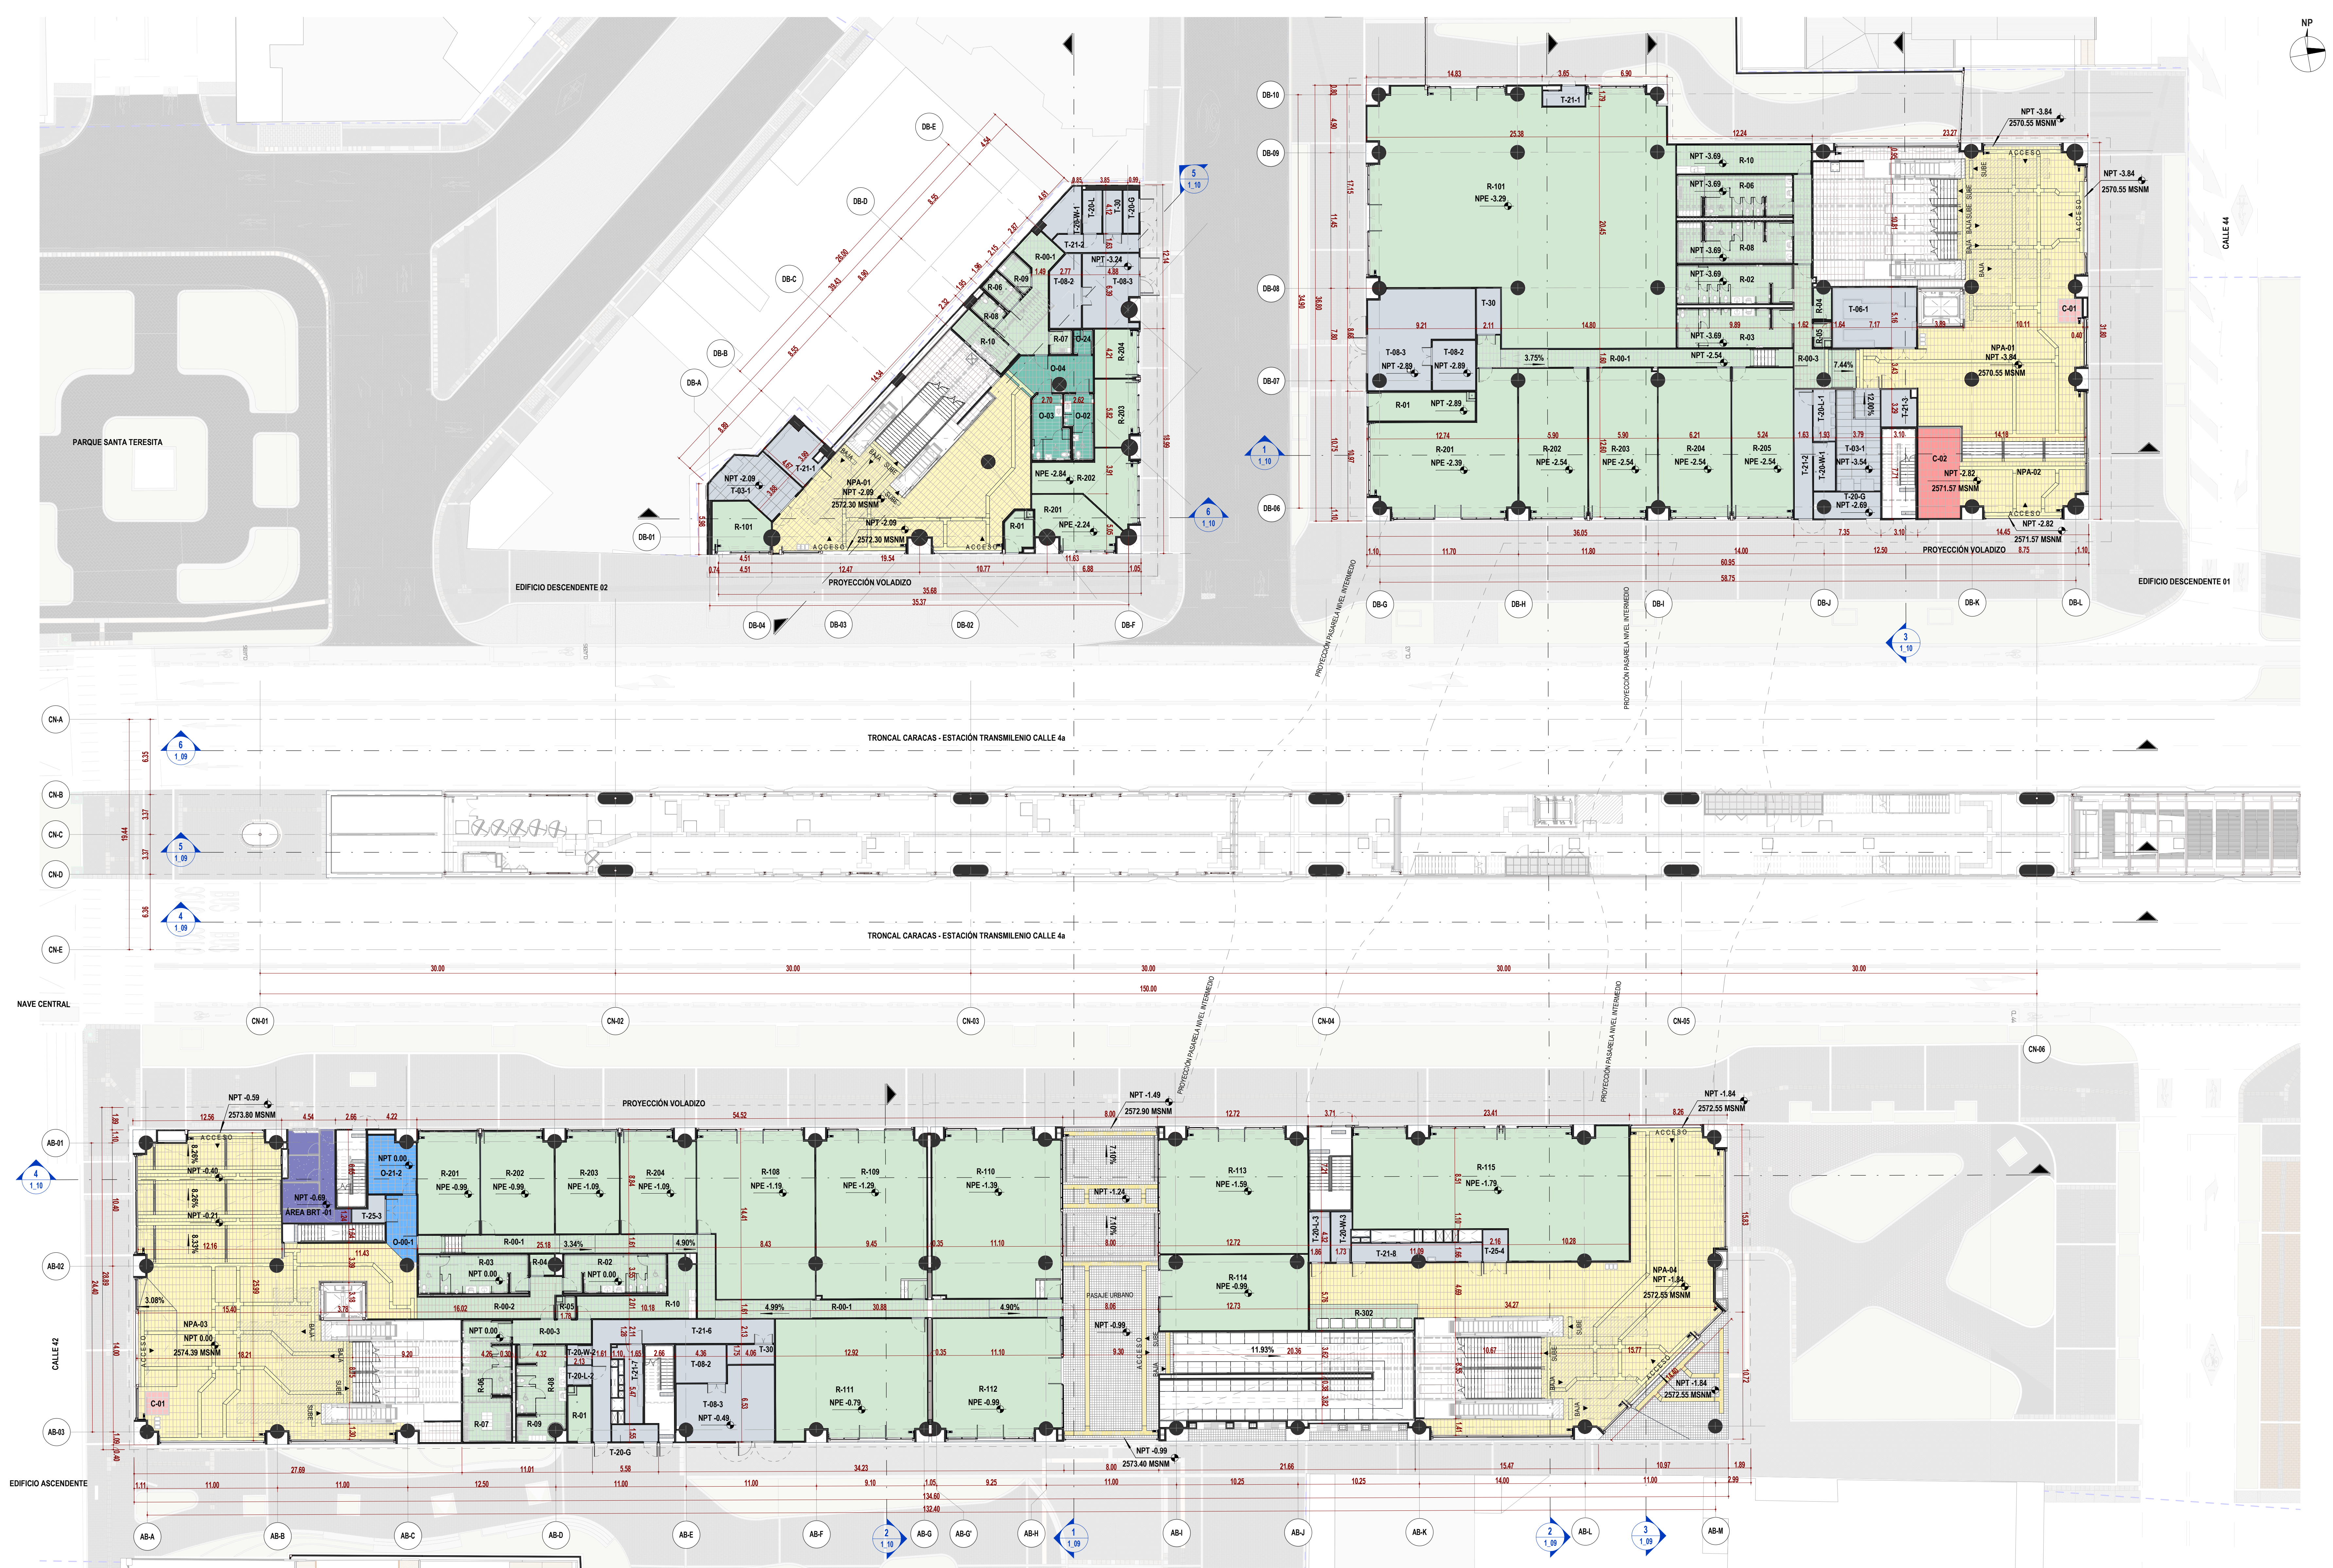

2 NIVEL ACCESO_GENERAL
ESC: 1 : 200

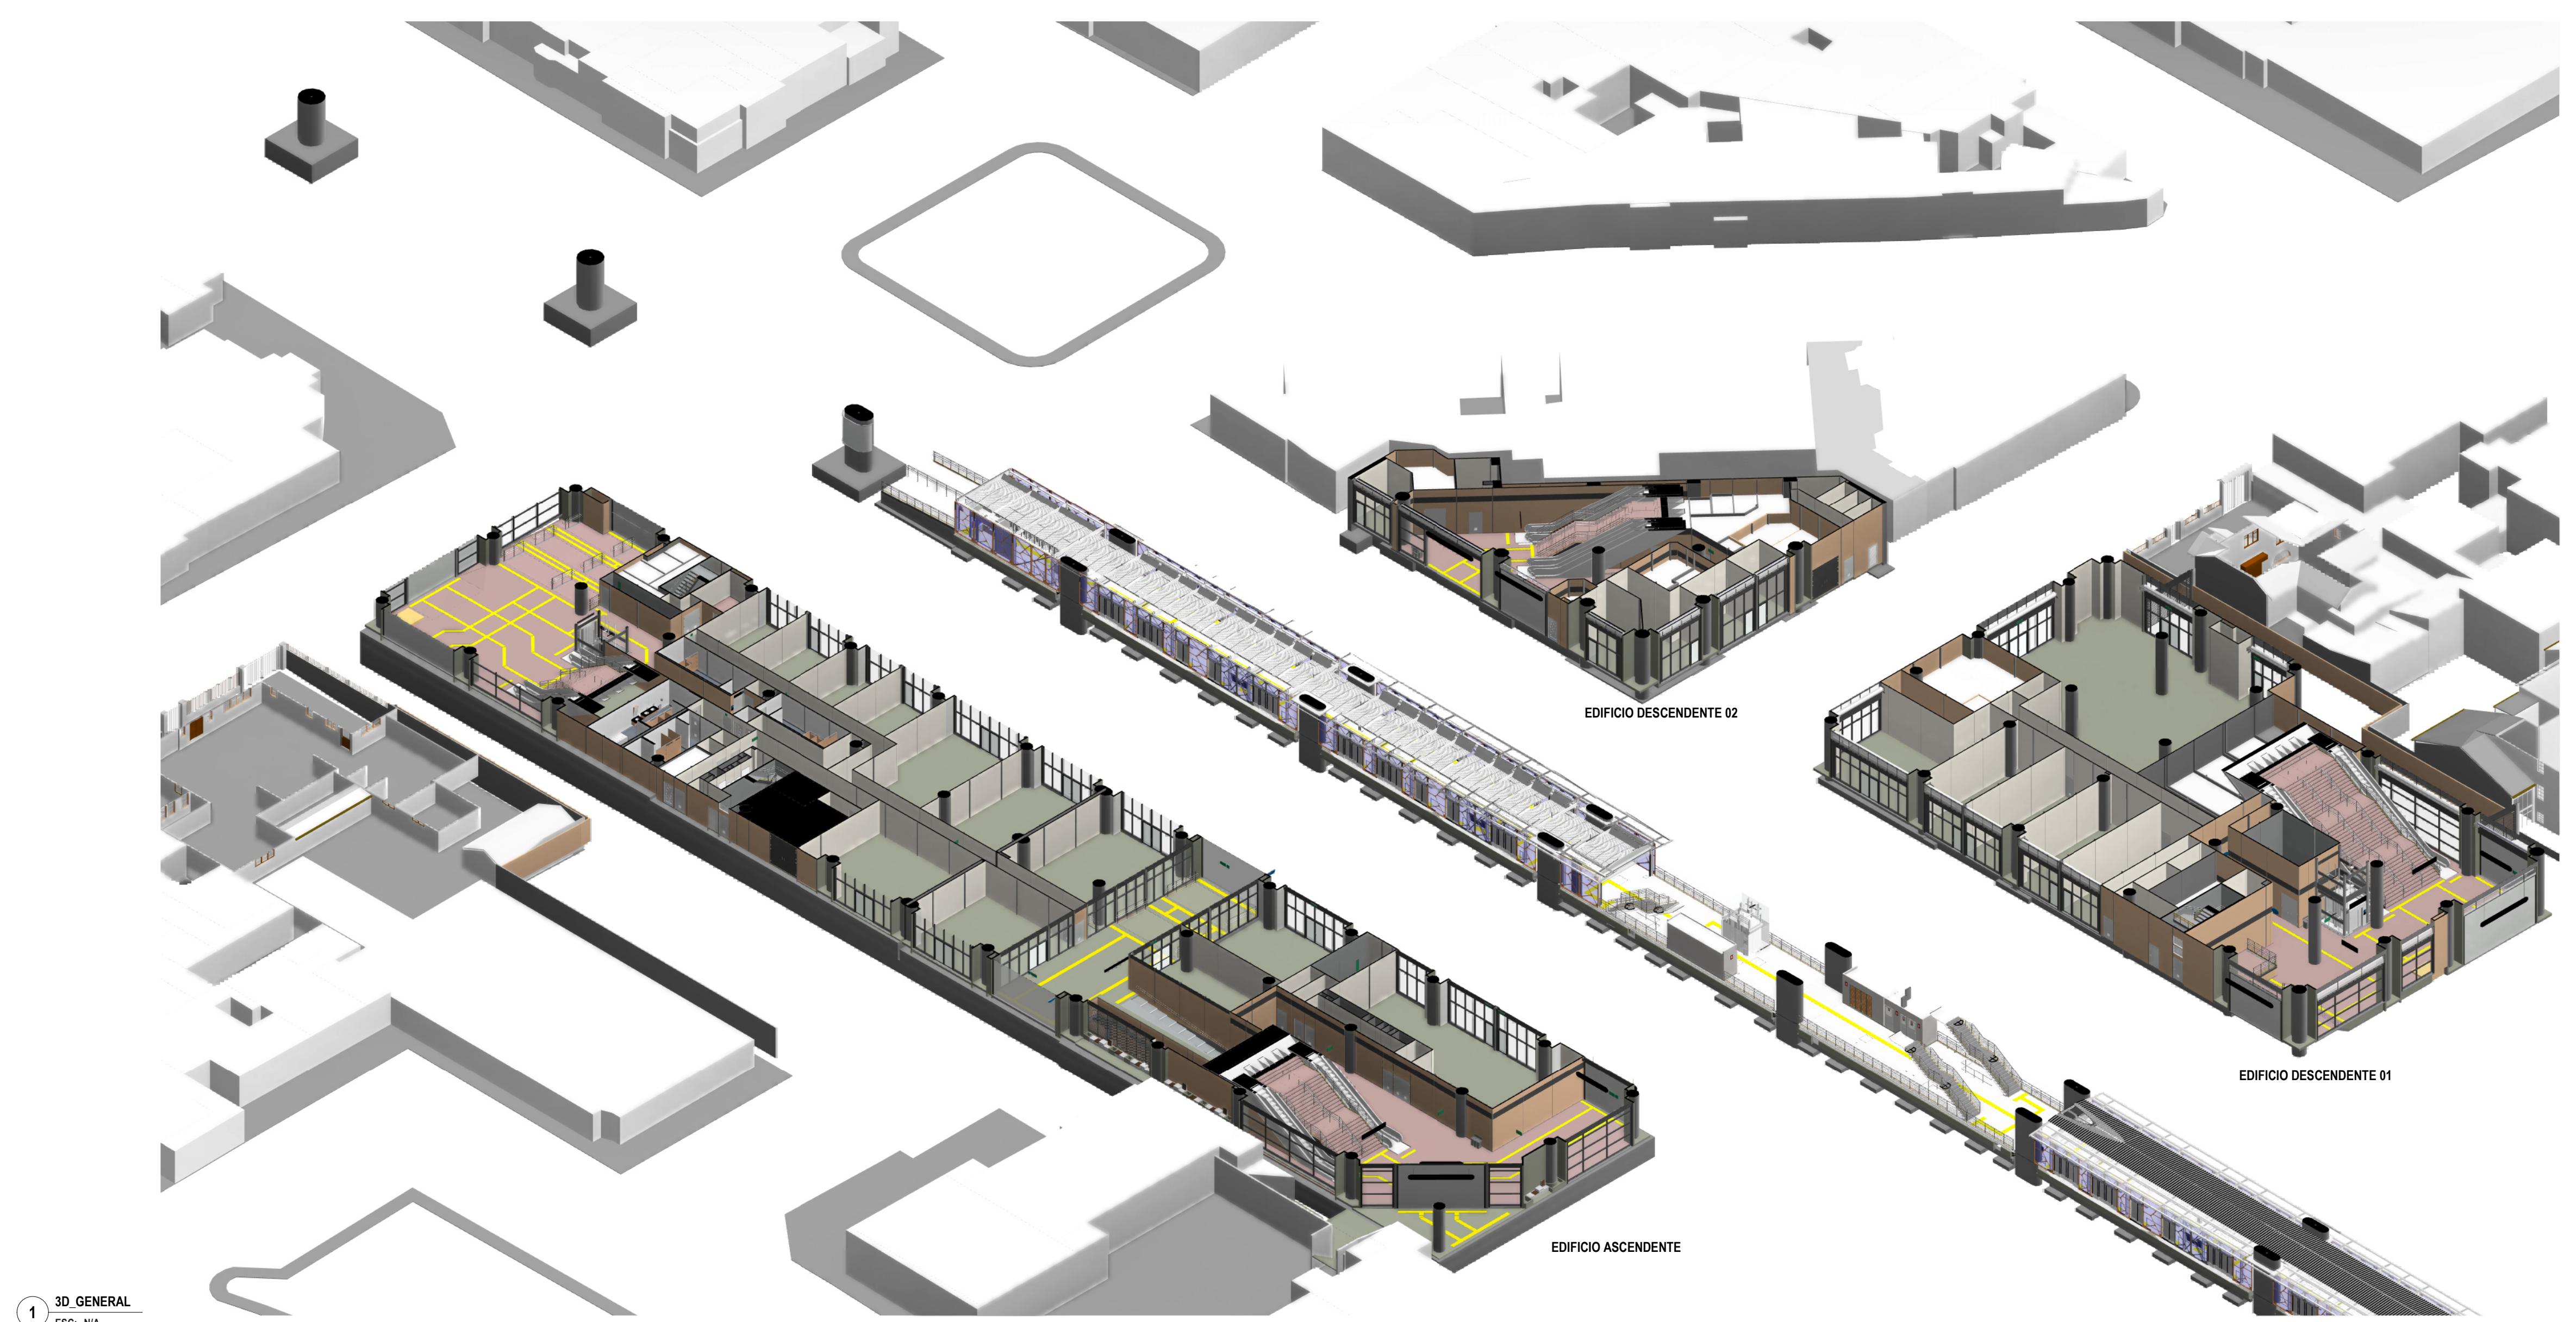

1 3D_GENERAL
ESC: N/A

TABLA DE ÁREAS ÚTILES (NIVEL ACCESO)

CÓDIGO	NOMBRE	ÁREA (m²)	DEPARTAMENTO
EDIFICIO ASCENDENTE			
ARQ_PL_00.11_ACCESO			
NPA-04	ÁREA NO PAGA	333.26	ÁREA NO PAGA
R-115	SERVICIOS ADICIONALES - ÁREA DE SERVICIO	220.27	SERVICIOS ADICIONALES - ÁREA NO PAGA
R-302	SERVICIOS ADICIONALES - MÁQUINAS EXPENDEDORAS/CAJEROS AUTOMÁTICOS	19.61	SERVICIOS ADICIONALES - ÁREA NO PAGA
T-20-L-3	MEDIDORES (LUZ)	7.31	ÁREA TÉCNICA
T-20-W-3	MEDIDORES (AGUA)	6.97	ÁREA TÉCNICA
T-21-8	ÁREA DE INSPECCIÓN	16.37	ÁREA TÉCNICA
T-25-4	NODO DE ACCESO DE TELECOMUNICACIONES	5.40	ÁREA TÉCNICA
		609.19	
ARQ_PL_00.12_ACCESO			
R-110	SERVICIOS ADICIONALES - ÁREA DE SERVICIO	148.15	SERVICIOS ADICIONALES - ÁREA NO PAGA
R-113	SERVICIOS ADICIONALES - ÁREA DE SERVICIO	123.15	SERVICIOS ADICIONALES - ÁREA NO PAGA
		271.30	
ARQ_PL_00.13_ACCESO			
R-108	SERVICIOS ADICIONALES - ÁREA DE SERVICIO	130.33	SERVICIOS ADICIONALES - ÁREA NO PAGA
R-109	SERVICIOS ADICIONALES - ÁREA DE SERVICIO	128.73	SERVICIOS ADICIONALES - ÁREA NO PAGA
		259.06	
ARQ_PL_00.14_ACCESO			
R-203	SERVICIOS ADICIONALES - ÁREA DE COMIDAS	45.34	SERVICIOS ADICIONALES - ÁREA NO PAGA
R-204	SERVICIOS ADICIONALES - ÁREA DE COMIDAS	52.48	SERVICIOS ADICIONALES - ÁREA NO PAGA
		97.82	
ARQ_PL_00.15_ACCESO			
R-00-1	SERVICIOS ADICIONALES - CORREDOR OPERATIVO	91.83	SERVICIOS ADICIONALES - ÁREA NO PAGA
R-112	SERVICIOS ADICIONALES - ÁREA DE SERVICIO	105.89	SERVICIOS ADICIONALES - ÁREA NO PAGA
R-114	SERVICIOS ADICIONALES - ÁREA DE SERVICIO	77.08	SERVICIOS ADICIONALES - ÁREA NO PAGA
R-201	SERVICIOS ADICIONALES - ÁREA DE COMIDAS	44.76	SERVICIOS ADICIONALES - ÁREA NO PAGA
R-202	SERVICIOS ADICIONALES - ÁREA DE COMIDAS	52.11	SERVICIOS ADICIONALES - ÁREA NO PAGA
		371.67	
ARQ_PL_00.16_ACCESO			
R-111	SERVICIOS ADICIONALES - ÁREA DE SERVICIO	126.26	SERVICIOS ADICIONALES - ÁREA NO PAGA
		126.26	
ARQ_PL_00.17_ACCESO			
NPA-02	ÁREA NO PAGA	123.65	ÁREA NO PAGA
ÁREA BRT -01	ÁREA BRT	35.34	ÁREA DE TAQUILLAS BRT
		158.99	
ARQ_PL_00.18_ACCESO			
R-01	SERVICIOS ADICIONALES - CUARTO DE BASURAS PARA METRO	9.26	SERVICIOS ADICIONALES - ÁREA NO PAGA
T-08-2	CENTRO DE TRANSFORMACIÓN ENEL-CODENSA (CT)_CUARTO BAJA TENSIÓN	13.27	ÁREA TÉCNICA
T-08-3	CENTRO DE TRANSFORMACIÓN ENEL-CODENSA (CT)_CUARTO MEDIA TENSIÓN	44.25	ÁREA TÉCNICA
T-20-G	MEDIDORES (GAS)	5.48	ÁREA TÉCNICA
T-20-L-2	MEDIDORES (LUZ)	3.21	ÁREA TÉCNICA
T-20-W-2	MEDIDORES (AGUA)	3.33	ÁREA TÉCNICA
T-21-6	ÁREA DE INSPECCIÓN	43.06	ÁREA TÉCNICA
T-21-7	ÁREA DE INSPECCIÓN	11.19	ÁREA TÉCNICA
T-30	SISTEMA PROTECCIÓN CONTRA INCENDIO ENEL	6.28	ÁREA TÉCNICA
		139.35	
ARQ_PL_01_ACCESO			
C-01	ÁREAS DE USO CULTURAL	4.00	ÁREA CULTURAL
NPA-03	ÁREA NO PAGA	288.48	ÁREA NO PAGA
O-00-1	CIRCULACIÓN ÁREAS OPERATIVAS	12.99	ÁREA OPERATIVA
O-21-2	ALMACENAMIENTO DE LA ESTACIÓN	18.50	ÁREA OPERATIVA
R-00-2	SERVICIOS ADICIONALES - CORREDOR OPERATIVO	25.57	SERVICIOS ADICIONALES - ÁREA NO PAGA
R-00-3	SERVICIOS ADICIONALES - CORREDOR OPERATIVO	13.53	SERVICIOS ADICIONALES - ÁREA NO PAGA
R-02	SERVICIOS ADICIONALES - BAÑO PÚBLICO DE MUJERES	27.82	SERVICIOS ADICIONALES - ÁREA NO PAGA
R-03	SERVICIOS ADICIONALES - BAÑO PÚBLICO DE HOMBRES	29.77	SERVICIOS ADICIONALES - ÁREA NO PAGA
R-04	SERVICIOS ADICIONALES - CONTROL DE ACCESO BAÑOS PÚBLICOS	3.16	SERVICIOS ADICIONALES - ÁREA NO PAGA
R-05	SERVICIOS ADICIONALES - CUARTO DE LIMPIEZA	3.05	SERVICIOS ADICIONALES - ÁREA NO PAGA
R-06	SERVICIOS ADICIONALES - BAÑOS EMPLEADOS MUJERES	25.54	SERVICIOS ADICIONALES - ÁREA NO PAGA
R-07	SERVICIOS ADICIONALES - VESTIDORES EMPLEADOS MUJERES	15.61	SERVICIOS ADICIONALES - ÁREA NO PAGA
R-08	SERVICIOS ADICIONALES - BAÑOS EMPLEADOS HOMBRES	23.69	SERVICIOS ADICIONALES - ÁREA NO PAGA
R-09	SERVICIOS ADICIONALES - VESTIDORES EMPLEADOS HOMBRES	7.61	SERVICIOS ADICIONALES - ÁREA NO PAGA
R-10	SERVICIOS ADICIONALES - SALA DE EMPLEADOS	25.88	SERVICIOS ADICIONALES - ÁREA NO PAGA
T-25-3	NODO DE ACCESO DE TELECOMUNICACIONES	4.72	ÁREA TÉCNICA
		529.90	
EDIFICIO DESCENDENTE 01			
ARQ_PL_00.01_ACCESO			
C-01	ÁREAS DE USO CULTURAL	4.00	ÁREA CULTURAL
NPA-01	ÁREA NO PAGA	313.98	ÁREA NO PAGA
T-03-1	LOCAL SECUNDARIO DE TELECOMUNICACIONES	31.12	ÁREA TÉCNICA
T-06-1	LOCAL SECUNDARIO DE TABLEROS	35.29	ÁREA TÉCNICA
T-21-3	ÁREA DE INSPECCIÓN	8.91	ÁREA TÉCNICA
		393.31	
ARQ_PL_00.02_ACCESO			
R-00-2	SERVICIOS ADICIONALES - CORREDOR OPERATIVO	11.19	SERVICIOS ADICIONALES - ÁREA NO PAGA
R-00-3	SERVICIOS ADICIONALES - CORREDOR OPERATIVO	26.66	SERVICIOS ADICIONALES - ÁREA NO PAGA
R-02	SERVICIOS ADICIONALES - BAÑO PÚBLICO DE MUJERES	31.30	SERVICIOS ADICIONALES - ÁREA NO PAGA
R-03	SERVICIOS ADICIONALES - BAÑO PÚBLICO DE HOMBRES	31.42	SERVICIOS ADICIONALES - ÁREA NO PAGA
R-04	SERVICIOS ADICIONALES - CONTROL DE ACCESO BAÑOS PÚBLICOS	3.46	SERVICIOS ADICIONALES - ÁREA NO PAGA
R-05	SERVICIOS ADICIONALES - CUARTO DE LIMPIEZA	3.10	SERVICIOS ADICIONALES - ÁREA NO PAGA
R-06	SERVICIOS ADICIONALES - BAÑOS EMPLEADOS MUJERES	25.65	SERVICIOS ADICIONALES - ÁREA NO PAGA
R-07	SERVICIOS ADICIONALES - VESTIDORES EMPLEADOS MUJERES	7.81	SERVICIOS ADICIONALES - ÁREA NO PAGA
R-08	SERVICIOS ADICIONALES - BAÑOS EMPLEADOS HOMBRES	26.22	SERVICIOS ADICIONALES - ÁREA NO PAGA
R-09	SERVICIOS ADICIONALES - VESTIDORES EMPLEADOS HOMBRES	7.56	SERVICIOS ADICIONALES - ÁREA NO PAGA
R-10	SERVICIOS ADICIONALES - SALA DE EMPLEADOS	27.20	SERVICIOS ADICIONALES - ÁREA NO PAGA
		201.55	
ARQ_PL_00.04_ACCESO			
R-101	SERVICIOS ADICIONALES - ÁREA DE SERVICIO	487.43	SERVICIOS ADICIONALES - ÁREA NO PAGA
T-21-1	ÁREA DE INSPECCIÓN	5.26	ÁREA TÉCNICA
		492.69	
ARQ_PL_00.07_ACCESO			
C-02	ÁREAS DE USO CULTURAL	26.79	ÁREA CULTURAL
NPA-02	ÁREA NO PAGA	44.65	ÁREA NO PAGA
R-01	SERVICIOS ADICIONALES - CUARTO DE BASURAS PARA METRO	22.16	SERVICIOS ADICIONALES - ÁREA NO PAGA
T-08-2	CENTRO DE TRANSFORMACIÓN ENEL-CODENSA (CT)_CUARTO BAJA TENSIÓN	15.01	ÁREA TÉCNICA
T-08-3	CENTRO DE TRANSFORMACIÓN ENEL-CODENSA (CT)_CUARTO MEDIA TENSIÓN	58.76	ÁREA TÉCNICA
		167.37	
ARQ_PL_00.08_ACCESO			
T-20-G	MEDIDORES (GAS)	11.20	ÁREA TÉCNICA
		11.20	
ARQ_PL_00.09_ACCESO			
R-00-1	SERVICIOS ADICIONALES - CORREDOR OPERATIVO	42.22	SERVICIOS ADICIONALES - ÁREA NO PAGA
R-201	SERVICIOS ADICIONALES - ÁREA DE COMIDAS	110.93	SERVICIOS ADICIONALES - ÁREA NO PAGA
R-202	SERVICIOS ADICIONALES - ÁREA DE COMIDAS	71.06	SERVICIOS ADICIONALES - ÁREA NO PAGA
R-203	SERVICIOS ADICIONALES - ÁREA DE COMIDAS	70.84	SERVICIOS ADICIONALES - ÁREA NO PAGA
R-204	SERVICIOS ADICIONALES - ÁREA DE COMIDAS	74.94	SERVICIOS ADICIONALES - ÁREA NO PAGA
R-205	SERVICIOS ADICIONALES - ÁREA DE COMIDAS	64.34	SERVICIOS ADICIONALES - ÁREA NO PAGA
T-20-L-1	MEDIDORES (LUZ)	7.84	ÁREA TÉCNICA
T-20-W-1	MEDIDORES (AGUA)	7.48	ÁREA TÉCNICA
T-21-2	ÁREA DE INSPECCIÓN	16.54	ÁREA TÉCNICA
T-30	SISTEMA PROTECCIÓN CONTRA INCENDIO ENEL	7.70	ÁREA TÉCNICA
		473.88	

TABLA DE ÁREAS ÚTILES (NIVEL ACCESO)

CÓDIGO	NOMBRE	ÁREA (m²)	DEPARTAMENTO
EDIFICIO DESCENDENTE 02			
ARQ_PL_00.03_ACCESO			
T-20-G	MEDIDORES (GAS)	4.77	ÁREA TÉCNICA
		4.77	
ARQ_PL_00.04_ACCESO			
T-08-2	CENTRO DE TRANSFORMACIÓN ENEL-CODENSA (CT)_CUARTO BAJA TENSIÓN	15.39	ÁREA TÉCNICA
T-08-3	CENTRO DE TRANSFORMACIÓN ENEL-CODENSA (CT)_CUARTO MEDIA TENSIÓN	26.91	ÁREA TÉCNICA
T-20-L	MEDIDORES (LUZ)	5.79	ÁREA TÉCNICA
T-20-W-1	MEDIDORES (AGUA)	9.68	ÁREA TÉCNICA
T-21-2	ÁREA DE INSPECCIÓN	10.40	ÁREA TÉCNICA
T-30	SISTEMA PROTECCIÓN CONTRA INCENDIO ENEL	5.80	ÁREA TÉCNICA
		73.97	
ARQ_PL_00.06_ACCESO			
R-203	SERVICIOS ADICIONALES - ÁREA DE COMIDAS	19.31	SERVICIOS ADICIONALES - ÁREA NO PAGA
R-204	SERVICIOS ADICIONALES - ÁREA DE COMIDAS	14.64	SERVICIOS ADICIONALES - ÁREA NO PAGA
		33.94	
ARQ_PL_00.07_ACCESO			
R-202	SERVICIOS ADICIONALES - ÁREA DE COMIDAS	34.86	SERVICIOS ADICIONALES - ÁREA NO PAGA
		34.86	
ARQ_PL_00.09_ACCESO			
R-201	SERVICIOS ADICIONALES - ÁREA DE COMIDAS	25.89	SERVICIOS ADICIONALES - ÁREA NO PAGA
		25.89	
ARQ_PL_00.10_ACCESO			
NPA-01	ÁREA NO PAGA	172.33	ÁREA NO PAGA
O-02	BAÑOS PÚBLICOS DE HOMBRES	11.56	SERVICIO PÚBLICO
O-03	BAÑOS PÚBLICOS DE MUJERES	15.69	SERVICIO PÚBLICO
O-04	CONTROL DE ACCESO BAÑOS PÚBLICOS	19.72	SERVICIO PÚBLICO
O-24	CUARTO DE LIMPIEZA DE BAÑOS PÚBLICOS	3.28	SERVICIO PÚBLICO
R-00-1	SERVICIOS ADICIONALES - CORREDOR OPERATIVO	28.36	SERVICIOS ADICIONALES - ÁREA NO PAGA
R-01	SERVICIOS ADICIONALES - CUARTO DE BASURAS PARA METRO	7.71	SERVICIOS ADICIONALES - ÁREA NO PAGA
R-06	SERVICIOS ADICIONALES - BAÑOS EMPLEADOS MUJERES	5.33	SERVICIOS ADICIONALES - ÁREA NO PAGA
R-07	SERVICIOS ADICIONALES - VESTIDORES EMPLEADOS MUJERES	3.76	SERVICIOS ADICIONALES - ÁREA NO PAGA
R-08	SERVICIOS ADICIONALES - BAÑOS EMPLEADOS HOMBRES	4.43	SERVICIOS ADICIONALES - ÁREA NO PAGA
R-09	SERVICIOS ADICIONALES - VESTIDORES EMPLEADOS HOMBRES	5.56	SERVICIOS ADICIONALES - ÁREA NO PAGA
R-10	SERVICIOS ADICIONALES - SALA DE EMPLEADOS	12.41	SERVICIOS ADICIONALES - ÁREA NO PAGA
T-03-1	LOCAL SECUNDARIO DE TELECOMUNICACIONES	25.60	ÁREA TÉCNICA
T-21-1	ÁREA DE INSPECCIÓN	15.38	ÁREA TÉCNICA
		331.14	
ARQ_PL_00.11_ACCESO			
R-101	SERVICIOS ADICIONALES - ÁREA DE SERVICIO	18.46	SERVICIOS ADICIONALES - ÁREA NO PAGA
		18.46	
TOTAL NIVEL ACCESO		4826.58	

TABLA DE ÁREAS ÚTILES POR DEPARTAMENTO (NIVEL ACCESO)

DEPARTAMENTO	ÁREA (m²)
EDIFICIO ASCENDENTE	
ARQ_PL_00.11_ACCESO	
SERVICIOS ADICIONALES - ÁREA NO PAGA	239.88
ÁREA NO PAGA	333.26
ÁREA TÉCNICA	36.05
ARQ_PL_00.12_ACCESO	
SERVICIOS ADICIONALES - ÁREA NO PAGA	271.30
ARQ_PL_00.13_ACCESO	
SERVICIOS ADICIONALES - ÁREA NO PAGA	259.06
ARQ_PL_00.14_ACCESO	
SERVICIOS ADICIONALES - ÁREA NO PAGA	97.82
ARQ_PL_00.15_ACCESO	
SERVICIOS ADICIONALES - ÁREA NO PAGA	371.67
ARQ_PL_00.16_ACCESO	
SERVICIOS ADICIONALES - ÁREA NO PAGA	126.26
ARQ_PL_00.17_ACCESO	
ÁREA DE TAQUILLAS BRT	35.34
ÁREA NO PAGA	123.65
ARQ_PL_00.18_ACCESO	
SERVICIOS ADICIONALES - ÁREA NO PAGA	9.26
ÁREA TÉCNICA	130.09
ARQ_PL_01_ACCESO	
SERVICIOS ADICIONALES - ÁREA NO PAGA	201.21
ÁREA CULTURAL	4.00
ÁREA NO PAGA	288.48
ÁREA OPERATIVA	31.49
ÁREA TÉCNICA	4.72

TABLA DE ÁREAS ÚTILES POR DEPARTAMENTO (NIVEL ACCESO)

DEPARTAMENTO	ÁREA (m²)
EDIFICIO DESCENDENTE 01	
ARQ_PL_00.01_ACCESO	
ÁREA CULTURAL	4.00
ÁREA NO PAGA	313.98
ÁREA TÉCNICA	75.32
ARQ_PL_00.02_ACCESO	
SERVICIOS ADICIONALES - ÁREA NO PAGA	201.55
ARQ_PL_00.04_ACCESO	
SERVICIOS ADICIONALES - ÁREA NO PAGA	487.43
ÁREA TÉCNICA	5.26
ARQ_PL_00.07_ACCESO	
SERVICIOS ADICIONALES - ÁREA NO PAGA	22.16
ÁREA CULTURAL	26.79
ÁREA NO PAGA	44.65
ÁREA TÉCNICA	73.77
ARQ_PL_00.08_ACCESO	
ÁREA TÉCNICA	11.20
ARQ_PL_00.09_ACCESO	
SERVICIOS ADICIONALES - ÁREA NO PAGA	434.32
ÁREA TÉCNICA	39.56
EDIFICIO DESCENDENTE 02	
ARQ_PL_00.03_ACCESO	
ÁREA TÉCNICA	4.77
ARQ_PL_00.04_ACCESO	
ÁREA TÉCNICA	73.97
ARQ_PL_00.06_ACCESO	
SERVICIOS ADICIONALES - ÁREA NO PAGA	33.94
ARQ_PL_00.07_ACCESO	
SERVICIOS ADICIONALES - ÁREA NO PAGA	34.86
ARQ_PL_00.09_ACCESO	
SERVICIOS ADICIONALES - ÁREA NO PAGA	25.89
ARQ_PL_00.10_ACCESO	
SERVICIO PÚBLICO	50.25
SERVICIOS ADICIONALES - ÁREA NO PAGA	67.57
ÁREA NO PAGA	172.33
ÁREA TÉCNICA	40.98
ARQ_PL_00.11_ACCESO	
SERVICIOS ADICIONALES - ÁREA NO PAGA	18.46
TOTAL NIVEL ACCESO	4826.58

TABLA GENERAL DE NIVELES

NOMBRE	NIVEL	ELEVACIÓN (m)
ARQ_PL_00.01_ACCESO	ACCESO	-3.84
ARQ_PL_00.02_ACCESO	ACCESO	-3.69
ARQ_PL_00.03_ACCESO	ACCESO	-3.39
ARQ_PL_00.04_ACCESO	ACCESO	-3.29
ARQ_PL_00.05_ACCESO	ACCESO	-3.19
ARQ_PL_00.06_ACCESO	ACCESO	-3.04
ARQ_PL_00.07_ACCESO	ACCESO	-2.89
ARQ_PL_00.08_ACCESO	ACCESO	-2.69
ARQ_PL_00.09_ACCESO	ACCESO	-2.54
ARQ_PL_00.10_ACCESO	ACCESO	-2.09
ARQ_PL_00.11_ACCESO	ACCESO	-1.84
ARQ_PL_00.12_ACCESO	ACCESO	-1.59
ARQ_PL_00.13_ACCESO	ACCESO	-1.29
ARQ_PL_00.14_ACCESO	ACCESO	-1.09
ARQ_PL_00.15_ACCESO	ACCESO	-0.99
ARQ_PL_00.16_ACCESO	ACCESO	-0.79
ARQ_PL_00.17_ACCESO	ACCESO	-0.69
ARQ_PL_00.18_ACCESO	ACCESO	-0.49
ARQ_PL_00.19_ACCESO	ACCESO	-0.34
ARQ_PL_00_SÓTANO	SÓTANO	-7.94
ARQ_PL_01_ACCESO	ACCESO*	2574.39 M.S.N.M./ 0.00
ARQ_PL_02.2_TOR	TOPE DE RIEL	14.24
ARQ_PL_02_INTERMEDIO	INTERMEDIO	6.64
ARQ_PL_03_PLATAFORMA	PLATAFORMA	15.38
ARQ_PL_04_CUB_EDIFICACIONES	CUBIERTA EDIFICACIONES	21.98
ARQ_PL_05_CUB_NVC	CUBIERTA NAVE CENTRAL	24.64

LOCALIZACIÓN

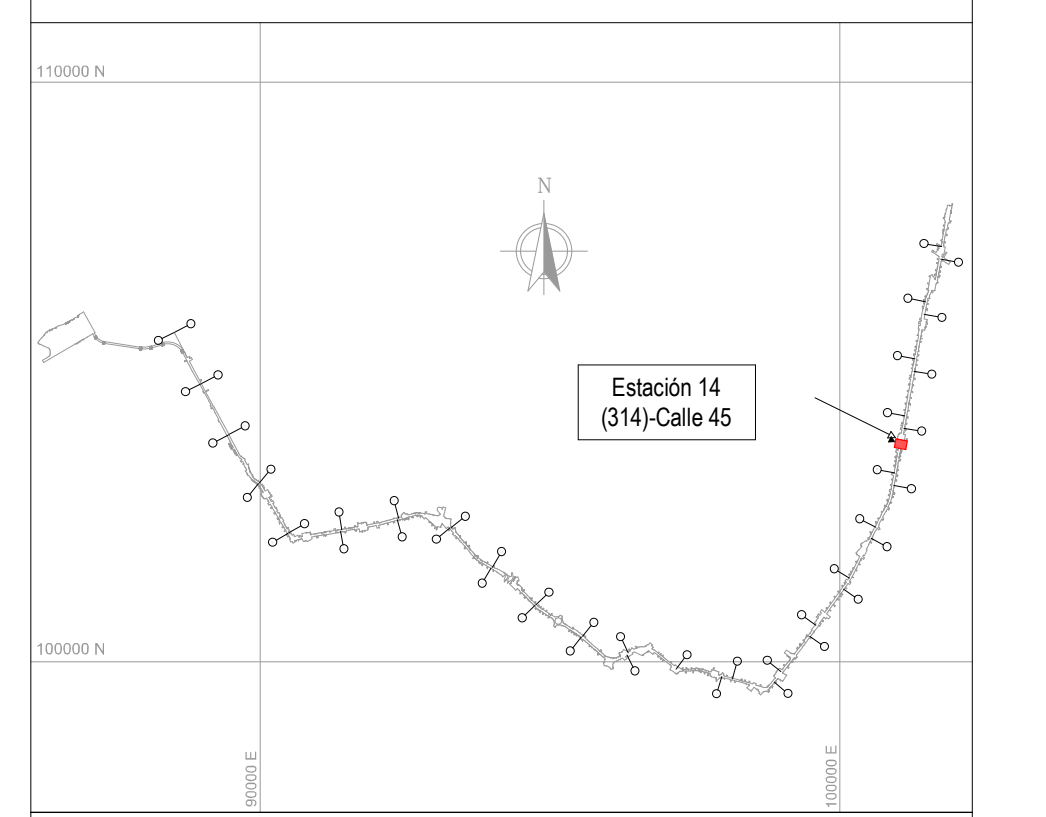

NOTAS

01 TODAS LAS DIMENSIONES ESTÁN CONFIGURADAS EN METROS A MENOS QUE SE INDIQUE UNA UNIDAD DE MEDIDA DIFERENTE.

02 TODAS LAS MEDIDAS, UBICACIÓN Y NIVELES DEBEN VERIFICARSE EN EL LUGAR DE CONSTRUCCIÓN.

03 EL NIVEL DE ACCESO AL EDIFICIO PL 01 CORRESPONDE AL +0,00 DE LA ESTACIÓN Y REFERENCIA AL NIVEL 2574.39 M.S.N.M.

04 LOS NOMBRES ESPECÍFICOS DE LAS ÁREAS PUEDEN SER CONSULTADAS EN EL PLANO NO. 3 Ó EN LAS VISTAS EN PLANTA.

05 LOS COLORES QUE SE MUESTRAN EN LOS PLANOS COMO PROYECCIÓN DE ELEMENTOS ARQUITECTÓNICOS COMO CUBIERTAS FACHADAS MUROS ETC. NO REPRESENTAN LA MATERIALIDAD Y REALIDAD DE ACABADOS DEL PROYECTO, SOLO SON INDICATIVOS PARA REALIZAR UNA CORRECTA LECTURA DE LA PLANIMETRÍA.

06 LAS ESCALERAS ELÉCTRICAS INDICAN SU SENTIDO CON LA SIGUIENTE NOMENCLATURA: "SUBE" Y "BAJA".

07 SE DEBEN REVISAR LOS NIVELES ESTRUCTURALES PARA NIVEL DE ACCESO PL_01 Y SUBNIVELES, PL_02 (INTERMEDIO), PL_03 (PLATAFORMA) CON LA PLANIMETRÍA DE PLACAS ESTRUCTURALES EN LOS ENTREGABLES L1T1-1300-414-CON-ED-EST-PL-0038, 39, 42, 43, 126, 86, RESPECTIVAMENTE. EL NIVEL ESTRUCTURAL (NE) REFERENCIA LOS ESPACIOS DONDE SE DEBE ACONDICIONAR EL ACABADO DE PISO SEGÚN CORRESPONDA, CON LOS NIVELES DE PISO TERMINADO (NPT). LOS NIVELES PROYECTADOS DE EMPATE (NPE) EN LAS ÁREAS DE SERVICIOS ADICIONALES, REFERENCIAN LA ADECUACIÓN DE LOS DESNIVELES EN ESTAS ÁREAS; QUEDA COMO RESPONSABILIDAD DEL LOCATARIO DEFINIR Y ACONDICIONAR ESTE ACABADO DE PISO (NPE) EN LÍNEA CON EL NIVEL (NPT) DE ESPACIOS COLINDANTES. EL NIVEL ESTRUCTURAL (NE) SE ENCUENTRA A (- 0.10M) POR DEBAJO DE LOS NIVELES DE PISO TERMINADO (NPT) Y LOS NIVELES PROYECTADOS DE EMPATE (NPE) MARCADOS EN LA PLANIMETRÍA.

08 RESPECTO A LAS ÁREAS CONSTRUIDAS Y DE ACUERDO CON LA COMUNICACIÓN EXTS22-0002544 DE EMB, SE IDENTIFICA QUE EL CONCESIONARIO SE ENCUENTRA BUSCANDO ESTRATEGIAS PARA MEJORAR EL DISEÑO CON EL PROGRAMA ARQUITECTÓNICO, UNA DE ESTAS ESTRATEGIAS ES MEJORAR EL FUNCIONAMIENTO DEL DISEÑO URBANO Y BRINDAR UNA SOLUCIÓN INTEGRAL RESPECTO A LOS INMUEBLES DE INTERÉS CULTURAL. DE ACUERDO CON LO ANTERIOR, PARA LA EMB, ESTAS ACTIVIDADES OBEDECEN AL PROCESO NATURAL DE LOS ESTUDIOS Y DISEÑOS DEFINITIVOS QUE DEBE DESARROLLAR METRO LÍNEA 1.

CONVENCIONES

- LÍMITE DE INTERVENCIÓN
- HUELLA APÉNDICE TÉCNICO
- HUELLA DE EDIFICIOS EXISTENTES
- MURO DIVISORIO
- PROYECCIÓN NIVEL SUPERIOR

🟩	SERVICIOS ADICIONALES - ÁREA NO PAGA	🟨	ÁREA NO PAGA
🟩	SERVICIOS ADICIONALES - ÁREA PAGA	🟧	ÁREA PAGA
🟩	SERVICIO PÚBLICO	🟦	ÁREA PÚBLICA
🟦	ZONA DE REFUGIO	⬜	ÁREA TÉCNICA
🟥	ÁREA CULTURAL	🟦	ÁREA OPERATIVA
🟪	ÁREA DE TAQUILLAS BRT		

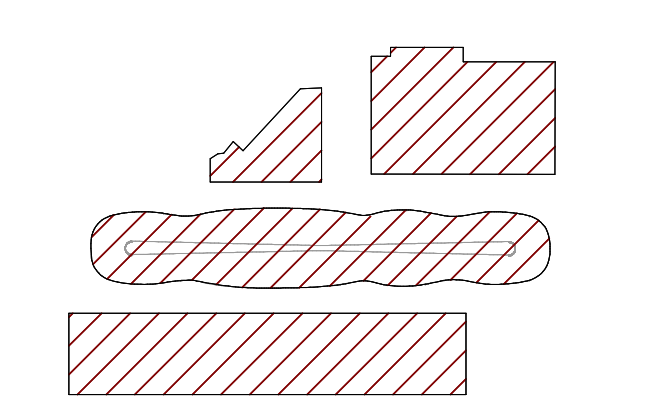

PLANO CLAVE ESTACIÓN 14

No.	PLANOS DE REFERENCIA	REV.
No.	**MODELO BIM DE REFERENCIA**	**REV.**
1	L1T1-1100-214-CON-ED-EST-MO-0001.rvt	V00
2	L1T1-1100-215-CON-ED-EST-MO-0001.rvt	V00
3	L1T1-1100-314-CON-ED-EST-MO-0001.rvt	V00
4	L1T1-1150-214-CON-ED-EST-MO-0001.rvt	V00
5	L1T1-1150-215-CON-ED-EST-MO-0001.rvt	V00
6	L1T1-1150-314-CON-ED-EST-MO-0001.rvt	V00
7	L1T1-1200-314-CON-ED-EST-MO-0001.rvt	V00
8	L1T1-1300-414-CON-ED-EST-MO-0001.rvt	V01
9	L1T1-1300-414-CON-ED-EST-MO-0002.rvt	V01
10	L1T1-1300-414-CON-ED-EST-MO-0003.rvt	V01
11	L1T1-1310-414-CON-ED-EST-MO-0001.rvt	V00
12	L1T1-1410-314-CON-ED-MEC-MO-0001.rvt	V00
13	L1T1-1420-314-CON-ED-MEC-MO-0002.rvt	V00
14	L1T1-2320-588-CON-ED-EST-MO-0001.rvt	V00
15	L1T1-2320-588-CON-ED-ARQ-MO-0001.rvt	V00
16	L1T1-5160-314-CON-ED-EST-MO-0001.rvt	V00
17	L1T1-5160-314-CON-ED-ARQ-MO-0001.rvt	V00
18	L1T1-5300-314-CON-ED-MEC-MO-0001.rvt	V00
19	L1T1-5600-314-CON-ED-INS-MO-0001.rvt	V00
No.	**PAQUETE DE TRABAJO DE REFERENCIA**	**REV.**
1	XREF-URBANISM_CONTEXT_ST14.rvt	
2	XREF-SECONDARY-STRUCTURE-ST14.rvt	

0 2 10m
1:200

METRO BOGOTÁ
GCS Consorcio Consultores PMO Bogotá
CONSORCIO SUPERVISOR PLMB
wsp

DISEÑÓ: Santiago A. David G.
SANTIAGO ANDRES DAVID GUZMÁN
Mat.: A413202011-1010176190

APROBÓ:
MAURICIO MEJÍA RESTREPO
Mat.: 25202-72411 CND

REVISÓ:
FREDDY BAUTISTA R.
Mat.:25202-092831 CND

DIBUJÓ:
EQUIPO WSP

REVISIÓN No.	FECHA	DESCRIPCIÓN	REVISÓ	APROBÓ	APROBACIÓN CLIENTE
V01	12/11/2025	REVISIÓN NO OBJETADA - EMITIDO PARA CONSTRUCCIÓN	F.B.R	M.M.R	
VB1	20/03/2025	EMITIDO PARA REVISIÓN Y COMENTARIOS DEL CLIENTE E INTERVENTORÍA	F.B.R	E.O.M	
V00	13/02/2025	REVISIÓN NO OBJETADA - EMITIDO PARA CONSTRUCCIÓN	F.B.R	E.O.M	
VFF	18/10/2024	EMITIDO PARA REVISIÓN Y COMENTARIOS DEL CLIENTE E INTERVENTORÍA - INCLUYE COMENTARIOS /(AJUSTES V3)	F.B.R	E.O.M	
VEE	17/07/2024	EMITIDO PARA REVISIÓN Y COMENTARIOS DEL CLIENTE E INTERVENTORÍA - INCLUYE COMENTARIOS /(AJUSTES V2)	F.B.R	E.O.M	
VDD	18/12/2022	EMITIDO PARA REVISIÓN Y COMENTARIOS DEL CLIENTE E INTERVENTORÍA - INCLUYE COMENTARIOS /(AJUSTES)	J.E.M	M.B.M	
VCC	02/06/2022	EMITIDO PARA REVISIÓN Y COMENTARIOS DEL CLIENTE E INTERVENTORÍA - INCLUYE COMENTARIOS /(ENTREGA 90%)	J.E.M	M.B.M	
VBB	06/12/2021	EMITIDO PARA REVISIÓN Y COMENTARIOS DEL CLIENTE E INTERVENTORÍA	J.E.M	M.B.M	
VA0	30/06/2021	EMITIDO PARA COMENTARIOS INTERNOS - EMISIÓN PRELIMINAR PARA COMENTARIOS	J.E.M	M.B.M	

METRO LÍNEA 1

METRO LÍNEA 1
CONTRATO DE CONCESIÓN No. 163 DE 2019

PROYECTO PRIMERA LÍNEA DEL METRO DE BOGOTÁ - TRAMO 1

DIRECTOR DE INTERVENTORÍA:
JAVIER DESCARGA N.
Mat.:25202-68697 CND

ESPECIALISTA INTERVENTORÍA:
MARIA AUXILIADORA SANCHEZ HERMOSIN
INT: PAH138382-RES.NO.34 DE 2021

FECHA: NOVIEMBRE 2025

INFRAESTRUCTURA VIAL
ARQUITECTURA
ESTACIÓN METRO 14 - (CALLE 45)
GENERAL
VISTA EN PLANTA Y 3D - NIVEL ACCESO

PLANCHA No: L1T1-0000-314-CON-ED-ARQ-PL-0001_05_V01
ARCHIVO: L1T1-0000-314-CON-ED-ARQ-MO-0001_V01.rvt
ESCALA: INDICADA
FECHA: JUNIO 2021
REVISIÓN No. V01
PLANO No. 05 DE 96