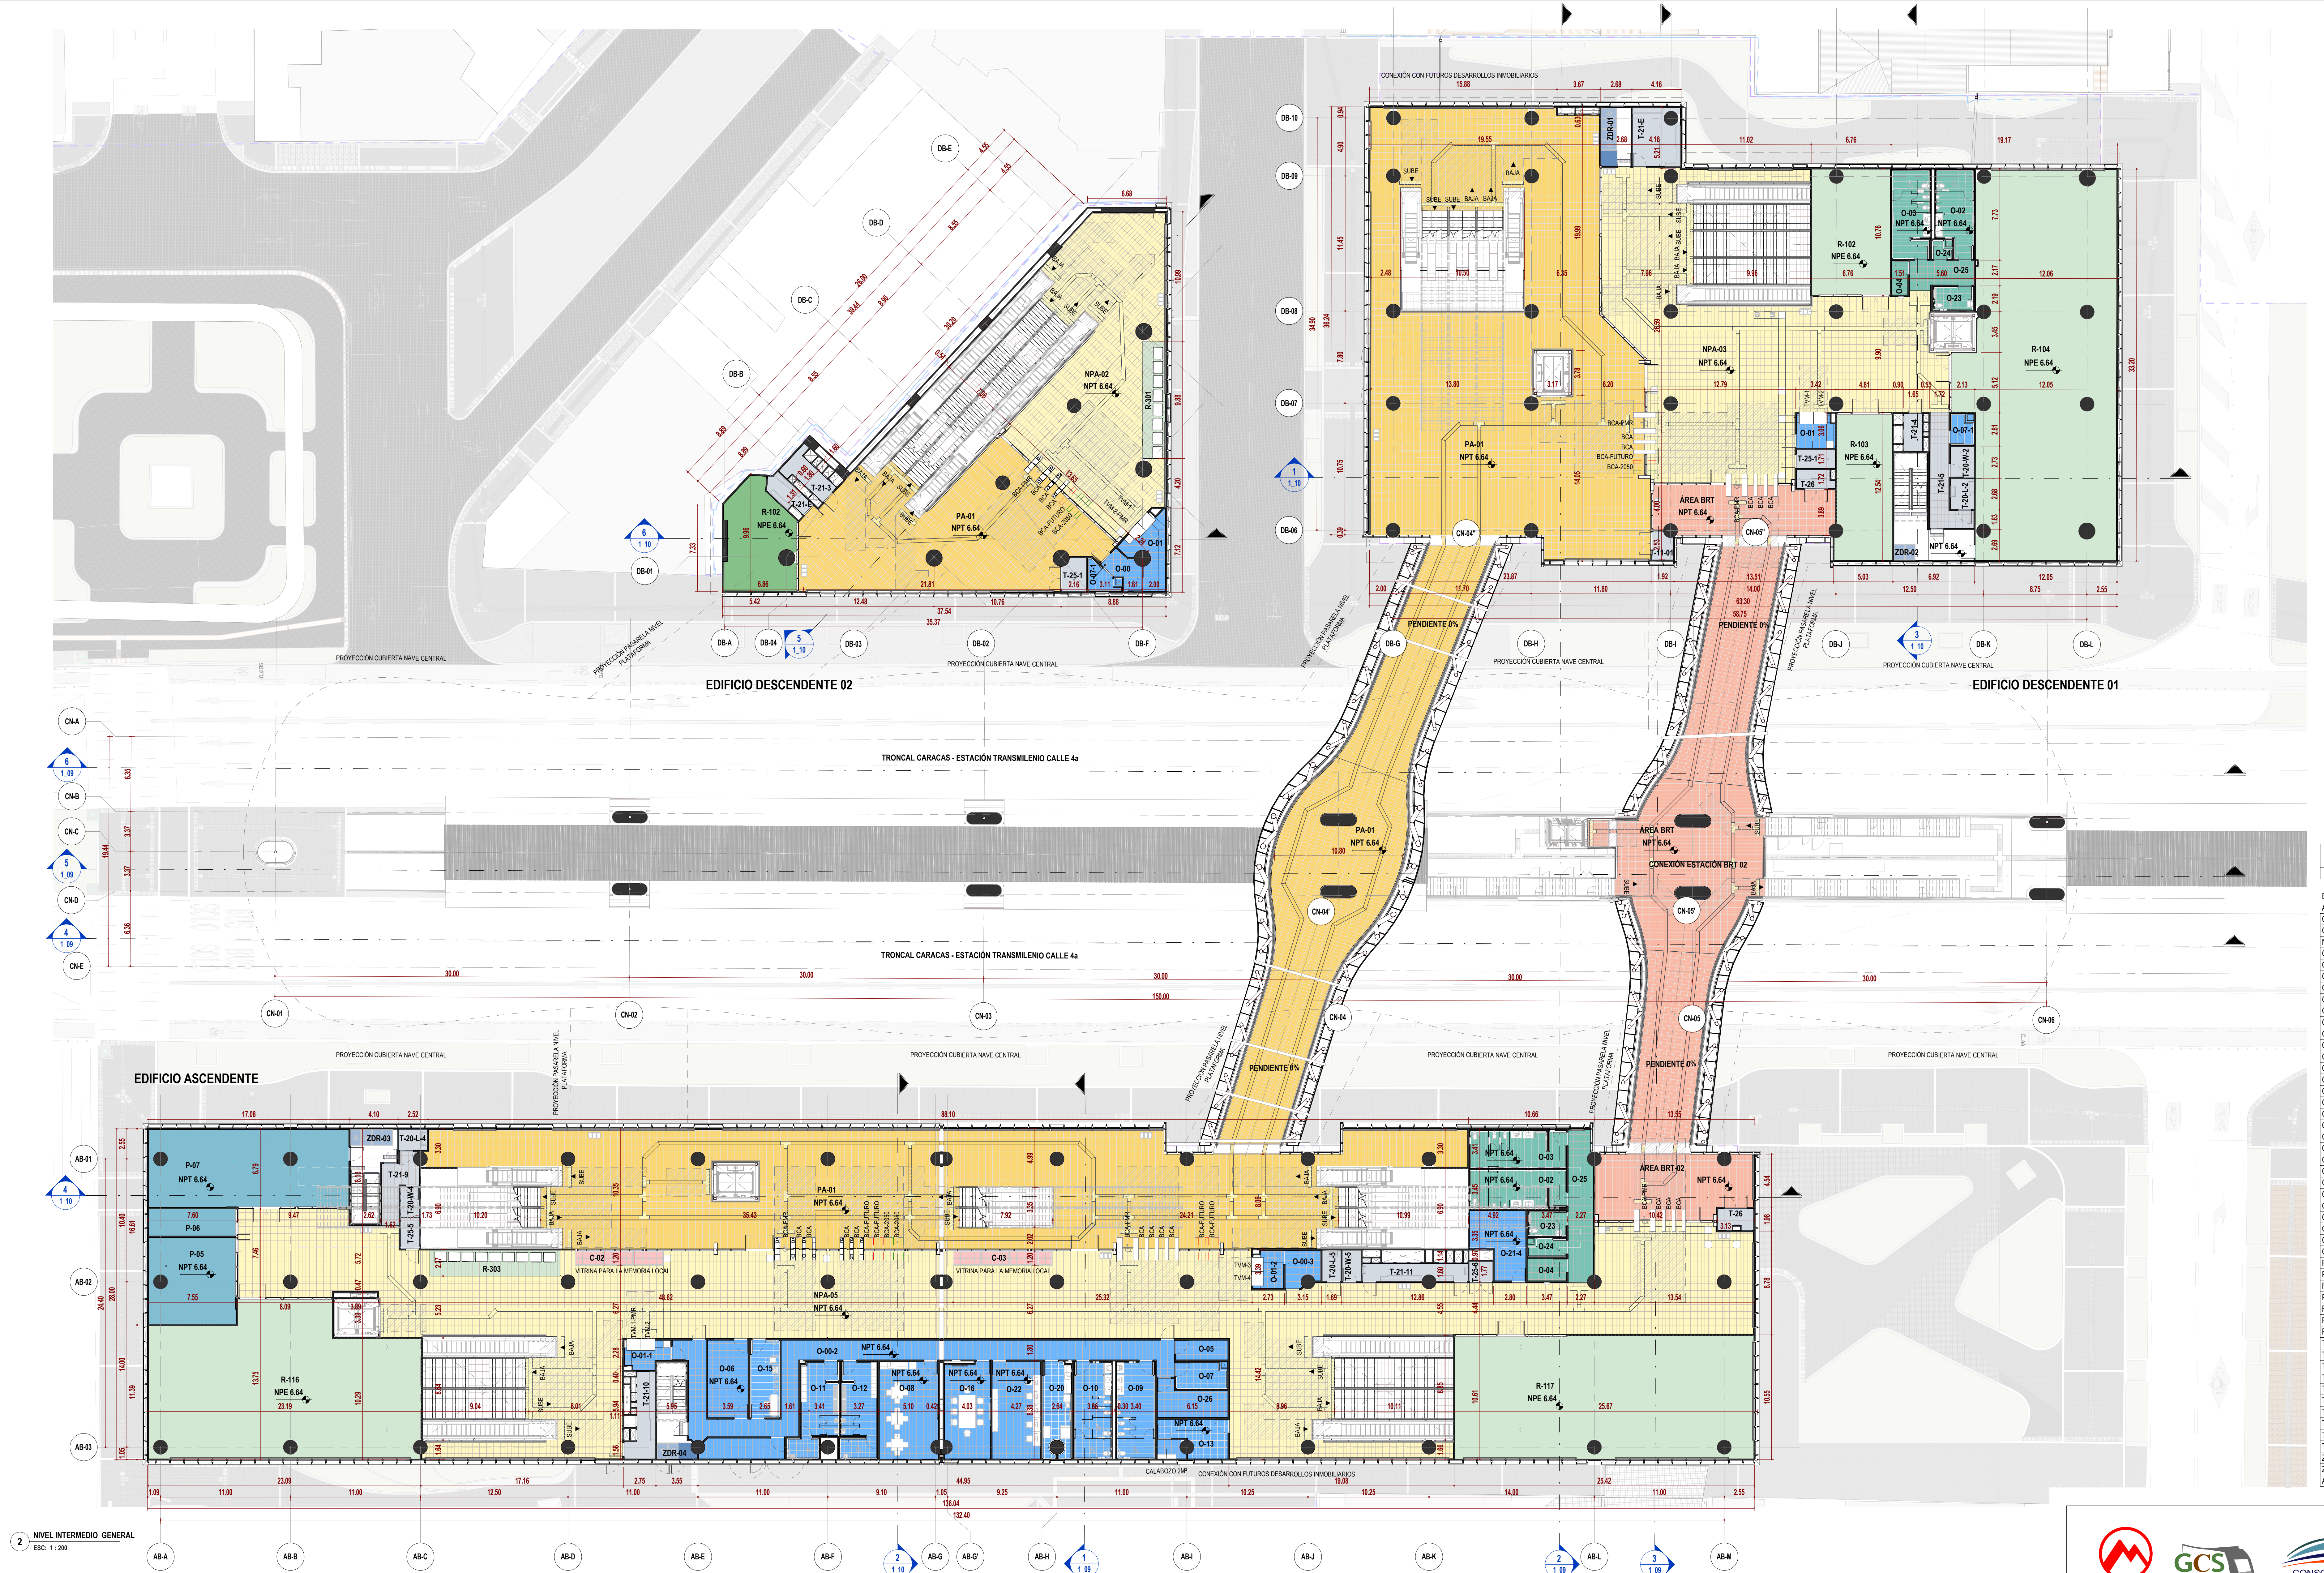

2 NIVEL INTERMEDIO_GENERAL
ESC: 1:200

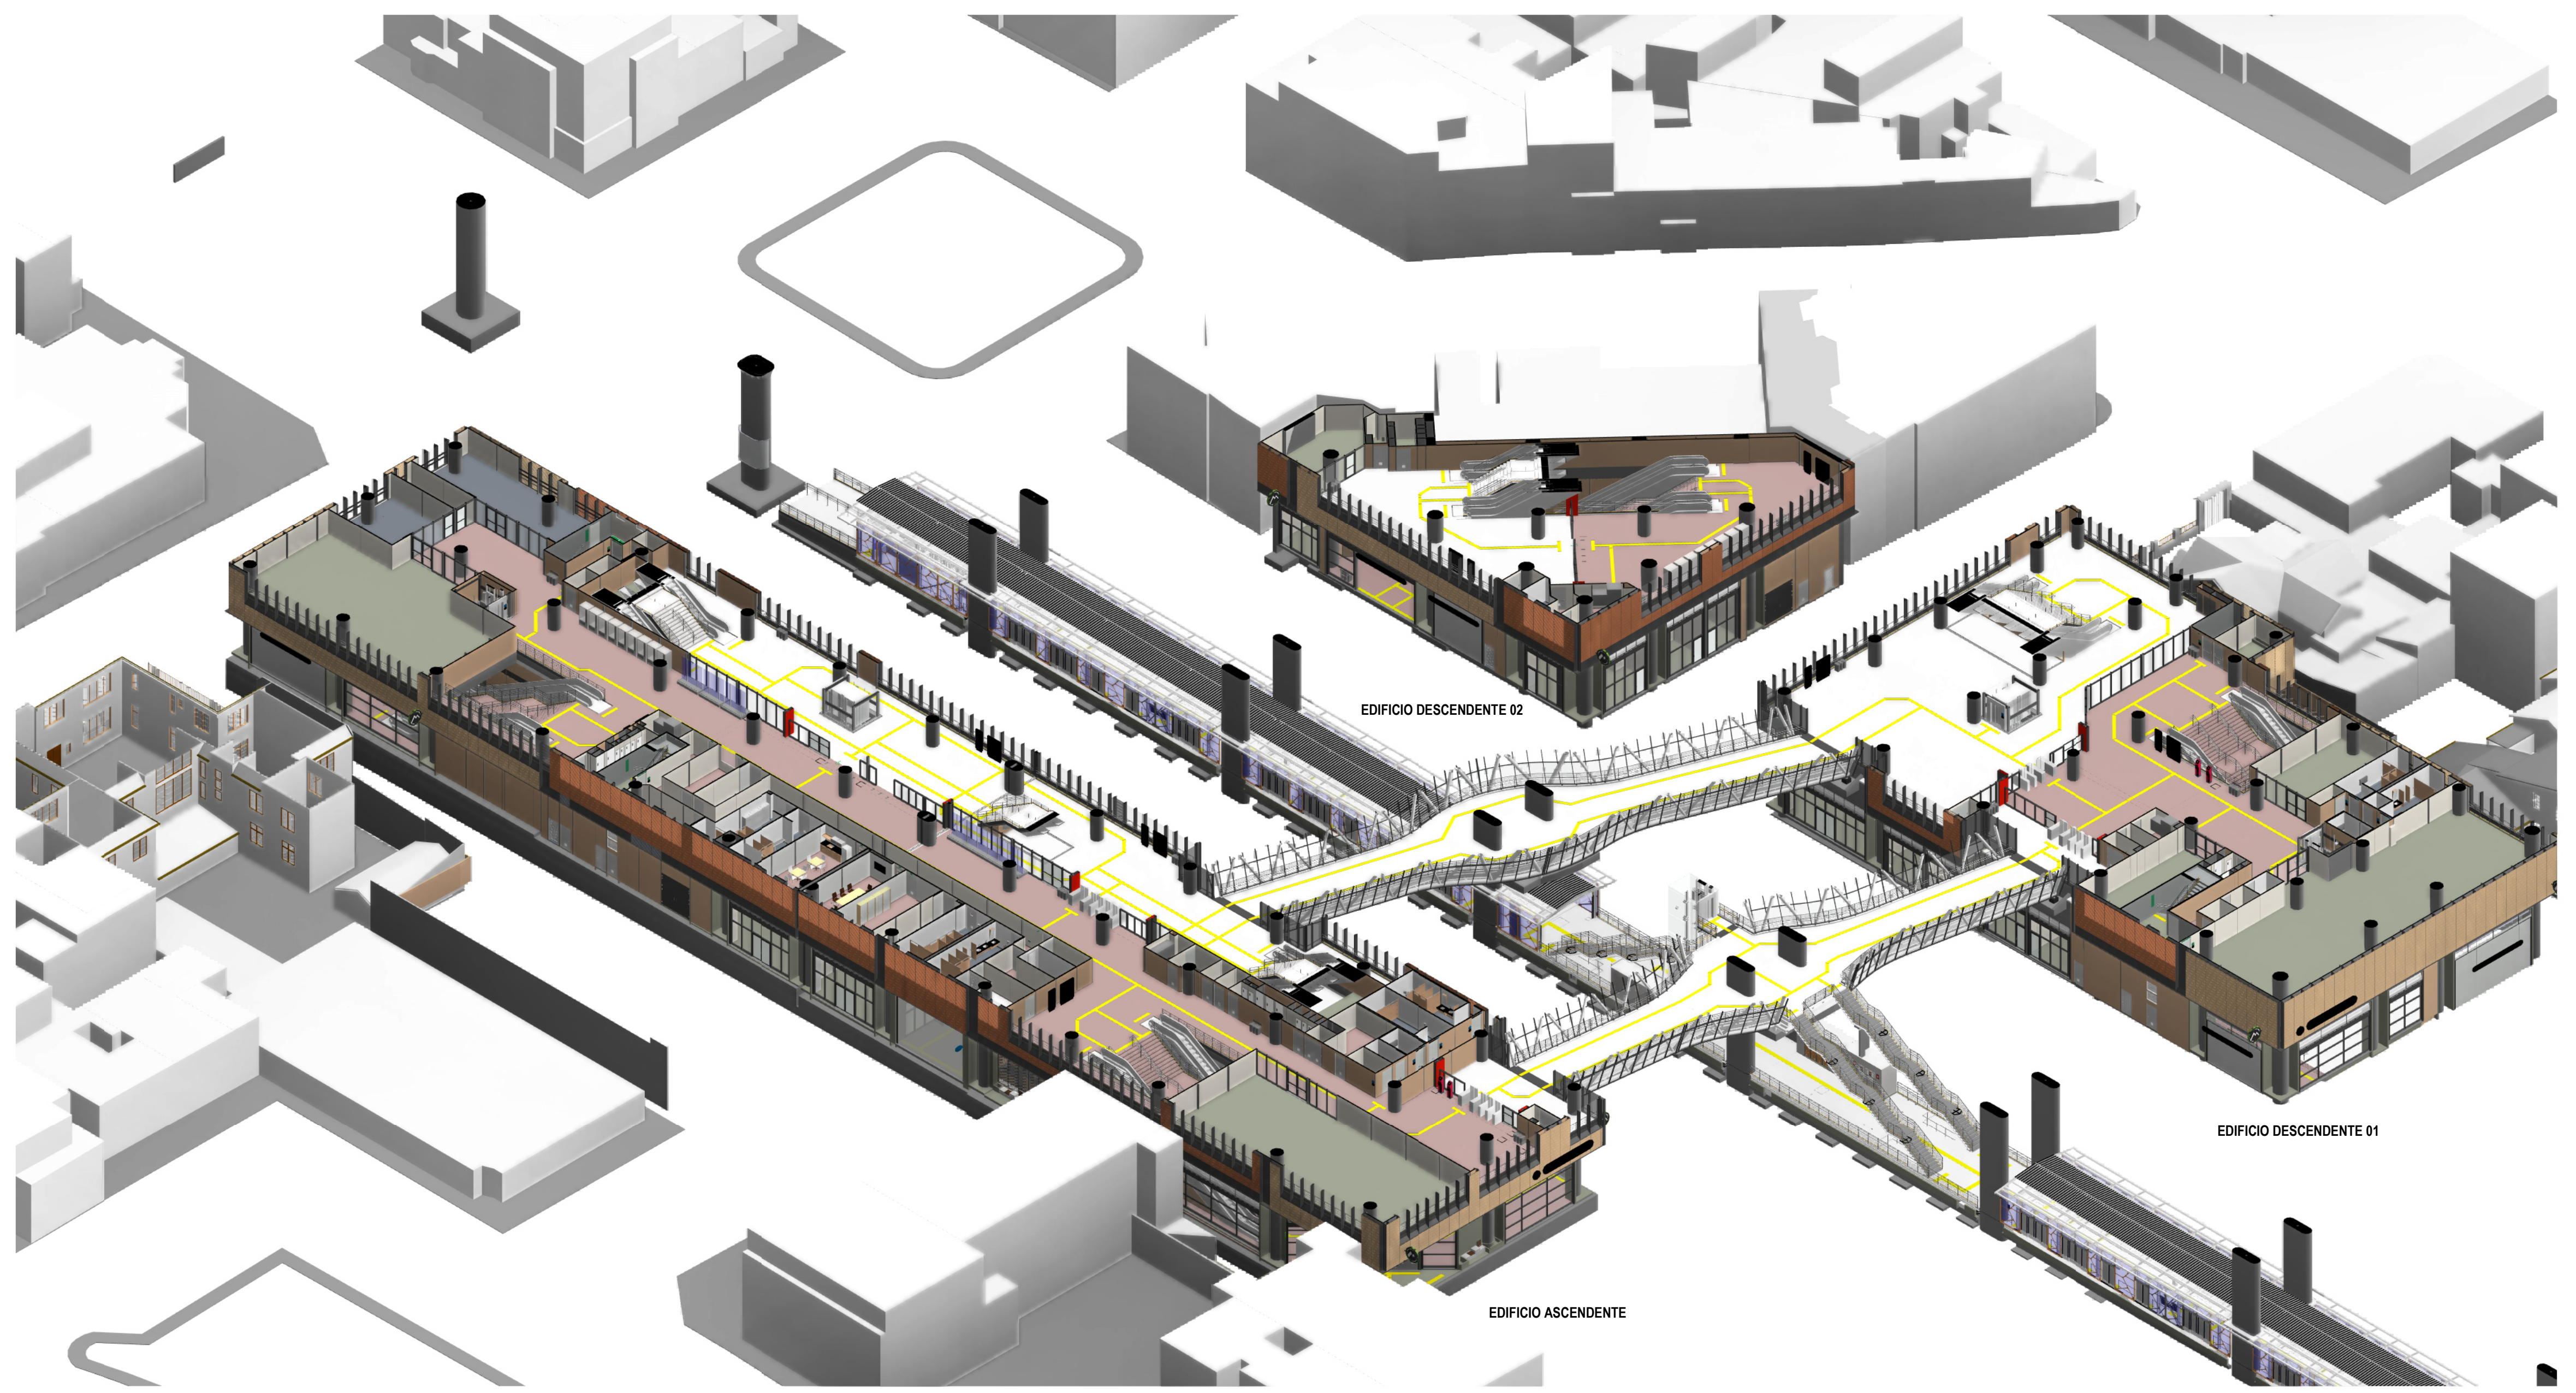

1 3D_GENERAL
ESC: N/A

TABLA DE ÁREAS ÚTILES (NIVEL INTERMEDIO)

EDIFICIO ASCENDENTE
ARQ_PL_02_INTERMEDIO

CÓDIGO	NOMBRE	ÁREA (m²)	DEPARTAMENTO
C-02	ÁREAS DE USO CULTURAL	10.02	ÁREA CULTURAL
C-03	ÁREAS DE USO CULTURAL	10.08	ÁREA CULTURAL
NPA-05	ÁREA NO PAGA	1000.38	ÁREA NO PAGA
O-00-2	CIRCULACIÓN ÁREAS OPERATIVAS	92.30	ÁREA OPERATIVA
O-00-3	CIRCULACIÓN ÁREAS OPERATIVAS	8.31	ÁREA OPERATIVA
O-01-1	VENTA AUTOMÁTICA DE BOLETOS	8.67	ÁREA OPERATIVA
O-01-2	VENTA AUTOMÁTICA DE BOLETOS	8.18	ÁREA OPERATIVA
O-02	BAÑOS PÚBLICOS DE HOMBRES	25.50	SERVICIO PÚBLICO
O-03	BAÑOS PÚBLICOS DE MUJERES	25.67	SERVICIO PÚBLICO
O-04	CONTROL DE ACCESO BAÑOS PÚBLICOS	6.42	SERVICIO PÚBLICO
O-05	LOCAL DE INFORMACIÓN	7.39	ÁREA OPERATIVA
O-06	OFICINA DEL SUPERVISOR DE LA ESTACIÓN	22.64	ÁREA OPERATIVA
O-07	CUARTO DE LIMPIEZA	10.26	ÁREA OPERATIVA
O-08	SALA DE DESCANSO PARA EMPLEADOS	40.26	ÁREA OPERATIVA
O-09	BAÑOS EMPLEADOS HOMBRES	26.60	ÁREA OPERATIVA
O-10	BAÑOS EMPLEADOS MUJERES	26.25	ÁREA OPERATIVA
O-11	VESTIDORES EMPLEADOS HOMBRES	25.17	ÁREA OPERATIVA
O-12	VESTIDORES EMPLEADOS MUJERES	25.07	ÁREA OPERATIVA
O-13	LOCAL DE POLICÍA	15.12	ÁREA OPERATIVA
O-14	CALABOZO	3.46	ÁREA OPERATIVA
O-15	LOCAL PRIMEROS AUXILIOS	16.59	ÁREA OPERATIVA
O-16	SALA DE REUNIONES	30.66	ÁREA OPERATIVA
O-20	SALA DE LACTANCIA	19.06	ÁREA OPERATIVA
O-21-3	ALMACENAMIENTO DE LA ESTACIÓN	12.18	ÁREA OPERATIVA
O-21-4	ALMACENAMIENTO DE LA ESTACIÓN	22.84	ÁREA OPERATIVA
O-22	OFICINA DE MANTENIMIENTO	33.61	ÁREA OPERATIVA
O-23	BAÑO PÚBLICO - FAMILIAR	6.88	SERVICIO PÚBLICO
O-24	CUARTO DE LIMPIEZA DE BAÑOS PÚBLICOS	5.13	SERVICIO PÚBLICO
O-25	BAÑO PÚBLICO - CORREDOR OPERACIONAL	26.53	SERVICIO PÚBLICO
O-26	ALMACENAMIENTO DE BASURAS METRO	15.05	ÁREA OPERATIVA
P-05	BIBLIOMETRO	52.65	ÁREA PÚBLICA
P-06	ESPACIO IPES (INSTITUTO PARA LA ECONOMÍA SOCIAL)	16.60	ÁREA PÚBLICA
P-07	SALÓN MÚLTIPLE EMB	108.76	ÁREA PÚBLICA
PA-01	ÁREA PAGA	647.99	ÁREA PAGA
R-116	SERVICIOS ADICIONALES - ÁREA DE SERVICIO	264.46	SERVICIOS ADICIONALES - ÁREA NO PAGA
R-117	SERVICIOS ADICIONALES - ÁREA DE SERVICIO	260.96	SERVICIOS ADICIONALES - ÁREA NO PAGA
R-303	SERVICIOS ADICIONALES - MÁQUINAS EXPENDEDORAS/CAJEROS AUTOMÁTICOS	24.37	SERVICIOS ADICIONALES - ÁREA NO PAGA
T-20-L-4	MEDIDORES (LUZ)	4.22	ÁREA TÉCNICA
T-20-L-5	MEDIDORES (LUZ)	4.11	ÁREA TÉCNICA
T-20-W-4	MEDIDORES (AGUA)	4.07	ÁREA TÉCNICA
T-20-W-5	MEDIDORES (AGUA)	4.16	ÁREA TÉCNICA
T-21-9	ÁREA DE INSPECCIÓN	12.24	ÁREA TÉCNICA
T-21-10	ÁREA DE INSPECCIÓN	12.77	ÁREA TÉCNICA
T-21-11	ÁREA DE INSPECCIÓN	12.67	ÁREA TÉCNICA
T-25-5	NODO DE ACCESO DE TELECOMUNICACIONES	4.10	ÁREA TÉCNICA
T-25-6	NODO DE ACCESO DE TELECOMUNICACIONES	3.29	ÁREA TÉCNICA
T-26	NODO DE ACCESO DE TELECOMUNICACIONES TMSA	5.14	ÁREA TÉCNICA
ZDR-03	ZONA DE REFUGIO (PMR)	4.86	ZONA DE REFUGIO
ZDR-04	ZONA DE REFUGIO (PMR)	4.16	ZONA DE REFUGIO
ÁREA BRT-02	ÁREA BRT	70.65	ÁREA BRT

TABLA DE ÁREAS ÚTILES (NIVEL INTERMEDIO)

EDIFICIO DESCENDENTE 01
ARQ_PL_02_INTERMEDIO

CÓDIGO	NOMBRE	ÁREA (m²)	DEPARTAMENTO
NPA-03	ÁREA NO PAGA	409.60	ÁREA NO PAGA
O-01	VENTA AUTOMÁTICA DE BOLETOS	9.26	ÁREA OPERATIVA
O-02	BAÑOS PÚBLICOS DE HOMBRES	21.85	SERVICIO PÚBLICO
O-03	BAÑOS PÚBLICOS DE MUJERES	24.18	SERVICIO PÚBLICO
O-04	CONTROL DE ACCESO BAÑOS PÚBLICOS	4.03	SERVICIO PÚBLICO
O-07-1	CUARTO DE LIMPIEZA COMPLEMENTARIO	5.20	ÁREA OPERATIVA
O-23	BAÑO PÚBLICO - FAMILIAR	6.69	SERVICIO PÚBLICO
O-24	CUARTO DE LIMPIEZA DE BAÑOS PÚBLICOS	2.76	SERVICIO PÚBLICO
O-25	BAÑO PÚBLICO - CORREDOR OPERACIONAL	12.10	SERVICIO PÚBLICO
PA-01	ÁREA PAGA	665.94	ÁREA PAGA
R-102	SERVICIOS ADICIONALES - ÁREA DE SERVICIO	69.08	SERVICIOS ADICIONALES - ÁREA NO PAGA
R-103	SERVICIOS ADICIONALES - ÁREA DE SERVICIO	57.78	SERVICIOS ADICIONALES - ÁREA NO PAGA
R-104	SERVICIOS ADICIONALES - ÁREA DE SERVICIO	392.53	SERVICIOS ADICIONALES - ÁREA NO PAGA
T-11-01	CUARTO DE VENTILACIÓN	3.92	ÁREA TÉCNICA
T-20-L-2	MEDIDORES (LUZ)	5.10	ÁREA TÉCNICA
T-20-W-2	MEDIDORES (AGUA)	5.24	ÁREA TÉCNICA
T-21-4	ÁREA DE INSPECCIÓN	4.88	ÁREA TÉCNICA
T-21-5	ÁREA DE INSPECCIÓN	18.51	ÁREA TÉCNICA
T-21-E	CUARTO ELÉCTRICO SECUNDARIO	18.82	ÁREA TÉCNICA
T-25-1	NODO DE ACCESO DE TELECOMUNICACIONES	5.27	ÁREA TÉCNICA
T-26	NODO DE ACCESO DE TELECOMUNICACIONES TMSA	4.84	ÁREA TÉCNICA
ZDR-01	ZONA DE REFUGIO (PMR)	6.68	ZONA DE REFUGIO
ZDR-02	ZONA DE REFUGIO (PMR)	2.43	ZONA DE REFUGIO
ÁREA BRT	ÁREA BRT	63.11	ÁREA BRT

EDIFICIO DESCENDENTE 02
ARQ_PL_02_INTERMEDIO

CÓDIGO	NOMBRE	ÁREA (m²)	DEPARTAMENTO
NPA-02	ÁREA NO PAGA	223.48	ÁREA NO PAGA
O-00	CIRCULACIÓN ÁREAS OPERATIVAS	6.94	ÁREA OPERATIVA
O-01	VENTA AUTOMÁTICA DE BOLETOS	15.62	ÁREA OPERATIVA
O-07-1	CUARTO DE LIMPIEZA COMPLEMENTARIO	5.35	ÁREA OPERATIVA
PA-01	ÁREA PAGA	225.39	ÁREA PAGA
R-102	SERVICIOS ADICIONALES - ÁREA DE SERVICIO	49.60	SERVICIOS ADICIONALES - ÁREA PAGA
R-301	SERVICIOS ADICIONALES - MÁQUINAS EXPENDEDORAS/CAJEROS AUTOMÁTICOS	18.49	SERVICIOS ADICIONALES - ÁREA NO PAGA
T-21-3	ÁREA DE INSPECCIÓN	8.76	ÁREA TÉCNICA
T-21-E	CUARTO ELÉCTRICO SECUNDARIO	6.56	ÁREA TÉCNICA
T-25-1	NODO DE ACCESO DE TELECOMUNICACIONES	5.45	ÁREA TÉCNICA

NAVE CENTRAL
ARQ_PL_02_INTERMEDIO

CÓDIGO	NOMBRE	ÁREA (m²)	DEPARTAMENTO
PA-01	ÁREA PAGA	320.58	ÁREA PAGA
ÁREA BRT	ÁREA BRT	328.80	ÁREA BRT
TOTAL NIVEL INTERMEDIO		6143.35	

TABLA DE ÁREAS ÚTILES POR DEPARTAMENTO (NIVEL INTERMEDIO)

EDIFICIO ASCENDENTE
ARQ_PL_02_INTERMEDIO

DEPARTAMENTO	ÁREA (m²)
SERVICIO PÚBLICO	96.13
SERVICIOS ADICIONALES - ÁREA NO PAGA	549.79
ZONA DE REFUGIO	9.02
ÁREA BRT	70.65
ÁREA CULTURAL	20.10
ÁREA NO PAGA	1000.38
ÁREA OPERATIVA	469.69
ÁREA PAGA	647.99
ÁREA PÚBLICA	178.01
ÁREA TÉCNICA	66.78

EDIFICIO DESCENDENTE 01
ARQ_PL_02_INTERMEDIO

DEPARTAMENTO	ÁREA (m²)
SERVICIO PÚBLICO	71.60
SERVICIOS ADICIONALES - ÁREA NO PAGA	519.39
ZONA DE REFUGIO	9.11
ÁREA BRT	63.11
ÁREA NO PAGA	409.60
ÁREA OPERATIVA	14.47
ÁREA PAGA	665.94
ÁREA TÉCNICA	66.58

EDIFICIO DESCENDENTE 02
ARQ_PL_02_INTERMEDIO

DEPARTAMENTO	ÁREA (m²)
SERVICIOS ADICIONALES - ÁREA NO PAGA	18.49
SERVICIOS ADICIONALES - ÁREA PAGA	49.60
ÁREA NO PAGA	223.48
ÁREA OPERATIVA	27.91
ÁREA PAGA	225.39
ÁREA TÉCNICA	20.77

NAVE CENTRAL
ARQ_PL_02_INTERMEDIO

DEPARTAMENTO	ÁREA (m²)
ÁREA BRT	328.80
ÁREA PAGA	320.58
TOTAL NIVEL INTERMEDIO	6143.35

TABLA GENERAL DE NIVELES

NOMBRE	NIVEL	ELEVACIÓN (m)
ARQ_PL_00.01_ACCESO	ACCESO	-3.84
ARQ_PL_00.02_ACCESO	ACCESO	-3.69
ARQ_PL_00.03_ACCESO	ACCESO	-3.39
ARQ_PL_00.04_ACCESO	ACCESO	-3.29
ARQ_PL_00.05_ACCESO	ACCESO	-3.19
ARQ_PL_00.06_ACCESO	ACCESO	-3.04
ARQ_PL_00.07_ACCESO	ACCESO	-2.89
ARQ_PL_00.08_ACCESO	ACCESO	-2.69
ARQ_PL_00.09_ACCESO	ACCESO	-2.54
ARQ_PL_00.10_ACCESO	ACCESO	-2.09
ARQ_PL_00.11_ACCESO	ACCESO	-1.84
ARQ_PL_00.12_ACCESO	ACCESO	-1.59
ARQ_PL_00.13_ACCESO	ACCESO	-1.29
ARQ_PL_00.14_ACCESO	ACCESO	-1.09
ARQ_PL_00.15_ACCESO	ACCESO	-0.99
ARQ_PL_00.16_ACCESO	ACCESO	-0.79
ARQ_PL_00.17_ACCESO	ACCESO	-0.69
ARQ_PL_00.18_ACCESO	ACCESO	-0.49
ARQ_PL_00.19_ACCESO	ACCESO	-0.34
ARQ_PL_00_SÓTANO	SÓTANO	-7.94
ARQ_PL_01_ACCESO	ACCESO*	2574.39 M.S.N.M./ 0.00
ARQ_PL_02.2_TOR	TOPE DE RIEL	14.24
ARQ_PL_02_INTERMEDIO	INTERMEDIO	6.64
ARQ_PL_03_PLATAFORMA	PLATAFORMA	15.38
ARQ_PL_04_CUB_EDIFICACIONES	CUBIERTA EDIFICACIONES	21.98
ARQ_PL_05_CUB_NVC	CUBIERTA NAVE CENTRAL	24.64

LOCALIZACIÓN

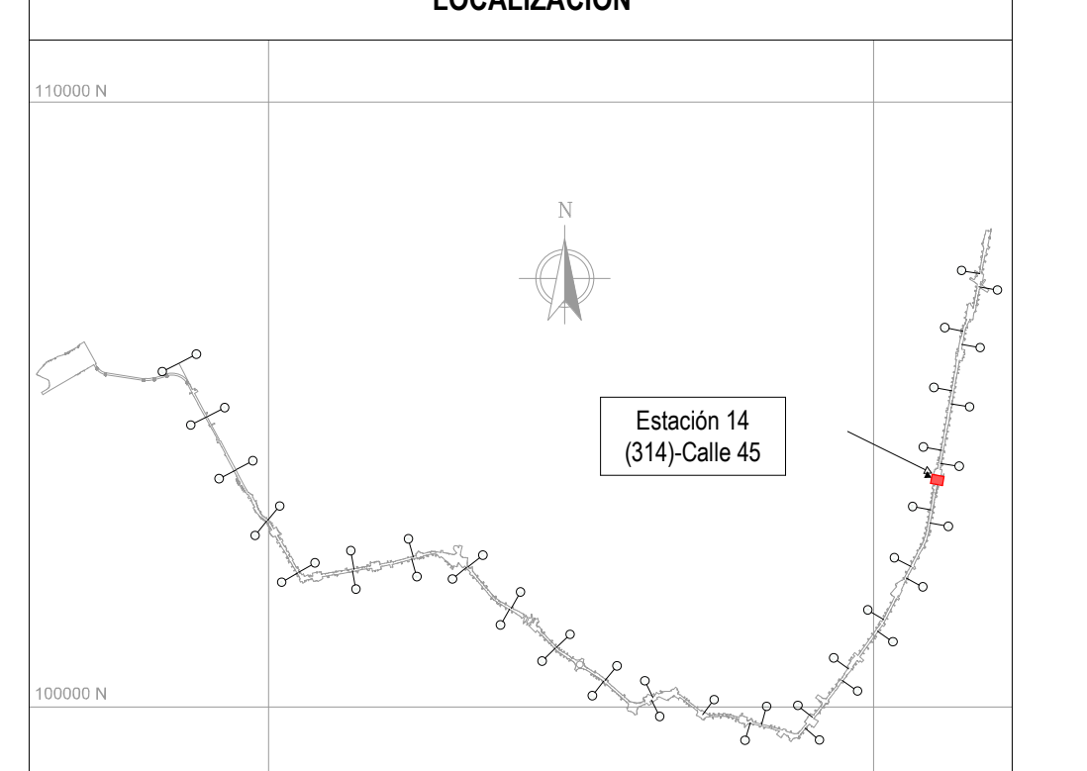

NOTAS

01 TODAS LAS DIMENSIONES ESTÁN CONFIGURADAS EN METROS A MENOS QUE SE INDIQUE UNA UNIDAD DE MEDIDA DIFERENTE.

02 TODAS LAS MEDIDAS, UBICACIÓN Y NIVELES DEBEN VERIFICARSE EN EL LUGAR DE CONSTRUCCIÓN.

03 EL NIVEL DE ACCESO AL EDIFICIO PL 01 CORRESPONDE AL +0,00 DE LA ESTACIÓN Y REFERENCIA AL NIVEL 2574.39 M.S.N.M.

04 LOS NOMBRES ESPECÍFICOS DE LAS ÁREAS PUEDEN SER CONSULTADAS EN EL PLANO NO. 3 Ó EN LAS VISTAS EN PLANTA.

05 LOS COLORES QUE SE MUESTRAN EN LOS PLANOS COMO PROYECCIÓN DE ELEMENTOS ARQUITECTÓNICOS COMO CUBIERTAS FACHADAS MUROS ETC. NO REPRESENTAN LA MATERIALIDAD Y REALIDAD DE ACABADOS DEL PROYECTO, SOLO SON INDICATIVOS PARA REALIZAR UNA CORRECTA LECTURA DE LA PLANIMETRÍA.

06 LAS ESCALERAS ELÉCTRICAS INDICAN SU SENTIDO CON LA SIGUIENTE NOMENCLATURA: "SUBE" Y "BAJA".

07 SE DEBEN REVISAR LOS NIVELES ESTRUCTURALES PARA NIVEL DE ACCESO PL_01 Y SUBNIVELES, PL_02 (INTERMEDIO), PL_03 (PLATAFORMA) CON LA PLANIMETRÍA DE PLACAS ESTRUCTURALES EN LOS ENTREGABLES L1T1-1300-414-CON-ED-EST-PL-0038, 39, 42, 43, 126, 86, RESPECTIVAMENTE. EL NIVEL ESTRUCTURAL (NE) REFERENCIA LOS ESPACIOS DONDE SE DEBE ACONDICIONAR EL ACABADO DE PISO SEGÚN CORRESPONDA, CON LOS NIVELES DE PISO TERMINADO (NPT). LOS NIVELES PROYECTADOS DE EMPATE (NPE) EN LAS ÁREAS DE SERVICIOS ADICIONALES, REFERENCIAN LA ADECUACIÓN DE LOS DESNIVELES EN ESTAS ÁREAS; QUEDA COMO RESPONSABILIDAD DEL LOCATARIO DEFINIR Y ACONDICIONAR ESTE ACABADO DE PISO (NPE) EN LÍNEA CON EL NIVEL (NPT) DE ESPACIOS COLINDANTES. EL NIVEL ESTRUCTURAL (NE) SE ENCUENTRA A (- 0.10M) POR DEBAJO DE LOS NIVELES DE PISO TERMINADO (NPT) Y LOS NIVELES PROYECTADOS DE EMPATE (NPE) MARCADOS EN LA PLANIMETRÍA.

08 RESPECTO A LAS ÁREAS CONSTRUIDAS Y DE ACUERDO CON LA COMUNICACIÓN EXTS22-0002544 DE EMB, SE IDENTIFICA QUE EL CONCESIONARIO SE ENCUENTRA BUSCANDO ESTRATEGIAS PARA MEJORAR EL DISEÑO CON EL PROGRAMA ARQUITECTÓNICO, UNA DE ESTAS ESTRATEGIAS ES MEJORAR EL FUNCIONAMIENTO DEL DISEÑO URBANO Y BRINDAR UNA SOLUCIÓN INTEGRAL RESPECTO A LOS INMUEBLES DE INTERÉS CULTURAL. DE ACUERDO CON LO ANTERIOR, PARA LA EMB, ESTAS ACTIVIDADES OBEDECEN AL PROCESO NATURAL DE LOS ESTUDIOS Y DISEÑOS DEFINITIVOS QUE DEBE DESARROLLAR METRO LÍNEA 1.

CONVENCIONES

▬ ▬ ▬	LÍMITE DE INTERVENCIÓN
‐ ‐ ‐	HUELLA APÉNDICE TÉCNICO
‐ ‐ ‐	HUELLA DE EDIFICIOS EXISTENTES
■	MURO DIVISORIO
— — —	PROYECCIÓN NIVEL SUPERIOR

🟩	SERVICIOS ADICIONALES - ÁREA NO PAGA	🟨	ÁREA NO PAGA
🟩	SERVICIOS ADICIONALES - ÁREA PAGA	🟧	ÁREA PAGA
🟩	SERVICIO PÚBLICO	🟦	ÁREA PÚBLICA
🟦	ZONA DE REFUGIO	⬜	ÁREA TÉCNICA
🟥	ÁREA CULTURAL	🟦	ÁREA OPERATIVA
🟪	ÁREA DE TAQUILLAS BRT		

No.	PLANOS DE REFERENCIA	REV.

No.	MODELO BIM DE REFERENCIA	REV.
1	L1T1-1100-214-CON-ED-EST-MO-0001.rvt	V00
2	L1T1-1100-215-CON-ED-EST-MO-0001.rvt	V00
3	L1T1-1100-314-CON-ED-EST-MO-0001.rvt	V00
4	L1T1-1150-214-CON-ED-EST-MO-0001.rvt	V00
5	L1T1-1150-215-CON-ED-EST-MO-0001.rvt	V00
6	L1T1-1150-314-CON-ED-EST-MO-0001.rvt	V00
7	L1T1-1200-314-CON-ED-EST-MO-0001.rvt	V00
8	L1T1-1300-414-CON-ED-EST-MO-0001.rvt	V01
9	L1T1-1300-414-CON-ED-EST-MO-0002.rvt	V01
10	L1T1-1300-414-CON-ED-EST-MO-0003.rvt	V01
11	L1T1-1310-414-CON-ED-EST-MO-0001.rvt	V00
12	L1T1-1410-314-CON-ED-MEC-MO-0001.rvt	V00
13	L1T1-1420-314-CON-ED-MEC-MO-0002.rvt	V00
14	L1T1-2320-588-CON-ED-EST-MO-0001.rvt	V00
15	L1T1-2320-588-CON-ED-ARQ-MO-0001.rvt	V00
16	L1T1-5160-314-CON-ED-EST-MO-0001.rvt	V00
17	L1T1-5160-314-CON-ED-ARQ-MO-0001.rvt	V00
18	L1T1-5300-314-CON-ED-MEC-MO-0001.rvt	V00
19	L1T1-5600-314-CON-ED-INS-MO-0001.rvt	V00

No.	PAQUETE DE TRABAJO DE REFERENCIA	REV.
1	XREF-URBANISM_CONTEXT_ST14.rvt	
2	XREF-SECONDARY-STRUCTURE-ST14.rvt	

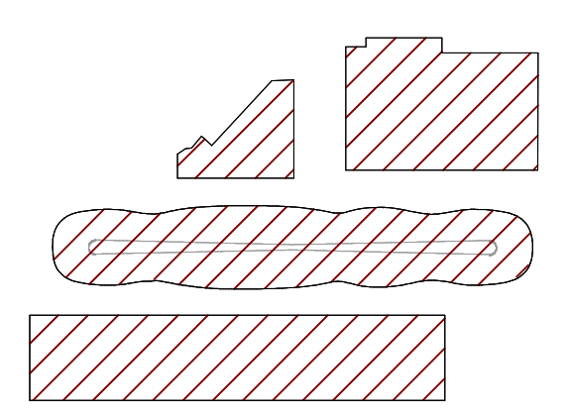

PLANO CLAVE ESTACIÓN 14

METRO BOGOTÁ
GCS Consorcio Consultores PMO Bogotá
CONSORCIO SUPERVISOR PLMB
wsp

DISEÑÓ: Santiago A. David G.
SANTIAGO ANDRES DAVID GUZMÁN
Mat.: A413202011-1010176190

APROBÓ:
MAURICIO MEJÍA RESTREPO
Mat.: 25202-72411 CND

REVISÓ:
FREDDY BAUTISTA R.
Mat.:25202-092831 CND

DIBUJÓ:
EQUIPO WSP

REVISIÓN No.	FECHA	DESCRIPCIÓN	REVISÓ	APROBÓ	APROBACIÓN CLIENTE
V01	12/11/2025	REVISIÓN NO OBJETADA - EMITIDO PARA CONSTRUCCIÓN	F.B.R	M.M.R	
VB1	20/03/2025	EMITIDO PARA REVISIÓN Y COMENTARIOS DEL CLIENTE E INTERVENTORÍA	F.B.R	E.O.M	
V00	13/02/2025	REVISIÓN NO OBJETADA - EMITIDO PARA CONSTRUCCIÓN	F.B.R	E.O.M	
VFF	18/10/2024	EMITIDO PARA REVISIÓN Y COMENTARIOS DEL CLIENTE E INTERVENTORÍA - INCLUYE COMENTARIOS /(AJUSTES V3)	F.B.R	E.O.M	
VEE	17/07/2024	EMITIDO PARA REVISIÓN Y COMENTARIOS DEL CLIENTE E INTERVENTORÍA - INCLUYE COMENTARIOS /(AJUSTES V2)	F.B.R	E.O.M	
VDD	18/12/2022	EMITIDO PARA REVISIÓN Y COMENTARIOS DEL CLIENTE E INTERVENTORÍA - INCLUYE COMENTARIOS /(AJUSTES)	J.E.M	M.B.M	
VCC	02/06/2022	EMITIDO PARA REVISIÓN Y COMENTARIOS DEL CLIENTE E INTERVENTORÍA - INCLUYE COMENTARIOS /(ENTREGA 90%)	J.E.M	M.B.M	
VBB	06/12/2021	EMITIDO PARA REVISIÓN Y COMENTARIOS DEL CLIENTE E INTERVENTORÍA	J.E.M	M.B.M	
VA0	30/06/2021	EMITIDO PARA COMENTARIOS INTERNOS - EMISIÓN PRELIMINAR PARA COMENTARIOS	J.E.M	M.B.M	

METRO LÍNEA 1

DIRECTOR DE INTERVENTORÍA:
JAVIER DESCARGA N.
Mat.:25202-68697 CND

ESPECIALISTA INTERVENTORÍA:
MARIA AUXILIADORA SANCHEZ HERMOSIN
INT: PAH138382-RES.NO.34 DE 2021

FECHA: NOVIEMBRE 2025

METRO LÍNEA 1
CONTRATO DE CONCESIÓN No. 163 DE 2019

PROYECTO PRIMERA LÍNEA DEL METRO DE BOGOTÁ - TRAMO 1

INFRAESTRUCTURA VIAL

ARQUITECTURA

ESTACIÓN METRO 14 - (CALLE 45)
GENERAL
VISTA EN PLANTA Y 3D - NIVEL INTERMEDIO

PLANCHA No: L1T1-0000-314-CON-ED-ARQ-PL-0001_06_V01
ARCHIVO: L1T1-0000-314-CON-ED-ARQ-MO-0001_V01.rvt
ESCALA: INDICADA
FECHA: JUNIO 2021
REVISIÓN No. V01
PLANO No. 06 DE 96