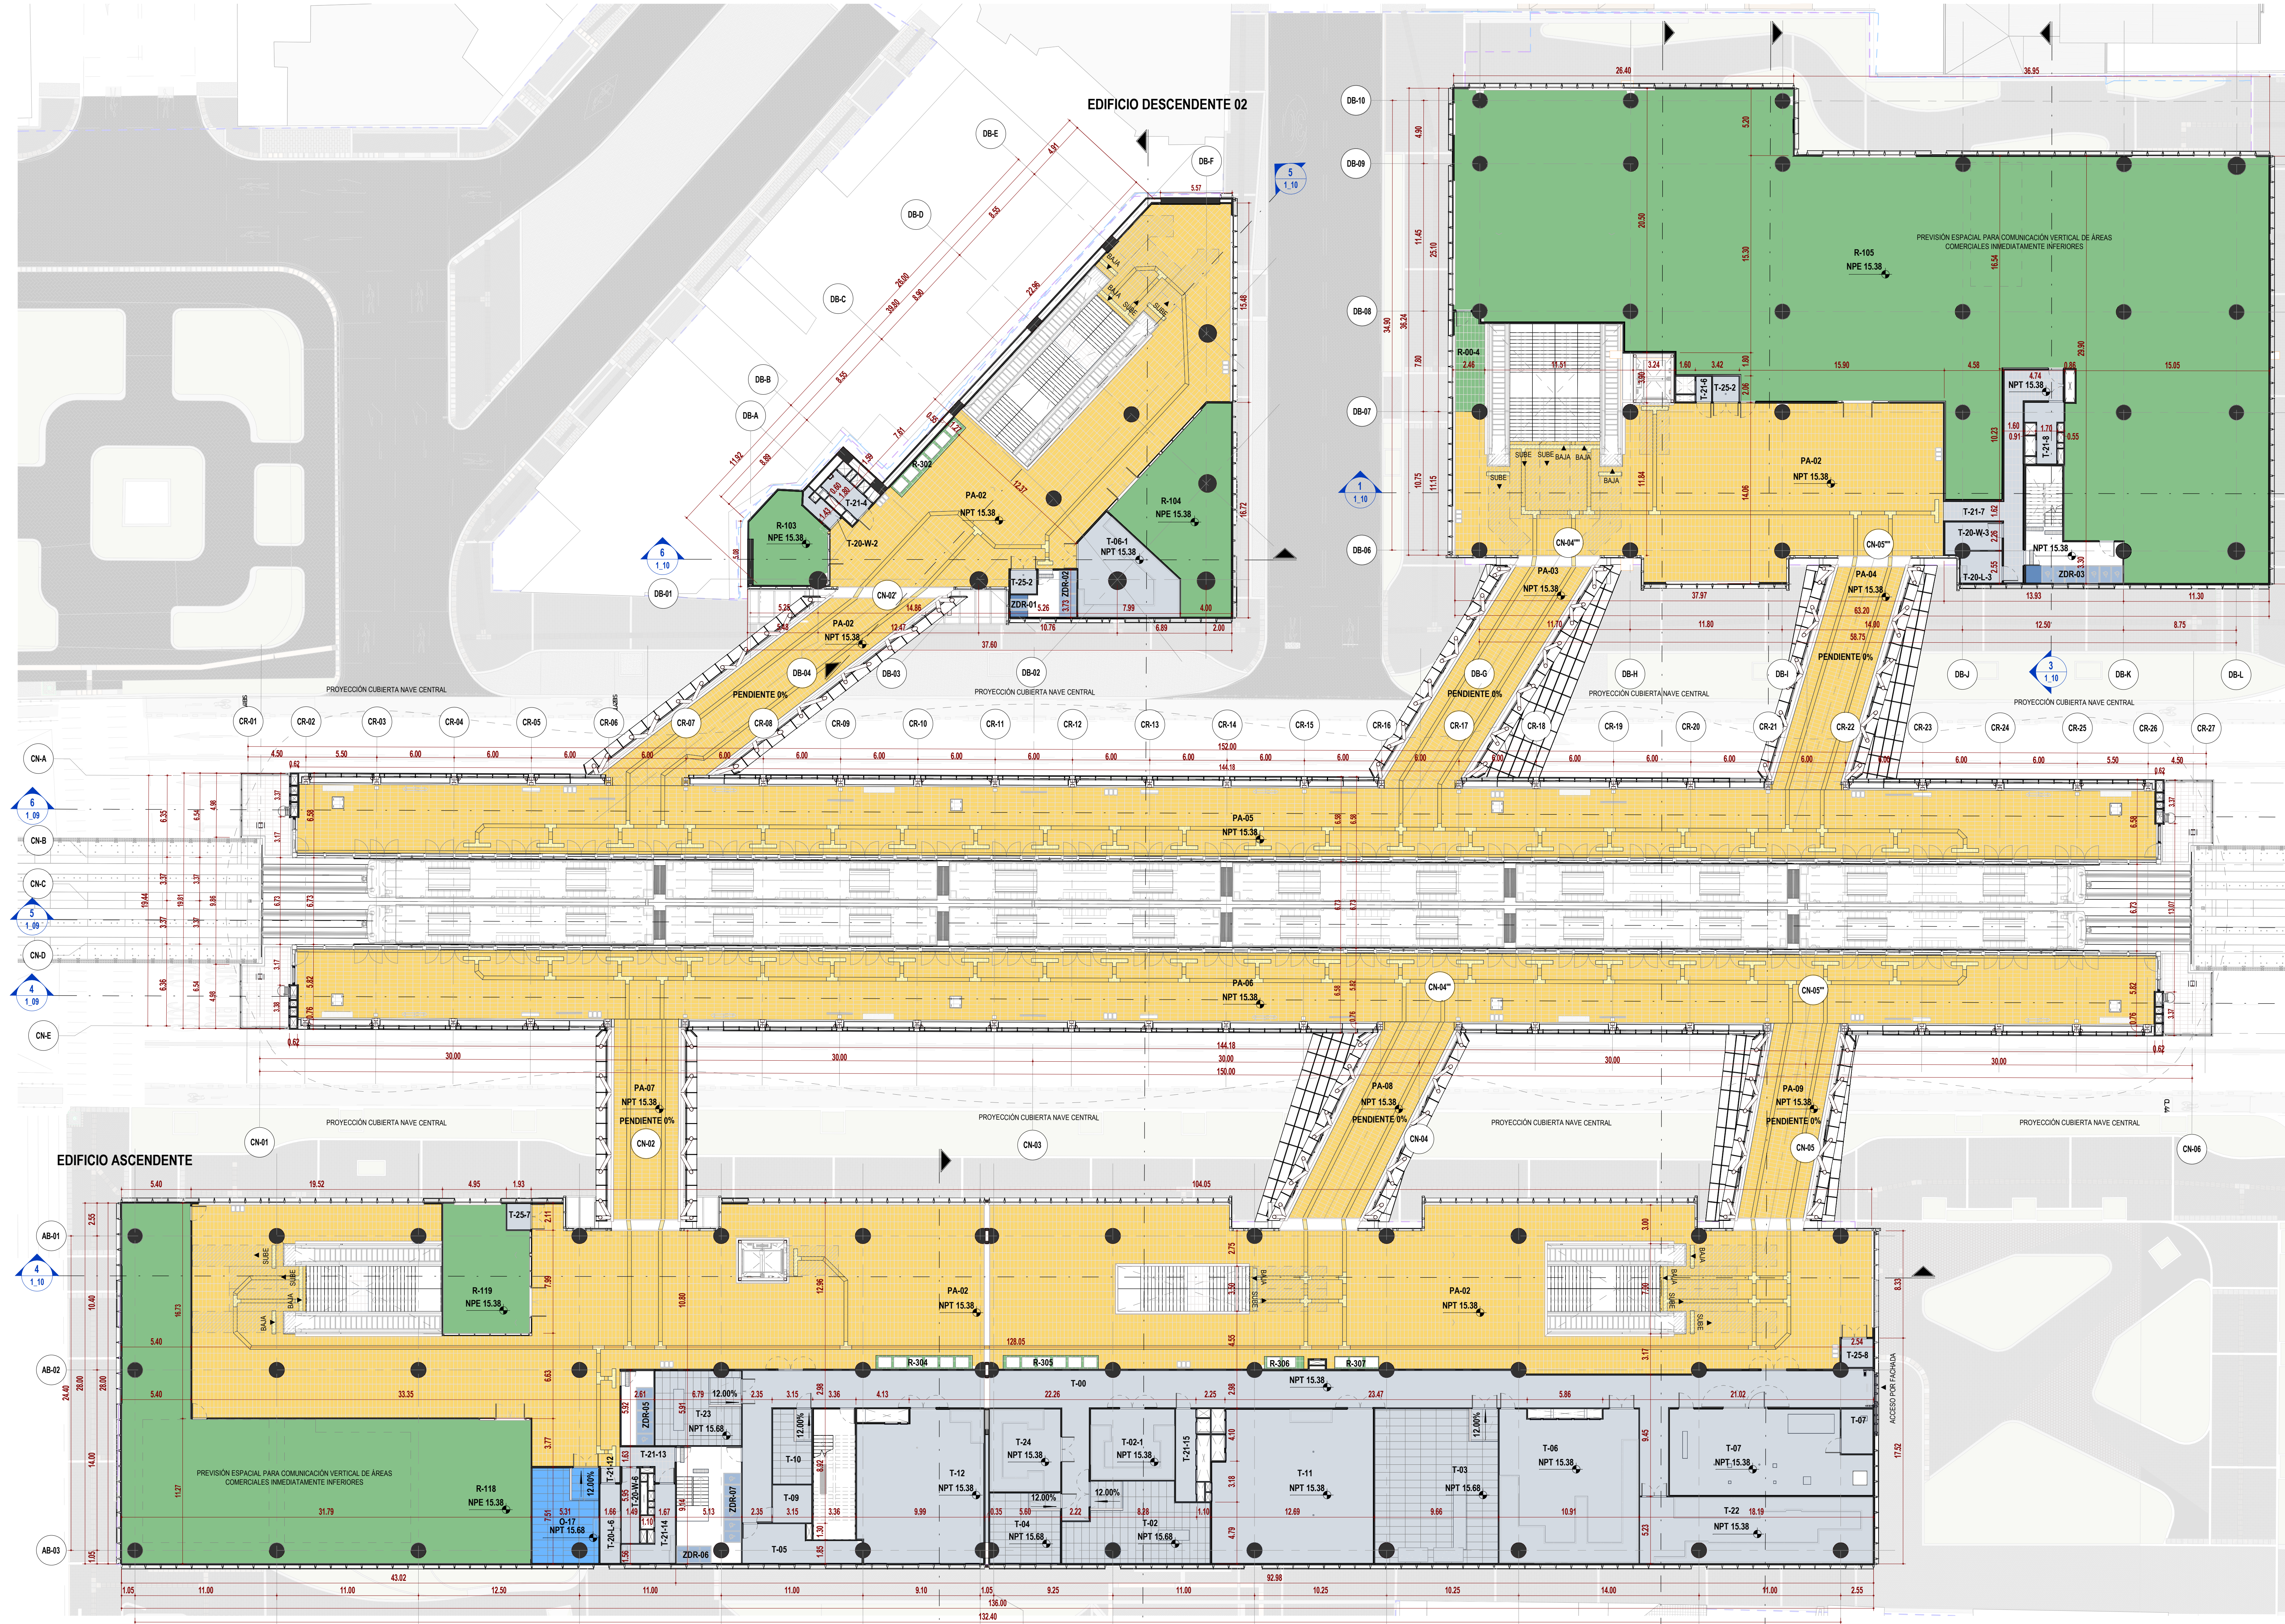

2 NIVEL PLATAFORMA_GENERAL
ESC: 1 : 200

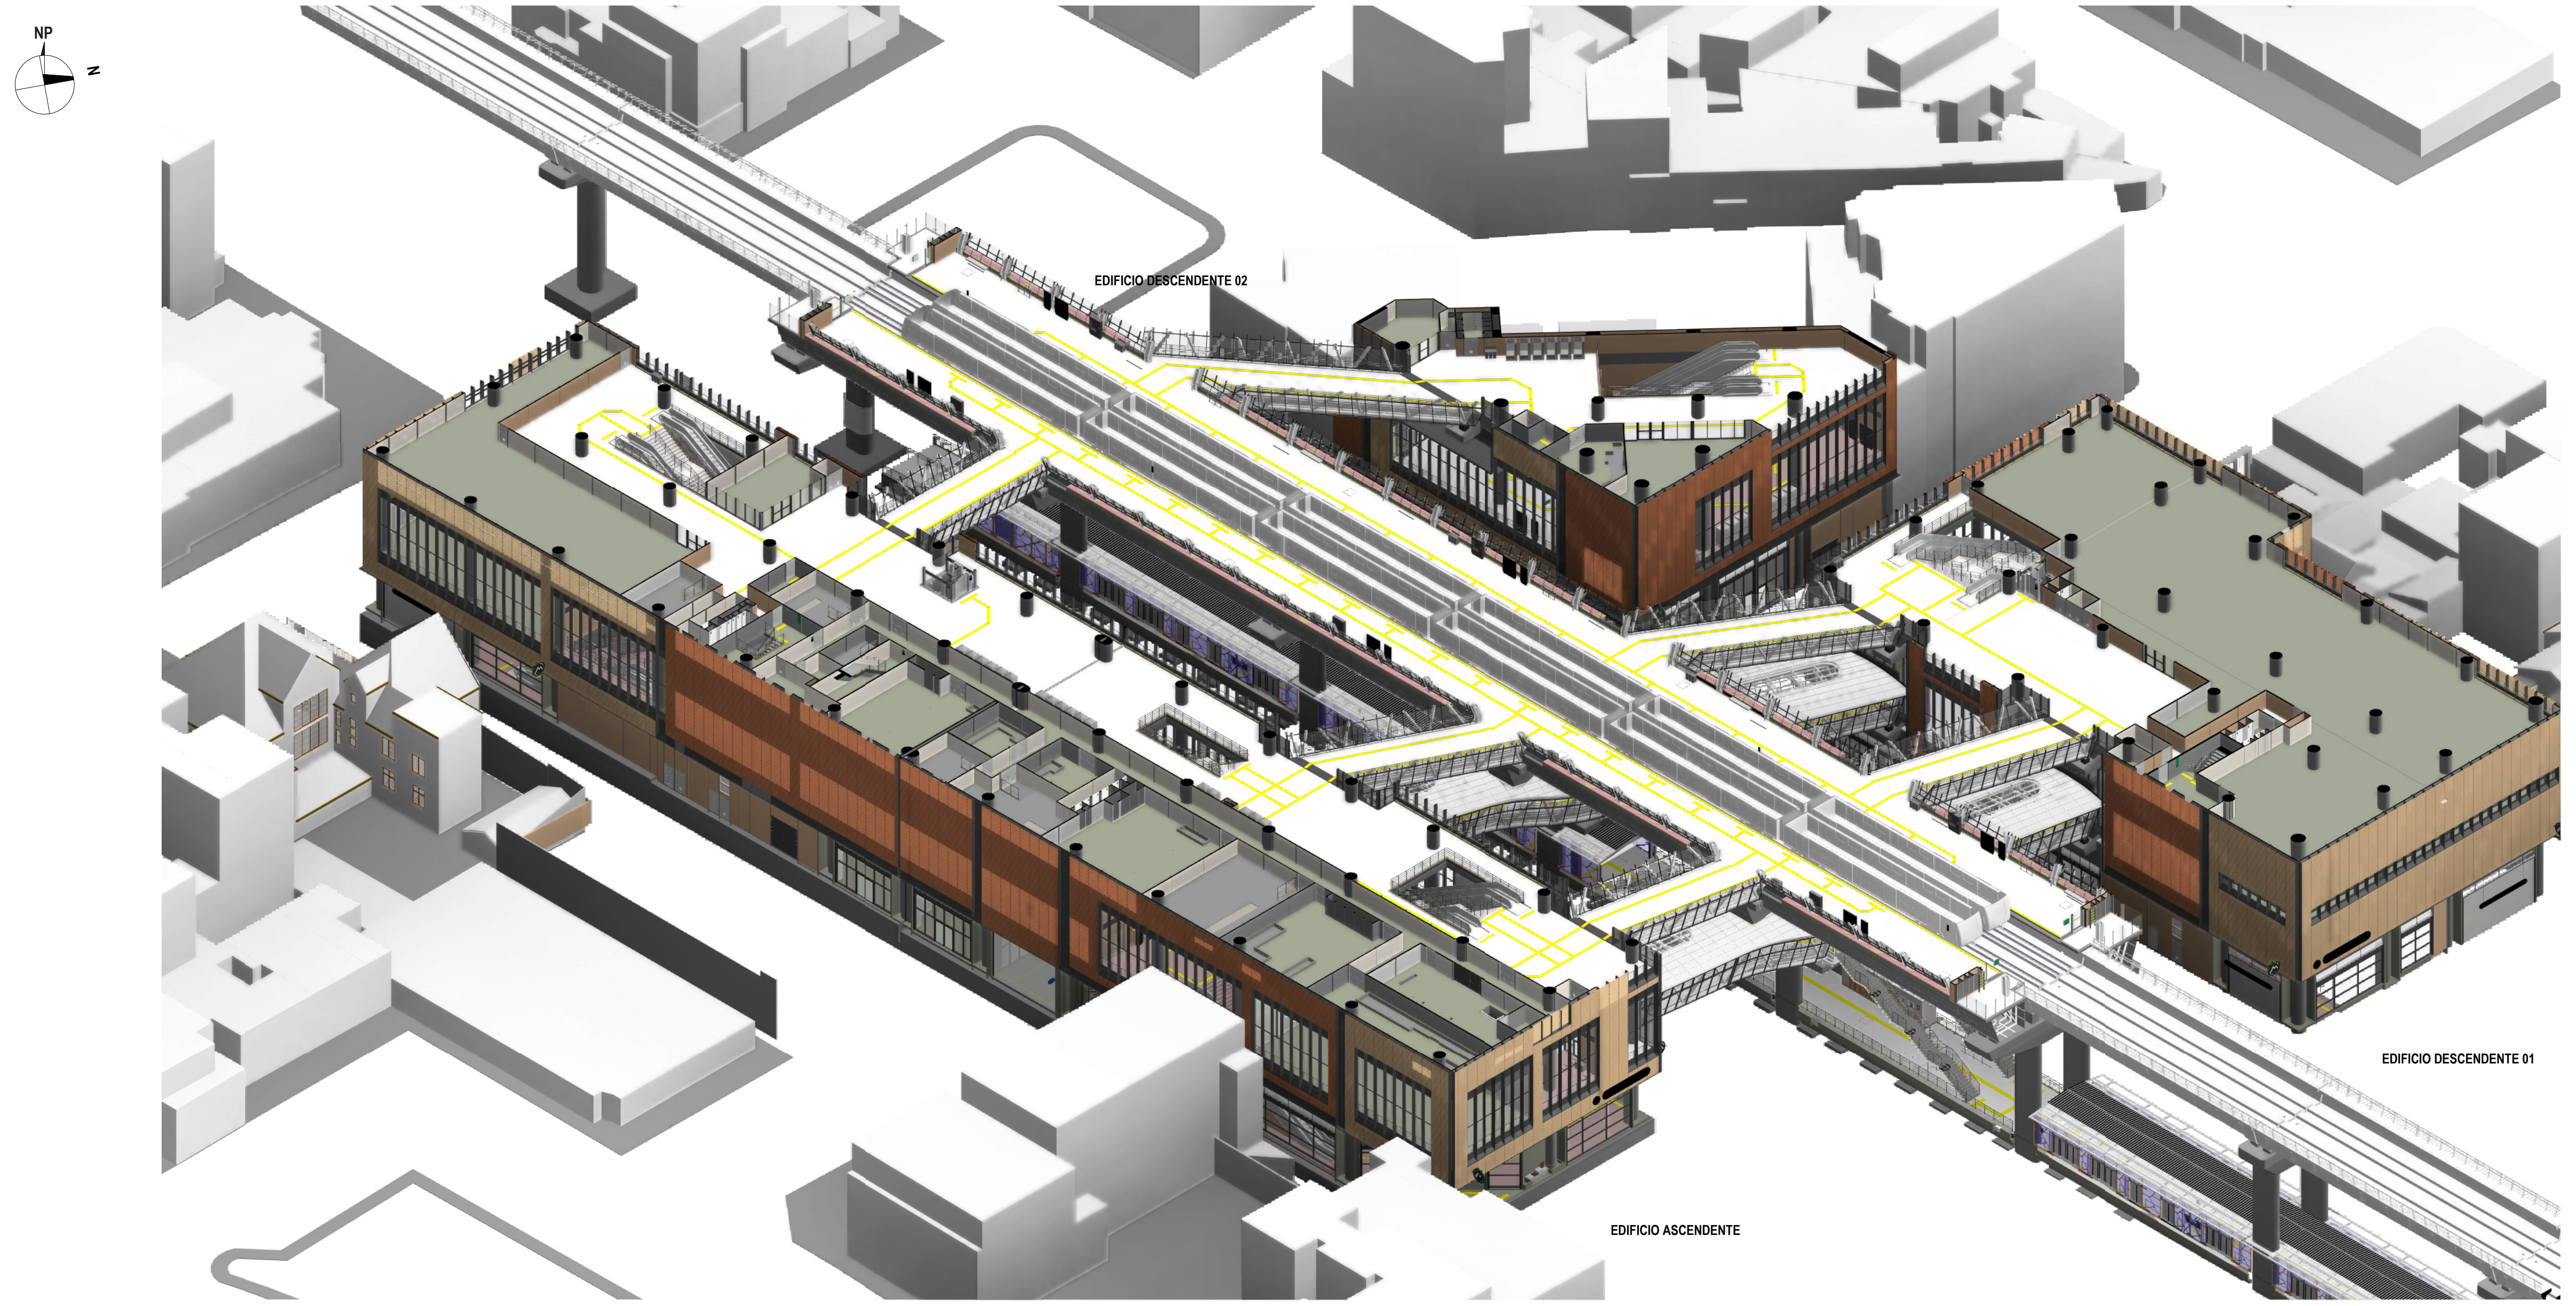

1 3D_GENERAL
ESC: N/A

TABLA DE ÁREAS ÚTILES (NIVEL PLATAFORMA)

EDIFICIO ASCENDENTE
ARQ_PL_03_PLATAFORMA

CÓDIGO	NOMBRE	ÁREA (m²)	DEPARTAMENTO
O-17	OPERADORES TELECOMUNICACIONES EXTERIORES	36.94	ÁREA OPERATIVA
PA-02	ÁREA PAGA	1410.86	ÁREA PAGA
R-118	SERVICIOS ADICIONALES - ÁREA DE SERVICIO	435.42	SERVICIOS ADICIONALES - ÁREA PAGA
R-119	SERVICIOS ADICIONALES - ÁREA DE SERVICIO	62.75	SERVICIOS ADICIONALES - ÁREA PAGA
R-304	SERVICIOS ADICIONALES - MÁQUINAS EXPENDEDORAS/CAJEROS AUTOMÁTICOS	8.03	SERVICIOS ADICIONALES - ÁREA PAGA
R-305	SERVICIOS ADICIONALES - MÁQUINAS EXPENDEDORAS/CAJEROS AUTOMÁTICOS	7.92	SERVICIOS ADICIONALES - ÁREA PAGA
R-306	SERVICIOS ADICIONALES - MÁQUINAS EXPENDEDORAS/CAJEROS AUTOMÁTICOS	3.06	SERVICIOS ADICIONALES - ÁREA PAGA
R-307	SERVICIOS ADICIONALES - MÁQUINAS EXPENDEDORAS/CAJEROS AUTOMÁTICOS	3.42	SERVICIOS ADICIONALES - ÁREA PAGA
T-00	CIRCULACIÓN TÉCNICA	297.39	ÁREA TÉCNICA
T-02	LOCAL DE CONDUCCIÓN AUTOMÁTICA (CBTC)	60.37	ÁREA TÉCNICA
T-02-1	UPS DEDICADA (CBTC)	35.49	ÁREA TÉCNICA
T-03	TELECOMUNICACIONES ESTACIÓN - CORRIENTE DÉBIL	113.27	ÁREA TÉCNICA
T-04	EQUIPO BOLETERÍA	29.11	ÁREA TÉCNICA
T-05	ALMACÉN PARA MANTENIMIENTO	21.90	ÁREA TÉCNICA
T-06	SALA DE TABLEROS	122.88	ÁREA TÉCNICA
T-07	CENTRO DE TRANSFORMACIÓN (CT)	104.29	ÁREA TÉCNICA
T-09	ALMACÉN EQUIPO ELÉCTRICO	8.70	ÁREA TÉCNICA
T-10	CUARTO DE EQUIPO ELECTROMECÁNICO	17.49	ÁREA TÉCNICA
T-11	CUARTO DE VENTILACIÓN	143.49	ÁREA TÉCNICA
T-12	PLANTA DE REFRIGERACIÓN PARA LA CLIMATIZACIÓN	110.22	ÁREA TÉCNICA
T-20-L-6	MEDIDORES (LUZ)	9.47	ÁREA TÉCNICA
T-20-W-6	MEDIDORES (AGUA)	8.03	ÁREA TÉCNICA
T-21-12	ÁREA DE INSPECCIÓN	1.92	ÁREA TÉCNICA
T-21-13	ÁREA DE INSPECCIÓN	8.39	ÁREA TÉCNICA
T-21-14	ÁREA DE INSPECCIÓN	13.31	ÁREA TÉCNICA
T-21-15	ÁREA DE INSPECCIÓN	11.18	ÁREA TÉCNICA
T-22	CUARTO DE UPS	89.80	ÁREA TÉCNICA
T-23	CUARTO PDAP	38.25	ÁREA TÉCNICA
T-24	TETRA UPS	34.84	ÁREA TÉCNICA
T-25-7	NODO DE ACCESO DE TELECOMUNICACIONES	3.60	ÁREA TÉCNICA
T-25-8	NODO DE ACCESO DE TELECOMUNICACIONES	5.11	ÁREA TÉCNICA
ZDR-05	ZONA DE REFUGIO (PMR)	6.07	ZONA DE REFUGIO
ZDR-06	ZONA DE REFUGIO (PMR)	3.64	ZONA DE REFUGIO
ZDR-07	ZONA DE REFUGIO (PMR)	7.29	ZONA DE REFUGIO

TABLA DE ÁREAS ÚTILES (NIVEL PLATAFORMA)

EDIFICIO DESCENDENTE 01
ARQ_PL_03_PLATAFORMA

CÓDIGO	NOMBRE	ÁREA (m²)	DEPARTAMENTO
PA-02	ÁREA PAGA	426.03	ÁREA PAGA
R-00-4	SERVICIOS ADICIONALES - CORREDOR OPERATIVO	16.81	SERVICIOS ADICIONALES - ÁREA PAGA
R-105	SERVICIOS ADICIONALES - ÁREA DE SERVICIO	1425.85	SERVICIOS ADICIONALES - ÁREA PAGA
T-20-L-3	MEDIDORES (LUZ)	7.49	ÁREA TÉCNICA
T-20-W-3	MEDIDORES (AGUA)	9.18	ÁREA TÉCNICA
T-21-6	ÁREA DE INSPECCIÓN	2.32	ÁREA TÉCNICA
T-21-7	ÁREA DE INSPECCIÓN	39.40	ÁREA TÉCNICA
T-21-8	ÁREA DE INSPECCIÓN	9.59	ÁREA TÉCNICA
T-25-2	NODO DE ACCESO DE TELECOMUNICACIONES	3.87	ÁREA TÉCNICA
ZDR-03	ZONA DE REFUGIO (PMR)	10.14	ZONA DE REFUGIO

EDIFICIO DESCENDENTE 02
ARQ_PL_03_PLATAFORMA

CÓDIGO	NOMBRE	ÁREA (m²)	DEPARTAMENTO
PA-02	ÁREA PAGA	349.10	ÁREA PAGA
R-103	SERVICIOS ADICIONALES - ÁREA DE SERVICIO	35.14	SERVICIOS ADICIONALES - ÁREA PAGA
R-104	SERVICIOS ADICIONALES - ÁREA DE SERVICIO	91.19	SERVICIOS ADICIONALES - ÁREA PAGA
R-302	SERVICIOS ADICIONALES - MÁQUINAS EXPENDEDORAS/CAJEROS AUTOMÁTICOS	8.95	SERVICIOS ADICIONALES - ÁREA PAGA
T-06-1	LOCAL SECUNDARIO DE TABLEROS	45.02	ÁREA TÉCNICA
T-20-W-2	MEDIDORES (AGUA)	3.82	ÁREA TÉCNICA
T-21-4	ÁREA DE INSPECCIÓN	6.52	ÁREA TÉCNICA
T-25-2	NODO DE ACCESO DE TELECOMUNICACIONES	3.61	ÁREA TÉCNICA
ZDR-01	ZONA DE REFUGIO (PMR)	2.27	ZONA DE REFUGIO
ZDR-02	ZONA DE REFUGIO (PMR)	4.87	ZONA DE REFUGIO

NAVE CENTRAL
ARQ_PL_03_PLATAFORMA

CÓDIGO	NOMBRE	ÁREA (m²)	DEPARTAMENTO
PA-02	ÁREA PAGA	119.75	ÁREA PAGA
PA-03	ÁREA PAGA	101.64	ÁREA PAGA
PA-04	ÁREA PAGA	91.30	ÁREA PAGA
PA-05	ÁREA PAGA	766.89	ÁREA PAGA
PA-06	ÁREA PAGA	766.86	ÁREA PAGA
PA-07	ÁREA PAGA	78.57	ÁREA PAGA
PA-08	ÁREA PAGA	86.44	ÁREA PAGA
PA-09	ÁREA PAGA	78.09	ÁREA PAGA
TOTAL NIVEL PLATAFORMA		7864.65	

TABLA DE ÁREAS ÚTILES POR DEPARTAMENTO (NIVEL PLATAFORMA)

NAVE CENTRAL
ARQ_PL_03_PLATAFORMA

DEPARTAMENTO	ÁREA (m²)
ÁREA PAGA	2089.55

EDIFICIO DESCENDENTE 02
ARQ_PL_03_PLATAFORMA

DEPARTAMENTO	ÁREA (m²)
SERVICIOS ADICIONALES - ÁREA PAGA	135.27
ZONA DE REFUGIO	7.13
ÁREA PAGA	349.10
ÁREA TÉCNICA	58.97

EDIFICIO DESCENDENTE 01
ARQ_PL_03_PLATAFORMA

DEPARTAMENTO	ÁREA (m²)
SERVICIOS ADICIONALES - ÁREA PAGA	1442.66
ZONA DE REFUGIO	10.14
ÁREA PAGA	426.03
ÁREA TÉCNICA	71.86

EDIFICIO ASCENDENTE
ARQ_PL_03_PLATAFORMA

DEPARTAMENTO	ÁREA (m²)
SERVICIOS ADICIONALES - ÁREA PAGA	520.60
ZONA DE REFUGIO	17.01
ÁREA OPERATIVA	36.94
ÁREA PAGA	1410.86
ÁREA TÉCNICA	1288.52
TOTAL NIVEL PLATAFORMA	7864.65

TABLA GENERAL DE NIVELES

NOMBRE	NIVEL	ELEVACIÓN (m)
ARQ_PL_00.01_ACCESO	ACCESO	-3.84
ARQ_PL_00.02_ACCESO	ACCESO	-3.69
ARQ_PL_00.03_ACCESO	ACCESO	-3.39
ARQ_PL_00.04_ACCESO	ACCESO	-3.29
ARQ_PL_00.05_ACCESO	ACCESO	-3.19
ARQ_PL_00.06_ACCESO	ACCESO	-3.04
ARQ_PL_00.07_ACCESO	ACCESO	-2.89
ARQ_PL_00.08_ACCESO	ACCESO	-2.69
ARQ_PL_00.09_ACCESO	ACCESO	-2.54
ARQ_PL_00.10_ACCESO	ACCESO	-2.09
ARQ_PL_00.11_ACCESO	ACCESO	-1.84
ARQ_PL_00.12_ACCESO	ACCESO	-1.59
ARQ_PL_00.13_ACCESO	ACCESO	-1.29
ARQ_PL_00.14_ACCESO	ACCESO	-1.09
ARQ_PL_00.15_ACCESO	ACCESO	-0.99
ARQ_PL_00.16_ACCESO	ACCESO	-0.79
ARQ_PL_00.17_ACCESO	ACCESO	-0.69
ARQ_PL_00.18_ACCESO	ACCESO	-0.49
ARQ_PL_00.19_ACCESO	ACCESO	-0.34
ARQ_PL_00_SÓTANO	SÓTANO	-7.94
ARQ_PL_01_ACCESO	ACCESO*	2574.39 M.S.N.M./ 0.00
ARQ_PL_02.2_TOR	TOPE DE RIEL	14.24
ARQ_PL_02_INTERMEDIO	INTERMEDIO	6.64
ARQ_PL_03_PLATAFORMA	PLATAFORMA	15.38
ARQ_PL_04_CUB_EDIFICACIONES	CUBIERTA EDIFICACIONES	21.98
ARQ_PL_05_CUB_NVC	CUBIERTA NAVE CENTRAL	24.64

LOCALIZACIÓN

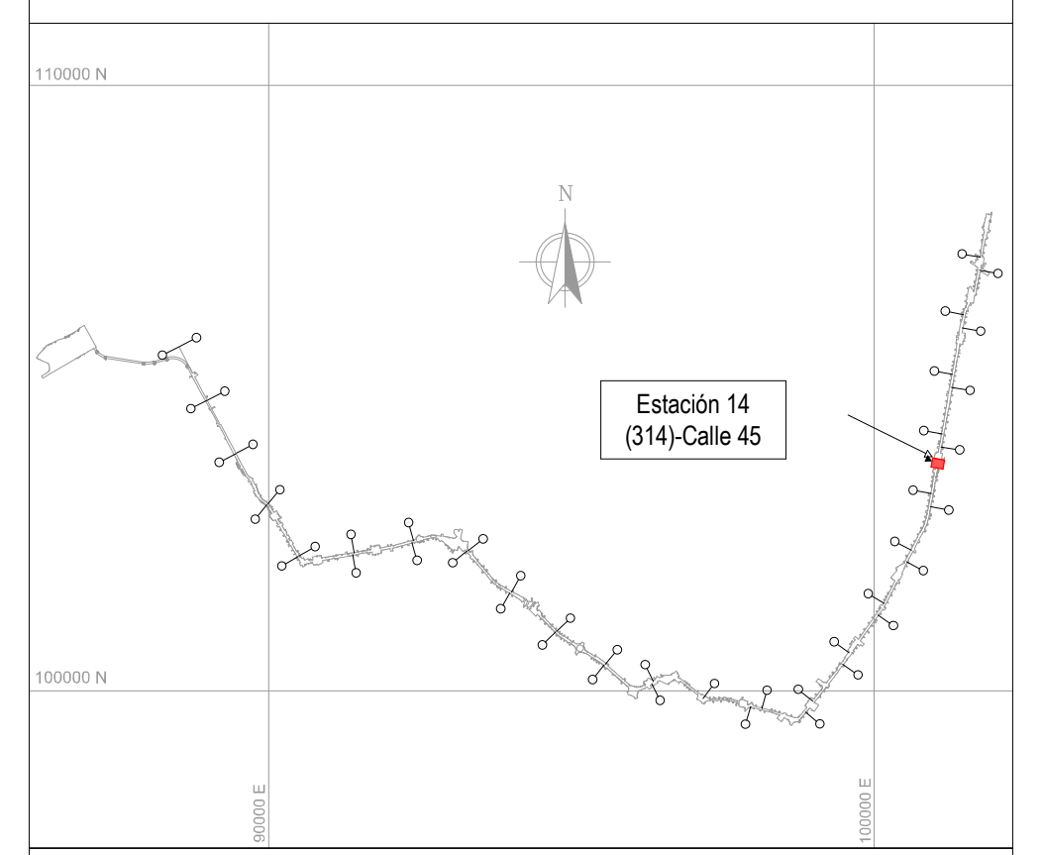

NOTAS

01 TODAS LAS DIMENSIONES ESTÁN CONFIGURADAS EN METROS A MENOS QUE SE INDIQUE UNA UNIDAD DE MEDIDA DIFERENTE.

02 TODAS LAS MEDIDAS, UBICACIÓN Y NIVELES DEBEN VERIFICARSE EN EL LUGAR DE CONSTRUCCIÓN.

03 EL NIVEL DE ACCESO AL EDIFICIO PL 01 CORRESPONDE AL +0,00 DE LA ESTACIÓN Y REFERENCIA AL NIVEL 2574.39 M.S.N.M.

04 LOS NOMBRES ESPECÍFICOS DE LAS ÁREAS PUEDEN SER CONSULTADAS EN EL PLANO NO. 3 Ó EN LAS VISTAS EN PLANTA.

05 LOS COLORES QUE SE MUESTRAN EN LOS PLANOS COMO PROYECCIÓN DE ELEMENTOS ARQUITECTÓNICOS COMO CUBIERTAS FACHADAS MUROS ETC. NO REPRESENTAN LA MATERIALIDAD Y REALIDAD DE ACABADOS DEL PROYECTO, SOLO SON INDICATIVOS PARA REALIZAR UNA CORRECTA LECTURA DE LA PLANIMETRÍA.

06 LAS ESCALERAS ELÉCTRICAS INDICAN SU SENTIDO CON LA SIGUIENTE NOMENCLATURA: "SUBE" Y "BAJA".

07 SE DEBEN REVISAR LOS NIVELES ESTRUCTURALES PARA NIVEL DE ACCESO PL_01 Y SUBNIVELES, PL_02 (INTERMEDIO), PL_03 (PLATAFORMA) CON LA PLANIMETRÍA DE PLACAS ESTRUCTURALES EN LOS ENTREGABLES L1T1-1300-414-CON-ED-EST-PL-0038, 39, 42, 43, 126, 86, RESPECTIVAMENTE. EL NIVEL ESTRUCTURAL (NE) REFERENCIA LOS ESPACIOS DONDE SE DEBE ACONDICIONAR EL ACABADO DE PISO SEGÚN CORRESPONDA, CON LOS NIVELES DE PISO TERMINADO (NPT). LOS NIVELES PROYECTADOS DE EMPATE (NPE) EN LAS ÁREAS DE SERVICIOS ADICIONALES, REFERENCIAN LA ADECUACIÓN DE LOS DESNIVELES EN ESTAS ÁREAS; QUEDA COMO RESPONSABILIDAD DEL LOCATARIO DEFINIR Y ACONDICIONAR ESTE ACABADO DE PISO (NPE) EN LÍNEA CON EL NIVEL (NPT) DE ESPACIOS COLINDANTES. EL NIVEL ESTRUCTURAL (NE) SE ENCUENTRA A (- 0.10M) POR DEBAJO DE LOS NIVELES DE PISO TERMINADO (NPT) Y LOS NIVELES PROYECTADOS DE EMPATE (NPE) MARCADOS EN LA PLANIMETRÍA.

08 RESPECTO A LAS ÁREAS CONSTRUIDAS Y DE ACUERDO CON LA COMUNICACIÓN EXTS22-0002544 DE EMB, SE IDENTIFICA QUE EL CONCESIONARIO SE ENCUENTRA BUSCANDO ESTRATEGIAS PARA MEJORAR EL DISEÑO CON EL PROGRAMA ARQUITECTÓNICO, UNA DE ESTAS ESTRATEGIAS ES MEJORAR EL FUNCIONAMIENTO DEL DISEÑO URBANO Y BRINDAR UNA SOLUCIÓN INTEGRAL RESPECTO A LOS INMUEBLES DE INTERÉS CULTURAL. DE ACUERDO CON LO ANTERIOR, PARA LA EMB, ESTAS ACTIVIDADES OBEDECEN AL PROCESO NATURAL DE LOS ESTUDIOS Y DISEÑOS DEFINITIVOS QUE DEBE DESARROLLAR METRO LÍNEA 1.

CONVENCIONES

- - - LÍMITE DE INTERVENCIÓN
- - - HUELLA APÉNDICE TÉCNICO
- - - HUELLA DE EDIFICIOS EXISTENTES
▬ MURO DIVISORIO
— — PROYECCIÓN NIVEL SUPERIOR

🟩	SERVICIOS ADICIONALES - ÁREA NO PAGA	🟨	ÁREA NO PAGA
🟩	SERVICIOS ADICIONALES - ÁREA PAGA	🟨	ÁREA PAGA
🟩	SERVICIO PÚBLICO	🟦	ÁREA PÚBLICA
🟦	ZONA DE REFUGIO	⬜	ÁREA TÉCNICA
🟥	ÁREA CULTURAL	🟦	ÁREA OPERATIVA
🟪	ÁREA DE TAQUILLAS BRT		

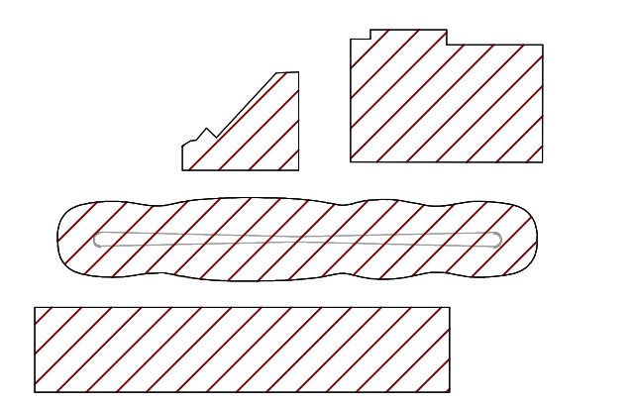

PLANO CLAVE ESTACIÓN 14

No.	PLANOS DE REFERENCIA	REV.

No.	MODELO BIM DE REFERENCIA	REV.
1	L1T1-1100-214-CON-ED-EST-MO-0001.rvt	V00
2	L1T1-1100-215-CON-ED-EST-MO-0001.rvt	V00
3	L1T1-1100-314-CON-ED-EST-MO-0001.rvt	V00
4	L1T1-1150-214-CON-ED-EST-MO-0001.rvt	V00
5	L1T1-1150-215-CON-ED-EST-MO-0001.rvt	V00
6	L1T1-1150-314-CON-ED-EST-MO-0001.rvt	V00
7	L1T1-1200-314-CON-ED-EST-MO-0001.rvt	V00
8	L1T1-1300-414-CON-ED-EST-MO-0001.rvt	V01
9	L1T1-1300-414-CON-ED-EST-MO-0002.rvt	V01
10	L1T1-1300-414-CON-ED-EST-MO-0003.rvt	V01
11	L1T1-1310-414-CON-ED-EST-MO-0001.rvt	V00
12	L1T1-1410-314-CON-ED-MEC-MO-0001.rvt	V00
13	L1T1-1420-314-CON-ED-MEC-MO-0002.rvt	V00
14	L1T1-2320-588-CON-ED-EST-MO-0001.rvt	V00
15	L1T1-2320-588-CON-ED-ARQ-MO-0001.rvt	V00
16	L1T1-5160-314-CON-ED-EST-MO-0001.rvt	V00
17	L1T1-5160-314-CON-ED-ARQ-MO-0001.rvt	V00
18	L1T1-5300-314-CON-ED-MEC-MO-0001.rvt	V00
19	L1T1-5600-314-CON-ED-INS-MO-0001.rvt	V00

No.	PAQUETE DE TRABAJO DE REFERENCIA	REV.
1	XREF-URBANISM_CONTEXT_ST14.rvt	
2	XREF-SECONDARY-STRUCTURE-ST14.rvt	

0 2 10m
1:200

METRO BOGOTÁ
GCS Consorcio Consultores PMO Bogotá
CONSORCIO SUPERVISOR PLMB
wsp

DISEÑÓ: Santiago A. David G.
SANTIAGO ANDRES DAVID GUZMÁN
Mat.: A413202011-1010176190

APROBÓ:
MAURICIO MEJÍA RESTREPO
Mat.: 25202-72411 CND

REVISÓ:
FREDDY BAUTISTA R.
Mat.:25202-092831 CND

DIBUJÓ:
EQUIPO WSP

REVISIÓN No.	FECHA	DESCRIPCIÓN	REVISÓ	APROBÓ	APROBACIÓN CLIENTE
V01	12/11/2025	REVISIÓN NO OBJETADA - EMITIDO PARA CONSTRUCCIÓN	F.B.R	M.M.R	
VB1	20/03/2025	EMITIDO PARA REVISIÓN Y COMENTARIOS DEL CLIENTE E INTERVENTORÍA	F.B.R	E.O.M	
V00	13/02/2025	REVISIÓN NO OBJETADA - EMITIDO PARA CONSTRUCCIÓN	F.B.R	E.O.M	
VFF	18/10/2024	EMITIDO PARA REVISIÓN Y COMENTARIOS DEL CLIENTE E INTERVENTORÍA - INCLUYE COMENTARIOS /(AJUSTES V3)	F.B.R	E.O.M	
VEE	17/07/2024	EMITIDO PARA REVISIÓN Y COMENTARIOS DEL CLIENTE E INTERVENTORÍA - INCLUYE COMENTARIOS /(AJUSTES V2)	F.B.R	E.O.M	
VDD	18/12/2022	EMITIDO PARA REVISIÓN Y COMENTARIOS DEL CLIENTE E INTERVENTORÍA - INCLUYE COMENTARIOS /(AJUSTES)	J.E.M	M.B.M	
VCC	02/06/2022	EMITIDO PARA REVISIÓN Y COMENTARIOS DEL CLIENTE E INTERVENTORÍA - INCLUYE COMENTARIOS /(ENTREGA 90%)	J.E.M	M.B.M	
VBB	06/12/2021	EMITIDO PARA REVISIÓN Y COMENTARIOS DEL CLIENTE E INTERVENTORÍA	J.E.M	M.B.M	
VA0	30/06/2021	EMITIDO PARA COMENTARIOS INTERNOS - EMISIÓN PRELIMINAR PARA COMENTARIOS	J.E.M	M.B.M	

METRO LÍNEA 1

METRO LÍNEA 1
CONTRATO DE CONCESIÓN No. 163 DE 2019

PROYECTO PRIMERA LÍNEA DEL METRO DE BOGOTÁ - TRAMO 1

DIRECTOR DE INTERVENTORÍA:
JAVIER DESCARGA N.
Mat.:25202-68697 CND

ESPECIALISTA INTERVENTORÍA:
MARIA AUXILIADORA SANCHEZ HERMOSIN
INT: PAH138382-RES.NO.34 DE 2021

FECHA: NOVIEMBRE 2025

INFRAESTRUCTURA VIAL

ARQUITECTURA

ESTACIÓN METRO 14 - (CALLE 45)
GENERAL
VISTA EN PLANTA Y 3D - NIVEL PLATAFORMA

PLANCHA No: L1T1-0000-314-CON-ED-ARQ-PL-0001_07_V01
ARCHIVO: L1T1-0000-314-CON-ED-ARQ-MO-0001_V01.rvt
ESCALA: INDICADA
FECHA: JUNIO 2021
REVISIÓN No. V01
PLANO No. 07 DE 96