L1T1-CON-CAL-FR-0120 - B1 : 1000x707mm

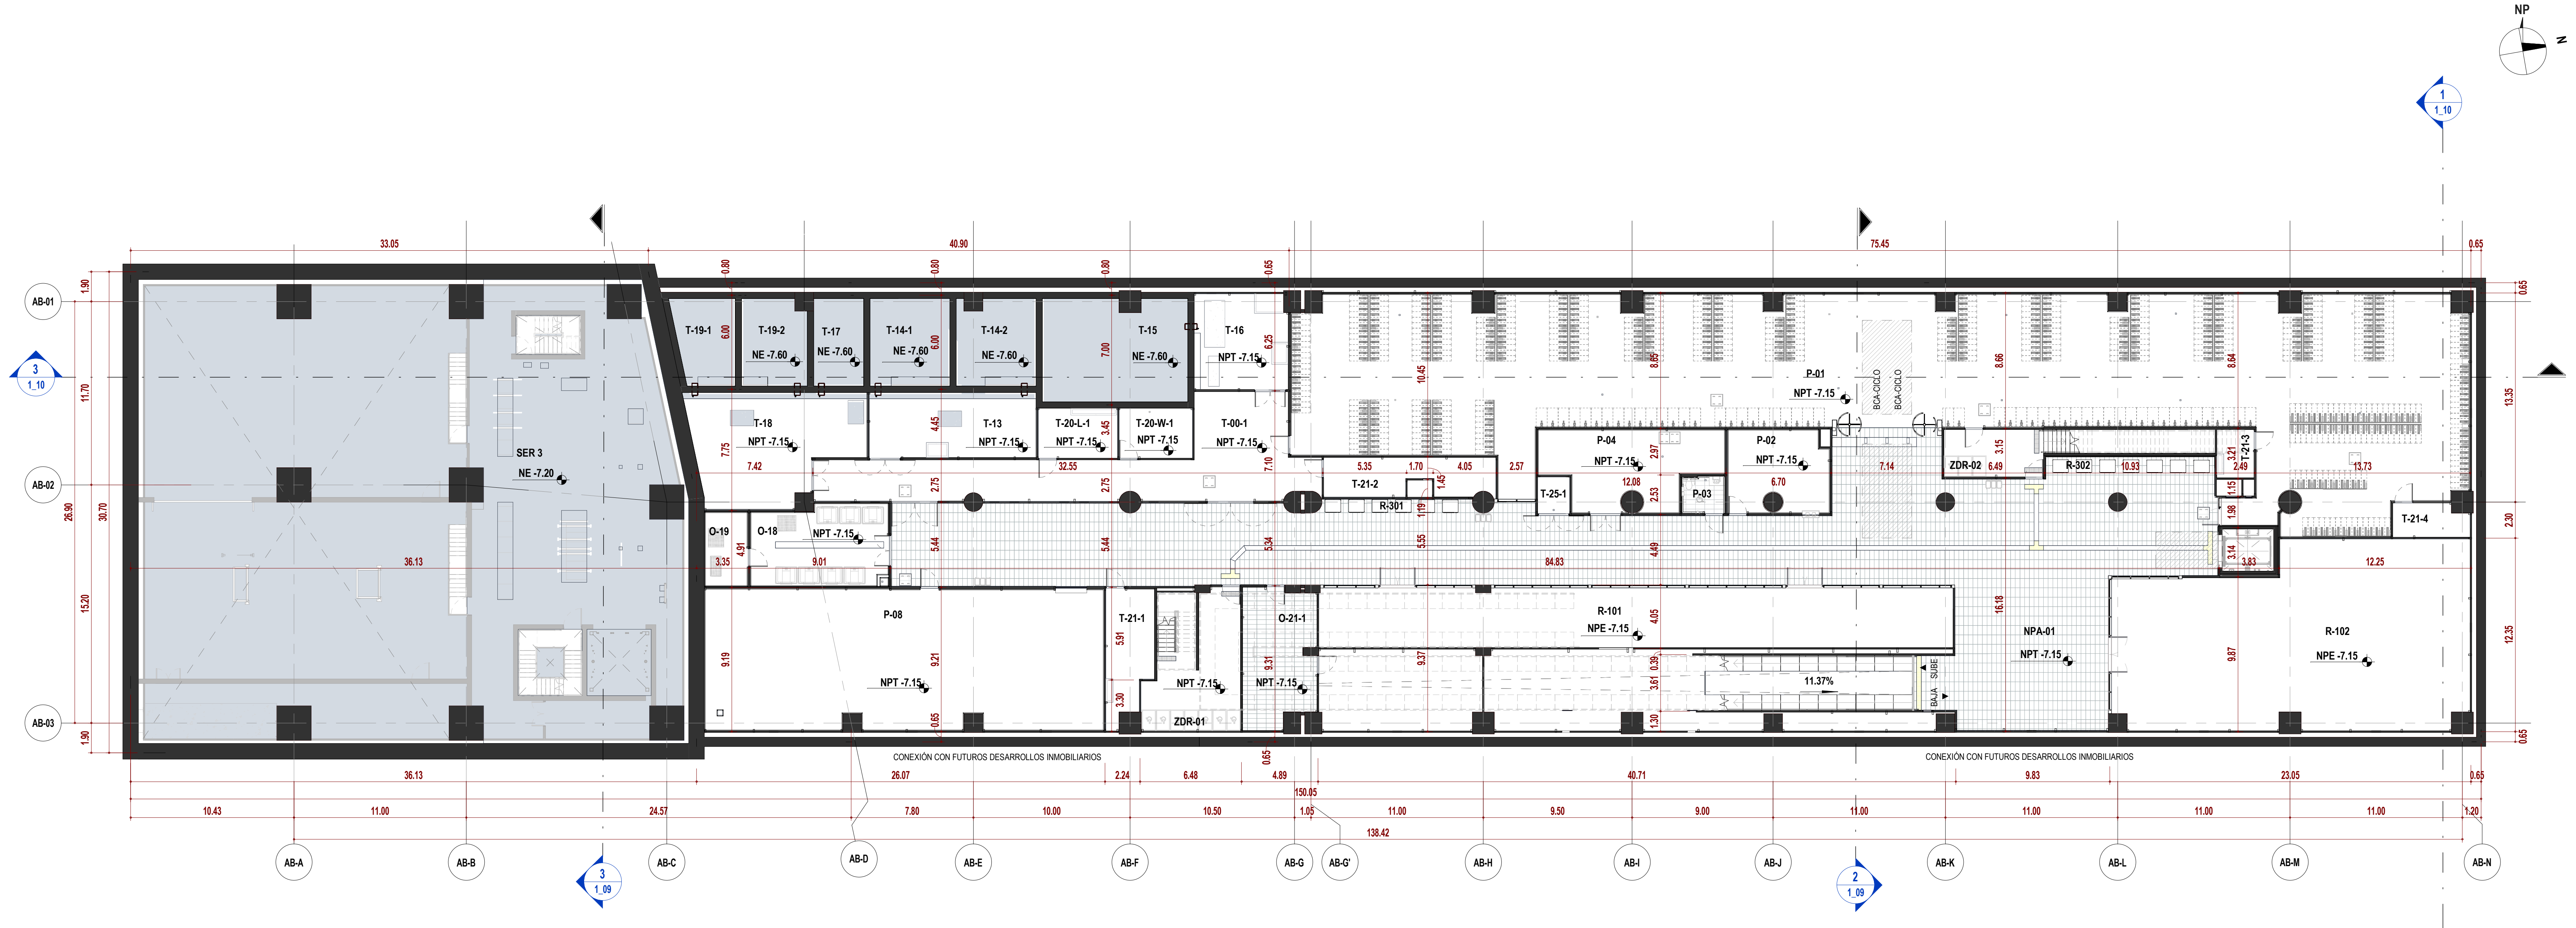

2 NIVEL SÓTANO_EDIFICIO ASCENDENTE
ESC: 1 : 200

TABLA DE ÁREAS ÚTILES (NIVEL SÓTANO_EDIFICIO ASCENDENTE)

CÓDIGO	NOMBRE	ÁREA (m²)	DEPARTAMENTO
EDIFICIO ASCENDENTE			
ARQ_PL_00_SÓTANO			
NPA-01	ÁREA NO PAGA	575.89	ÁREA NO PAGA
O-18	CUARTO DE ALMACENAMIENTO DE RESIDUOS SÓLIDOS	45.19	ÁREA OPERATIVA
O-19	CUARTO DE ALMACENAMIENTO DE RESIDUOS PELIGROSOS	13.06	ÁREA OPERATIVA
O-21-1	ALMACENAMIENTO DE LA ESTACIÓN	37.23	ÁREA OPERATIVA
P-01	ÁREA CICLO-PARQUEADEROS	746.68	ÁREA PÚBLICA
P-02	ÁREA OPERATIVA CICLO-PARQUEADEROS	32.96	ÁREA PÚBLICA
P-03	BAÑO OPERADOR CICLO-PARQUEADEROS	6.39	ÁREA PÚBLICA
P-04	TALLER DE BICICLETAS	50.18	ÁREA PÚBLICA
P-08	ESPACIO CARGA DE VEHÍCULOS ELÉCTRICOS	228.60	ÁREA PÚBLICA
R-101	SERVICIOS ADICIONALES - ÁREA DE SERVICIO	153.43	SERVICIOS ADICIONALES - ÁREA NO PAGA
R-102	SERVICIOS ADICIONALES - ÁREA DE SERVICIO	249.06	SERVICIOS ADICIONALES - ÁREA NO PAGA
R-301	SERVICIOS ADICIONALES - MÁQUINAS EXPENDEDORAS/CAJEROS AUTOMÁTICOS	9.06	SERVICIOS ADICIONALES - ÁREA NO PAGA
R-302	SERVICIOS ADICIONALES - MÁQUINAS EXPENDEDORAS/CAJEROS AUTOMÁTICOS	15.53	SERVICIOS ADICIONALES - ÁREA NO PAGA
SER 3	SER 3	931.80	ÁREA TÉCNICA
T-00-1	CIRCULACIÓN TÉCNICA	108.98	ÁREA TÉCNICA
T-13	CUARTO DE BOMBAS DE SUMINISTRO DE AGUA	44.18	ÁREA TÉCNICA
T-14-1	TANQUE DE SUMINISTRO DE AGUA	28.46	ÁREA TÉCNICA
T-14-2	TANQUE DE SUMINISTRO DE AGUA	27.49	ÁREA TÉCNICA
T-15	TANQUE SISTEMA DE EXTINCIÓN DE INCENDIOS (RCI)	59.90	ÁREA TÉCNICA
T-16	CUARTO DE BOMBAS PARA ROCIADORES	36.24	ÁREA TÉCNICA
T-17	TANQUE RECUPERACIÓN AGUAS LLUVIAS	17.84	ÁREA TÉCNICA
T-18	CUARTO DE BOMBAS DE RECUPERACIÓN DE AGUAS LLUVIAS Y EQUIPO DE FILTRACIÓN	69.24	ÁREA TÉCNICA
T-19-1	TANQUE DE AGUA TRATADA	20.50	ÁREA TÉCNICA
T-19-2	TANQUE DE AGUA TRATADA	22.79	ÁREA TÉCNICA
T-20-L-1	MEDIDORES (LUZ)	16.10	ÁREA TÉCNICA
T-20-W-1	MEDIDORES (AGUA)	14.93	ÁREA TÉCNICA
T-21-1	ÁREA DE INSPECCIÓN	23.32	ÁREA TÉCNICA
T-21-2	ÁREA DE INSPECCIÓN	25.12	ÁREA TÉCNICA
T-21-3	ÁREA DE INSPECCIÓN	7.33	ÁREA TÉCNICA
T-21-4	ÁREA DE INSPECCIÓN	10.02	ÁREA TÉCNICA
T-25-1	NODO DE ACCESO DE TELECOMUNICACIONES	4.74	ÁREA TÉCNICA
ZDR-01	ZONA DE REFUGIO (PMR)	8.51	ZONA DE REFUGIO
ZDR-02	ZONA DE REFUGIO (PMR)	3.65	ZONA DE REFUGIO
TOTAL NIVEL SÓTANO EDIFICIO ASCENDENTE		3644.40	

TABLA DE ÁREAS ÚTILES POR DEPARTAMENTO (NIVEL SÓTANO_EDIFICIO ASCENDENTE)

DEPARTAMENTO	ÁREA (m²)
EDIFICIO ASCENDENTE	
ARQ_PL_00.4_ACCESO	
	424.37
SERVICIOS ADICIONALES - ÁREA NO PAGA	0.00
ZONA DE REFUGIO	0.00
ÁREA NO PAGA	0.00
ÁREA OPERATIVA	0.00
ÁREA PÚBLICA	0.00
ÁREA TÉCNICA	0.00
ARQ_PL_00_SÓTANO	
SERVICIOS ADICIONALES - ÁREA NO PAGA	427.08
ZONA DE REFUGIO	12.15
ÁREA NO PAGA	575.89
ÁREA OPERATIVA	95.48
ÁREA PÚBLICA	1064.81
ÁREA TÉCNICA	1468.98
TOTAL NIVEL SÓTANO EDIFICIO ASCENDENTE	4068.77

TABLA DE CICLO-PARQUEADEROS ESPECÍFICA

DESCRIPCIÓN	CANTIDAD (und)	USUARIOS
ARQ_PL_00_SÓTANO		
BICIPARQUEADERO ASISTIDO EN ACERO INOXIDABLE ASTM A240, a=0.70m X l=1.20m, h=1.70m.	1	EMPLEADOS
BICIPARQUEADERO DE COLGAR, 1 PUESTO, a=1.20m X l=0.70m, h=2.40m. ACABADO EN PINTURA ELECTROSTÁTICA COLOR RAL9005 "NEGRO INTENSO".	2	EMPLEADOS
BICIPARQUEADERO DE COLGAR, 2 PUESTOS, a=1.20m X l=0.70m, h=2.40m. ACABADO EN PINTURA ELECTROSTÁTICA COLOR RAL9005 "NEGRO INTENSO".	2	EMPLEADOS
EMPLEADOS	5	
BICIPARQUEADERO ASISTIDO EN ACERO INOXIDABLE ASTM A240, a=0.70m X l=1.20m, h=1.70m.	50	VISITANTE
BICIPARQUEADERO DE COLGAR DE 6 PUESTOS EN ACERO, a=1.20m X l=2.10m, h=2.40m. ACABADO EN PINTURA ELECTROSTÁTICA COLOR RAL9005 "NEGRO INTENSO".	270	VISITANTE
BICIPARQUEADERO DE COLGAR, 1 PUESTO, a=1.20m X l=0.70m, h=2.40m. ACABADO EN PINTURA ELECTROSTÁTICA COLOR RAL9005 "NEGRO INTENSO".	24	VISITANTE
BICIPARQUEADERO DE COLGAR, 2 PUESTOS, a=1.20m X l=0.70m, h=2.40m. ACABADO EN PINTURA ELECTROSTÁTICA COLOR RAL9005 "NEGRO INTENSO".	166	VISITANTE
VISITANTE	510	
TOTAL CUPOS	515	

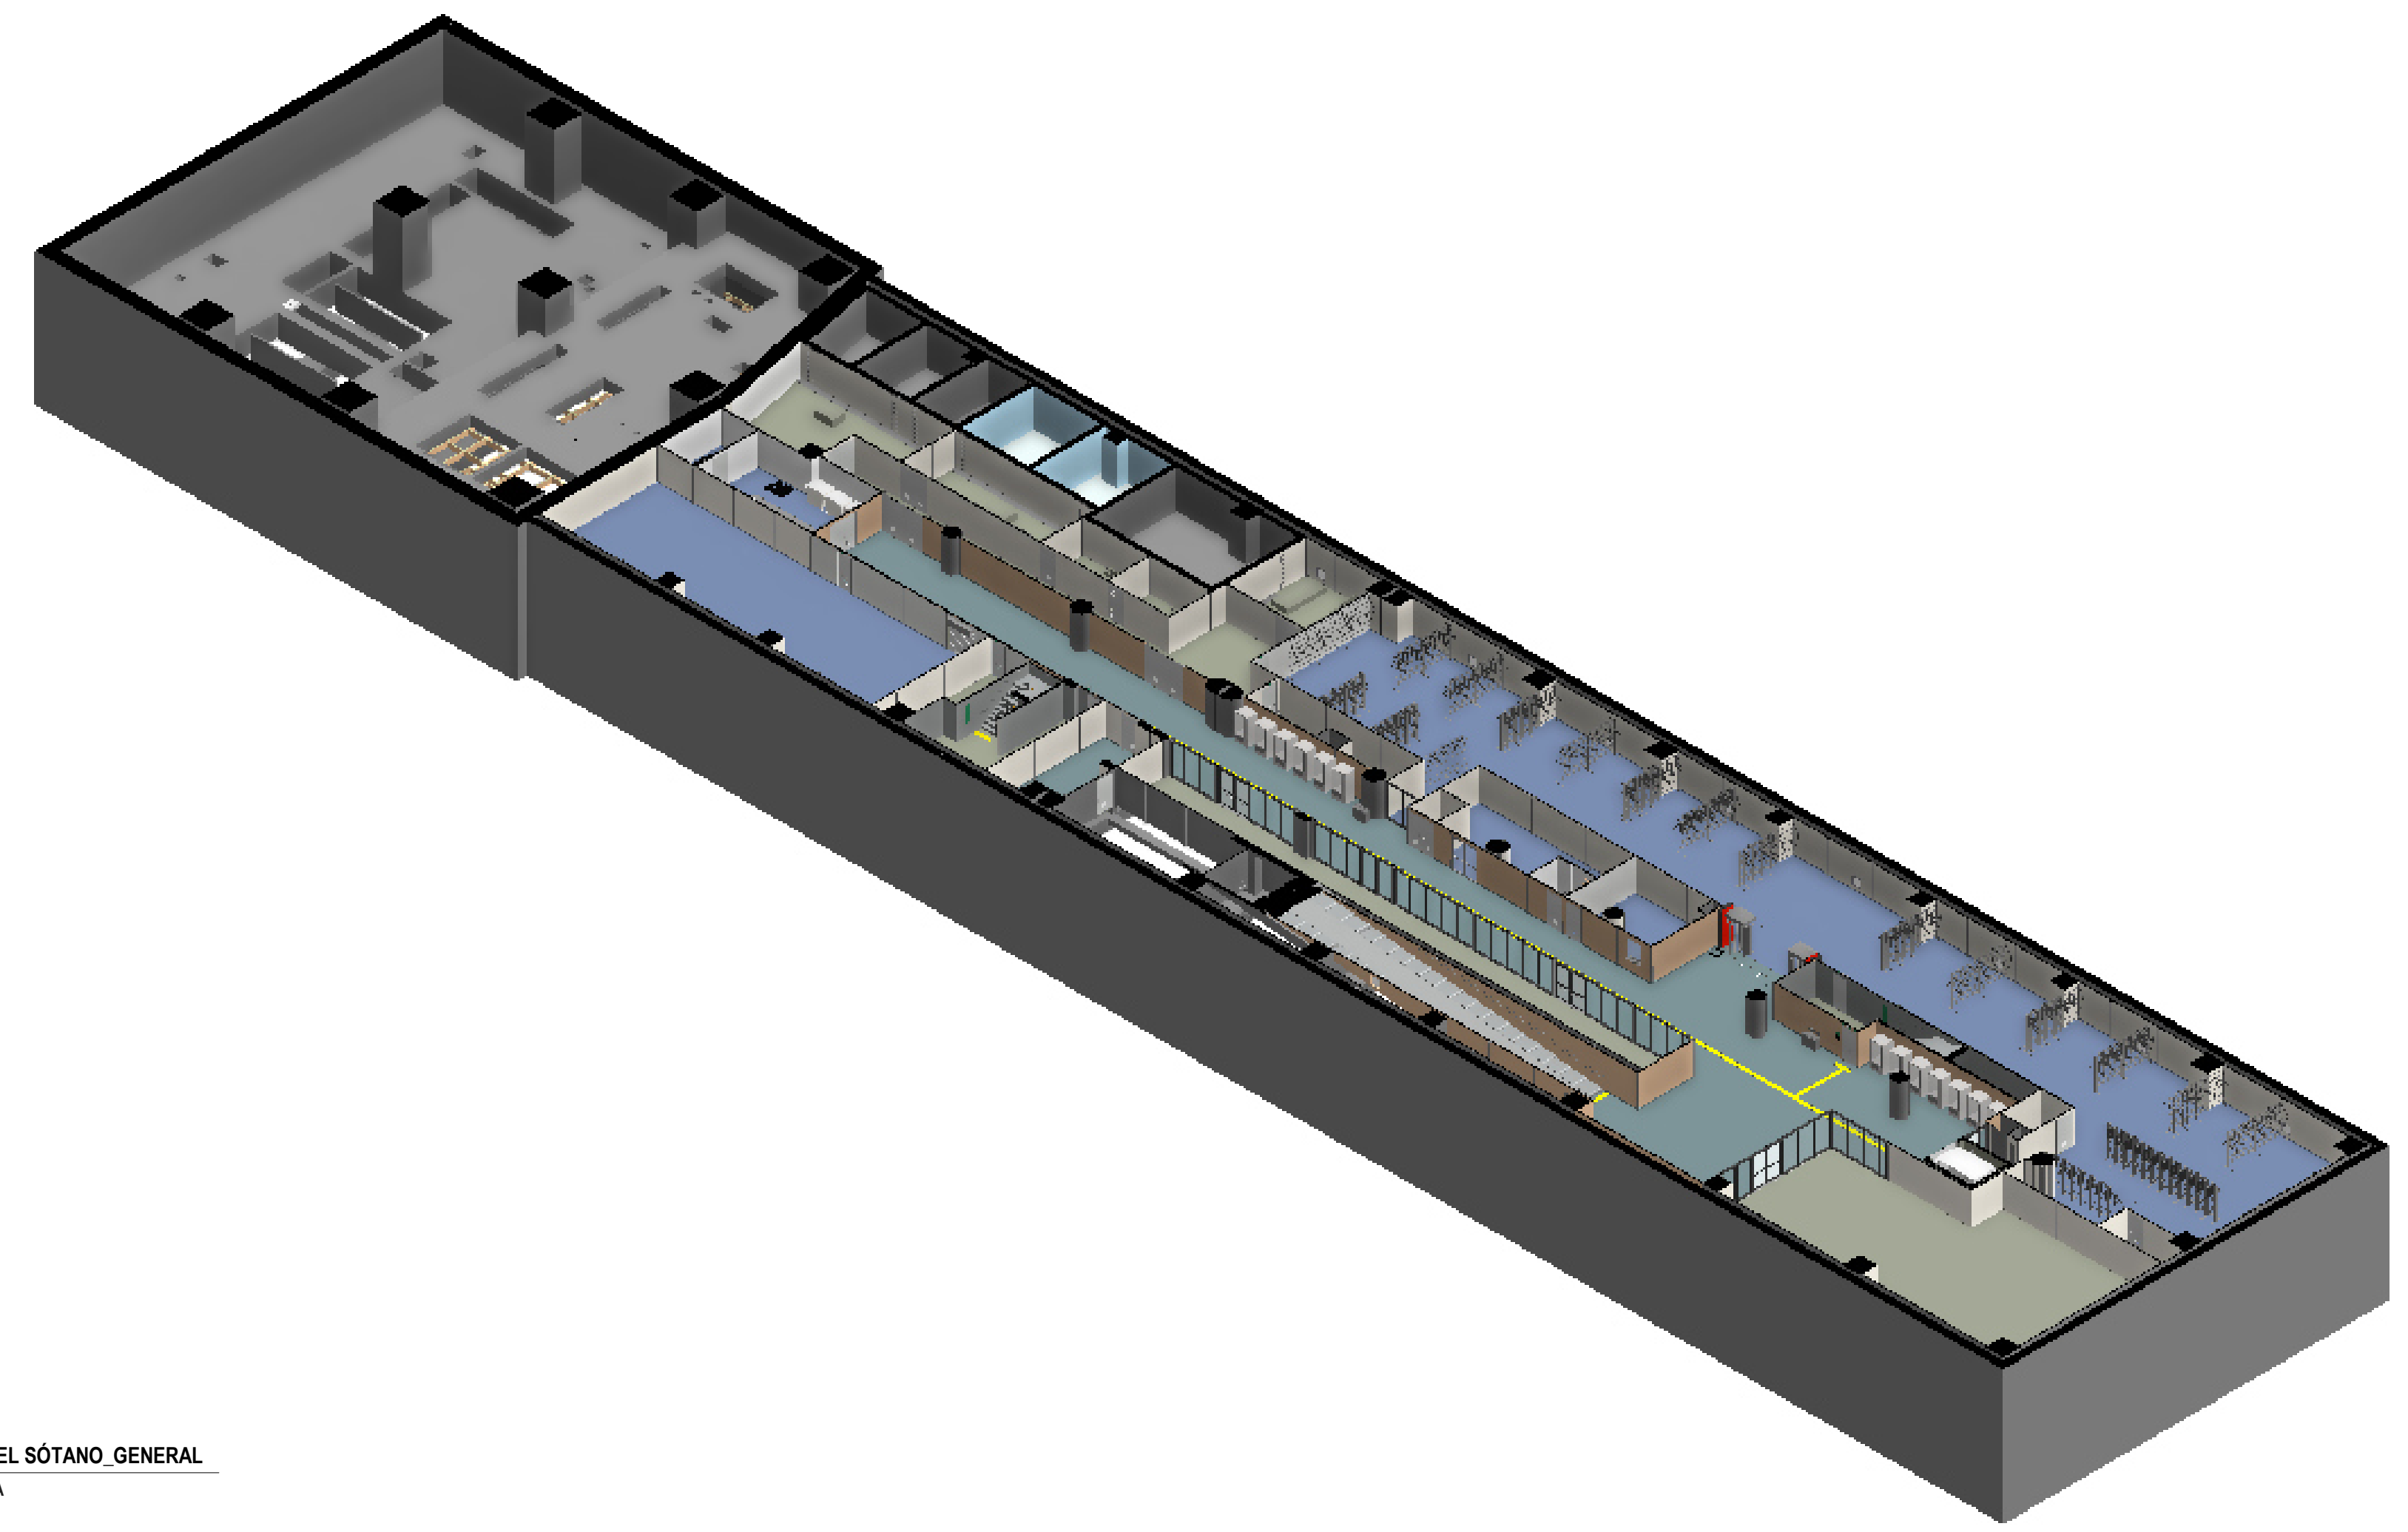

1 3D_NIVEL SÓTANO_GENERAL
ESC: N/A

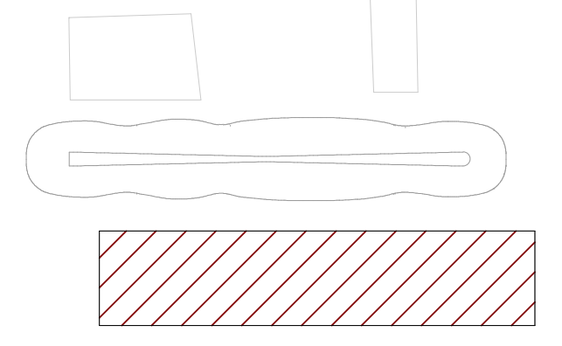

PLANO CLAVE ESTACIÓN 15

VÁLIDO PARA CONSTRUCCIÓN
31-03-26

LOCALIZACIÓN

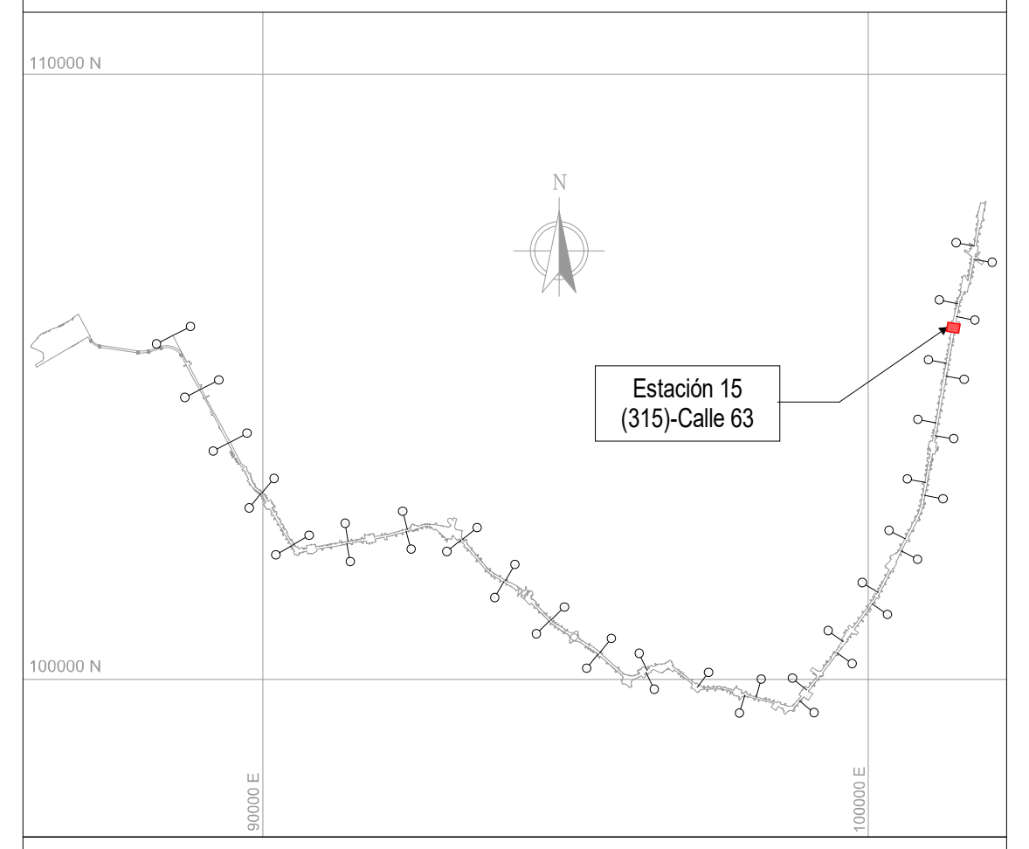

NOTAS

01 TODAS LAS DIMENSIONES ESTÁN CONFIGURADAS EN METROS A MENOS QUE SE INDIQUE UNA UNIDAD DE MEDIDA DIFERENTE.

02 TODAS LAS MEDIDAS, UBICACIÓN Y NIVELES DEBEN VERIFICARSE EN EL LUGAR DE CONSTRUCCIÓN.

03 EL NIVEL DE ACCESO AL EDIFICIO PL 01 CORRESPONDE AL +0,00 DE LA ESTACIÓN Y REFERENCIA AL NIVEL 2569.10 M.S.N.M.

04 LOS NOMBRES ESPECÍFICOS DE LAS ÁREAS PUEDEN SER CONSULTADAS EN EL PLANO NO. 3 Ó EN LAS VISTAS EN PLANTA.

05 LOS COLORES QUE SE MUESTRAN EN LOS PLANOS COMO PROYECCIÓN DE ELEMENTOS ARQUITECTÓNICOS COMO CUBIERTAS, FACHADAS, MUROS, ETC. NO REPRESENTAN LA MATERIALIDAD Y REALIDAD DE ACABADOS DEL PROYECTO, SOLO SON INDICATIVOS PARA REALIZAR UNA CORRECTA LECTURA DE LA PLANIMETRÍA.

06 SE DEBEN REVISAR LOS NIVELES ESTRUCTURALES PARA NIVEL DE ACCESO PL_01 Y SUBNIVELES, PL_02 (INTERMEDIO), PL_03 (PLATAFORMA) CON LA PLANIMETRÍA DE PLACAS ESTRUCTURALES EN LOS ENTREGABLES L1T1-1300-415-CON-ED-EST-PL-0040, 41, 126, 86 RESPECTIVAMENTE. EL NIVEL ESTRUCTURAL (NE) REFERENCIA LOS ESPACIOS DONDE SE DEBE ACONDICIONAR EL ACABADO DE PISO SEGÚN CORRESPONDA, CON LOS NIVELES DE PISO TERMINADO (NPT). LOS NIVELES PROYECTADOS DE EMPATE (NPE) EN LAS ÁREAS DE SERVICIOS ADICIONALES, REFERENCIAN LA ADECUACIÓN DE LOS DESNIVELES EN ESTAS ÁREAS; QUEDA COMO RESPONSABILIDAD DEL LOCATARIO DEFINIR Y ACONDICIONAR ESTE ACABADO DE PISO (NPE) EN LÍNEA CON EL NIVEL (NPT) DE ESPACIOS COLINDANTES. EL NIVEL ESTRUCTURAL (NE) SE ENCUENTRA A (- 0.10M) POR DEBAJO DE LOS NIVELES DE PISO TERMINADO (NPT) Y LOS NIVELES PROYECTADOS DE EMPATE (NPE) MARCADOS EN LA PLANIMETRÍA.

07 LOS MODELOS L1T1-5110-315-CON-ED-CIV-MO-0001.RVT, L1T1-5110-315-CON-ED-EST-MO-0001.RVT Y PLANO L1T1-5160-315-CON-ED-ARQ-PL-0001_V00 CORRESPONDEN AL DESARROLLO DE LA ARQUITECTURA U OBRA CIVIL DE LA SER ELABORADOS POR LA ESPECIALIDAD DE SAE (SISTEMA DE ALIMENTACIÓN ELÉCTRICA). TODO LO CORRESPONDIENTE A LA SER DEBE SER VERIFICADO EN LOS ENTREGABLES DE DICHA DISCIPLINA.

- ARQ_PL_-00.1 = SER 3 / NPT -11.00m
- ARQ_PL_00 = SÓTANO / NPT -7.15m
- ARQ_PL_00.1 = ACCESO / NPT -2.60m
- ARQ_PL_00.2 = ACCESO / NPT -1.85m
- ARQ_PL_00.3 = ACCESO / NPT -1.50m
- ARQ_PL_00.4 = ACCESO / NPT -1.45m
- ARQ_PL_00.5 = ACCESO / NPT -1.27m
- ARQ_PL_00.6 = ACCESO / NPT -1.00m
- ARQ_PL_00.7 = ACCESO / NPT -0.60m
- ARQ_PL_00.8 = ACCESO / NPT -0.45m
- ARQ_PL_00.9 = ACCESO / NPT -0.30m
- ARQ_PL_01 = ACCESO / NPT 0.00m
- ARQ_PL_01.1 = ACCESO / NPT 0.30m
- ARQ_PL_02 = INTERMEDIO / NPT 6.60m
- ARQ_PL_02.2 = TOPE DE RIEL (TOR) / NPT 14.20m
- ARQ_PL_03 = PLATAFORMA / NPT 15.34m
- ARQ_PL_03 = CUBIERTA EDIFICIOS ACCESO / NPT 21.94m
- ARQ_PL_05 = CUBIERTA NAVE CENTRAL / NPT 24.60m

CONVENCIONES

🟩	SERVICIOS ADICIONALES - ÁREA NO PAGA	🟨	ÁREA NO PAGA
🟩	SERVICIOS ADICIONALES - ÁREA PAGA	🟦	ÁREA OPERATIVA
🟩	SERVICIO PÚBLICO	🟨	ÁREA PAGA
🟦	ZONA DE REFUGIO	🟦	ÁREA PÚBLICA
🟥	ÁREA CULTURAL	⬜	ÁREA TÉCNICA
		🟧	ÁREA BRT

No.	PLANOS DE REFERENCIA	REV.
No.	**MODELO BIM DE REFERENCIA**	**REV.**
1	L1T1-1100-215-CON-ED-EST-MO-0001.rvt	V00
2	L1T1-1100-216-CON-ED-EST-MO-0001.rvt	V00
3	L1T1-1100-315-CON-ED-EST-MO-0001.rvt	V00
4	L1T1-1150-215-CON-ED-EST-MO-0001.rvt	V00
5	L1T1-1150-216-CON-ED-EST-MO-0001.rvt	V00
6	L1T1-1150-315-CON-ED-EST-MO-0001.rvt	V00
7	L1T1-1200-315-CON-ED-EST-MO-0001.rvt	V00
8	L1T1-1300-415-CON-ED-EST-MO-0001.rvt	V00
9	L1T1-1300-415-CON-ED-EST-MO-0002.rvt	V00
10	L1T1-1300-415-CON-ED-EST-MO-0003.rvt	V00
11	L1T1-1310-415-CON-ED-EST-MO-0001.rvt	V00
12	L1T1-1410-315-CON-ED-MEC-MO-0001.rvt	V00
13	L1T1-1420-315-CON-ED-MEC-MO-0001.rvt	V00
14	L1T1-2320-590-CON-ED-EST-MO-0001.rvt	V00
15	L1T1-2320-590-CON-ED-EST-MO-0002.rvt	V00
16	L1T1-2330-590-CON-ED-ARQ-MO-0001.rvt	V00
17	L1T1-5110-315-CON-ED-EST-MO-0001.rvt	V00
18	L1T1-5160-315-CON-ED-EST-MO-0001.rvt	V00
19	L1T1-5160-315-CON-ED-ARQ-MO-0001.rvt	V00
20	L1T1-5300-315-CON-ED-MEC-MO-0001.rvt	V00
21	L1T1-5600-315-CON-ED-INS-MO-0001.rvt	V00
22	L1T1-1330-415-CON-ED-ARQ-MO-0011.rvt	V00
23	L1T1-1330-415-CON-ED-ARQ-MO-0012.rvt	V00
24	L1T1-1330-415-CON-ED-ARQ-MO-0013.rvt	V00
No.	**PAQUETE DE TRABAJO DE REFERENCIA**	**REV.**
1	XREF-URBANISM_CONTEXT_ST15.rvt	
2	XREF-SECONDARY-STRUCTURE-ST15.rvt	

0 2 10m
1:200

METRO BOGOTÁ
Consorcio Consultores PMO Bogotá
CONSORCIO SUPERVISOR PLMB

DISEÑÓ:
REN ZHENHUA
Licencia de Arq.nivel I (China): 1101735-614

APROBÓ:
DIEGO ERNESTO DUEÑAS
Mat.: 25202-53876 CND

REVISÓ:
CARLOS MAURICIO BARRETO BARBOSA
Mat.: A4012012-14139353

DIBUJÓ:
EQUIPO CHEC

REVISIÓN No.	FECHA	DESCRIPCIÓN	REVISÓ	APROBÓ	APROBACIÓN CLIENTE
V01	31/03/2026	EMITIDO PARA CONSTRUCCIÓN	C.M.B.B	D.E.D	
V00	13/12/2024	REVISIÓN NO OBJETADA - EMITIDO PARA CONSTRUCCIÓN	F.B.R	E.O.M	
VFF	21/08/2024	EMITIDO PARA REVISIÓN Y COMENTARIOS DEL CLIENTE E INTERVENTORÍA - INCLUYE COMENTARIOS /(AJUSTES V3)	F.B.R	E.O.M	
VEE	02/05/2024	EMITIDO PARA REVISIÓN Y COMENTARIOS DEL CLIENTE E INTERVENTORÍA - INCLUYE COMENTARIOS /(AJUSTES V2)	F.B.R	E.O.M	
VDD	18/12/2022	EMITIDO PARA REVISIÓN Y COMENTARIOS DEL CLIENTE E INTERVENTORÍA - INCLUYE COMENTARIOS /(AJUSTES)	J.E.M	M.B.M	
VCC	02/06/2022	EMITIDO PARA REVISIÓN Y COMENTARIOS DEL CLIENTE E INTERVENTORÍA - INCLUYE COMENTARIOS /(ENTREGA 90%)	J.E.M	M.B.M	
VBB	06/12/2021	EMITIDO PARA REVISIÓN Y COMENTARIOS DEL CLIENTE E INTERVENTORÍA	J.E.M	M.B.M	
VA0	30/06/2021	EMITIDO PARA COMENTARIOS INTERNOS - EMISIÓN PRELIMINAR PARA COMENTARIOS	J.E.M	M.B.M	

METRO LÍNEA 1

METRO LÍNEA 1
CONTRATO DE CONCESIÓN No. 163 DE 2019

PROYECTO PRIMERA LÍNEA DEL METRO DE BOGOTÁ - TRAMO 1

DIRECTOR DE INTERVENTORÍA:
JAVIER DESCARGA N.
Mat.:25202-68697 CND

ESPECIALISTA INTERVENTORÍA:
CARLOS ALBERTO HOYOS SOTO
Mat.:A25072000-14251682

FECHA:
MARZO 2026

INFRAESTRUCTURA VIAL

ARQUITECTURA

ESTACIÓN METRO 15 - (CALLE 63)
EDIFICIO ASCENDENTE
VISTA EN PLANTA Y 3D - NIVEL SÓTANO

PLANCHA No: L1T1-0000-315-CON-ED-ARQ-PL-0001_04_V01
ARCHIVO: L1T1-0000-315-CON-ED-ARQ-MO-0001_V00.rvt
ESCALA: INDICADA
FECHA: JUNIO 2021
REVISIÓN No.: V01
PLANO No.: 04 DE 94