L1T1-CON-CAL-FR-0120 - B1 : 1000x707mm

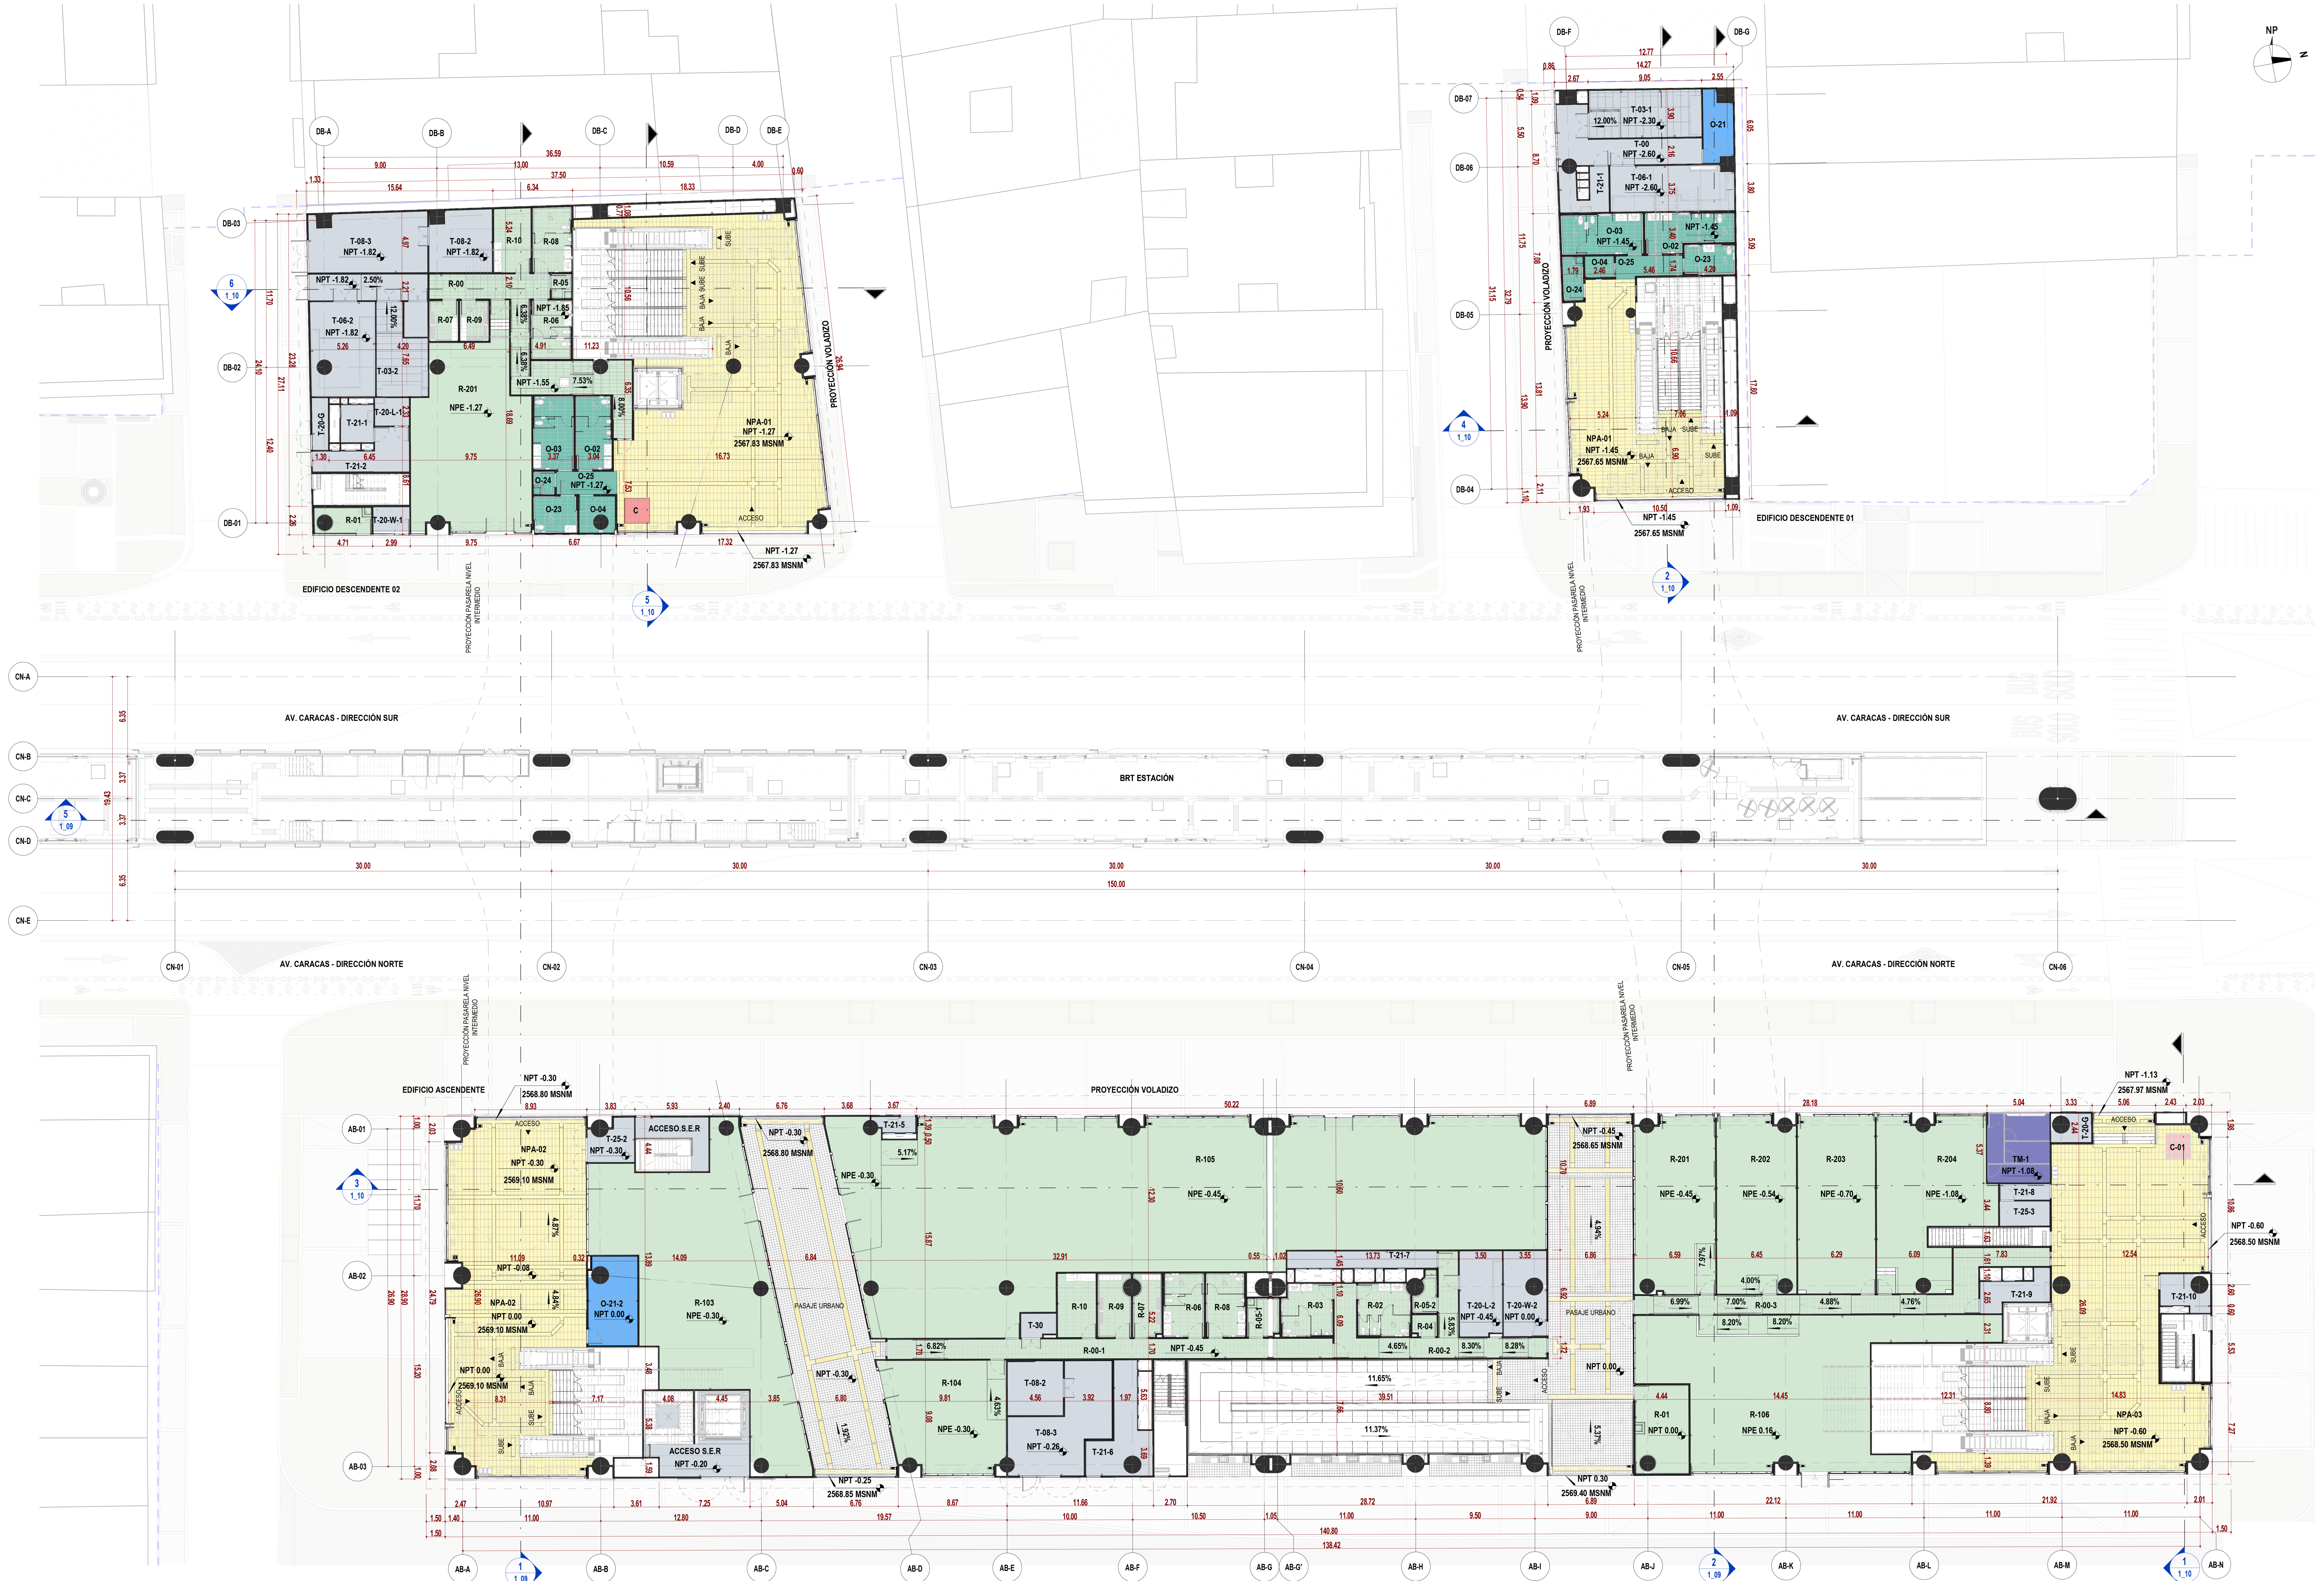

2 NIVEL ACCESO_GENERAL
ESC: 1 : 200

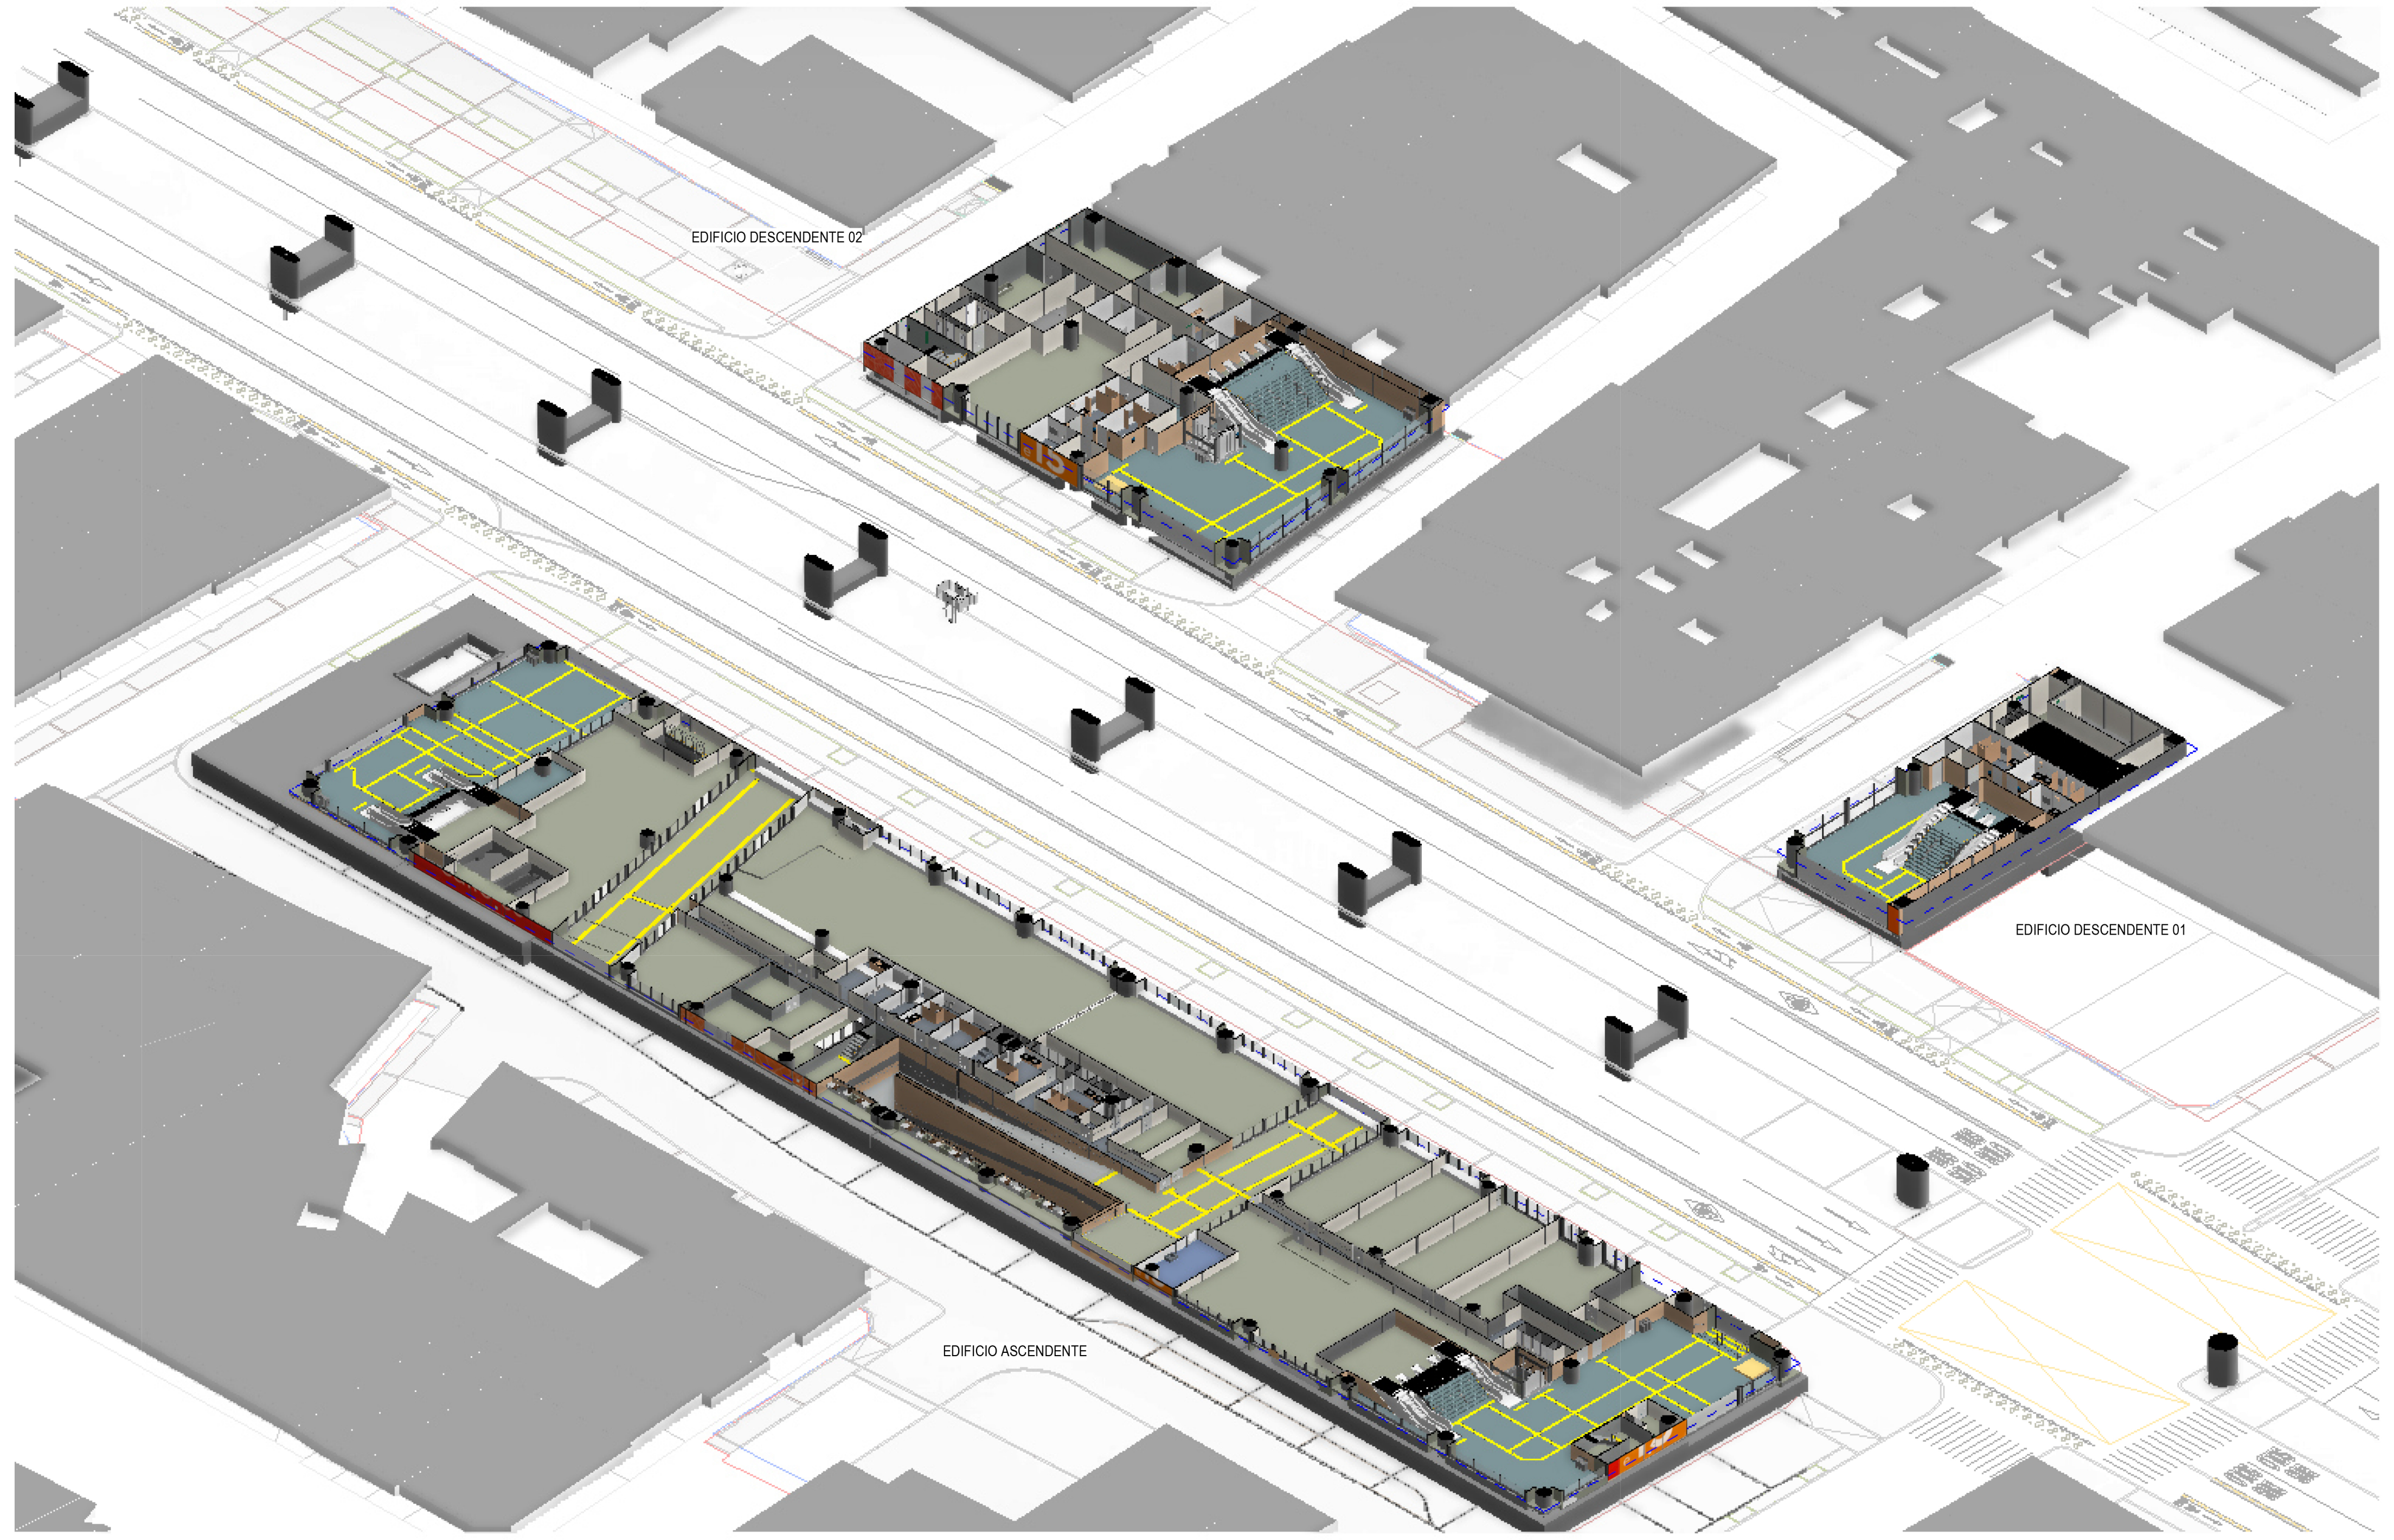

1 3D_NIVEL ACCESO_GENERAL
ESC: N/A

TABLA DE ÁREAS ÚTILES (NIVEL ACCESO)

CÓDIGO	NOMBRE	ÁREA (m²)	DEPARTAMENTO
EDIFICIO ASCENDENTE			
ARQ_PL_00.5_ACCESO			
T-20-G	MEDIDORES (GAS)	5.45	ÁREA TÉCNICA
NPA-03	ÁREA NO PAGA	318.36	ÁREA NO PAGA
R-204	SERVICIOS ADICIONALES - ÁREA DE COMIDAS	105.06	SERVICIOS ADICIONALES - ÁREA NO PAGA
TM-1	ÁREA DE TAQUILLAS BRT	27.33	ÁREA DE TAQUILLAS BRT
		456.20	
ARQ_PL_00.6_ACCESO			
R-203	SERVICIOS ADICIONALES - ÁREA DE COMIDAS	87.37	SERVICIOS ADICIONALES - ÁREA NO PAGA
		87.37	
ARQ_PL_00.7_ACCESO			
C-01	ÁREAS DE USO CULTURAL	4.00	ÁREA CULTURAL
T-21-10	ÁREA DE INSPECCIÓN	8.91	ÁREA TÉCNICA
T-25-3	NODO DE ACCESO DE TELECOMUNICACIONES	7.79	ÁREA TÉCNICA
R-202	SERVICIOS ADICIONALES - ÁREA DE COMIDAS	86.57	SERVICIOS ADICIONALES - ÁREA NO PAGA
R-00-3	SERVICIOS ADICIONALES - CORREDOR OPERATIVO	57.29	SERVICIOS ADICIONALES - ÁREA NO PAGA
T-21-9	ÁREA DE INSPECCIÓN	11.85	ÁREA TÉCNICA
T-21-8	ÁREA DE INSPECCIÓN	5.04	ÁREA TÉCNICA
		181.46	
ARQ_PL_00.8_ACCESO			
T-21-7	ÁREA DE INSPECCIÓN	15.98	ÁREA TÉCNICA
T-20-L-2	MEDIDORES (LUZ)	22.75	ÁREA TÉCNICA
T-21-5	ÁREA DE INSPECCIÓN	3.85	ÁREA TÉCNICA
R-04	SERVICIOS ADICIONALES - CONTROL DE ACCESO BAÑOS PÚBLICOS	3.31	SERVICIOS ADICIONALES - ÁREA NO PAGA
R-02	SERVICIOS ADICIONALES - BAÑO PÚBLICO DE MUJERES	17.08	SERVICIOS ADICIONALES - ÁREA NO PAGA
R-03	SERVICIOS ADICIONALES - BAÑO PÚBLICO DE HOMBRES	16.42	SERVICIOS ADICIONALES - ÁREA NO PAGA
R-05-2	SERVICIOS ADICIONALES - CUARTO DE LIMPIEZA	4.93	SERVICIOS ADICIONALES - ÁREA NO PAGA
R-08	SERVICIOS ADICIONALES - BAÑOS EMPLEADOS HOMBRES	15.59	SERVICIOS ADICIONALES - ÁREA NO PAGA
R-06	SERVICIOS ADICIONALES - BAÑOS EMPLEADOS MUJERES	16.05	SERVICIOS ADICIONALES - ÁREA NO PAGA
R-07	SERVICIOS ADICIONALES - VESTIDORES EMPLEADOS MUJERES	10.71	SERVICIOS ADICIONALES - ÁREA NO PAGA
R-10	SERVICIOS ADICIONALES - SALA DE EMPLEADOS	15.81	SERVICIOS ADICIONALES - ÁREA NO PAGA
R-09	SERVICIOS ADICIONALES - VESTIDORES EMPLEADOS HOMBRES	12.74	SERVICIOS ADICIONALES - ÁREA NO PAGA
R-05-1	SERVICIOS ADICIONALES - CUARTO DE LIMPIEZA	7.67	SERVICIOS ADICIONALES - ÁREA NO PAGA
R-00-1	SERVICIOS ADICIONALES - CORREDOR OPERATIVO	56.42	SERVICIOS ADICIONALES - ÁREA NO PAGA
R-201	SERVICIOS ADICIONALES - ÁREA DE COMIDAS	87.07	SERVICIOS ADICIONALES - ÁREA NO PAGA
R-105	SERVICIOS ADICIONALES - ÁREA DE SERVICIO	704.48	SERVICIOS ADICIONALES - ÁREA NO PAGA
R-00-2	SERVICIOS ADICIONALES - CORREDOR OPERATIVO	45.70	SERVICIOS ADICIONALES - ÁREA NO PAGA
T-30	SISTEMA PROTECCIÓN CONTRA INCENDIO ENEL	5.05	ÁREA TÉCNICA
		1061.61	
ARQ_PL_00.9_ACCESO			
NPA-02	ÁREA NO PAGA	269.59	ÁREA NO PAGA
T-08-3	CENTRO DE TRANSFORMACIÓN ENEL-CODENSA (CT)_CUARTO MEDIA TENSIÓN	49.39	ÁREA TÉCNICA
T-21-6	ÁREA DE INSPECCIÓN	27.77	ÁREA TÉCNICA
R-103	SERVICIOS ADICIONALES - ÁREA DE SERVICIO	241.79	SERVICIOS ADICIONALES - ÁREA NO PAGA
R-104	SERVICIOS ADICIONALES - ÁREA DE SERVICIO	79.97	SERVICIOS ADICIONALES - ÁREA NO PAGA
R-106	SERVICIOS ADICIONALES - ÁREA DE SERVICIO	226.87	SERVICIOS ADICIONALES - ÁREA NO PAGA
SER-3-A-2	ACCESO SER 3	55.22	ÁREA TÉCNICA
SER-3-A-1	ACCESO SER 3	25.13	ÁREA TÉCNICA
T-25-2	NODO DE ACCESO DE TELECOMUNICACIONES	10.65	ÁREA TÉCNICA
T-08-2	CENTRO DE TRANSFORMACIÓN ENEL-CODENSA (CT)_CUARTO BAJA TENSIÓN	19.22	ÁREA TÉCNICA
		1005.58	
ARQ_PL_01_ACCESO			
O-21-2	ALMACENAMIENTO DE LA ESTACIÓN	26.18	ÁREA OPERATIVA
T-20-W-2	MEDIDORES (AGUA)	21.75	ÁREA TÉCNICA
R-01	SERVICIOS ADICIONALES - CUARTO DE BASURAS PARA METRO	28.90	SERVICIOS ADICIONALES - ÁREA NO PAGA
		76.82	
EDIFICIO ASCENDENTE		2869.04	
EDIFICIO DESCENDENTE 01			
ARQ_PL_00.1_ACCESO			
T-00	CIRCULACIÓN TÉCNICA	29.90	ÁREA TÉCNICA
T-06-1	LOCAL SECUNDARIO DE TABLEROS	35.13	ÁREA TÉCNICA
T-21-1	ÁREA DE INSPECCIÓN	10.94	ÁREA TÉCNICA
O-21	ALMACENAMIENTO DE LA ESTACIÓN	12.46	ÁREA OPERATIVA
T-03-1	LOCAL SECUNDARIO DE TELECOMUNICACIONES	33.92	ÁREA TÉCNICA
		122.37	
ARQ_PL_00.4_ACCESO			
NPA-01	ÁREA NO PAGA	127.07	ÁREA NO PAGA
O-03	BAÑOS PÚBLICOS DE MUJERES	20.79	SERVICIO PÚBLICO
O-02	BAÑOS PÚBLICOS DE HOMBRES	19.20	SERVICIO PÚBLICO
O-23	BAÑO PÚBLICO - FAMILIAR	9.50	SERVICIO PÚBLICO
O-24	CUARTO DE LIMPIEZA DE BAÑOS PÚBLICOS	5.67	SERVICIO PÚBLICO
O-04	CONTROL DE ACCESO BAÑOS PÚBLICOS	4.03	SERVICIO PÚBLICO
O-25	BAÑO PÚBLICO - CORREDOR OPERACIONAL	9.01	SERVICIO PÚBLICO
		195.27	
EDIFICIO DESCENDENTE 01		317.64	
EDIFICIO DESCENDENTE 02			
ARQ_PL_00.2_ACCESO			
T-03-2	LOCAL SECUNDARIO DE TELECOMUNICACIONES	25.10	ÁREA TÉCNICA
T-08-3	CENTRO DE TRANSFORMACIÓN ENEL-CODENSA (CT)_CUARTO MEDIA TENSIÓN	44.14	ÁREA TÉCNICA
T-06-2	LOCAL SECUNDARIO DE TABLEROS	37.63	ÁREA TÉCNICA
T-00	CIRCULACIÓN TÉCNICA	19.77	ÁREA TÉCNICA
R-06	SERVICIOS ADICIONALES - BAÑOS EMPLEADOS MUJERES	14.81	SERVICIOS ADICIONALES - ÁREA NO PAGA
R-08	SERVICIOS ADICIONALES - BAÑOS EMPLEADOS HOMBRES	16.04	SERVICIOS ADICIONALES - ÁREA NO PAGA
R-05	SERVICIOS ADICIONALES - CUARTO DE LIMPIEZA	3.13	SERVICIOS ADICIONALES - ÁREA NO PAGA
R-10	SERVICIOS ADICIONALES - SALA DE EMPLEADOS	19.22	SERVICIOS ADICIONALES - ÁREA NO PAGA
R-00	SERVICIOS ADICIONALES - CORREDOR OPERATIVO	56.96	SERVICIOS ADICIONALES - ÁREA NO PAGA
T-30	SISTEMA PROTECCIÓN CONTRA INCENDIO ENEL	5.26	ÁREA TÉCNICA
R-07	SERVICIOS ADICIONALES - VESTIDORES EMPLEADOS MUJERES	7.35	SERVICIOS ADICIONALES - ÁREA NO PAGA
R-09	SERVICIOS ADICIONALES - VESTIDORES EMPLEADOS HOMBRES	7.35	SERVICIOS ADICIONALES - ÁREA NO PAGA
T-08-2	CENTRO DE TRANSFORMACIÓN ENEL-CODENSA (CT)_CUARTO BAJA TENSIÓN	23.76	ÁREA TÉCNICA
		280.52	
ARQ_PL_00.3_ACCESO			
T-21-2	ÁREA DE INSPECCIÓN	18.23	ÁREA TÉCNICA
T-20-G	MEDIDORES (GAS)	5.35	ÁREA TÉCNICA
T-21-1	ÁREA DE INSPECCIÓN	7.75	ÁREA TÉCNICA
T-20-L-1	MEDIDORES (LUZ)	6.09	ÁREA TÉCNICA
		37.42	
ARQ_PL_00.4_ACCESO			
R-01	SERVICIOS ADICIONALES - CUARTO DE BASURAS PARA METRO	9.26	SERVICIOS ADICIONALES - ÁREA NO PAGA
		9.26	
ARQ_PL_00.5_ACCESO			
NPA-01	ÁREA NO PAGA	296.10	ÁREA NO PAGA
T-20-W-1	MEDIDORES (AGUA)	5.51	ÁREA TÉCNICA
C	ÁREAS DE USO CULTURAL	4.00	ÁREA CULTURAL
O-02	BAÑOS PÚBLICOS DE HOMBRES	16.33	SERVICIO PÚBLICO
O-03	BAÑOS PÚBLICOS DE MUJERES	18.50	SERVICIO PÚBLICO
O-23	BAÑO PÚBLICO - FAMILIAR	11.11	SERVICIO PÚBLICO
O-04	CONTROL DE ACCESO BAÑOS PÚBLICOS	7.31	SERVICIO PÚBLICO
O-24	CUARTO DE LIMPIEZA DE BAÑOS PÚBLICOS	3.08	SERVICIO PÚBLICO
R-201	SERVICIOS ADICIONALES - ÁREA DE COMIDAS	132.37	SERVICIOS ADICIONALES - ÁREA NO PAGA
O-25	BAÑO PÚBLICO - CORREDOR OPERACIONAL	8.86	SERVICIO PÚBLICO
		503.17	
EDIFICIO DESCENDENTE 02		830.36	
TOTAL NIVEL ACCESO		4017.04	

TABLA DE ÁREAS ÚTILES POR DEPARTAMENTO (NIVEL ACCESO)

DEPARTAMENTO	ÁREA (m²)
	620.61
SERVICIO PÚBLICO	133.39
SERVICIOS ADICIONALES - ÁREA NO PAGA	2194.25
ÁREA CULTURAL	8.00
ÁREA DE TAQUILLAS BRT	27.33
ÁREA NO PAGA	1011.13
ÁREA OPERATIVA	38.64
ÁREA TÉCNICA	604.30
TOTAL NIVEL ACCESO	4637.65

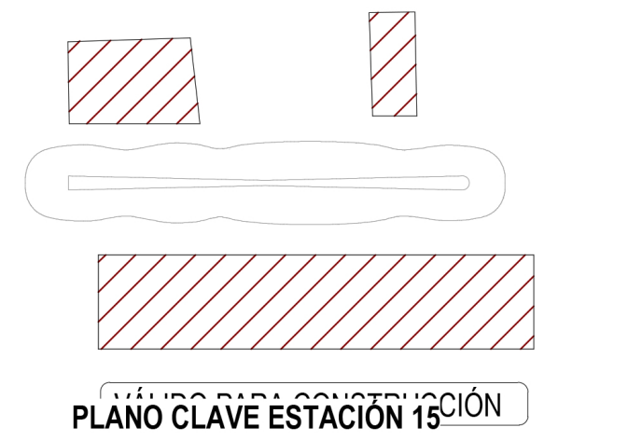

PLANO CLAVE ESTACIÓN 15
31-03-26

LOCALIZACIÓN

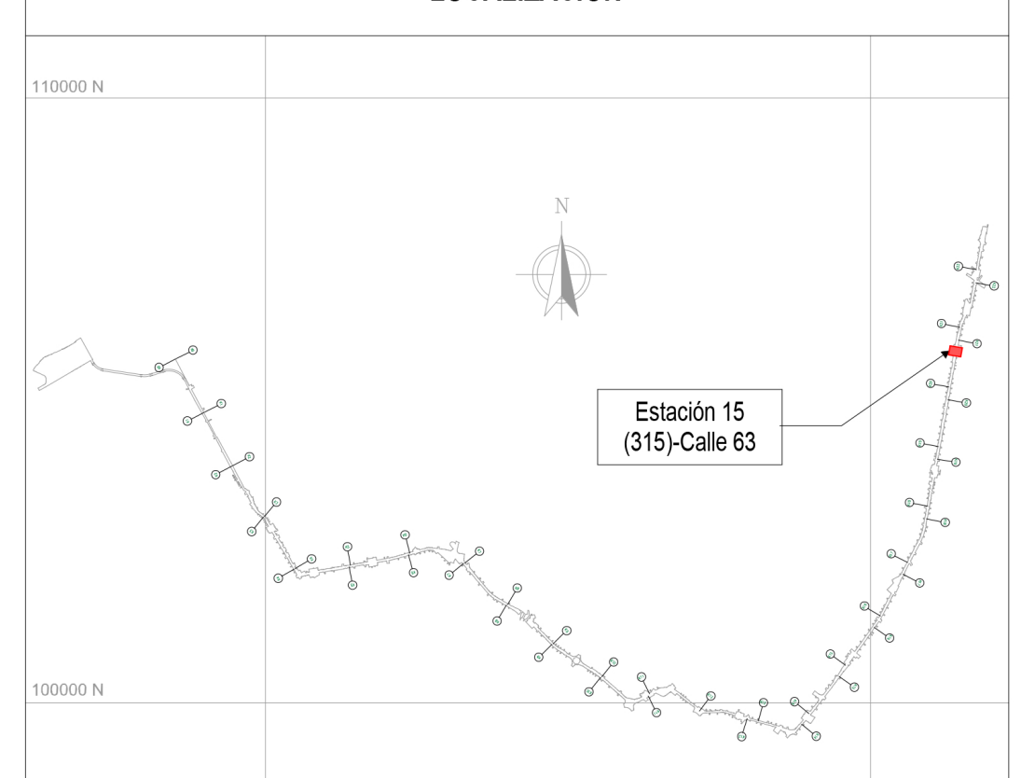

NOTAS

01 TODAS LAS DIMENSIONES ESTÁN CONFIGURADAS EN METROS A MENOS QUE SE INDIQUE UNA UNIDAD DE MEDIDA DIFERENTE.

02 TODAS LAS MEDIDAS, UBICACIÓN Y NIVELES DEBEN VERIFICARSE EN EL LUGAR DE CONSTRUCCIÓN.

03 EL NIVEL DE ACCESO AL EDIFICIO PL 01 CORRESPONDE AL +0,00 DE LA ESTACIÓN Y REFERENCIA AL NIVEL 2569.10 M.S.N.M.

04 LOS NOMBRES ESPECÍFICOS DE LAS ÁREAS PUEDEN SER CONSULTADAS EN EL PLANO NO. 3 Ó EN LAS VISTAS EN PLANTA.

05 LOS COLORES QUE SE MUESTRAN EN LOS PLANOS COMO PROYECCIÓN DE ELEMENTOS ARQUITECTÓNICOS COMO CUBIERTAS, FACHADAS, MUROS, ETC. NO REPRESENTAN LA MATERIALIDAD Y REALIDAD DE ACABADOS DEL PROYECTO, SOLO SON INDICATIVOS PARA REALIZAR UNA CORRECTA LECTURA DE LA PLANIMETRÍA.

06 LAS ESCALERAS ELÉCTRICAS INDICAN SU SENTIDO CON LA SIGUIENTE NOMENCLATURA: "SUBE" Y "BAJA".

07 SE DEBEN REVISAR LOS NIVELES ESTRUCTURALES PARA NIVEL DE ACCESO PL_01 Y SUBNIVELES, PL_02 (INTERMEDIO), PL_03 (PLATAFORMA) CON LA PLANIMETRÍA DE PLACAS ESTRUCTURALES EN LOS ENTREGABLES L1T1-1300-415-CON-ED-EST-PL-0040, 41, 126, 86 RESPECTIVAMENTE. EL NIVEL ESTRUCTURAL (NE) REFERENCIA LOS ESPACIOS DONDE SE DEBE ACONDICIONAR EL ACABADO DE PISO SEGÚN CORRESPONDA, CON LOS NIVELES DE PISO TERMINADO (NPT). LOS NIVELES PROYECTADOS DE EMPATE (NPE) EN LAS ÁREAS DE SERVICIOS ADICIONALES, REFERENCIAN LA ADECUACIÓN DE LOS DESNIVELES EN ESTAS ÁREAS; QUEDA COMO RESPONSABILIDAD DEL LOCATARIO DEFINIR Y ACONDICIONAR ESTE ACABADO DE PISO (NPE) EN LÍNEA CON EL NIVEL (NPT) DE ESPACIOS COLINDANTES. EL NIVEL ESTRUCTURAL (NE) SE ENCUENTRA A (- 0.10M) POR DEBAJO DE LOS NIVELES DE PISO TERMINADO (NPT) Y LOS NIVELES PROYECTADOS DE EMPATE (NPE) MARCADOS EN LA PLANIMETRÍA.

- ARQ_PL_-00.1 = SER 3 / NPT -11.00m
- ARQ_PL_00 = SÓTANO / NPT -7.15m
- ARQ_PL_00.1 = ACCESO / NPT -2.60m
- ARQ_PL_00.2 = ACCESO / NPT -1.85m
- ARQ_PL_00.3 = ACCESO / NPT -1.50m
- ARQ_PL_00.4 = ACCESO / NPT -1.45m
- ARQ_PL_00.5 = ACCESO / NPT -1.27m
- ARQ_PL_00.6 = ACCESO / NPT -1.00m
- ARQ_PL_00.7 = ACCESO / NPT -0.60m
- ARQ_PL_00.8 = ACCESO / NPT -0.45m
- ARQ_PL_00.9 = ACCESO / NPT -0.30m
- ARQ_PL_01 = ACCESO / NPT 0.00m
- ARQ_PL_01.1 = ACCESO / NPT 0.30m
- ARQ_PL_02 = INTERMEDIO / NPT 6.60m
- ARQ_PL_02.2 = TOPE DE RIEL (TOR) / NPT 14.20m
- ARQ_PL_03 = PLATAFORMA / NPT 15.34m
- ARQ_PL_03 = CUBIERTA EDIFICIOS ACCESO / NPT 21.94m
- ARQ_PL_05 = CUBIERTA NAVE CENTRAL / NPT 24.60m

CONVENCIONES

▬ ▬ ▬	LÍMITE DE INTERVENCIÓN
— — —	HUELLA APÉNDICE TÉCNICO
▬	MURO DIVISORIO
— — —	PROYECCIÓN NIVEL SUPERIOR
🟩	SERVICIOS ADICIONALES - ÁREA NO PAGA
🟩	SERVICIOS ADICIONALES - ÁREA PAGA
🟩	SERVICIO PÚBLICO
🟦	ZONA DE REFUGIO
🟥	ÁREA CULTURAL
🟨	ÁREA NO PAGA
🟦	ÁREA OPERATIVA
🟨	ÁREA PAGA
🟦	ÁREA PÚBLICA
⬜	ÁREA TÉCNICA
🟧	ÁREA BRT

No.	PLANOS DE REFERENCIA	REV.

No.	MODELO BIM DE REFERENCIA	REV.
1	L1T1-1100-215-CON-ED-EST-MO-0001.rvt	V00
2	L1T1-1100-216-CON-ED-EST-MO-0001.rvt	V00
3	L1T1-1100-315-CON-ED-EST-MO-0001.rvt	V00
4	L1T1-1150-215-CON-ED-EST-MO-0001.rvt	V00
5	L1T1-1150-216-CON-ED-EST-MO-0001.rvt	V00
6	L1T1-1150-315-CON-ED-EST-MO-0001.rvt	V00
7	L1T1-1200-315-CON-ED-EST-MO-0001.rvt	V00
8	L1T1-1300-415-CON-ED-EST-MO-0001.rvt	V00
9	L1T1-1300-415-CON-ED-EST-MO-0002.rvt	V00
10	L1T1-1300-415-CON-ED-EST-MO-0003.rvt	V00
11	L1T1-1310-415-CON-ED-EST-MO-0001.rvt	V00
12	L1T1-1410-315-CON-ED-MEC-MO-0001.rvt	V00
13	L1T1-1420-315-CON-ED-MEC-MO-0001.rvt	V00
14	L1T1-2320-590-CON-ED-EST-MO-0001.rvt	V00
15	L1T1-2320-590-CON-ED-EST-MO-0002.rvt	V00
16	L1T1-2330-590-CON-ED-ARQ-MO-0001.rvt	V00
17	L1T1-5110-315-CON-ED-EST-MO-0001.rvt	V00
18	L1T1-5160-315-CON-ED-EST-MO-0001.rvt	V00
19	L1T1-5160-315-CON-ED-ARQ-MO-0001.rvt	V00
20	L1T1-5300-315-CON-ED-MEC-MO-0001.rvt	V00
21	L1T1-5600-315-CON-ED-INS-MO-0001.rvt	V00
22	L1T1-1330-415-CON-ED-ARQ-MO-0011.rvt	V00
23	L1T1-1330-415-CON-ED-ARQ-MO-0012.rvt	V00
24	L1T1-1330-415-CON-ED-ARQ-MO-0013.rvt	V00

No.	PAQUETE DE TRABAJO DE REFERENCIA	REV.
1	XREF-URBANISM_CONTEXT_ST15.rvt	
2	XREF-SECONDARY-STRUCTURE-ST15.rvt	

0 2 10m
1:200

METRO BOGOTÁ
GCS Consorcio Consultores PMO Bogotá
CONSORCIO SUPERVISOR PLMB
CHEC

DISEÑÓ:
REN ZHENHUA
Licencia de Arq.nivel I (China): 1101735-614

APROBÓ:
DIEGO ERNESTO DUEÑAS
Mat.: 25202-53876 CND

REVISÓ:
CARLOS MAURICIO BARRETO BARBOSA
Mat.: A4012012-14139353

DIBUJÓ:
EQUIPO CHEC

REVISIÓN No.	FECHA	DESCRIPCIÓN	REVISÓ	APROBÓ	APROBACIÓN CLIENTE
V01	31/03/2026	EMITIDO PARA CONSTRUCCIÓN	C.M.B.B	D.E.D	
V00	13/12/2024	REVISIÓN NO OBJETADA - EMITIDO PARA CONSTRUCCIÓN	F.B.R	E.O.M	
VFF	21/08/2024	EMITIDO PARA REVISIÓN Y COMENTARIOS DEL CLIENTE E INTERVENTORÍA - INCLUYE COMENTARIOS /(AJUSTES V3)	F.B.R	E.O.M	
VEE	02/05/2024	EMITIDO PARA REVISIÓN Y COMENTARIOS DEL CLIENTE E INTERVENTORÍA - INCLUYE COMENTARIOS /(AJUSTES V2)	F.B.R	E.O.M	
VDD	18/12/2022	EMITIDO PARA REVISIÓN Y COMENTARIOS DEL CLIENTE E INTERVENTORÍA - INCLUYE COMENTARIOS /(AJUSTES)	J.E.M	M.B.M	
VCC	02/06/2022	EMITIDO PARA REVISIÓN Y COMENTARIOS DEL CLIENTE E INTERVENTORÍA - INCLUYE COMENTARIOS /(ENTREGA 90%)	J.E.M	M.B.M	
VBB	06/12/2021	EMITIDO PARA REVISIÓN Y COMENTARIOS DEL CLIENTE E INTERVENTORÍA	J.E.M	M.B.M	
VA0	30/06/2021	EMITIDO PARA COMENTARIOS INTERNOS - EMISIÓN PRELIMINAR PARA COMENTARIOS	J.E.M	M.B.M	

METRO LÍNEA 1

METRO LÍNEA 1
CONTRATO DE CONCESIÓN No. 163 DE 2019

PROYECTO PRIMERA LÍNEA DEL METRO DE BOGOTÁ - TRAMO 1

DIRECTOR DE INTERVENTORÍA:
JAVIER DESCARGA N.
Mat.:25202-68697 CND

ESPECIALISTA INTERVENTORÍA:
CARLOS ALBERTO HOYOS SOTO
Mat.:A25072000-14251682

FECHA:
MARZO 2026

INFRAESTRUCTURA VIAL
ARQUITECTURA
ESTACIÓN METRO 15 - (CALLE 63)
GENERAL
VISTA EN PLANTA Y 3D - NIVEL ACCESO

PLANCHA No: L1T1-0000-315-CON-ED-ARQ-PL-0001_05_V01
ARCHIVO: L1T1-0000-315-CON-ED-ARQ-MO-0001_V00.rvt
ESCALA: INDICADA
FECHA: JUNIO 2021
REVISIÓN No. V01
PLANO No. 05 DE 94