L1T1-CON-CAL-FR-0120 - B1 : 1000x707mm

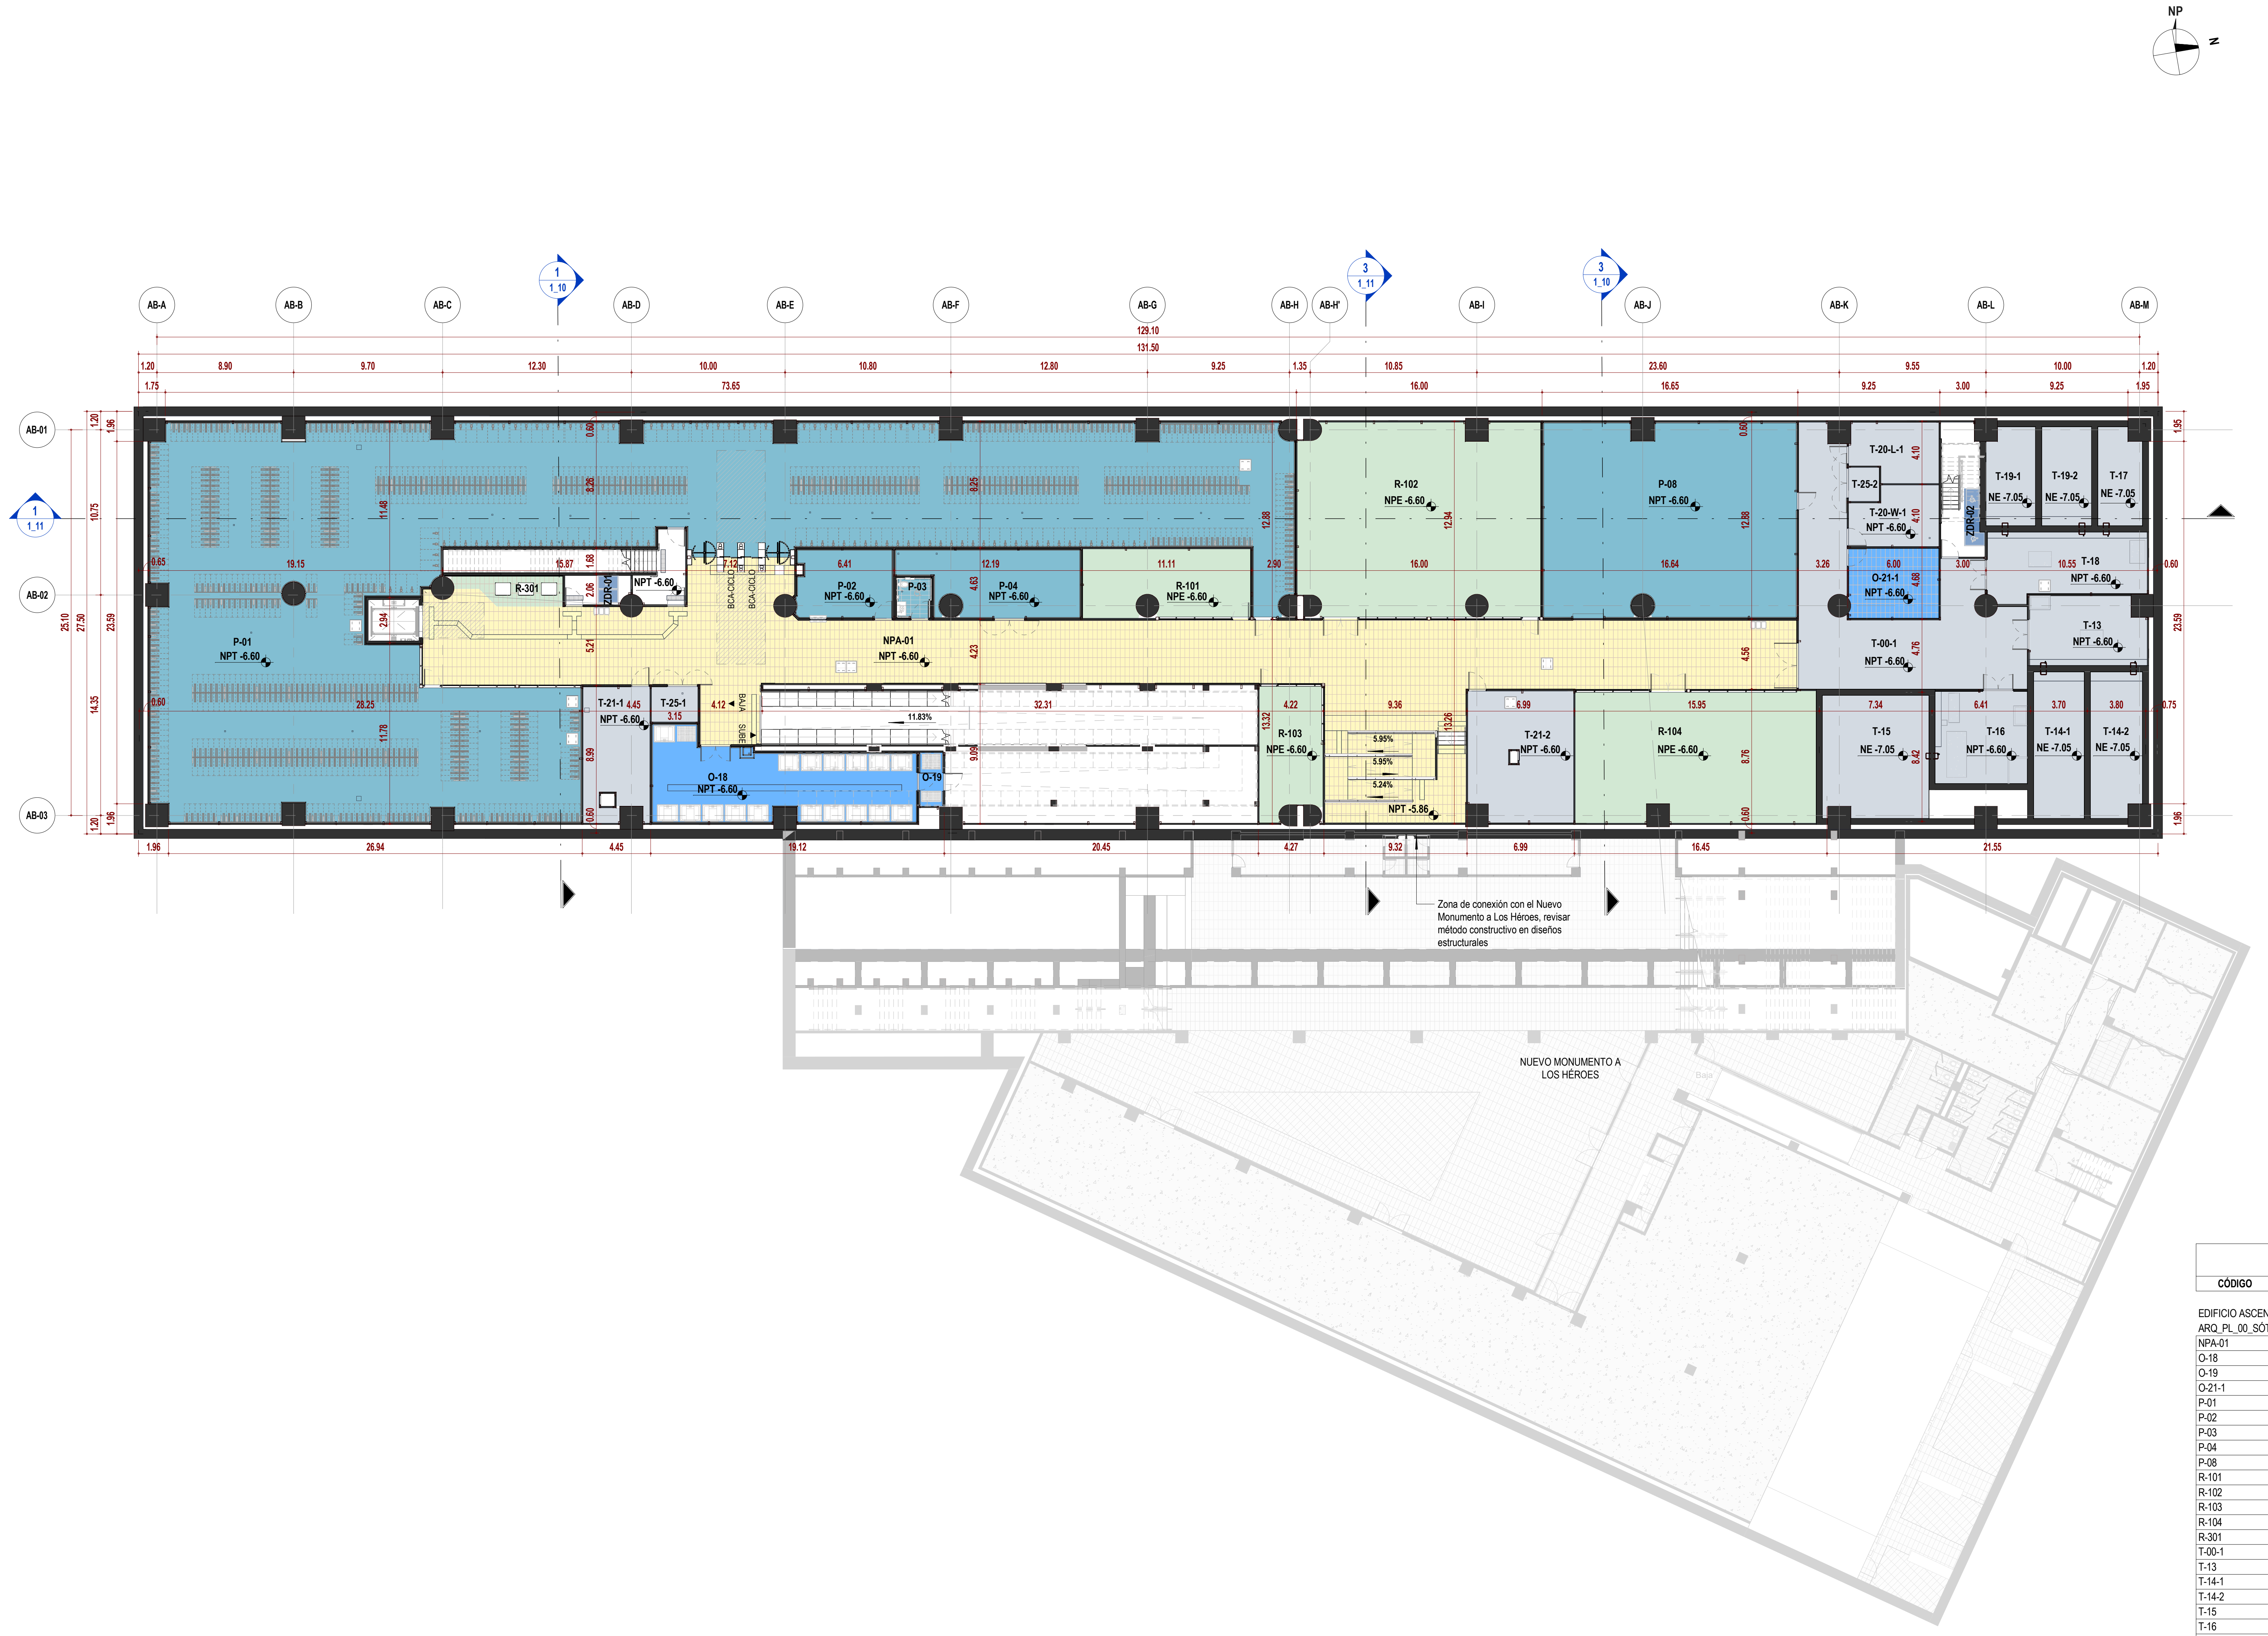

② NIVEL SÓTANO_EDIFICIO ASCENDENTE
ESC : 1 : 200

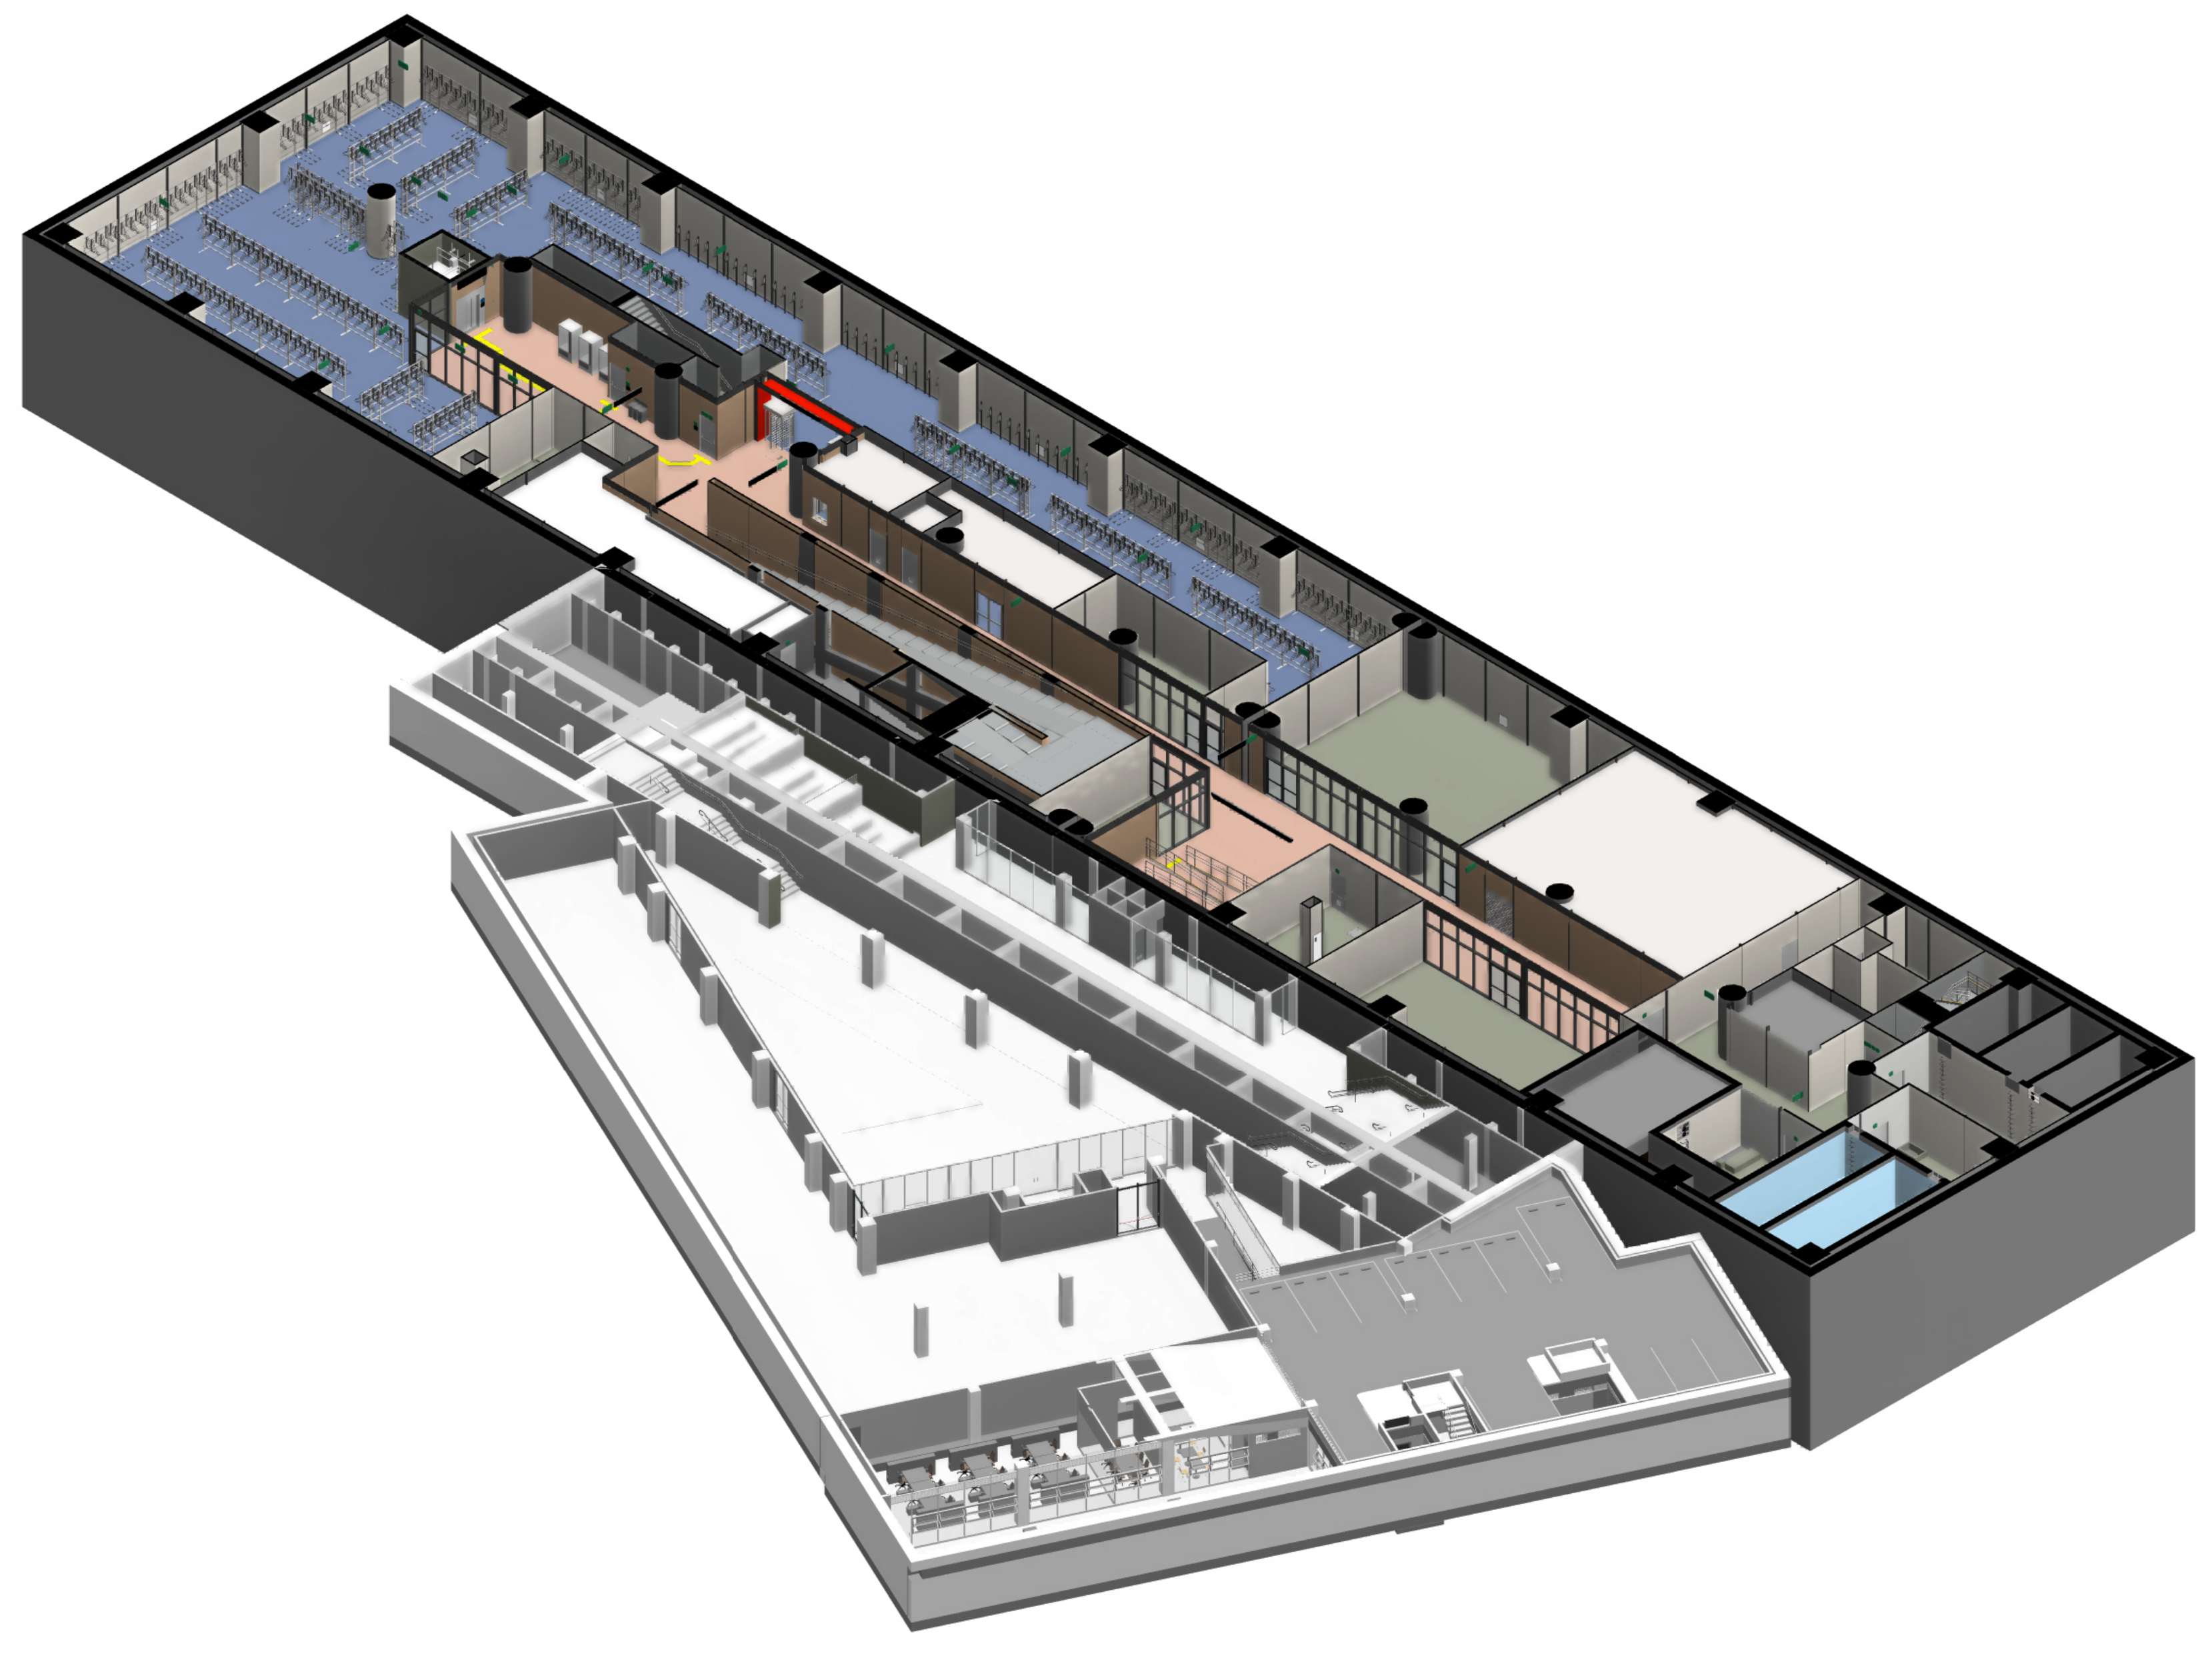

① VISTA_3D_SÓTANO
ESC : N/A

TABLA DE ÁREAS ÚTILES (NIVEL SÓTANO _ EDIFICIO ASCENDENTE)

EDIFICIO ASCENDENTE
ARQ_PL_00_SÓTANO

CÓDIGO	NOMBRE	ÁREA (m²)	DEPARTAMENTO
NPA-01	ÁREA NO PAGA	527.98	ÁREA NO PAGA
O-18	CUARTO DE ALMACENAMIENTO DE RESIDUOS SÓLIDOS	83.83	ÁREA OPERATIVA
O-19	CUARTO DE ALMACENAMIENTO DE RESIDUOS PELIGROSOS	5.33	ÁREA OPERATIVA
O-21-1	ALMACENAMIENTO DE LA ESTACIÓN	26.83	ÁREA OPERATIVA
P-01	ÁREA CICLO-PARQUEADEROS	998.77	ÁREA PÚBLICA
P-02	ÁREA OPERATIVA CICLO-PARQUEADEROS	27.56	ÁREA PÚBLICA
P-03	BAÑO OPERADOR CICLO-PARQUEADEROS	5.87	ÁREA PÚBLICA
P-04	TALLER DE BICICLETAS	45.01	ÁREA PÚBLICA
P-08	ESPACIO CARGA DE VEHÍCULOS ELÉCTRICOS	207.14	ÁREA PÚBLICA
R-101	SERVICIOS ADICIONALES - ÁREA DE SERVICIO	46.84	SERVICIOS ADICIONALES - ÁREA NO PAGA
R-102	SERVICIOS ADICIONALES - ÁREA DE SERVICIO	193.46	SERVICIOS ADICIONALES - ÁREA NO PAGA
R-103	SERVICIOS ADICIONALES - ÁREA DE SERVICIO	32.02	SERVICIOS ADICIONALES - ÁREA NO PAGA
R-104	SERVICIOS ADICIONALES - ÁREA DE SERVICIO	131.75	SERVICIOS ADICIONALES - ÁREA NO PAGA
R-301	SERVICIOS ADICIONALES - MÁQUINAS EXPENDEDORAS/CAJEROS AUTOMÁTICOS	11.66	SERVICIOS ADICIONALES - ÁREA NO PAGA
T-00-1	CIRCULACIÓN TÉCNICA	116.75	ÁREA TÉCNICA
T-13	CUARTO DE BOMBAS DE SUMINISTRO DE AGUA	33.27	ÁREA TÉCNICA
T-14-1	TANQUE DE SUMINISTRO DE AGUA	31.44	ÁREA TÉCNICA
T-14-2	TANQUE DE SUMINISTRO DE AGUA	31.40	ÁREA TÉCNICA
T-15	TANQUE SISTEMA DE EXTINCIÓN DE INCENDIOS (RCI)	54.28	ÁREA TÉCNICA
T-16	CUARTO DE BOMBAS PARA ROCIADORES	36.00	ÁREA TÉCNICA
T-17	TANQUE RECUPERACIÓN AGUAS LLUVIAS	17.85	ÁREA TÉCNICA
T-18	CUARTO DE BOMBAS DE RECUPERACIÓN DE AGUAS LLUVIAS Y EQUIPO DE FILTRACIÓN	43.10	ÁREA TÉCNICA
T-19-1	TANQUE DE AGUA TRATADA	20.03	ÁREA TÉCNICA
T-19-2	TANQUE DE AGUA TRATADA	20.88	ÁREA TÉCNICA
T-20-L-1	MEDIDORES (LUZ)	20.86	ÁREA TÉCNICA
T-20-W-1	MEDIDORES (AGUA)	21.05	ÁREA TÉCNICA
T-21-1	ÁREA DE INSPECCIÓN	35.66	ÁREA TÉCNICA
T-21-2	ÁREA DE INSPECCIÓN	56.53	ÁREA TÉCNICA
T-25-1	NODO DE ACCESO DE TELECOMUNICACIONES	6.91	ÁREA TÉCNICA
T-25-2	NODO DE ACCESO DE TELECOMUNICACIONES	4.41	ÁREA TÉCNICA
ZDR-01	ZONA DE REFUGIO (PMR)	2.43	ZONA DE REFUGIO
ZDR-02	ZONA DE REFUGIO (PMR)	4.06	ZONA DE REFUGIO
TOTAL NIVEL SÓTANO_EDIFICIO ASCENDENTE		2900.93	

TABLA DE ÁREAS ÚTILES POR DEPARTAMENTO (NIVEL SÓTANO)

EDIFICIO ASCENDENTE
ARQ_PL_00_SÓTANO

DEPARTAMENTO	ÁREA (m²)
SERVICIOS ADICIONALES - ÁREA NO PAGA	415.73
ZONA DE REFUGIO	6.49
ÁREA NO PAGA	527.98
ÁREA OPERATIVA	115.98
ÁREA PÚBLICA	1284.34
ÁREA TÉCNICA	550.40
TOTAL NIVEL SÓTANO	2900.93

TABLA DE CICLO-PARQUEADEROS ESPECÍFICOS

ARQ_PL_00_SÓTANO

DESCRIPCIÓN	CANTIDAD	USUARIOS
BICIPARQUEADERO ASISTIDO EN ACERO INOXIDABLE ASTM A240, a=0.70m X l=1.20m, h=1.70m.	1	EMPLEADOS
BICIPARQUEADERO DE COLGAR, 2 PUESTOS, a=1.20m X l=0.70m, h=2.40m. ACABADO EN PINTURA ELECTROSTÁTICA COLOR RAL9005 "NEGRO INTENSO".	4	EMPLEADOS
EMPLEADOS	5	
BICIPARQUEADERO ASISTIDO EN ACERO INOXIDABLE ASTM A240, a=0.70m X l=1.20m, h=1.70m.	97	VISITANTE
BICIPARQUEADERO DE COLGAR DE 6 PUESTOS EN ACERO, a=1.20m X l=2.10m, h=2.40m. ACABADO EN PINTURA ELECTROSTÁTICA COLOR RAL9005 "NEGRO INTENSO".	666	VISITANTE
BICIPARQUEADERO DE COLGAR, 1 PUESTO, a=1.20m X l=0.70m, h=2.40m. ACABADO EN PINTURA ELECTROSTÁTICA COLOR RAL9005 "NEGRO INTENSO".	40	VISITANTE
BICIPARQUEADERO DE COLGAR, 2 PUESTOS, a=1.20m X l=0.70m, h=2.40m. ACABADO EN PINTURA ELECTROSTÁTICA COLOR RAL9005 "NEGRO INTENSO".	166	VISITANTE
VISITANTE	969	
TOTAL CUPOS	974	

LOCALIZACIÓN

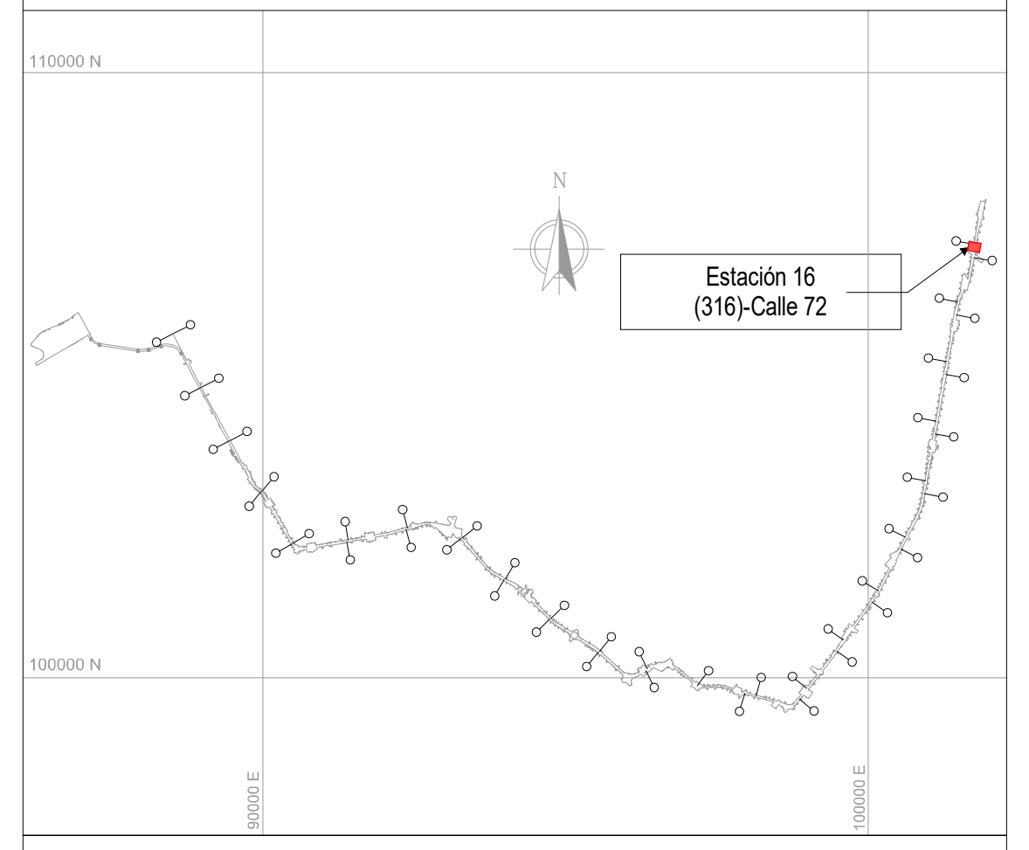

NOTAS

01 TODAS LAS DIMENSIONES ESTÁN CONFIGURADAS EN METROS A MENOS QUE SE INDIQUE UNA UNIDAD DE MEDIDA DIFERENTE.

02 TODAS LAS MEDIDAS, UBICACIÓN Y NIVELES DEBEN VERIFICARSE EN EL LUGAR DE CONSTRUCCIÓN.

03 EL NIVEL DE ACCESO AL EDIFICIO PL 01 CORRESPONDE AL +0,00 DE LA ESTACIÓN Y REFERENCIA AL NIVEL 2560.20 M.S.N.M.

04 LOS NOMBRES ESPECIFICOS DE LAS ÁREAS PUEDEN SER CONSULTADAS EN EL PLANO NO. 3 Ó EN LAS VISTAS EN PLANTA.

05 LOS COLORES QUE SE MUESTRAN EN LOS PLANOS COMO PROYECCIÓN DE ELEMENTOS ARQUITECTÓNICOS COMO CUBIERTAS FACHADAS MUROS ETC. NO REPRESENTAN LA MATERIALIDAD Y REALIDAD DE ACABADOS DEL PROYECTO, SOLO SON INDICATIVOS PARA REALIZAR UNA CORRECTA LECTURA DE LA PLANIMETRÍA.

06 SE DEBEN REVISAR LOS NIVELES ESTRUCTURALES PARA NIVEL DE ACCESO PL_01 Y SUBNIVELES, PL_02 (INTERMEDIO), PL_03 (PLATAFORMA) CON LA PLANIMETRÍA DE PLACAS ESTRUCTURALES EN LOS ENTREGABLES L1T1-1300-316-CON-ED-EST-PL-00035, 36, 38, RESPECTIVAMENTE. EL NIVEL ESTRUCTURAL (NE) REFERENCIA LOS ESPACIOS DONDE SE DEBE ACONDICIONAR EL ACABADO DE PISO SEGÚN CORRESPONDA, CON LOS NIVELES DE PISO TERMINADO (NPT). LOS NIVELES PROYECTADOS DE EMPATE (NPE) EN LAS ÁREAS DE SERVICIOS ADICIONALES, REFERENCIAN LA ADECUACIÓN DE LOS DESNIVELES EN ESTAS ÁREAS; QUEDA COMO RESPONSABILIDAD DEL LOCATARIO DEFINIR Y ACONDICIONAR ESTE ACABADO DE PISO (NPE) EN LÍNEA CON EL NIVEL (NPT) DE ESPACIOS COLINDANTES. EL NIVEL ESTRUCTURAL (NE) SE ENCUENTRA A (- 0.10M) POR DEBAJO DE LOS NIVELES DE PISO TERMINADO (NPT) Y LOS NIVELES PROYECTADOS DE EMPATE (NPE) MARCADOS EN LA PLANIMETRÍA.

07 RESPECTO A LAS ÁREAS CONSTRUIDAS Y DE ACUERDO CON LA COMUNICACIÓN EXTS22-0002544 DE EMB, SE IDENTIFICA QUE EL CONCESIONARIO SE ENCUENTRA BUSCANDO ESTRATEGIAS PARA MEJORAR EL DISEÑO CON EL PROGRAMA ARQUITECTÓNICO, UNA DE ESTAS ESTRATEGIAS ES MEJORAR EL FUNCIONAMIENTO DEL DISEÑO URBANO Y BRINDAR UNA SOLUCIÓN INTEGRAL RESPECTO A LOS INMUEBLES DE INTERÉS CULTURAL. DE ACUERDO CON LO ANTERIOR, PARA LA EMB, ESTAS ACTIVIDADES OBEDECEN AL PROCESO NATURAL DE LOS ESTUDIOS Y DISEÑOS DEFINITIVOS QUE DEBE DESARROLLAR METRO LÍNEA 1.

- ARQ_PL_00 = SÓTANO	/ NPT -6.60m	- ARQ_PL_00.7 = ACCESO	/ NPT -0.37m
- ARQ_PL_00 = SÓTANO CONEXIÓN HÉROES	/ NPT -5.86m	- ARQ_PL_01 = ACCESO	/ NPT 0.00m
		- ARQ_PL_02 = INTERMEDIO	/ NPT 6.60m
- ARQ_PL_00.1 = ACCESO	/ NPT -1.45m	- ARQ_PL_02.2 = TOPE DE RIEL (TOR)	/ NPT 14.20m
- ARQ_PL_00.2 = ACCESO	/ NPT -1.10m	- ARQ_PL_03 = PLATAFORMA	/ NPT 15.34m
- ARQ_PL_00.3 = ACCESO	/ NPT -0.95m	- ARQ_PL_04 = OFICINAS/ CUBIERTA EDIFICIO DESCENDENTE	/ NPT 21.94m
- ARQ_PL_00.4 = ACCESO	/ NPT -0.75m		
- ARQ_PL_00.5 = ACCESO	/ NPT -0.70m	- ARQ_PL_05 = CUBIERTA NAVE CENTRAL	/ NPT 24.61m
- ARQ_PL_00.6 = ACCESO	/ NPT -0.60m	- ARQ_PL_06 = CUBIERTA EDIFICIO ASCENDENTE	/ NPT 28.54m

CONVENCIONES

■	SERVICIOS ADICIONALES - ÁREA NO PAGA	■	SERVICIO PÚBLICO
■	SERVICIOS ADICIONALES - ÁREA PAGA	■	ZONA DE REFUGIO
■	MUSEO	■	ÁREA NO PAGA
■	ÁREA CULTURAL	■	ÁREA OPERATIVA
■	ÁREA DE TAQUILLAS BRT	■	ÁREA PAGA
■	SERVICIOS ADICIONALES - ÁREA OFICINAS	■	ÁREA PÚBLICA
■	ÁREA TÉCNICA OFICINAS	■	ÁREA TÉCNICA
■	ÁREA BRT		

No.	PLANOS DE REFERENCIA	REV.

No.	MODELO BIM DE REFERENCIA	REV.
1	L1T1-1100-216-CON-ED-EST-MO-0001.rvt	V00
2	L1T1-1100-217-CON-ED-EST-MO-0001.rvt	V00
3	L1T1-1100-316-CON-ED-EST-MO-0001.rvt	V00
4	L1T1-1150-216-CON-ED-EST-MO-0001.rvt	V00
5	L1T1-1150-217-CON-ED-EST-MO-0001.rvt	V00
6	L1T1-1150-316-CON-ED-EST-MO-0001.rvt	V00
7	L1T1-1200-316-CON-ED-EST-MO-0001.rvt	V00
8	L1T1-1300-416-CON-ED-EST-MO-0001.rvt	V00
9	L1T1-1300-416-CON-ED-EST-MO-0002.rvt	V00
10	L1T1-1310-416-CON-ED-EST-MO-0001.rvt	V00
11	L1T1-1410-316-CON-ED-MEC-MO-0001.rvt	V00
12	L1T1-1420-316-CON-ED-MEC-MO-0001.rvt	V00
13	L1T1-2320-593-CON-ED-EST-MO-0001.rvt	V00
14	L1T1-2330-593-CON-ED-ARQ-MO-0001.rvt	V00
15	L1T1-2430-541-CON-ED-ARQ-MO-0001.rvt	V00
16	L1T1-2430-541-CON-ED-EST-MO-0002.rvt	V00
17	L1T1-5160-316-CON-ED-EST-MO-0001.rvt	V00
18	L1T1-5160-316-CON-ED-ARQ-MO-0001.rvt	V00
19	L1T1-5300-316-CON-ED-MEC-MO-0001.rvt	V00
20	L1T1-5600-316-CON-ED-INS-MO-0001.rvt	V00
21	L1T1-1330-416-CON-ED-ARQ-MO-0011.rvt	V00
22	L1T1-1330-416-CON-ED-ARQ-MO-0012.rvt	V00

No.	PAQUETE DE TRABAJO DE REFERENCIA	REV.
1	XREF-URBANISM_CONTEXT_ST16.rvt	
2	RVT_MONUMENTO A LOS HEROES_v9.rvt	
3	XREF-SECONDARY-STRUCTURE-ST16.rvt	

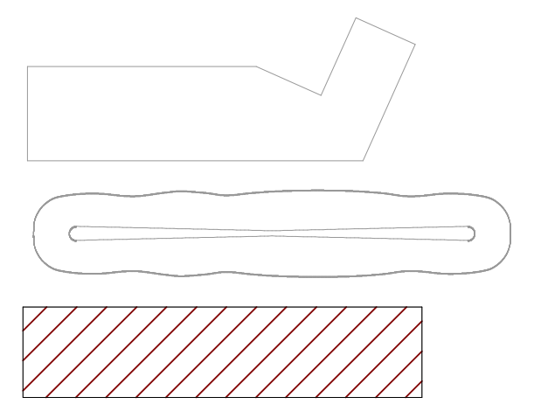

PLANO CLAVE ESTACIÓN 16

0 2 10m
1:200

VÁLIDO PARA CONSTRUCCIÓN
31-03-26

METRO BOGOTÁ
Consorcio Consultores PMO Bogotá
CONSORCIO SUPERVISOR PLMB

DISEÑÓ:	REN ZHENHUA Licencia de Arq.nivel I (China): 1101735-614
APROBÓ:	DIEGO ERNESTO DUEÑAS Mat.: 25202-53876 CND
REVISÓ:	CARLOS MAURICIO BARRETO BARBOSA Mat.: A4012012-14139353
DIBUJÓ:	EQUIPO CHEC

REVISIÓN No.	FECHA	DESCRIPCIÓN	REVISÓ	APROBÓ	APROBACIÓN CLIENTE
V01	31/03/2026	EMITIDO PARA CONSTRUCCIÓN	C.M.B.B	D.E.D	
V00	27/01/2025	REVISIÓN NO OBJETADA - EMITIDO PARA CONSTRUCCIÓN	F.B.R	E.O.M	
VFF	12/09/2024	EMITIDO PARA REVISIÓN Y COMENTARIOS DEL CLIENTE E INTERVENTORÍA - INCLUYE COMENTARIOS /(AJUSTES V2)	F.B.R	E.O.M	
VEE	04/06/2024	EMITIDO PARA REVISIÓN Y COMENTARIOS DEL CLIENTE E INTERVENTORÍA - INCLUYE COMENTARIOS /(AJUSTES)	F.B.R	E.O.M	
VDD	18/12/2022	EMITIDO PARA REVISIÓN Y COMENTARIOS DEL CLIENTE E INTERVENTORÍA - INCLUYE COMENTARIOS /(NO APLICA)	J.E.M	M.B.M	
VCC	22/08/2022	EMITIDO PARA REVISIÓN Y COMENTARIOS DEL CLIENTE E INTERVENTORÍA - INCLUYE COMENTARIOS /(NO APLICA)	J.E.M	M.B.M	
VBB	06/12/2021	EMITIDO PARA REVISIÓN Y COMENTARIOS DEL CLIENTE E INTERVENTORÍA	J.E.M	M.B.M	
VA0	30/06/2021	EMITIDO PARA COMENTARIOS INTERNOS - EMISIÓN PRELIMINAR PARA COMENTARIOS	J.E.M	M.B.M	

METRO LÍNEA 1

METRO LÍNEA 1
CONTRATO DE CONCESIÓN No. 163 DE 2019

PROYECTO PRIMERA LÍNEA DEL METRO DE BOGOTÁ - TRAMO 1

DIRECTOR DE INTERVENTORÍA:
JAVIER DESCARGA N.
Mat.:25202-68697 CND

ESPECIALISTA INTERVENTORÍA:
CARLOS ALBERTO HOYOS SOTO
Mat.:A25072000-14251682

FECHA: MARZO 2026

INFRAESTRUCTURA VIAL

ARQUITECTURA

ESTACIÓN METRO 16 (CALLE 72)
EDIFICIO ASCENDENTE
VISTA EN PLANTA Y 3D - NIVEL SÓTANO

PLANCHA No: L1T1-0000-316-CON-ED-ARQ-PL-0001_04_V01
ARCHIVO: L1T1-0000-316-CON-ED-ARQ-MO-0001_V00.rvt
ESCALA: INDICADA
FECHA: JUNIO 2021
REVISIÓN No.: V01
PLANO No.: 04 DE 85