L1T1-CON-CAL-FR-0120 - B1 : 1000x707mm

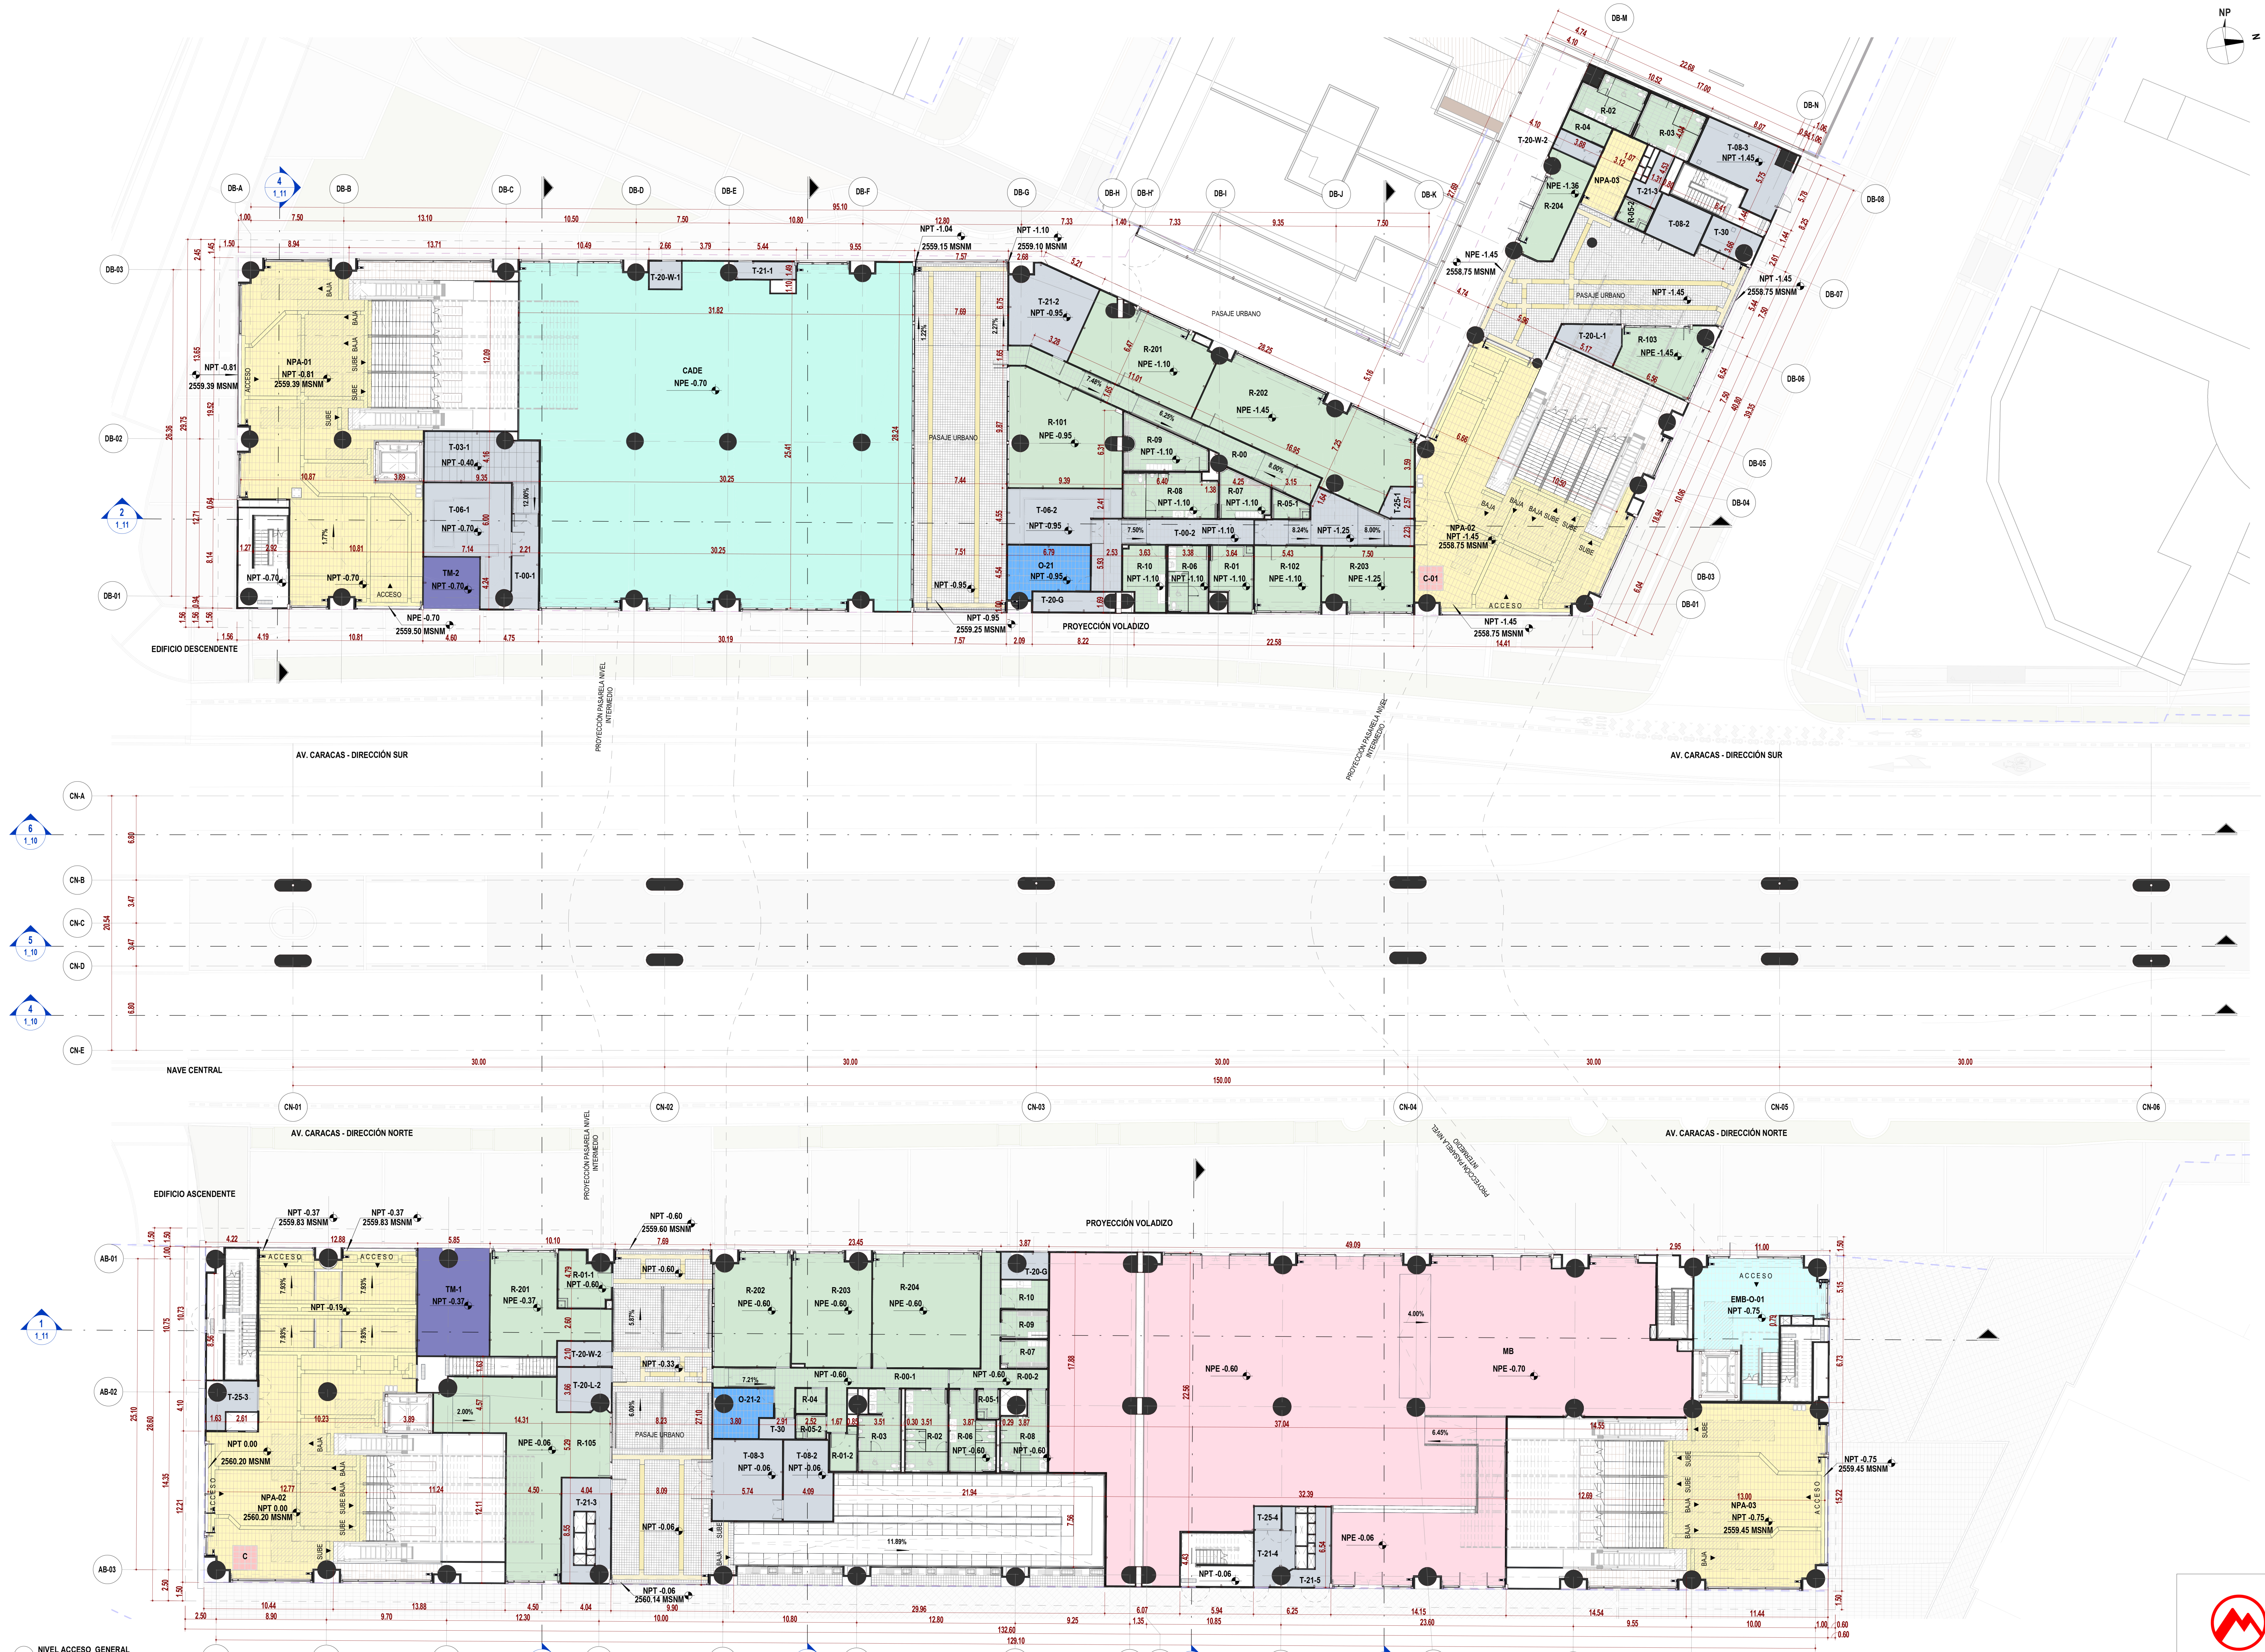

2 NIVEL ACCESO_GENERAL
ESC : 1 : 200

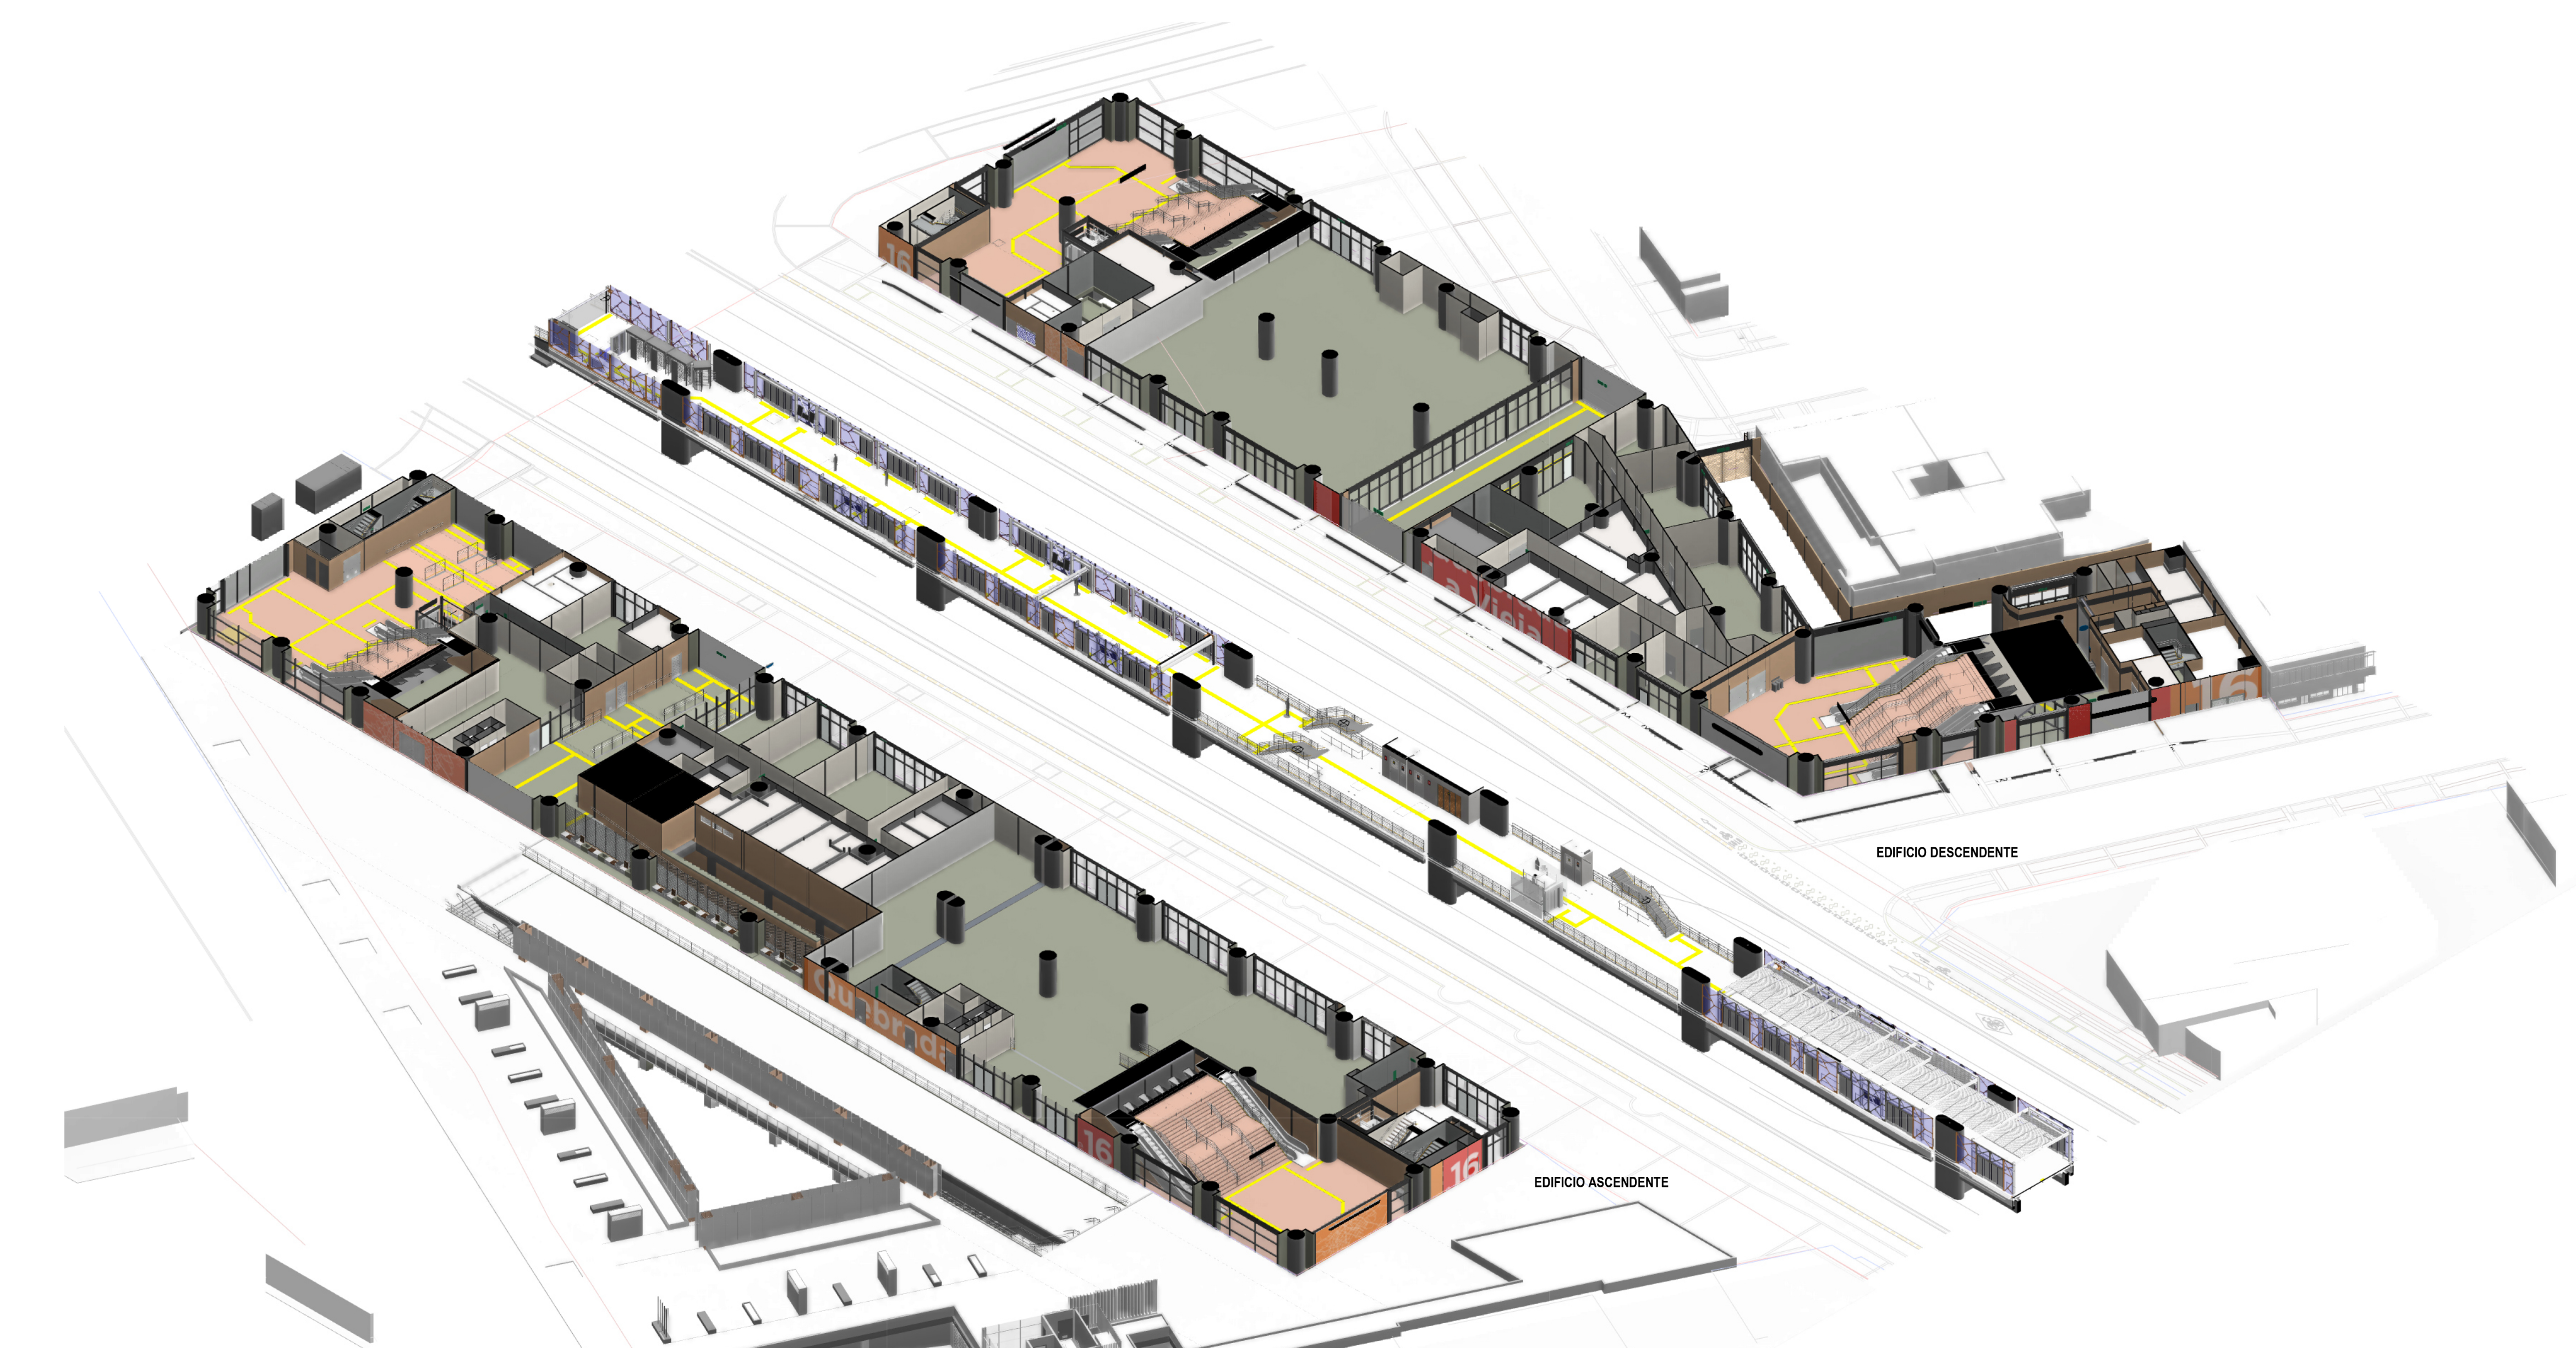

1 3D_NIVEL ACCESO_GENERAL
ESC : N/A

LOCALIZACIÓN

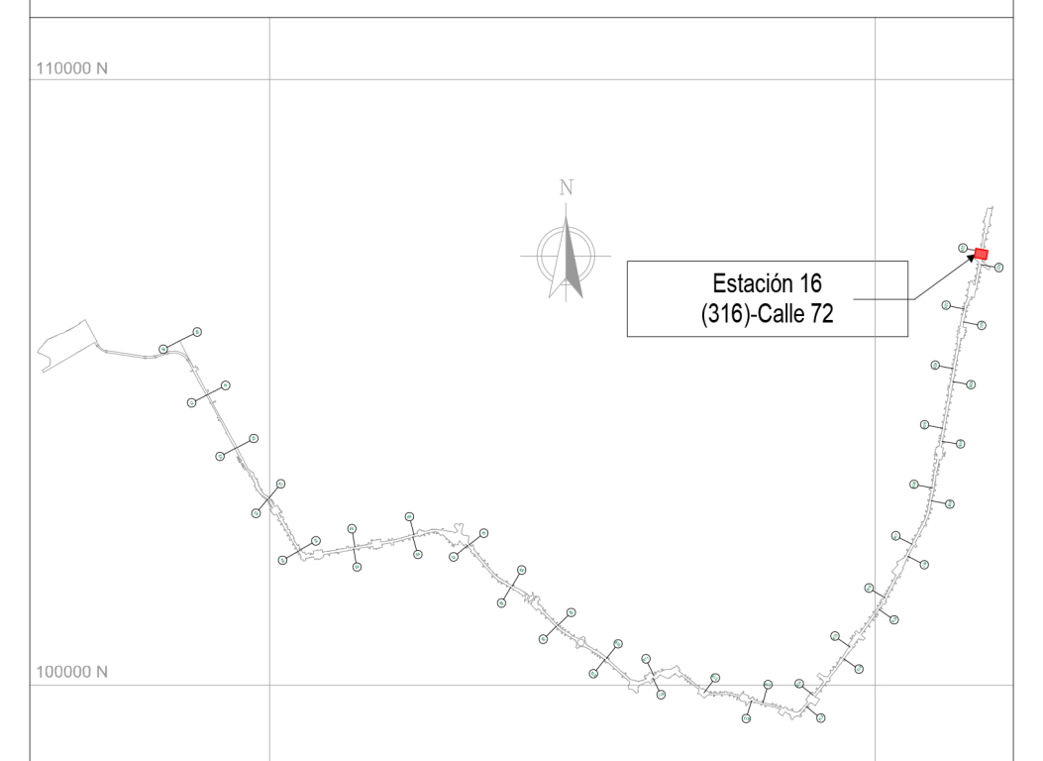

NOTAS

01 TODAS LAS DIMENSIONES ESTÁN CONFIGURADAS EN METROS A MENOS QUE SE INDIQUE UNA UNIDAD DE MEDIDA DIFERENTE.

02 TODAS LAS MEDIDAS, UBICACIÓN Y NIVELES DEBEN VERIFICARSE EN EL LUGAR DE CONSTRUCCIÓN.

03 EL NIVEL DE ACCESO AL EDIFICIO PL 01 CORRESPONDE AL +0,00 DE LA ESTACIÓN Y REFERENCIA AL NIVEL 2560.20 M.S.N.M.

04 LOS NOMBRES ESPECÍFICOS DE LAS ÁREAS PUEDEN SER CONSULTADAS EN EL PLANO NO. 3 Ó EN LAS VISTAS EN PLANTA.

05 LOS COLORES QUE SE MUESTRAN EN LOS PLANOS COMO PROYECCIÓN DE ELEMENTOS ARQUITECTÓNICOS COMO CUBIERTAS FACHADAS MUROS ETC. NO REPRESENTAN LA MATERIALIDAD Y REALIDAD DE ACABADOS DEL PROYECTO, SOLO SON INDICATIVOS PARA REALIZAR UNA CORRECTA LECTURA DE LA PLANIMETRÍA.

06 LAS ESCALERAS ELÉCTRICAS INDICAN SU SENTIDO CON LA SIGUIENTE NOMENCLATURA: "SUBE" Y "BAJA".

07 SE DEBEN REVISAR LOS NIVELES ESTRUCTURALES PARA NIVEL DE ACCESO PL_01 Y SUBNIVELES, PL_02 (INTERMEDIO), PL_03 (PLATAFORMA) CON LA PLANIMETRÍA DE PLACAS ESTRUCTURALES EN LOS ENTREGABLES L1T1-1300-316-CON-ED-EST-PL-00035, 36, 38, RESPECTIVAMENTE. EL NIVEL ESTRUCTURAL (NE) REFERENCIA LOS ESPACIOS DONDE SE DEBE ACONDICIONAR EL ACABADO DE PISO SEGÚN CORRESPONDA, CON LOS NIVELES DE PISO TERMINADO (NPT). LOS NIVELES PROYECTADOS DE EMPATE (NPE) EN LAS ÁREAS DE SERVICIOS ADICIONALES, REFERENCIAN LA ADECUACIÓN DE LOS DESNIVELES EN ESTAS ÁREAS; QUEDA COMO RESPONSABILIDAD DEL LOCATARIO DEFINIR Y ACONDICIONAR ESTE ACABADO DE PISO (NPE) EN LÍNEA CON EL NIVEL (NPT) DE ESPACIOS COLINDANTES. EL NIVEL ESTRUCTURAL (NE) SE ENCUENTRA A (- 0.10M) POR DEBAJO DE LOS NIVELES DE PISO TERMINADO (NPT) Y LOS NIVELES PROYECTADOS DE EMPATE (NPE) MARCADOS EN LA PLANIMETRÍA.

08 RESPECTO A LAS ÁREAS CONSTRUIDAS Y DE ACUERDO CON LA COMUNICACIÓN EXTS22-0002544 DE EMB, SE IDENTIFICA QUE EL CONCESIONARIO SE ENCUENTRA BUSCANDO ESTRATEGIAS PARA MEJORAR EL DISEÑO CON EL PROGRAMA ARQUITECTÓNICO, UNA DE ESTAS ESTRATEGIAS ES MEJORAR EL FUNCIONAMIENTO DEL DISEÑO URBANO Y BRINDAR UNA SOLUCIÓN INTEGRAL RESPECTO A LOS INMUEBLES DE INTERÉS CULTURAL. DE ACUERDO CON LO ANTERIOR, PARA LA EMB, ESTAS ACTIVIDADES OBEDECEN AL PROCESO NATURAL DE LOS ESTUDIOS Y DISEÑOS DEFINITIVOS QUE DEBE DESARROLLAR METRO LÍNEA 1.

- ARQ_PL_00 = SÓTANO / NPT -6.60m - ARQ_PL_00.7 = ACCESO / NPT -0.37m
- ARQ_PL_00 = SÓTANO CONEXIÓN HÉROES / NPT -5.86m - ARQ_PL_01 = ACCESO / NPT 0.00m
- ARQ_PL_00.1 = ACCESO / NPT -1.45m - ARQ_PL_02 = INTERMEDIO / NPT 6.60m
- ARQ_PL_00.2 = ACCESO / NPT -1.10m - ARQ_PL_02.2 = TOPE DE RIEL (TOR) / NPT 14.20m
- ARQ_PL_00.3 = ACCESO / NPT -0.95m - ARQ_PL_03 = PLATAFORMA / NPT 15.34m
- ARQ_PL_00.4 = ACCESO / NPT -0.75m - ARQ_PL_04 = OFICINAS/ CUBIERTA EDIFICIO DESCENDENTE / NPT 21.94m
- ARQ_PL_00.5 = ACCESO / NPT -0.70m - ARQ_PL_05 = CUBIERTA NAVE CENTRAL / NPT 24.61m
- ARQ_PL_00.6 = ACCESO / NPT -0.60m - ARQ_PL_06 = CUBIERTA EDIFICIO ASCENDENTE / NPT 28.54m

CONVENCIONES

- LÍMITE DE INTERVENCIÓN
- HUELLA APÉNDICE TÉCNICO
- MURO DIVISORIO
- PROYECCIÓN NIVEL SUPERIOR
- PATRIMONIO
- SERVICIOS ADICIONALES - ÁREA NO PAGA
- SERVICIOS ADICIONALES - ÁREA PAGA
- MUSEO
- ÁREA CULTURAL
- ÁREA DE TAQUILLAS BRT
- SERVICIOS ADICIONALES - ÁREA OFICINAS
- ÁREA TÉCNICA OFICINAS
- ÁREA BRT
- SERVICIO PÚBLICO
- ZONA DE REFUGIO
- ÁREA NO PAGA
- ÁREA OPERATIVA
- ÁREA PAGA
- ÁREA PÚBLICA
- ÁREA TÉCNICA

TABLA DE ÁREAS ÚTILES (NIVEL ACCESO)

CÓDIGO	NOMBRE	ÁREA (m²)	DEPARTAMENTO
EDIFICIO ASCENDENTE			
ARQ_PL_00.4_ACCESO			
EMB-O-01	SERVICIOS ADICIONALES - OFICINAS	76.18	SERVICIOS ADICIONALES - ÁREA OFICINAS
NPA-03	ÁREA NO PAGA	173.93	ÁREA NO PAGA
ARQ_PL_00.5_ACCESO			
MB	NUEVO MONUMENTO A LOS HÉROES - MUSEO DEL BICENTENARIO	1010.01	MUSEO BICENTENARIO
ARQ_PL_00.6_ACCESO			
O-21-2	ALMACENAMIENTO DE LA ESTACIÓN	15.72	ÁREA OPERATIVA
R-00-1	SERVICIOS ADICIONALES - CORREDOR OPERATIVO	38.77	SERVICIOS ADICIONALES - ÁREA NO PAGA
R-00-2	SERVICIOS ADICIONALES - CORREDOR OPERATIVO	26.34	SERVICIOS ADICIONALES - ÁREA NO PAGA
R-01-1	SERVICIOS ADICIONALES - CUARTO DE BASURAS PARA METRO	16.50	SERVICIOS ADICIONALES - ÁREA NO PAGA
R-01-2	SERVICIOS ADICIONALES - CUARTO DE BASURAS PARA METRO	6.87	SERVICIOS ADICIONALES - ÁREA NO PAGA
R-02	SERVICIOS ADICIONALES - BAÑO PÚBLICO DE MUJERES	22.18	SERVICIOS ADICIONALES - ÁREA NO PAGA
R-03	SERVICIOS ADICIONALES - BAÑO PÚBLICO DE HOMBRES	20.34	SERVICIOS ADICIONALES - ÁREA NO PAGA
R-04	SERVICIOS ADICIONALES - CONTROL DE ACCESO BAÑOS PÚBLICOS	4.81	SERVICIOS ADICIONALES - ÁREA NO PAGA
R-05-1	SERVICIOS ADICIONALES - CUARTO DE LIMPIEZA	4.08	SERVICIOS ADICIONALES - ÁREA NO PAGA
R-05-2	SERVICIOS ADICIONALES - CUARTO DE LIMPIEZA	4.52	SERVICIOS ADICIONALES - ÁREA NO PAGA
R-06	SERVICIOS ADICIONALES - BAÑOS EMPLEADOS MUJERES	20.51	SERVICIOS ADICIONALES - ÁREA NO PAGA
R-07	SERVICIOS ADICIONALES - VESTIDORES EMPLEADOS MUJERES	8.18	SERVICIOS ADICIONALES - ÁREA NO PAGA
R-08	SERVICIOS ADICIONALES - BAÑOS EMPLEADOS HOMBRES	19.87	SERVICIOS ADICIONALES - ÁREA NO PAGA
R-09	SERVICIOS ADICIONALES - VESTIDORES EMPLEADOS HOMBRES	8.32	SERVICIOS ADICIONALES - ÁREA NO PAGA
R-10	SERVICIOS ADICIONALES - SALA DE EMPLEADOS	8.68	SERVICIOS ADICIONALES - ÁREA NO PAGA
R-202	SERVICIOS ADICIONALES - ÁREA DE COMIDAS	53.72	SERVICIOS ADICIONALES - ÁREA NO PAGA
R-203	SERVICIOS ADICIONALES - ÁREA DE COMIDAS	55.92	SERVICIOS ADICIONALES - ÁREA NO PAGA
R-204	SERVICIOS ADICIONALES - ÁREA DE COMIDAS	79.17	SERVICIOS ADICIONALES - ÁREA NO PAGA
T-20-G	MEDIDORES (GAS)	6.05	ÁREA TÉCNICA
T-30	SISTEMA PROTECCIÓN CONTRA INCENDIO ENEL	4.48	ÁREA TÉCNICA
ARQ_PL_00.7_ACCESO			
NPA-02	ÁREA NO PAGA	304.78	ÁREA NO PAGA
R-105	SERVICIOS ADICIONALES - ÁREA DE SERVICIO	115.57	SERVICIOS ADICIONALES - ÁREA NO PAGA
R-201	SERVICIOS ADICIONALES - ÁREA DE COMIDAS	55.79	SERVICIOS ADICIONALES - ÁREA NO PAGA
T-08-2	CENTRO DE TRANSFORMACIÓN ENEL-CODENSA (CT)_CUARTO BAJA TENSIÓN	24.67	ÁREA TÉCNICA
T-08-3	CENTRO DE TRANSFORMACIÓN ENEL-CODENSA (CT)_CUARTO MEDIA TENSIÓN	36.50	ÁREA TÉCNICA
T-20-L-2	MEDIDORES (LUZ)	13.39	ÁREA TÉCNICA
T-20-W-2	MEDIDORES (AGUA)	8.69	ÁREA TÉCNICA
T-21-3	ÁREA DE INSPECCIÓN	23.09	ÁREA TÉCNICA
T-21-4	ÁREA DE INSPECCIÓN	14.24	ÁREA TÉCNICA
T-21-5	ÁREA DE INSPECCIÓN	10.65	ÁREA TÉCNICA
T-25-4	NODO DE ACCESO DE TELECOMUNICACIONES	3.81	ÁREA TÉCNICA
TM-1	ÁREA DE TAQUILLAS BRT	48.01	ÁREA DE TAQUILLAS BRT
ARQ_PL_01_ACCESO			
C	ÁREAS DE USO CULTURAL	4.00	ÁREA CULTURAL
T-25-3	NODO DE ACCESO DE TELECOMUNICACIONES	9.97	ÁREA TÉCNICA

TABLA DE ÁREAS ÚTILES (NIVEL ACCESO)

CÓDIGO	NOMBRE	ÁREA (m²)	DEPARTAMENTO
EDIFICIO DESCENDENTE			
ARQ_PL_00.1_ACCESO			
C-01	ÁREAS DE USO CULTURAL	4.00	ÁREA CULTURAL
NPA-02	ÁREA NO PAGA	211.82	ÁREA NO PAGA
NPA-03	ÁREA NO PAGA	19.86	ÁREA NO PAGA
R-00	SERVICIOS ADICIONALES - CORREDOR OPERATIVO	47.47	SERVICIOS ADICIONALES - ÁREA NO PAGA
R-02	SERVICIOS ADICIONALES - BAÑO PÚBLICO DE MUJERES	17.70	SERVICIOS ADICIONALES - ÁREA NO PAGA
R-03	SERVICIOS ADICIONALES - BAÑO PÚBLICO DE HOMBRES	18.62	SERVICIOS ADICIONALES - ÁREA NO PAGA
R-04	SERVICIOS ADICIONALES - CONTROL DE ACCESO BAÑOS PÚBLICOS	6.03	SERVICIOS ADICIONALES - ÁREA NO PAGA
R-05-2	SERVICIOS ADICIONALES - CUARTO DE LIMPIEZA	4.81	SERVICIOS ADICIONALES - ÁREA NO PAGA
R-103	SERVICIOS ADICIONALES - ÁREA DE SERVICIO	31.05	SERVICIOS ADICIONALES - ÁREA NO PAGA
R-202	SERVICIOS ADICIONALES - ÁREA DE COMIDAS	106.68	SERVICIOS ADICIONALES - ÁREA NO PAGA
R-203	SERVICIOS ADICIONALES - ÁREA DE COMIDAS	36.25	SERVICIOS ADICIONALES - ÁREA NO PAGA
R-204	SERVICIOS ADICIONALES - ÁREA DE COMIDAS	26.02	SERVICIOS ADICIONALES - ÁREA NO PAGA
T-00-3	CIRCULACIÓN TÉCNICA	35.03	ÁREA TÉCNICA
T-08-2	CENTRO DE TRANSFORMACIÓN ENEL-CODENSA (CT)_CUARTO BAJA TENSIÓN	14.99	ÁREA TÉCNICA
T-08-3	CENTRO DE TRANSFORMACIÓN ENEL-CODENSA (CT)_CUARTO MEDIA TENSIÓN	33.87	ÁREA TÉCNICA
T-20-L-1	MEDIDORES (LUZ)	12.15	ÁREA TÉCNICA
T-20-W-2	MEDIDORES (AGUA)	5.97	ÁREA TÉCNICA
T-21-3	ÁREA DE INSPECCIÓN	7.25	ÁREA TÉCNICA
T-25-1	NODO DE ACCESO DE TELECOMUNICACIONES	5.65	ÁREA TÉCNICA
T-30	SISTEMA PROTECCIÓN CONTRA INCENDIO ENEL	8.90	ÁREA TÉCNICA
ARQ_PL_00.2_ACCESO			
R-01	SERVICIOS ADICIONALES - CUARTO DE BASURAS PARA METRO	15.96	SERVICIOS ADICIONALES - ÁREA NO PAGA
R-05-1	SERVICIOS ADICIONALES - CUARTO DE LIMPIEZA	5.14	SERVICIOS ADICIONALES - ÁREA NO PAGA
R-06	SERVICIOS ADICIONALES - BAÑOS EMPLEADOS MUJERES	16.92	SERVICIOS ADICIONALES - ÁREA NO PAGA
R-07	SERVICIOS ADICIONALES - VESTIDORES EMPLEADOS MUJERES	13.49	SERVICIOS ADICIONALES - ÁREA NO PAGA
R-08	SERVICIOS ADICIONALES - BAÑOS EMPLEADOS HOMBRES	26.40	SERVICIOS ADICIONALES - ÁREA NO PAGA
R-09	SERVICIOS ADICIONALES - VESTIDORES EMPLEADOS HOMBRES	21.10	SERVICIOS ADICIONALES - ÁREA NO PAGA
R-10	SERVICIOS ADICIONALES - SALA DE EMPLEADOS	16.85	SERVICIOS ADICIONALES - ÁREA NO PAGA
R-102	SERVICIOS ADICIONALES - ÁREA DE SERVICIO	27.74	SERVICIOS ADICIONALES - ÁREA NO PAGA
R-201	SERVICIOS ADICIONALES - ÁREA DE COMIDAS	63.22	SERVICIOS ADICIONALES - ÁREA NO PAGA
T-00-2	CIRCULACIÓN TÉCNICA	35.39	ÁREA TÉCNICA
ARQ_PL_00.3_ACCESO			
NPA-01	ÁREA NO PAGA	283.47	ÁREA NO PAGA
O-21	ALMACENAMIENTO DE LA ESTACIÓN	25.28	ÁREA OPERATIVA
R-101	SERVICIOS ADICIONALES - ÁREA DE SERVICIO	72.02	SERVICIOS ADICIONALES - ÁREA NO PAGA
T-06-2	LOCAL SECUNDARIO DE TABLEROS	35.17	ÁREA TÉCNICA
T-20-G	MEDIDORES (GAS)	9.22	ÁREA TÉCNICA
T-21-2	ÁREA DE INSPECCIÓN	38.00	ÁREA TÉCNICA
ARQ_PL_00.5_ACCESO			
CADE	CADE	825.39	CADE
T-00-1	CIRCULACIÓN TÉCNICA	16.09	ÁREA TÉCNICA
T-03-1	LOCAL SECUNDARIO DE TELECOMUNICACIONES	39.48	ÁREA TÉCNICA
T-06-1	LOCAL SECUNDARIO DE TABLEROS	49.66	ÁREA TÉCNICA
T-20-W-1	MEDIDORES (AGUA)	5.55	ÁREA TÉCNICA
T-21-1	ÁREA DE INSPECCIÓN	6.60	ÁREA TÉCNICA
TM-2	ÁREA DE TAQUILLAS BRT	18.52	ÁREA DE TAQUILLAS BRT
TOTAL NIVEL ACCESO		4679.04	

TABLA DE ÁREAS ÚTILES POR DEPARTAMENTO (NIVEL ACCESO)

DEPARTAMENTO	ÁREA (m²)
EDIFICIO ASCENDENTE	
ARQ_PL_00.4_ACCESO	
SERVICIOS ADICIONALES - ÁREA OFICINAS	76.18
ÁREA NO PAGA	173.93
ARQ_PL_00.5_ACCESO	
MUSEO BICENTENARIO	1010.01
ARQ_PL_00.6_ACCESO	
SERVICIOS ADICIONALES - ÁREA NO PAGA	398.76
ÁREA OPERATIVA	15.72
ÁREA TÉCNICA	10.53
ARQ_PL_00.7_ACCESO	
SERVICIOS ADICIONALES - ÁREA NO PAGA	171.37
ÁREA DE TAQUILLAS BRT	48.01
ÁREA NO PAGA	304.78
ÁREA TÉCNICA	135.04
ARQ_PL_01_ACCESO	
ÁREA CULTURAL	4.00
ÁREA TÉCNICA	9.97
EDIFICIO DESCENDENTE	
ARQ_PL_00.1_ACCESO	
SERVICIOS ADICIONALES - ÁREA NO PAGA	294.63
ÁREA CULTURAL	4.00
ÁREA NO PAGA	231.68
ÁREA TÉCNICA	123.81
ARQ_PL_00.2_ACCESO	
SERVICIOS ADICIONALES - ÁREA NO PAGA	206.81
ÁREA TÉCNICA	35.39
ARQ_PL_00.3_ACCESO	
SERVICIOS ADICIONALES - ÁREA NO PAGA	72.02
ÁREA NO PAGA	283.47
ÁREA OPERATIVA	25.28
ÁREA TÉCNICA	82.38
ARQ_PL_00.5_ACCESO	
CADE	825.39
ÁREA DE TAQUILLAS BRT	18.52
ÁREA TÉCNICA	117.38
TOTAL NIVEL ACCESO	4679.04

No.	PLANOS DE REFERENCIA	REV.

No.	MODELO BIM DE REFERENCIA	REV.
1	L1T1-1100-216-CON-ED-EST-MO-0001.rvt	V00
2	L1T1-1100-217-CON-ED-EST-MO-0001.rvt	V00
3	L1T1-1100-316-CON-ED-EST-MO-0001.rvt	V00
4	L1T1-1150-216-CON-ED-EST-MO-0001.rvt	V00
5	L1T1-1150-217-CON-ED-EST-MO-0001.rvt	V00
6	L1T1-1150-316-CON-ED-EST-MO-0001.rvt	V00
7	L1T1-1200-316-CON-ED-EST-MO-0001.rvt	V00
8	L1T1-1300-416-CON-ED-EST-MO-0001.rvt	V00
9	L1T1-1300-416-CON-ED-EST-MO-0002.rvt	V00
10	L1T1-1310-416-CON-ED-EST-MO-0001.rvt	V00
11	L1T1-1410-316-CON-ED-MEC-MO-0001.rvt	V00
12	L1T1-1420-316-CON-ED-MEC-MO-0001.rvt	V00
13	L1T1-2320-593-CON-ED-EST-MO-0001.rvt	V00
14	L1T1-2330-593-CON-ED-ARQ-MO-0001.rvt	V00
15	L1T1-2430-541-CON-ED-ARQ-MO-0001.rvt	V00
16	L1T1-2430-541-CON-ED-EST-MO-0002.rvt	V00
17	L1T1-5160-316-CON-ED-EST-MO-0001.rvt	V00
18	L1T1-5160-316-CON-ED-ARQ-MO-0001.rvt	V00
19	L1T1-5300-316-CON-ED-MEC-MO-0001.rvt	V00
20	L1T1-5600-316-CON-ED-INS-MO-0001.rvt	V00
21	L1T1-1330-416-CON-ED-ARQ-MO-0011.rvt	V00
22	L1T1-1330-416-CON-ED-ARQ-MO-0012.rvt	V00

No.	PAQUETE DE TRABAJO DE REFERENCIA	REV.
1	XREF-URBANISM_CONTEXT_ST16.rvt	
2	RVT_MONUMENTO A LOS HEROES_v9.rvt	
3	XREF-SECONDARY-STRUCTURE-ST16.rvt	

0 2 10m
1:200

VÁLIDO PARA CONSTRUCCIÓN
31-03-26

PLANO CLAVE ESTACIÓN 16

DISEÑÓ:
REN ZHENHUA
Licencia de Arq.nivel I (China): 1101735-614

APROBÓ:
DIEGO ERNESTO DUEÑAS
Mat.: 25202-53876 CND

REVISÓ:
CARLOS MAURICIO BARRETO BARBOSA
Mat.: A4012012-14139353

DIBUJÓ:
EQUIPO CHEC

REVISIÓN No.	FECHA	DESCRIPCIÓN	REVISÓ	APROBÓ	APROBACIÓN CLIENTE
V01	31/03/2026	EMITIDO PARA CONSTRUCCIÓN	C.M.B.B	D.E.D	
V00	27/01/2025	REVISIÓN NO OBJETADA - EMITIDO PARA CONSTRUCCIÓN	F.B.R	E.O.M	
VFF	12/09/2024	EMITIDO PARA REVISIÓN Y COMENTARIOS DEL CLIENTE E INTERVENTORÍA - INCLUYE COMENTARIOS /(AJUSTES V2)	F.B.R	E.O.M	
VEE	04/06/2024	EMITIDO PARA REVISIÓN Y COMENTARIOS DEL CLIENTE E INTERVENTORÍA - INCLUYE COMENTARIOS /(AJUSTES)	F.B.R	E.O.M	
VDD	18/12/2022	EMITIDO PARA REVISIÓN Y COMENTARIOS DEL CLIENTE E INTERVENTORÍA - INCLUYE COMENTARIOS /(NO APLICA)	J.E.M	M.B.M	
VCC	22/08/2022	EMITIDO PARA REVISIÓN Y COMENTARIOS DEL CLIENTE E INTERVENTORÍA - INCLUYE COMENTARIOS /(NO APLICA)	J.E.M	M.B.M	
VBB	06/12/2021	EMITIDO PARA REVISIÓN Y COMENTARIOS DEL CLIENTE E INTERVENTORÍA	J.E.M	M.B.M	
VA0	30/06/2021	EMITIDO PARA COMENTARIOS INTERNOS - EMISIÓN PRELIMINAR PARA COMENTARIOS	J.E.M	M.B.M	

METRO LÍNEA 1

METRO LÍNEA 1
CONTRATO DE CONCESIÓN No. 163 DE 2019

PROYECTO PRIMERA LÍNEA DEL METRO DE BOGOTÁ - TRAMO 1

DIRECTOR DE INTERVENTORÍA:
JAVIER DESCARGA N.
Mat.:25202-68697 CND

ESPECIALISTA INTERVENTORÍA:
CARLOS ALBERTO HOYOS SOTO
Mat.:A25072000-14251682

FECHA:
MARZO 2026

INFRAESTRUCTURA VIAL

ARQUITECTURA

ESTACIÓN METRO 16 (CALLE 72)
EDIFICIO ASCENDENTE - NAVE CENTRAL - EDIFICIO DESCENDENTE
VISTA EN PLANTA Y 3D - NIVEL ACCESO

PLANCHA No: L1T1-0000-316-CON-ED-ARQ-PL-0001_05_V01
ARCHIVO: L1T1-0000-316-CON-ED-ARQ-MO-0001_V00.rvt
ESCALA: INDICADA
FECHA: JUNIO 2021
REVISIÓN No.: V01
PLANO No.: 05 DE 85