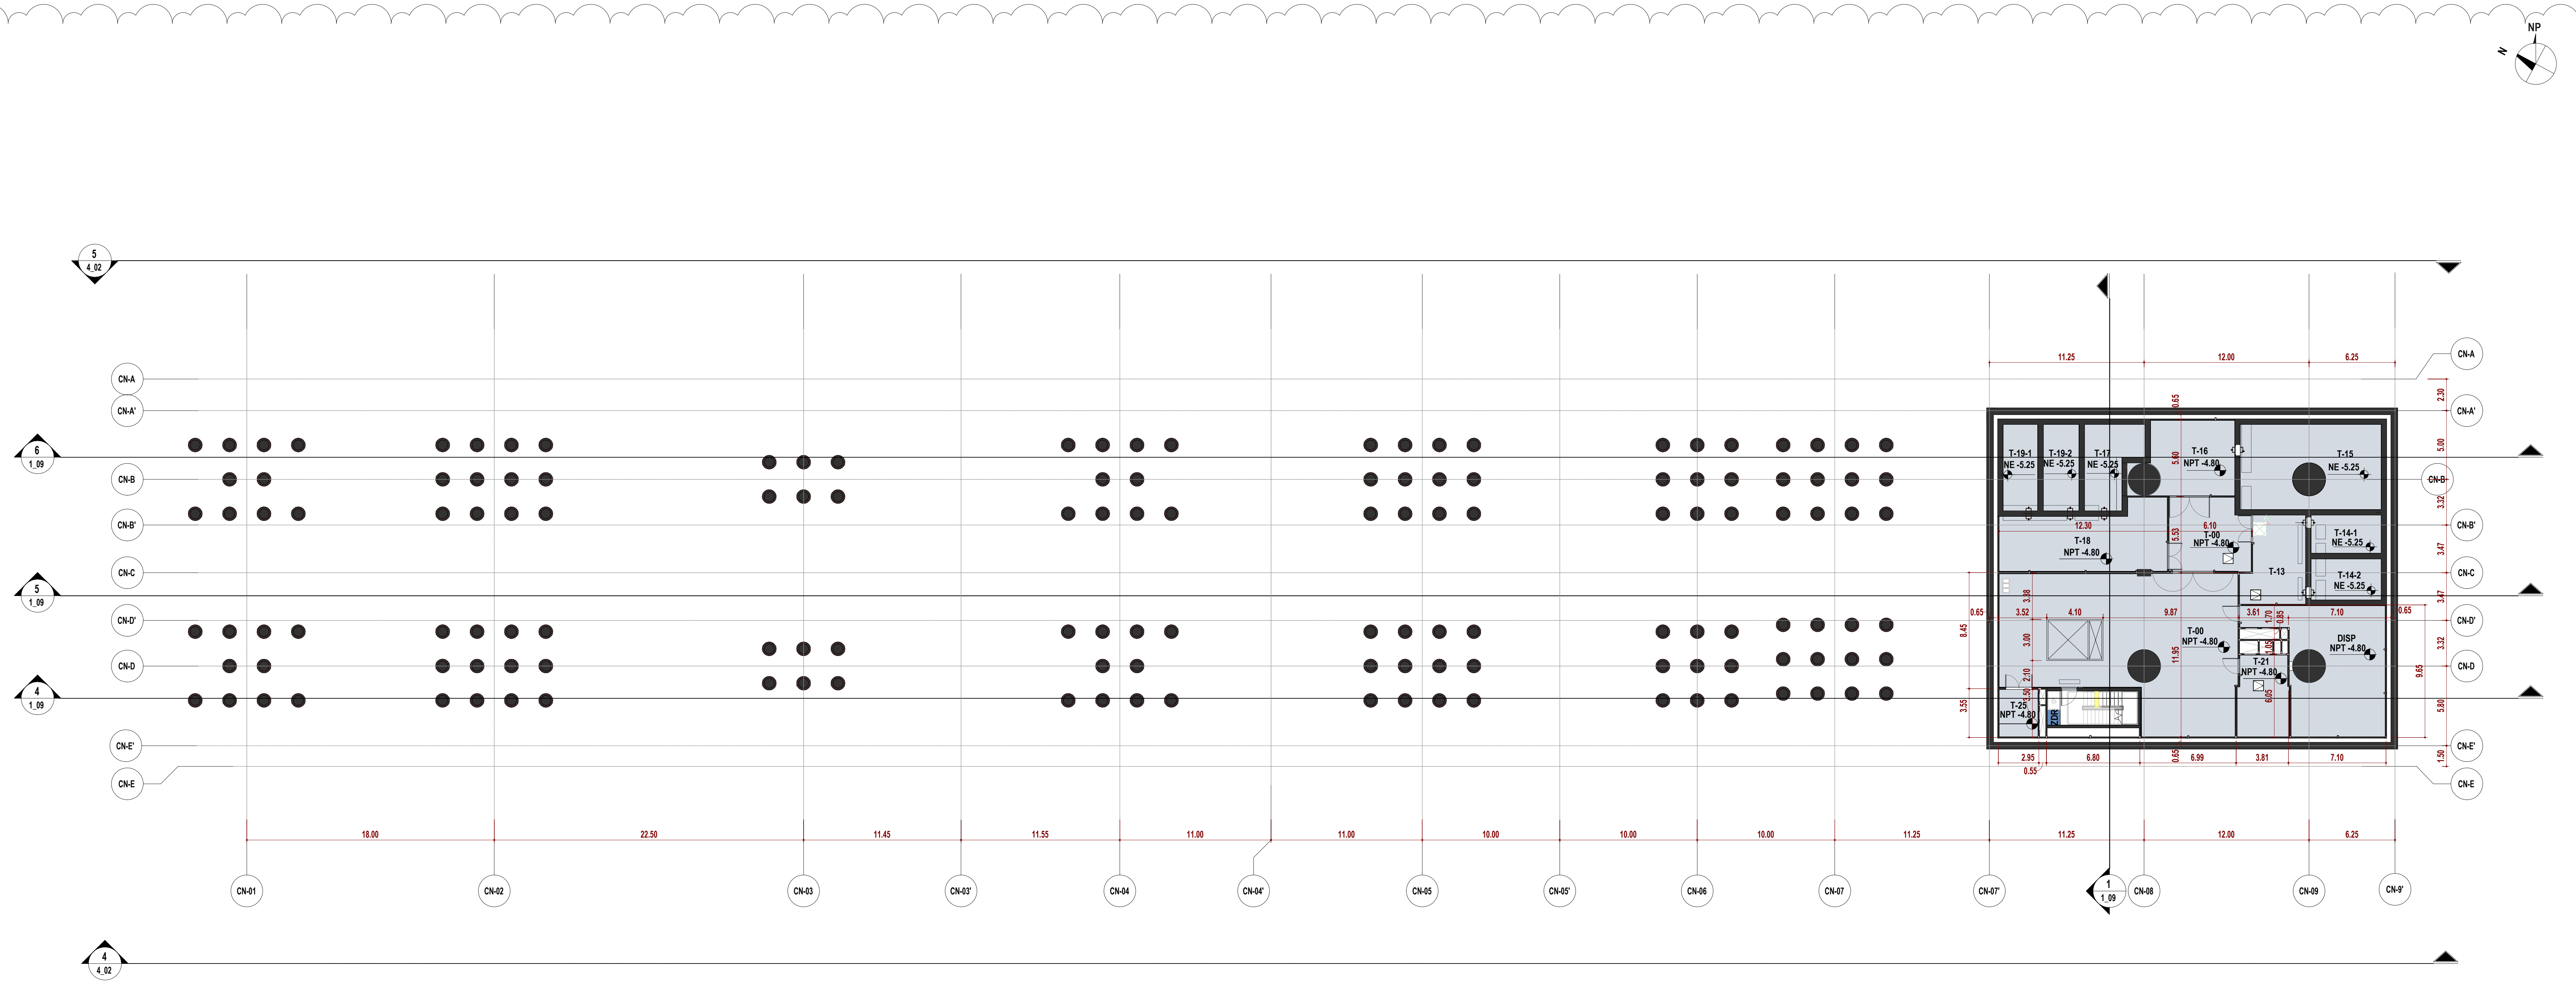

2 **NIVEL SÓTANO_NAVE CENTRAL**
ESC: 1 : 200

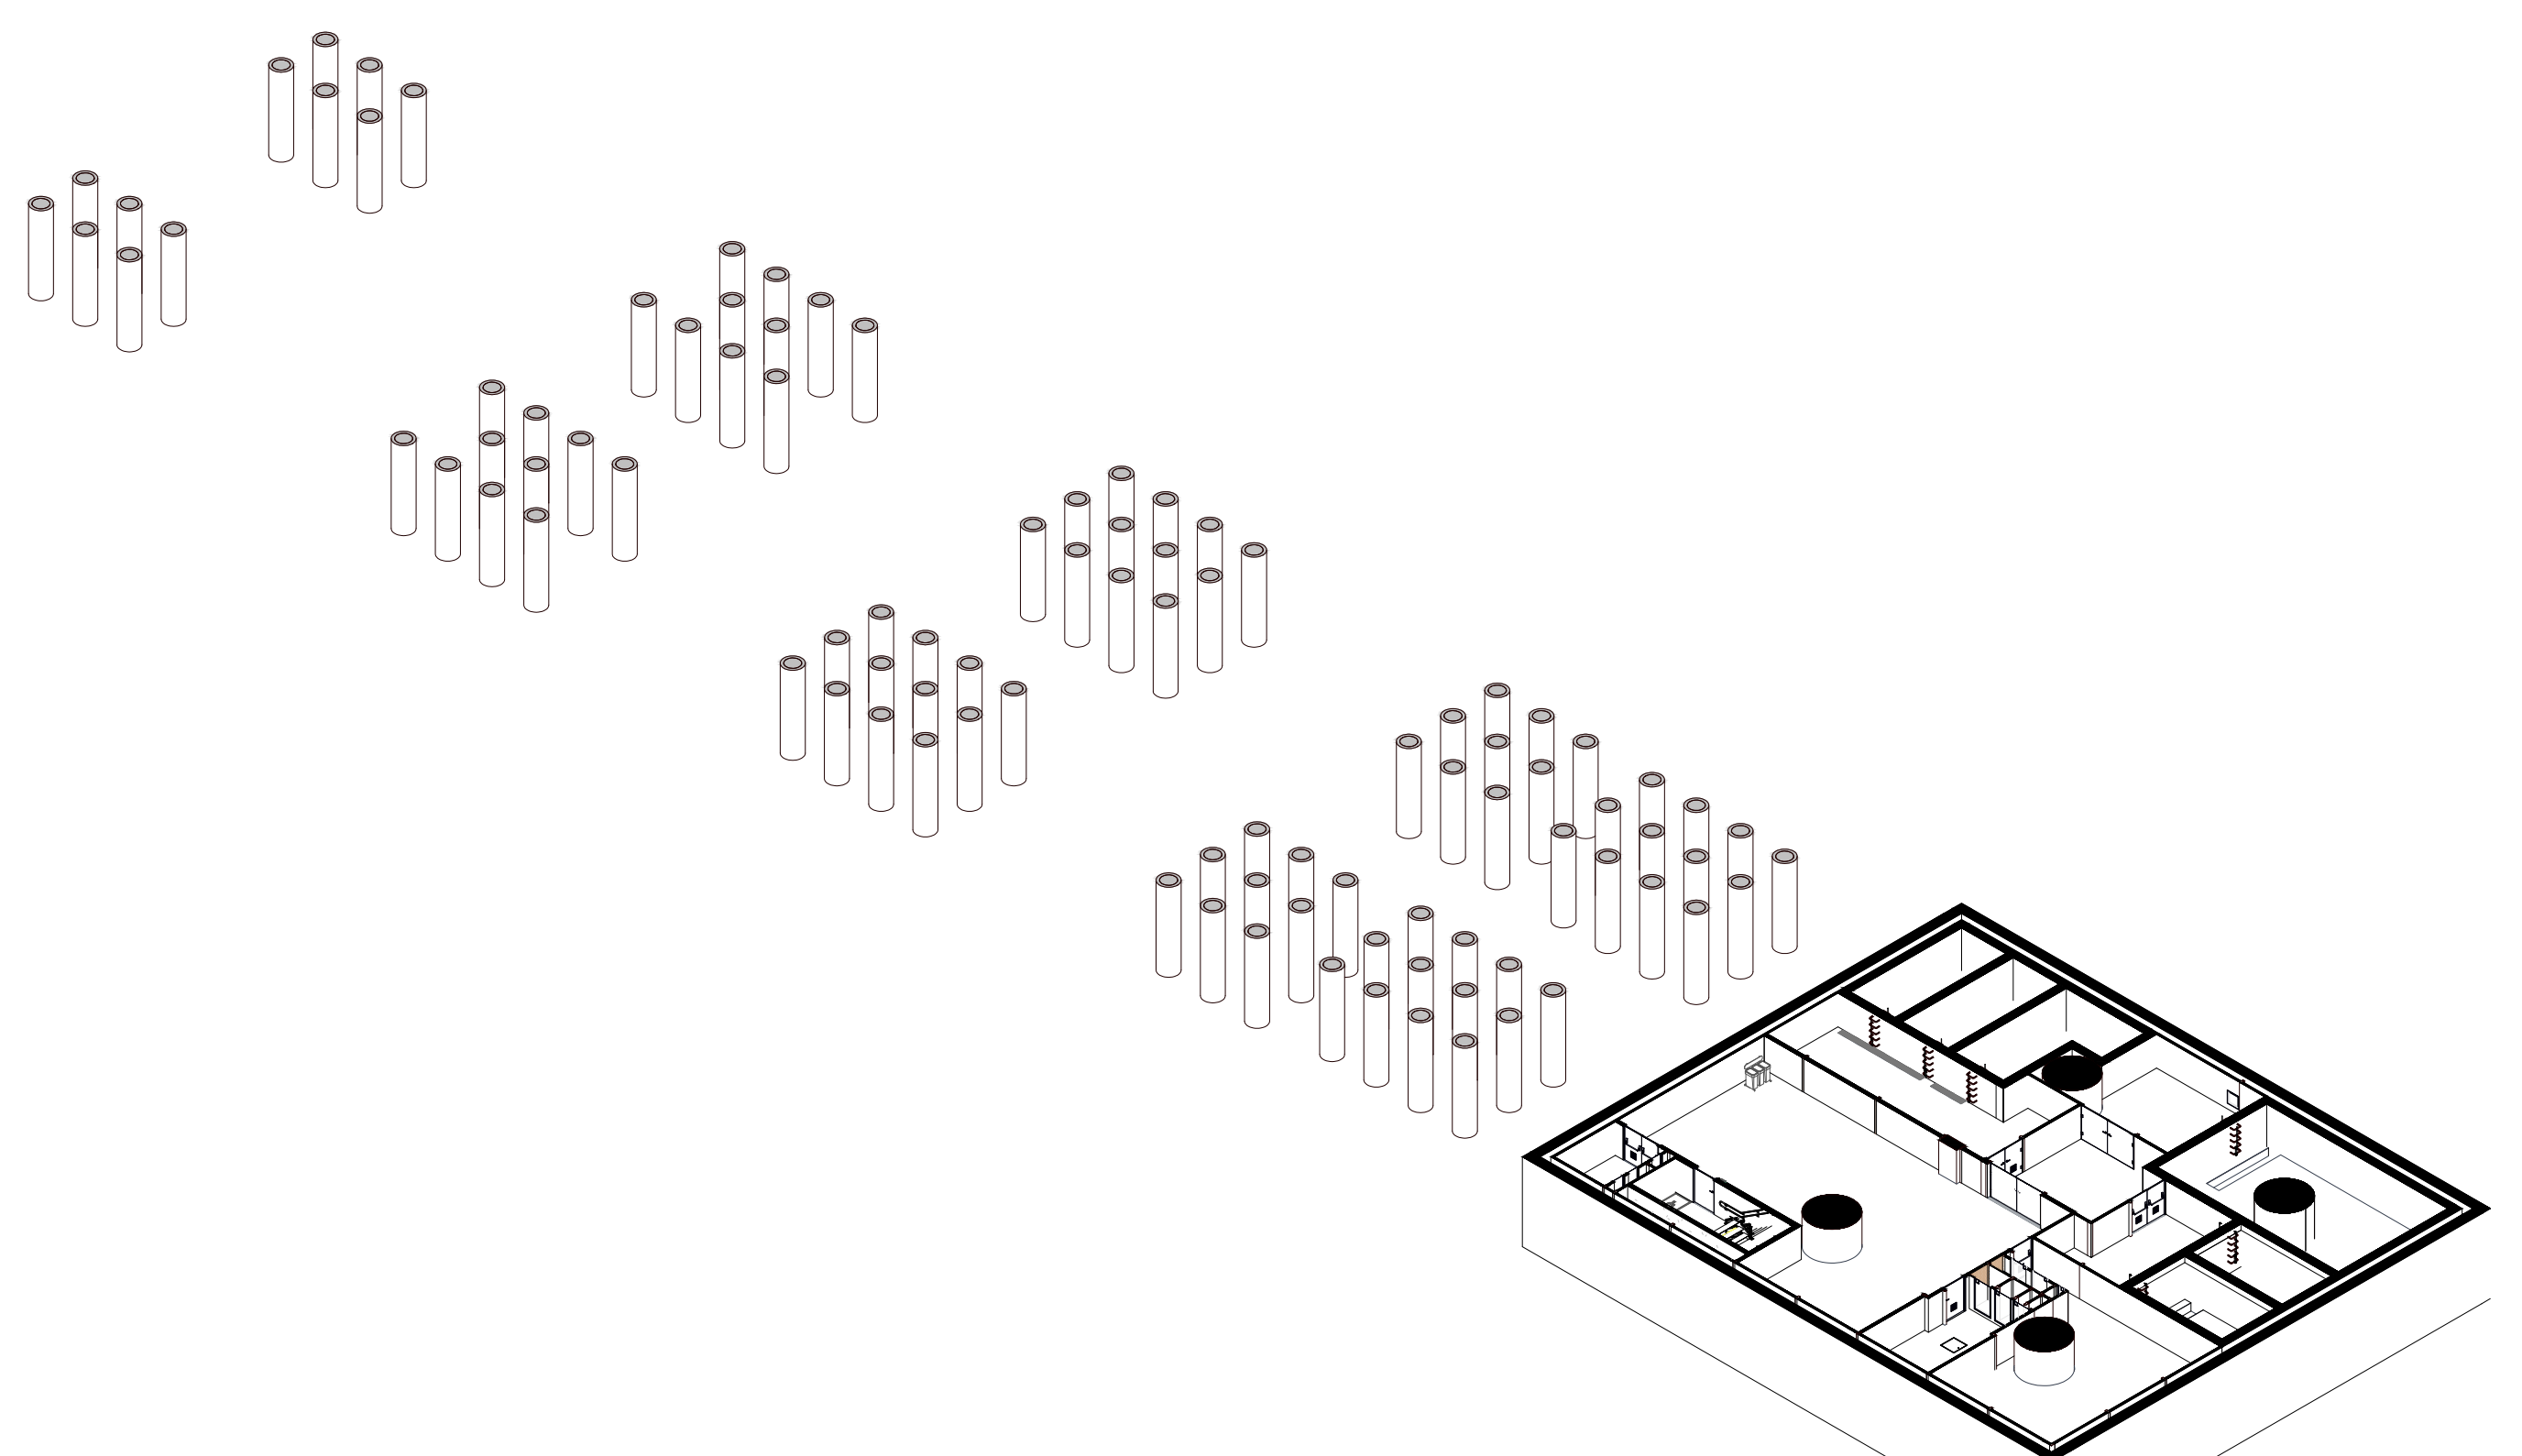

1 **3D_NIVEL SÓTANO_NAVE CENTRAL**
ESC: N/A

07_TABLA DE ÁREAS ÚTILES (NIVEL SÓTANO_NAVE CENTRAL)

CÓDIGO	NOMBRE	ÁREA (m2)	DEPARTAMENTO
ARC_PL_00			
DISP	DISPONIBLE	67.23	ÁREA TÉCNICA
T-00	CIRCULACIÓN TÉCNICA	30.70	ÁREA TÉCNICA
T-00	CIRCULACIÓN TÉCNICA	163.32	ÁREA TÉCNICA
T-13	CUARTO DE BOMBAS DE SUMINISTRO DE AGUA	27.00	ÁREA TÉCNICA
T-14-1	TANQUE DE SUMINISTRO DE AGUA	14.12	ÁREA TÉCNICA
T-14-2	TANQUE DE SUMINISTRO DE AGUA	15.23	ÁREA TÉCNICA
T-15	TANQUE SISTEMA CONTRA INCENDIOS (RCI)	58.83	ÁREA TÉCNICA
T-16	CUARTO DE BOMBAS DE ROCIADORES	38.57	ÁREA TÉCNICA
T-17	TANQUE DE RECUPERACIÓN DE AGUAS LLUVIAS	21.09	ÁREA TÉCNICA
T-18	CUARTO DE BOMBAS DE RECUPERACIÓN DE AGUAS LLUVIAS Y EQUIPO DE FILTRACIÓN	55.40	ÁREA TÉCNICA
T-19-1	TANQUE DE AGUA TRATADA	15.78	ÁREA TÉCNICA
T-19-2	TANQUE DE AGUA TRATADA	16.32	ÁREA TÉCNICA
T-21	ÁREA DE INSPECCIÓN	21.79	ÁREA TÉCNICA
T-25	NODO DE ACCESO DE TELECOMUNICACIONES	9.76	ÁREA TÉCNICA
ZDR	ZONA DE REFUGIO (PMR)	2.36	ZONA DE REFUGIO
TOTAL NIVEL SÓTANO_NAVE CENTRAL		557.49	

05_TABLA DE ÁREAS ÚTILES POR DEPARTAMENTO (NIVEL SÓTANO)

DEPARTAMENTO	ÁREA (m²)
ARC_PL_00	
ZONA DE REFUGIO	2.36
ÁREA TÉCNICA	555.13
TOTAL NIVEL	557.49

LOCALIZACIÓN

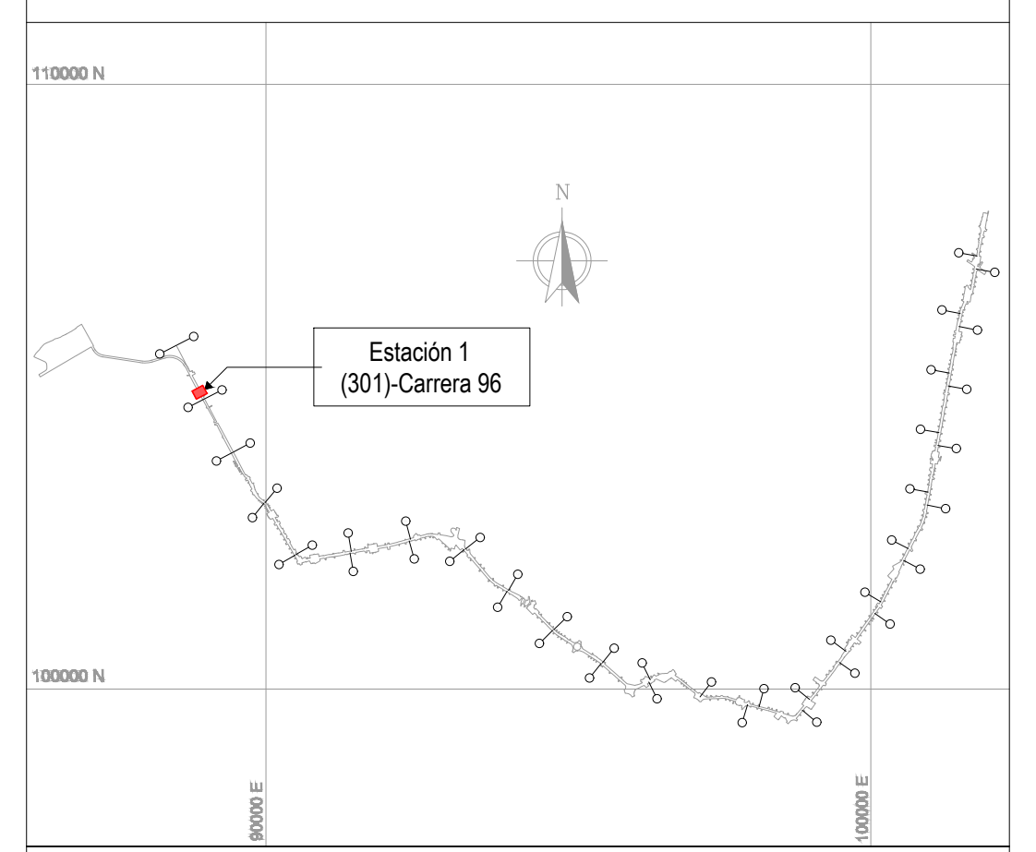

NOTAS

01 TODAS LAS DIMENSIONES ESTÁN CONFIGURADAS EN METROS A MENOS QUE SE INDIQUE UNA UNIDAD DE MEDIDA DIFERENTE.

02 TODAS LAS MEDIDAS, UBICACIÓN Y NIVELES DEBEN VERIFICARSE EN EL LUGAR DE CONSTRUCCIÓN.

03 EL NIVEL DE ACCESO AL EDIFICIO PL 01 CORRESPONDE AL +0,00 DE LA ESTACIÓN Y REFERENCIA AL NIVEL 2540.90 M.S.N.M

04 LOS NOMBRES ESPECIFICOS DE LAS ÁREAS PUEDEN SER CONSULTADAS EN EL PLANO NO. 3 O EN LAS VISTAS EN PLANTA.

05 LOS COLORES QUE SE MUESTRAN EN LOS PLANOS COMO PROYECCIÓN DE ELEMENTOS ARQUITECTÓNICOS COMO CUBIERTAS FACHADAS MUROS ETC. NO REPRESENTAN LA MATERIALIDAD Y REALIDAD DE ACABADOS DEL PROYECTO, SOLO SON INDICATIVOS PARA REALIZAR UNA CORRECTA LECTURA DE LA PLANIMETRÍA.

06 EL NIVEL ESTRUCTURAL (NE) SE ENCUENTRA A (- 0.10m) POR DEBAJO DE LOS NIVELES DE PISO TERMINADO (NPT) MARCADOS EN LA PLANIMETRÍA.

- ARC_PL_00 = SÓTANO	/ NPT -5.80 m
- ARC_PL_01 = ACCESO	/ NPT -0.00 m
- ARC_PL_02 = INTERMEDIO	/ NPT -7.60 m
- ARC_PL_02.1 = PLACA INFERIOR VIGA CAJÓN	/ NPT -14.07 m
- ARC_PL_02.2 = TOPE DE RIEL (TOR)	/ NPT -16.20 m
- ARC_PL_03 = PLATAFORMA	/ NPT -17.34 m
- ARC_PL_05 = CUBIERTA NAVE CENTRAL	/ NPT -26.70 m

CONVENCIONES

- - -	LIMITE DE INTERVENCIÓN
- - -	AREAS DE ACUMULACIÓN
▬	MURO DIVISORIO
— — —	PROYECCIÓN NIVEL SUPERIOR
🟩	SERVICIOS ADICIONALES - ÁREA NO PAGA
🟩	SERVICIOS ADICIONALES - ÁREA PAGA
🟩	SERVICIO PÚBLICO
🟦	ZONA DE REFUGIO
🟥	ÁREA CULTURAL
🟩	ÁREA JARDÍN
🟨	ÁREA NO PAGA
🟦	ÁREA OPERACIONAL
🟧	ÁREA PAGA
🟦	ÁREA PÚBLICA
⬜	ÁREA TÉCNICA

VB1
CAMBIOS REALIZADOS
1. SE AJUSTA MURO DE LIMPIEZA Y CUADROS DE ÁREAS

No.	PLANOS DE REFERENCIA	REV.

No.	MODELO BIM DE REFERENCIA	REV.
1	L1T1-1100-201-CON-ED-EST-MO-0001.rvt	V01
2	L1T1-1100-202-CON-ED-EST-MO-0001.rvt	V01
3	L1T1-1100-301-CON-ED-EST-MO-0001.rvt	V03
4	L1T1-1150-201-CON-ED-EST-MO-0001.rvt	V01
5	L1T1-1150-202-CON-ED-EST-MO-0001.rvt	V01
6	L1T1-1410-301-CON-ED-MEC-MO-0001.rvt	V00
7	L1T1-1420-301-CON-ED-MEC-MO-0001.rvt	V00
8	L1T1-1430-301-CON-ED-MEC-MO-0001.rvt	V00

No.	PAQUETE DE TRABAJO DE REFERENCIA	REV.
1	XREF-URBANISM_CONTEXT_ST01.rvt	

1
VB1

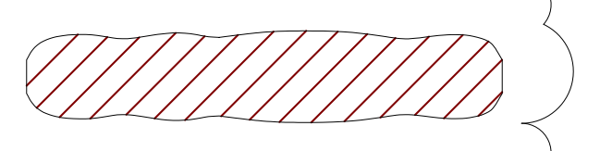

PLANO CLAVE ESTACIÓN 01

0 2 10m
1:200

METRO BOGOTÁ
GCS Consorcio Consultores PMO Bogotá
CONSORCIO SUPERVISOR PLMB
PEDELTA

DISEÑÓ:
OSCAR HIGUERA H.
Mat.:A20622022-1022410319

APROBÓ:
FELIPE SAAVEDRA
Mat:.25202-149684 CND

REVISÓ:
VERóNICA MIRANDA
Mat.:A25032002-52387701

DIBUJÓ:
EQUIPO PEDELTA

REVISIÓN No.	FECHA	DESCRIPCIÓN	REVISÓ	APROBÓ	APROBACIÓN CLIENTE
VB1	23/12/2025	EMITIDO PARA REVISIÓN Y COMENTARIOS DEL CLIENTE E INTERVENTORÍA	V.M.	F.S	
V00	23/08/2024	REVISIÓN NO OBJETADA - EMITIDO PARA CONSTRUCCIÓN	V.M.	F.S	
VDD	06/05/2024	EMITIDO PARA REVISIÓN Y COMENTARIOS DEL CLIENTE E INTERVENTORÍA	V.M.	F.S	
VCC	15/03/2024	EMITIDO PARA REVISIÓN Y COMENTARIOS DEL CLIENTE E INTERVENTORÍA	V.M.	F.S	
VBB	20/12/2023	EMITIDO PARA REVISIÓN Y COMENTARIOS DEL CLIENTE E INTERVENTORÍA	A.B.H	F.S	

METRO LÍNEA 1

METRO LÍNEA 1
CONTRATO DE CONCESIÓN No. 163 DE 2019

PROYECTO PRIMERA LÍNEA DEL METRO DE BOGOTÁ - TRAMO 1

DIRECTOR DE INTERVENTORÍA:
JAVIER DESCARGA N.
Mat.:2520268697 CND

ESPECIALISTA INTERVENTORÍA:
YOLANDA TARRIDA LÓPEZ
INT:

FECHA:
DICIEMBRE 2025

INFRAESTRUCTURA VIAL

ARQUITECTURA

ESTACIÓN METRO 1 (CARRERA 96)
NAVE CENTRAL
VISTA EN PLANTA - NIVEL SÓTANO 01

PLANCHA No: L1T1-0000-301-CON-ED-ARQ-PL-0096_04_VB1
ARCHIVO: L1T1-0000-301-CON-ED-ARQ-MO-0001_V00.rvt
ESCALA: 1:200
FECHA: DICIEMBRE 2023
REVISIÓN No. VB1
PLANO No. 04 DE 45